Қазақстан, 010000,Нур-Султан қ.
Керей, Жәнибек хандар көш. 5, оф. 62
+7 (717) 227 75 92
Казахстан Республикасы, Алматы қаласы,
Бостандық аудыны, Тимирязева көшесі,
42 үй, 15/108 корпус, 408 кеңсе,
+7 701 026 46 77

АстанаИнжПроект

5 Kerei Zhanibek khandar str, 62
Nur-Sultan, 010000, Kazakhstan
+7 (717) 227 75 92
Republic of Kazakhstan, city of Almaty,
Bostandyk district, Timiryazev street, 42,
building block 15/108, office 408
+7 701 026 46 77

ГСЛ № 14015145

РАБОЧИЙ ПРОЕКТ

«Строительство многопрофильной больницы на 250 коек с онкологическим центром и поликлиникой на 350 посещений, по адресу: Медеуский район, г.Алматы»

Конструкции железобетонные. Блок 1 Секция 1
ТОМ - 6

Альбом 1

г. Астана, 2025 г.

Қазақстан, 010000,Нур-Султан қ.
Керей, Жәнибек хандар көш. 5, оф. 62
+7 (717) 227 75 92
Казахстан Республикасы, Алматы қаласы,
Бостандық ауданы, Тимирязева көшесі,
42 үй, 15/108 корпус, 408 кеңсе,
+7 701 026 46 77

АстанаИнжПроект

5 Kerei Zhanibek khandar str, 62
Nur-Sultan, 010000, Kazakhstan
+7 (717) 227 75 92
Republic of Kazakhstan, city of Almaty,
Bostandyk district, Timiryazev street, 42,
building block 15/108, office 408
+7 701 026 46 77

ГСЛ № 14015145

Объект:

«Строительство многопрофильной больницы на 250 коек с онкологическим центром и поликлиникой на 350 посещений, по адресу: Медеуский район, г.Алматы»

Стадия: Рабочий проект
Раздел: КЖ - Конструкции железобетонные
Альбом: 65П-АИП-2024-1-КЖ

Директор "ТОО Астанаинжпроект"_____ Баймбетов Д.С.

ГИП "ТОО Астанаинжпроект"_____ Нурмухамбетов Е.К.

г. Астана, 2025 г.

Общие указания

1. Проектная документация по конструктивному разделу проекта разработана на основании:
- задания на проектирование;
- архитектурного, технологического и инженерного разделов проекта;

отчёта об инженерно-геологических изысканиях на объекте «Строительство многопрофильной больницы на 250 коек онкологическим центром и поликлиникой на 350 посещений по адресу Медеуский район,г.Алматы» в октябре 2024 г.

2. Характеристика района строительства:
- Климатический район: III-В. СП РК 2.04-01-2017
- Снеговой район – II
- Ветровой район -II
- нормативная снеговая нагрузка -1,2 кПа согласно НП к СП РК EN 1991-1-3:2003/2011, Часть 1-3 (НП. 3 Приложение);
- нормативная ветровая нагрузка 0,398 кПа согласно НП к СП РК EN 1991-1-4:2005/2011. Часть 1-4 (НП. 4 Приложение);
- Температура воздуха наиболее холодной пятидневки с обеспеченностью 0,98 – (– 23,3 °С);

Согласно СП РК 2.04-01-2017 нормативная глубина сезонного промерзания грунтов: для суглинков – 1,19 м, для песка 1,55м. Максимальная глубина проникновения нулевой изотермы в грунт – 155 см

Грунтовые воды на участке в период изысканий (октябрь-ноябрь- декабрь 2024 года) вскрыты на глубине 3,99-6,15м. По данным режимных наблюдений амплитуда колебания грунтовых вод составляет 1,5м. Максимальное положение уровня грунтовых вод отмечается в апреле-мае, минимальное с декабря по февраль (13)

3. КОНСТРУКТИВНЫЕ РЕШЕНИЯ

Здание представляет собой простое в плане и по высоте трехэтажное здание с подвалом и техническим этажом с эксплуатированные кровлем . Размеры в плане по осям 30х27.8м .

Высота подвала -4,27 м, высота типового этажа -3,9м , технический этаж -2,4м в конструкциях.

Тип конструктивной системы - каркас рамно-связевая система колонн и ригелей со всеми или некоторыми жесткими узлами их соединений (способными воспринимать изгибающие моменты), воспринимающая всю совокупность вертикальных и горизонтальных нагрузок;

- Фундаменты под несущие конструкции выполнены ввиду плиточного железобетонного фундамента высотой(h) 0.8 м. Бетон С20/25, Арматура класса А500С по ГОСТ 34028-2016.

Под фундаментную плиту выполняется бетонная подготовка толщиной 0,1 м из бетона класса С8/10 W6 F100, превышающую габариты плиты на 0,1 м. с каждой стороны.

- Стены- железобетонные, толщиной 0.25м. Бетон класса С20/25. Арматура класса А500С по ГОСТ 34028-2016.
- Колонны - железобетонные, сечением 0.6х0.6(h)м; 0.5х0.5(h)м и 0,4х0,5(h)м. Бетон С20/25. Арматура класса А500С по ГОСТ 34028-2016.
- Ригели - железобетонные, сечением 0.45х0.5(h)м; 0.3х0.45(h)м. Бетон С20/25. Арматура класса А500С по ГОСТ 34028-2016
- Плита перекрытия и покрытия - железобетонные, толщиной 0.22 м. Бетон С20/25. Арматура класса А500С по ГОСТ 34028-2016.
- Стыковку стержней рабочей арматуры колонн и ригелей выполнить и стен при >Ф20 при помощи ручной дуговой сварки типа С21-Рн протяженными швами с накладками из стержней в соответствии с ГОСТ 14098-2014. Стыки рабочей арматуры внахлестку без сварки, на скрутках из вязальной проволоки не менее 3 шт. на стык. Длина нахлеста 71d. Стыки располагать вразбежку, чтобы площадь рабочей арматуры, стыкуемой в одном сечении, не превышала 50%. Гнутые арматурные стержни должны гнуться механическим способом в холодном состоянии с радиусом гиба 4d-6d, где d - диаметр стержня.
- Обеспечить качество строительно-монтажных работ - в соответствии со СН РК 1.03-00-2011
- Освидетельствование скрытых работ с составлением актов на них необходимо производить на работы, указанные в нормативных документах СН РК 1.03-00-2011.
- Производство по устройству монолитных конструкций необходимо вести в соответствии со СП РК 5.03-107-2013 и СН РК 5.03-07-2013 "Несущие и ограждающие конструкции"
- При производстве всех видов работ руководствоваться СП РК 1.03-05-2011 и СН РК 1.03-106-2012 "Охрана труда и техника безопасности в строительстве".
- Стальные конструкции и выступающие из бетона части закладных деталей, доступные для

возобновления покрасить эмалью ГОСТ 6465-76* в 2 слоя по грунту ГФ-021 ГОСТ 25129-82* в 1 слой согласно СП РК 2.01-101-2013 и СН РК 2.01-01-2013 "Защита строительных конструкций от коррозии".

Указания по производству работ в зимних условиях

При производстве работ в зимних условиях следует руководствоваться строительными нормами и правилами на производство и приёмку бетонных и железобетонных конструкций, СН РК 5.03-07-2013 и СП РК 5.03-107-2013 «Несущие и ограждающие конструкции», другими действующими и техническими указаниями, а так же настоящими указаниями.

- Бетонирование при отрицательной температуре окружающей среды и температуре воздуха

выше +25 С должно выполняться согласно требованиям СП РК 5.03-107-2013 "Несущие и ограждающие конструкции".

Защита строительных конструкций от коррозии

Все мероприятия по проведению антикоррозийной защиты должны производиться согласно СН РК 2.01-01-2013 «Защита строительных конструкций и сооружений от коррозии». Антикоррозийная защита железобетонных конструкций обеспечивается соблюдением требуемой проектом толщины защитного слоя бетона и антикоррозийными покрытиями.

Гидроизоляция всех поверхностей фундаментов и стен соприкасающихся с грунтом, выполняется обмазкой битумной мастикой по ГОСТ 30693-2000 за два раза по слою грунтовки (ТУ2312-021-10861980-2013).

Все металлические конструкции здания, после сварных работ, очищаются от пыли и грязи, покрываются грунтовкой ГФ 021 (ГОСТ 25129-2020) в 2 слоя, затем окрашиваются эмалью ПФ 115 (ГОСТ 6465-76*). Закладные детали после изготовления подлежат оцинкованию.

АНТИСЕЙСМИЧЕСКАЯ МЕРОПРИЯТИЯ

Антисейсмические мероприятия предусмотрены в соответствии с требованиями СП РК 2.03.30-2017 "Строительство в сейсмических районах."

ПРОТИВОПОЖАРНЫЕ МЕРОПРИЯТИЯ

Противопожарные мероприятия осуществлять в соответствии со СН РК 2.02-01-2019 "Пожарная безопасность зданий и сооружений".

Устройства по основания фундамента возводимых на дресвяных грунтах

В проекте оснований и фундаментов должна предусматриваться защита элювиальных грунтов от разрушения атмосферными воздействиями и водой в период устройства котлованов. Для этой цели следует применять водозащитные мероприятия, не допускать перерывы в устройстве оснований и последующем возведении фундаментов; предусматривать недобор грунта в котловане; применять взрывной способ разработки скальных грунтов лишь при условии мелкошпуровой отпалки.

Поэтому устройство засыпки из песчано-гравийной смеси необходимо выполнять захватками, сразу же после выхода на проектную отметку котлована.


Ведомость ссылочных документов

Лист	Наименование	Примечание
	Ссылочные документы	
СП РК 2.03.30-2017	Строительство в сейсмических районах.	
СН РК 5.01-02-2013	Основания зданий и сооружений.	
СН РК 3.04-02-2019	Проектирование бетонные и железобетонные конструкции.	
СН РК 2.01-01-2013	Защита строительных конструкций от коррозии.	
СП РК EN 1990	Основы проектирования несущих конструкций	
СП РК EN 1991	Воздействия на несущие конструкции	
СП РК EN 1992	Основы проектирования несущих конструкций	
СП РК EN 1993	Проектирование стальных конструкций	
СП РК EN 1997	Геотехническое проектирование	
СП РК EN 1998	Проектирование сейсмостойких конструкций	

Перечень видов работ, для которых необходимо составление актов освидетельствования скрытых работ

1. Освидетельствование качества грунтов основания
2. Правильность геодезической разбивки осей и отметок фундаментов
3. Устройство бетонной подготовки под фундаменты
4. Устройство опалубки фундаментов
5. Армирование фундаментов
6. Бетонирование фундаментов
7. Устройство гидроизоляции фундаментов
8. Армирование колонн
9. Бетонирование колонн
10. Армирование ригелей.
11. Бетонирование ригелей
12. Армирование стен
13. Бетонирование стен
14. Армирование перекрытий
15. Бетонирование перекрытий
16. Антикоррозийная защита сварных соединений
17. Устройство обратной засыпки фундаментов
18. Антикоррозионная защита конструкций

Схема блокировка

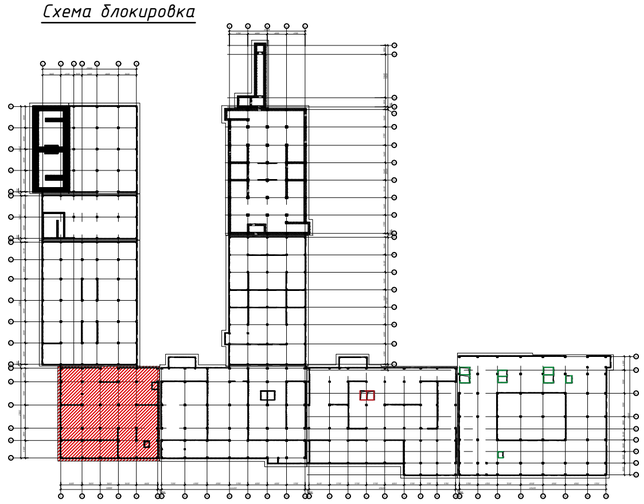

Согласовано:

Архитектор	Ютай М.	
Конструктор	Шолпанбаев Т	
Гл.спец.ОВиК	Алеев Е	
Гл.спец.ВК	Джумагулыева К.	
Гл.спец.ЭП	Нукешов Ж.М.	
Гл.спец.СС	Ивлев С.С.	

Взам. инв. №

Подп. и дата

Инв. № подл.

Рабочий проект разработан в соответствии с действующими на территории Республики Казахстан нормами и правилами, и предусматривает мероприятия, обеспечивающие взрыво-пожаробезопасность и исключающие вредные воздействия на окружающую среду и воздушный бассейн, а также предупреждающие чрезвычайные ситуации природного и техногенного характера

Главный инженер проекта _____ Нурмухамбетов Е.К.

Изм.	Кол.уч	Лист	N док.	Подп.	Дата
ГИП		Нурмухамбетов Е.К			
ГАП		Югай М.			
ГКП		Курал М			
Проверил		Кыдырбай А			
Разраб.		Ауез Б			
Н.контроль		Ешенкулова			

65П-АИП-2024-1-КЖ

Строительство многопрофильной больницы на 250 коек с онкологическим центром и поликлиникой на 350 посещений, по адресу: Медеуский район, г. Алматы

"Блок 1 Секция 1"

Стадия	Лист	Листов
РП	1.1	

Общие данные

АстанаИнжПроект

Формат А2

Ведомость рабочих чертежей основного комплекта (начало)

Лист	Наименование	Примечание
1.1	Общие данные	
1.2	Ведомость чертежей (начало)	
1.3	Ведомость чертежей (продолжение)	
1.4	Ведомость чертежей (конец)	
1.5	Схема располодение котлована	
1.6	Разрез 1 – 1; 2 – 2	
2.1	Схема расположения элементов на отм. -4.350	
2.2	Схема расположения элементов на отм. -0.080	
2.3	Схема расположения элементов на отм. +3.820	
2.4	Схема расположения элементов на отм. +7.720	
2.5	Схема расположения элементов на отм. +11.620	
2.6	Схема расположения элементов на отм. +14.020	
2.7	Разрез 1 – 1	
3.1	Опалубочный чертеж фундамента Фм-1 на отм. -4.350	
3.2	Схема расположения основных арматуры фундамента Фм-1 на отм -4.350	
3.3	Схема расположения дополнительного арматуры фундамента Фм-1 нижней зоны по буквенным осям на отм. -4.350	
3.4	Схема расположения дополнительного арматуры фундамента Фм-1 верхней зоны по буквенным осям на отм. -4.350	
3.5	Схема расположения дополнительного арматуры фундамента Фм-1 нижней зоны по цифровым осям на отм. -4.350	
3.6	Схема расположения дополнительного арматуры фундамента Фм-1 верхней зоны по цифровым осям на отм. -4.350	
3.7	Схема расположения поперечный арматуры фундамента Фм-1 на отм -4.350	
3.8	Спецификация фундамента Фм-1 на отм. -4.350	
3.9	Схема расположения выпусков из фундамента Фм-1 на отм -4.350	
3.10	Спецификация выпусков из фундамента Фм-1 на отм -4.350	
4.1	Колонна Км-1.1	
4.2	Колонна Км-1.2	
4.3	Колонна Км-2.1	
4.4	Колонна Км-2.2	
4.5	Колонна Км-3.1	
4.6	Колонна Км-4.1	
4.7	Колонна Км-4.2	
4.8	Колонна Км-4.3	
4.9	Колонна Км-5.1	

Ведомость рабочих чертежей основного комплекта (продолжение)

Лист	Наименование	Примечание
4.10	Колонна Км-5.2	
4.11	Колонна Км-5.3	
4.12	Колонна Км-6.1	
4.13	Колонна Км-7.1	
4.14	Колонна Км-7.2	
4.15	Колонна Км-8.1	
4.16	Колонна Км-9.1	
4.17	Колонна Км-9.2	
4.18	Колонна Км-10.1	
5.1	Узел стыковки арматуры нахлеста, накладка, анкеровки и Фрагмент обрамления проема	
5.2	Опалубочный чертеж монолитной стены по оси 1с стена См-1 (тол.250мм)	
5.3	Основное армирование монолитной стены по оси 1с стена См-1 (тол.250мм)	
5.4	Разрезы 1 – 1 … 13 – 13.	
5.5	Разрезы 8 – 8 … 11 – 11	
5.6	Спецификация стены См-1	
5.7	Опалубочный чертеж монолитной стены по оси 4с стена См-2 (тол.250мм)	
5.8	Основное армирование монолитной стены по оси 4с стена См-2 (тол.250мм)	
5.9	Разрезы 2 – 2 … 9 – 9.	
5.10	Спецификация стены См-2	
5.11	Опалубочный чертеж монолитной стены по оси 5с стена См-3 (тол.250мм)	
5.12	Основное армирование монолитной стены по оси 5с стена См-3 (тол.250мм)	
5.13	Спецификация стены См3	
5.14	Опалубочный чертеж монолитной стены по оси 6с стена См-4 (тол.250мм)	
5.15	Основное армирование монолитной стены по оси 6с стена См-4 (тол.250мм)	

Взам. инв. №

Подп. и дата

Инв. № подл.

Изм.	Кол.уч	Лист	N док.	Подп.	Дата
ГКП		Курал М			
Проверил		Кыдырбай А			
Разраб.		Ауез Б			
Н.контроль		Ешенкулова			

65П-АИП-2024-1-КЖ

Строительство многопрофильной больницы на 250 коек с онкологическим центром и поликлиникой на 350 посещений, по адресу: Медеуский район, г. Алматы

"Блок 1 Секция 1"

Стадия	Лист	Листов
РП	1.2	

Ведомость чертежей (начало)

АстанаИнжПроект

Формат А3

Ведомость рабочих чертежей основного комплекта (начало)

Лист	Наименование	Примечание
5.16	Разрезы 1 - 1 ... 8 - 8	
5.17	Спецификация стены См 4	
5.18	Опалубочный чертеж монолитной стены по оси Ас стена См-5 (тол.250мм)	
5.19	Основное армирование монолитной стены по оси Ас стена См-5 (тол.250мм)	
5.20	Спецификация монолитной стены по оси Ас стена См-5 (тол.250мм)	
5.21	Свободный лист	
5.22	Схема расположения опалубочный чертеж монолитной стены по оси Бс стена См-6 (тол.250мм)	
5.23	Схема расположения основное армирование монолитной стены по оси Бс стена См-6 (тол.250мм)	
5.24	Спецификация монолитной стены по оси Бс стена См-6 (тол.250мм)	
5.25	Схема расположения опалубочный чертеж монолитной стены по оси Гс стена См-7 (тол.250мм)	
5.26	Схема расположения основное армирование монолитной стены по оси Гс стена См-7 (тол.250мм)	
5.27	Спецификация монолитной стены по оси Гс стена См-7 (тол.250мм)	
5.28	Схема расположения опалубочный чертеж монолитной стены по оси Дс стена См-8 (тол.250мм)	
5.29	Схема расположения основное армирование монолитной стены по оси Дс стена См-8 (тол.250мм)	
5.30	Спецификация монолитной стены по оси Дс стена См-8 (тол.250мм)	
5.31	Опалубочный чертеж монолитной стены по оси Ес стена См-9 (тол.250мм)	
5.32	Опалубочный чертеж монолитной стены по оси Ес стена См-9 (тол.250мм)	
5.33	Опалубочный чертеж монолитной стены по оси Ес стена См-9 (тол.250мм)	
5.34	Спецификация стены См-9 (тол.200мм)	
5.35	Спецификация стены См-10 (тол.200мм)	
5.36	Стены См-10 (тол.200мм)	
5.37	Стена См-11 (тол.200мм)	
5.38	Стена См-11 (тол.200мм)	
5.39	Стена См-12 (тол.200мм)	
5.40	Стена См-12 (тол.200мм)	
5.41	Стена См-13 (тол.200мм)	
5.42	Стена См-14 (тол.200мм)	
5.43	Стена См-15 (тол.200мм)	
5.44	Стена См-16 (тол.200мм)	
5.45	Стена См-16 (тол.200мм)	
5.46	Спецификация монолитной стены по оси 5с стена См-17 (тол.250мм)	

Ведомость рабочих чертежей основного комплекта (продолжение)

Лист	Наименование	Примечание
6.1	Ригель Рм-1	
6.2	Ригель Рм-2	
6.3	Ригель Рм-3	
6.4	Ригель Рм-4	
6.5	Ригель Рм-5	
6.6	Ригель Рм-6	
6.7	Ригель Рм-7	
6,8	Ригель Рм-8	
6,9	Ригель Рм-9	
6,10	Ригель Рм-10	
6,11	Ригель Рм-11	
6,12	Ригель Рм-12	
6,13	Ригель Рм-13	
6,14	Ригель Рм-14	
6,15	Ригель Рм-15	
6,16	Ригель Рм-16	
6,17	Ригель Рм-17	
6,18	Ригель Рм-18	
6,19	Ригель Рм-19	
6,20	Ригель Рм-20	
6,21	Ригель Рм-21	
6,22	Ригель Рм-22	
6,23	Ригель Рм-23	
6,24	Ригель Рм-24	

Взам. инв. №

Подп. и дата

Инв. № подл.

Изм.	Кол.уч	Лист	N док.	Подп.	Дата
ГКП		Курал М			
Проверил		Кыдырбай А			
Разраб.		Ауез Б			
Н.контроль		Ешенкулова			

65П-АИП-2024-1-КЖ

Строительство многопрофильной больницы на 250 коек с онкологическим центром и поликлиникой на 350 посещений, по адресу: Медеуский район, г. Алматы

"Блок 1 Секция 1"

Стадия	Лист	Листов
РП	1.3	

Ведомость чертежей (продолжение)

АстанаИнжПроект

Формат А3

Ведомость рабочих чертежей основного комплекта (начало)

Лист	Наименование	Примечание
6,25	Ригель Рм-25	
6,26	Ригель Рм-26	
6,27	Ригель Рм-27	
6,28	Ригель Рм-28	
6.29	Ригель Рм-29	
6.30	Ригель Рм-30	
7.1	Опалубочный чертеж плиты перекрытия Пм-1 на отм. -0.080	
7.2	Схема расположения основных арматуры плиты перекрытия Пм-1 на отм -0.080	
7.3	Схема расположения дополнительного арматуры плиты перекрытия Пм-1 нижней зоны по буквенным осям на отм -0.080	
7.4	Схема расположения дополнительного арматуры плиты перекрытия Пм-1 верхней зоны по буквенным осям на отм -0.080	
7,5	Схема расположения дополнительного арматуры плиты перекрытия Пм-1 нижней зоны по цифровым осям на отм -0.080	
7,6	Схема расположения дополнительного арматуры плиты перекрытия Пм-1 верхней зоны по цифровым осям на отм -0.080	
7,7	Спецификация плиты перекрытия Пм-1 на отм -0.080	
7,8	Опалубочный чертеж плиты перекрытия Пм-2 на отм.+3.820	
7,9	Схема расположения основных арматуры плиты перекрытия Пм-2 на отм +3.820	
7.10	Схема расположения дополнительного арматуры плиты перекрытия Пм-2 нижней зоны по буквенным осям на отм +3.820	
7.11	Схема расположения дополнительного арматуры плиты перекрытия Пм-2 верхней зоны по буквенным осям на отм +3.820	
7.12	Схема расположения дополнительного арматуры плиты перекрытия Пм-2 нижней зоны по цифровым осям на отм +3.820	
7,13	Схема расположения дополнительного арматуры плиты перекрытия Пм-2 верхней зоны по цифровым осям на отм +3.820	
7,14	Спецификация плиты перекрытия Пм-2 на отм +3.820	
7,15	Опалубочный чертеж плиты перекрытия Пм-3 на отм.+7.720	
7,16	Схема расположения основных арматуры плиты перекрытия Пм-3 на отм +7.720	
7,17	Схема расположения дополнительного арматуры плиты перекрытия Пм-3 нижней зоны по буквенным осям на отм +7.720	
7,18	Схема расположения дополнительного арматуры плиты перекрытия Пм-3 верхней зоны по буквенным осям на отм +7.720	
7,19	Схема расположения дополнительного арматуры плиты перекрытия Пм-3 нижней зоны по цифровым осям на отм +7.720	
7,20	Схема расположения дополнительного арматуры плиты перекрытия Пм-3 верхней зоны по цифровым осям на отм +7.720	
7,21	Спецификация плиты перекрытия Пм-3 на отм +7.720	
7,22	Опалубочный чертеж плиты перекрытия Пм-4 на отм.+11.620	
7,23	Схема расположения основных арматуры плиты перекрытия Пм-4 на отм +11.620	
7,24	Схема расположения дополнительного арматуры плиты перекрытия Пм-4 нижней зоны по буквенным осям на отм +11.620	
7,25	Схема расположения дополнительного арматуры плиты перекрытия Пм-4 верхней зоны по буквенным осям на отм +11.620	

Ведомость рабочих чертежей основного комплекта (продолжение)

Лист	Наименование	Примечание
7,26	Схема расположения дополнительного арматуры плиты перекрытия Пм-4 нижней зоны по цифровым осям на отм +11.620	
7,27	Схема расположения дополнительного арматуры плиты перекрытия Пм-4 верхней зоны по цифровым осям на отм +11.620	
7,28	Спецификация плиты перекрытия Пм-4 на отм +11.620	
7,29	Опалубочный чертеж плиты перекрытия Пм-5 на отм.+14.020	
7.30	Схема расположения основных арматуры плиты перекрытия Пм-5 на отм +14.020	
7.31	Схема расположения дополнительного арматуры плиты перекрытия Пм-5 нижней зоны по буквенным осям на отм +14.020	
7.32	Схема расположения дополнительного арматуры плиты перекрытия Пм-5 верхней зоны по буквенным осям на отм +14.020	
7.33	Схема расположения дополнительного арматуры плиты перекрытия Пм-5 нижней зоны по цифровым осям на отм +14.020	
7,34	Схема расположения дополнительного арматуры плиты перекрытия Пм-5 верхней зоны по цифровым осям на отм +14.020	
7,35	Спецификация плиты перекрытия Пм-5 на отм +14.020	
7,36	Схема расположения выпуск из плиты покрытия на отм. +14.020	
7,37	Опалубочный чертеж плиты перекрытия Пм-6 на отм.+16.520	
7,38	Схема расположения выпуск из плиты покрытия на отм. +16.520	
8,1	Схема опалубочный чертеж парапета ПтМ-1 на отм. +14.020	
8,2	Спецификация схема основное армирование парапета ПтМ-1 на отм. +14.020	
8,3	Спецификация схема основное армирование парапета ПтМ-1 на отм. +16.520	
9,1	Опалубочный чертеж лестницы Л-1 по оси 1с - 2с	
9,2	Лестничный марш Лм-1...Лм-5	
9,3	Спецификация лестницы Л-1 по оси 1с - 2с	

Взам. инв. №

Подп. и дата

Инв. № подл.

Изм.	Кол.уч	Лист	N док.	Подп.	Дата
ГКП		Курал М			
Проверил		Кыдырбай А			
Разраб.		Ауез Б			
Н.контроль		Ешенкулова			

65П-АИП-2024-1-КЖ

Строительство многопрофильной больницы на 250 коек с онкологическим центром и поликлиникой на 350 посещений, по адресу: Медеуский район, г. Алматы

"Блок 1 Секция 1"

Стадия	Лист	Листов
РП	1.4	

Ведомость чертежей (конец)

АстанаИнжПроект

Формат А3