
Схема расположения элементов на отм. -4.350

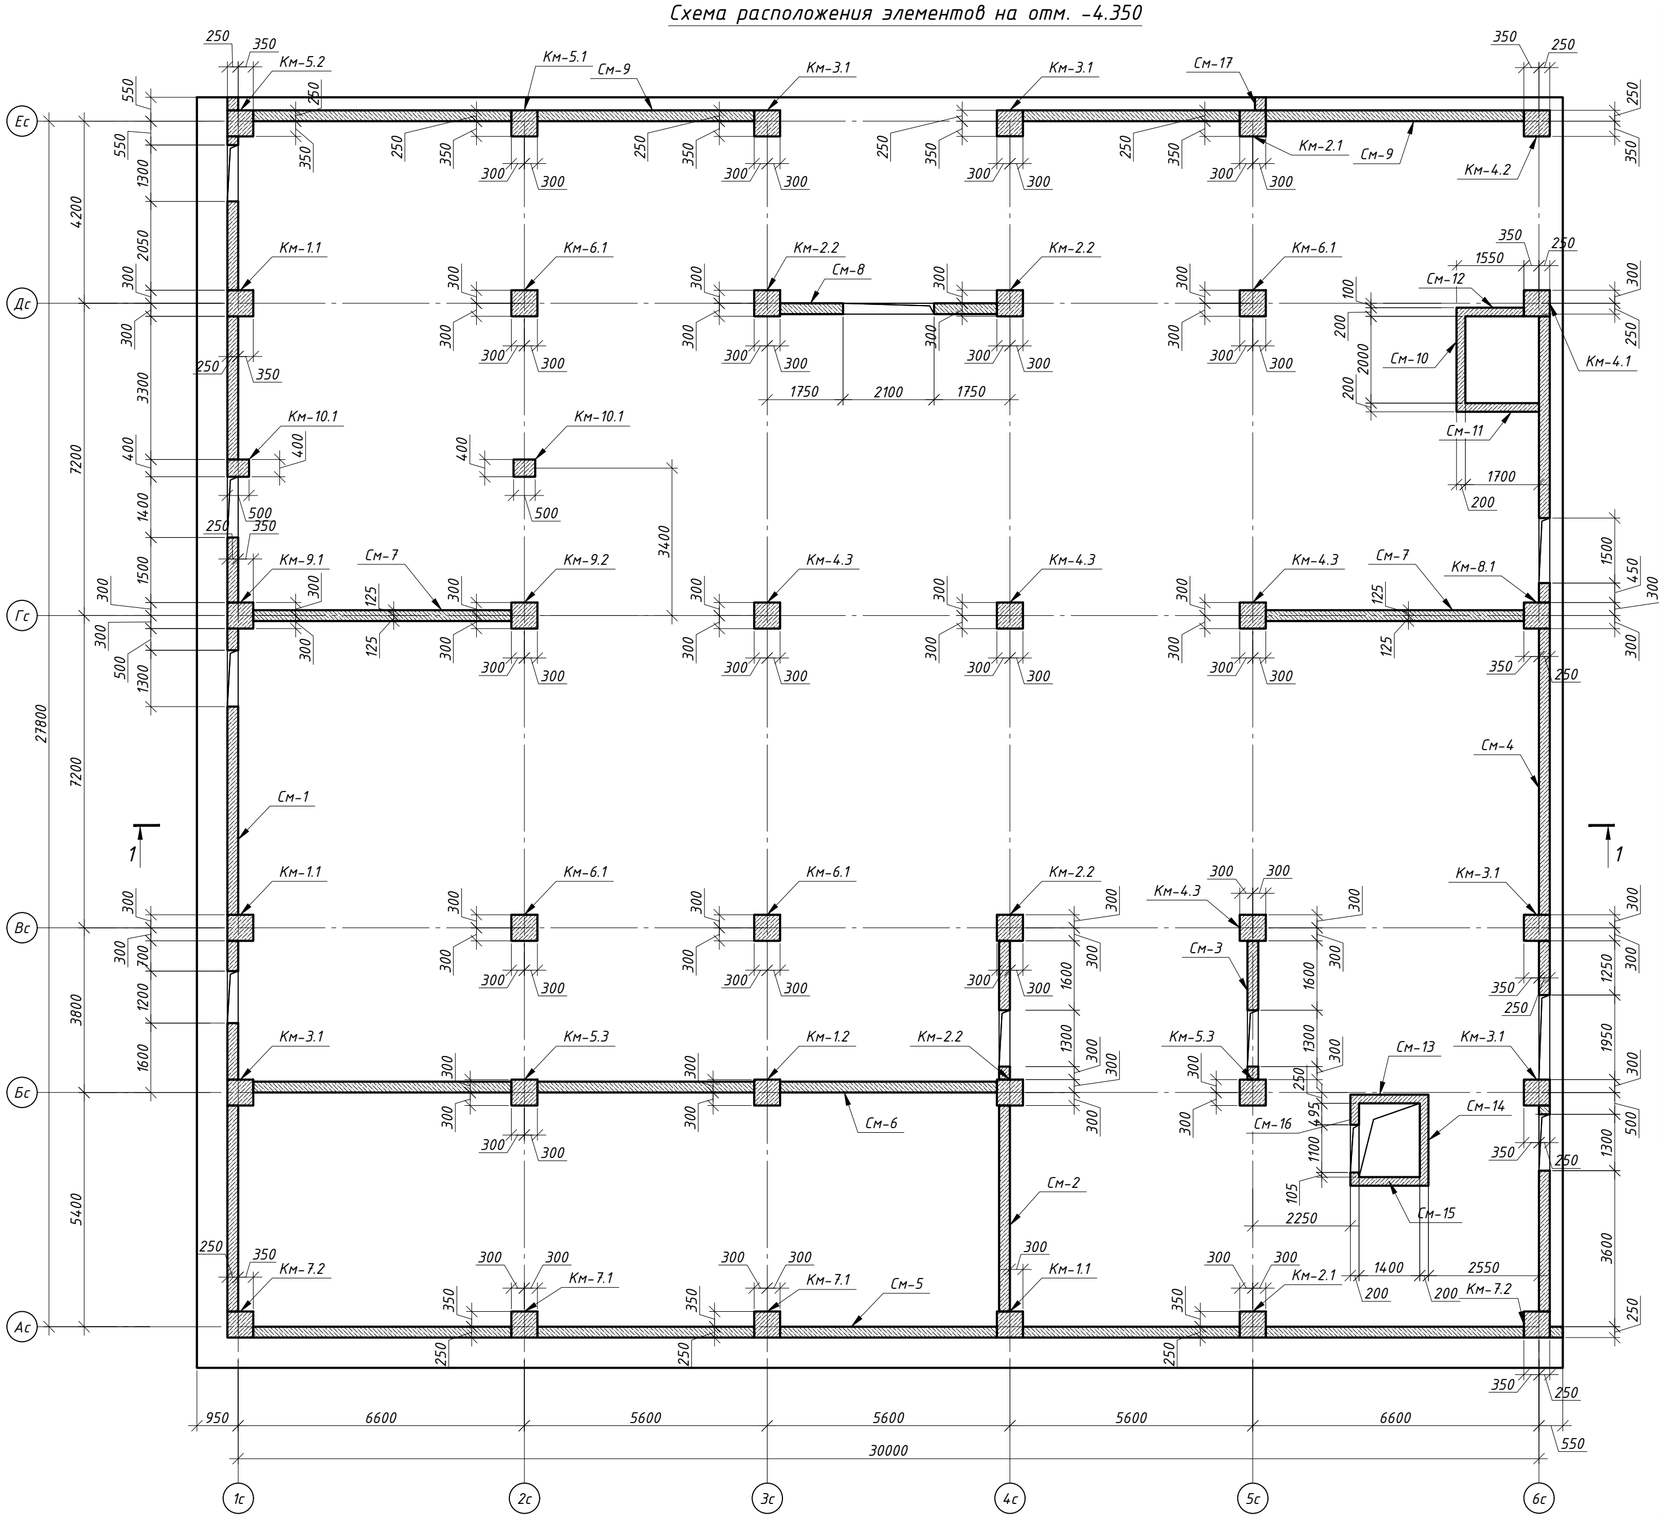

Спецификация элементов каркаса на отм.-4.350


Поз.	Обозначение	Наименование	Кол.	Масса ед.кг	Примечание
		Фундамент:			
Фм-1	лист 3.1	Фундамент Фм-1	1		
		Колонна:			
Км-1.1	лист 4.1	Колонна Км-1	3		
Км-1.2	лист 4.2	Колонна Км-1.2	1		
Км-2.1	лист 4.3	Колонна Км-2.1	2		
Км-2.2	лист 4.4	Колонна Км-2.2	4		
Км-3.1	лист 4.5	Колонна Км-3.1	5		
Км-4.1	лист 4.6	Колонна Км-4.1	1		
Км-4.2	лист 4.7	Колонна Км-4.2	1		
Км-4.3	лист 4.8	Колонна Км-4.3	4		
Км-5.1	лист 4.9	Колонна Км-5.1	1		
Км-5.2	лист 4.10	Колонна Км-5.2	1		
Км-5.3	лист 4.11	Колонна Км-5.3	2		
Км-6.1	лист 4.12	Колонна Км-6.1	4		
Км-7.1	лист 4.13	Колонна Км-7.1	2		
Км-7.2	лист 4.14	Колонна Км-7.2	2		
Км-8.1	лист 4.15	Колонна Км-8.1	1		
Км-9.1	лист 4.16	Колонна Км-9.1	1		
Км-9.2	лист 4.17	Колонна Км-9.2	1		
Км-10.1	лист 4.18	Колонна Км-10.1	2		
		Стена:			
См-1	лист 5.2	Стена См-1	1		
См-2	лист 5.7	Стена См-2	1		
См-3	лист 5.11	Стена См-3	1		
См-4	лист 5.14	Стена См-4	1		
См-5	лист 5.18	Стена См-5	1		
См-6	лист 5.22	Стена См-6	1		
См-7	лист 5.25	Стена См-7	1		
См-8	лист 5.28	Стена См-8	1		
См-9	лист 5.31	Стена См-9	1		
См-10	лист 5.36	Стена См-10	1		
См-11	лист 5.37	Стена См-11	1		
См-12	лист 5.39	Стена См-12	1		
См-13	лист 5.41	Стена См-13	1		
См-14	лист 5.42	Стена См-14	1		
См-15	лист 5.43	Стена См-15	1		
См-16	лист 5.44	Стена См-16	1		
См-17	лист 5.46	Стена См-17	1		

1. Общие указания см. л. – 1.
2. Данный лист читать совместно с л. 2.1 ... 2.8.

Изм.	Кол.уч.	Лист	N док.	Подп.	Дата	65П-АИП-2024-1-КЖ		
						Строительство многопрофильной больницы на 250 коек с онкологическим центром и поликлиникой на 350 посещений, по адресу: Медеуский район, г. Алматы		
						Блок 1 Секция1	Стадия: РП	Лист: 2.1
ГКП		Курал М						
Проверил		Кыдырбай А				Схема расположения элементов на отм. -4.350	АстанаИнжПроект	
Разраб.		Ауез Б						
Н.контроль		Ешенкулова						

Формат А2

Схема расположения элементов на отм. -0.080

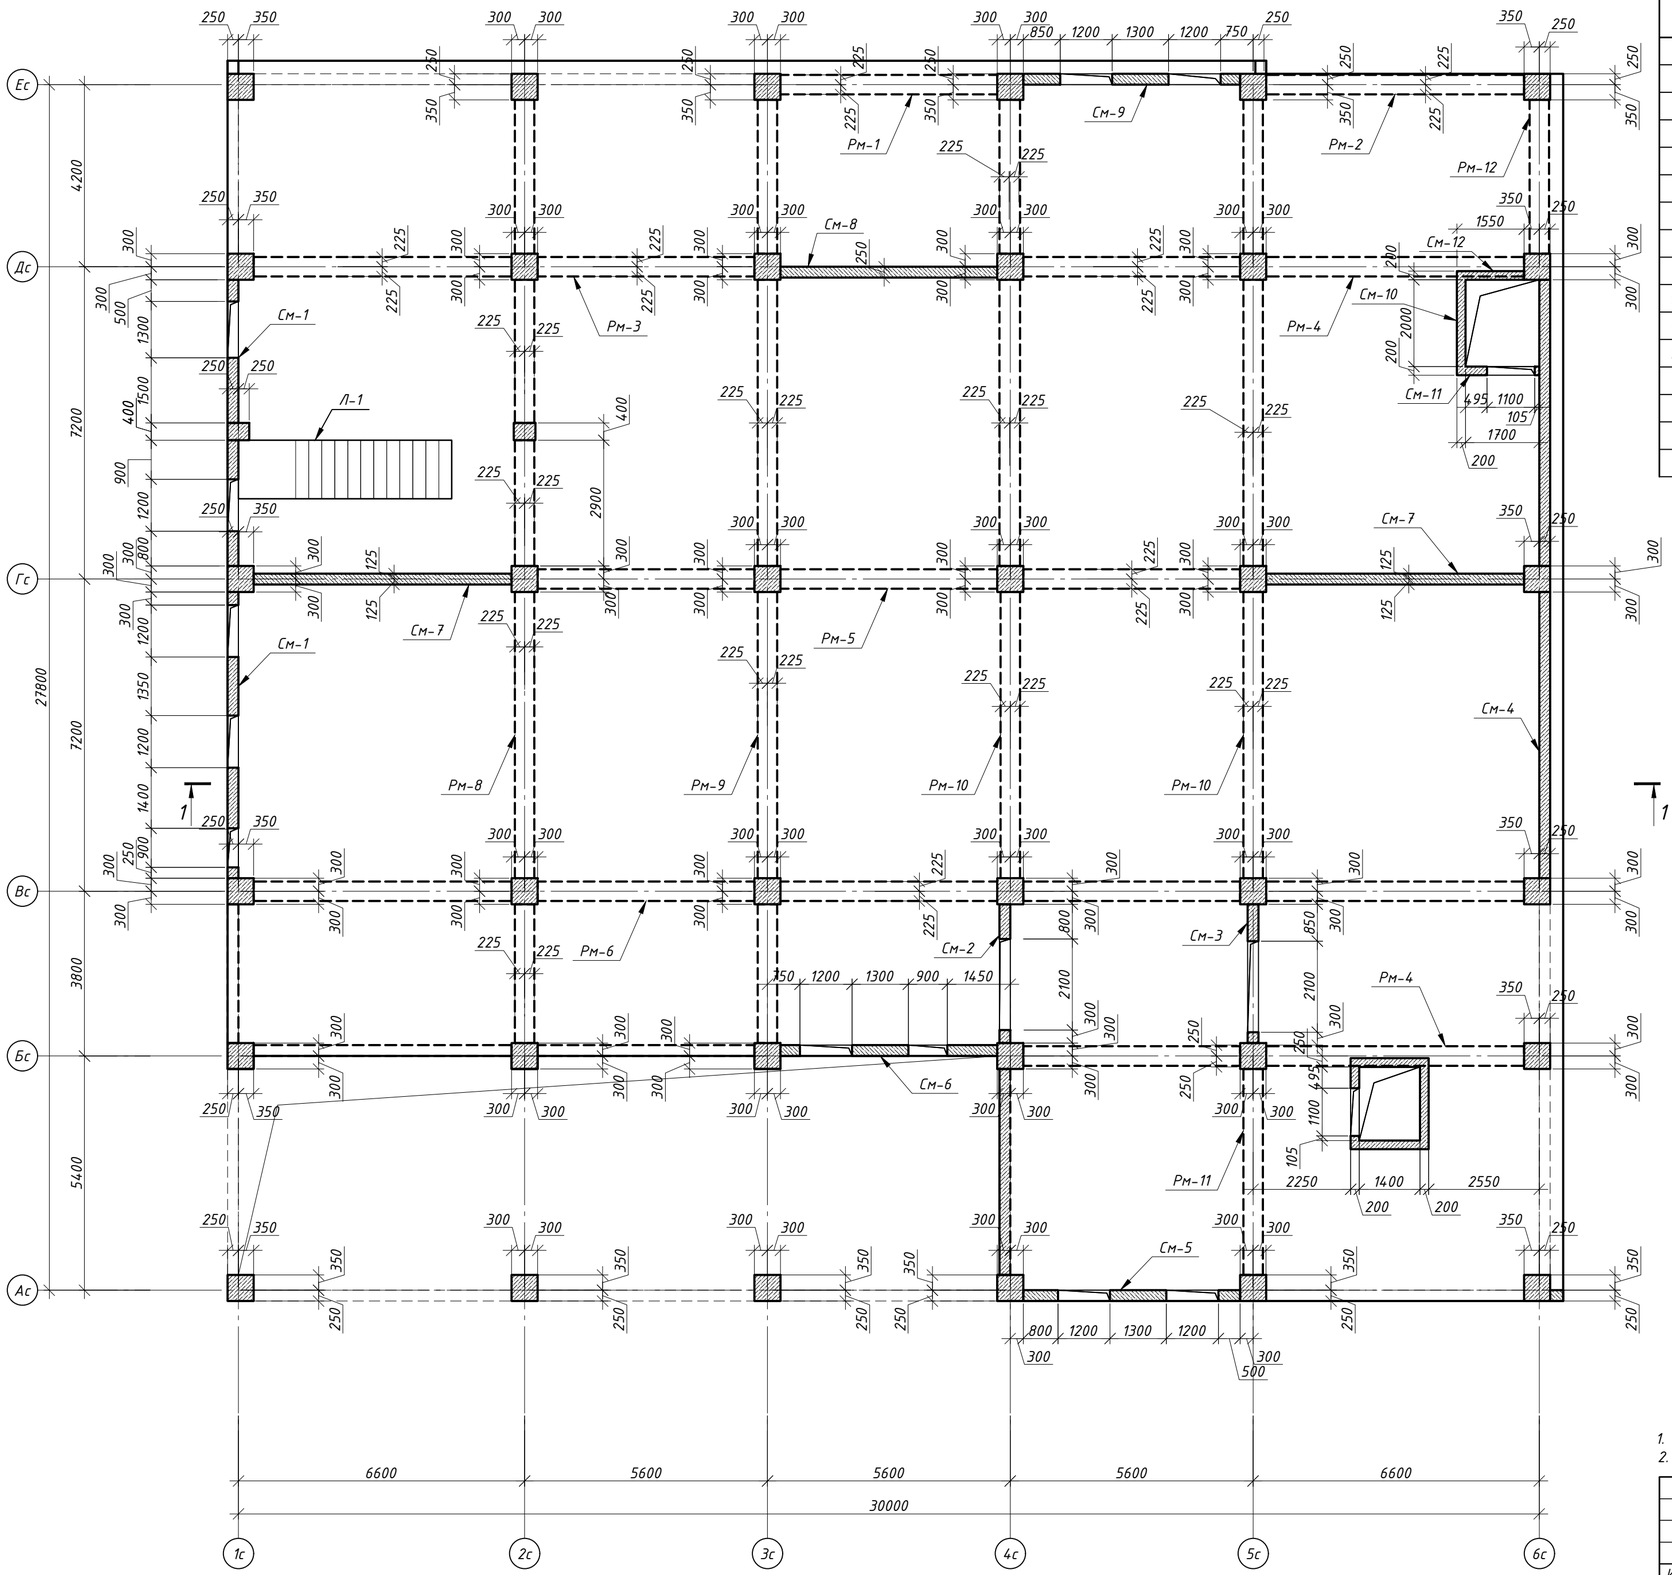

Спецификация элементов каркаса на отм.-0.080


Поз.	Обозначение	Наименование	Кол.	Масса ед.кг	Примечание
		Ригель:			
Рм-1	лист 6.1	Ригель Рм-1	1		
Рм-2	лист 6.2	Ригель Рм-2	1		
Рм-3	лист 6.3	Ригель Рм-3	1		
Рм-4	лист 6.4	Ригель Рм-4	2		
Рм-5	лист 6.5	Ригель Рм-5	1		
Рм-6	лист 6.6	Ригель Рм-6	1		
Рм-8	лист 6.8	Ригель Рм-8	1		
Рм-9	лист 6.9	Ригель Рм-9	1		
Рм-10	лист 6.10	Ригель Рм-10	2		
Рм-11	лист 6.11	Ригель Рм-11	1		
Рм-12	лист 6.12	Ригель Рм-12	1		
		Плита:			
Пм-1	лист 7.1	Плита Пм-1	1		
		Лестница:			
Л-1	лист 9.1	Лестница Л-1	1		

1. Общие указания см. л. - 1.
2. Данный лист читать совместно с л. 2.1 ... 2.8.

Изм.	Кол.уч.	Лист	N док.	Подп.	Дата	65П-АИП-2024-1-КЖ			
						Строительство многопрофильной больницы на 250 коек с онкологическим центром и поликлиникой на 350 посещений, по адресу: Медеуский район, г. Алматы			
						Блок 1 Секция1	Стадия	Лист	Листов
							РП	2.2	
ГКП		Курал М				Схема расположения элементов на отм. -0.080	АстанаИнжПроект		
Проверил		Кыдырбай А							
Разраб.		Ауез Б							
Н.контроль		Ешенкулова							

Формат А2

Схема расположения элементов на отм. +3.820

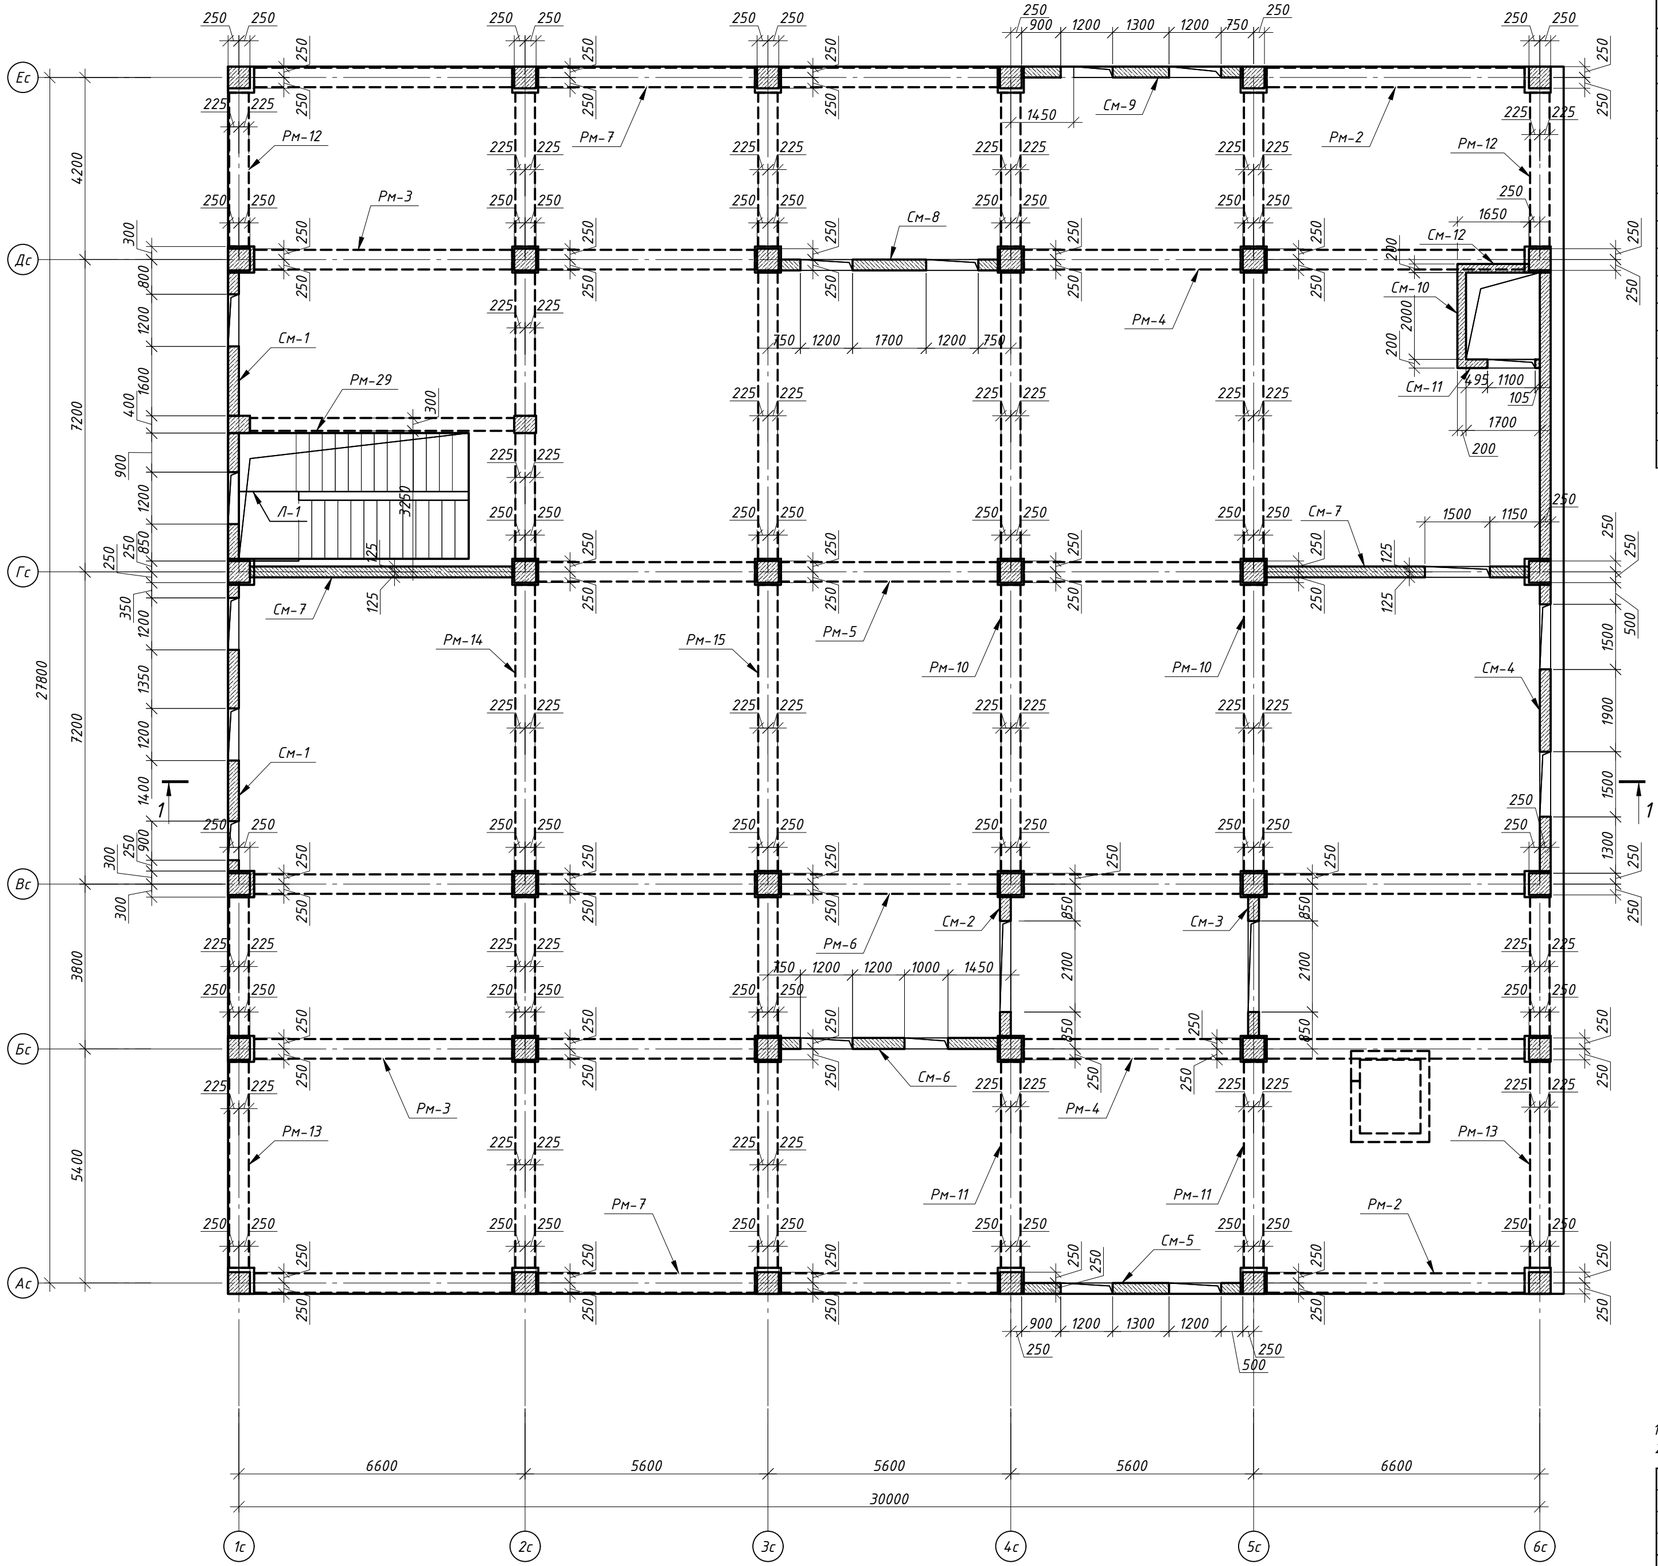

Спецификация элементов каркаса на отм.+3.220


Поз.	Обозначение	Наименование	Кол.	Масса ед.кг	Примечание
		Ригель:			
Рм-2	лист 6.2	Ригель Рм-2	2		
Рм-3	лист 6.3	Ригель Рм-3	2		
Рм-4	лист 6.4	Ригель Рм-4	2		
Рм-5	лист 6.5	Ригель Рм-5	1		
Рм-6	лист 6.6	Ригель Рм-6	1		
Рм-7	лист 6.6	Ригель Рм-7	2		
Рм-10	лист 6.10	Ригель Рм-10	2		
Рм-11	лист 6.11	Ригель Рм-11	2		
Рм-12	лист 6.12	Ригель Рм-12	2		
Рм-13	лист 6.13	Ригель Рм-13	2		
Рм-14	лист 6.14	Ригель Рм-14	1		
Рм-15	лист 6.15	Ригель Рм-15	1		
Рм-29	лист 6.29	Ригель Рм-29	1		
		Плита:			
Пм-2	лист 7.8	Плита Пм-2	1		

1. Общие указания см. л. – 1.
2. Данный лист читать совместно с л. 2.1 ... 2.8.

						65П-АИП-2024-1-КЖ
						Строительство многопрофильной больницы на 250 коек с онкологическим центром и поликлиникой на 350 посещений, по адресу: Медеуский район, г. Алматы
Изм.	Кол.уч	Лист	N док.	Подп.	Дата	
						Блок 1 Секция1
ГКП		Курал М				Стадия: РП; Лист: 2.3; Листов:
Проверил		Кыдырбай А				
Разраб.		Ауез Б				Схема расположения элементов на отм. +3.820
Н.контроль		Ешенкулова				АстанаИнжПроект

Формат А2

Схема расположения элементов на отм. +7.720

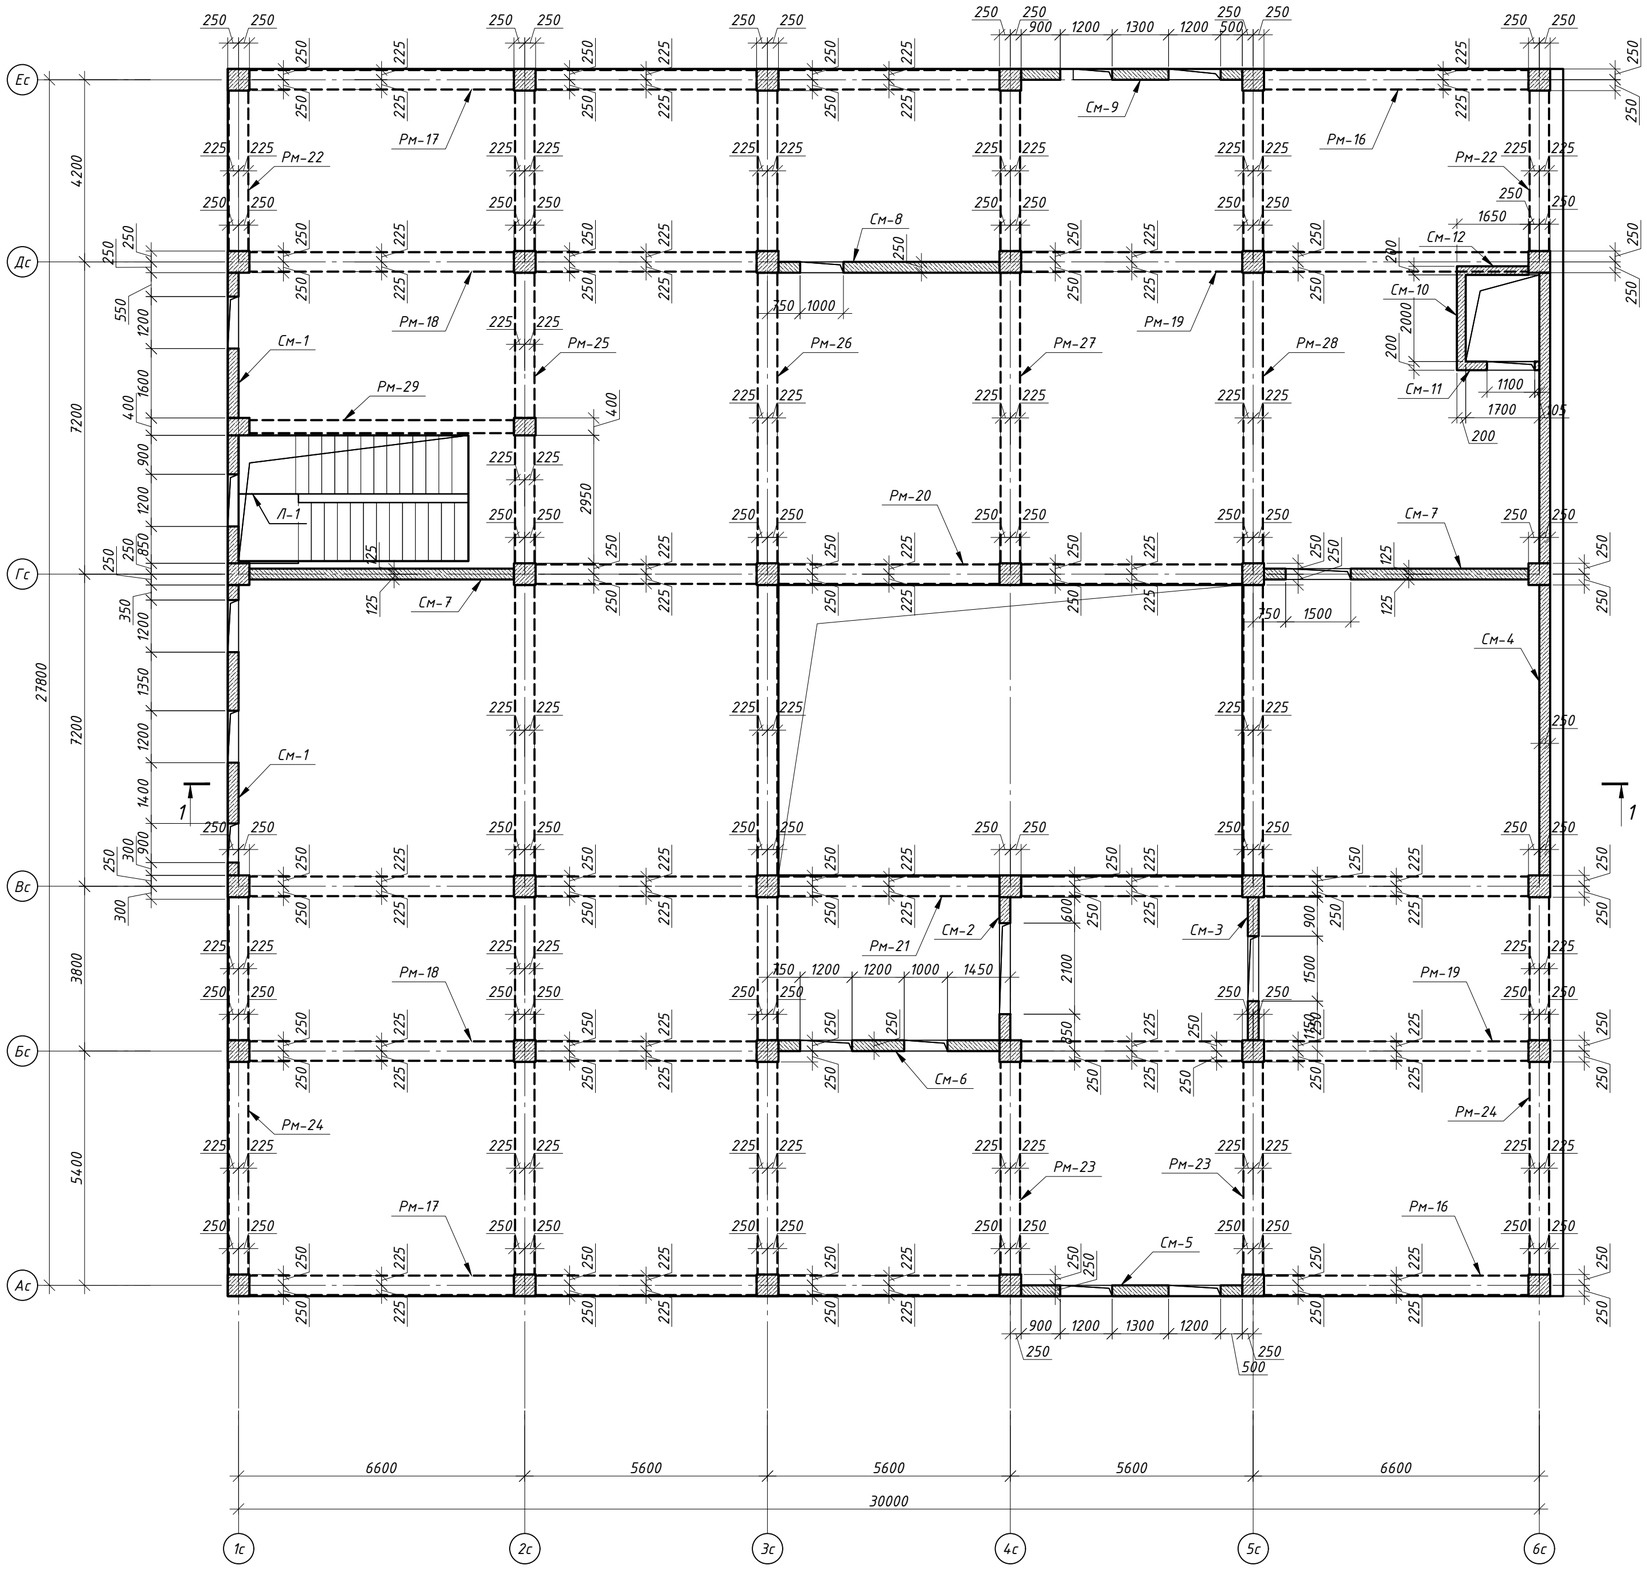

Спецификация элементов каркаса на отм.+3.720


Поз.	Обозначение	Наименование	Кол.	Масса ед.кг	Примечание
		Ригель:			
Рм-16	лист 6.16	Ригель Рм-16	2		
Рм-17	лист 6.17	Ригель Рм-17	2		
Рм-18	лист 6.18	Ригель Рм-18	2		
Рм-19	лист 6.19	Ригель Рм-19	2		
Рм-20	лист 6.2	Ригель Рм-20	1		
Рм-21	лист 6.21	Ригель Рм-21	1		
Рм-22	лист 6.22	Ригель Рм-22	2		
Рм-23	лист 6.23	Ригель Рм-23	2		
Рм-24	лист 6.24	Ригель Рм-24	4		
Рм-25	лист 6.25	Ригель Рм-25	1		
Рм-26	лист 6.26	Ригель Рм-26	1		
Рм-27	лист 6.27	Ригель Рм-27	1		
Рм-28	лист 6.28	Ригель Рм-28	1		
Рм-29	лист 6.29	Ригель Рм-29	1		
		Плита:			
Пм-3	лист 7.15	Плита Пм-3	1		

1. Общие указания см. л. – 1.
2. Данный лист читать совместно с л. 2.1 ... 2.8.

						65П-АИП-2024-1-КЖ
						Строительство многопрофильной больницы на 250 коек с онкологическим центром и поликлиникой на 350 посещений, по адресу: Медеуский район, г. Алматы
Изм.	Кол.уч	Лист	N док.	Подп.	Дата	
						Блок 1 Секция1
ГКП		Курал М				Стадия: РП; Лист: 2.4; Листов:
Проверил		Кыдырбай А				
Разраб.		Ауез Б				Схема расположения элементов на отм. +7.720
Н.контроль		Ешенкулова				АстанаИнжПроект

Формат А2

Схема расположения элементов на отм. +11.620

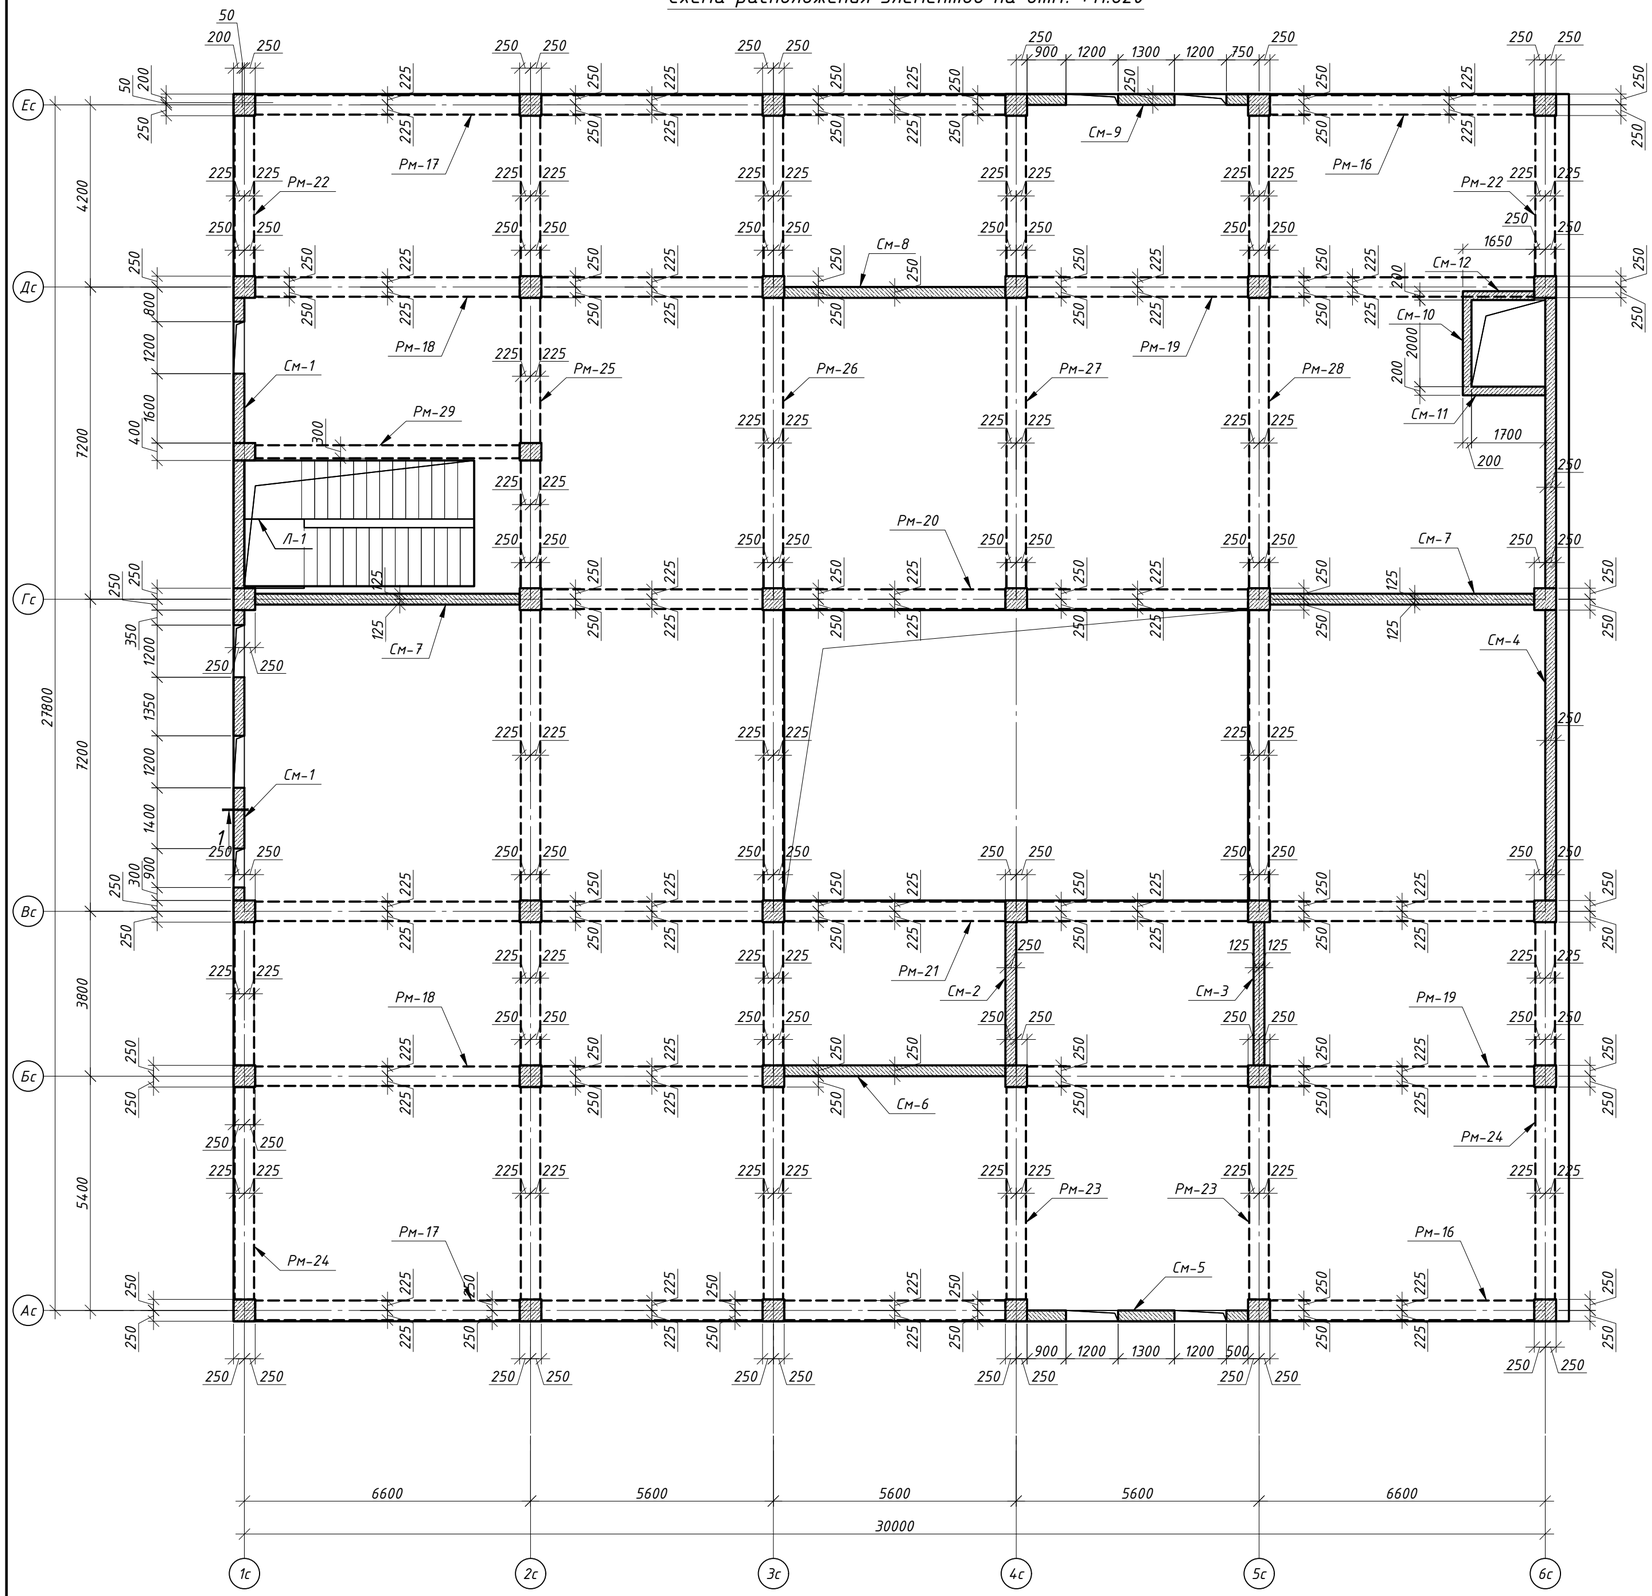

Спецификация элементов каркаса на отм.+11.620

Поз.	Обозначение	Наименование	Кол.	Масса ед.кг	Примечание
		Ригель:			
Рм-16	лист 6.16	Ригель Рм-16	2		
Рм-17	лист 6.17	Ригель Рм-17	2		
Рм-18	лист 6.18	Ригель Рм-18	2		
Рм-19	лист 6.19	Ригель Рм-19	2		
Рм-20	лист 6.2	Ригель Рм-20	1		
Рм-21	лист 6.21	Ригель Рм-21	1		
Рм-22	лист 6.22	Ригель Рм-22	2		
Рм-23	лист 6.23	Ригель Рм-23	2		
Рм-24	лист 6.24	Ригель Рм-24	4		
Рм-25	лист 6.25	Ригель Рм-25	1		
Рм-26	лист 6.26	Ригель Рм-26	1		
Рм-27	лист 6.27	Ригель Рм-27	1		
Рм-28	лист 6.28	Ригель Рм-28	1		
Рм-29	лист 6.29	Ригель Рм-29	1		
		Плита:			
Пм-4	лист 7.22	Плита Пм-4	1		

1. Общие указания см. л. – 1.
2. Данный лист читать совместно с л. 2.1 ... 2.8.

Изм.	Кол.уч.	Лист	N док.	Подп.	Дата	65П-АИП-2024-1-КЖ		
						Строительство многопрофильной больницы на 250 коек с онкологическим центром и поликлиникой на 350 посещений, по адресу: Медеуский район, г. Алматы		
						Блок 1 Секция1	Стадия: РП	Лист: 2.5	Листов:
ГКП		Курал М							
Проверил		Кыдырбай А				Схема расположения элементов на отм. +11.620	АстанаИнжПроект		
Разраб.		Ауез Б							
Н.контроль		Ешенкулова							

Формат А2

Схема расположения элементов на отм. +14.020


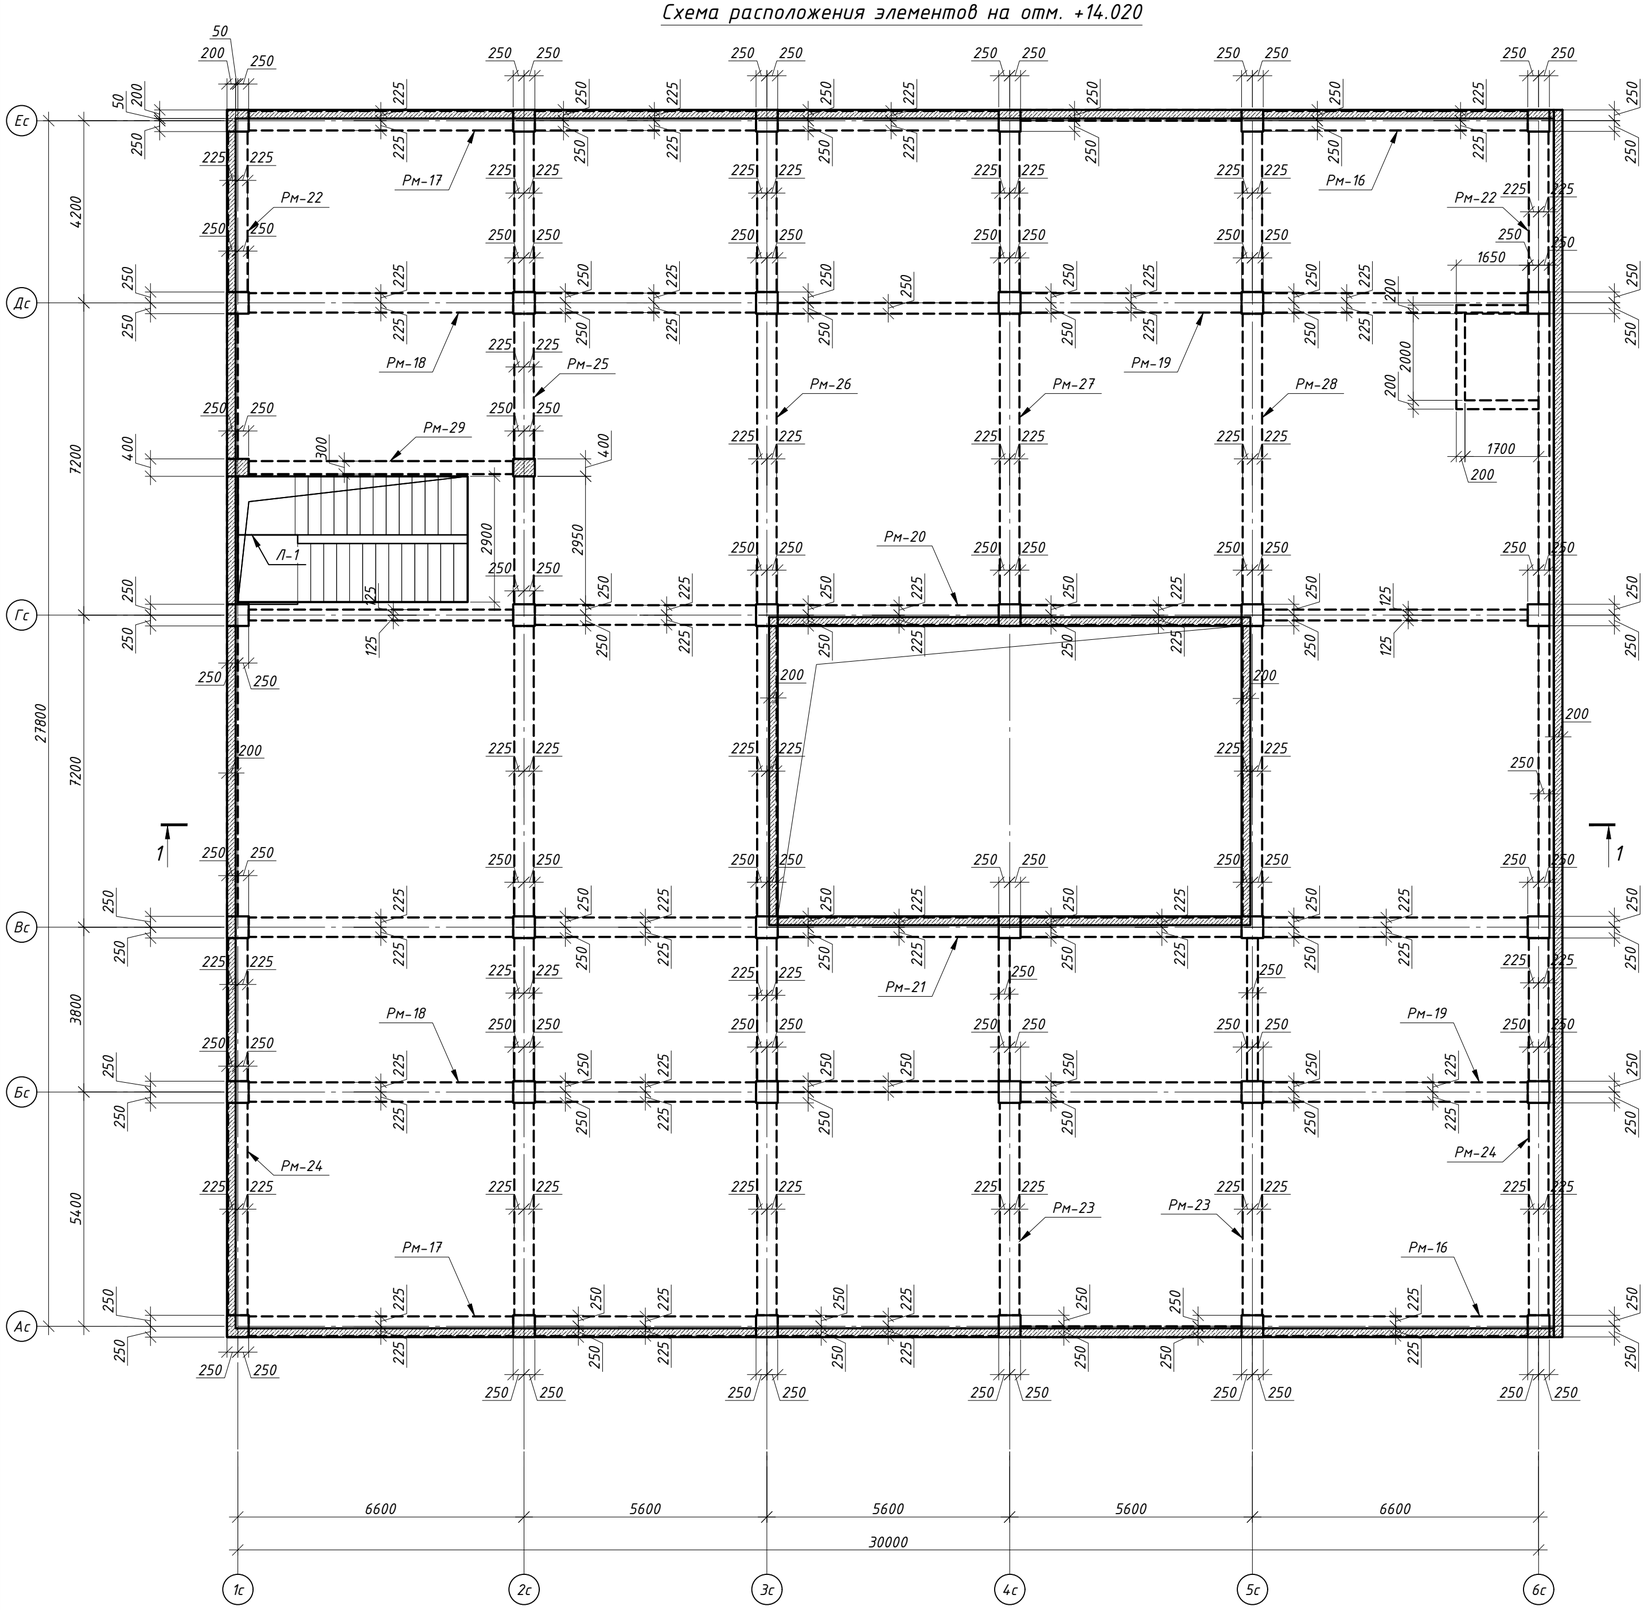


Схема расположения элементов на отм. +16.520

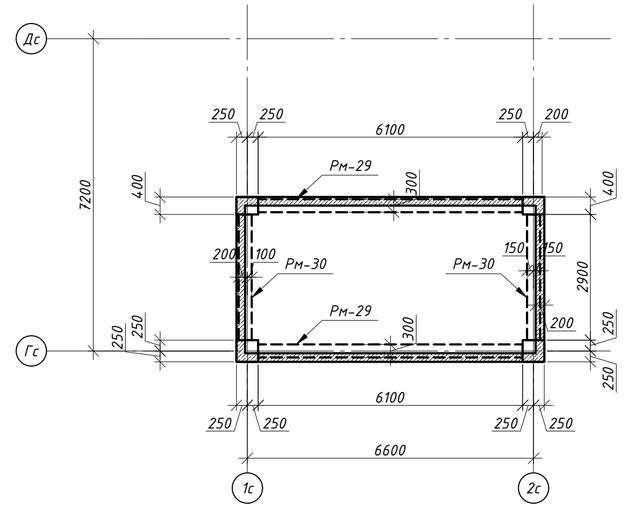

Спецификация элементов каркаса на отм.+14.020

Поз.	Обозначение	Наименование	Кол.	Масса ед.кг	Примечание
		Ригель:			
Рм-16	лист 6.16	Ригель Рм-16	2		
Рм-17	лист 6.17	Ригель Рм-17	2		
Рм-18	лист 6.18	Ригель Рм-18	2		
Рм-19	лист 6.19	Ригель Рм-19	2		
Рм-20	лист 6.2	Ригель Рм-20	1		
Рм-21	лист 6.21	Ригель Рм-21	1		
Рм-22	лист 6.22	Ригель Рм-22	2		
Рм-23	лист 6.23	Ригель Рм-23	2		
Рм-24	лист 6.24	Ригель Рм-24	4		
Рм-25	лист 6.25	Ригель Рм-25	1		
Рм-26	лист 6.26	Ригель Рм-26	1		
Рм-27	лист 6.27	Ригель Рм-27	1		
Рм-28	лист 6.28	Ригель Рм-28	1		
Рм-29	лист 6.29	Ригель Рм-29	1		
		Плита:			
Пм-5	лист 7.29	Плита Пм-5	1		
		Парапет:			
ПтМ-4	лист 8.1	Парапет ПтМ-1	1		

Спецификация элементов каркаса на отм.+16.220


Поз.	Обозначение	Наименование	Кол.	Масса ед.кг	Примечание
		Ригель:			
Рм-28	лист 6.28	Ригель Рм-28	2		
Рм-29	лист 6.29	Ригель Рм-29	2		
		Плита:			
Пм-6	лист 7.37	Плита Пм-6	1		
		Парапет:			
ПтМ-2	лист 8.3	Парапет ПтМ-2	1		

1. Общие указания см. л. – 1.
2. Данный лист читать совместно с л. 2.1 ... 2.8.

Изм.	Кол.уч.	Лист	N док.	Подп.	Дата	65П-АИП-2024-1-КЖ		
						Строительство многопрофильной больницы на 250 коек с онкологическим центром и поликлиникой на 350 посещений, по адресу: Медеуский район, г. Алматы		
						Блок 1 Секция1	Стадия: РП	Лист: 2.6
ГКП		Курал М						Листов:
Проверил		Кыдырбай А				Схема расположения элементов на отм. +14.020	АстанаИнжПроект	
Разраб.		Ауез Б						
Н.контроль		Ешенкулова						

Формат А2

Разрез 1 - 1

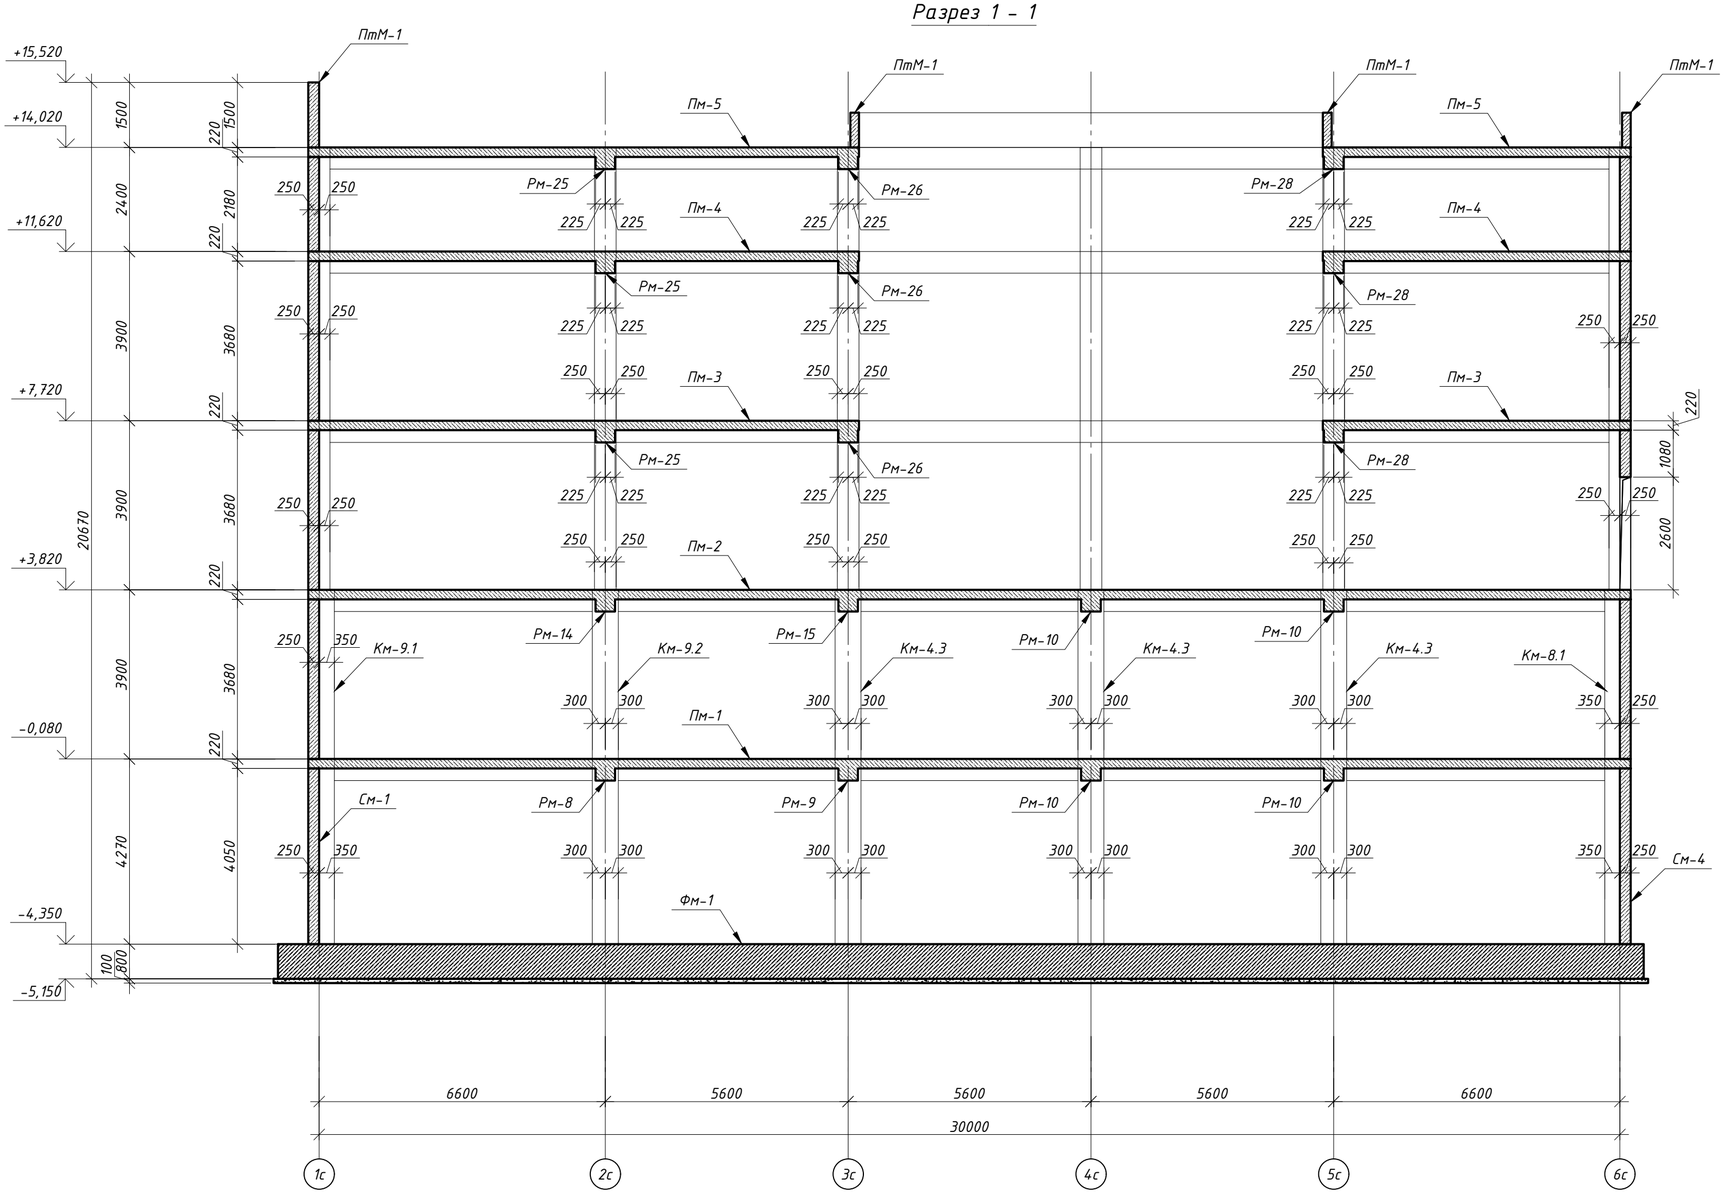

1. Общие указания см. л. - 1.
2. Данный лист читать совместно с л. 2.1 ... 2.8.

						65П-АИП-2024-1-КЖ	
						Строительство многопрофильной больницы на 250 коек с онкологическим центром и поликлиникой на 350 посещений, по адресу: Медеуский район, г. Алматы	
Изм.	Кол.уч	Лист	N док.	Подп.	Дата		
						Блок 1 Секция1	Стадия: РП; Лист: 2.7; Листов:
ГКП		Курал М					
Проверил		Кыдырбай А				Разрез 1 - 1	АстанаИнжПроект
Разраб.		Ауез Б					
Н.контроль		Ешенкулова					

Формат А2