


Опалубочный чертеж фундамента Фм-1 на отм. -4.350

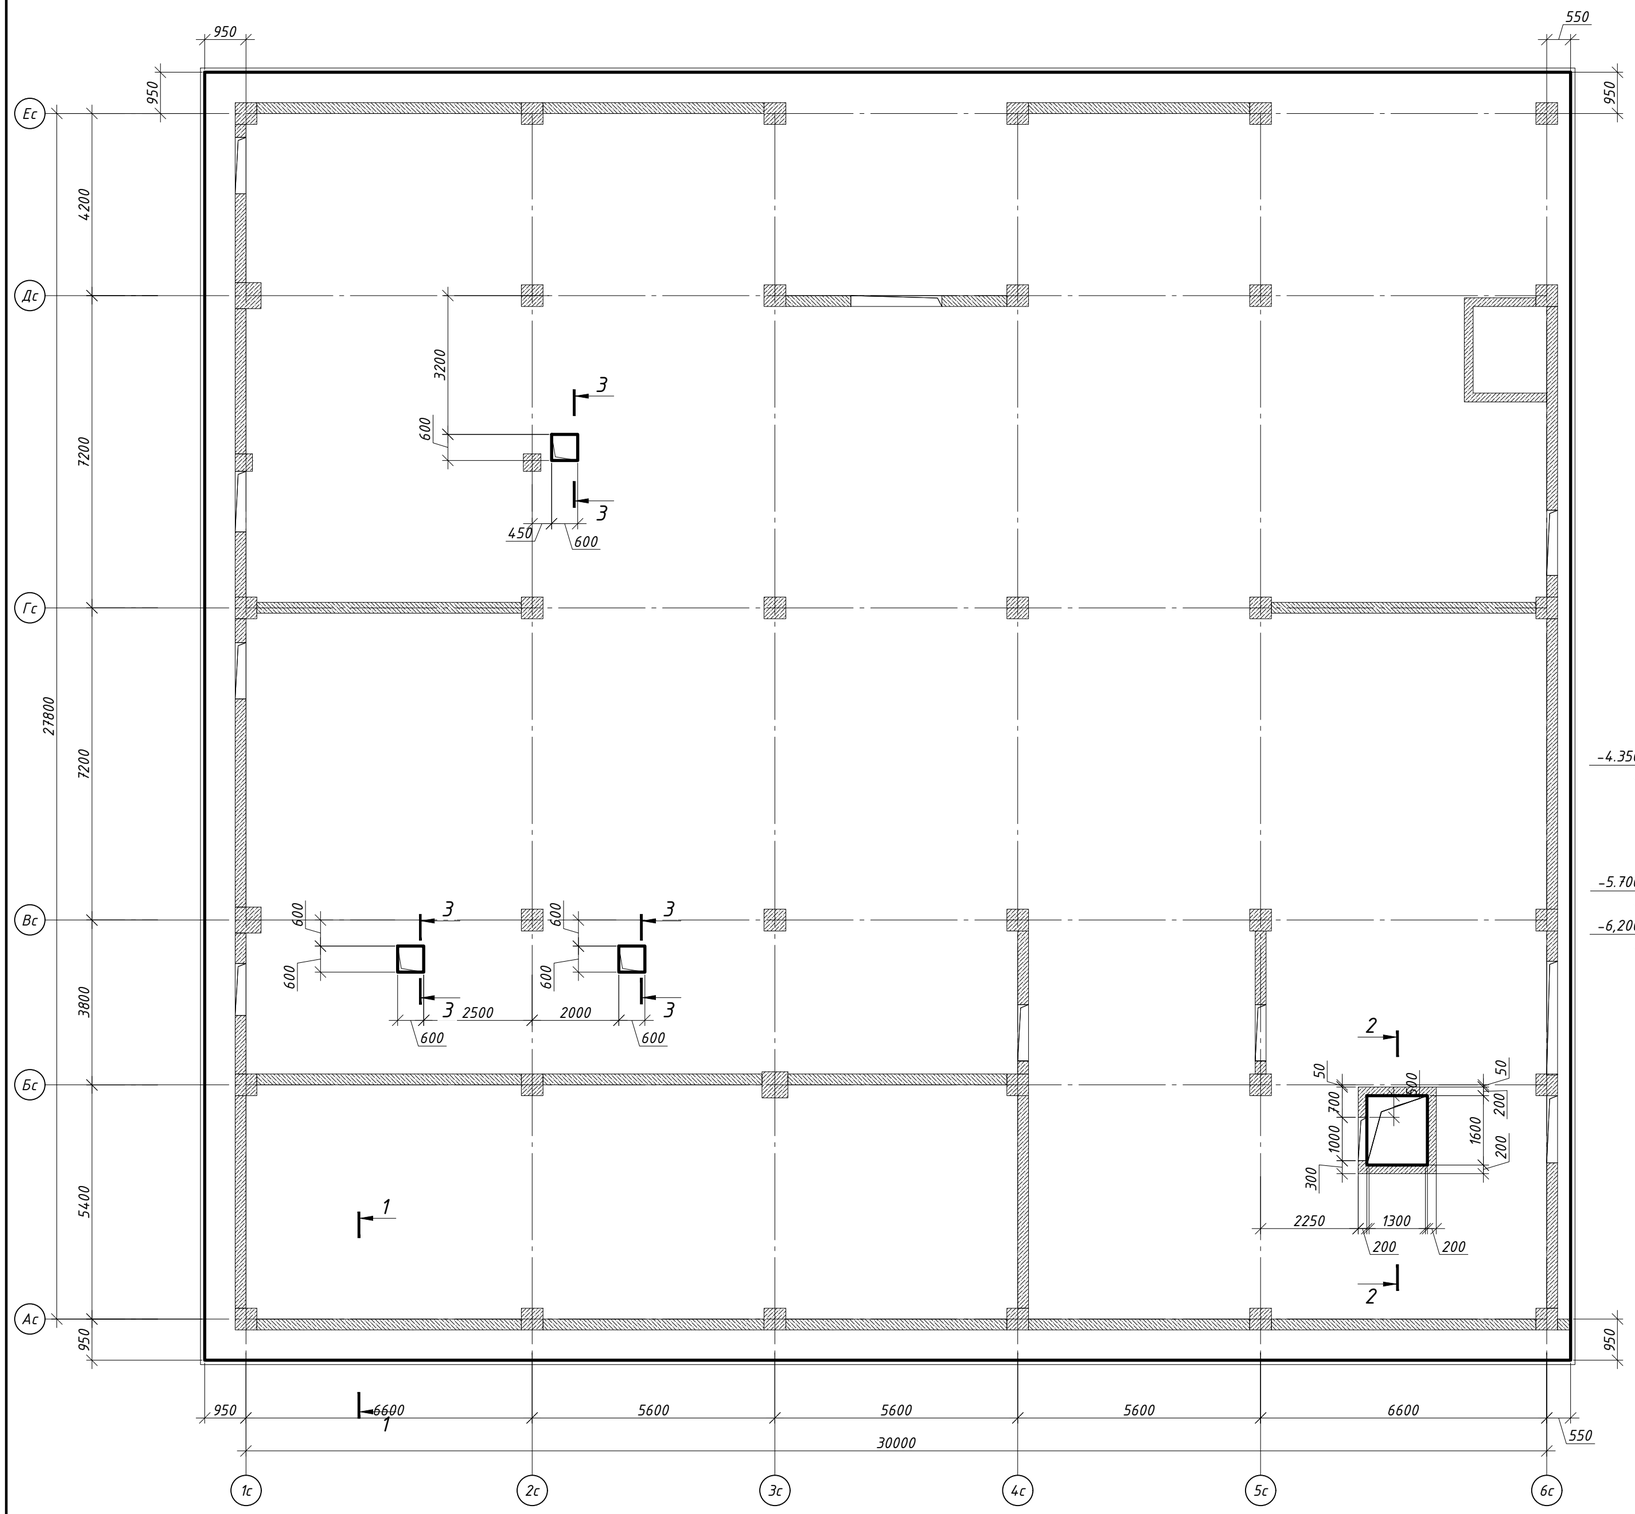


Разрез 1-1 (опалубка)
М 1:50

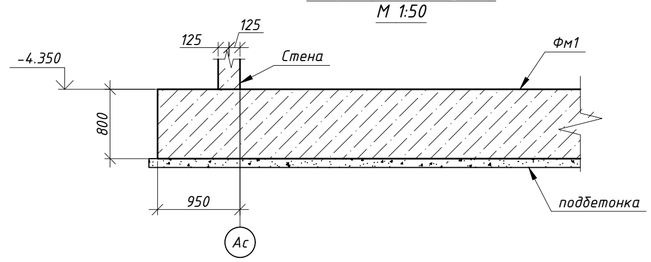

Разрез 3 - 3 (опалубка)

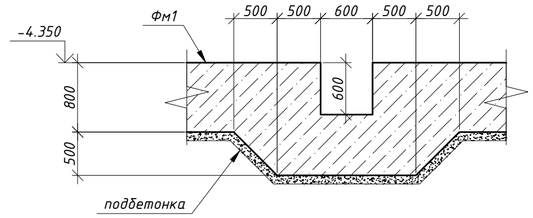


Разрез 2 - 2 (Опалубка)
М 1:50

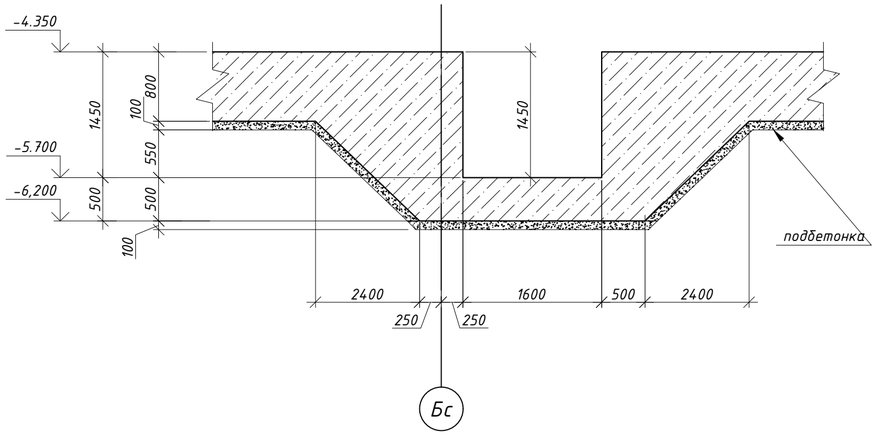


						65П-АИП-2024-1-КЖ	
						Строительство многопрофильной больницы на 250 коек с онкологическим центром и поликлиникой на 350 посещений, по адресу: Медеуский район, г. Алматы	
Изм.	Кол.уч	Лист	N док.	Подп.	Дата		
						"Блок 1 Секция 1"	Стадия: РП; Лист: 3.1; Листов:
ГКП		Курал М					
Проверил		Кыдырбай А				Опалубочный чертеж фундамента Фм-1 на отм. -4.350	АстанаИнжПроект
Разраб.		Ауез Б					
Н.контроль		Ешенкулова					

Формат А2


Схема расположения основных арматуры фундамента Фм-1 на отм -4.350

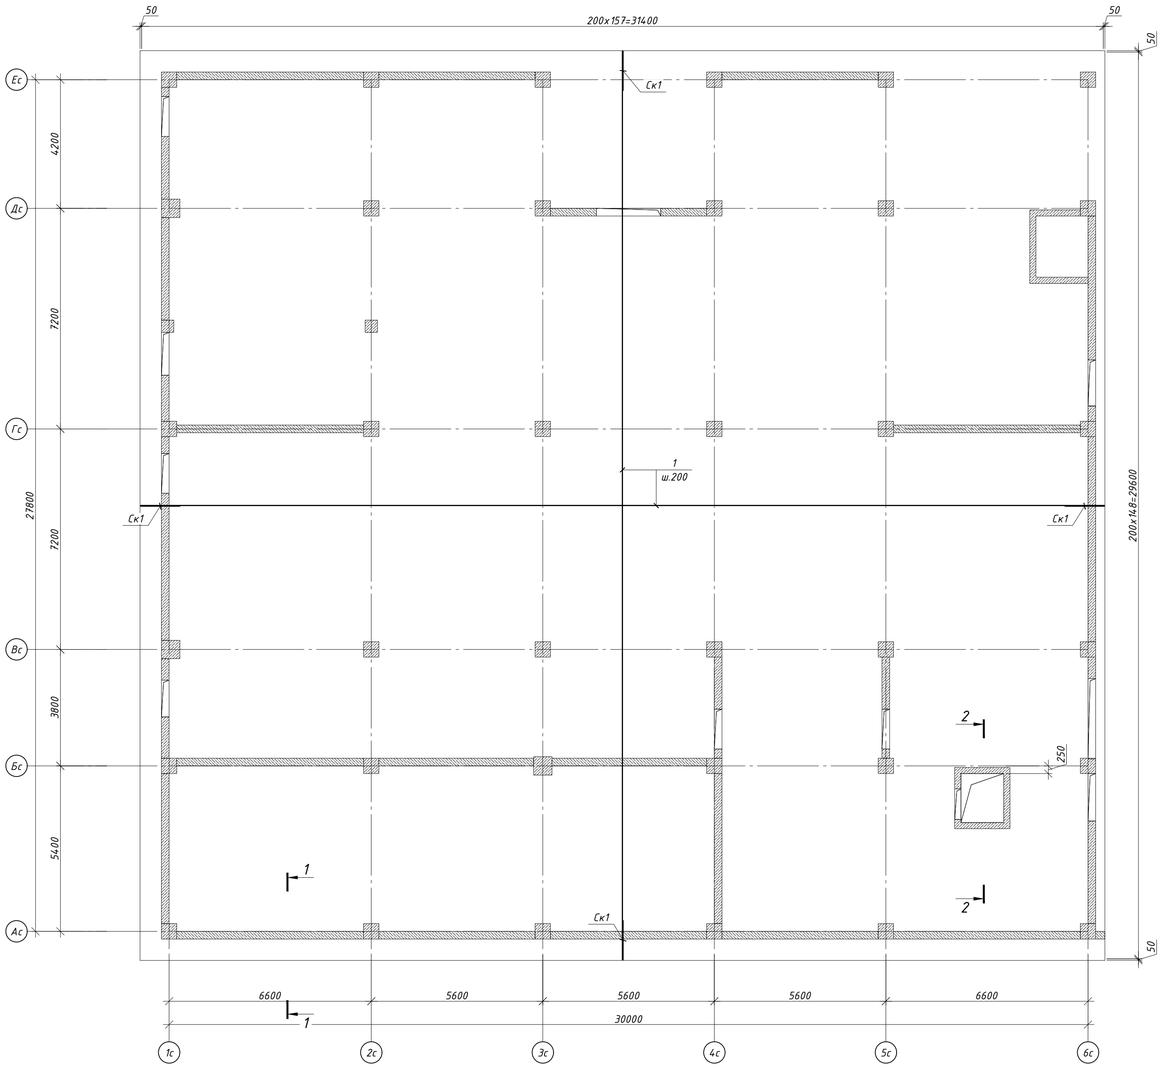


Разрез 1-1 (Армирование)
М 1:50

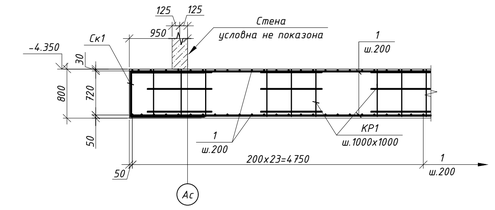

Разрез 2 - 2 (Армирование)
М 1:25

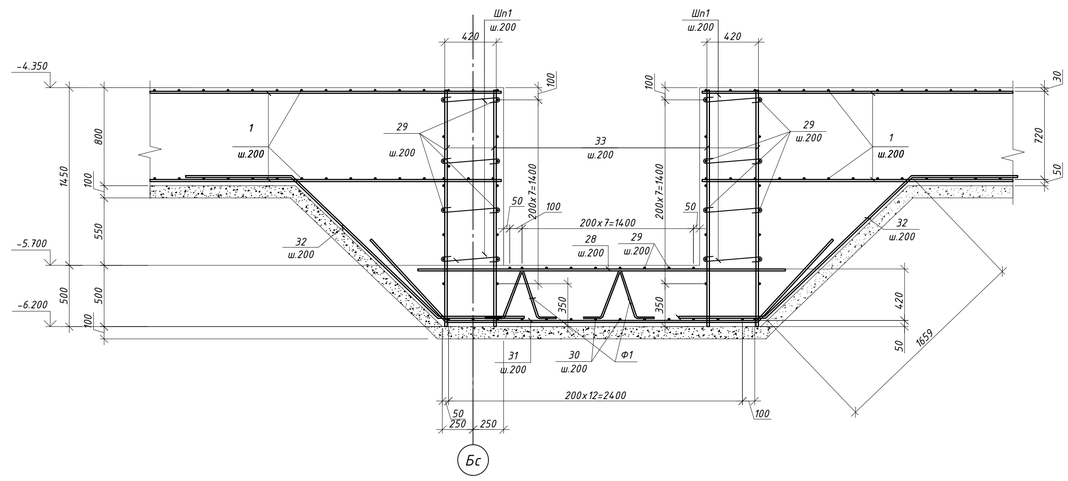


Разрез 3 - 3 (Армирование)
М 1:25

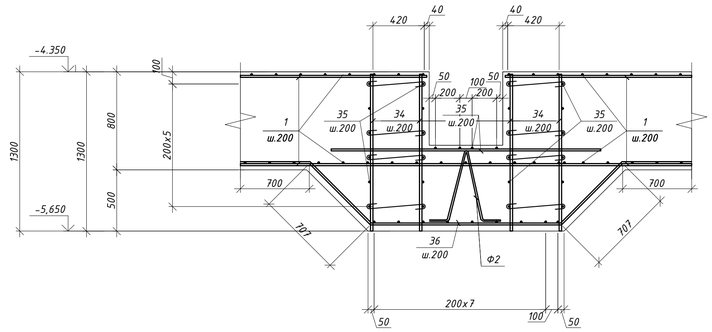

						65П-АИП-2024-1-КЖ	
						Строительство многопрофильной больницы на 250 коек с онкологическим центром и поликлиникой на 350 посещений, по адресу: Медеуский район, г. Алматы	
Изм.	Колуч	Лист	N док.	Подп.	Дата		
						"Блок 1 Секция 1"	Стадия: РП; Лист: 3.2; Листов:
ГКП		Курал М					
Проверил		Кыдырбай А				Схема расположения основных арматуры фундамента Фм-1 на отм -4.350	АстанаИнжПроект
Разраб.		Ауез Б					
Н.контроль		Ешенкулова					

Формат А1

Схема расположения дополнительного арматуры фундамента Фм-1 нижней зоны по буквенным осям на отм. -4.350

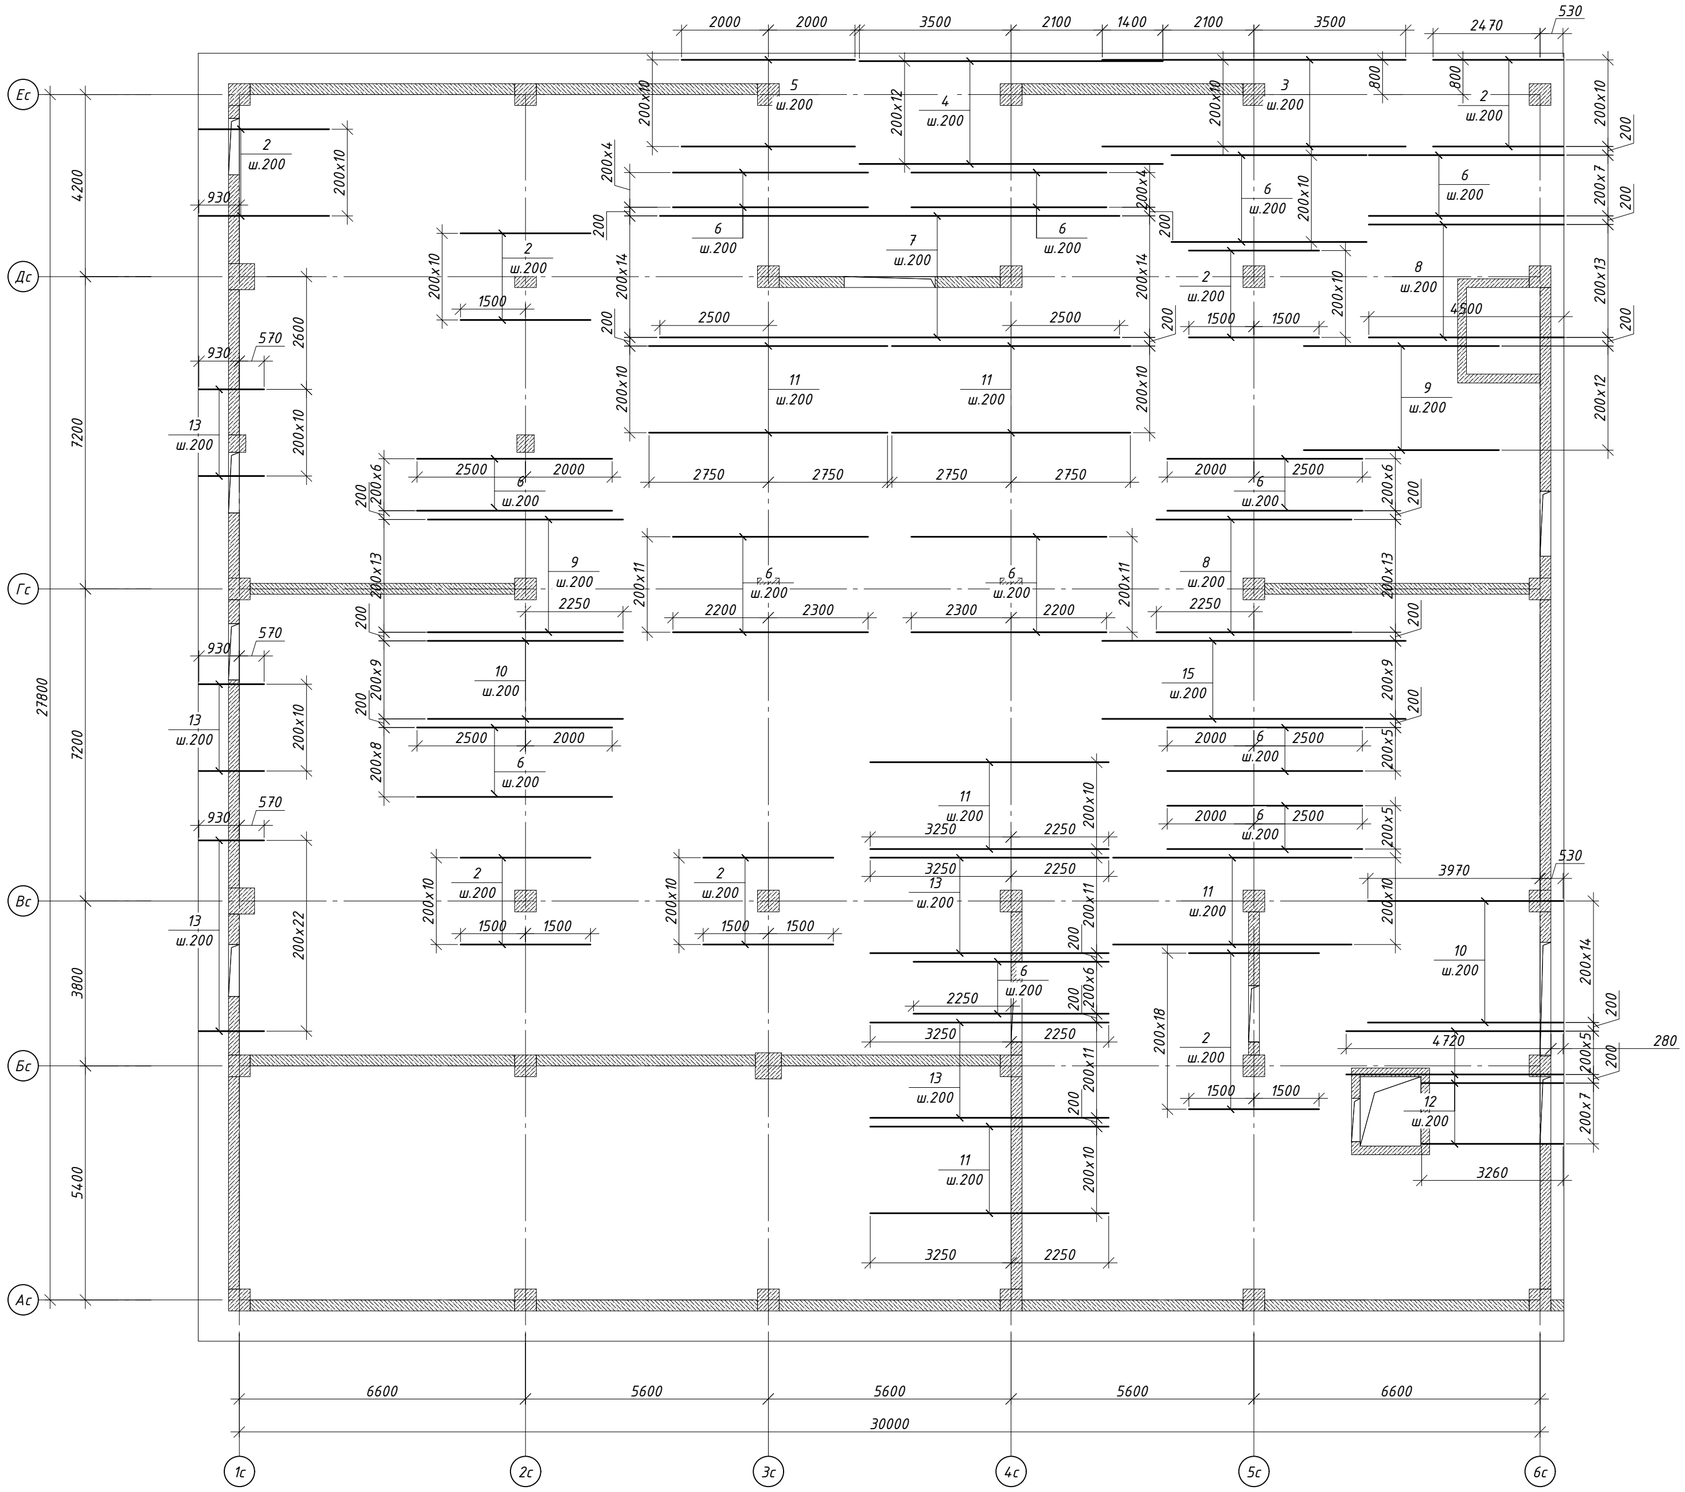


1. Общие указания см. л. – 1.1.
2. Данный лист читать совместно с л. КЖ-2.5 и 3.1 ... 3.10
3. Стыки рабочей арматуры внахлестку без сварки, на скрутках из вязальной проволоки не менее 3 шт. на стык. Длина нахлеста 71d. Стыки располагать вразбежку, чтобы площадь рабочей арматуры, стыкуемой в одном сечении, не превышала 50%.
4. Расход арматуры в погонных метрах приведен с учетом нахлеста.
5. Стержни, указанные в "Ведомости деталей", должны гнуться механическим способом в холодном состоянии с радиусом гиба 3d – 5d, где d – диаметр стержня

						65П-АИП-2024-1-КЖ
						Строительство многопрофильной больницы на 250 коек с онкологическим центром и поликлиникой на 350 посещений, по адресу: Медеуский район, г. Алматы
Изм.	Кол.уч.	Лист	N док.	Подп.	Дата	
						"Блок 1 Секция 1" — Стадия: РП; Лист: 3.3; Листов:
ГКП		Курал М				Схема расположения дополнительного арматуры фундамента Фм-1 нижней зоны по буквенным осям на отм. -4.350
Проверил		Кыдырбай А				АстанаИнжПроект
Разраб.		Ауез Б				
Н.контроль		Ешенкулова				

Формат А2


Схема расположения дополнительного арматуры фундамента Фм-1 верхней зоны по буквенным осям на отм. -4.350

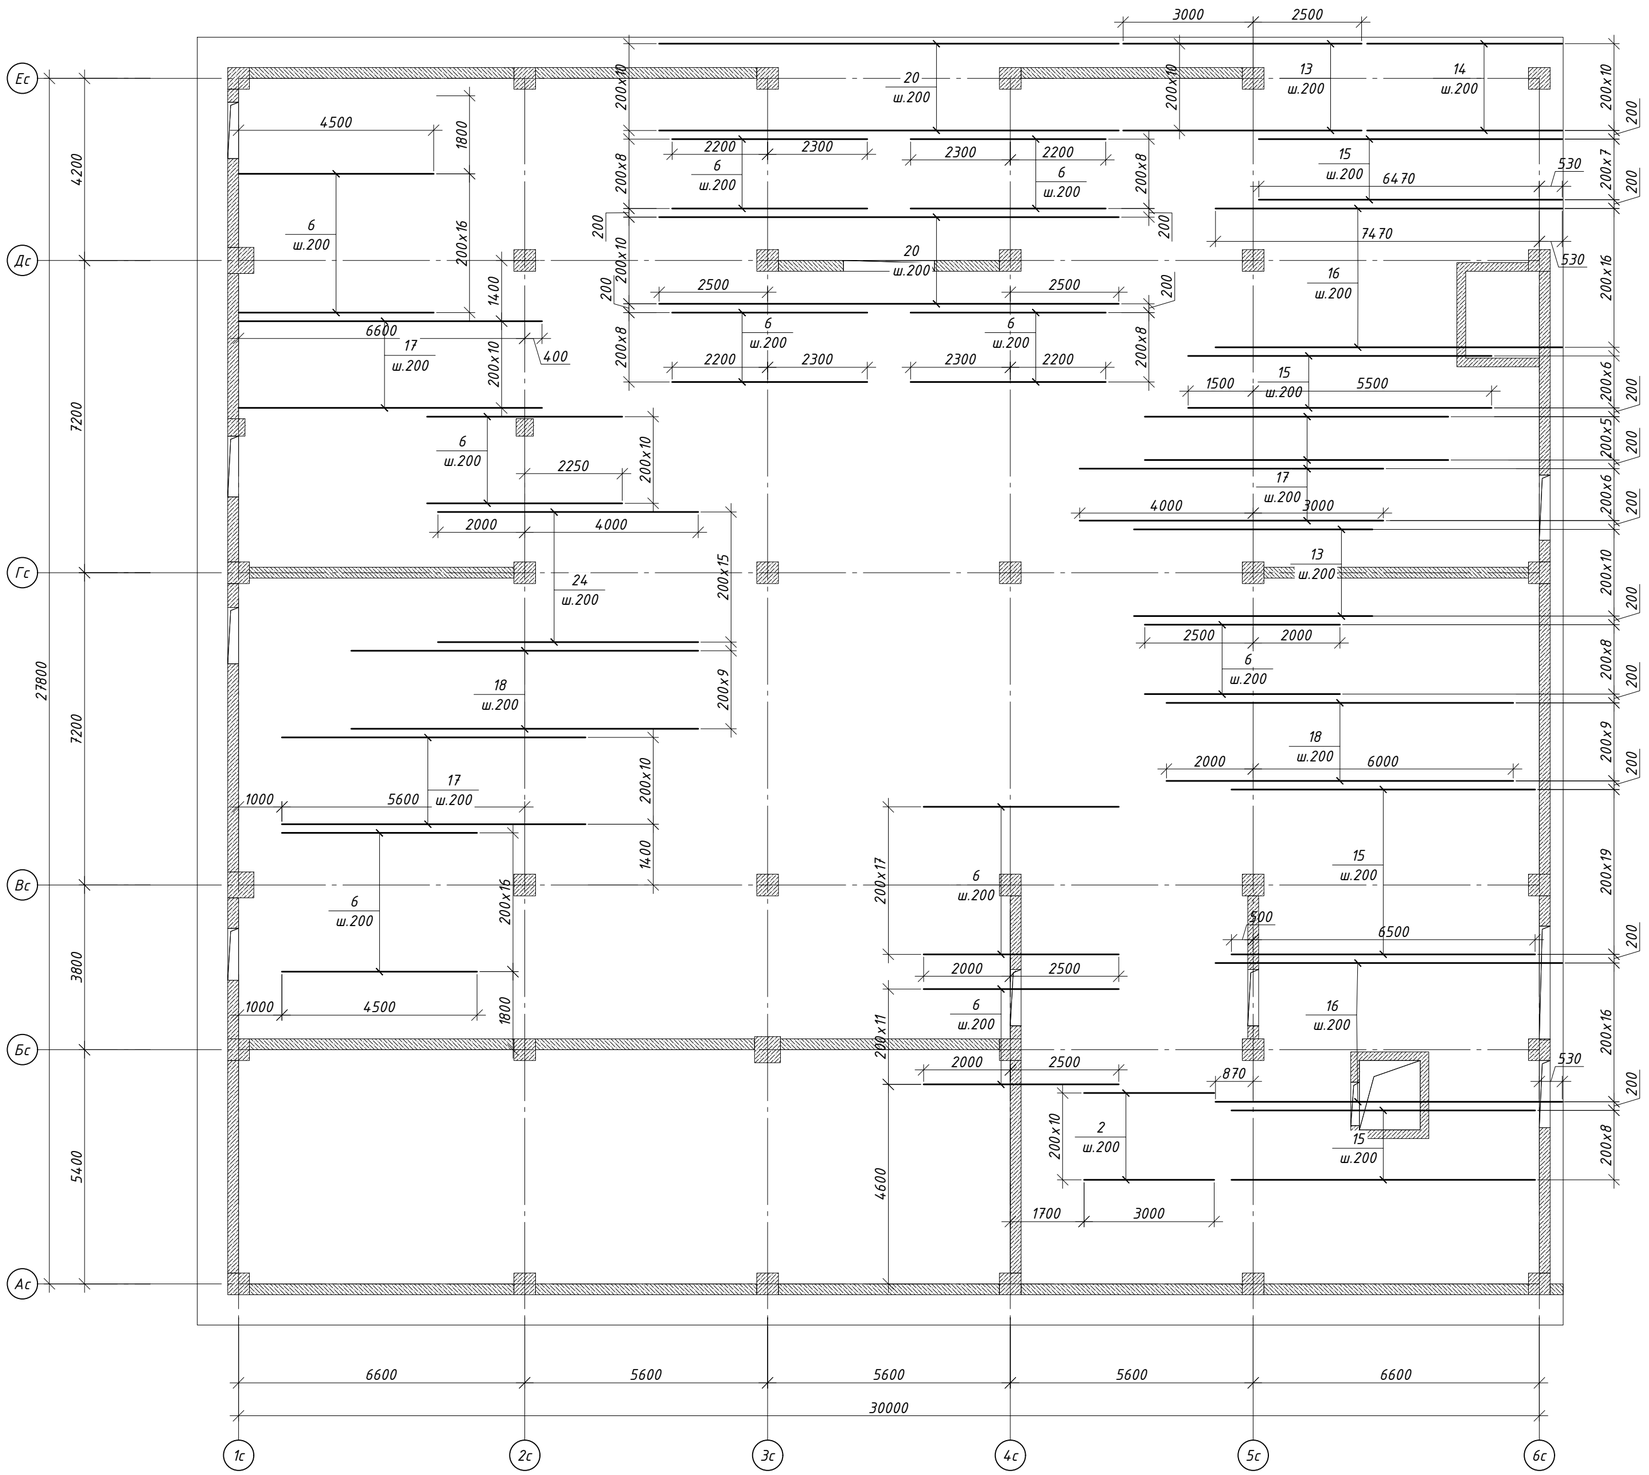

1. Общие указания см. л. - 1.1.
2. Данный лист читать совместно с л. КЖ-2.5 и 3.1 ... 3.10
3. Стыки рабочей арматуры внахлестку без сварки, на скрутках из вязальной проволоки не менее 3 шт. на стык. Длина нахлеста 71d. Стыки располагать вразбежку, чтобы площадь рабочей арматуры, стыкуемой в одном сечении, не превышала 50%.
4. Расход арматуры в погонных метрах приведен с учетом нахлеста.
5. Стержни, указанные в "Ведомости деталей", должны гнуться механическим способом в холодном состоянии с радиусом гиба 3d - 5d, где d - диаметр стержня

						65П-АИП-2024-1-КЖ
						Строительство многопрофильной больницы на 250 коек с онкологическим центром и поликлиникой на 350 посещений, по адресу: Медеуский район, г. Алматы
Изм.	Кол.уч.	Лист	N док.	Подп.	Дата	
						"Блок 1 Секция 1"
ГКП		Курал М				Стадия: РП; Лист: 3.4; Листов:
Проверил		Кыдырбай А				Схема расположения дополнительного арматуры фундамента Фм-1 верхней зоны по буквенным осям на отм. -4.350
Разраб.		Ауез Б				АстанаИнжПроект
Н.контроль		Ешенкулова				Формат А2


Схема расположения дополнительного арматуры фундамента Фм-1 нижней зоны по цифровым осям на отм. -4.350

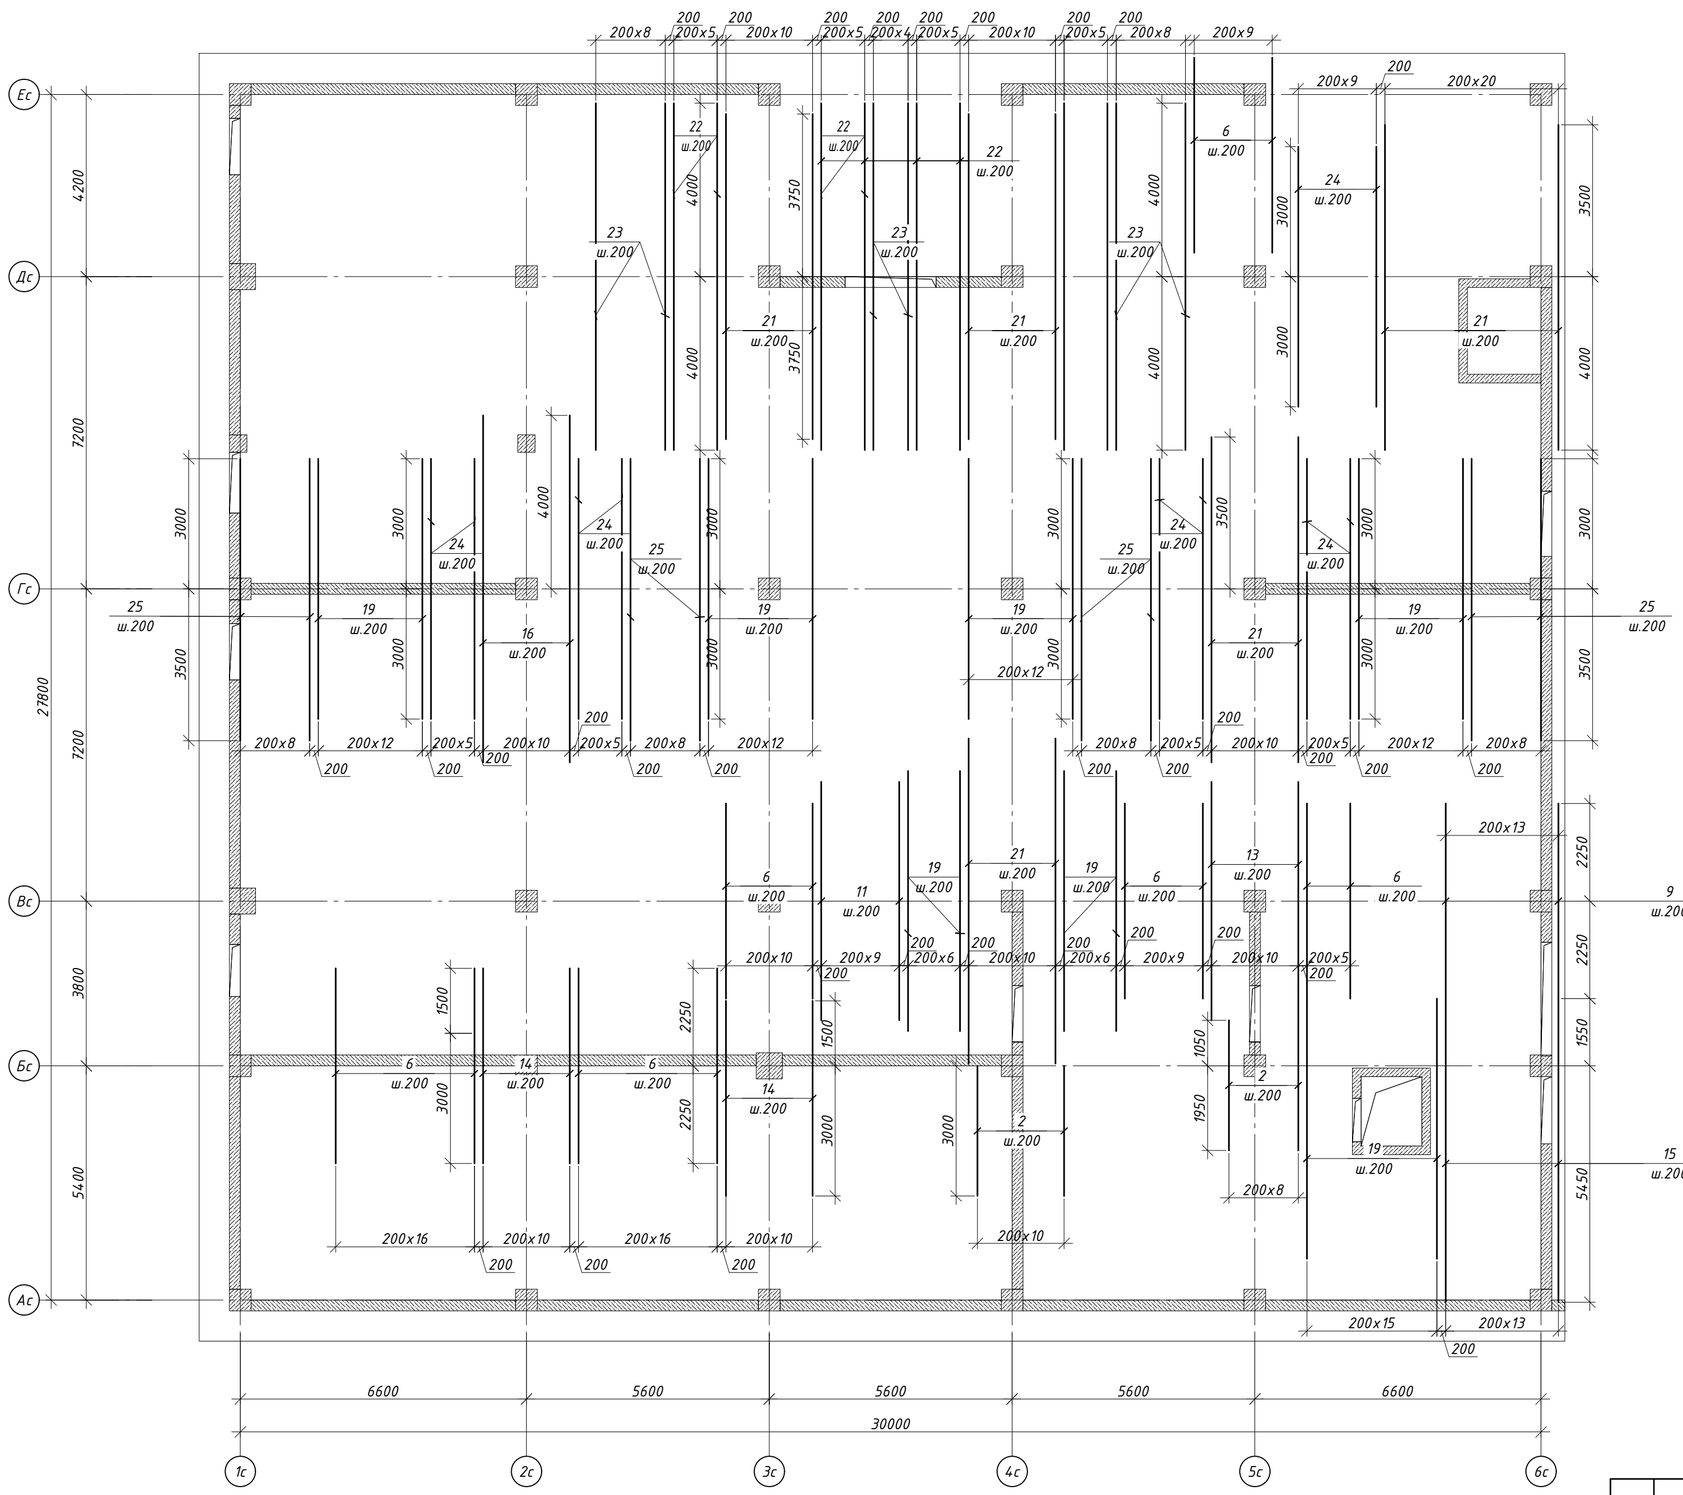

1. Общие указания см. л. - 1.1.
2. Данный лист читать совместно с л. КЖ-2.5 и 3.1 ... 3.10
3. Стыки рабочей арматуры внахлестку без сварки, на скрутках из вязальной проволоки не менее 3 шт. на стык. Длина нахлеста 71d. Стыки располагать вразбежку, чтобы площадь рабочей арматуры, стыкуемой в одном сечении, не превышала 50%.
4. Расход арматуры в погонных метрах приведен с учетом нахлеста.
5. Стержни, указанные в "Ведомости деталей", должны гнуться механическим способом в холодном состоянии с радиусом гиба 3d - 5d, где d - диаметр стержня

						65П-АИП-2024-1-КЖ
						Строительство многопрофильной больницы на 250 коек с онкологическим центром и поликлиникой на 350 посещений, по адресу: Медеуский район, г. Алматы
Изм.	Кол.уч	Лист	N док.	Подп.	Дата	
						"Блок 1 Секция 1" — Стадия: РП; Лист: 3.5; Листов:
ГКП		Курал М				
Проверил		Кыдырбай А				Схема расположения дополнительного арматуры фундамента Фм-1 нижней зоны по цифровым осям на отм. -4.350
Разраб.		Ауез Б				АстанаИнжПроект
Н.контроль		Ешенкулова				Формат А2


Схема расположения дополнительного арматуры фундамента Фм-1 верхней зоны по цифровым осям на отм. -4.350

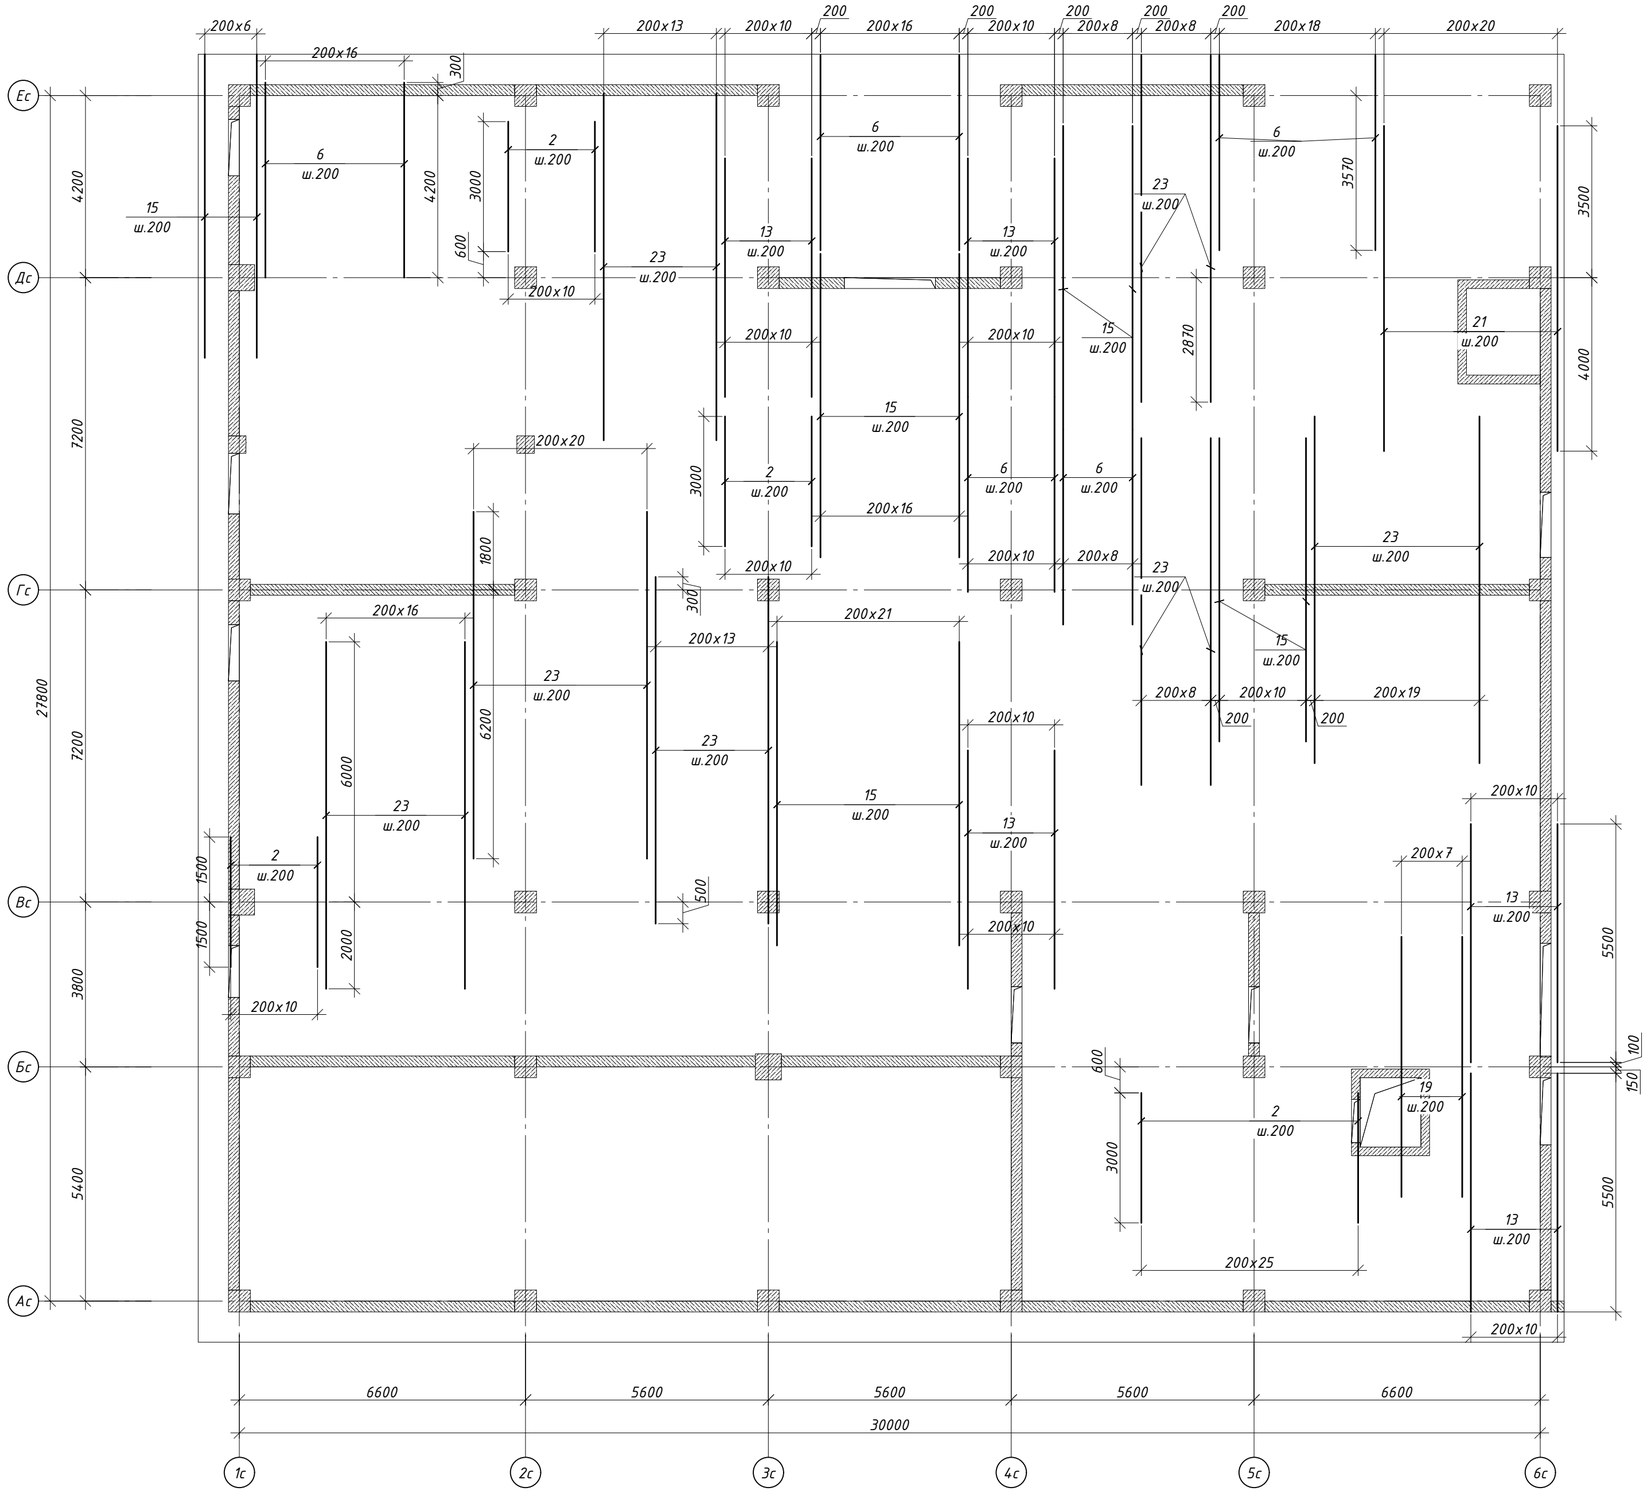


1. Общие указания см. л. - 1.1.
2. Данный лист читать совместно с л. КЖ-2.5 и 3.1 ... 3.10
3. Стыки рабочей арматуры внахлестку без сварки, на скрутках из вязальной проволоки не менее 3 шт. на стык. Длина нахлеста 71d. Стыки располагать вразбежку, чтобы площадь рабочей арматуры, стыкуемой в одном сечении, не превышала 50%.
4. Расход арматуры в погонных метрах приведен с учетом нахлеста.
5. Стержни, указанные в "Ведомости деталей", должны гнуться механическим способом в холодном состоянии с радиусом гиба 3d - 5d, где d - диаметр стержня

						65П-АИП-2024-1-КЖ
						Строительство многопрофильной больницы на 250 коек с онкологическим центром и поликлиникой на 350 посещений, по адресу: Медеуский район, г. Алматы
Изм.	Кол.уч	Лист	N док.	Подп.	Дата	
						"Блок 1 Секция 1"
ГКП		Курал М				Стадия: РП; Лист: 3.6; Листов:
Проверил		Кыдырбай А				Схема расположения дополнительного арматуры фундамента Фм-1 верхней зоны по цифровым осям на отм. -4.350
Разраб.		Ауез Б				АстанаИнжПроект
Н.контроль		Ешенкулова				Формат А2

Схема расположения поперечный арматуры фундамента Фм-1 на отм -4.350

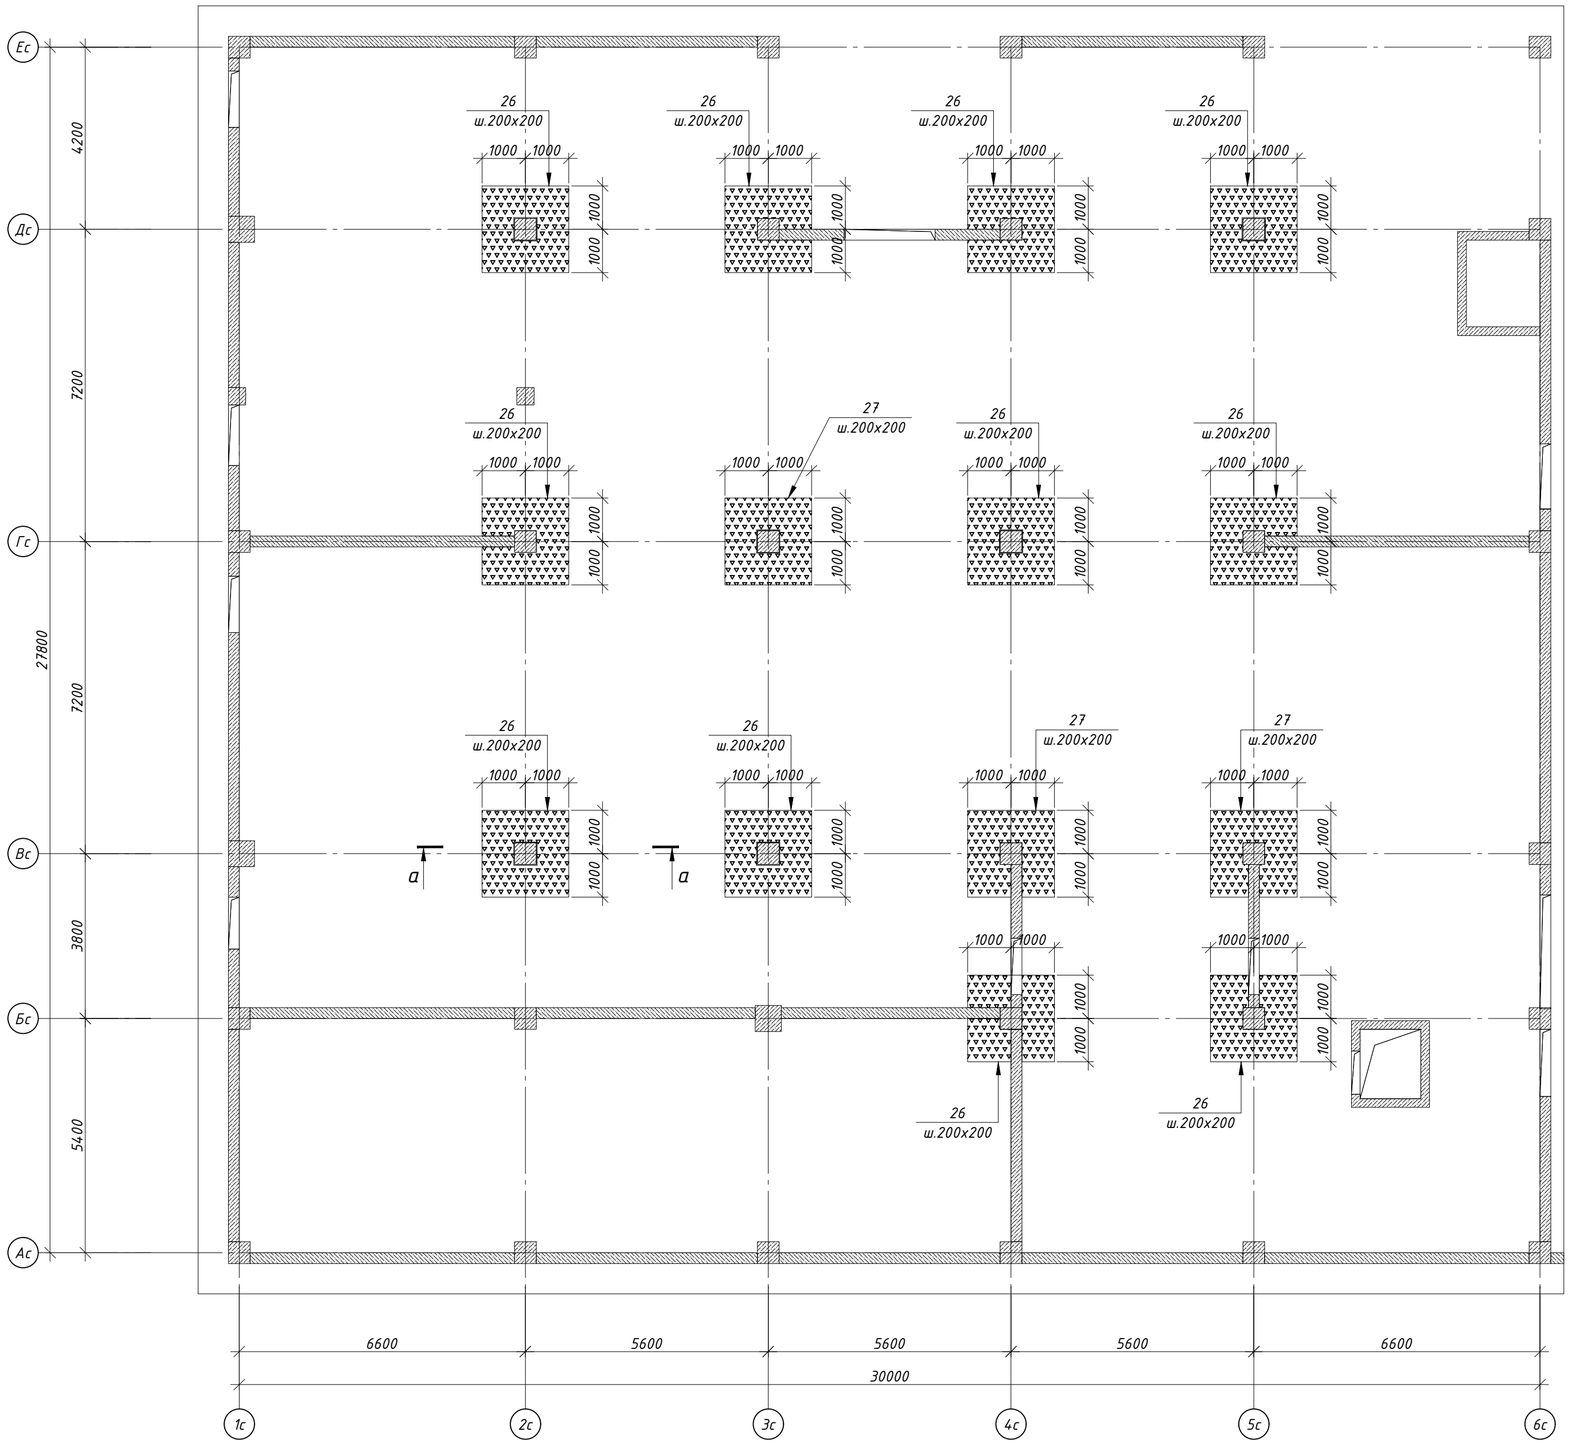

Разрез а-а (Армирование)
М 1:50

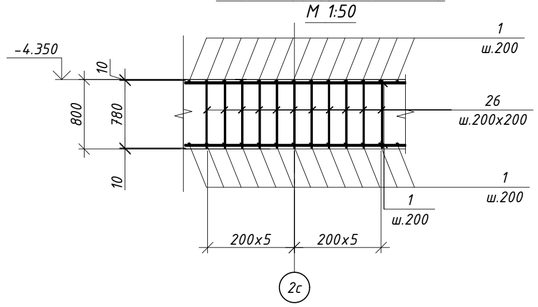

						65П-АИП-2024-1-КЖ	
						Строительство многопрофильной больницы на 250 коек с онкологическим центром и поликлиникой на 350 посещений, по адресу: Медеуский район, г. Алматы	
Изм.	Кол.уч	Лист	N док.	Подп.	Дата		
						"Блок 1 Секция 1"	Стадия: РП; Лист: 3.7; Листов:
ГКП		Курал М					
Проверил		Кыдырбай А				Схема расположения поперечный арматуры фундамента Фм-1 на отм -4.350	АстанаИнжПроект
Разраб.		Ауез Б					
Н.контроль		Ешенкулова					


Формат А2


Спецификация элементов

Поз.	Обозначение	Наименование	Кол.	Масса ед.кг	Примечание
		Фундамент Фм-1			86429.42
1	ГОСТ 34028-2016(214-210-0502-0004)	ф 18 А500С L= пог.м.	19637.98	2.00	39228.47
2	ГОСТ 34028-2016(214-210-0502-0001)	ф 12 А500С L= 3000	164	2.66	436.80
3	ГОСТ 34028-2016(214-210-0502-0008)	ф 28 А500С L= 7000	11	33.84	372.19
4	ГОСТ 34028-2016(214-210-0502-0006)	ф 22 А500С L= 7000	13	20.89	271.55
5	ГОСТ 34028-2016(214-210-0502-0004)	ф 18 А500С L= 4000	11	7.99	87.89
6	ГОСТ 34028-2016(214-210-0502-0002)	ф 14 А500С L= 6500	359	7.85	2819.83
7	ГОСТ 34028-2016(214-210-0502-0008)	ф 28 А500С L= 10600	15	51.24	768.55
8	ГОСТ 34028-2016(214-210-0502-0009)	ф 32 А500С L= 4500	28	28.41	795.48
9	ГОСТ 34028-2016(214-210-0101-0002)	ф 28 А500С L= 4500	41	21.75	891.81
10	ГОСТ 34028-2016(214-210-0502-0006)	ф 22 А500С L= 4500	25	13.43	335.70
11	ГОСТ 34028-2016(214-210-0502-0003)	ф 16 А500С L= 5500	43	8.68	373.28
12	ГОСТ 34028-2016(214-210-0502-005)	ф 20 А500С L= пог.м.	58.88	2.47	145.22
13	ГОСТ 34028-2016(214-210-0502-0007)	ф 25 А500С L= 5500	112	21.19	2373.67
14	ГОСТ 34028-2016(214-210-0502-0004)	ф 18 А500С L= 4500	33	8.99	296.64
15	ГОСТ 34028-2016(214-210-0502-0004)	ф 18 А500С L= 7000	134	13.98	1873.73
16	ГОСТ 34028-2016(214-210-0502-0008)	ф 28 А500С L= 8000	45	38.67	1740.12
17	ГОСТ 34028-2016(214-210-0502-0002)	ф 14 А500С L= 7000	35	8.46	296.06
18	ГОСТ 34028-2016(214-210-0502-0001)	ф 12 А500С L= 8000	20	7.10	142.05
19	ГОСТ 34028-2016(214-210-0502-0005)	ф 20 А500С L= 6000	90	14.80	1331.72
20	ГОСТ 34028-2016(214-210-0502-0006)	ф 22 А500С L= 10600	22	31.63	695.88
21	ГОСТ 34028-2016(214-210-0502-0009)	ф 32 А500С L= 7500	86	47.35	4072.11
22	ГОСТ 34028-2016(214-210-0502-0006)	ф 22 А500С L= 8000	24	23.87	572.94
23	ГОСТ 34028-2016(214-210-0502-0002)	ф 14 А500С L= 8000	127	9.67	1227.75
24	ГОСТ 34028-2016(214-210-0502-0006)	ф 22 А500С L= 6000	50	17.90	895.21
25	ГОСТ 34028-2016(214-210-0502-0002)	ф 14 А500С L= 6500	36	7.85	282.77
26	ГОСТ 34028-2016(214-210-0502-0002)	ф 14 А500С L= 780	1080	0.94	1017.97
27	ГОСТ 34028-2016(214-210-0502-0004)	ф 18 А500С L= 780	297	1.56	462.76
Ск1	ГОСТ 34028-2016(214-210-0502-0004)	ф 18 А500С L= 3340	644	6.67	4296.72
28*	ГОСТ 34028-2016(214-210-0502-0003)	ф 16 А500С L= 3000	24	4.74	113.64
29*	ГОСТ 34028-2016(214-210-0502-0003)	ф 16 А500С L= 2800	25	4.42	110.48
30*	ГОСТ 34028-2016(214-210-0502-0003)	ф 16 А500С L= 3930	14	6.20	86.84
31*	ГОСТ 34028-2016(214-210-0502-0003)	ф 16 А500С L= 3730	13	5.89	76.53
32*	ГОСТ 34028-2016(214-210-0502-0003)	ф 16 А500С L= 3100	54	4.89	264.21
33*	ГОСТ 34028-2016(214-210-0502-0003)	ф 16 А500С L= 1910	58	3.01	174.85
34	ГОСТ 34028-2016(214-210-0502-0003)	ф 16 А500С L= 1260	144	1.99	286.37
35	ГОСТ 34028-2016(214-210-0502-0003)	ф 16 А500С L= 2200	180	3.47	625.02
36*	ГОСТ 34028-2016(214-210-0502-0003)	ф 16 А500С L= 4380	24	6.91	165.91
Ф1	ГОСТ 34028-2016(214-210-0502-0001)	ф 12 А500С L= 1676	5	1.49	7.44
Ф2	ГОСТ 34028-2016(214-210-0502-0001)	ф 12 А500С L= 2076	6	1.84	11.06
Шп1*	ГОСТ 34028-2016(214-210-0101-0002)	ф 8 А 240 L= 620	284	0.24	69.48
		Каркас Кр1	1852	8.82	16332.70
40	ГОСТ 34028-2016(214-210-0502-0003)	ф 16 А500С L= 780	5	1.23	6.16
41	ГОСТ 34028-2016(214-210-0502-0001)	ф 12 А500С L= 1000	3	0.89	2.66
		Материалы:			
	(212-101-0902)	Класс бетона С20/25 (В25),W6 F100,м³			776.92
	(212-101-0308)	Класс бетона С8/10 (В7.5),W6 F100,м³			94.82









Позиции со "*" см. "Ведомость деталей" см. на данном листе.

Каркас Кр-1

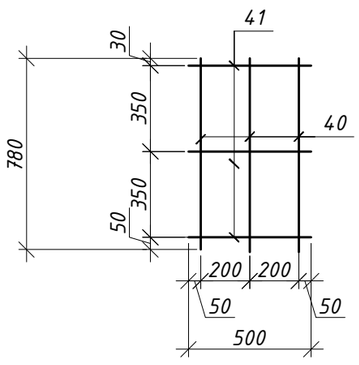

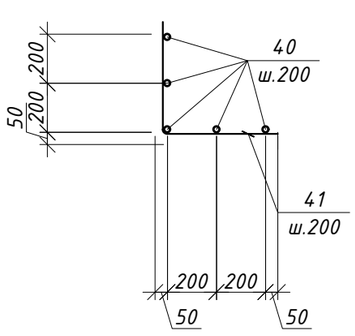

Ведомость деталей

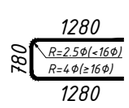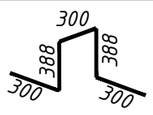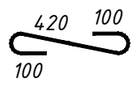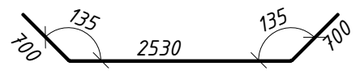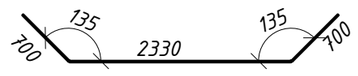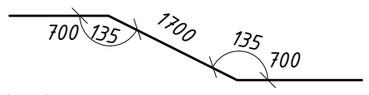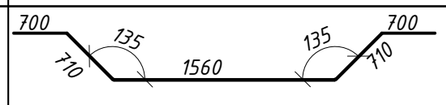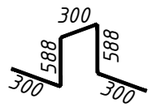Поз.	Эскиз
Ск1	 по н.г. L=3340
Ф1	 по н.г. L=1676
Шп1	 по в.г. L=620
30	 по н.г. L=3930
31	 по н.г. L=3730
32	 по н.г. L=3100
36	 L=4380
Ф2	 по н.г. L=2076


Ведомость расхода стали, кг


Марка элемента	Изделия арматурные														Всего
	Арматура класса														
	А240 ГОСТ 34028-2016(214-210-0101)				А500С ГОСТ 34028-2016(214-210-0502)										
	Ф6	Ф8	Ф10	Итого	Ф12	Ф14	Ф16	Ф18	Ф20	Ф22	Ф25	Ф28	Ф32	Итого	
Фм-1	---	69.48	---	69.48	5530.05	5644.38	13677.15	46246.22	1476.94	2771.28	2373.67	3772.67	4867.59	86359.94	86429.42

						65П-АИП-2024-1-КЖ
						Строительство многопрофильной больницы на 250 коек с онкологическим центром и поликлиникой на 350 посещений, по адресу: Медеуский район, г. Алматы
Изм.	Кол.уч.	Лист	N док.	Подп.	Дата	
ГКП		Курал М				"Блок 1 Секция 1"
Проверил		Кыдырбай А				Стадия: РП; Лист: 3.8; Листов:
Разраб.		Ауез Б				Спецификация фундамента Фм-1 на отм. -4.350
Н.контроль		Ешенкулова				АстанаИнжПроект


Формат А2

Выпуск из фундамента на отм. -4.350

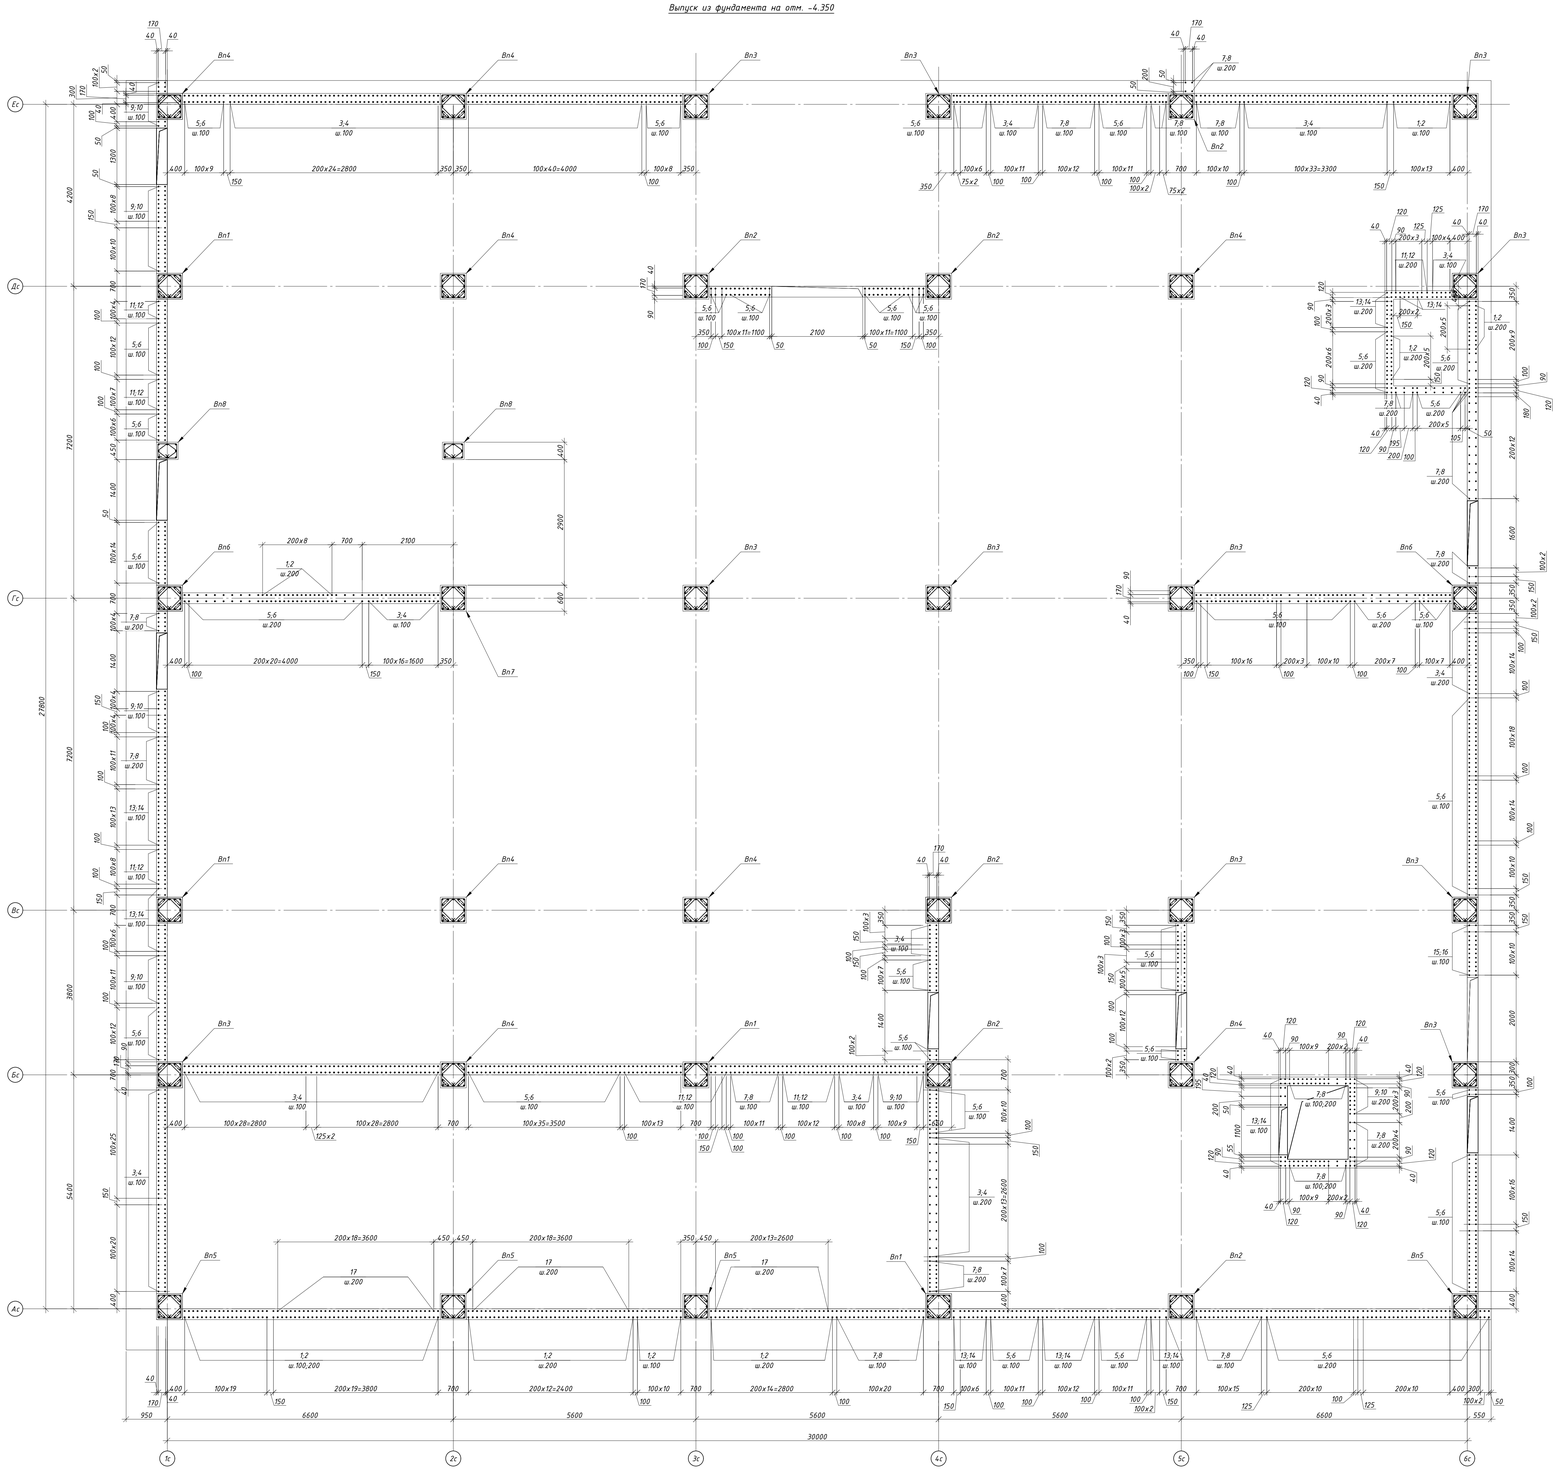

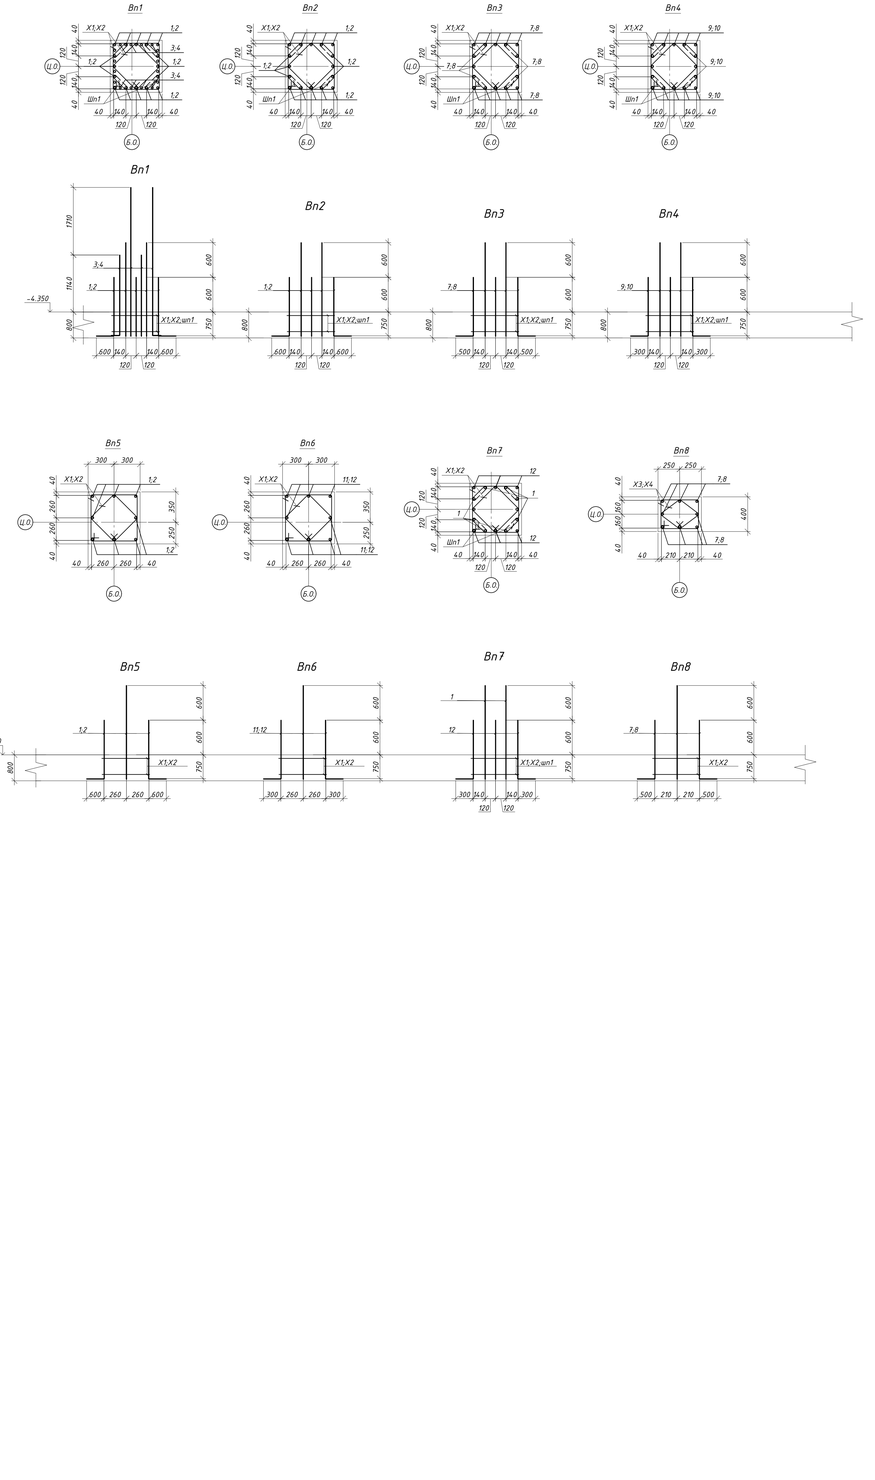

Выпуск из фундамента для стен

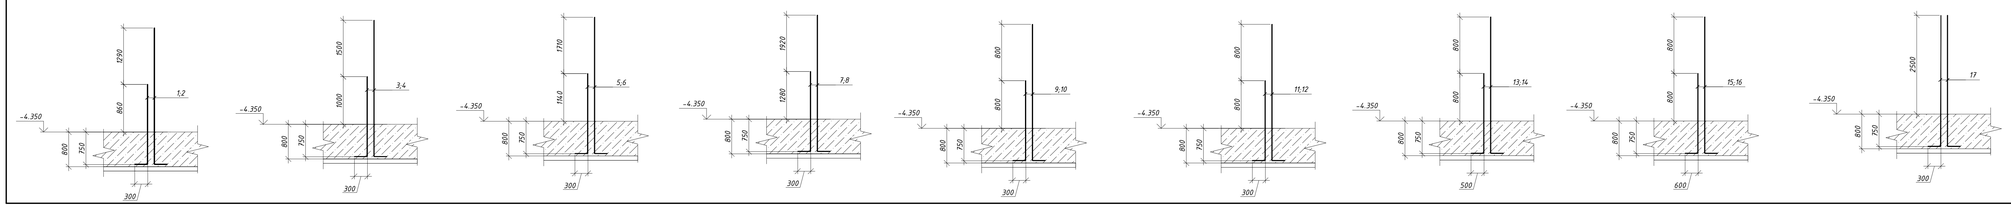

1. Общие указания см. л. – 1.1.
2. Данный лист читать совместно с л. КЖ-2.5 и 3.1 ... 3.10
3. Стыки рабочей арматуры внахлестку без сварки, на скрутках из вязальной проволоки не менее 3 шт. на стык. Длина нахлеста 71d. Стыки располагать вразбежку, чтобы площадь рабочей арматуры, стыкуемой в одном сечении, не превышала 50%.
4. Расход арматуры в погонных метрах приведен с учетом нахлеста.
5. Стержни, указанные в "Ведомости деталей", должны гнуться механическим способом в холодном состоянии с радиусом гиба 3d - 5d, где d – диаметр стержня

							65П-АИП-2024-1-КЖ
							Строительство многопрофильной больницы на 250 коек с онкологическим центром и поликлиникой на 350 посещений, по адресу: Медеуский район, г. Алматы
Изм.	Кол.уч.	Лист	N док.	Подп.	Дата		
							"Блок 1 Секция 1"
ГИП		Курал М					
Проверил		Кыдырбай А.					
Разраб.		Ауез Б.					Схема расположения выпусков из фундамента Фм-1 на отм -4.350
Н.контроль		Евенкулова					

Стадия	Лист	Листов
РП	3.9	

АстанаИнжПроект

Формат А0




Спецификация элементов

Поз.	Обозначение	Наименование	Кол.	Масса ед.кг	Примечание
		Выпуски из фундамента для стены			12251.60
1	ГОСТ 34028-2016(214-210-0502-0001)	ф 12 А500С L= 1910	121	1.70	205.18
2	ГОСТ 34028-2016(214-210-0502-0001)	ф 12 А500С L= 3200	121	2.84	343.76
3	ГОСТ 34028-2016(214-210-0502-0002)	ф 14 А500С L= 2050	315	2.48	780.33
4	ГОСТ 34028-2016(214-210-0502-0002)	ф 14 А500С L= 3550	315	4.29	1351.31
5	ГОСТ 34028-2016(214-210-0502-0003)	ф 16 А500С L= 2190	439	3.46	1517.43
6	ГОСТ 34028-2016(214-210-0502-0003)	ф 16 А500С L= 3900	439	6.16	2702.27
7	ГОСТ 34028-2016(214-210-0502-0004)	ф 18 А500С L= 2330	158	4.65	735.39
8	ГОСТ 34028-2016(214-210-0502-0004)	ф 18 А500С L= 4250	158	8.49	1341.38
9	ГОСТ 34028-2016(214-210-0502-0005)	ф 20 А500С L= 1850	53	4.56	241.81
10	ГОСТ 34028-2016(214-210-0502-0005)	ф 20 А500С L= 2650	53	6.54	346.37
11	ГОСТ 34028-2016(214-210-0502-0006)	ф 22 А500С L= 1850	58	5.52	320.19
12	ГОСТ 34028-2016(214-210-0502-0006)	ф 22 А500С L= 2650	58	7.91	458.65
13	ГОСТ 34028-2016(214-210-0502-0007)	ф 25 А500С L= 2050	68	7.90	537.16
14	ГОСТ 34028-2016(214-210-0502-0007)	ф 25 А500С L= 2850	68	10.98	746.78
15	ГОСТ 34028-2016(214-210-0502-0008)	ф 28 А500С L= 2150	12	10.39	124.71
16	ГОСТ 34028-2016(214-210-0502-0008)	ф 28 А500С L= 2950	12	14.26	171.11
17	ГОСТ 34028-2016(214-210-0502-0001)	ф 12 А500С L= 3550	104	3.15	327.78
					5084.22
Вп-1	данный лист	Выпуск Вп-1	4	252.80	1011.21
Вп-2	данный лист	Выпуск Вп-2	6	178.43	1070.59
Вп-3	данный лист	Выпуск Вп-3	11	136.97	1506.72
Вп-4	данный лист	Выпуск Вп-4	8	97.52	780.17
Вп-5	данный лист	Выпуск Вп-5	4	90.16	360.65
Вп-6	данный лист	Выпуск Вп-6	2	41.63	83.26
Вп-7	данный лист	Выпуск Вп-7	1	133.80	133.80
Вп-8	данный лист	Выпуск Вп-8	2	68.91	137.83
		Вп-1			252.80
1	ГОСТ 34028-2016(214-210-0502-0008)	ф 28 А500С L= 1950	8	9.43	75.41
2	ГОСТ 34028-2016(214-210-0502-0008)	ф 28 А500С L= 2550	8	12.33	98.61
3	ГОСТ 34028-2016(214-210-0502-0003)	ф 16 А500С L= 3800	8	6.00	47.98
4	ГОСТ 34028-2016(214-210-0502-0003)	ф 16 А500С L= 2090	8	3.30	26.39
X1*	ГОСТ 34028-2016(214-210-0101-0002)	ф 8 А 240 L= 2280	2	0.90	1.80
X2*	ГОСТ 34028-2016(214-210-0101-0002)	ф 8 А 240 L= 1720	2	0.68	1.36
Шп1*	ГОСТ 34028-2016(214-210-0101-0002)	ф 8 А 240 L= 400	8	0.16	1.26
		Вп-2			178.43
1	ГОСТ 34028-2016(214-210-0502-0008)	ф 28 А500С L= 1950	8	9.43	75.41
2	ГОСТ 34028-2016(214-210-0502-0008)	ф 28 А500С L= 2550	8	12.33	98.61
X1*	ГОСТ 34028-2016(214-210-0101-0002)	ф 8 А 240 L= 2280	2	0.90	1.80
X2*	ГОСТ 34028-2016(214-210-0101-0002)	ф 8 А 240 L= 1720	2	0.68	1.36
Шп1*	ГОСТ 34028-2016(214-210-0101-0002)	ф 8 А 240 L= 400	8	0.16	1.26
		Вп-3			136.97
7	ГОСТ 34028-2016(214-210-0502-0007)	ф 25 А500С L= 1850	8	7.13	57.03
8	ГОСТ 34028-2016(214-210-0502-0007)	ф 25 А500С L= 2450	8	9.44	75.53
X1*	ГОСТ 34028-2016(214-210-0101-0002)	ф 8 А 240 L= 2280	2	0.90	1.80
X2*	ГОСТ 34028-2016(214-210-0101-0002)	ф 8 А 240 L= 1720	2	0.68	1.36
Шп1*	ГОСТ 34028-2016(214-210-0101-0002)	ф 8 А 240 L= 400	8	0.16	1.26
		Вп-4			97.52
9	ГОСТ 34028-2016(214-210-0502-0006)	ф 22 А500С L= 1650	8	4.92	39.39
10	ГОСТ 34028-2016(214-210-0502-0006)	ф 22 А500С L= 2250	8	6.71	53.71
X1*	ГОСТ 34028-2016(214-210-0101-0002)	ф 8 А 240 L= 2280	2	0.90	1.80
X2*	ГОСТ 34028-2016(214-210-0101-0002)	ф 8 А 240 L= 1720	2	0.68	1.36
Шп1*	ГОСТ 34028-2016(214-210-0101-0002)	ф 8 А 240 L= 400	8	0.16	1.26

Спецификация элементов

Поз.	Обозначение	Наименование	Кол.	Масса ед.кг	Примечание
		Вп-5			90.16
1	ГОСТ 34028-2016(214-210-0502-0008)	ф 28 А500С L= 1950	4	9.43	37.70
2	ГОСТ 34028-2016(214-210-0502-0008)	ф 28 А500С L= 2550	4	12.33	49.30
X1*	ГОСТ 34028-2016(214-210-0101-0002)	ф 8 А 240 L= 2280	2	0.90	1.80
X2*	ГОСТ 34028-2016(214-210-0101-0002)	ф 8 А 240 L= 1720	2	0.68	1.36
		Вп-6			41.63
11	ГОСТ 34028-2016(214-210-0502-0005)	ф 20 А500С L= 1650	4	4.07	16.28
12	ГОСТ 34028-2016(214-210-0502-0005)	ф 20 А500С L= 2250	4	5.55	22.20
X1*	ГОСТ 34028-2016(214-210-0101-0002)	ф 8 А 240 L= 2280	2	0.90	1.80
X2*	ГОСТ 34028-2016(214-210-0101-0002)	ф 8 А 240 L= 1720	2	0.68	1.36
		Вп-7			133.80
1	ГОСТ 34028-2016(214-210-0502-0008)	ф 28 А500С L= 2550	8	12.33	98.61
12	ГОСТ 34028-2016(214-210-0502-0005)	ф 20 А500С L= 1650	8	4.07	32.55
X1*	ГОСТ 34028-2016(214-210-0101-0002)	ф 8 А 240 L= 1880	2	0.74	1.48
X2*	ГОСТ 34028-2016(214-210-0101-0002)	ф 8 А 240 L= 1460	2	0.58	1.15
		Вп-8			68.91
7	ГОСТ 34028-2016(214-210-0502-0007)	ф 25 А500С L= 1850	4	7.13	28.51
8	ГОСТ 34028-2016(214-210-0502-0007)	ф 25 А500С L= 2450	4	9.44	37.76
X1*	ГОСТ 34028-2016(214-210-0101-0002)	ф 8 А 240 L= 1880	2	0.74	1.48
X2*	ГОСТ 34028-2016(214-210-0101-0002)	ф 8 А 240 L= 1460	2	0.58	1.15

Ведомость деталей

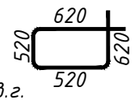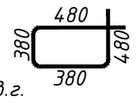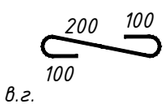Поз.	Эскиз
X1	
X2	
Шп1	

Ведомость расхода стали на элемент, кг

Марка элемента	Изделия арматурные												Всего
	Арматура класса												
	А240			А500С									
	ГОСТ 34028-2016(214-210-0101)			ГОСТ 34028-2016(214-210-0502)									
	Ф6	Ф8	Итого	Ф12	Ф14	Ф16	Ф18	Ф20	Ф22	Ф25	Ф28	Итого	
Выпуски из фундамента	0.00	155.01	155.01	876.73	2131.64	4517.18	2076.77	697.67	1523.65	2874.61	2483	17180.81	17335.82

1. Общие указания см. л. - 1.1.
2. Данный лист читать совместно с л. КЖ-2.5 и 3.1 ... 3.10
3. Стыки рабочей арматуры внахлестку без сварки, на скрутках из вязальной проволоки не менее 3 шт. на стык. Длина нахлеста 71d. Стыки располагать вразбежку, чтобы площадь рабочей арматуры, стыкуемой в одном сечении, не превышала 50%.
4. Расход арматуры в погонных метрах приведен с учетом нахлеста.
5. Стержни, указанные в "Ведомости деталей", должны гнуться механическим способом в холодном состоянии с радиусом гиба 3d - 5d, где d - диаметр стержня

Изм.	Кол.уч.	Лист	N док.	Подп.	Дата	65П-АИП-2024-1-КЖ			
						Строительство многопрофильной больницы на 250 коек с онкологическим центром и поликлиникой на 350 посещений, по адресу: Медеуский район, г. Алматы			
ГКП		Курал М				"Блок 1 Секция 1"	Стадия	Лист	Листов
Проверил		Кыдырбай А					РП	3.10	
Разраб.		Ауез Б				Спецификация выпусков из фундамента Фм-1 на отм -4.350	АстанаИнжПроект		
Н.контроль		Ешенкулова							

Согласовано | Взам. инв. № | Подп. и дата | Инв. № подл.

Формат А2