


Колонна Км-1.1

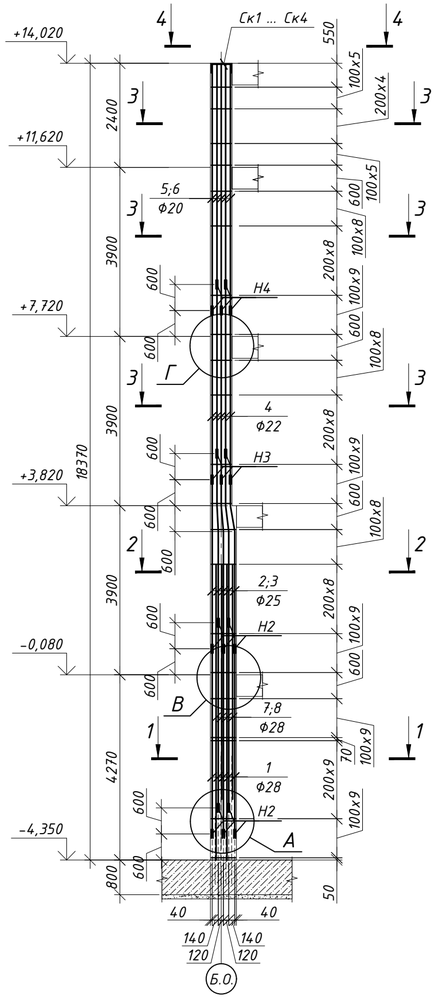


Разрез 1 - 1

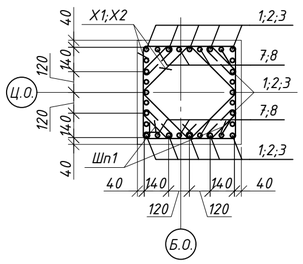


Разрез 2 - 2

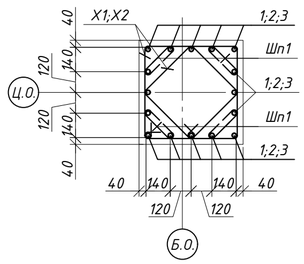


Разрез 3 - 3

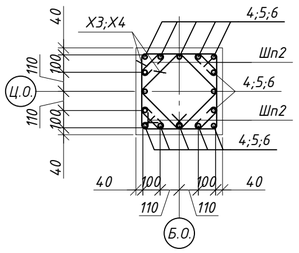


Разрез 4 - 4

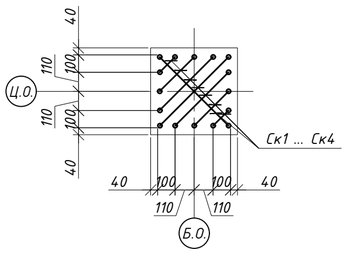



Сетка С1

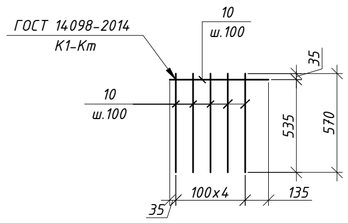


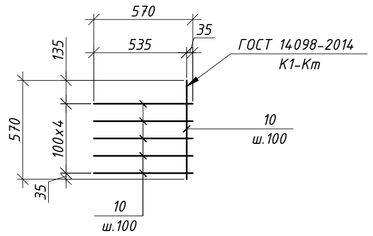

Сетка С2

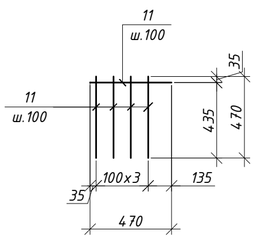

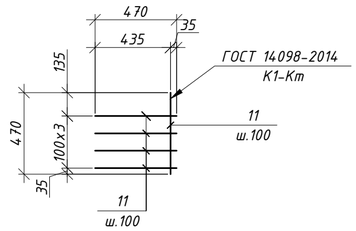


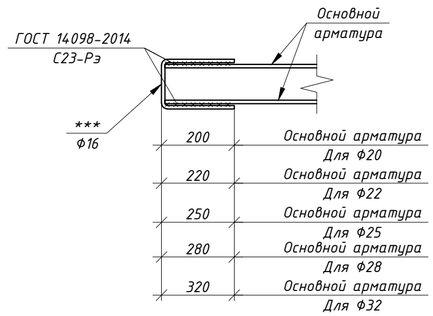



В

Г


Узел расположения сетки С1;

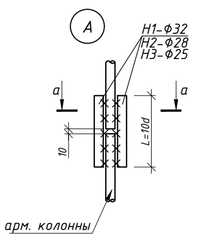

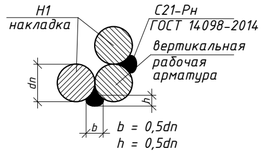

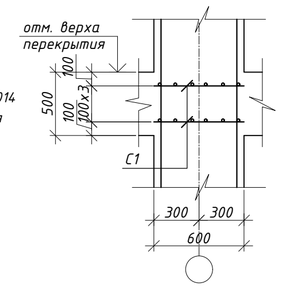

Узел расположения сетки С2

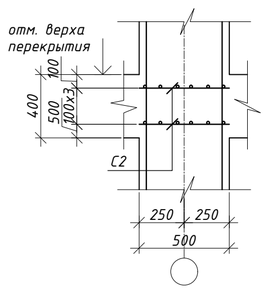

1. Схему расположения монолитных колонн см. листы КЖ-2.1; .... 2.7.
2. Бетонирование колонн в местах примыкания ригелей и монолитной плиты вести после установки рабочей арматуры ригеля, плиты и сеток косвенного армирования.
3. Сварные соединения выполнять ручной электродуговой сваркой, электроды типа Э-42А по ГОСТ 9467-75.
4. Защитный слой бетона принят по наружной грани продольной арматуры.
5. Стыковку продольной арматуры выполнять по ГОСТ 14098-91, тип соединения С21-Рн.
6. Сетки С-1 составляются из двух взаимно перпендикулярных элементов.

Ведомость деталей

Поз.	Эскиз
Ск1	220; 560; 220; по н.г. L=1000
Ск2	220; 440; 220; по н.г. L=880
Ск3	220; 280; 220; по н.г. L=720
Ск4	220; 130; 220; по н.г. L=570
Х1	620; 520; 620; 520; по в.г. L=2280
Х2	480; 380; 480; 380; по в.г. L=1720
Х3	520; 420; 520; 420; по в.г. L=1880
Х4	410; 310; 410; 310; по в.г. L=1440
Шп1	200; 100; 100; по в.г. L=400
Шп2	150; 100; 100; по в.г. L=350

Таблица размеров накладок

Марка эл-та	dн	L	вес
	мм.		кг.
Н1	32	320	2.01
Н2	28	280	1.35
Н3	25	250	0.96
Н4	22	220	0.66
Н5	20	200	0.49

Спецификация элементов

Поз.	Обозначение	Наименование	Кол.	Масса ед.кг	Примечание
		Колонна Км-1.1			1589.59
Х1*	ГОСТ 34028-2016(214-210-0101-0002)	Ф 8 А 240 L= 2280	55	0.90	49.48
Х2*	ГОСТ 34028-2016(214-210-0101-0002)	Ф 8 А 240 L= 1720	55	0.68	37.33
Х3*	ГОСТ 34028-2016(214-210-0101-0002)	Ф 8 А 240 L= 1880	67	0.74	49.70
Х4*	ГОСТ 34028-2016(214-210-0101-0002)	Ф 8 А 240 L= 1440	67	0.57	38.07
Шп1*	ГОСТ 34028-2016(214-210-0101-0002)	Ф 8 А 240 L= 400	220	0.16	34.72
Шп2*	ГОСТ 34028-2016(214-210-0101-0002)	Ф 8 А 240 L= 350	268	0.14	37.01
Ск1*	ГОСТ 34028-2016(214-210-0502-0003)	Ф 16 А500С L= 1000	2	1.58	3.16
Ск2*	ГОСТ 34028-2016(214-210-0502-0003)	Ф 16 А500С L= 880	2	1.39	2.78
Ск3*	ГОСТ 34028-2016(214-210-0502-0003)	Ф 16 А500С L= 720	2	1.14	2.27
Ск4*	ГОСТ 34028-2016(214-210-0502-0003)	Ф 16 А500С L= 570	2	0.90	1.80
1	ГОСТ 34028-2016(214-210-0502-0008)	Ф 28 А500С L= 4270	16	20.64	330.24
Н2	ГОСТ 34028-2016(214-210-0502-0008)	Ф 28 А500С L= 280	64	1.35	86.62
2	ГОСТ 34028-2016(214-210-0502-0007)	Ф 25 А500С L= 3900	8	15.03	120.22
3	ГОСТ 34028-2016(214-210-0502-0007)	Ф 25 А500С L= 4000	8	15.41	123.31
Н3	ГОСТ 34028-2016(214-210-0502-0007)	Ф 25 А500С L= 250	32	0.96	30.83
4	ГОСТ 34028-2016(214-210-0502-0006)	Ф 22 А500С L= 3900	16	11.64	186.20
Н4	ГОСТ 34028-2016(214-210-0502-0006)	Ф 22 А500С L= 220	32	0.66	21.01
5	ГОСТ 34028-2016(214-210-0502-0005)	Ф 20 А500С L= 5680	8	14.01	112.06
6	ГОСТ 34028-2016(214-210-0502-0005)	Ф 20 А500С L= 5080	8	12.53	100.22
7	ГОСТ 34028-2016(214-210-0502-0003)	Ф 16 А500С L= 6800	8	10.73	85.86
8	ГОСТ 34028-2016(214-210-0502-0003)	Ф 16 А500С L= 5400	8	8.52	68.18
С1	данные лист	Сетка С1	8	4.22	33.74
С2	данные лист	Сетка С2	12	2.90	34.77
		Материалы:			
	(212-101-0901)	Класс бетона С 20/25 (В25), м³			5.49
		Сетка С1			
10	ГОСТ 34028-2016(214-210-0501-0005)	Ф 10 А500С L= 570	12	0.35	4.22
		Сетка С2			
11	ГОСТ 34028-2016(214-210-0501-0005)	Ф 10 А500С L= 470	10	0.29	2.90

Позиции со "*" см. "Ведомость деталей" см. на данном листе.


Ведомость расхода стали, кг

Марка элемента	Изделия арматурные										Всего
	Арматура класса										
	А240			А500С							
	ГОСТ 34028-2016(214-210-0101)			ГОСТ 34028-2016(214-210-0502)							
	Ф6	Ф8	Итого	Ф10	Ф16	Ф20	Ф22	Ф25	Ф28	Итого	
Колонна Км-1.1	0.00	246.32	246.32	68.51	164.05	212.29	207.21	274.36	416.85	1343.27	1589.59


							65П-АИП-2024-1-КЖ
							Строительство многопрофильной больницы на 250 коек с онкологическим центром и поликлиникой на 350 посещений, по адресу: Медеуский район, г. Алматы
Изм.	Кол.уч	Лист	N док.	Подп.	Дата		
ГКП		Курал М				"Блок 1 Секция 1"	Стадия: РП; Лист: 4.1; Листов:
Проверил		Кыдырбай А				Колонна Км-1.1	АстанаИнжПроект
Разраб.		Ауез Б					
Н.контроль		Ешенкулова					

Формат А2


Колонна Км-1.2

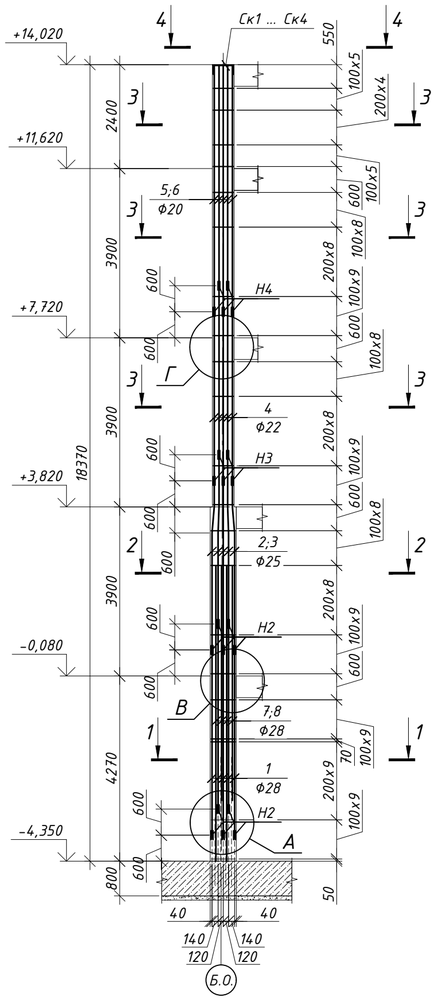


Разрез 1 - 1

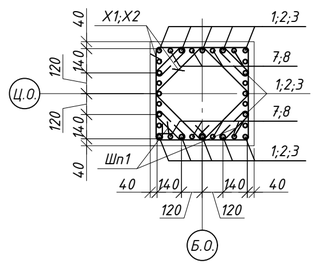


Разрез 2 - 2

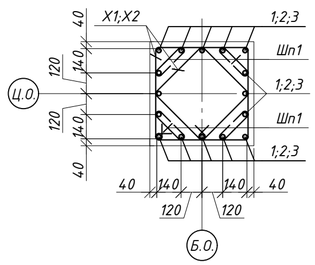


Разрез 3 - 3

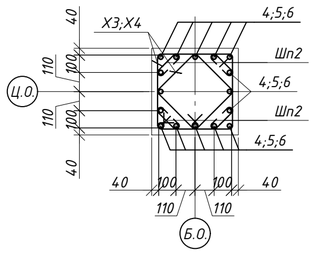


Разрез 4 - 4

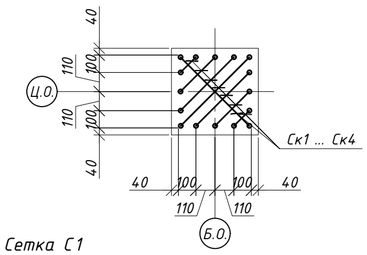


Сетка С1

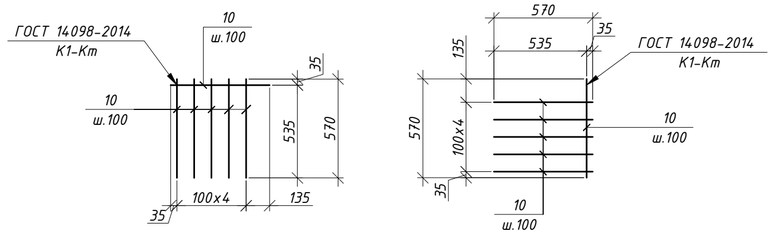


Сетка С2

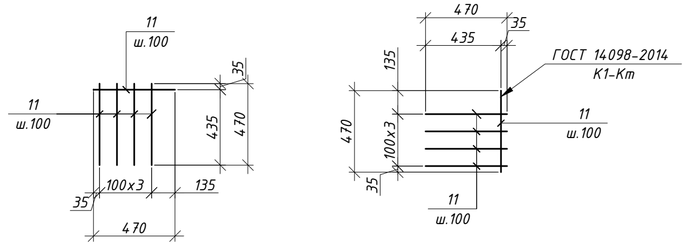


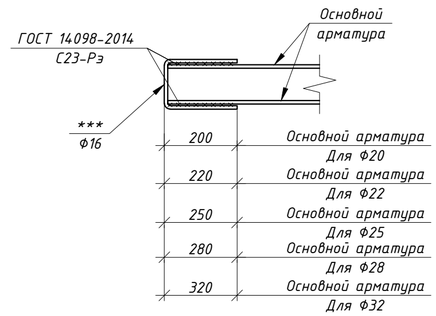


Узел расположения сетки С1;

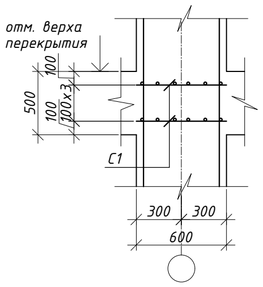

Узел расположения сетки С2

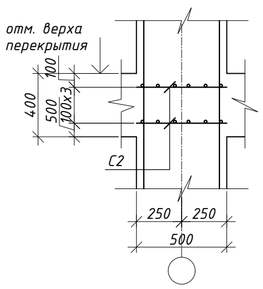

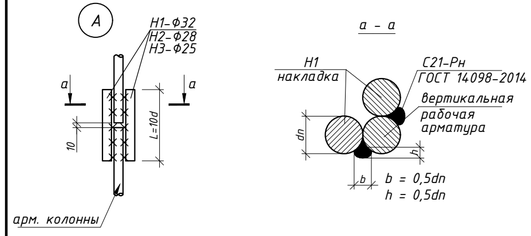

Ведомость деталей

Поз.	Эскиз
Ск1	220 / 560 / 220 — по н.г. — L=1000
Ск2	220 / 440 / 220 — по н.г. — L=880
Ск3	220 / 280 / 220 — по н.г. — L=720
Ск4	220 / 130 / 220 — по н.г. — L=570
Х1	620 / 520 / 620 — по в.г. — L=2280
Х2	480 / 380 / 480 — по в.г. — L=1720
Х3	520 / 420 / 520 — по в.г. — L=1880
Х4	410 / 310 / 410 — по в.г. — L=1440
Шп1	200 / 100 / 100 — по в.г. — L=400
Шп2	150 / 100 / 100 — по в.г. — L=350

Таблица размеров накладок

Марка эл-та	dн	L	вес
	мм.		кг.
Н1	32	320	2.01
Н2	28	280	1.35
Н3	25	250	0.96
Н4	22	220	0.66
Н5	20	200	0.49

Спецификация элементов

Поз.	Обозначение	Наименование	Кол.	Масса ед.кг	Примечание
		Колонна Км-1.2			1589.59
Х1*	ГОСТ 34028-2016(214-210-0101-0002)	Ф 8 А 240 L= 2280	55	0.90	49.48
Х2*	ГОСТ 34028-2016(214-210-0101-0002)	Ф 8 А 240 L= 1720	55	0.68	37.33
Х3*	ГОСТ 34028-2016(214-210-0101-0002)	Ф 8 А 240 L= 1880	67	0.74	49.70
Х4*	ГОСТ 34028-2016(214-210-0101-0002)	Ф 8 А 240 L= 1440	67	0.57	38.07
Шп1*	ГОСТ 34028-2016(214-210-0101-0002)	Ф 8 А 240 L= 400	220	0.16	34.72
Шп2*	ГОСТ 34028-2016(214-210-0101-0002)	Ф 8 А 240 L= 350	268	0.14	37.01
Ск1*	ГОСТ 34028-2016(214-210-0502-0003)	Ф 16 А500С L= 1000	2	1.58	3.16
Ск2*	ГОСТ 34028-2016(214-210-0502-0003)	Ф 16 А500С L= 880	2	1.39	2.78
Ск3*	ГОСТ 34028-2016(214-210-0502-0003)	Ф 16 А500С L= 720	2	1.14	2.27
Ск4*	ГОСТ 34028-2016(214-210-0502-0003)	Ф 16 А500С L= 570	2	0.90	1.80
1	ГОСТ 34028-2016(214-210-0502-0008)	Ф 28 А500С L= 4270	16	20.64	330.24
Н2	ГОСТ 34028-2016(214-210-0502-0008)	Ф 28 А500С L= 280	64	1.35	86.62
2	ГОСТ 34028-2016(214-210-0502-0007)	Ф 25 А500С L= 3900	8	15.03	120.22
3	ГОСТ 34028-2016(214-210-0502-0007)	Ф 25 А500С L= 4000	8	15.41	123.31
Н3	ГОСТ 34028-2016(214-210-0502-0007)	Ф 25 А500С L= 250	32	0.96	30.83
4	ГОСТ 34028-2016(214-210-0502-0007)	Ф 22 А500С L= 3900	16	11.64	186.20
Н4	ГОСТ 34028-2016(214-210-0502-0007)	Ф 22 А500С L= 220	32	0.66	21.01
5	ГОСТ 34028-2016(214-210-0502-0005)	Ф 20 А500С L= 5680	8	14.01	112.06
6	ГОСТ 34028-2016(214-210-0502-0005)	Ф 20 А500С L= 5080	8	12.53	100.22
7	ГОСТ 34028-2016(214-210-0502-0003)	Ф 16 А500С L= 6800	8	10.73	85.86
8	ГОСТ 34028-2016(214-210-0502-0003)	Ф 16 А500С L= 5400	8	8.52	68.18
С1	данные лист	Сетка С1	8	4.22	33.74
С2	данные лист	Сетка С2	12	2.90	34.77
		Материалы:			
	(212-101-0901)	Класс бетона С 20/25 (В25), м³			5.49
		Сетка С1			
10	ГОСТ 34028-2016(214-210-0501-0005)	Ф 10 А500С L= 570	12	0.35	4.22
		Сетка С2			
11	ГОСТ 34028-2016(214-210-0501-0005)	Ф 10 А500С L= 470	10	0.29	2.90

Позиции со "*" см. "Ведомость деталей" см. на данном листе.

Ведомость расхода стали, кг


Марка элемента	Изделия арматурные										Всего
	Арматура класса										
	А240			А500С							
	ГОСТ 34028-2016(214-210-0101)			ГОСТ 34028-2016(214-210-0502)							
	Ф6	Ф8	Итого	Ф10	Ф16	Ф20	Ф22	Ф25	Ф28	Итого	
Колонна Км-1.2	0.00	246.32	246.32	68.51	164.05	212.29	207.21	274.36	416.85	1343.27	1589.59

1. Схему расположения монолитных колонн см. листы КЖ-2.1; .... 2.7.
2. Бетонирование колонн в местах примыкания ригелей и монолитной плиты вести после установки рабочей арматуры ригеля, плиты и сеток косвенного армирования.
3. Сварные соединения выполнять ручной электродуговой сваркой, электроды типа Э-42А по ГОСТ 9467-75.
4. Защитный слой бетона принят по наружной грани продольной арматуры.
5. Стыковку продольной арматуры выполнять по ГОСТ 14098-91, тип соединения С21-Рн.
6. Сетки С-1 составляются из двух взаимно перпендикулярных элементов.


Изм.	Кол.уч.	Лист	N док.	Подп.	Дата	65П-АИП-2024-1-КЖ		
						Строительство многопрофильной больницы на 250 коек с онкологическим центром и поликлиникой на 350 посещений, по адресу: Медеуский район, г. Алматы		
ГКП		Курал М				"Блок 1 Секция 1"	Стадия: РП	Лист: 4.2 / Листов:
Проверил		Кыдырбай А						
Разраб.		Ауез Б				Колонна Км-1.2	АстанаИнжПроект	
Н.контроль		Ешенкулова						

Формат А2


Колонна Км-2.1

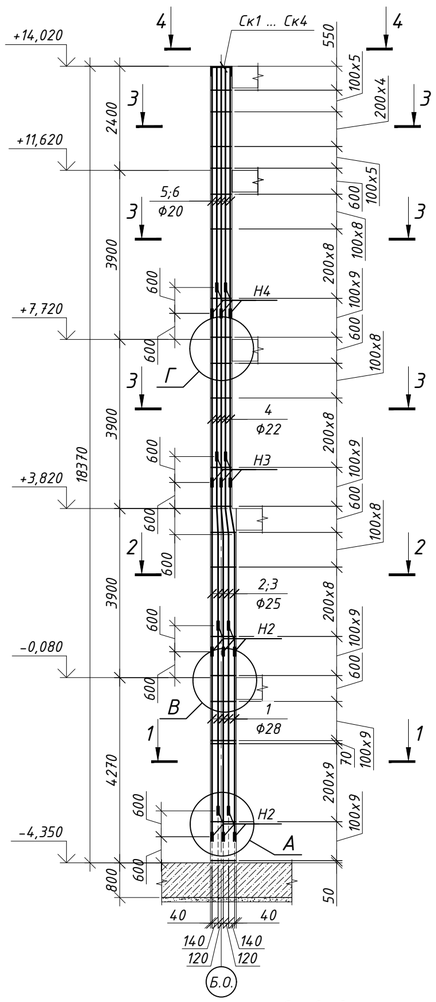


Разрез 1 - 1

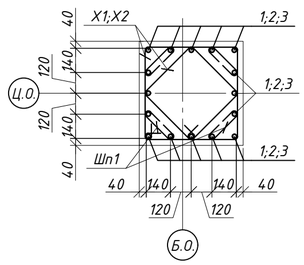


Разрез 2 - 2

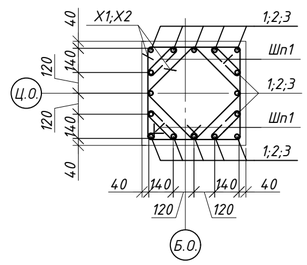


Разрез 3 - 3

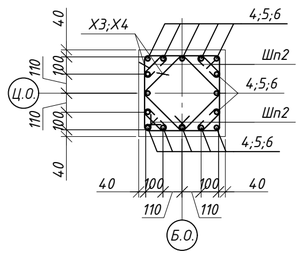


Разрез 4 - 4

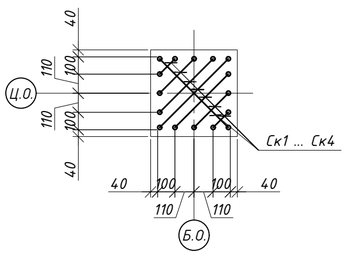



Сетка С1

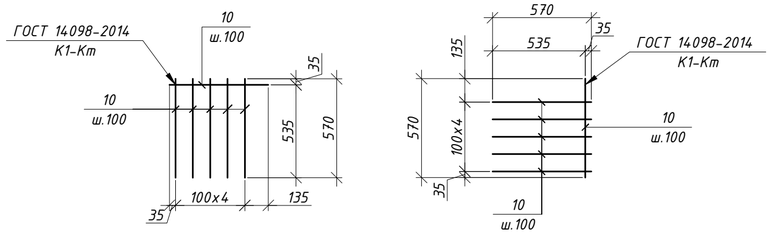


Сетка С2

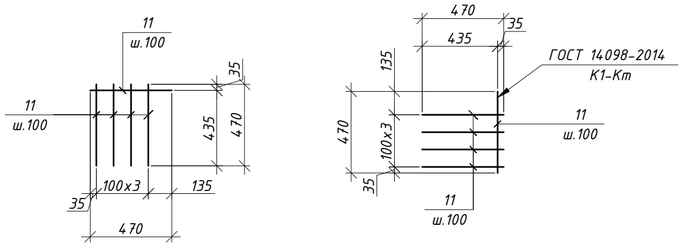


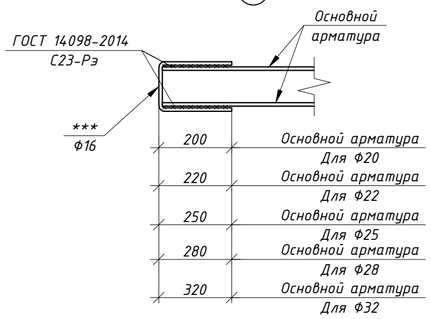

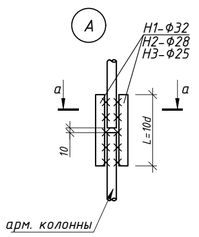


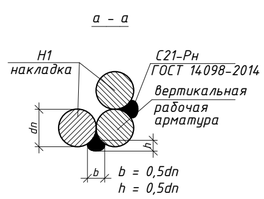

Узел расположения сетки С1;

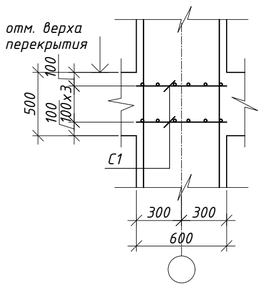

Узел расположения сетки С2

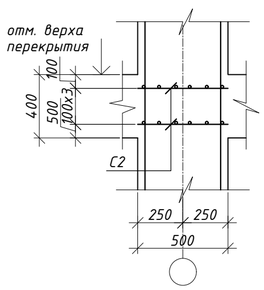

Ведомость деталей

Поз.	Эскиз
Ск1	220; 560; 220; по н.г. L=1000
Ск2	220; 440; 220; по н.г. L=880
Ск3	220; 280; 220; по н.г. L=720
Ск4	220; 130; 220; по н.г. L=570
Х1	620; 520; 620; 520; по в.г. L=2280
Х2	480; 380; 480; 380; по в.г. L=1720
Х3	520; 420; 520; 420; по в.г. L=1880
Х4	410; 310; 410; 310; по в.г. L=1440
Шп1	200; 100; 100; по в.г. L=400
Шп2	150; 100; 100; по в.г. L=350

Таблица размеров накладок

Марка эл-та	dн мм.	L мм.	вес кг.
Н1	32	320	2.01
Н2	28	280	1.35
Н3	25	250	0.96
Н4	22	220	0.66
Н5	20	200	0.49

Спецификация элементов

Поз.	Обозначение	Наименование	Кол.	Масса ед.кг	Примечание
		Колонна Км-2.1			1435.54
Х1*	ГОСТ 34028-2016(214-210-0101-0002)	Ф 8 А 240 L= 2280	55	0.90	49.48
Х2*	ГОСТ 34028-2016(214-210-0101-0002)	Ф 8 А 240 L= 1720	55	0.68	37.33
Х3*	ГОСТ 34028-2016(214-210-0101-0002)	Ф 8 А 240 L= 1880	67	0.74	49.70
Х4*	ГОСТ 34028-2016(214-210-0101-0002)	Ф 8 А 240 L= 1440	67	0.57	38.07
Шп1*	ГОСТ 34028-2016(214-210-0101-0002)	Ф 8 А 240 L= 400	220	0.16	34.72
Шп2*	ГОСТ 34028-2016(214-210-0101-0002)	Ф 8 А 240 L= 350	268	0.14	37.01
Ск1*	ГОСТ 34028-2016(214-210-0502-0003)	Ф 16 А500С L= 1000	2	1.58	3.16
Ск2*	ГОСТ 34028-2016(214-210-0502-0003)	Ф 16 А500С L= 880	2	1.39	2.78
Ск3*	ГОСТ 34028-2016(214-210-0502-0003)	Ф 16 А500С L= 720	2	1.14	2.27
Ск4*	ГОСТ 34028-2016(214-210-0502-0003)	Ф 16 А500С L= 570	2	0.90	1.80
1	ГОСТ 34028-2016(214-210-0502-0008)	Ф 28 А500С L= 4270	16	20.64	330.24
Н2	ГОСТ 34028-2016(214-210-0502-0008)	Ф 28 А500С L= 280	64	1.35	86.62
2	ГОСТ 34028-2016(214-210-0502-0007)	Ф 25 А500С L= 3900	8	15.03	120.22
3	ГОСТ 34028-2016(214-210-0502-0007)	Ф 25 А500С L= 4000	8	15.41	123.31
Н3	ГОСТ 34028-2016(214-210-0502-0007)	Ф 25 А500С L= 250	32	0.96	30.83
4	ГОСТ 34028-2016(214-210-0502-0006)	Ф 22 А500С L= 3900	16	11.64	186.20
Н4	ГОСТ 34028-2016(214-210-0502-0006)	Ф 22 А500С L= 220	32	0.66	21.01
5	ГОСТ 34028-2016(214-210-0502-0005)	Ф 20 А500С L= 5680	8	14.01	112.06
6	ГОСТ 34028-2016(214-210-0502-0005)	Ф 20 А500С L= 5080	8	12.53	100.22
С1	данные лист	Сетка С1	8	4.22	33.74
С2	данные лист	Сетка С2	12	2.90	34.77
		Материалы:			
		Класс бетона С 20/25 (В25), м³			5.49
		Сетка С1			
10	ГОСТ 34028-2016(214-210-0501-0005)	Ф 10 А500С L= 570	12	0.35	4.22
		Сетка С2			
11	ГОСТ 34028-2016(214-210-0501-0005)	Ф 10 А500С L= 470	10	0.29	2.90

Позиции со "*" см. "Ведомость деталей" см. на данном листе.

Ведомость расхода стали, кг


Марка элемента	Изделия арматурные										Всего
	Арматура класса										
	А240			А500С							
	ГОСТ 34028-2016(214-210-0101)			ГОСТ 34028-2016(214-210-0502)							
	Ф6	Ф8	Итого	Ф10	Ф16	Ф20	Ф22	Ф25	Ф28	Итого	
Колонна Км-2.1	0.00	246.32	246.32	68.51	10.01	212.29	207.21	274.36	416.85	1189.23	1435.54

1. Схему расположения монолитных колонн см. листы КЖ-2.1; .... 2.7.
2. Бетонирование колонн в местах примыкания ригелей и монолитной плиты вести после установки рабочей арматуры ригеля, плиты и сеток косвенного армирования.
3. Сварные соединения выполнять ручной электродуговой сваркой, электроды типа Э-42А по ГОСТ 9467-75.
4. Защитный слой бетона принят по наружной грани продольной арматуры.
5. Стыковку продольной арматуры выполнять по ГОСТ 14098-91, тип соединения С21-Рн.
6. Сетки С-1 составляются из двух взаимно перпендикулярных элементов.


Изм.	Кол.уч	Лист	N док.	Подп.	Дата	65П-АИП-2024-1-КЖ		
						Строительство многопрофильной больницы на 250 коек с онкологическим центром и поликлиникой на 350 посещений, по адресу: Медеуский район, г. Алматы		
ГКП		Курал М				"Блок 1 Секция 1"	Стадия: РП	Лист: 4.3
Проверил		Кыдырбай А						Листов:
Разраб.		Ауез Б				Колонна Км-2.1	АстанаИнжПроект	
Н.контроль		Ешенкулова						

Формат А2


Колонна Км-2.2

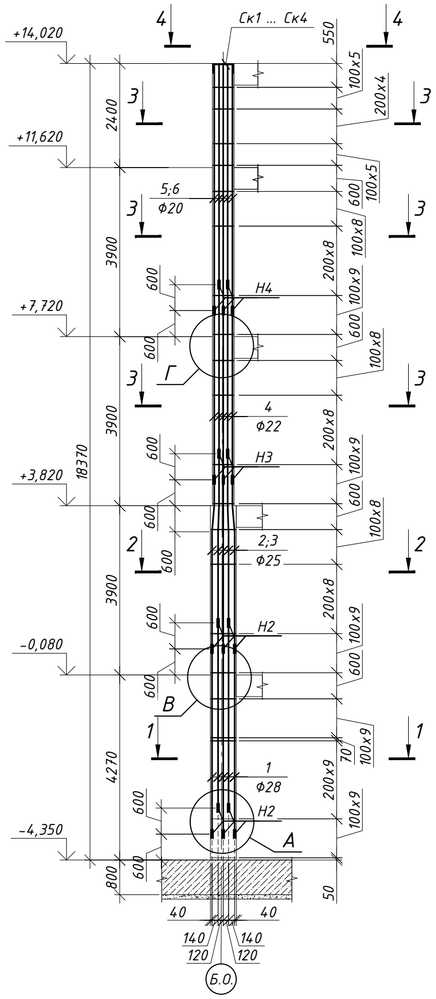


Разрез 1 - 1

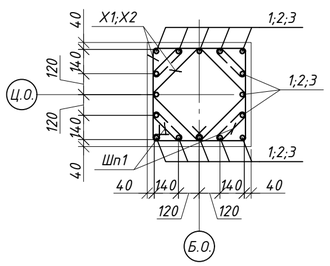


Разрез 2 - 2

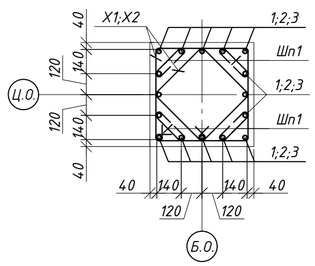


Разрез 3 - 3

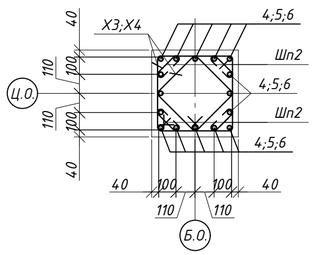


Разрез 4 - 4

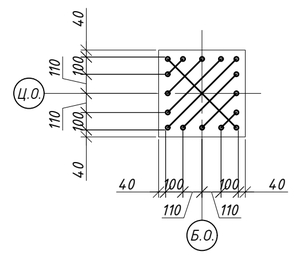

Сетка С1

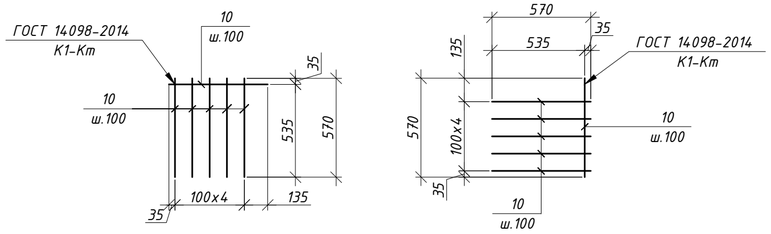

Сетка С2

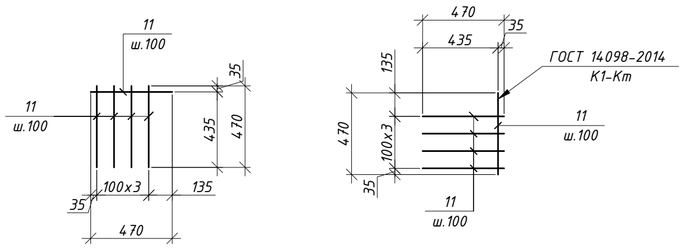

Ведомость деталей

Поз.	Эскиз
Ск1	220 / 560 / 220 / по н.г. L=1000
Ск2	220 / 440 / 220 / по н.г. L=880
Ск3	220 / 280 / 220 / по н.г. L=720
Ск4	220 / 130 / 220 / по н.г. L=570
Х1	620 / 520 / 520 / 620 / по в.г. L=2280
Х2	480 / 380 / 380 / 480 / по в.г. L=1720
Х3	520 / 420 / 420 / 520 / по в.г. L=1880
Х4	410 / 310 / 310 / 410 / по в.г. L=1440
Шп1	200 / 100 / 100 / по в.г. L=400
Шп2	150 / 100 / 100 / по в.г. L=350

Таблица размеров накладок

Марка эл-та	dн	L	вес
	мм.		кг.
Н1	32	320	2.01
Н2	28	280	1.35
Н3	25	250	0.96
Н4	22	220	0.66
Н5	20	200	0.49

Спецификация элементов


Поз.	Обозначение	Наименование	Кол.	Масса ед.кг	Примечание
		Колонна Км-2.2			1435.54
Х1*	ГОСТ 34028-2016(214-210-0101-0002)	Ф 8 А 240 L= 2280	55	0.90	49.48
Х2*	ГОСТ 34028-2016(214-210-0101-0002)	Ф 8 А 240 L= 1720	55	0.68	37.33
Х3*	ГОСТ 34028-2016(214-210-0101-0002)	Ф 8 А 240 L= 1880	67	0.74	49.70
Х4*	ГОСТ 34028-2016(214-210-0101-0002)	Ф 8 А 240 L= 1440	67	0.57	38.07
Шп1*	ГОСТ 34028-2016(214-210-0101-0002)	Ф 8 А 240 L= 400	220	0.16	34.72
Шп2*	ГОСТ 34028-2016(214-210-0101-0002)	Ф 8 А 240 L= 350	268	0.14	37.01
Ск1*	ГОСТ 34028-2016(214-210-0502-0003)	Ф 16 А500С L= 1000	2	1.58	3.16
Ск2*	ГОСТ 34028-2016(214-210-0502-0003)	Ф 16 А500С L= 880	2	1.39	2.78
Ск3*	ГОСТ 34028-2016(214-210-0502-0003)	Ф 16 А500С L= 720	2	1.14	2.27
Ск4*	ГОСТ 34028-2016(214-210-0502-0003)	Ф 16 А500С L= 570	2	0.90	1.80
1	ГОСТ 34028-2016(214-210-0502-0008)	Ф 28 А500С L= 4270	16	20.64	330.24
Н2	ГОСТ 34028-2016(214-210-0502-0008)	Ф 28 А500С L= 280	64	1.35	86.62
2	ГОСТ 34028-2016(214-210-0502-0007)	Ф 25 А500С L= 3900	8	15.03	120.22
3	ГОСТ 34028-2016(214-210-0502-0007)	Ф 25 А500С L= 4000	8	15.41	123.31
Н3	ГОСТ 34028-2016(214-210-0502-0007)	Ф 25 А500С L= 250	32	0.96	30.83
4	ГОСТ 34028-2016(214-210-0502-0006)	Ф 22 А500С L= 3900	16	11.64	186.20
Н4	ГОСТ 34028-2016(214-210-0502-0006)	Ф 22 А500С L= 220	32	0.66	21.01
5	ГОСТ 34028-2016(214-210-0502-0005)	Ф 20 А500С L= 5680	8	14.01	112.06
6	ГОСТ 34028-2016(214-210-0502-0005)	Ф 20 А500С L= 5080	8	12.53	100.22
С1	данные лист	Сетка С1	8	4.22	33.74
С2	данные лист	Сетка С2	12	2.90	34.77
		Материалы:			
	(212-101-0901)	Класс бетона С 20/25 (В25), м³			5.49
		Сетка С1			
10	ГОСТ 34028-2016(214-210-0501-0005)	Ф 10 А500С L= 570	12	0.35	4.22
		Сетка С2			
11	ГОСТ 34028-2016(214-210-0501-0005)	Ф 10 А500С L= 470	10	0.29	2.90

Позиции со "*" см. "Ведомость деталей" см. на данном листе.


Ведомость расхода стали, кг


Марка элемента	Изделия арматурные										Всего
	Арматура класса										
	А240			А500С							
	ГОСТ 34028-2016(214-210-0101)			ГОСТ 34028-2016(214-210-0502)							
	Ф6	Ф8	Итого	Ф10	Ф16	Ф20	Ф22	Ф25	Ф28	Итого	
Колонна Км-2.2	0.00	246.32	246.32	68.51	10.01	212.29	207.21	274.36	416.85	1189.23	1435.54

Узел расположения сетки С1;

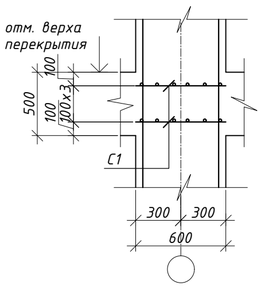

Узел расположения сетки С2

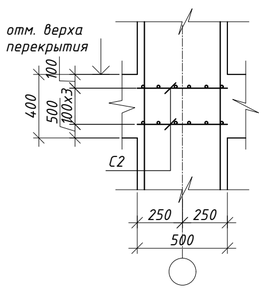

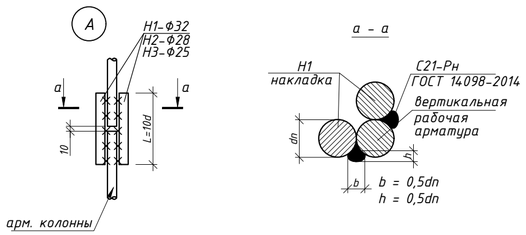


1. Схему расположения монолитных колонн см. листы КЖ-2.1; .... 2.7.
2. Бетонирование колонн в местах примыкания ригелей и монолитной плиты вести после установки рабочей арматуры ригеля, плиты и сеток косвенного армирования.
3. Сварные соединения выполнять ручной электродуговой сваркой, электроды типа Э-42А по ГОСТ 9467-75.
4. Защитный слой бетона принят по наружной грани продольной арматуры.
5. Стыковку продольной арматуры выполнять по ГОСТ 14098-91, тип соединения С21-Рн.
6. Сетки С-1 составляются из двух взаимно перпендикулярных элементов.


Изм.	Кол.уч.	Лист	N док.	Подп.	Дата	65П-АИП-2024-1-КЖ		
						Строительство многопрофильной больницы на 250 коек с онкологическим центром и поликлиникой на 350 посещений, по адресу: Медеуский район, г. Алматы		
ГКП		Курал М				"Блок 1 Секция 1"	Стадия: РП	Лист: 4.4
Проверил		Кыдырбай А						Листов:
Разраб.		Ауез Б				Колонна Км-2.2	АстанаИнжПроект	
Н.контроль		Ешенкулова						

Формат А2


Колонна Км-3.1

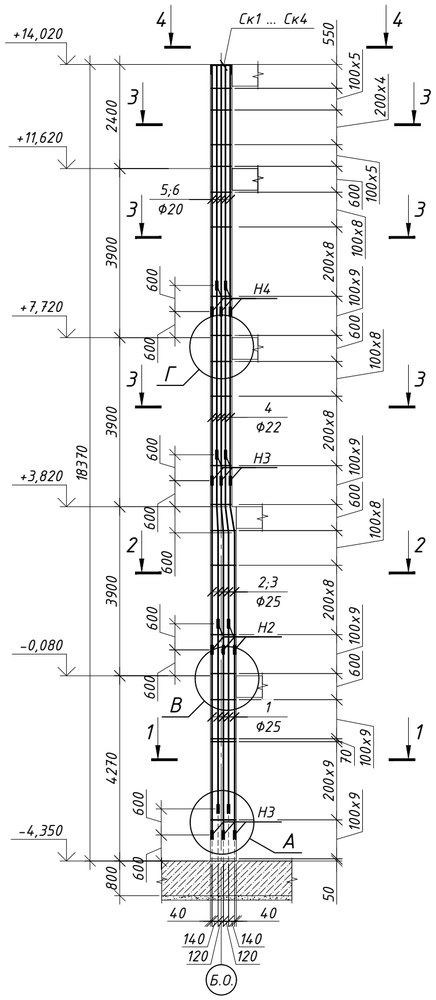


Разрез 1 - 1

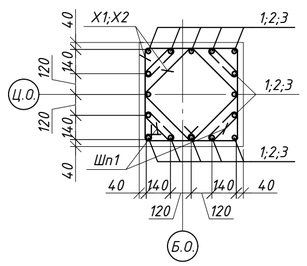


Разрез 2 - 2

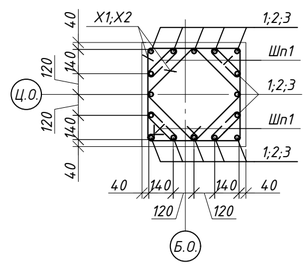


Разрез 3 - 3

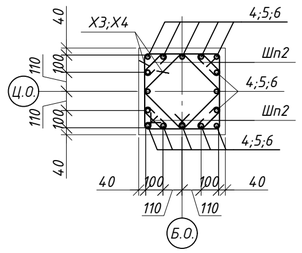


Разрез 4 - 4

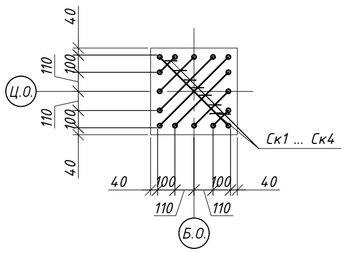

Сетка С1

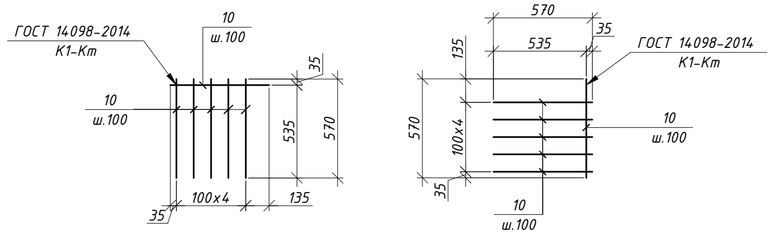

Сетка С2

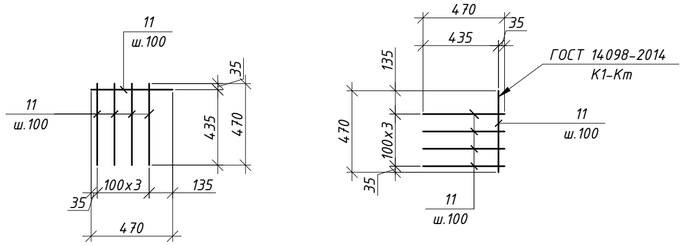

Ведомость деталей


Поз.	Эскиз
Ск1	220 / 560 / 220 по н.г. L=1000
Ск2	220 / 440 / 220 по н.г. L=880
Ск3	220 / 280 / 220 по н.г. L=720
Ск4	220 / 130 / 220 по н.г. L=570
Х1	620 / 520 / 520 / 620 по в.г. L=2280
Х2	480 / 380 / 380 / 480 по в.г. L=1720
Х3	520 / 420 / 420 / 520 по в.г. L=1880
Х4	410 / 310 / 310 / 410 по в.г. L=1440
Шп1	200 / 100 / 100 по в.г. L=400
Шп2	150 / 100 / 100 по в.г. L=350

Спецификация элементов


Поз.	Обозначение	Наименование	Кол.	Масса ед.кг	Примечание
		Колонна Км-3.1			1343.60
Х1*	ГОСТ 34028-2016(214-210-0101-0002)	Ф 8 А 240 L= 2280	55	0.90	49.48
Х2*	ГОСТ 34028-2016(214-210-0101-0002)	Ф 8 А 240 L= 1720	55	0.68	37.33
Х3*	ГОСТ 34028-2016(214-210-0101-0002)	Ф 8 А 240 L= 1880	67	0.74	49.70
Х4*	ГОСТ 34028-2016(214-210-0101-0002)	Ф 8 А 240 L= 1440	67	0.57	38.07
Шп1*	ГОСТ 34028-2016(214-210-0101-0002)	Ф 8 А 240 L= 400	220	0.16	34.72
Шп2*	ГОСТ 34028-2016(214-210-0101-0002)	Ф 8 А 240 L= 350	268	0.14	37.01
Ск1*	ГОСТ 34028-2016(214-210-0502-0003)	Ф 16 А500С L= 1000	2	1.58	3.16
Ск2*	ГОСТ 34028-2016(214-210-0502-0003)	Ф 16 А500С L= 880	2	1.39	2.78
Ск3*	ГОСТ 34028-2016(214-210-0502-0003)	Ф 16 А500С L= 720	2	1.14	2.27
Ск4*	ГОСТ 34028-2016(214-210-0502-0003)	Ф 16 А500С L= 570	2	0.90	1.80
1	ГОСТ 34028-2016(214-210-0502-0007)	Ф 25 А500С L= 4270	16	16.45	263.26
2	ГОСТ 34028-2016(214-210-0502-0007)	Ф 25 А500С L= 3900	8	15.03	120.22
3	ГОСТ 34028-2016(214-210-0502-0007)	Ф 25 А500С L= 4000	8	15.41	123.31
Н3	ГОСТ 34028-2016(214-210-0502-0007)	Ф 25 А500С L= 250	96	0.96	92.48
4	ГОСТ 34028-2016(214-210-0502-0006)	Ф 22 А500С L= 3900	16	11.64	186.20
Н4	ГОСТ 34028-2016(214-210-0502-0006)	Ф 22 А500С L= 220	32	0.66	21.01
5	ГОСТ 34028-2016(214-210-0502-0005)	Ф 20 А500С L= 5680	8	14.01	112.06
6	ГОСТ 34028-2016(214-210-0502-0005)	Ф 20 А500С L= 5080	8	12.53	100.22
С1	данные лист	Сетка С1	8	4.22	33.74
С2	данные лист	Сетка С2	12	2.90	34.77
		Материалы:			
	(212-101-0901)	Класс бетона С 20/25 (В25), м³			5.49
		Сетка С1			
10	ГОСТ 34028-2016(214-210-0501-0005)	Ф 10 А500С L= 570	12	0.35	4.22
		Сетка С2			
11	ГОСТ 34028-2016(214-210-0501-0005)	Ф 10 А500С L= 470	10	0.29	2.90

Позиции со "*" см. "Ведомость деталей" см. на данном листе.

Узел расположения сетки С1;

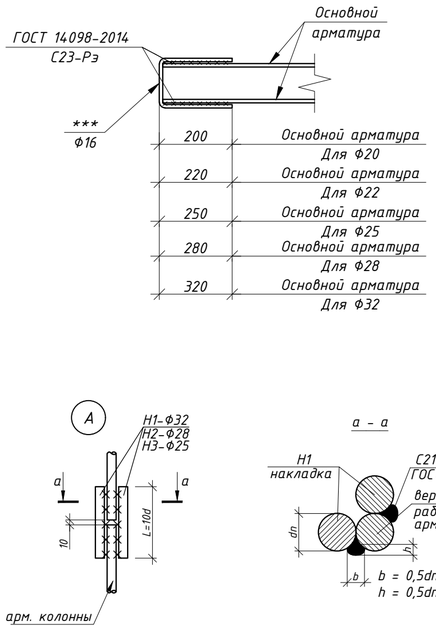

Узел расположения сетки С2

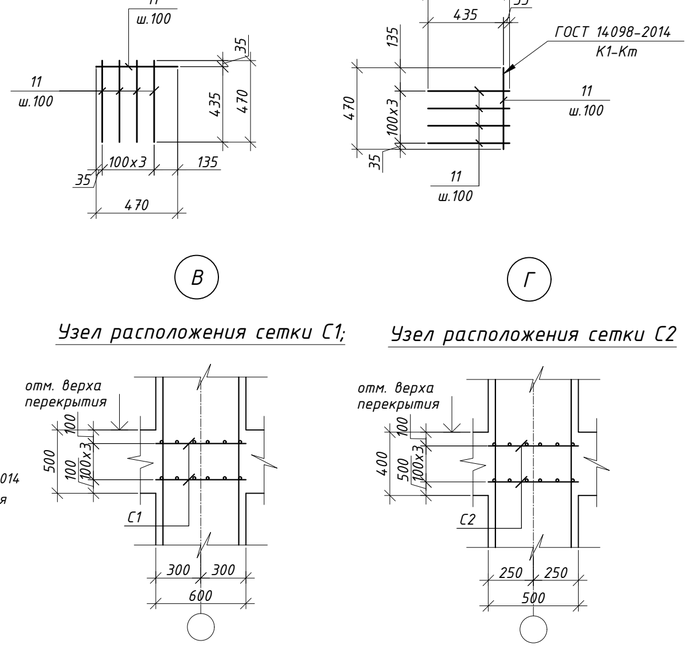

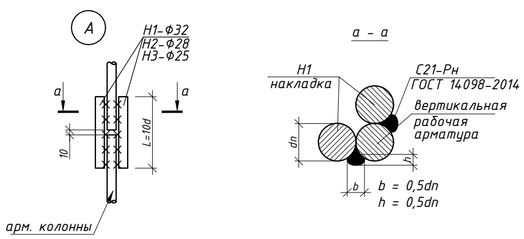


Таблица размеров накладок

Марка эл-та	dн мм.	L мм.	вес кг.
Н1	32	320	2.01
Н2	28	280	1.35
Н3	25	250	0.96
Н4	22	220	0.66
Н5	20	200	0.49

Ведомость расхода стали, кг


Марка элемента	Изделия арматурные									Всего
	Арматура класса									
	А240 ГОСТ 34028-2016(214-210-0101)			А500С ГОСТ 34028-2016(214-210-0502)						
	Ф6	Ф8	Итого	Ф10	Ф16	Ф20	Ф22	Ф25	Итого	
Колонна Км-3.1	0.00	246.32	246.32	68.51	10.01	212.29	207.21	599.27	1097.29	1343.60

1. Схему расположения монолитных колонн см. листы КЖ-2.1; .... 2.7.
2. Бетонирование колонн в местах примыкания ригелей и монолитной плиты вести после установки рабочей арматуры ригеля, плиты и сеток косвенного армирования.
3. Сварные соединения выполнять ручной электродуговой сваркой, электроды типа Э-42А по ГОСТ 9467-75.
4. Защитный слой бетона принят по наружной грани продольной арматуры.
5. Стыковку продольной арматуры выполнять по ГОСТ 14098-91, тип соединения С21-Рн.
6. Сетки С-1 составляются из двух взаимно перпендикулярных элементов.


Изм.	Кол.уч.	Лист	N док.	Подп.	Дата	65П-АИП-2024-1-КЖ		
						Строительство многопрофильной больницы на 250 коек с онкологическим центром и поликлиникой на 350 посещений, по адресу: Медеуский район, г. Алматы		
ГКП		Курал М				"Блок 1 Секция 1"	Стадия: РП	Лист: 4.5 / Листов:
Проверил		Кыдырбай А						
Разраб.		Ауез Б				Колонна Км-3.1	АстанаИнжПроект	
Н.контроль		Ешенкулова						

Формат А2


Колонна Км-4.1

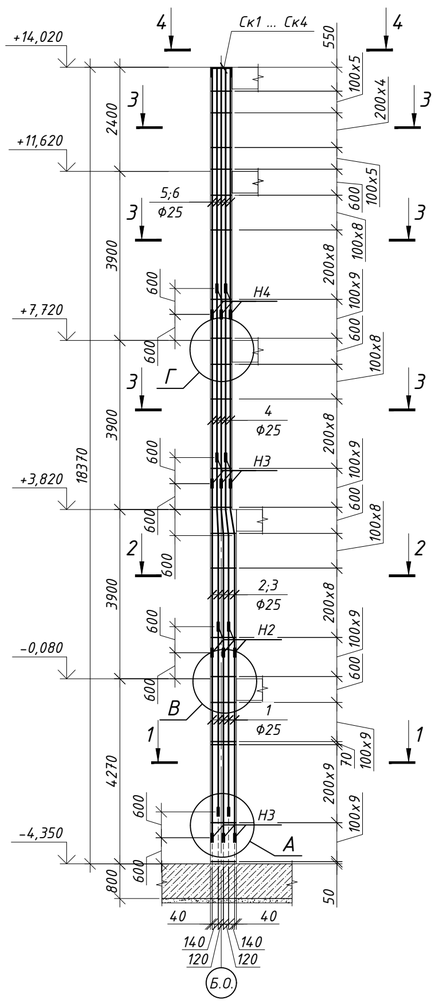


Разрез 1 - 1

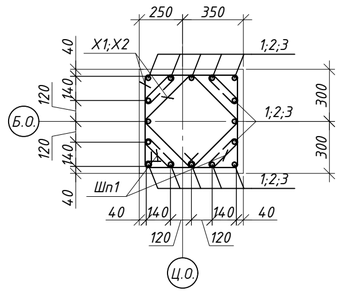


Разрез 2 - 2

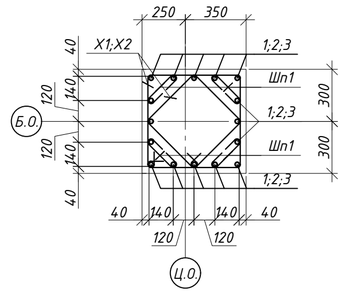


Разрез 3 - 3

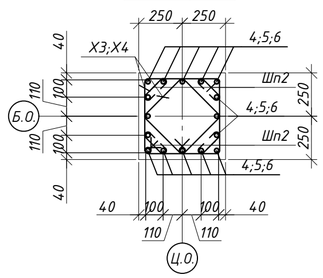


Разрез 4 - 4

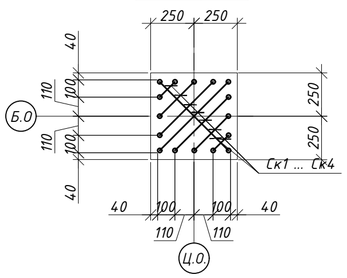

Сетка С1

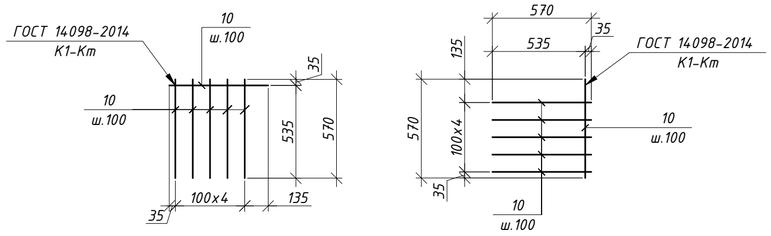

Сетка С2

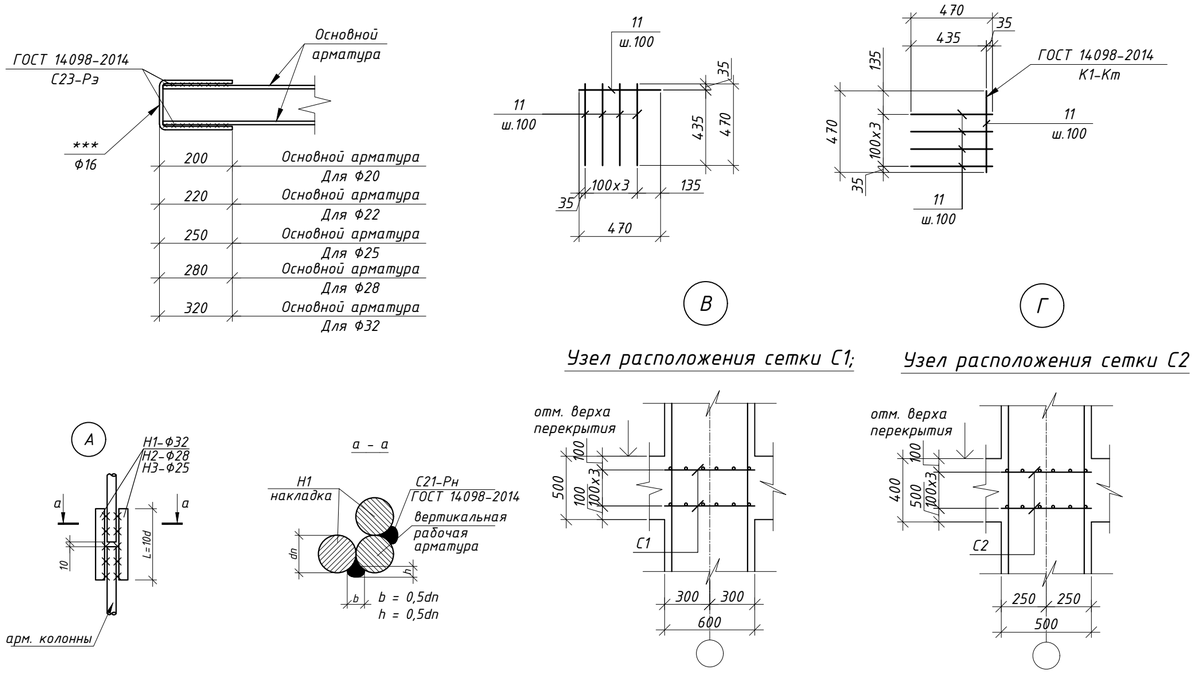

Узел расположения сетки С1;

Узел расположения сетки С2

Ведомость деталей

Поз.	Эскиз
Ск1	220 / 560 / 220 / по н.г. / L=1000
Ск2	220 / 440 / 220 / по н.г. / L=880
Ск3	220 / 280 / 220 / по н.г. / L=720
Ск4	220 / 130 / 220 / по н.г. / L=570
Х1	620 / 520 / 620 / 520 / по в.г. / L=2280
Х2	480 / 380 / 480 / 380 / по в.г. / L=1720
Х3	520 / 420 / 520 / 420 / по в.г. / L=1880
Х4	410 / 310 / 410 / 310 / по в.г. / L=1440
Шп1	200 / 100 / 100 / по в.г. / L=400
Шп2	150 / 100 / 100 / по в.г. / L=350

Таблица размеров накладок

Марка эл-та	dн	L	вес
	мм.		кг.
Н1	32	320	2.01
Н2	28	280	1.35
Н3	25	250	0.96
Н4	22	220	0.66
Н5	20	200	0.49

Спецификация элементов

Поз.	Обозначение	Наименование	Кол.	Масса ед.кг	Примечание
		Колонна Км-4.1			1527.08
Х1*	ГОСТ 34028-2016(214-210-0101-0002)	Ф 8 А 240 L= 2280	55	0.90	49.48
Х2*	ГОСТ 34028-2016(214-210-0101-0002)	Ф 8 А 240 L= 1720	55	0.68	37.33
Х3*	ГОСТ 34028-2016(214-210-0101-0002)	Ф 8 А 240 L= 1880	67	0.74	49.70
Х4*	ГОСТ 34028-2016(214-210-0101-0002)	Ф 8 А 240 L= 1440	67	0.57	38.07
Шп1*	ГОСТ 34028-2016(214-210-0101-0002)	Ф 8 А 240 L= 400	220	0.16	34.72
Шп2*	ГОСТ 34028-2016(214-210-0101-0002)	Ф 8 А 240 L= 350	268	0.14	37.01
Ск1*	ГОСТ 34028-2016(214-210-0502-0003)	Ф 16 А500С L= 1000	2	1.58	3.16
Ск2*	ГОСТ 34028-2016(214-210-0502-0003)	Ф 16 А500С L= 880	2	1.39	2.78
Ск3*	ГОСТ 34028-2016(214-210-0502-0003)	Ф 16 А500С L= 720	2	1.14	2.27
Ск4*	ГОСТ 34028-2016(214-210-0502-0003)	Ф 16 А500С L= 570	2	0.90	1.80
1	ГОСТ 34028-2016(214-210-0502-0007)	Ф 25 А500С L= 4270	16	16.45	263.26
2	ГОСТ 34028-2016(214-210-0502-0007)	Ф 25 А500С L= 3900	8	15.03	120.22
3	ГОСТ 34028-2016(214-210-0502-0007)	Ф 25 А500С L= 4000	8	15.41	123.31
Н3	ГОСТ 34028-2016(214-210-0502-0007)	Ф 25 А500С L= 250	128	0.96	123.31
4	ГОСТ 34028-2016(214-210-0502-0007)	Ф 25 А500С L= 3900	16	15.03	240.45
5	ГОСТ 34028-2016(214-210-0502-0007)	Ф 25 А500С L= 5680	8	21.89	175.10
6	ГОСТ 34028-2016(214-210-0502-0007)	Ф 25 А500С L= 5080	8	19.58	156.60
С1	данные лист	Сетка С1	8	4.22	33.74
С2	данные лист	Сетка С2	12	2.90	34.77
		Материалы:			
	(212-101-0901)	Класс бетона С 20/25 (В25), м³			5.49
		Сетка С1			
10	ГОСТ 34028-2016(214-210-0501-0005)	Ф 10 А500С L= 570	12	0.35	4.22
		Сетка С2			
11	ГОСТ 34028-2016(214-210-0501-0005)	Ф 10 А500С L= 470	10	0.29	2.90

Позиции со "*" см. "Ведомость деталей" см. на данном листе.

Ведомость расхода стали, кг


Марка элемента	Изделия арматурные									Всего
	Арматура класса									
	А240			А500С						
	ГОСТ 34028-2016(214-210-0101)			ГОСТ 34028-2016(214-210-0502)						
	Ф6	Ф8	Итого	Ф10	Ф16	Ф20	Ф22	Ф25	Итого	
Колонна Км-4.1	0.00	246.32	246.32	68.51	10.01	--	--	1202.25	1280.76	1527.08

1. Схему расположения монолитных колонн см. листы КЖ-2.1; .... 2.7.
2. Бетонирование колонн в местах примыкания ригелей и монолитной плиты вести после установки рабочей арматуры ригеля, плиты и сеток косвенного армирования.
3. Сварные соединения выполнять ручной электродуговой сваркой, электроды типа Э-42А по ГОСТ 9467-75.
4. Защитный слой бетона принят по наружной грани продольной арматуры.
5. Стыковку продольной арматуры выполнять по ГОСТ 14098-91, тип соединения С21-Рн.
6. Сетки С-1 составляются из двух взаимно перпендикулярных элементов.


Изм.	Кол.уч.	Лист	N док.	Подп.	Дата	65П-АИП-2024-1-КЖ		
						Строительство многопрофильной больницы на 250 коек с онкологическим центром и поликлиникой на 350 посещений, по адресу: Медеуский район, г. Алматы		
						"Блок 1 Секция 1"	Стадия: РП	Лист: 4.6
ГКП		Курал М						
Проверил		Кыдырбай А				Колонна Км-4.1	АстанаИнжПроект	
Разраб.		Ауез Б						
Н.контроль		Ешенкулова						

Формат А2


Колонна Км-4.2

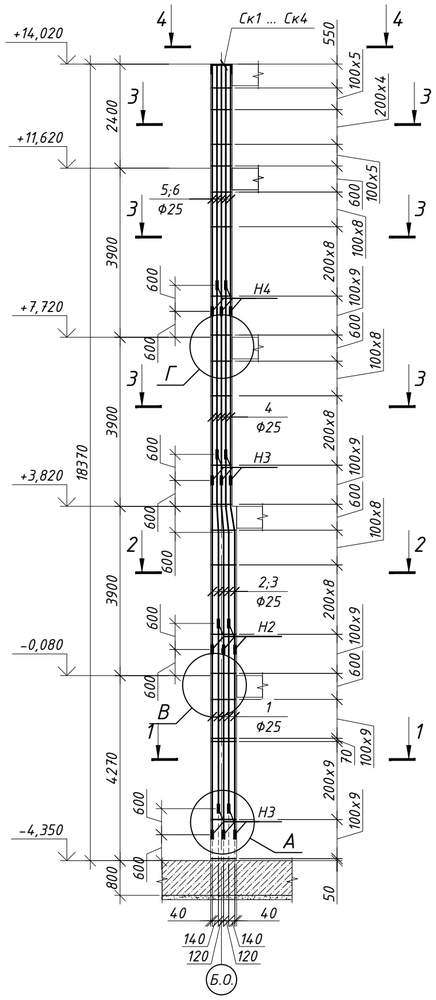


Разрез 1 - 1

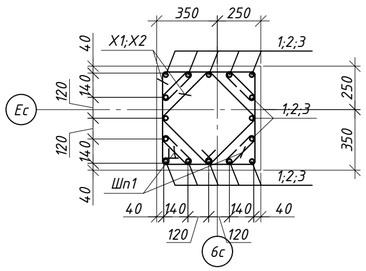


Разрез 2 - 2

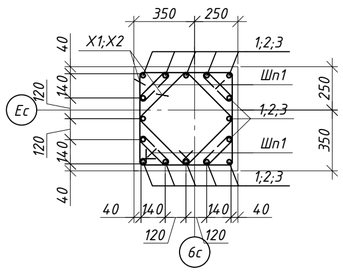


Разрез 3 - 3

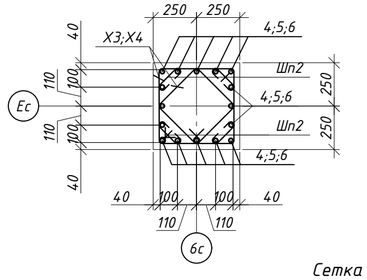


Разрез 4 - 4

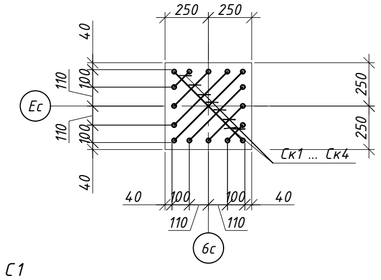


Сетка С1

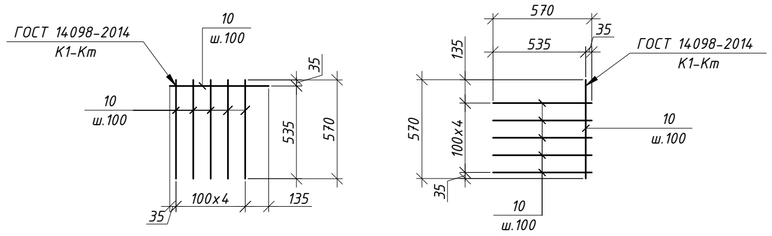

Сетка С2

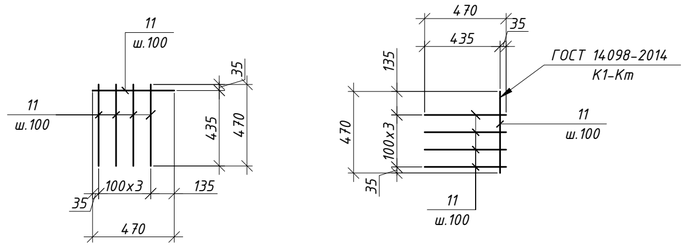


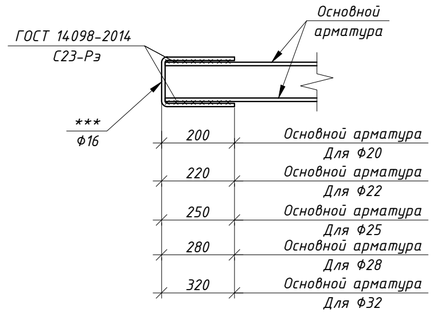



В

Г


Узел расположения сетки С1;

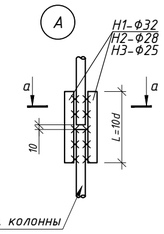

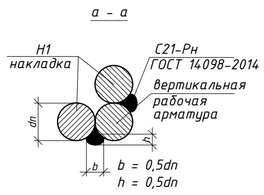

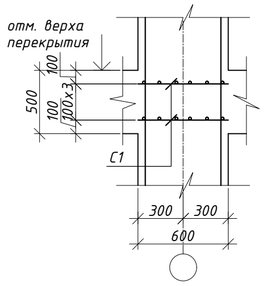

Узел расположения сетки С2

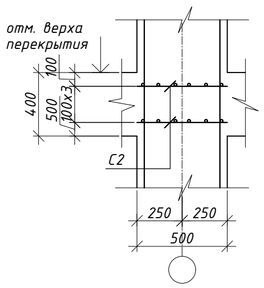

Ведомость деталей

Поз.	Эскиз
Ск1	220 / 560 / 220 по н.г. L=1000
Ск2	220 / 440 / 220 по н.г. L=880
Ск3	220 / 280 / 220 по н.г. L=720
Ск4	220 / 130 / 220 по н.г. L=570
Х1	620 / 520 / 620 по в.г. L=2280
Х2	480 / 380 / 480 по в.г. L=1720
Х3	520 / 420 / 520 по в.г. L=1880
Х4	410 / 310 / 410 по в.г. L=1440
Шп1	200 / 100 / 100 по в.г. L=400
Шп2	150 / 100 / 100 по в.г. L=350

Таблица размеров накладок

Марка эл-та	dн	L	вес
	мм.		кг.
Н1	32	320	2.01
Н2	28	280	1.35
Н3	25	250	0.96
Н4	22	220	0.66
Н5	20	200	0.49

Спецификация элементов

Поз.	Обозначение	Наименование	Кол.	Масса ед.кг	Примечание
		Колонна Км-4.2			1527.08
Х1*	ГОСТ 34028-2016(214-210-0101-0002)	Ф 8 А 240 L= 2280	55	0.90	49.48
Х2*	ГОСТ 34028-2016(214-210-0101-0002)	Ф 8 А 240 L= 1720	55	0.68	37.33
Х3*	ГОСТ 34028-2016(214-210-0101-0002)	Ф 8 А 240 L= 1880	67	0.74	49.70
Х4*	ГОСТ 34028-2016(214-210-0101-0002)	Ф 8 А 240 L= 1440	67	0.57	38.07
Шп1*	ГОСТ 34028-2016(214-210-0101-0002)	Ф 8 А 240 L= 400	220	0.16	34.72
Шп2*	ГОСТ 34028-2016(214-210-0101-0002)	Ф 8 А 240 L= 350	268	0.14	37.01
Ск1*	ГОСТ 34028-2016(214-210-0502-0003)	Ф 16 А500С L= 1000	2	1.58	3.16
Ск2*	ГОСТ 34028-2016(214-210-0502-0003)	Ф 16 А500С L= 880	2	1.39	2.78
Ск3*	ГОСТ 34028-2016(214-210-0502-0003)	Ф 16 А500С L= 720	2	1.14	2.27
Ск4*	ГОСТ 34028-2016(214-210-0502-0003)	Ф 16 А500С L= 570	2	0.90	1.80
1	ГОСТ 34028-2016(214-210-0502-0007)	Ф 25 А500С L= 4270	16	16.45	263.26
2	ГОСТ 34028-2016(214-210-0502-0007)	Ф 25 А500С L= 3900	8	15.03	120.22
3	ГОСТ 34028-2016(214-210-0502-0007)	Ф 25 А500С L= 4000	8	15.41	123.31
Н3	ГОСТ 34028-2016(214-210-0502-0007)	Ф 25 А500С L= 250	128	0.96	123.31
4	ГОСТ 34028-2016(214-210-0502-0007)	Ф 25 А500С L= 3900	16	15.03	240.45
5	ГОСТ 34028-2016(214-210-0502-0007)	Ф 25 А500С L= 5680	8	21.89	175.10
6	ГОСТ 34028-2016(214-210-0502-0007)	Ф 25 А500С L= 5080	8	19.58	156.60
С1	данные лист	Сетка С1	8	4.22	33.74
С2	данные лист	Сетка С2	12	2.90	34.77
		Материалы:			
	(212-101-0901)	Класс бетона С 20/25 (В25), м³			5.49
		Сетка С1			
10	ГОСТ 34028-2016(214-210-0501-0005)	Ф 10 А500С L= 570	12	0.35	4.22
		Сетка С2			
11	ГОСТ 34028-2016(214-210-0501-0005)	Ф 10 А500С L= 470	10	0.29	2.90

Позиции со "*" см. "Ведомость деталей" см. на данном листе.

Ведомость расхода стали, кг


Марка элемента	Изделия арматурные									Всего
	Арматура класса									
	А240			А500С						
	ГОСТ 34028-2016(214-210-0101)			ГОСТ 34028-2016(214-210-0502)						
	Ф6	Ф8	Итого	Ф10	Ф16	Ф20	Ф22	Ф25	Итого	
Колонна Км-4.2	0.00	246.32	246.32	68.51	10.01	--	--	1202.25	1280.76	1527.08

1. Схему расположения монолитных колонн см. листы КЖ-2.1; .... 2.7.
2. Бетонирование колонн в местах примыкания ригелей и монолитной плиты вести после установки рабочей арматуры ригеля, плиты и сеток косвенного армирования.
3. Сварные соединения выполнять ручной электродуговой сваркой, электроды типа Э-42А по ГОСТ 9467-75.
4. Защитный слой бетона принят по наружной грани продольной арматуры.
5. Стыковку продольной арматуры выполнять по ГОСТ 14098-91, тип соединения С21-Рн.
6. Сетки С-1 составляются из двух взаимно перпендикулярных элементов.


Изм.	Кол.уч.	Лист	N док.	Подп.	Дата	65П-АИП-2024-1-КЖ		
						Строительство многопрофильной больницы на 250 коек с онкологическим центром и поликлиникой на 350 посещений, по адресу: Медеуский район, г. Алматы		
ГКП		Курал М				"Блок 1 Секция 1"	Стадия: РП	Лист: 4.7
Проверил		Кыдырбай А						
Разраб.		Ауез Б				Колонна Км-4.2	АстанаИнжПроект	
Н.контроль		Ешенкулова						

Формат А2


Колонна Км-4.3

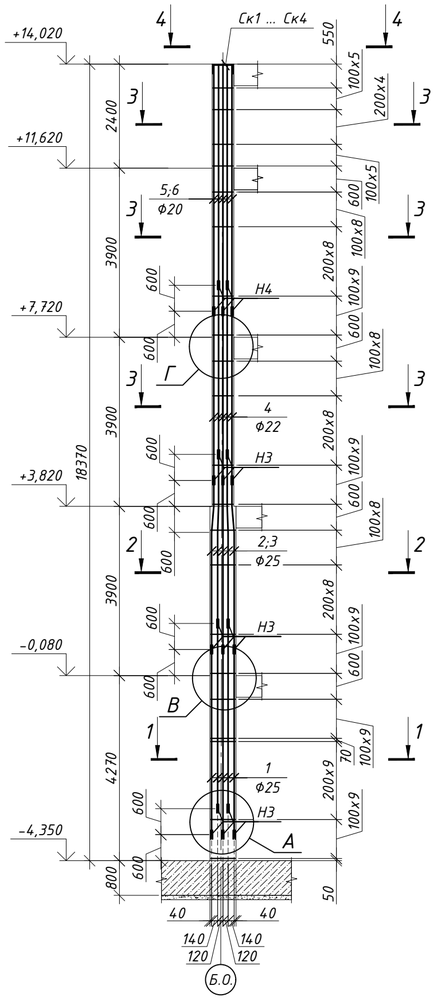


Разрез 1 - 1

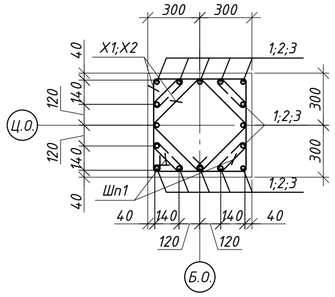


Разрез 2 - 2

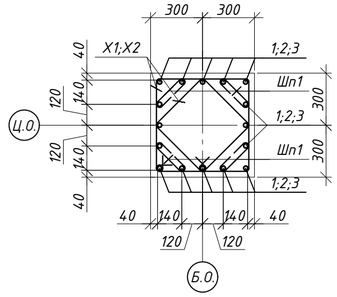


Разрез 3 - 3

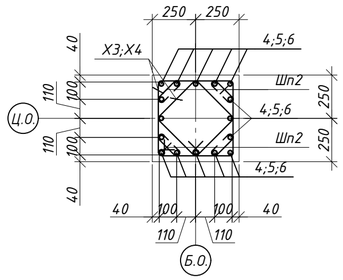


Разрез 4 - 4

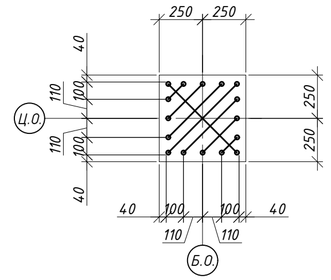


Сетка С1

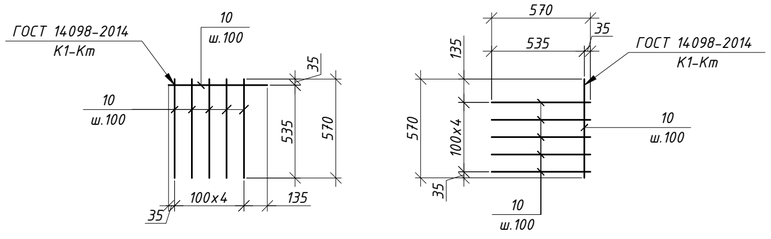



Сетка С2

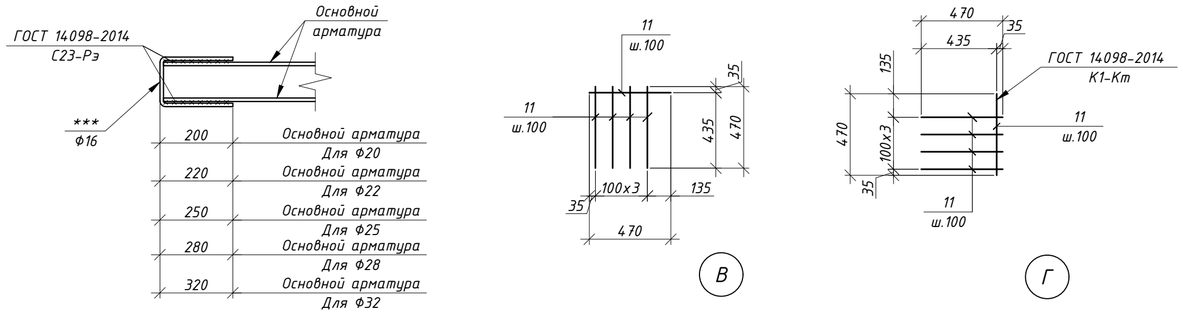


Узел расположения сетки С1;

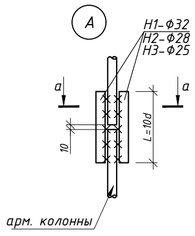

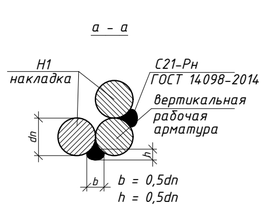

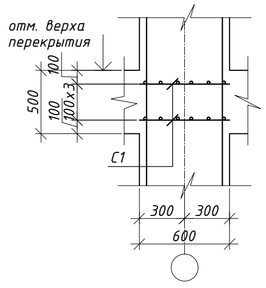

Узел расположения сетки С2

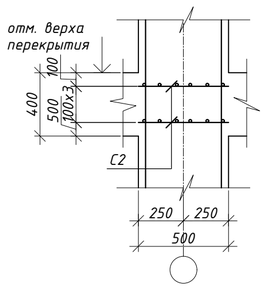

Ведомость деталей

Поз.	Эскиз
Ск1	220 / 560 / 220 по н.г. L=1000
Ск2	220 / 440 / 220 по н.г. L=880
Ск3	220 / 280 / 220 по н.г. L=720
Ск4	220 / 130 / 220 по н.г. L=570
Х1	620 / 520 / 520 620 по в.г. L=2280
Х2	480 / 380 / 380 480 по в.г. L=1720
Х3	520 / 420 / 420 520 по в.г. L=1880
Х4	410 / 310 / 310 410 по в.г. L=1440
Шп1	200 100 / 100 по в.г. L=400
Шп2	150 100 / 100 по в.г. L=350

Таблица размеров накладок

Марка эл-та	dн, мм.	L, мм.	вес кг.
Н1	32	320	2.01
Н2	28	280	1.35
Н3	25	250	0.96
Н4	22	220	0.66
Н5	20	200	0.49

Спецификация элементов

Поз.	Обозначение	Наименование	Кол.	Масса ед.кг	Примечание
		Колонна Км-4.3			1527.08
Х1*	ГОСТ 34028-2016(214-210-0101-0002)	Ф 8 А 240 L= 2280	55	0.90	49.48
Х2*	ГОСТ 34028-2016(214-210-0101-0002)	Ф 8 А 240 L= 1720	55	0.68	37.33
Х3*	ГОСТ 34028-2016(214-210-0101-0002)	Ф 8 А 240 L= 1880	67	0.74	49.70
Х4*	ГОСТ 34028-2016(214-210-0101-0002)	Ф 8 А 240 L= 1440	67	0.57	38.07
Шп1*	ГОСТ 34028-2016(214-210-0101-0002)	Ф 8 А 240 L= 400	220	0.16	34.72
Шп2*	ГОСТ 34028-2016(214-210-0101-0002)	Ф 8 А 240 L= 350	268	0.14	37.01
Ск1*	ГОСТ 34028-2016(214-210-0502-0003)	Ф 16 А500С L= 1000	2	1.58	3.16
Ск2*	ГОСТ 34028-2016(214-210-0502-0003)	Ф 16 А500С L= 880	2	1.39	2.78
Ск3*	ГОСТ 34028-2016(214-210-0502-0003)	Ф 16 А500С L= 720	2	1.14	2.27
Ск4*	ГОСТ 34028-2016(214-210-0502-0003)	Ф 16 А500С L= 570	2	0.90	1.80
1	ГОСТ 34028-2016(214-210-0502-0007)	Ф 25 А500С L= 4270	16	16.45	263.26
2	ГОСТ 34028-2016(214-210-0502-0007)	Ф 25 А500С L= 3900	8	15.03	120.22
3	ГОСТ 34028-2016(214-210-0502-0007)	Ф 25 А500С L= 4000	8	15.41	123.31
Н3	ГОСТ 34028-2016(214-210-0502-0007)	Ф 25 А500С L= 250	128	0.96	123.31
4	ГОСТ 34028-2016(214-210-0502-0007)	Ф 25 А500С L= 3900	16	15.03	240.45
5	ГОСТ 34028-2016(214-210-0502-0007)	Ф 25 А500С L= 5680	8	21.89	175.10
6	ГОСТ 34028-2016(214-210-0502-0007)	Ф 25 А500С L= 5080	8	19.58	156.60
С1	данные лист	Сетка С1	8	4.22	33.74
С2	данные лист	Сетка С2	12	2.90	34.77
		Материалы:			
	(212-101-0901)	Класс бетона С 20/25 (В25), м³			5.49
		Сетка С1			
10	ГОСТ 34028-2016(214-210-0501-0005)	Ф 10 А500С L= 570	12	0.35	4.22
		Сетка С2			
11	ГОСТ 34028-2016(214-210-0501-0005)	Ф 10 А500С L= 470	10	0.29	2.90

Позиции со "*" см. "Ведомость деталей" см. на данном листе.

Ведомость расхода стали, кг


Марка элемента	Изделия арматурные									Всего
	Арматура класса									
	А240			А500С						
	ГОСТ 34028-2016(214-210-0101)			ГОСТ 34028-2016(214-210-0502)						
	Ф6	Ф8	Итого	Ф10	Ф16	Ф20	Ф22	Ф25	Итого	
Колонна Км-4.3	0.00	246.32	246.32	68.51	10.01	--	--	1202.25	1280.76	1527.08

1. Схему расположения монолитных колонн см. листы КЖ-2.1; .... 2.7.
2. Бетонирование колонн в местах примыкания ригелей и монолитной плиты вести после установки рабочей арматуры ригеля, плиты и сеток косвенного армирования.
3. Сварные соединения выполнять ручной электродуговой сваркой, электроды типа Э-42А по ГОСТ 9467-75.
4. Защитный слой бетона принят по наружной грани продольной арматуры.
5. Стыковку продольной арматуры выполнять по ГОСТ 14098-91, тип соединения С21-Рн.
6. Сетки С-1 составляются из двух взаимно перпендикулярных элементов.


Изм.	Кол.уч.	Лист	N док.	Подп.	Дата	65П-АИП-2024-1-КЖ		
						Строительство многопрофильной больницы на 250 коек с онкологическим центром и поликлиникой на 350 посещений, по адресу: Медеуский район, г. Алматы		
						"Блок 1 Секция 1"	Стадия: РП	Лист: 4.8	Листов:
ГКП		Курал М							
Проверил		Кыдырбай А				Колонна Км-4.3	АстанаИнжПроект		
Разраб.		Ауез Б							
Н.контроль		Ешенкулова							

Формат А2


Колонна Км-5.1

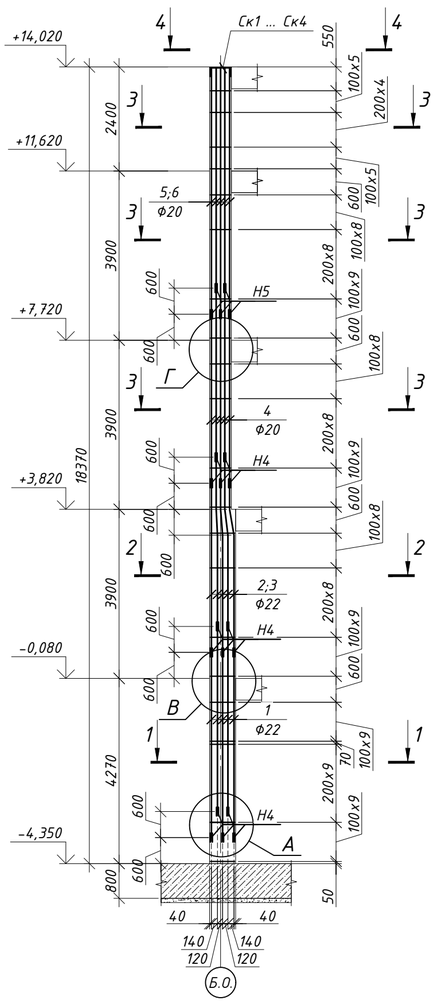


Разрез 1 - 1

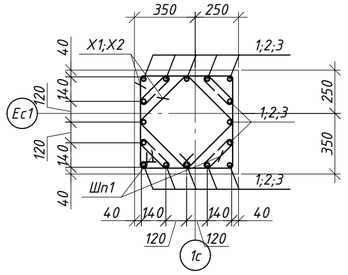


Разрез 2 - 2

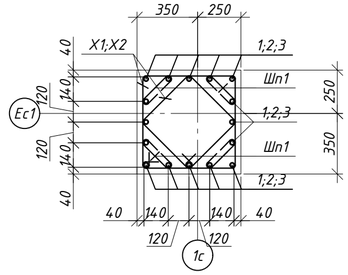


Разрез 3 - 3

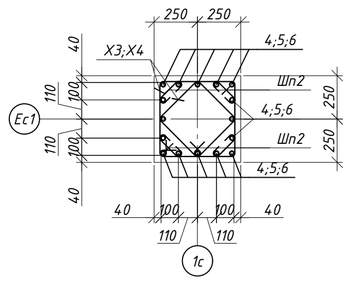


Разрез 4 - 4

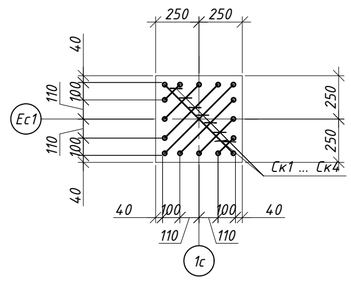


Сетка С1

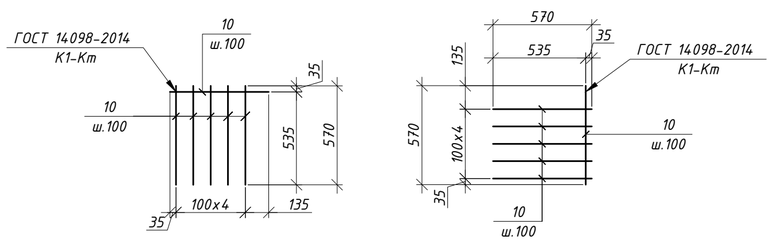


Сетка С2

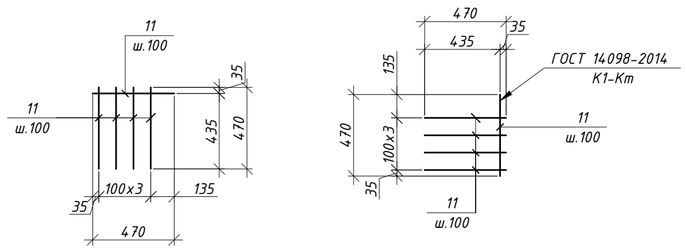


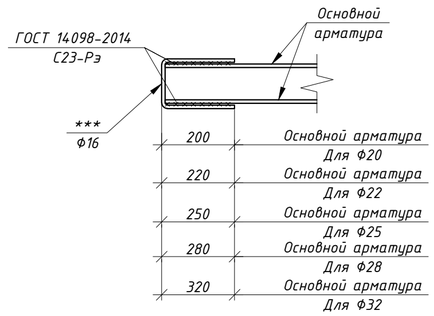

Узел расположения сетки С1;

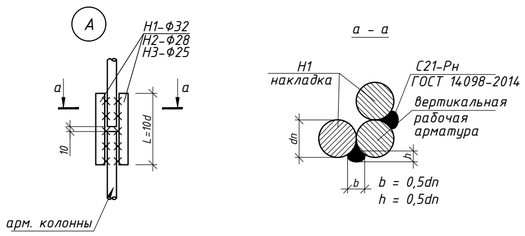

Узел расположения сетки С2

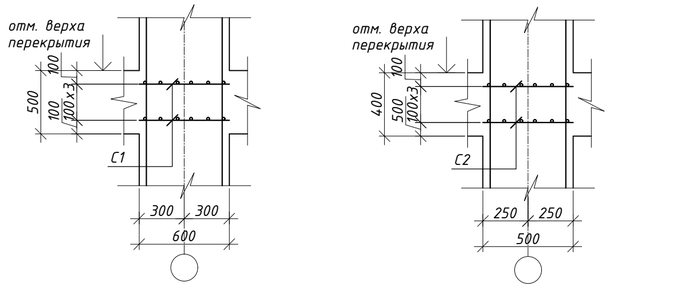

Ведомость деталей

Поз.	Эскиз
Ск1	220 / 560 / 220 — по н.г. — L=1000
Ск2	220 / 440 / 220 — по н.г. — L=880
Ск3	220 / 280 / 220 — по н.г. — L=720
Ск4	220 / 130 / 220 — по н.г. — L=570
Х1	620 / 520 / 620 — по в.г. — L=2280
Х2	480 / 380 / 480 — по в.г. — L=1720
Х3	520 / 420 / 520 — по в.г. — L=1880
Х4	410 / 310 / 410 — по в.г. — L=1440
Шп1	200 / 100 / 100 — по в.г. — L=400
Шп2	150 / 100 / 100 — по в.г. — L=350

Таблица размеров накладок

Марка эл-та	dн	L	вес
	мм.		кг.
Н1	32	320	2.01
Н2	28	280	1.35
Н3	25	250	0.96
Н4	22	220	0.66
Н5	20	200	0.49

Спецификация элементов

Поз.	Обозначение	Наименование	Кол.	Масса ед.кг	Примечание
		Колонна Км-5.1			1162.27
Х1*	ГОСТ 34028-2016(214-210-0101-0002)	Ф 8 А 240 L= 2280	55	0.90	49.48
Х2*	ГОСТ 34028-2016(214-210-0101-0002)	Ф 8 А 240 L= 1720	55	0.68	37.33
Х3*	ГОСТ 34028-2016(214-210-0101-0002)	Ф 8 А 240 L= 1880	67	0.74	49.70
Х4*	ГОСТ 34028-2016(214-210-0101-0002)	Ф 8 А 240 L= 1440	67	0.57	38.07
Шп1*	ГОСТ 34028-2016(214-210-0101-0002)	Ф 8 А 240 L= 400	220	0.16	34.72
Шп2*	ГОСТ 34028-2016(214-210-0101-0002)	Ф 8 А 240 L= 350	268	0.14	37.01
Ск1*	ГОСТ 34028-2016(214-210-0502-0003)	Ф 16 А500С L= 1000	2	1.58	3.16
Ск2*	ГОСТ 34028-2016(214-210-0502-0003)	Ф 16 А500С L= 880	2	1.39	2.78
Ск3*	ГОСТ 34028-2016(214-210-0502-0003)	Ф 16 А500С L= 720	2	1.14	2.27
Ск4*	ГОСТ 34028-2016(214-210-0502-0003)	Ф 16 А500С L= 570	2	0.90	1.80
1	ГОСТ 34028-2016(214-210-0502-0006)	Ф 22 А500С L= 4270	16	12.74	203.87
2	ГОСТ 34028-2016(214-210-0502-0006)	Ф 22 А500С L= 3900	8	11.64	93.10
3	ГОСТ 34028-2016(214-210-0502-0006)	Ф 22 А500С L= 4000	8	11.94	95.49
Н4	ГОСТ 34028-2016(214-210-0502-0006)	Ф 22 А500С L= 220	96	0.66	63.02
4	ГОСТ 34028-2016(214-210-0502-0005)	Ф 20 А500С L= 3900	16	9.62	153.89
5	ГОСТ 34028-2016(214-210-0502-0005)	Ф 20 А500С L= 5680	8	14.01	112.06
6	ГОСТ 34028-2016(214-210-0502-0005)	Ф 20 А500С L= 5080	8	12.53	100.22
Н5	ГОСТ 34028-2016(214-210-0502-0005)	Ф 20 А500С L= 200	32	0.49	15.78
С1	данные лист	Сетка С1	8	4.22	33.74
С2	данные лист	Сетка С2	12	2.90	34.77
		Материалы:			
	(212-101-0901)	Класс бетона С 20/25 (В25), м³			5.49
		Сетка С1			
10	ГОСТ 34028-2016(214-210-0501-0005)	Ф 10 А500С L= 570	12	0.35	4.22
		Сетка С2			
11	ГОСТ 34028-2016(214-210-0501-0005)	Ф 10 А500С L= 470	10	0.29	2.90

Позиции со "*" см. "Ведомость деталей" см. на данном листе.

Ведомость расхода стали, кг


Марка элемента	Изделия арматурные									Всего
	Арматура класса									
	А240			А500С						
	ГОСТ 34028-2016(214-210-0101)			ГОСТ 34028-2016(214-210-0502)						
	Ф6	Ф8	Итого	Ф10	Ф16	Ф20	Ф22	Ф25	Итого	
Колонна Км-5.1	0.00	246.32	246.32	68.51	10.01	381.96	455.5	--	915.96	1162.27

1. Схему расположения монолитных колонн см. листы КЖ-2.1; .... 2.7.
2. Бетонирование колонн в местах примыкания ригелей и монолитной плиты вести после установки рабочей арматуры ригеля, плиты и сеток косвенного армирования.
3. Сварные соединения выполнять ручной электродуговой сваркой, электроды типа Э-42А по ГОСТ 9467-75.
4. Защитный слой бетона принят по наружной грани продольной арматуры.
5. Стыковку продольной арматуры выполнять по ГОСТ 14098-91, тип соединения С21-Рн.
6. Сетки С-1 составляются из двух взаимно перпендикулярных элементов.


Изм.	Кол.уч.	Лист	N док.	Подп.	Дата	65П-АИП-2024-1-КЖ		
						Строительство многопрофильной больницы на 250 коек с онкологическим центром и поликлиникой на 350 посещений, по адресу: Медеуский район, г. Алматы		
						"Блок 1 Секция 1"	Стадия: РП	Лист: 4.9
ГКП		Курал М						
Проверил		Кыдырбай А				Колонна Км-5.1	АстанаИнжПроект	
Разраб.		Ауез Б						
Н.контроль		Ешенкулова						

Формат А2


Колонна Км-5.2

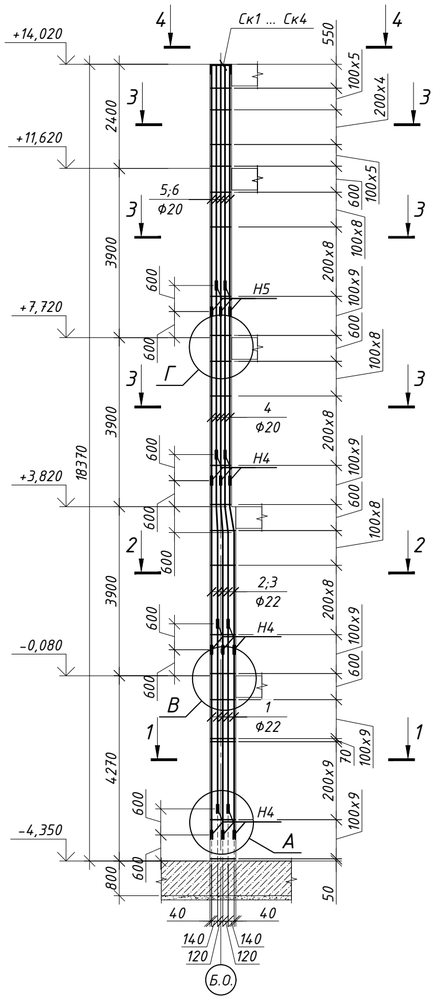


Разрез 1 - 1

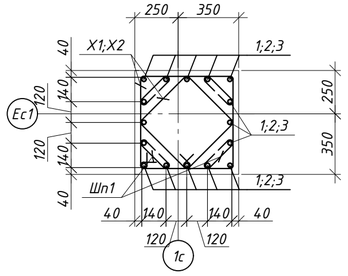


Разрез 2 - 2

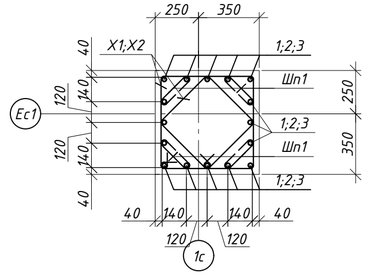


Разрез 3 - 3

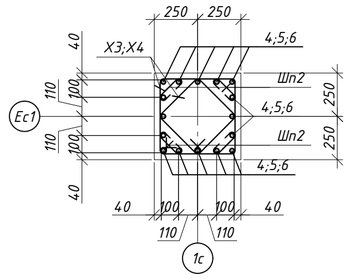


Разрез 4 - 4

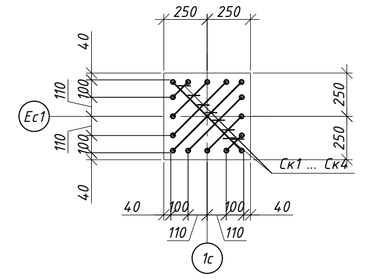

Сетка С1

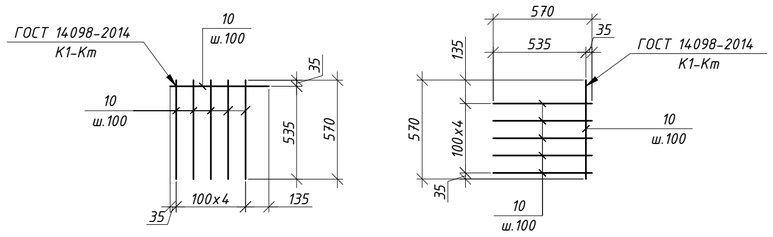

Сетка С2

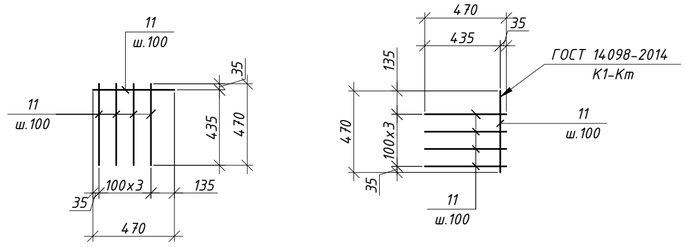

Ведомость деталей

Поз.	Эскиз
Ск1	220 / 560 / 220 / по н.г. / L=1000
Ск2	220 / 440 / 220 / по н.г. / L=880
Ск3	220 / 280 / 220 / по н.г. / L=720
Ск4	220 / 130 / 220 / по н.г. / L=570
Х1	620 / 520 / 620 / 520 / по в.г. / L=2280
Х2	480 / 380 / 480 / 380 / по в.г. / L=1720
Х3	520 / 420 / 520 / 420 / по в.г. / L=1880
Х4	410 / 310 / 410 / 310 / по в.г. / L=1440
Шп1	200 / 100 / 100 / по в.г. / L=400
Шп2	150 / 100 / 100 / по в.г. / L=350

Таблица размеров накладок

Марка эл-та	dн	L	вес
	мм.		кг.
Н1	32	320	2.01
Н2	28	280	1.35
Н3	25	250	0.96
Н4	22	220	0.66
Н5	20	200	0.49


Спецификация элементов

Поз.	Обозначение	Наименование	Кол.	Масса ед.кг	Примечание
		Колонна Км-5.2			1162.27
Х1*	ГОСТ 34028-2016(214-210-0101-0002)	Ф 8 А 240 L= 2280	55	0.90	49.48
Х2*	ГОСТ 34028-2016(214-210-0101-0002)	Ф 8 А 240 L= 1720	55	0.68	37.33
Х3*	ГОСТ 34028-2016(214-210-0101-0002)	Ф 8 А 240 L= 1880	67	0.74	49.70
Х4*	ГОСТ 34028-2016(214-210-0101-0002)	Ф 8 А 240 L= 1440	67	0.57	38.07
Шп1*	ГОСТ 34028-2016(214-210-0101-0002)	Ф 8 А 240 L= 400	220	0.16	34.72
Шп2*	ГОСТ 34028-2016(214-210-0101-0002)	Ф 8 А 240 L= 350	268	0.14	37.01
Ск1*	ГОСТ 34028-2016(214-210-0502-0003)	Ф 16 А500С L= 1000	2	1.58	3.16
Ск2*	ГОСТ 34028-2016(214-210-0502-0003)	Ф 16 А500С L= 880	2	1.39	2.78
Ск3*	ГОСТ 34028-2016(214-210-0502-0003)	Ф 16 А500С L= 720	2	1.14	2.27
Ск4*	ГОСТ 34028-2016(214-210-0502-0003)	Ф 16 А500С L= 570	2	0.90	1.80
1	ГОСТ 34028-2016(214-210-0502-0006)	Ф 22 А500С L= 4270	16	12.74	203.87
2	ГОСТ 34028-2016(214-210-0502-0006)	Ф 22 А500С L= 3900	8	11.64	93.10
3	ГОСТ 34028-2016(214-210-0502-0006)	Ф 22 А500С L= 4000	8	11.94	95.49
Н4	ГОСТ 34028-2016(214-210-0502-0006)	Ф 22 А500С L= 220	96	0.66	63.02
4	ГОСТ 34028-2016(214-210-0502-0005)	Ф 20 А500С L= 3900	16	9.62	153.89
5	ГОСТ 34028-2016(214-210-0502-0005)	Ф 20 А500С L= 5680	8	14.01	112.06
6	ГОСТ 34028-2016(214-210-0502-0005)	Ф 20 А500С L= 5080	8	12.53	100.22
Н5	ГОСТ 34028-2016(214-210-0502-0005)	Ф 20 А500С L= 200	32	0.49	15.78
С1	данные лист	Сетка С1	8	4.22	33.74
С2	данные лист	Сетка С2	12	2.90	34.77
		Материалы:			
	(212-101-0901)	Класс бетона С 20/25 (В25), м³			5.49
		Сетка С1			
10	ГОСТ 34028-2016(214-210-0501-0005)	Ф 10 А500С L= 570	12	0.35	4.22
		Сетка С2			
11	ГОСТ 34028-2016(214-210-0501-0005)	Ф 10 А500С L= 470	10	0.29	2.90

Позиции со "*" см. "Ведомость деталей" см. на данном листе.

Ведомость расхода стали, кг


Марка элемента	Изделия арматурные									Всего
	Арматура класса									
	А240			А500С						
	ГОСТ 34028-2016(214-210-0101)			ГОСТ 34028-2016(214-210-0502)						
	Ф6	Ф8	Итого	Ф10	Ф16	Ф20	Ф22	Ф25	Итого	
Колонна Км-5.2	0.00	246.32	246.32	68.51	10.01	381.96	455.5	--	915.96	1162.27

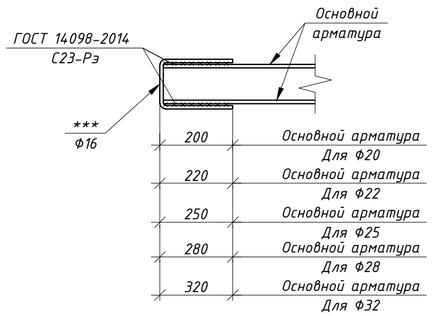



В

Г


Узел расположения сетки С1;

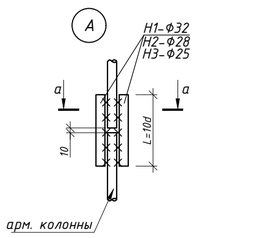

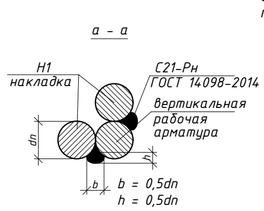

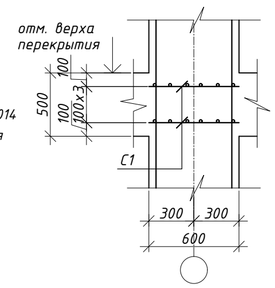

Узел расположения сетки С2

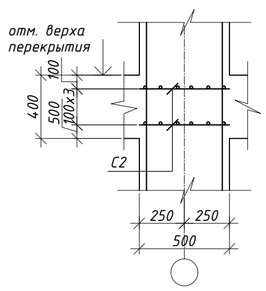


1. Схему расположения монолитных колонн см. листы КЖ-2.1; .... 2.7.
2. Бетонирование колонн в местах примыкания ригелей и монолитной плиты вести после установки рабочей арматуры ригеля, плиты и сеток косвенного армирования.
3. Сварные соединения выполнять ручной электродуговой сваркой, электроды типа Э-42А по ГОСТ 9467-75.
4. Защитный слой бетона принят по наружной грани продольной арматуры.
5. Стыковку продольной арматуры выполнять по ГОСТ 14098-91, тип соединения С21-Рн.
6. Сетки С-1 составляются из двух взаимно перпендикулярных элементов.


Изм.	Кол.уч.	Лист	N док.	Подп.	Дата	65П-АИП-2024-1-КЖ		
						Строительство многопрофильной больницы на 250 коек с онкологическим центром и поликлиникой на 350 посещений, по адресу: Медеуский район, г. Алматы		
ГКП		Курал М				"Блок 1 Секция 1"	Стадия: РП	Лист: 4.10
Проверил		Кыдырбай А						
Разраб.		Ауез Б				Колонна Км-5.2	АстанаИнжПроект	
Н.контроль		Ешенкулова						

Формат А2


Колонна Км-5.3

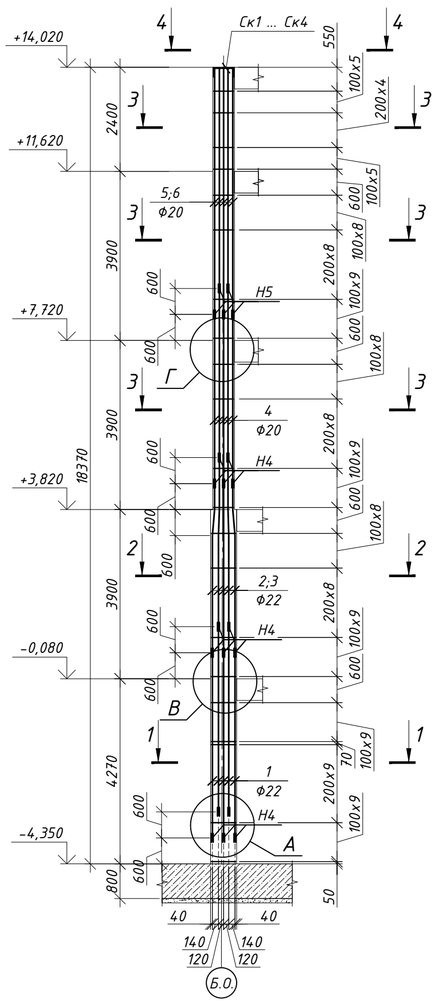


Разрез 1 - 1

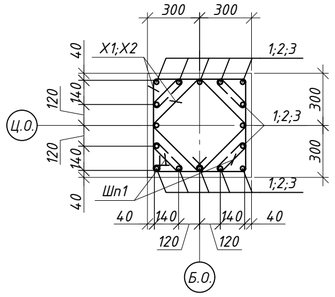


Разрез 2 - 2

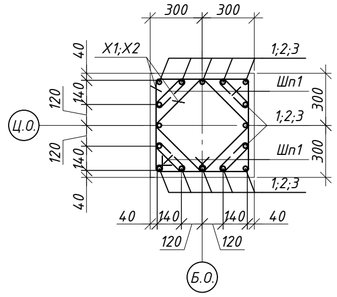


Разрез 3 - 3

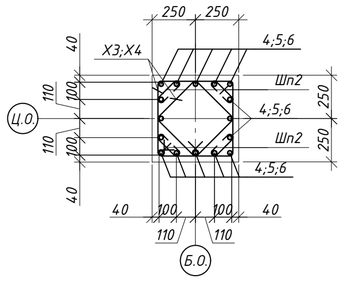


Разрез 4 - 4

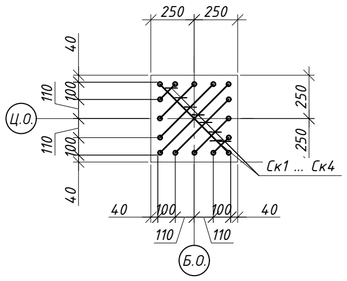


Сетка С1

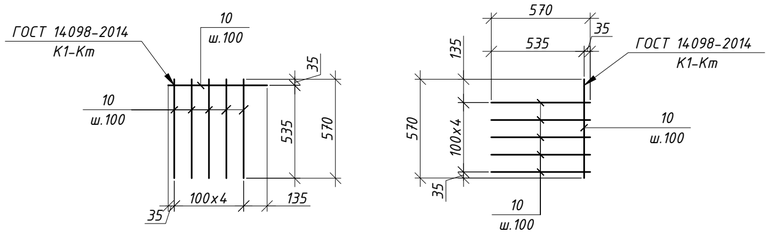


Сетка С2

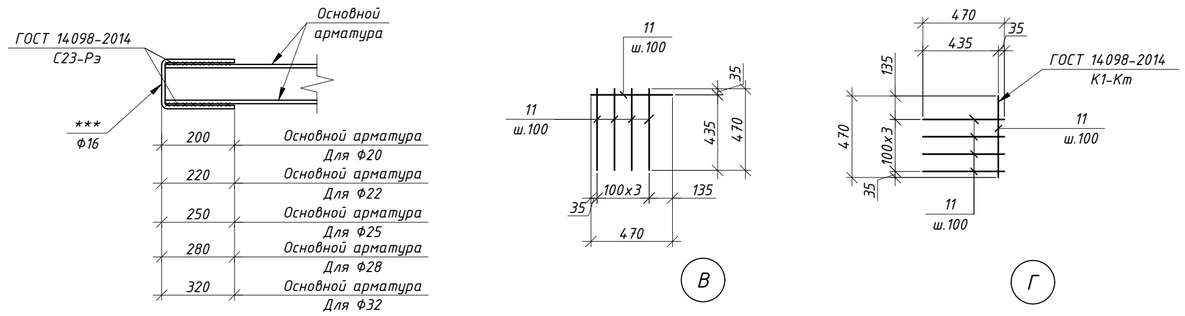



Узел расположения сетки С1;

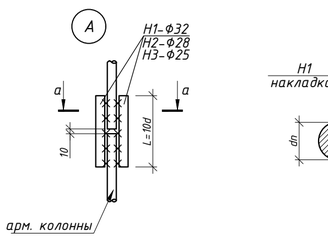

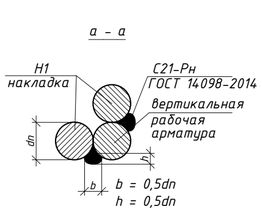

Узел расположения сетки С2

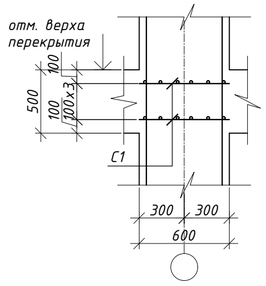

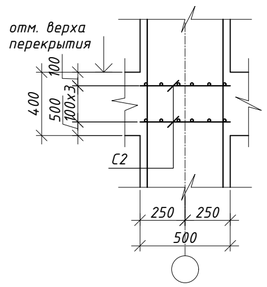

Ведомость деталей

Поз.	Эскиз
Ск1	220 / 560 / 220 по н.г. L=1000
Ск2	220 / 440 / 220 по н.г. L=880
Ск3	220 / 280 / 220 по н.г. L=720
Ск4	220 / 130 / 220 по н.г. L=570
Х1	620 / 520 / 520 620 по в.г. L=2280
Х2	480 / 380 / 380 480 по в.г. L=1720
Х3	520 / 420 / 420 520 по в.г. L=1880
Х4	410 / 310 / 310 410 по в.г. L=1440
Шп1	200 100 / 100 по в.г. L=400
Шп2	150 100 / 100 по в.г. L=350

Таблица размеров накладок

Марка эл-та	dн	L	вес
	мм.		кг.
Н1	32	320	2.01
Н2	28	280	1.35
Н3	25	250	0.96
Н4	22	220	0.66
Н5	20	200	0.49

Спецификация элементов

Поз.	Обозначение	Наименование	Кол.	Масса ед.кг	Примечание
		Колонна Км-5.3			1162.27
Х1*	ГОСТ 34028-2016(214-210-0101-0002)	Ф 8 А 240 L= 2280	55	0.90	49.48
Х2*	ГОСТ 34028-2016(214-210-0101-0002)	Ф 8 А 240 L= 1720	55	0.68	37.33
Х3*	ГОСТ 34028-2016(214-210-0101-0002)	Ф 8 А 240 L= 1880	67	0.74	49.70
Х4*	ГОСТ 34028-2016(214-210-0101-0002)	Ф 8 А 240 L= 1440	67	0.57	38.07
Шп1*	ГОСТ 34028-2016(214-210-0101-0002)	Ф 8 А 240 L= 400	220	0.16	34.72
Шп2*	ГОСТ 34028-2016(214-210-0101-0002)	Ф 8 А 240 L= 350	268	0.14	37.01
Ск1*	ГОСТ 34028-2016(214-210-0502-0003)	Ф 16 А500С L= 1000	2	1.58	3.16
Ск2*	ГОСТ 34028-2016(214-210-0502-0003)	Ф 16 А500С L= 880	2	1.39	2.78
Ск3*	ГОСТ 34028-2016(214-210-0502-0003)	Ф 16 А500С L= 720	2	1.14	2.27
Ск4*	ГОСТ 34028-2016(214-210-0502-0003)	Ф 16 А500С L= 570	2	0.90	1.80
1	ГОСТ 34028-2016(214-210-0502-0006)	Ф 22 А500С L= 4270	16	12.74	203.87
2	ГОСТ 34028-2016(214-210-0502-0006)	Ф 22 А500С L= 3900	8	11.64	93.10
3	ГОСТ 34028-2016(214-210-0502-0006)	Ф 22 А500С L= 4000	8	11.94	95.49
Н4	ГОСТ 34028-2016(214-210-0502-0006)	Ф 22 А500С L= 220	96	0.66	63.02
4	ГОСТ 34028-2016(214-210-0502-0005)	Ф 20 А500С L= 3900	16	9.62	153.89
5	ГОСТ 34028-2016(214-210-0502-0005)	Ф 20 А500С L= 5680	8	14.01	112.06
6	ГОСТ 34028-2016(214-210-0502-0005)	Ф 20 А500С L= 5080	8	12.53	100.22
Н5	ГОСТ 34028-2016(214-210-0502-0005)	Ф 20 А500С L= 200	32	0.49	15.78
С1	данные лист	Сетка С1	8	4.22	33.74
С2	данные лист	Сетка С2	12	2.90	34.77
		Материалы:			
	(212-101-0901)	Класс бетона С 20/25 (В25), м³			5.49
		Сетка С1			
10	ГОСТ 34028-2016(214-210-0501-0005)	Ф 10 А500С L= 570	12	0.35	4.22
		Сетка С2			
11	ГОСТ 34028-2016(214-210-0501-0005)	Ф 10 А500С L= 470	10	0.29	2.90

Позиции со "*" см. "Ведомость деталей" см. на данном листе.

Ведомость расхода стали, кг


Марка элемента	Изделия арматурные									Всего
	Арматура класса									
	А240			А500С						
	ГОСТ 34028-2016(214-210-0101)			ГОСТ 34028-2016(214-210-0502)						
	Ф6	Ф8	Итого	Ф10	Ф16	Ф20	Ф22	Ф25	Итого	
Колонна Км-5.3	0.00	246.32	246.32	68.51	10.01	381.96	455.5	--	915.96	1162.27

1. Схему расположения монолитных колонн см. листы КЖ-2.1; .... 2.7.
2. Бетонирование колонн в местах примыкания ригелей и монолитной плиты вести после установки рабочей арматуры ригеля, плиты и сеток косвенного армирования.
3. Сварные соединения выполнять ручной электродуговой сваркой, электроды типа Э-42А по ГОСТ 9467-75.
4. Защитный слой бетона принят по наружной грани продольной арматуры.
5. Стыковку продольной арматуры выполнять по ГОСТ 14098-91, тип соединения С21-Рн.
6. Сетки С-1 составляются из двух взаимно перпендикулярных элементов.


Изм.	Кол.уч.	Лист	N док.	Подп.	Дата	65П-АИП-2024-1-КЖ		
						Строительство многопрофильной больницы на 250 коек с онкологическим центром и поликлиникой на 350 посещений, по адресу: Медеуский район, г. Алматы		
						"Блок 1 Секция 1"	Стадия: РП	Лист: 4.11
ГКП		Курал М						
Проверил		Кыдырбай А				Колонна Км-5.3	АстанаИнжПроект	
Разраб.		Ауез Б						
Н.контроль		Ешенкулова						

Формат А2


Колонна Км-6.1

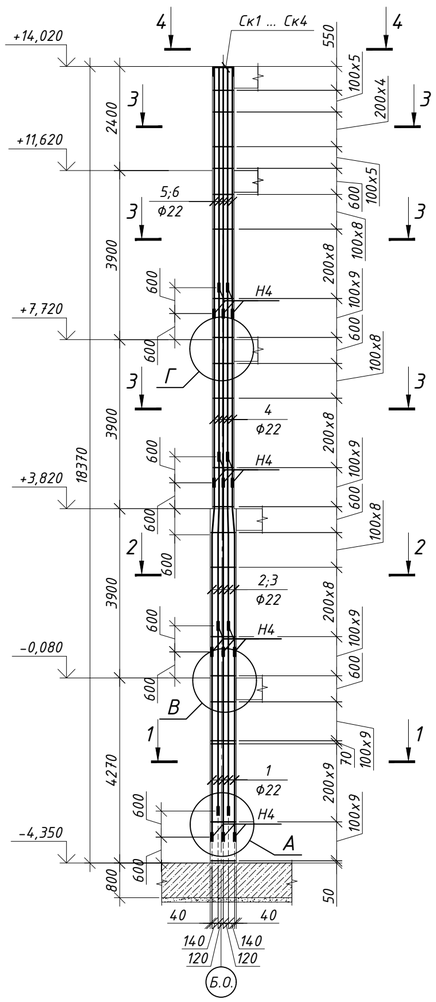


Разрез 1 - 1

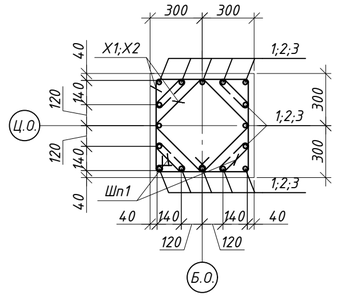


Разрез 2 - 2

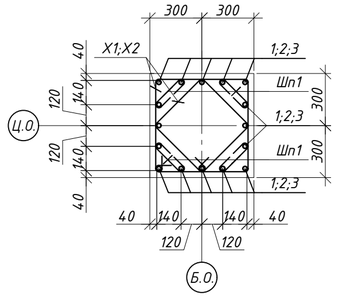


Разрез 3 - 3

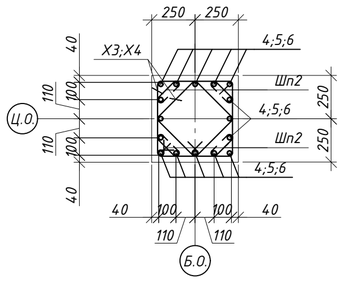


Разрез 4 - 4

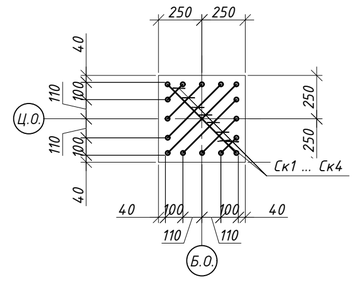

Сетка С1

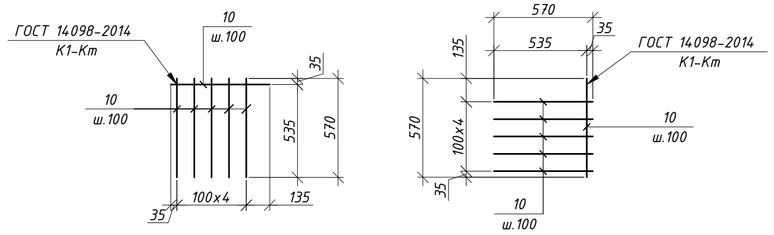

Сетка С2

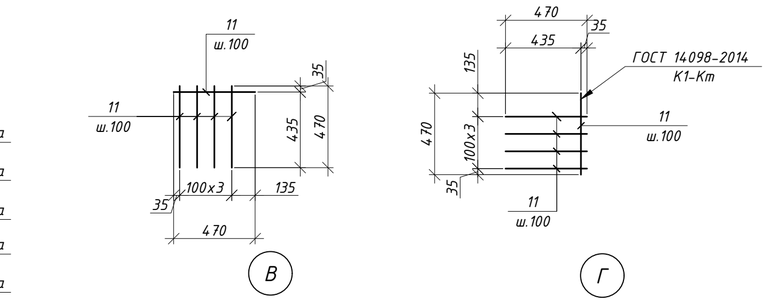

Ведомость деталей

Поз.	Эскиз
Ск1	220 / 560 / 220 — по н.г. — L=1000
Ск2	220 / 440 / 220 — по н.г. — L=880
Ск3	220 / 280 / 220 — по н.г. — L=720
Ск4	220 / 130 / 220 — по н.г. — L=570
Х1	620 / 520 / 620 — по в.г. — L=2280
Х2	480 / 380 / 480 — по в.г. — L=1720
Х3	520 / 420 / 520 — по в.г. — L=1880
Х4	410 / 310 / 410 — по в.г. — L=1440
Шп1	200 / 100 / 100 — по в.г. — L=400
Шп2	150 / 100 / 100 — по в.г. — L=350

Таблица размеров накладок

Марка эл-та	dн	L	вес
	мм.		кг.
Н1	32	320	2.01
Н2	28	280	1.35
Н3	25	250	0.96
Н4	22	220	0.66
Н5	20	200	0.49

Спецификация элементов


Поз.	Обозначение	Наименование	Кол.	Масса ед.кг	Примечание
		Колонна Км-6.1			1244.39
Х1*	ГОСТ 34028-2016(214-210-0101-0002)	Ф 8 А 240 L= 2280	55	0.90	49.48
Х2*	ГОСТ 34028-2016(214-210-0101-0002)	Ф 8 А 240 L= 1720	55	0.68	37.33
Х3*	ГОСТ 34028-2016(214-210-0101-0002)	Ф 8 А 240 L= 1880	67	0.74	49.70
Х4*	ГОСТ 34028-2016(214-210-0101-0002)	Ф 8 А 240 L= 1440	67	0.57	38.07
Шп1*	ГОСТ 34028-2016(214-210-0101-0002)	Ф 8 А 240 L= 400	220	0.16	34.72
Шп2*	ГОСТ 34028-2016(214-210-0101-0002)	Ф 8 А 240 L= 350	268	0.14	37.01
Ск1*	ГОСТ 34028-2016(214-210-0502-0003)	Ф 16 А500С L= 1000	2	1.58	3.16
Ск2*	ГОСТ 34028-2016(214-210-0502-0003)	Ф 16 А500С L= 880	2	1.39	2.78
Ск3*	ГОСТ 34028-2016(214-210-0502-0003)	Ф 16 А500С L= 720	2	1.14	2.27
Ск4*	ГОСТ 34028-2016(214-210-0502-0003)	Ф 16 А500С L= 570	2	0.90	1.80
1	ГОСТ 34028-2016(214-210-0502-0006)	Ф 22 А500С L= 4270	16	12.74	203.87
2	ГОСТ 34028-2016(214-210-0502-0006)	Ф 22 А500С L= 3900	8	11.64	93.10
3	ГОСТ 34028-2016(214-210-0502-0006)	Ф 22 А500С L= 4000	8	11.94	95.49
Н4	ГОСТ 34028-2016(214-210-0502-0006)	Ф 22 А500С L= 220	128	0.66	84.03
4	ГОСТ 34028-2016(214-210-0502-0006)	Ф 22 А500С L= 3900	16	11.64	186.20
5	ГОСТ 34028-2016(214-210-0502-0006)	Ф 22 А500С L= 5680	8	16.95	135.59
6	ГОСТ 34028-2016(214-210-0502-0006)	Ф 22 А500С L= 5080	8	15.16	121.27
С1	данные лист	Сетка С1	8	4.22	33.74
С2	данные лист	Сетка С2	12	2.90	34.77
		Материалы:			
	(212-101-0901)	Класс бетона С 20/25 (В25), м³			5.49
		Сетка С1			
10	ГОСТ 34028-2016(214-210-0501-0005)	Ф 10 А500С L= 570	12	0.35	4.22
		Сетка С2			
11	ГОСТ 34028-2016(214-210-0501-0005)	Ф 10 А500С L= 470	10	0.29	2.90


Позиции со "*" см. "Ведомость деталей" см. на данном листе.


Ведомость расхода стали, кг

Марка элемента	Изделия арматурные									Всего
	Арматура класса									
	А240			А500С						
	ГОСТ 34028-2016(214-210-0101)			ГОСТ 34028-2016(214-210-0502)						
	Ф6	Ф8	Итого	Ф10	Ф16	Ф20	Ф22	Ф25	Итого	
Колонна Км-6.1	0.00	246.32	246.32	68.51	10.01	---	919.6	--	998.08	1244.39


Узел расположения сетки С1;

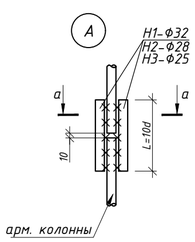

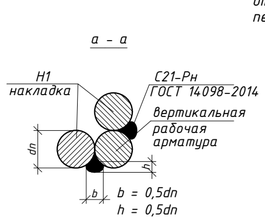

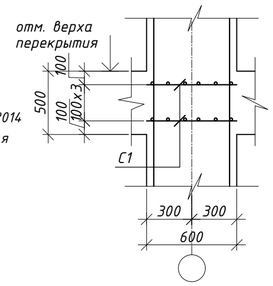

Узел расположения сетки С2

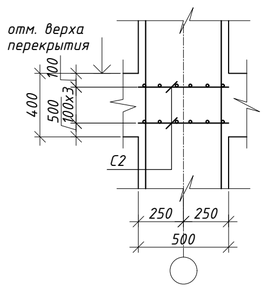


1. Схему расположения монолитных колонн см. листы КЖ-2.1; .... 2.7.
2. Бетонирование колонн в местах примыкания ригелей и монолитной плиты вести после установки рабочей арматуры ригеля, плиты и сеток косвенного армирования.
3. Сварные соединения выполнять ручной электродуговой сваркой, электроды типа Э-42А по ГОСТ 9467-75.
4. Защитный слой бетона принят по наружной грани продольной арматуры.
5. Стыковку продольной арматуры выполнять по ГОСТ 14098-91, тип соединения С21-Рн.
6. Сетки С-1 составляются из двух взаимно перпендикулярных элементов.


Изм.	Кол.уч.	Лист	N док.	Подп.	Дата	65П-АИП-2024-1-КЖ		
						Строительство многопрофильной больницы на 250 коек с онкологическим центром и поликлиникой на 350 посещений, по адресу: Медеуский район, г. Алматы		
ГКП		Курал М				"Блок 1 Секция 1"	Стадия: РП	Лист: 4.12 / Листов:
Проверил		Кыдырбай А						
Разраб.		Ауез Б				Колонна Км-6.1	АстанаИнжПроект	
Н.контроль		Ешенкулова						

Формат А2


Колонна Км-7.1

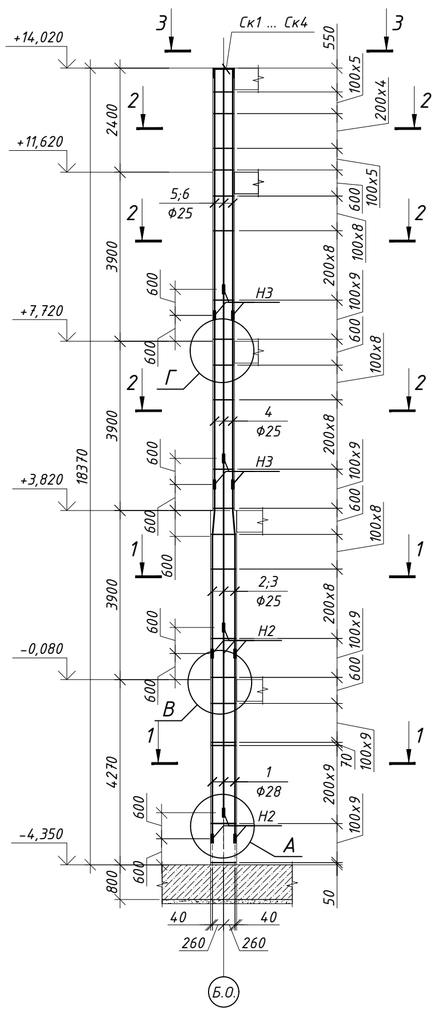


Разрез 1 - 1

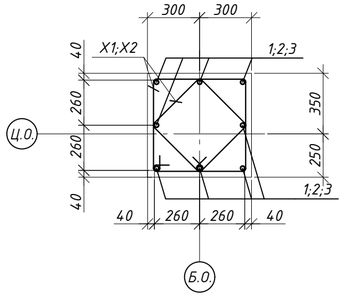

Разрез 2 - 2

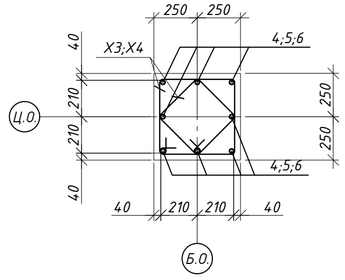

Разрез 3 - 3

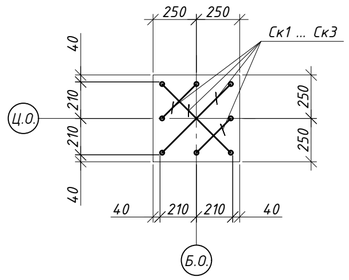


Ведомость деталей

Поз.	Эскиз
Ск1	220 / 560 / 220 — по н.г. L=1000
Ск3	220 / 280 / 220 — по н.г. L=720
Х1	620 / 520 / 520 / 620 — по в.г. L=2280
Х2	480 / 380 / 380 / 480 — по в.г. L=1720
Х3	520 / 420 / 420 / 520 — по в.г. L=1880
Х4	410 / 310 / 310 / 410 — по в.г. L=1440


Таблица размеров накладок

Марка эл-та	dн	L	вес
	мм.		кг.
Н1	32	320	2.01
Н2	28	280	1.35
Н3	25	250	0.96
Н4	22	220	0.66
Н5	20	200	0.49

Сетка С1

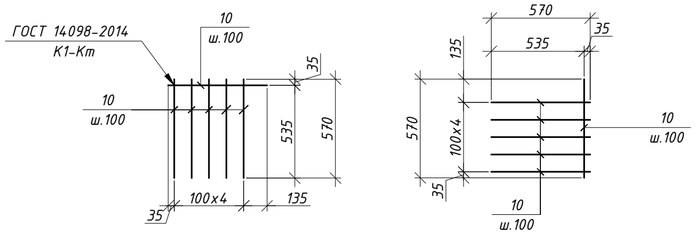

Сетка С2

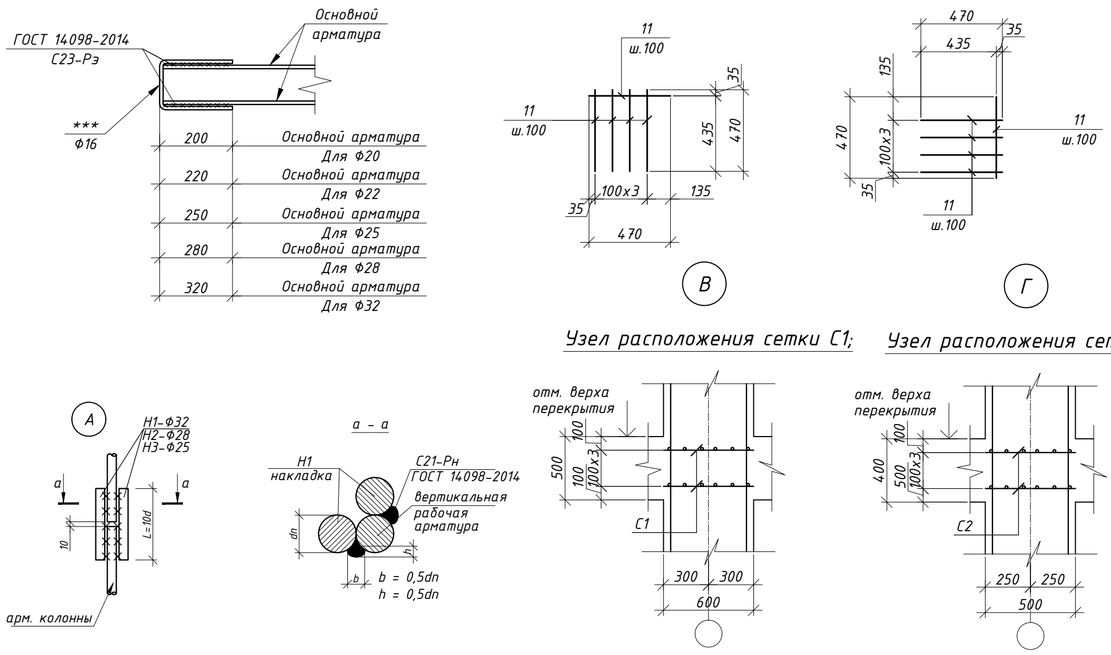

Узел расположения сетки С1;

Узел расположения сетки С2

1. Схему расположения монолитных колонн см. листы КЖ-2.1; .... 2.7.
2. Бетонирование колонн в местах примыкания ригелей и монолитной плиты вести после установки рабочей арматуры ригеля, плиты и сеток косвенного армирования.
3. Сварные соединения выполнять ручной электродуговой сваркой, электроды типа Э-42А по ГОСТ 9467-75.
4. Защитный слой бетона принят по наружной грани продольной арматуры.
5. Стыковку продольной арматуры выполнять по ГОСТ 14098-91, тип соединения С21-Рн.
6. Сетки С-1 составляются из двух взаимно перпендикулярных элементов.

Спецификация элементов

Поз.	Обозначение	Наименование	Кол.	Масса ед.кг	Примечание
		Колонна Км-7.1			882.63
Х1*	ГОСТ 34028-2016(214-210-0101-0002)	Ф 8 А 240 L= 2280	55	0.90	49.48
Х2*	ГОСТ 34028-2016(214-210-0101-0002)	Ф 8 А 240 L= 1720	55	0.68	37.33
Х3*	ГОСТ 34028-2016(214-210-0101-0002)	Ф 8 А 240 L= 1880	67	0.74	49.70
Х4*	ГОСТ 34028-2016(214-210-0101-0002)	Ф 8 А 240 L= 1440	67	0.57	38.07
Ск1*	ГОСТ 34028-2016(214-210-0502-0003)	Ф 16 А500С L= 1000	2	1.58	3.16
Ск3*	ГОСТ 34028-2016(214-210-0502-0003)	Ф 16 А500С L= 720	2	1.14	2.27
1	ГОСТ 34028-2016(214-210-0502-0008)	Ф 28 А500С L= 4270	8	20.64	165.12
Н2	ГОСТ 34028-2016(214-210-0502-0008)	Ф 28 А500С L= 220	32	1.06	34.03
2	ГОСТ 34028-2016(214-210-0502-0007)	Ф 25 А500С L= 3900	4	15.03	60.11
3	ГОСТ 34028-2016(214-210-0502-0007)	Ф 25 А500С L= 4000	4	15.41	61.65
Н3	ГОСТ 34028-2016(214-210-0502-0007)	Ф 25 А500С L= 220	32	0.85	27.13
4	ГОСТ 34028-2016(214-210-0502-0007)	Ф 25 А500С L= 3900	8	15.03	120.22
5	ГОСТ 34028-2016(214-210-0502-0007)	Ф 25 А500С L= 5680	4	21.89	87.55
6	ГОСТ 34028-2016(214-210-0502-0007)	Ф 25 А500С L= 5080	4	19.58	78.30
С1	данные лист	Сетка С1	8	4.22	33.74
С2	данные лист	Сетка С2	12	2.90	34.77
		Материалы:			
	(212-101-0901)	Класс бетона С 20/25 (В25), м³			5.49
		Сетка С1			
10	ГОСТ 34028-2016(214-210-0501-0005)	Ф 10 А500С L= 570	12	0.35	4.22
		Сетка С2			
11	ГОСТ 34028-2016(214-210-0501-0005)	Ф 10 А500С L= 470	10	0.29	2.90

Позиции со "*" см. "Ведомость деталей" см. на данном листе.


Ведомость расхода стали, кг

Марка элемента	Изделия арматурные									Всего
	Арматура класса									
	А240			А500С						
	ГОСТ 34028-2016(214-210-0101)			ГОСТ 34028-2016(214-210-0502)						
	Ф6	Ф8	Итого	Ф10	Ф16	Ф20	Ф25	Ф28	Итого	
Колонна Км-7.1	0.00	174.58	174.58	68.51	5.43	---	435.0	199	708.05	882.63


Изм.	Кол.уч.	Лист	N док.	Подп.	Дата	65П-АИП-2024-1-КЖ		
						Строительство многопрофильной больницы на 250 коек с онкологическим центром и поликлиникой на 350 посещений, по адресу: Медеуский район, г. Алматы		
						"Блок 1 Секция 1"	Стадия: РП	Лист: 4.13
ГКП		Курал М						Листов:
Проверил		Кыдырбай А				Колонна Км-7.1	АстанаИнжПроект	
Разраб.		Ауез Б						
Н.контроль		Ешенкулова						

Формат А2


Колонна Км-7.2

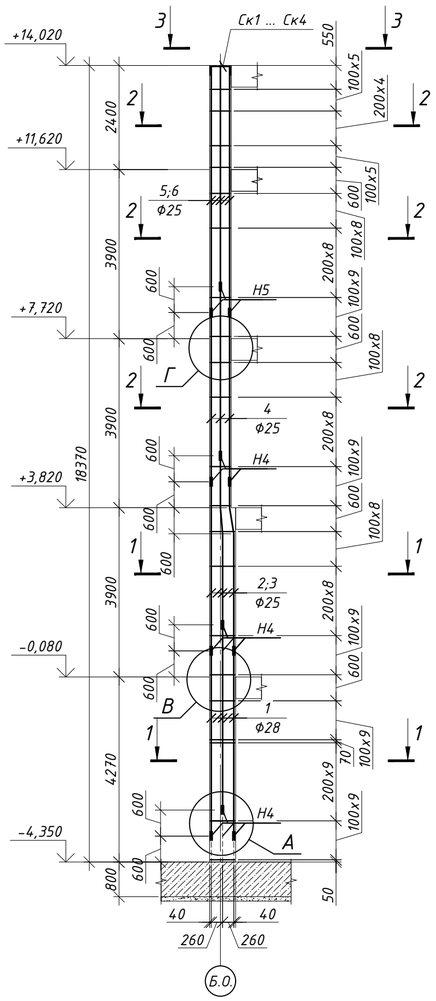


Разрез 1 - 1

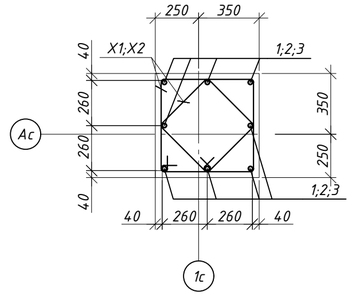

Разрез 2 - 2

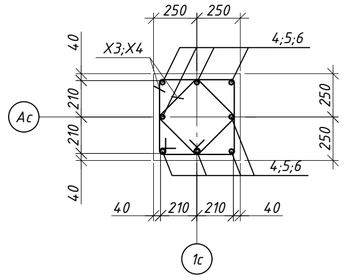

Разрез 3 - 3

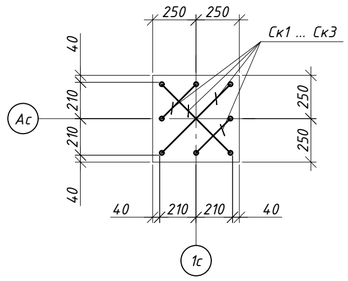


Ведомость деталей

Поз.	Эскиз
Ск1	220 / 560 / 220 — по н.г. — L=1000
Ск3	220 / 280 / 220 — по н.г. — L=720
X1	620 / 520 / 620 — по в.г. — L=2280
X2	480 / 380 / 480 — по в.г. — L=1720
X3	520 / 420 / 520 — по в.г. — L=1880
X4	410 / 310 / 410 — по в.г. — L=1440


Таблица размеров накладок

Марка эл-та	dн	L	вес
	мм.		кг.
Н1	32	320	2.01
Н2	28	280	1.35
Н3	25	250	0.96
Н4	22	220	0.66
Н5	20	200	0.49


Сетка С1

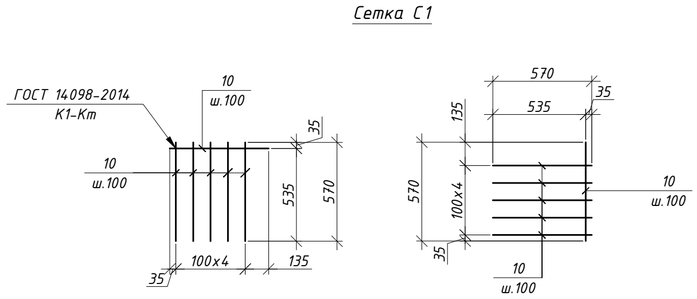


Сетка С2

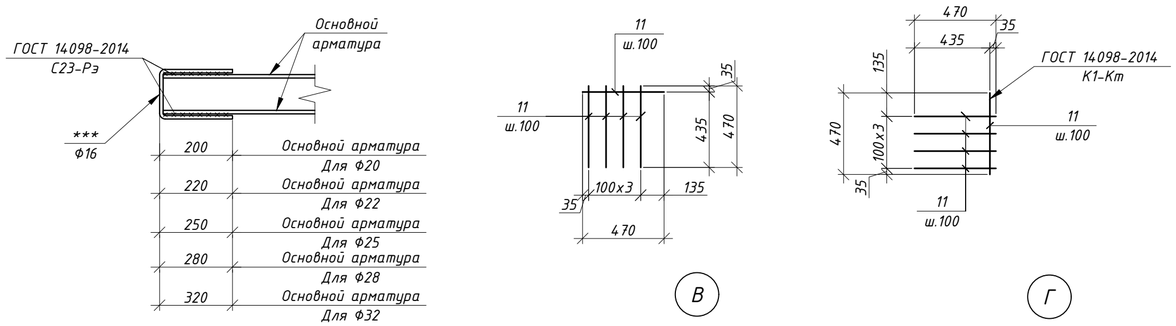

Узел расположения сетки С1;

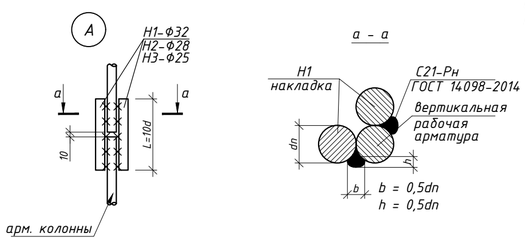

Узел расположения сетки С2

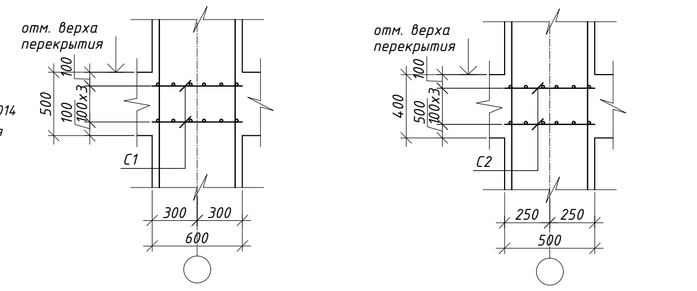

Спецификация элементов

Поз.	Обозначение	Наименование	Кол.	Масса ед.кг	Примечание
		Колонна Км-7.2			882.63
X1*	ГОСТ 34028-2016(214-210-0101-0002)	Ф 8 А 240 L= 2280	55	0.90	49.48
X2*	ГОСТ 34028-2016(214-210-0101-0002)	Ф 8 А 240 L= 1720	55	0.68	37.33
X3*	ГОСТ 34028-2016(214-210-0101-0002)	Ф 8 А 240 L= 1880	67	0.74	49.70
X4*	ГОСТ 34028-2016(214-210-0101-0002)	Ф 8 А 240 L= 1440	67	0.57	38.07
Ск1*	ГОСТ 34028-2016(214-210-0502-0003)	Ф 16 А500С L= 1000	2	1.58	3.16
Ск3*	ГОСТ 34028-2016(214-210-0502-0003)	Ф 16 А500С L= 720	2	1.14	2.27
1	ГОСТ 34028-2016(214-210-0502-0008)	Ф 28 А500С L= 4270	8	20.64	165.12
Н2	ГОСТ 34028-2016(214-210-0502-0008)	Ф 28 А500С L= 220	32	1.06	34.03
2	ГОСТ 34028-2016(214-210-0502-0007)	Ф 25 А500С L= 3900	4	15.03	60.11
3	ГОСТ 34028-2016(214-210-0502-0007)	Ф 25 А500С L= 4000	4	15.41	61.65
Н3	ГОСТ 34028-2016(214-210-0502-0007)	Ф 25 А500С L= 220	32	0.85	27.13
4	ГОСТ 34028-2016(214-210-0502-0007)	Ф 25 А500С L= 3900	8	15.03	120.22
5	ГОСТ 34028-2016(214-210-0502-0007)	Ф 25 А500С L= 5680	4	21.89	87.55
6	ГОСТ 34028-2016(214-210-0502-0007)	Ф 25 А500С L= 5080	4	19.58	78.30
С1	данные лист	Сетка С1	8	4.22	33.74
С2	данные лист	Сетка С2	12	2.90	34.77
		Материалы:			
	(212-101-0901)	Класс бетона С 20/25 (В25), м³			5.49
		Сетка С1			
10	ГОСТ 34028-2016(214-210-0501-0005)	Ф 10 А500С L= 570	12	0.35	4.22
		Сетка С2			
11	ГОСТ 34028-2016(214-210-0501-0005)	Ф 10 А500С L= 470	10	0.29	2.90

Позиции со "*" см. "Ведомость деталей" см. на данном листе.


Ведомость расхода стали, кг

Марка элемента	Изделия арматурные									Всего
	Арматура класса									
	А240			А500С						
	ГОСТ 34028-2016(214-210-0101)			ГОСТ 34028-2016(214-210-0502)						
	Ф6	Ф8	Итого	Ф10	Ф16	Ф20	Ф25	Ф28	Итого	
Колонна Км-7.2	0.00	174.58	174.58	68.51	5.43	---	435.0	199	708.05	882.63


1. Схему расположения монолитных колонн см. листы КЖ-2.1; .... 2.7.
2. Бетонирование колонн в местах примыкания ригелей и монолитной плиты вести после установки рабочей арматуры ригеля, плиты и сеток косвенного армирования.
3. Сварные соединения выполнять ручной электродуговой сваркой, электроды типа Э-42А по ГОСТ 9467-75.
4. Защитный слой бетона принят по наружной грани продольной арматуры.
5. Стыковку продольной арматуры выполнять по ГОСТ 14098-91, тип соединения С21-Рн.
6. Сетки С-1 составляются из двух взаимно перпендикулярных элементов.

Изм.	Кол.уч.	Лист	N док.	Подп.	Дата	65П-АИП-2024-1-КЖ		
						Строительство многопрофильной больницы на 250 коек с онкологическим центром и поликлиникой на 350 посещений, по адресу: Медеуский район, г. Алматы		
						"Блок 1 Секция 1"	Стадия: РП	Лист: 4.14 / Листов:
ГКП		Курал М				Колонна Км-7.2	АстанаИнжПроект	
Проверил		Кыдырбай А						
Разраб.		Ауез Б						
Н.контроль		Ешенкулова					Формат А2	


Колонна Км-8.1

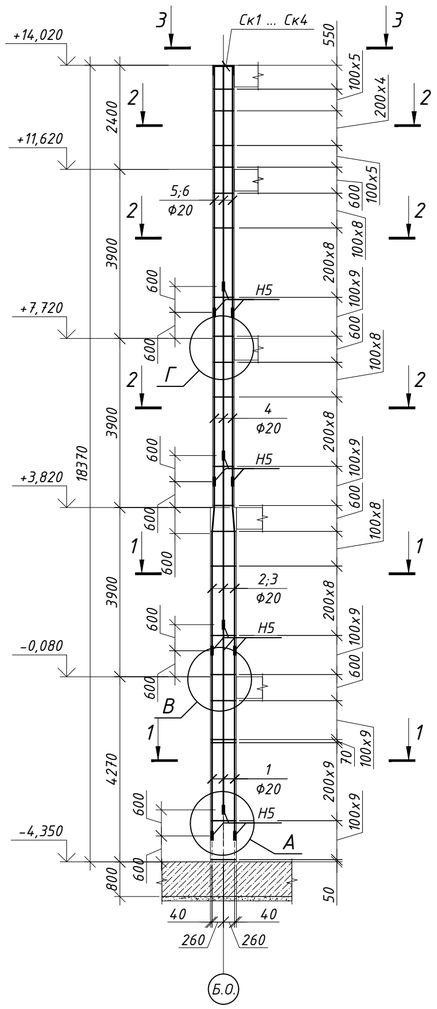


Разрез 1 - 1

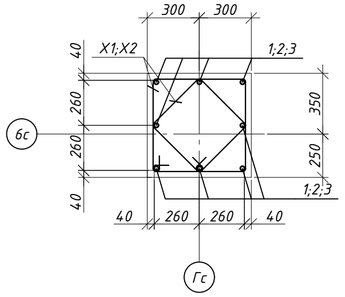

Разрез 2 - 2

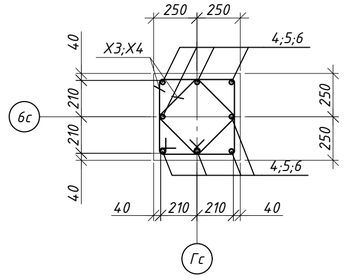

Разрез 3 - 3

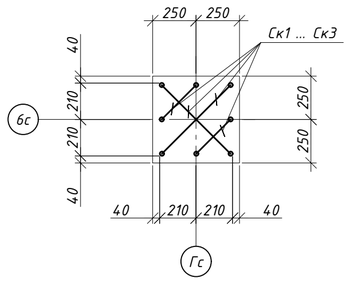

Ведомость деталей

Поз.	Эскиз
Ск1	220, 560, 220; по н.г. L=1000
Ск2	220, 440, 220; по н.г. L=880
Ск3	220, 280, 220; по н.г. L=720
Ск4	220, 130, 220; по н.г. L=570
X1	620, 520, 620; по в.г. L=2280
X2	480, 380, 480; по в.г. L=1720
X3	520, 420, 520; по в.г. L=1880
X4	410, 310, 410; по в.г. L=1440

Спецификация элементов

Поз.	Обозначение	Наименование	Кол.	Масса ед.кг	Примечание
		Колонна Км-8.1			633.08
X1*	ГОСТ 34028-2016(214-210-0101-0002)	Ф 8 А 240 L= 2280	55	0.90	49.48
X2*	ГОСТ 34028-2016(214-210-0101-0002)	Ф 8 А 240 L= 1720	55	0.68	37.33
X3*	ГОСТ 34028-2016(214-210-0101-0002)	Ф 8 А 240 L= 1880	67	0.74	49.70
X4*	ГОСТ 34028-2016(214-210-0101-0002)	Ф 8 А 240 L= 1440	67	0.57	38.07
Ск1*	ГОСТ 34028-2016(214-210-0502-0003)	Ф 16 А500С L= 1000	2	1.58	3.16
Ск2*	ГОСТ 34028-2016(214-210-0502-0003)	Ф 16 А500С L= 880	2	1.39	2.78
Ск3*	ГОСТ 34028-2016(214-210-0502-0003)	Ф 16 А500С L= 720	2	1.14	2.27
Ск4*	ГОСТ 34028-2016(214-210-0502-0003)	Ф 16 А500С L= 570	2	0.90	1.80
1	ГОСТ 34028-2016(214-210-0502-0005)	Ф 20 А500С L= 4270	8	10.53	84.24
Н5	ГОСТ 34028-2016(214-210-0502-0005)	Ф 20 А500С L= 220	64	0.54	34.72
2	ГОСТ 34028-2016(214-210-0502-0005)	Ф 20 А500С L= 3900	4	9.62	38.47
3	ГОСТ 34028-2016(214-210-0502-0005)	Ф 20 А500С L= 4000	4	9.86	39.46
4	ГОСТ 34028-2016(214-210-0502-0005)	Ф 20 А500С L= 3900	8	9.62	76.94
5	ГОСТ 34028-2016(214-210-0502-0005)	Ф 20 А500С L= 5680	4	14.01	56.03
6	ГОСТ 34028-2016(214-210-0502-0005)	Ф 20 А500С L= 5080	4	12.53	50.11
С1	данные лист	Сетка С1	8	4.22	33.74
С2	данные лист	Сетка С2	12	2.90	34.77
		Материалы:			
	(212-101-0901)	Класс бетона С 20/25 (В25), м³			5.49
		Сетка С1			
10	ГОСТ 34028-2016(214-210-0501-0005)	Ф 10 А500С L= 570	12	0.35	4.22
		Сетка С2			
11	ГОСТ 34028-2016(214-210-0501-0005)	Ф 10 А500С L= 470	10	0.29	2.90

Позиции со "*" см. "Ведомость деталей" см. на данном листе.

Сетка С1


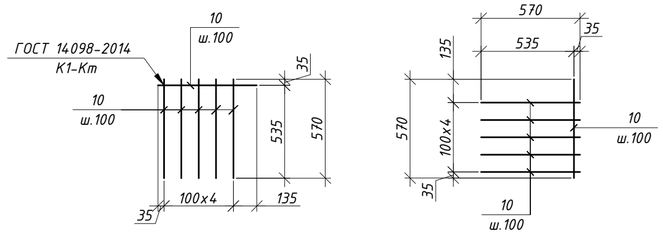


Таблица размеров накладок

Марка эл-та	dн мм.	L мм.	вес кг.
Н1	32	320	2.01
Н2	28	280	1.35
Н3	25	250	0.96
Н4	22	220	0.66
Н5	20	200	0.49


Сетка С2

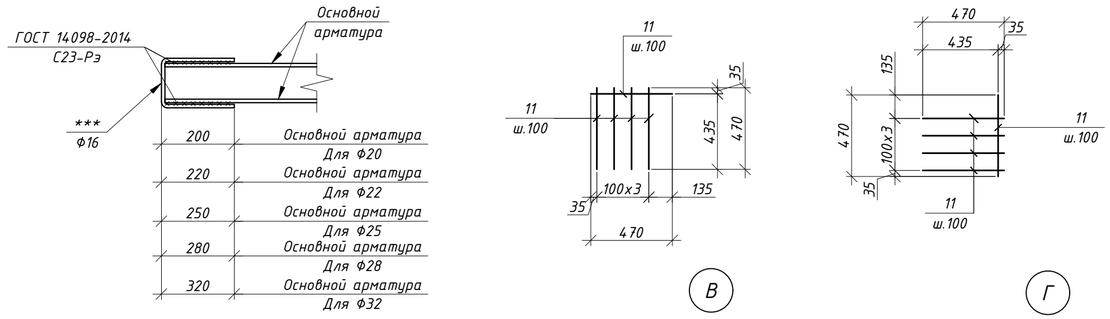


Ведомость расхода стали, кг


Марка элемента	Изделия арматурные									Всего
	Арматура класса									
	А240			А500С						
	ГОСТ 34028-2016(214-210-0101)			ГОСТ 34028-2016(214-210-0502)						
	Ф6	Ф8	Итого	Ф10	Ф16	Ф20	Ф25	Ф28	Итого	
Колонна Км-8.1	0.00	174.58	174.58	68.51	10.01	379.98	---	---	458.50	633.08


Узел расположения сетки С1;

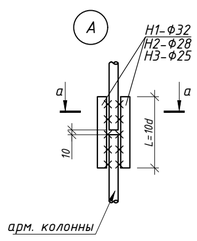

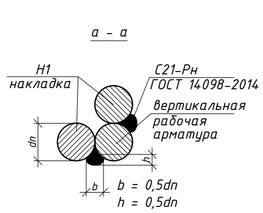

Узел расположения сетки С2

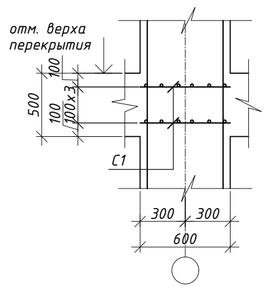

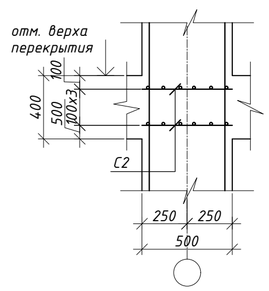


1. Схему расположения монолитных колонн см. листы КЖ-2.1; .... 2.7.
2. Бетонирование колонн в местах примыкания ригелей и монолитной плиты вести после установки рабочей арматуры ригеля, плиты и сеток косвенного армирования.
3. Сварные соединения выполнять ручной электродуговой сваркой, электроды типа Э-42А по ГОСТ 9467-75.
4. Защитный слой бетона принят по наружной грани продольной арматуры.
5. Стыковку продольной арматуры выполнять по ГОСТ 14098-91, тип соединения С21-Рн.
6. Сетки С-1 составляются из двух взаимно перпендикулярных элементов.


						65П-АИП-2024-1-КЖ
						Строительство многопрофильной больницы на 250 коек с онкологическим центром и поликлиникой на 350 посещений, по адресу: Медеуский район, г. Алматы
Изм.	Кол.уч.	Лист	N док.	Подп.	Дата	
ГКП		Курал М				"Блок 1 Секция 1"
Проверил		Кыдырбай А				Стадия: РП; Лист: 4.15; Листов:
Разраб.		Ауез Б				Колонна Км-8.1
Н.контроль		Ешенкулова				АстанаИнжПроект

Формат А2


Колонна Км-9.1

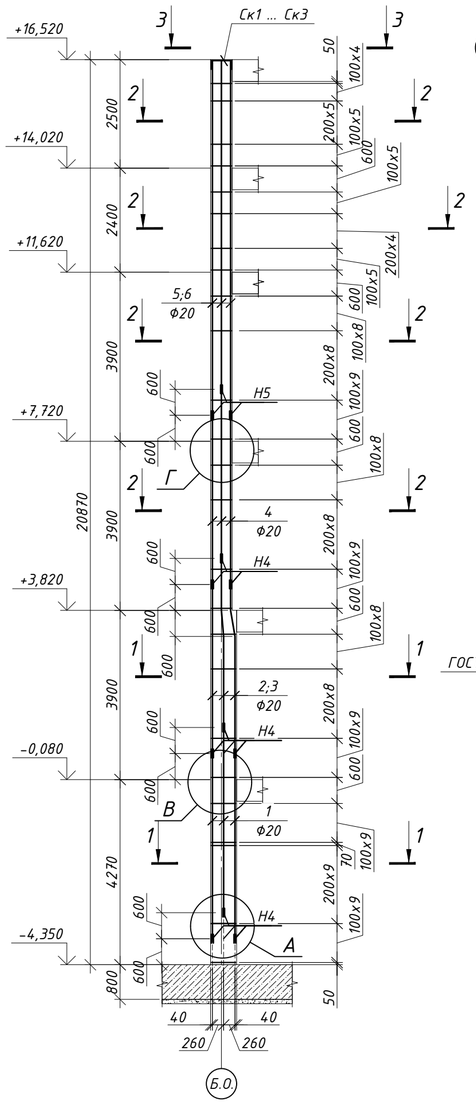


Разрез 1 - 1

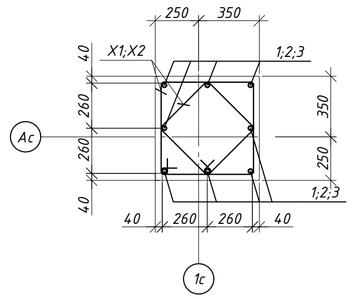

Разрез 2 - 2

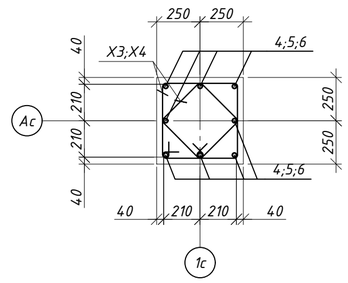

Разрез 3 - 3

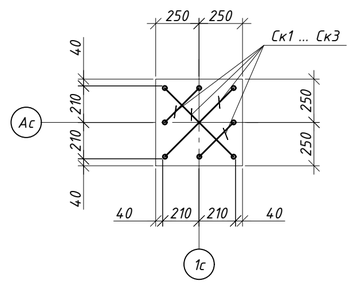


Ведомость деталей

Поз.	Эскиз
Ск1	220; 560; 220; по н.г. L=1000
Ск3	220; 280; 220; по н.г. L=720
Х1	620; 520; 620; 520; по в.г. L=2280
Х2	480; 380; 480; 380; по в.г. L=1720
Х3	520; 420; 520; 420; по в.г. L=1880
Х4	410; 310; 410; 310; по в.г. L=1440


Таблица размеров накладок

Марка эл-та	dн, мм.	L, мм.	вес, кг.
Н1	32	320	2.01
Н2	28	280	1.35
Н3	25	250	0.96
Н4	22	220	0.66
Н5	20	200	0.49

Сетка С1

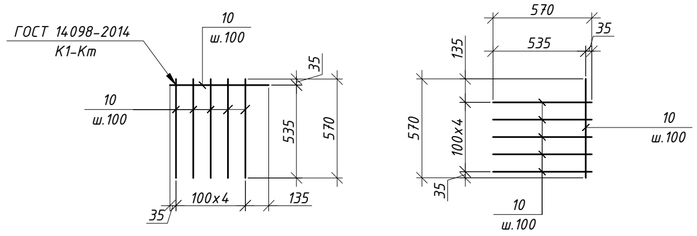

Сетка С2

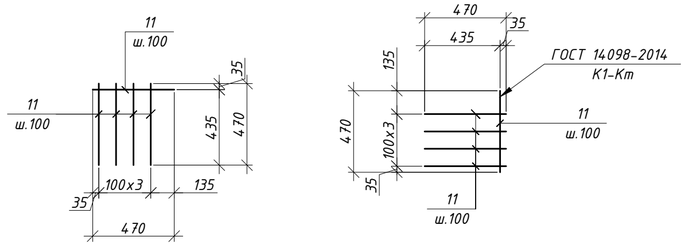

Спецификация элементов


Поз.	Обозначение	Наименование	Кол.	Масса ед.кг	Примечание
		Колонна Км-9.1			709.07
Х1*	ГОСТ 34028-2016(214-210-0101-0002)	Ф 8 А 240 L= 2280	55	0.90	49.48
Х2*	ГОСТ 34028-2016(214-210-0101-0002)	Ф 8 А 240 L= 1720	55	0.68	37.33
Х3*	ГОСТ 34028-2016(214-210-0101-0002)	Ф 8 А 240 L= 1880	82	0.74	60.83
Х4*	ГОСТ 34028-2016(214-210-0101-0002)	Ф 8 А 240 L= 1440	82	0.57	46.59
Ск1*	ГОСТ 34028-2016(214-210-0502-0003)	Ф 16 А500С L= 1000	2	1.58	3.16
Ск3*	ГОСТ 34028-2016(214-210-0502-0003)	Ф 16 А500С L= 720	2	1.14	2.27
1	ГОСТ 34028-2016(214-210-0502-0005)	Ф 20 А500С L= 4270	8	10.53	84.24
Н5	ГОСТ 34028-2016(214-210-0502-0005)	Ф 20 А500С L= 220	64	0.54	34.72
2	ГОСТ 34028-2016(214-210-0502-0005)	Ф 20 А500С L= 3900	4	9.62	38.47
3	ГОСТ 34028-2016(214-210-0502-0005)	Ф 20 А500С L= 4000	4	9.86	39.46
4	ГОСТ 34028-2016(214-210-0502-0005)	Ф 20 А500С L= 3900	8	9.62	76.94
5	ГОСТ 34028-2016(214-210-0502-0005)	Ф 20 А500С L= 8180	4	20.17	80.69
6	ГОСТ 34028-2016(214-210-0502-0005)	Ф 20 А500С L= 7580	4	18.69	74.77
С1	данные лист	Сетка С1	8	4.22	33.74
С2	данные лист	Сетка С2	16	2.90	46.36
		Материалы:			
	(212-101-0901)	Класс бетона С 20/25 (В25), м³			6.37
		Сетка С1			
10	ГОСТ 34028-2016(214-210-0501-0005)	Ф 10 А500С L= 570	12	0.35	4.22
		Сетка С2			
11	ГОСТ 34028-2016(214-210-0501-0005)	Ф 10 А500С L= 470	10	0.29	2.90


Позиции со "*" см. "Ведомость деталей" см. на данном листе.


Ведомость расхода стали, кг

Марка элемента	Изделия арматурные									Всего
	Арматура класса									
	А240			А500С						
	ГОСТ 34028-2016(214-210-0101)			ГОСТ 34028-2016(214-210-0502)						
	Ф6	Ф8	Итого	Ф10	Ф16	Ф20	Ф25	Ф28	Итого	
Колонна Км-9.1	0.00	194.23	194.23	80.10	5.43	429.31	---	---	514.84	709.07


Узел расположения сетки С1;

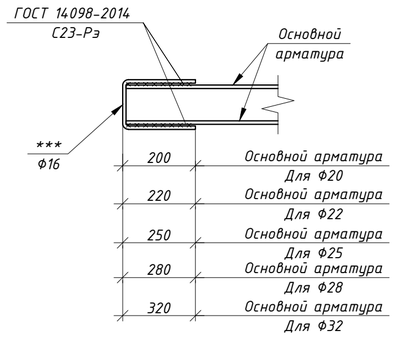

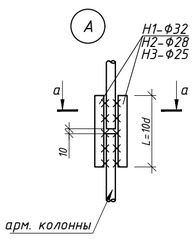

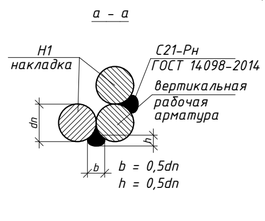


В

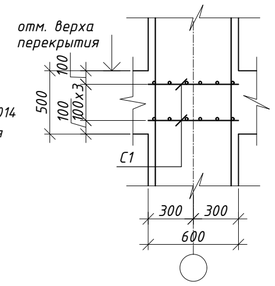

Узел расположения сетки С2

Г

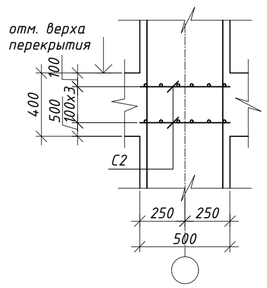


1. Схему расположения монолитных колонн см. листы КЖ-2.1; .... 2.7.
2. Бетонирование колонн в местах примыкания ригелей и монолитной плиты вести после установки рабочей арматуры ригеля, плиты и сеток косвенного армирования.
3. Сварные соединения выполнять ручной электродуговой сваркой, электроды типа Э-42А по ГОСТ 9467-75.
4. Защитный слой бетона принят по наружной грани продольной арматуры.
5. Стыковку продольной арматуры выполнять по ГОСТ 14098-91, тип соединения С21-Рн.
6. Сетки С-1 составляются из двух взаимно перпендикулярных элементов.


Изм.	Кол.уч.	Лист	N док.	Подп.	Дата	65П-АИП-2024-1-КЖ		
						Строительство многопрофильной больницы на 250 коек с онкологическим центром и поликлиникой на 350 посещений, по адресу: Медеуский район, г. Алматы		
						"Блок 1 Секция 1"	Стадия: РП	Лист: 4.16
ГКП		Курал М						
Проверил		Кыдырбай А				Колонна Км-9.1	АстанаИнжПроект	
Разраб.		Ауез Б						
Н.контроль		Ешенкулова						

Формат А2


Колонна Км-9.2

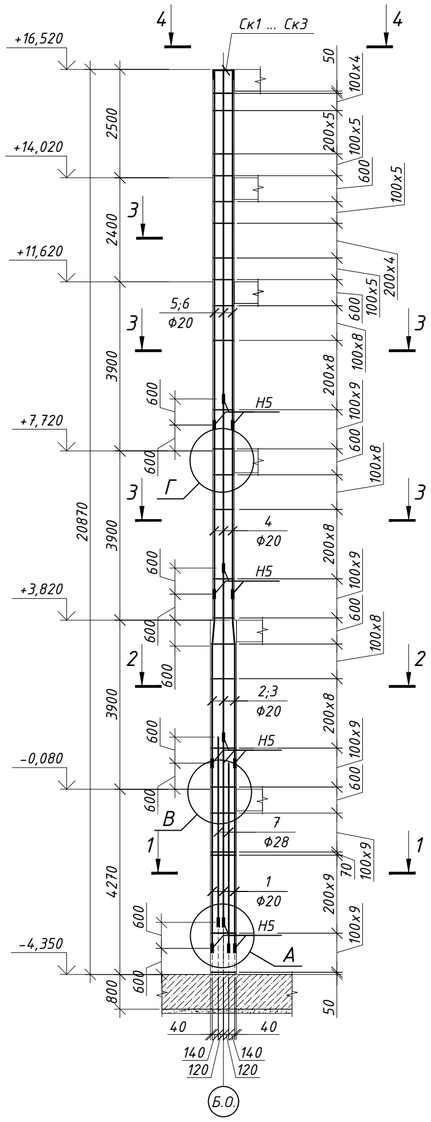


Разрез 1 - 1

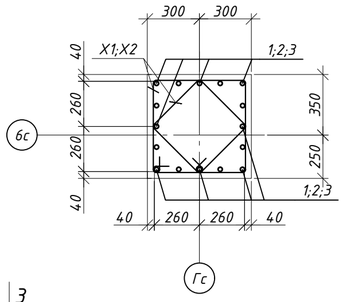


Разрез 2 - 2

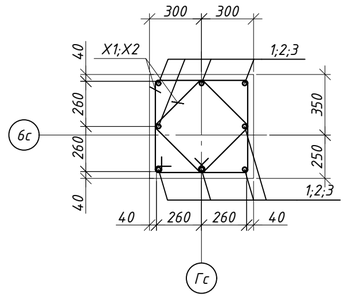

Разрез 3 - 3

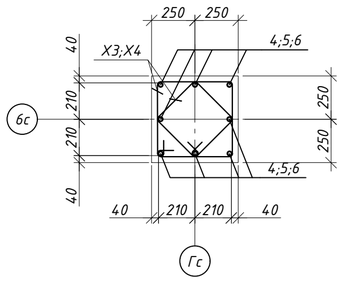

Разрез 4 - 4

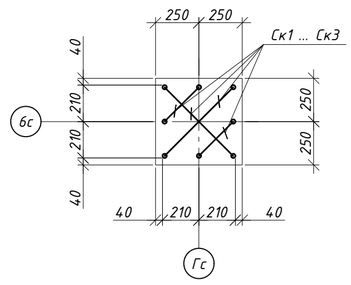


Ведомость деталей

Поз.	Эскиз
Ск1	220, 560, 220; по н.г. L=1000
Ск3	220, 280, 220; по н.г. L=720
Х1	620, 520, 620, 520; по в.г. L=2280
Х2	480, 380, 480, 380; по в.г. L=1720
Х3	520, 420, 520, 420; по в.г. L=1880
Х4	410, 310, 410, 310; по в.г. L=1440


Таблица размеров накладок


Марка эл-та	dн	L	вес
	мм.		кг.
Н1	32	320	2.01
Н2	28	280	1.35
Н3	25	250	0.96
Н4	22	220	0.66
Н5	20	200	0.49


Сетка С1

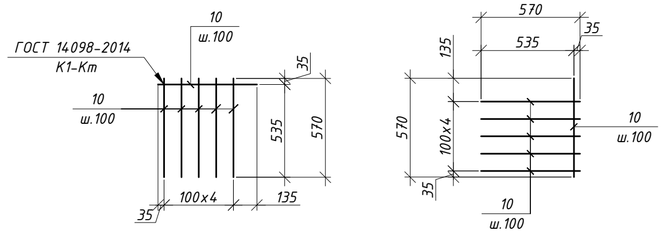


Сетка С2

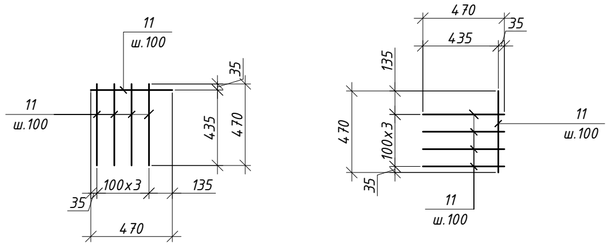

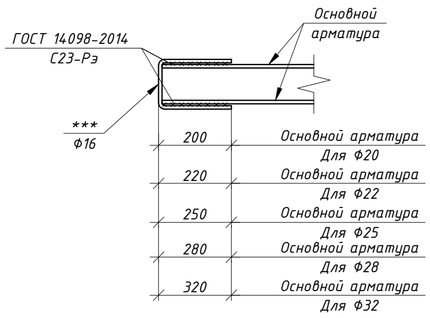


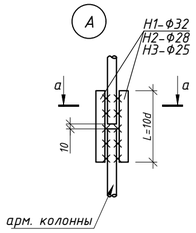

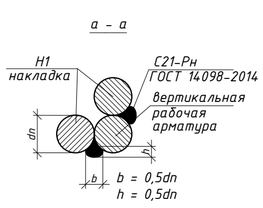


В

Узел расположения сетки С1;

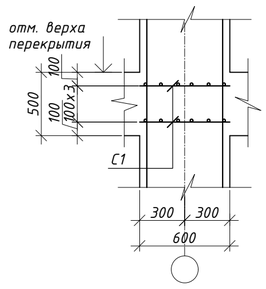

Г

Узел расположения сетки С2

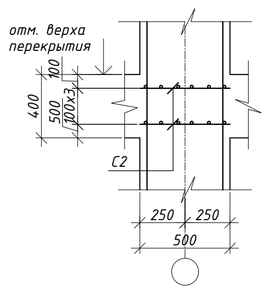

Спецификация элементов

Поз.	Обозначение	Наименование	Кол.	Масса ед.кг	Примечание
		Колонна Км-9.2			895.84
Х1*	ГОСТ 34028-2016(214-210-0101-0002)	Ф 8 А 240 L= 2280	55	0.90	49.48
Х2*	ГОСТ 34028-2016(214-210-0101-0002)	Ф 8 А 240 L= 1720	55	0.68	37.33
Х3*	ГОСТ 34028-2016(214-210-0101-0002)	Ф 8 А 240 L= 1880	82	0.74	60.83
Х4*	ГОСТ 34028-2016(214-210-0101-0002)	Ф 8 А 240 L= 1440	82	0.57	46.59
Ск1*	ГОСТ 34028-2016(214-210-0502-0003)	Ф 16 А500С L= 1000	2	1.58	3.16
Ск3*	ГОСТ 34028-2016(214-210-0502-0003)	Ф 16 А500С L= 720	2	1.14	2.27
1	ГОСТ 34028-2016(214-210-0502-0005)	Ф 20 А500С L= 4270	8	10.53	84.24
Н5	ГОСТ 34028-2016(214-210-0502-0005)	Ф 20 А500С L= 220	64	0.54	34.72
2	ГОСТ 34028-2016(214-210-0502-0005)	Ф 20 А500С L= 3900	4	9.62	38.47
3	ГОСТ 34028-2016(214-210-0502-0005)	Ф 20 А500С L= 4000	4	9.86	39.46
4	ГОСТ 34028-2016(214-210-0502-0005)	Ф 20 А500С L= 3900	8	9.62	76.94
5	ГОСТ 34028-2016(214-210-0502-0005)	Ф 20 А500С L= 8180	4	20.17	80.69
6	ГОСТ 34028-2016(214-210-0502-0005)	Ф 20 А500С L= 7580	4	18.69	74.77
7	ГОСТ 34028-2016(214-210-0502-0008)	Ф 28 А500С L= 4270	8	20.64	165.12
Н2	ГОСТ 34028-2016(214-210-0502-0008)	Ф 28 А500С L= 280	16	1.35	21.65
С1	данные лист	Сетка С1	8	4.22	33.74
С2	данные лист	Сетка С2	16	2.90	46.36
		Материалы:			
	(212-101-0901)	Класс бетона С 20/25 (В25), м³			6.12
		Сетка С1			
10	ГОСТ 34028-2016(214-210-0501-0005)	Ф 10 А500С L= 570	12	0.35	4.22
		Сетка С2			
11	ГОСТ 34028-2016(214-210-0501-0005)	Ф 10 А500С L= 470	10	0.29	2.90

Позиции со "*" см. "Ведомость деталей" см. на данном листе.

Ведомость расхода стали, кг


Марка элемента	Изделия арматурные									Всего
	Арматура класса									
	А240			А500С						
	ГОСТ 34028-2016(214-210-0101)			ГОСТ 34028-2016(214-210-0502)						
	Ф6	Ф8	Итого	Ф10	Ф16	Ф20	Ф25	Ф28	Итого	
Колонна Км-9.2	0.00	194.23	194.23	80.10	5.43	429.31	---	186.77	701.61	895.84

1. Схему расположения монолитных колонн см. листы КЖ-2.1; .... 2.7.
2. Бетонирование колонн в местах примыкания ригелей и монолитной плиты вести после установки рабочей
арматуры ригеля, плиты и сеток косвенного армирования.
3. Сварные соединения выполнять ручной электродуговой сваркой, электроды типа Э-42А по ГОСТ 9467-75.
4. Защитный слой бетона принят по наружной грани продольной арматуры.
5. Стыковку продольной арматуры выполнять по ГОСТ 14098-91, тип соединения С21-Рн.
6. Сетки С-1 составляются из двух взаимно перпендикулярных элементов.


Изм.	Кол.уч.	Лист	N док.	Подп.	Дата	65П-АИП-2024-1-КЖ		
						Строительство многопрофильной больницы на 250 коек с онкологическим центром и поликлиникой на 350 посещений, по адресу: Медеуский район, г. Алматы		
						"Блок 1 Секция 1"	Стадия: РП	Лист: 4.17
ГКП		Курал М						Листов:
Проверил		Кыдырбай А				Колонна Км-9.2	АстанаИнжПроект	
Разраб.		Ауез Б						
Н.контроль		Ешенкулова						

Формат А2


Колонна Км-10.1

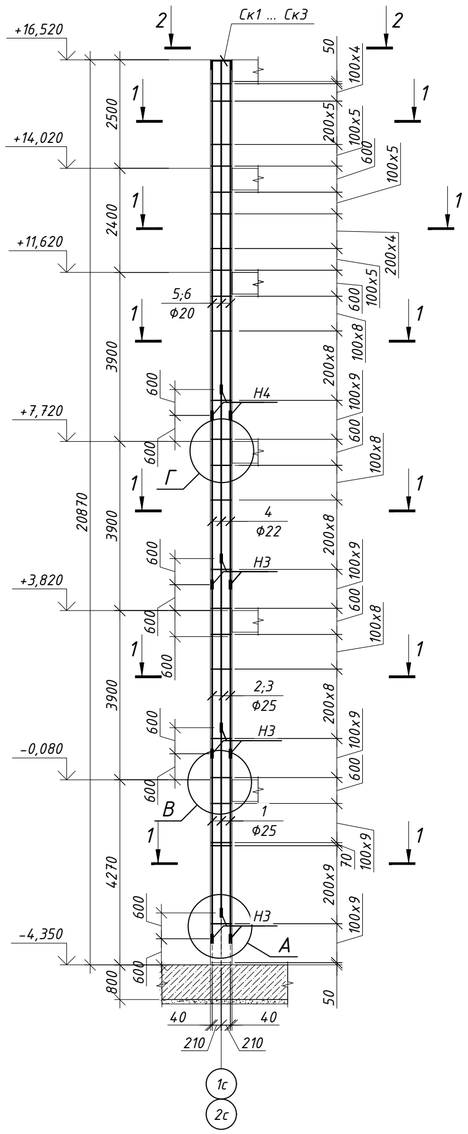

Разрез 1 - 1

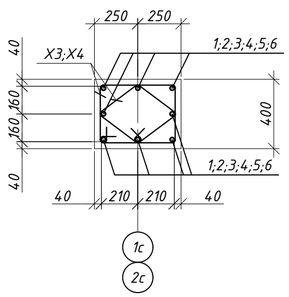

Разрез 2 - 2

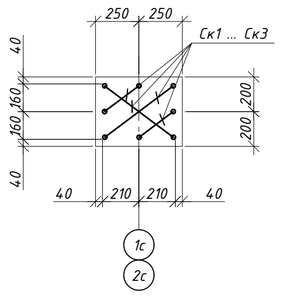

Ведомость деталей

Поз.	Эскиз
Ск1	220; 495; 220; по н.г. L=935
Ск3	220; 250; 220; по н.г. L=690
Х5	520; 320; 420; 420; по в.г. L=1680
Х6	370; 270; 270; 370; по в.г. L=1280

Таблица размеров накладок


Марка эл-та	dн	L	вес
	мм.		кг.
Н1	32	320	2.01
Н2	28	280	1.35
Н3	25	250	0.96
Н4	22	220	0.66
Н5	20	200	0.49

Спецификация элементов

Поз.	Обозначение	Наименование	Кол.	Масса ед.кг	Примечание
		Колонна Км-10.1			789.20
Х5*	ГОСТ 34028-2016(214-210-0101-0002)	ф 8 А 240 L= 1680	137	0.66	90.82
Х6*	ГОСТ 34028-2016(214-210-0101-0002)	ф 8 А 240 L= 1280	137	0.51	69.19
Ск1*	ГОСТ 34028-2016(214-210-0502-0003)	ф 16 А500С L= 935	2	1.48	2.95
Ск3*	ГОСТ 34028-2016(214-210-0502-0003)	ф 16 А500С L= 690	2	1.09	2.18
1	ГОСТ 34028-2016(214-210-0502-0007)	ф 25 А500С L= 4270	8	16.45	131.63
Н3	ГОСТ 34028-2016(214-210-0502-0007)	ф 25 А500С L= 250	64	0.96	61.65
2	ГОСТ 34028-2016(214-210-0502-0007)	ф 25 А500С L= 3900	4	15.03	60.11
3	ГОСТ 34028-2016(214-210-0502-0007)	ф 25 А500С L= 4000	4	15.41	61.65
4	ГОСТ 34028-2016(214-210-0502-0006)	ф 22 А500С L= 3900	8	11.64	93.10
Н4	ГОСТ 34028-2016(214-210-0502-0006)	ф 22 А500С L= 220	8	0.66	5.25
5	ГОСТ 34028-2016(214-210-0502-0005)	ф 20 А500С L= 8180	4	20.17	80.69
6	ГОСТ 34028-2016(214-210-0502-0005)	ф 20 А500С L= 7580	4	18.69	74.77
С1	данные лист	Сетка С3	24	2.30	55.19
		Материалы:			
	(212-101-0901)	Класс бетона С 20/25 (В25), м³			4.17
		Сетка С1			
10	ГОСТ 34028-2016(214-210-0501-0005)	ф 10 А500С L= 470	4	0.29	1.16
11	ГОСТ 34028-2016(214-210-0501-0005)	ф 10 А500С L= 370	5	0.23	1.14

Позиции со "*" см. "Ведомость деталей" см. на данном листе.


Сетка С3

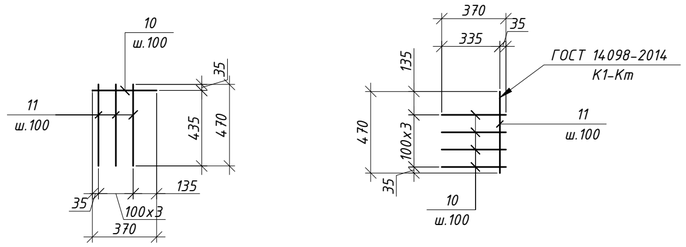



Ведомость расхода стали, кг

Марка элемента	Изделия арматурные									Всего
	Арматура класса									
	А240			А500С						
	ГОСТ 34028-2016(214-210-0101)			ГОСТ 34028-2016(214-210-0502)						
	Ф6	Ф8	Итого	Ф10	Ф16	Ф20	Ф22	Ф25	Итого	
Колонна Км-10.1	0.00	160.01	160.01	55.19	5.13	155.47	98.35	315.05	629.19	789.20

1. Схему расположения монолитных колонн см. листы КЖ-2.1; .... 2.7.
2. Бетонирование колонн в местах примыкания ригелей и монолитной плиты вести после установки рабочей
арматуры ригеля, плиты и сеток косвенного армирования.
3. Сварные соединения выполнять ручной электродуговой сваркой, электроды типа Э-42А по ГОСТ 9467-75.
4. Защитный слой бетона принят по наружной грани продольной арматуры.
5. Стыковку продольной арматуры выполнять по ГОСТ 14098-91, тип соединения С21-Рн.
6. Сетки С-1 составляются из двух взаимно перпендикулярных элементов.

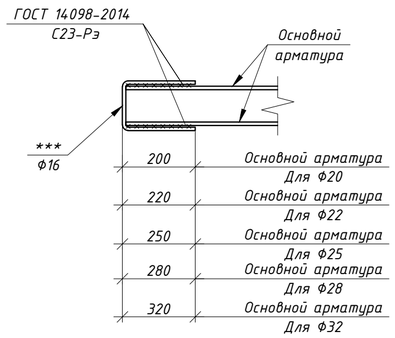


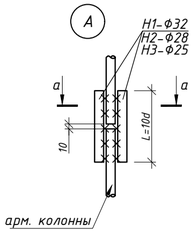

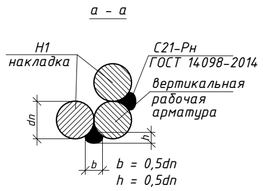

Г

Узел расположения сетки С3

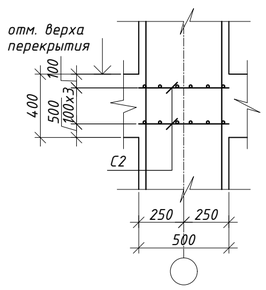

Изм.	Кол.уч	Лист	N док.	Подп.	Дата	65П-АИП-2024-1-КЖ		
						Строительство многопрофильной больницы на 250 коек с онкологическим центром и поликлиникой на 350 посещений, по адресу: Медеуский район, г. Алматы		
						"Блок 1 Секция 1"	Стадия: РП	Лист: 4.18
ГКП		Курал М						
Проверил		Кыдырбай А						
Разраб.		Ауез Б				Колонна Км-10.1	АстанаИнжПроект	
Н.контроль		Ешенкулова						

Формат А2