



Анкеровка

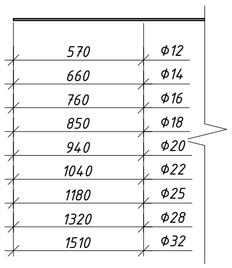


Узел стыковки вертикальной арматуры в нахлест и накладка

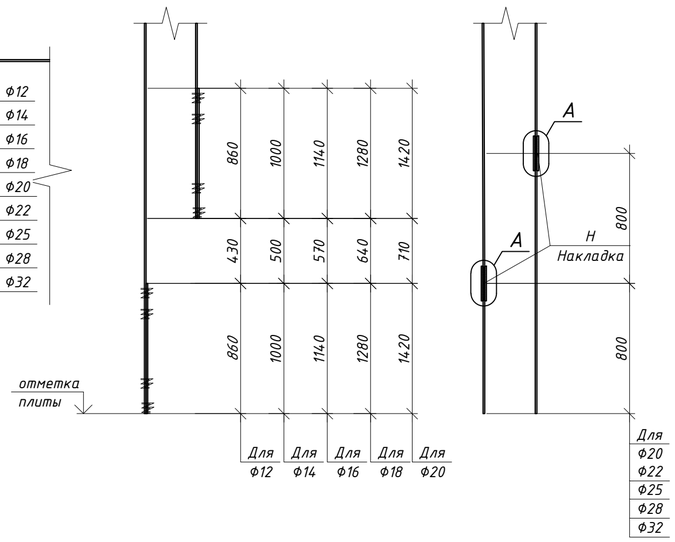

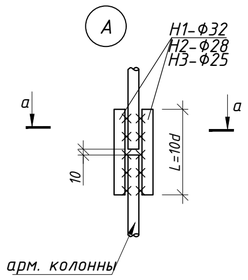

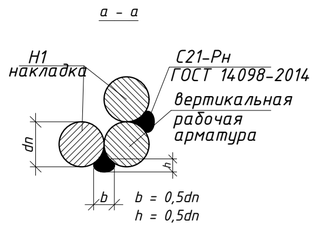


Фрагмент обрамления проема

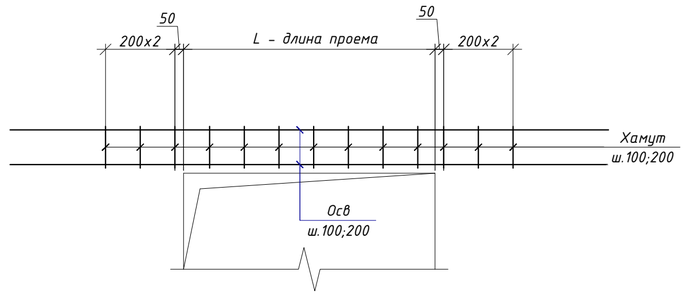

Узел стыковки Горизонтальной арматуры в нахлест

Б

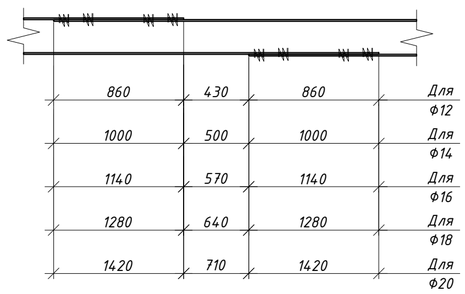

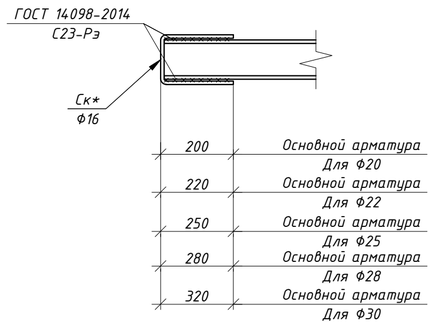


Таблица размеров Накладка

Марка эл-та	dн	L	вес
	мм.		кг.
H1	32	320	2.01
H2	28	280	1.35
H3	25	250	0.96
H4	22	220	0.66
H5	20	200	0.49

Взам. инв. №


Подп. и дата

Инв. № подл.


Изм.	Кол.уч.	Лист	N док.	Подп.	Дата	65П-АИП-2024-1-КЖ		
						Строительство многопрофильной больницы на 250 коек с онкологическим центром и поликлиникой на 350 посещений, по адресу: Медеуский район, г. Алматы		
						"Блок 1 Секция 1"	Стадия: РП	Лист: 5.1
ГКП		Курал М						
Проверил		Кыдырбай А				Узел стыковки арматуры нахлеста, накладка, анкеровки и Фрагмент обрамления проема	АстанаИнжПроект	
Разраб.		Ауез Б						
Н.контроль		Ешенкулова						

Формат А2


Опалубочный чертеж монолитной стены по оси 1с стена См-1 (тол.250мм)

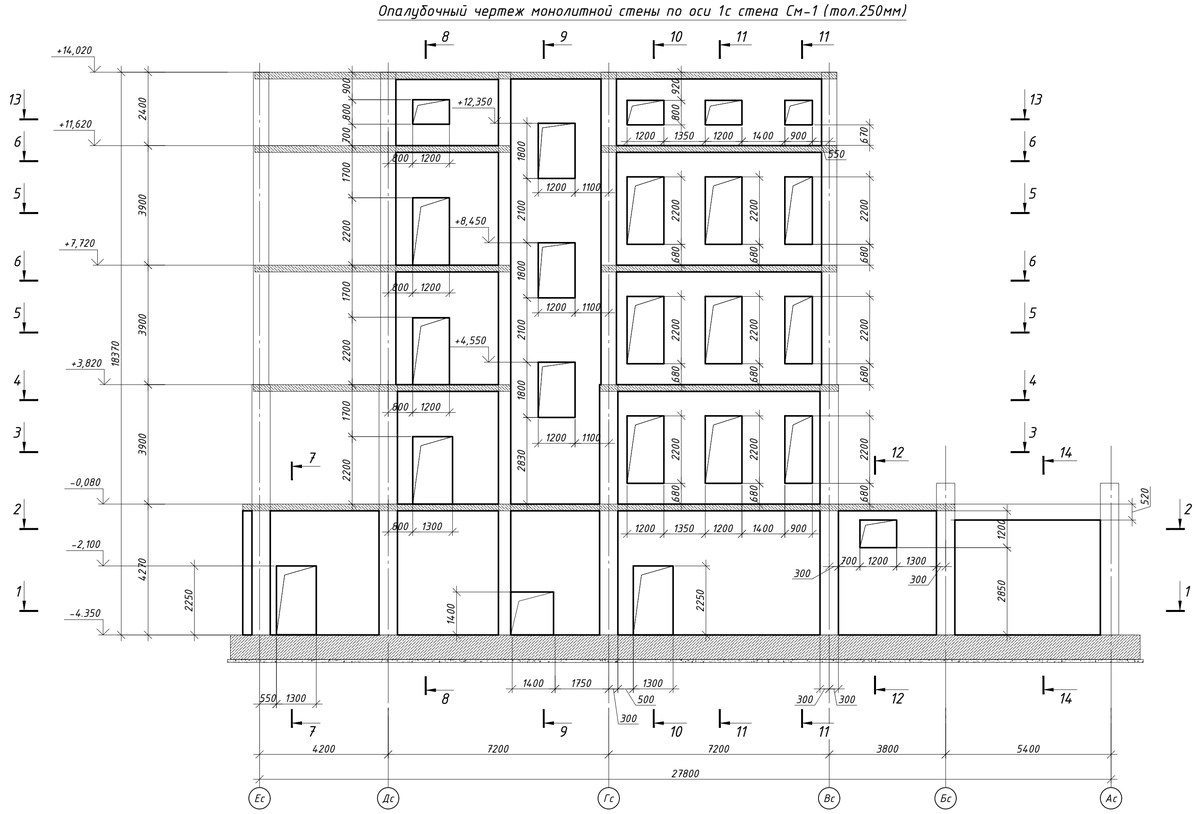


Разрез 1-1 (Опалубка) М 1:100

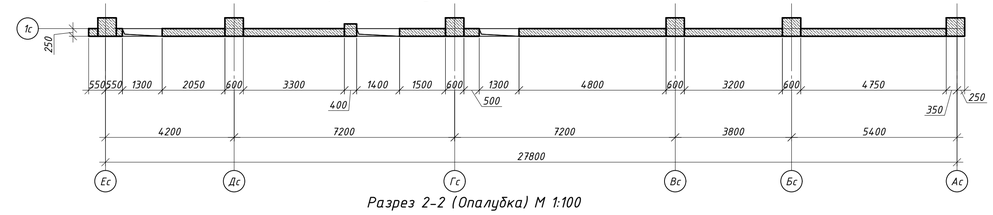


Разрез 2-2 (Опалубка) М 1:100

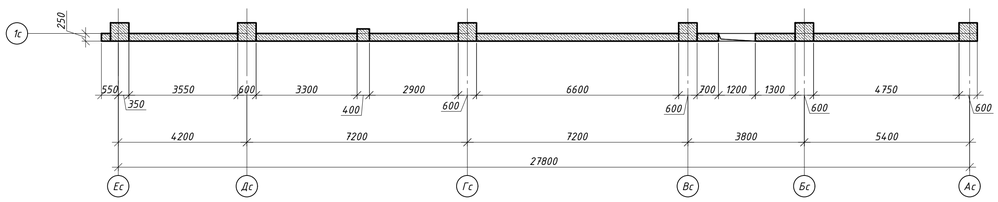


Разрез 3-3 (Опалубка) М 1:100

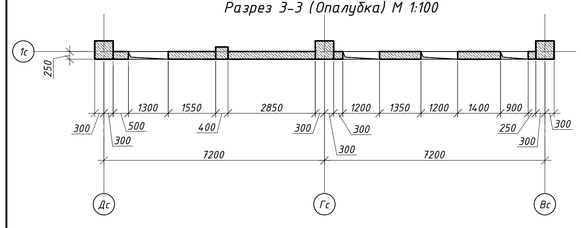


Разрез 4-4 (Опалубка) М 1:100

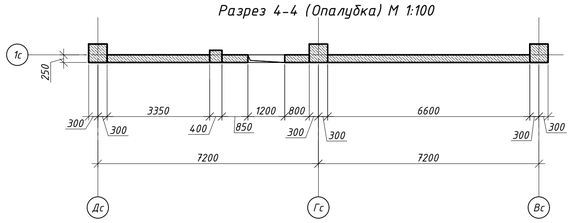


Разрез 5-5; 13-13 (Опалубка) М 1:100

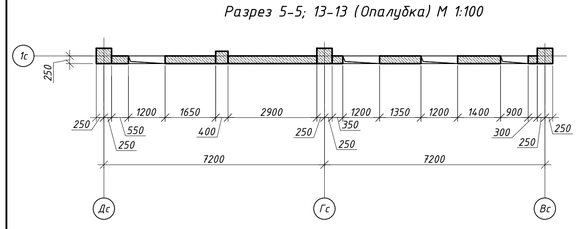


Разрез 6-6 (Опалубка) М 1:100

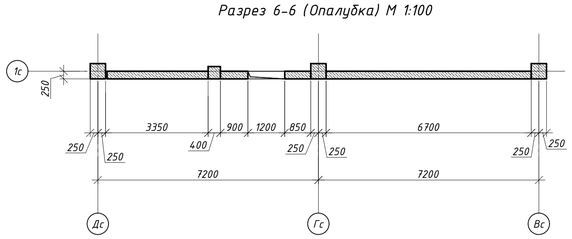


Разрез 7-7 (Опалубка)

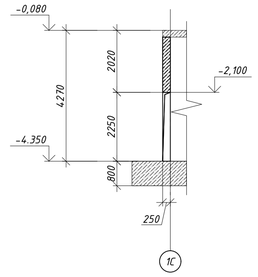


Разрез 8-8 (Опалубка)

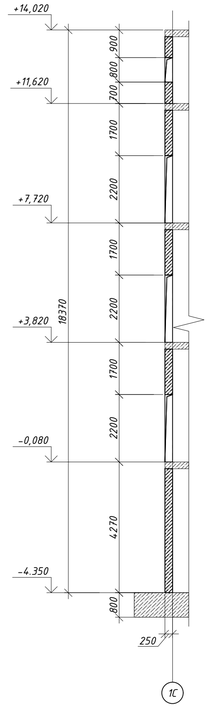


Разрез 9-9 (Опалубка)

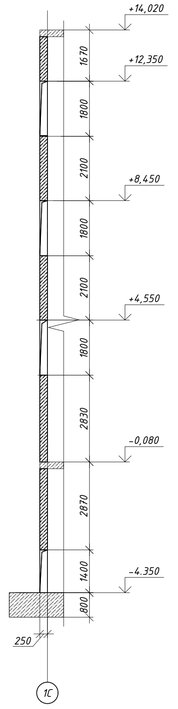


Разрез 10-10 (Опалубка)

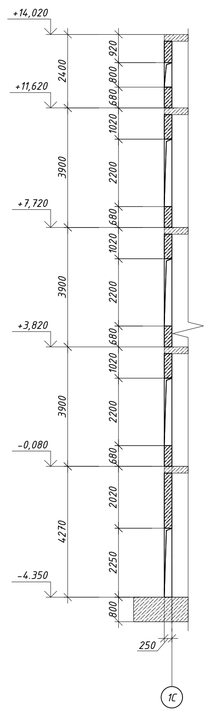


Разрез 11-11 (Опалубка)

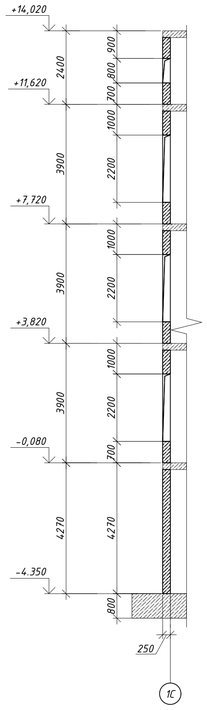

Разрез 12-12 (Опалубка)

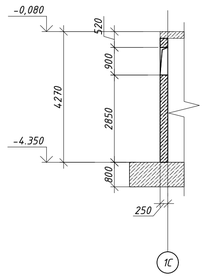

Разрез 14 - 14 (Опалубка)

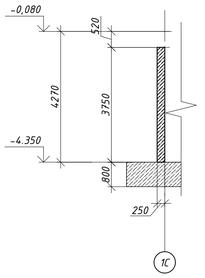


1. Общие указания см. л. - 1.
2. Данный лист читать совместно с л. КЖ-2.1...2.7 и 5.2 ... 5.6
3. Стыки рабочей арматуры внахлестку без сварки, на скрутках из вязальной проволоки не менее 3 шт. на стык. Длина нахлеста 71d. Стыки располагать враздежку, чтобы площадь рабочей арматуры, стыкуемой в одном сечении, не превышала 50%.
4. Расход арматуры в погонных метрах приведен с учетом нахлеста.
5. Стержни, указанные в "Ведомости деталей", должны гнуться механическим способом в холодном состоянии с радиусом гиба 3d - 5d, где d - диаметр стержня
6. Узел стыковки арматуры нахлеста, анкеровки и Фрагмент обрамления проема смотреть на листе 4


						65П-АИП-2024-1-КЖ	
						Строительство многопрофильной больницы на 250 коек с онкологическим центром и поликлиникой на 350 посещений, по адресу: Медеуский район, г. Алматы	
Изм.	Кол.уч	Лист	N док.	Подп.	Дата		
						"Блок 1 Секция 1"	Стадия: РП; Лист: 5.2; Листов:
ГКП		Курал М					
Проверил		Кыдырбай А				Опалубочный чертеж монолитной стены по оси 1с стена См-1 (тол.250мм)	АстанаИнжПроект
Разраб.		Ауез Б					
Н.контроль		Ешенкулова					

Формат А1


Основное вертикальное армирование монолитной стены по оси 1с стена См-1 (тол.250мм)

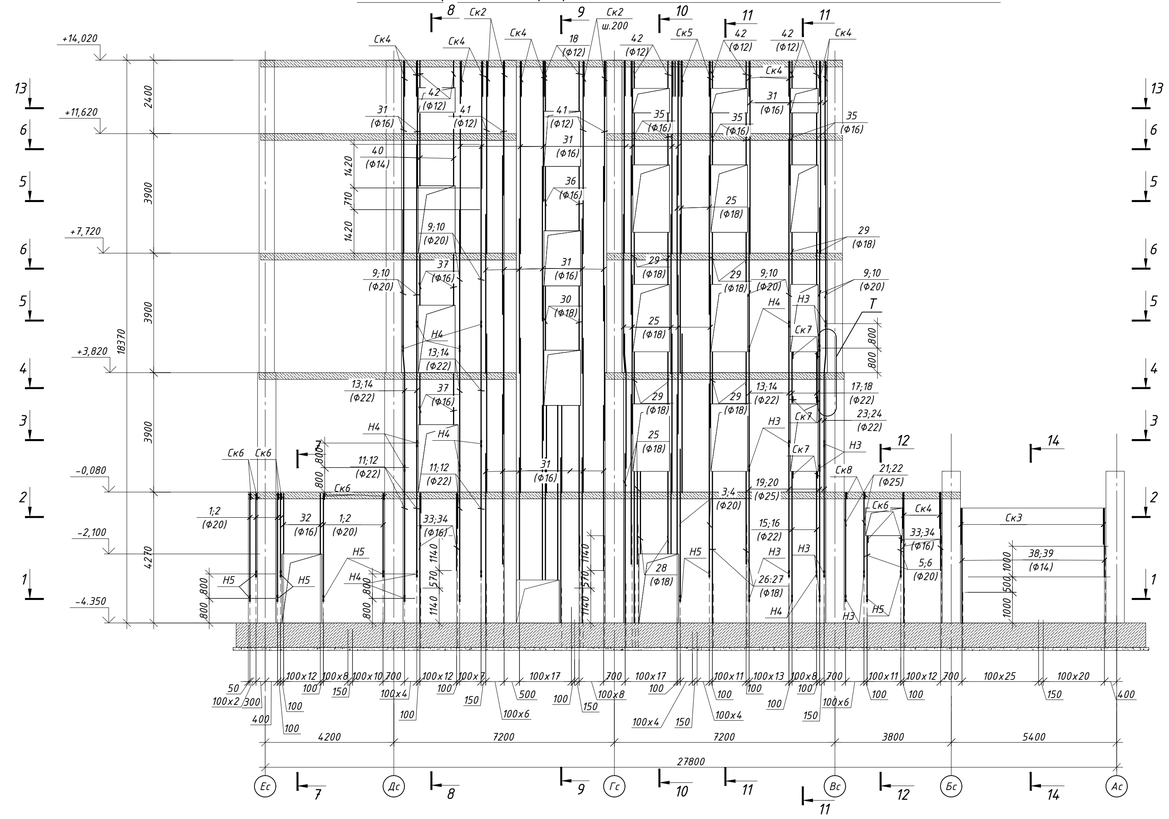


Дополнительное горизонтальное армирование монолитной стены по оси 1с стена См-1 (тол.250мм)

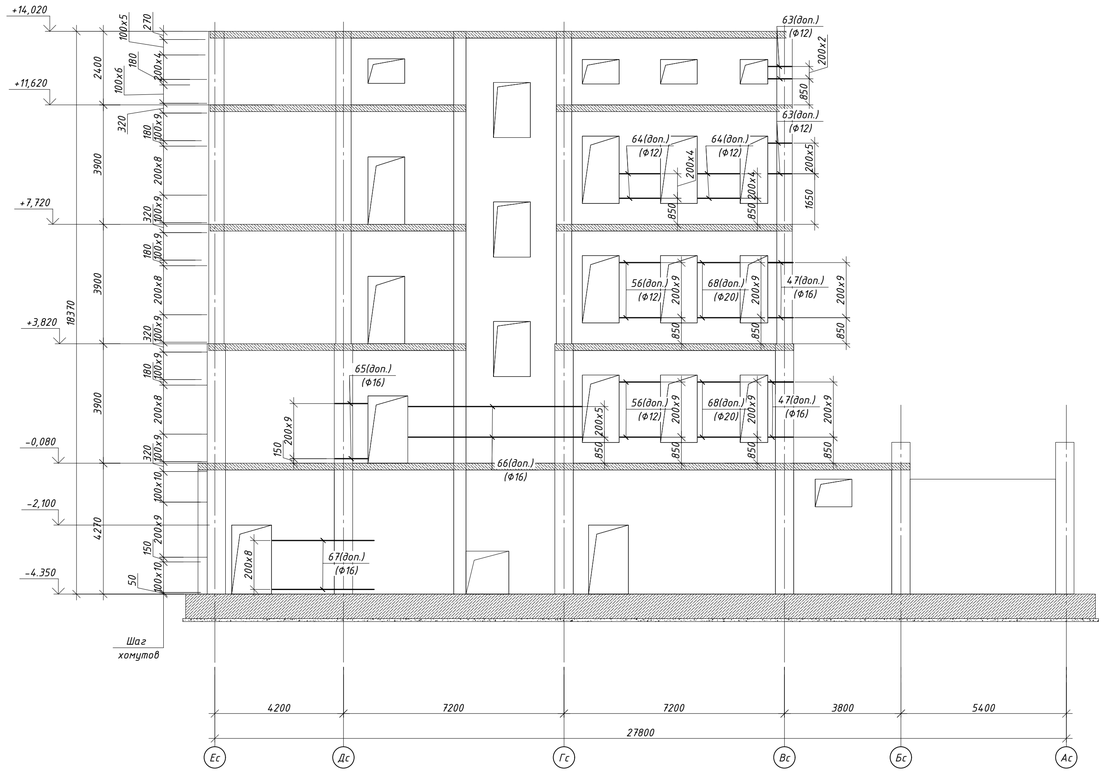


Основное горизонтальное армирование монолитной стены по оси 1с стена См-1 (тол.250мм)

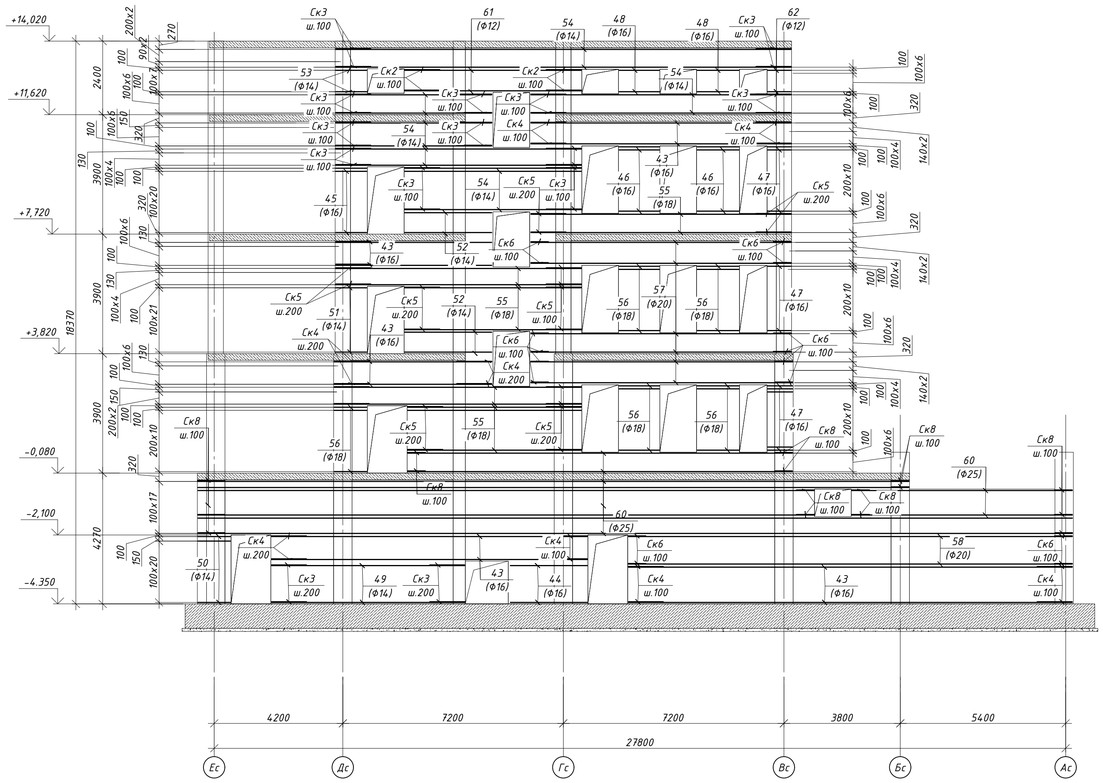


Разрез 7-7 (Армирование)

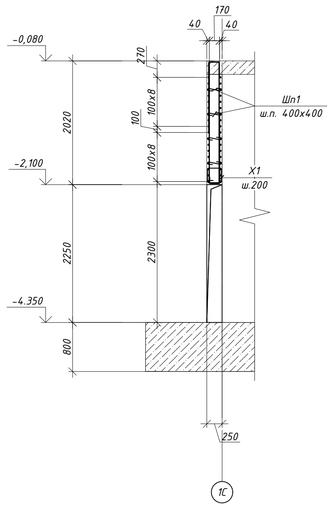

Разрез 12-12 (Армирование)

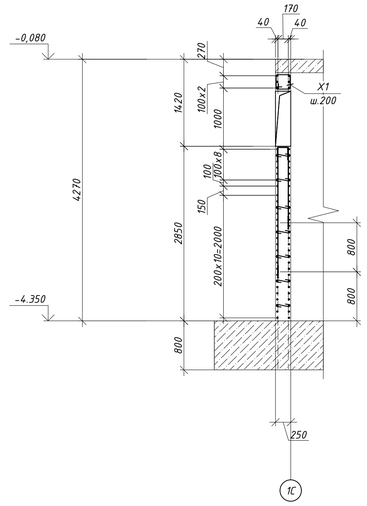


Разрез 14 - 14 (Армирование)

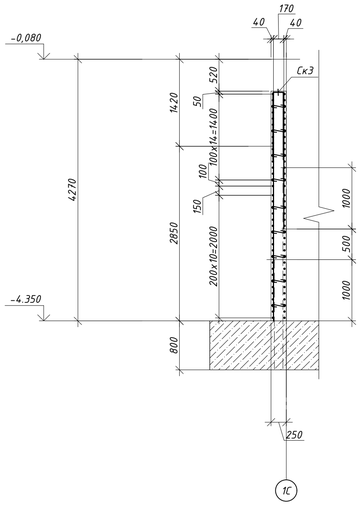


1. Общие указания см. л. - 1.
2. Данный лист читать совместно с л. КЖ-2.1...2.7 и 5.2 ... 5.6
3. Стыки рабочей арматуры внахлестку без сварки, на скрутках из вязальной проволоки не менее 3 шт. на стык. Длина нахлеста 71d. Стыки располагать вразбежку, чтобы площадь рабочей арматуры, стыкуемой в одном сечении, не предышала 50%.
4. Расход арматуры в погонных метрах приведен с учетом нахлеста.
5. Стержни, указанные в "Ведомости деталей", должны гнуться механическим способом в холодном состоянии с радиусом гиба 3d - 5d, где d - диаметр стержня
6. Узел стыковки арматуры нахлеста, анкеровки и Фрагмент обрамления проема смотреть на листе 4

						65П-АИП-2024-1-КЖ	
						Строительство многопрофильной больницы на 250 коек с онкологическим центром и поликлиникой на 350 посещений, по адресу: Медеуский район, г. Алматы	
Изм.	Кол.уч.	Лист	N док.	Подп.	Дата		
						"Блок 1 Секция 1"	Стадия: РП; Лист: 5.3; Листов:
ГКП		Курал М					
Проверил		Кыдырбай А				Основное армирование монолитной стены по оси 1с стена См-1 (тол.250мм)	АстанаИнжПроект
Разраб.		Ауез Б					
Н.контроль		Ешенкулова					Формат А1


Разрез 1-1 (Армирование) М 1:50

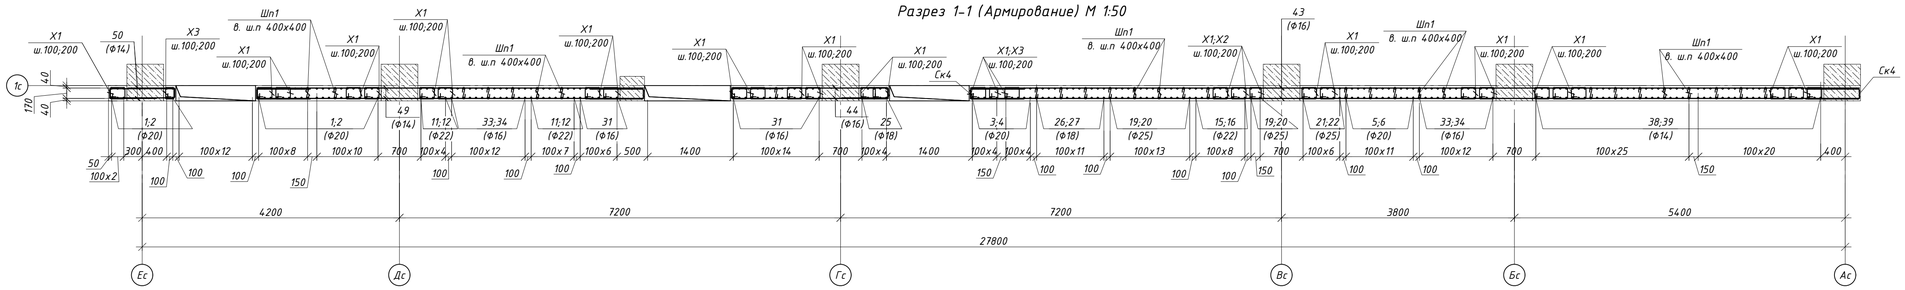


Разрез 2-2 (Армирование) М 1:50

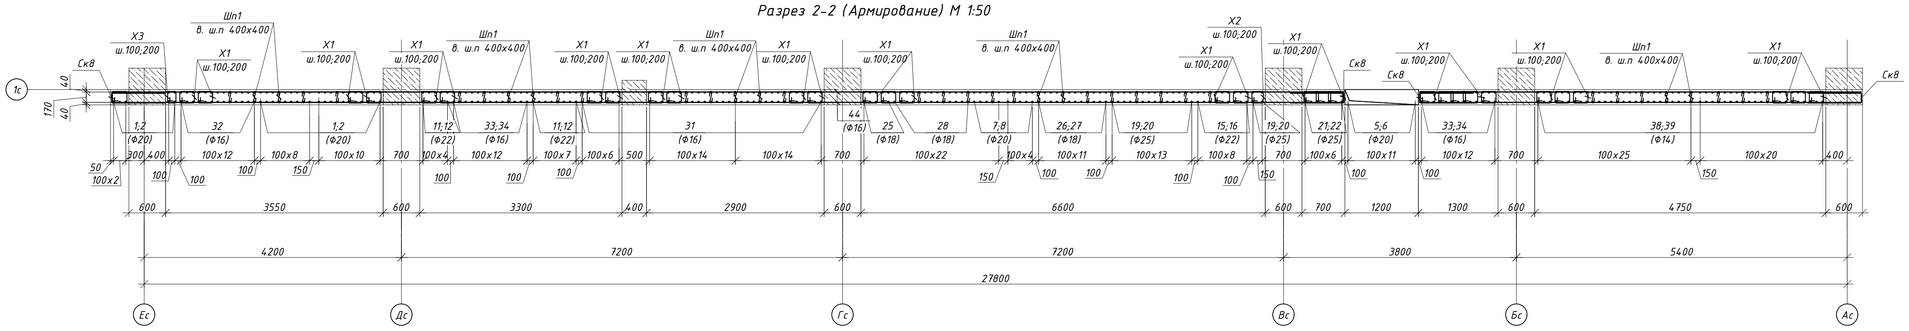


Разрез 3-3 (Армирование) М 1:50

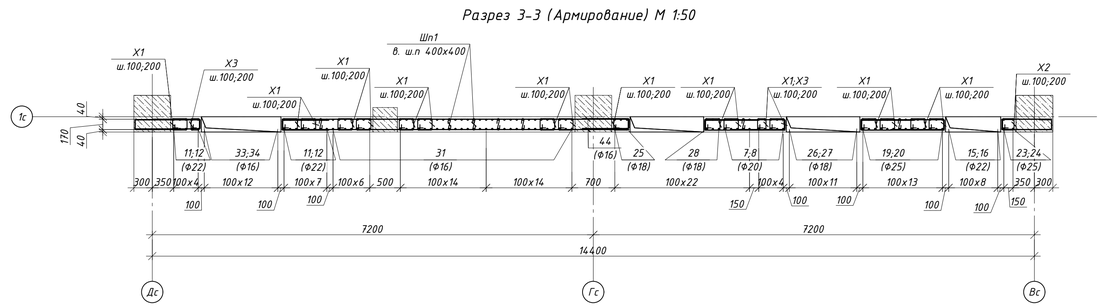


Разрез 4-4 (Армирование) М 1:50

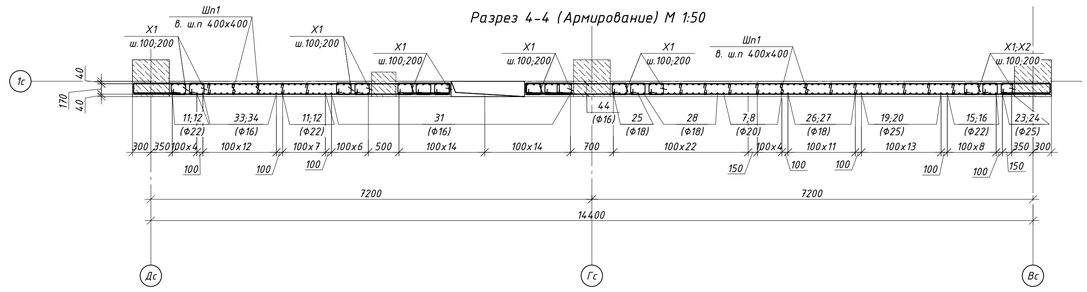


Разрез 5-5 (Армирование) М 1:50

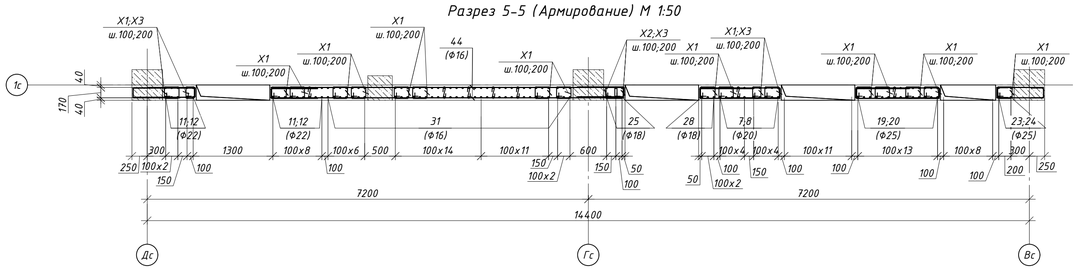

Разрез 6-6 (Армирование) М 1:50

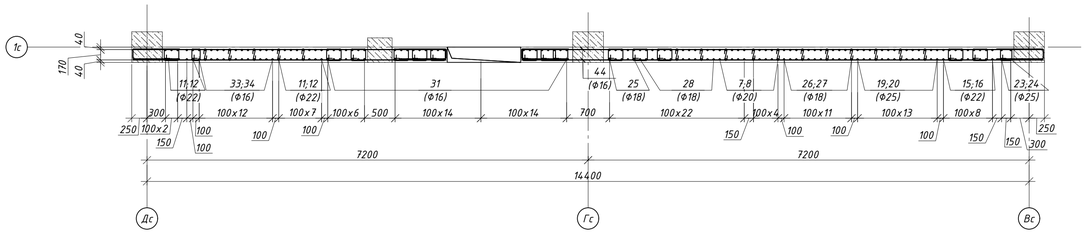

Разрез 13-13 (Армирование) М 1:50

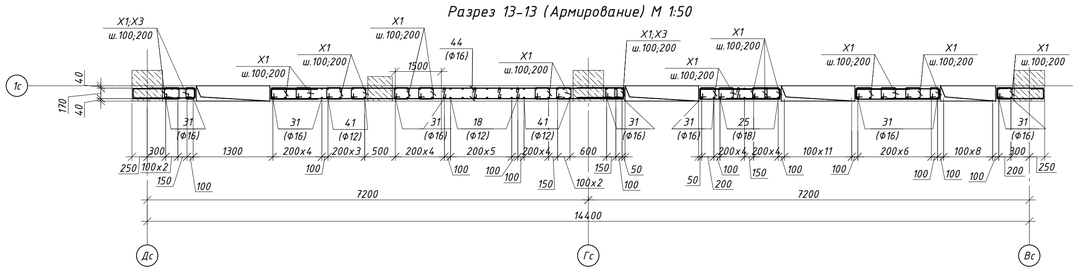


1. Общие указания см. л. – 1.
2. Данный лист читать совместно с л. КЖ-2.1...2.7 и 5.2 ... 5.6
3. Стыки рабочей арматуры внахлестку без сварки, на скрутках из вязальной проволоки не менее 3 шт. на стык. Длина нахлеста 71d. Стыки располагать вразбежку, чтобы площадь рабочей арматуры, стыкуемой в одном сечении, не превышала 50%.
4. Расход арматуры в погонных метрах приведен с учетом нахлеста.
5. Стержни, указанные в "Ведомости деталей", должны гнуться механическим способом в холодном состоянии с радиусом гиба 3d – 5d, где d – диаметр стержня
6. Узел стыковки арматуры нахлеста, анкеровки и Фрагмент обрамления проема смотреть на листе 4


						65П-АИП-2024-1-КЖ	
						Строительство многопрофильной больницы на 250 коек с онкологическим центром и поликлиникой на 350 посещений, по адресу: Медеуский район, г. Алматы	
Изм.	Кол.уч.	Лист	N док.	Подп.	Дата		
						"Блок 1 Секция 1"	Стадия: РП; Лист: 5.4; Листов:
ГКП		Курал М					
Проверил		Кыдырбай А				Разрезы 1-1;.....13-13.	АстанаИнжПроект
Разраб.		Ауез Б					
Н.контроль		Ешенкулова					

Формат А1


Разрез 8-8 (Армирование) М 1:50

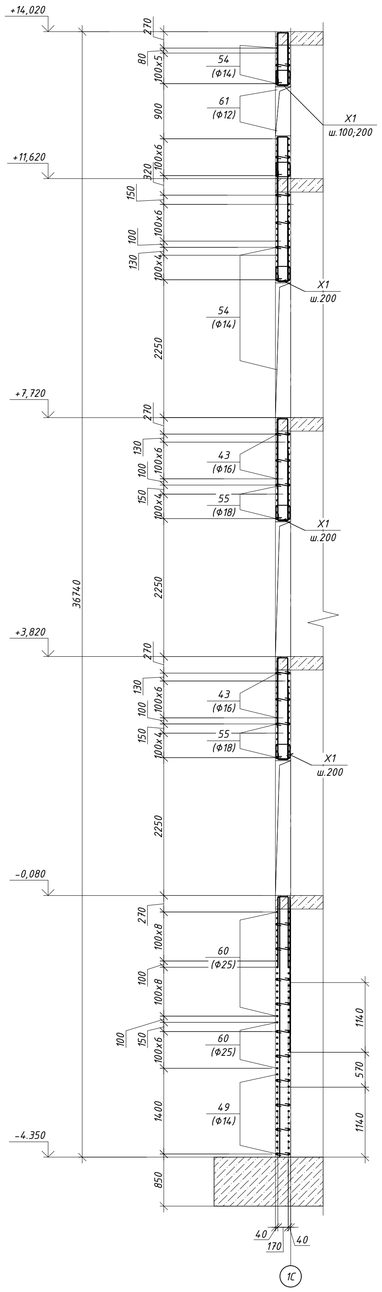


Разрез 9-9 (Армирование) М 1:50

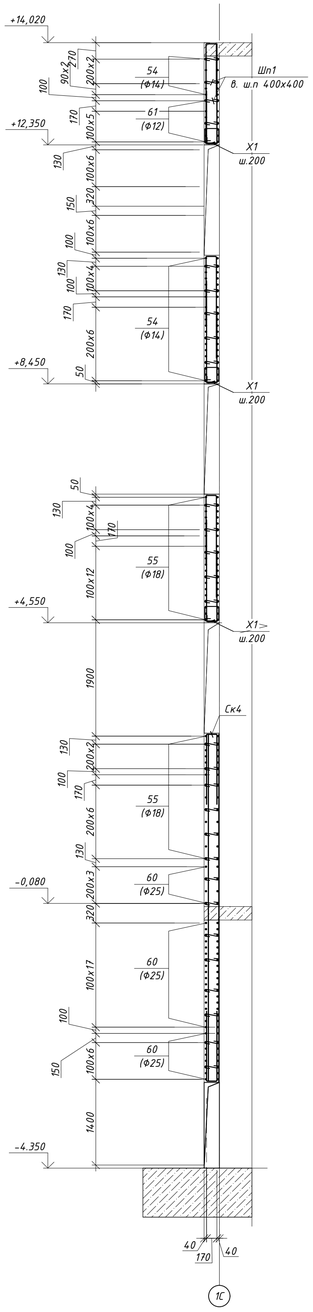


Разрез 10-10 (Армирование) М 1:50

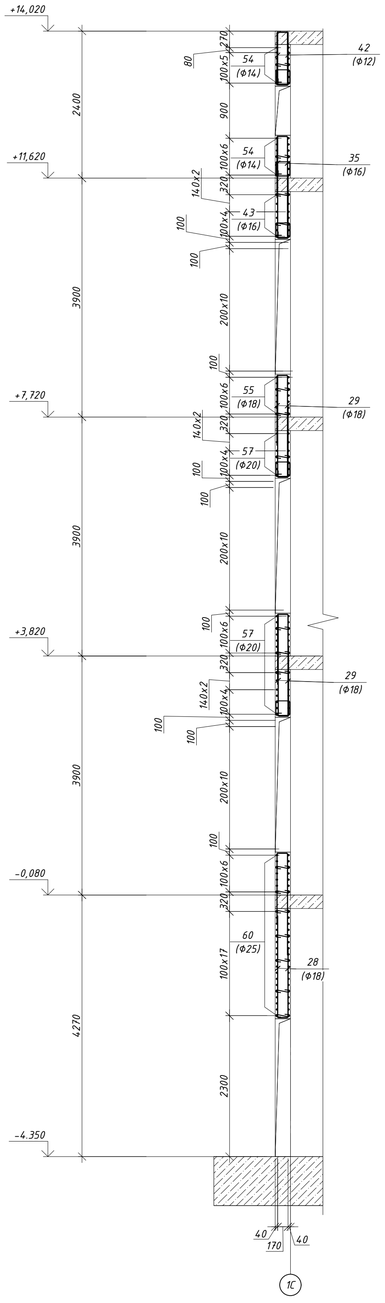

Разрез 11-11 (Армирование) М 1:50

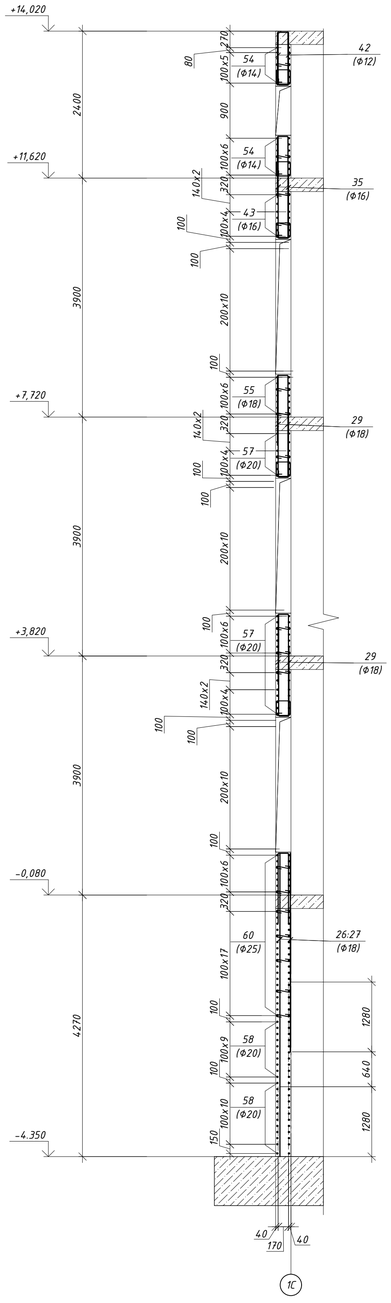

Узел Т

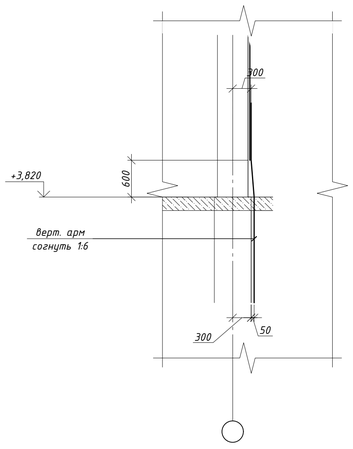

						65П-АИП-2024-1-КЖ	
						Строительство многопрофильной больницы на 250 коек с онкологическим центром и поликлиникой на 350 посещений, по адресу: Медеуский район, г. Алматы	
Изм.	Колуч	Лист	N док.	Подп.	Дата		
						"Блок 1 Секция 1"	Стадия: РП; Лист: 5.5; Листов:
ГКП		Курал М					
Проверил		Кыдырбай А					
Разраб.		Ауез Б				Разрезы 8-8;.....11-11	АстанаИнжПроект
Н.контроль		Ешенкулова					

Формат А1

Спецификация элементов

Поз.	Обозначение	Наименование	Кол.	Масса ед.кг	Примечание
		Стена Ст-1			24925.85
Х1*	ГОСТ 34028-2016(214-210-0101-0002)	Ф 8 А 240 L= 980	274.7	0.39	1062.24
Х2*	ГОСТ 34028-2016(214-210-0101-0002)	Ф 8 А 240 L= 880	115	0.35	39.93
Х3*	ГОСТ 34028-2016(214-210-0101-0002)	Ф 8 А 240 L= 780	334	0.31	102.80
Шп1*	ГОСТ 34028-2016(214-210-0101-0002)	Ф 8 А 240 L= 370	1989	0.15	290.39
Ск2*	ГОСТ 34028-2016(214-210-0502-0001)	Ф 12 А500С L= 1890	28	1.68	46.98
Ск3*	ГОСТ 34028-2016(214-210-0502-0002)	Ф 14 А500С L= 2170	155	2.62	406.45
Ск4*	ГОСТ 34028-2016(214-210-0502-0003)	Ф 16 А500С L= 2450	131	3.87	506.57
Ск5*	ГОСТ 34028-2016(214-210-0502-0004)	Ф 18 А500С L= 2730	92	5.45	501.71
Ск6*	ГОСТ 34028-2016(214-210-0502-0003)	Ф 16 А500С L= 570	191	0.90	171.83
Ск8*	ГОСТ 34028-2016(214-210-0502-0003)	Ф 16 А500С L= 670	55	1.06	58.16
Н3	ГОСТ 34028-2016(214-210-0502-0007)	Ф 25 А500С L= 250	136	0.96	131.01
Н4	ГОСТ 34028-2016(214-210-0502-0006)	Ф 22 А500С L= 220	180	0.66	118.17
Н5	ГОСТ 34028-2016(214-210-0502-0005)	Ф 20 А500С L= 200	188	0.49	92.73
1	ГОСТ 34028-2016(214-210-0502-0005)	Ф 20 А500С L= 3430	25	8.46	211.47
2	ГОСТ 34028-2016(214-210-0502-0005)	Ф 20 А500С L= 2630	25	6.49	162.15
3	ГОСТ 34028-2016(214-210-0502-0005)	Ф 20 А500С L= 4870	10	12.01	120.10
4	ГОСТ 34028-2016(214-210-0502-0005)	Ф 20 А500С L= 6200	10	15.29	152.90
5	ГОСТ 34028-2016(214-210-0502-0005)	Ф 20 А500С L= 2030	12	5.01	60.08
6	ГОСТ 34028-2016(214-210-0502-0005)	Ф 20 А500С L= 1230	12	3.03	36.40
9	ГОСТ 34028-2016(214-210-0502-0005)	Ф 20 А500С L= 4520	30	11.15	334.41
10	ГОСТ 34028-2016(214-210-0502-0005)	Ф 20 А500С L= 5850	30	14.43	432.81
11	ГОСТ 34028-2016(214-210-0502-0006)	Ф 22 А500С L= 4270	13	12.74	165.64
12	ГОСТ 34028-2016(214-210-0502-0006)	Ф 22 А500С L= 4270	13	12.74	165.64
13	ГОСТ 34028-2016(214-210-0502-0006)	Ф 22 А500С L= 3900	27	11.64	314.22
14	ГОСТ 34028-2016(214-210-0502-0006)	Ф 22 А500С L= 3920	27	11.70	315.83
15	ГОСТ 34028-2016(214-210-0502-0006)	Ф 22 А500С L= 4130	9	12.32	110.92
16	ГОСТ 34028-2016(214-210-0502-0006)	Ф 22 А500С L= 3330	9	9.94	89.43
17	ГОСТ 34028-2016(214-210-0502-0006)	Ф 22 А500С L= 1660	9	4.95	44.58
18	ГОСТ 34028-2016(214-210-0502-0001)	Ф 12 А500С L= 2660	24	2.36	56.68
19	ГОСТ 34028-2016(214-210-0502-0007)	Ф 25 А500С L= 4250	14	16.38	229.27
20	ГОСТ 34028-2016(214-210-0502-0007)	Ф 25 А500С L= 4250	14	16.38	229.27
21	ГОСТ 34028-2016(214-210-0502-0007)	Ф 25 А500С L= 3450	14	13.29	186.12
22	ГОСТ 34028-2016(214-210-0502-0007)	Ф 25 А500С L= 2650	7	10.21	71.48
23	ГОСТ 34028-2016(214-210-0502-0007)	Ф 25 А500С L= 3920	2	15.11	30.21
24	ГОСТ 34028-2016(214-210-0502-0007)	Ф 25 А500С L= 3925	2	15.12	30.25
25	ГОСТ 34028-2016(214-210-0502-0004)	Ф 18 А500С L= пог.м.	583.64	2.00	1165.87
26	ГОСТ 34028-2016(214-210-0502-0004)	Ф 18 А500С L= 4930	12	9.85	118.18
27	ГОСТ 34028-2016(214-210-0502-0004)	Ф 18 А500С L= 3010	12	6.01	72.15
28	ГОСТ 34028-2016(214-210-0502-0004)	Ф 18 А500С L= 4130	20	8.25	165.00
29	ГОСТ 34028-2016(214-210-0502-0004)	Ф 18 А500С L= 3110	48	6.21	298.20

Позиции со "*" см. "Ведомость деталей" см. на данном листе.

Спецификация элементов


Поз.	Обозначение	Наименование	Кол.	Масса ед.кг	Примечание
30	ГОСТ 34028-2016(214-210-0502-0004)	Ф 18 А500С L= 3510	24	7.01	168.28
31	ГОСТ 34028-2016(214-210-0502-0003)	Ф 16 А500С L= пог.м.	1382.44	1.58	2181.95
32	ГОСТ 34028-2016(214-210-0502-0003)	Ф 16 А500С L= 3290	26	5.19	135.01
33	ГОСТ 34028-2016(214-210-0502-0003)	Ф 16 А500С L= 4250	13	6.71	87.20
34	ГОСТ 34028-2016(214-210-0502-0003)	Ф 16 А500С L= 2540	13	4.01	52.12
35	ГОСТ 34028-2016(214-210-0502-0003)	Ф 16 А500С L= 2970	66	4.69	309.39
36	ГОСТ 34028-2016(214-210-0502-0003)	Ф 16 А500С L= 2970	24	4.69	112.50
37	ГОСТ 34028-2016(214-210-0502-0003)	Ф 16 А500С L= 2660	48	4.20	201.52
38	ГОСТ 34028-2016(214-210-0502-0002)	Ф 14 А500С L= 3730	47	4.51	211.85
39	ГОСТ 34028-2016(214-210-0502-0002)	Ф 14 А500С L= 2230	47	2.69	126.65
40	ГОСТ 34028-2016(214-210-0502-0002)	Ф 14 А500С L= 3530	24	4.27	102.38
41	ГОСТ 34028-2016(214-210-0502-0001)	Ф 12 А500С L= пог.м.	170.24	0.89	151.14
42	ГОСТ 34028-2016(214-210-0502-0001)	Ф 12 А500С L= 1890	90	1.68	151.02
43	ГОСТ 34028-2016(214-210-0502-0003)	Ф 16 А500С L= пог.м.	713.72	1.58	1126.49
44	ГОСТ 34028-2016(214-210-0502-0003)	Ф 16 А500С L= 3870	26	6.11	158.81
45	ГОСТ 34028-2016(214-210-0502-0003)	Ф 16 А500С L= 2190	64	3.46	221.22
46	ГОСТ 34028-2016(214-210-0502-0003)	Ф 16 А500С L= 2620	48	4.14	198.49
47	ГОСТ 34028-2016(214-210-0502-0003)	Ф 16 А500С L= 1690	24	2.67	64.02
48	ГОСТ 34028-2016(214-210-0502-0003)	Ф 16 А500С L= 2290	32	3.61	115.66
49	ГОСТ 34028-2016(214-210-0502-0002)	Ф 14 А500С L= 6310	26	7.63	198.25
50	ГОСТ 34028-2016(214-210-0502-0002)	Ф 14 А500С L= 2330	44	2.82	123.89
51	ГОСТ 34028-2016(214-210-0502-0002)	Ф 14 А500С L= 2190	44	2.65	116.44
52	ГОСТ 34028-2016(214-210-0502-0002)	Ф 14 А500С L= 2840	28	3.43	96.09
53	ГОСТ 34028-2016(214-210-0502-0002)	Ф 14 А500С L= 5760	30	6.96	208.81
54	ГОСТ 34028-2016(214-210-0502-0002)	Ф 14 А500С L= пог.м.	445.16	1.21	537.94
55	ГОСТ 34028-2016(214-210-0502-0004)	Ф 18 А500С L= пог.м.	565.76	2.00	1130.15
56	ГОСТ 34028-2016(214-210-0502-0004)	Ф 18 А500С L= 2540	136	5.07	690.04
57	ГОСТ 34028-2016(214-210-0502-0005)	Ф 20 А500С L= 8540	42	21.06	884.56
58	ГОСТ 34028-2016(214-210-0502-0005)	Ф 20 А500С L= пог.м.	304.50	2.47	750.94
59	ГОСТ 34028-2016(214-210-0502-0005)	Ф 20 А500С L= 1360	40	3.35	134.16
60	ГОСТ 34028-2016(214-210-0502-0007)	Ф 25 А500С L= пог.м.	1265.71	3.85	4877.24
61	ГОСТ 34028-2016(214-210-0502-0001)	Ф 12 А500С L= 5760	16	5.11	81.82
62	ГОСТ 34028-2016(214-210-0502-0001)	Ф 12 А500С L= 2620	34	2.33	79.09
64	ГОСТ 34028-2016(214-210-0502-0001)	Ф 12 А500С L= 2290	20	2.03	40.66
66	ГОСТ 34028-2016(214-210-0502-0003)	Ф 16 А500С L= 5660	12	8.93	107.20
67	ГОСТ 34028-2016(214-210-0502-0003)	Ф 16 А500С L= 3330	18	5.26	94.61
		Материалы:			
	(212-101-0901)	Класс бетона С 20/25 (B25) W4 F100, м³			22.71
	(212-101-0901)	Класс бетона С 20/25 (B25), м³			33.26

Позиции со "*" см. "Ведомость деталей" см. на данном листе.


Ведомость деталей

Поз.	Эскиз	Поз.	Эскиз	Поз.	Эскиз	Поз.	Эскиз	Поз.	Эскиз	Поз.	Эскиз
Х1	320, 170, 270, 220; по в.г. L=980	Ск3	1000, 170, 1000; по н.г. L=2170	28	1280, 170, 2680; по н.г. L=4130	36	1140, 170, 2060; по н.г. L=3370	45	1010, 170, 1010; по н.г. L=2190	51	1010, 170, 1010; по н.г. L=2190
Х2	270, 170, 270, 170; по в.г. L=880	Ск4	1140, 170, 1140; по н.г. L=2450	29	1280, 170, 1660; по н.г. L=3110	37	860, 170, 1630; по н.г. L=2660	46	1140, 170, 1310; по н.г. L=2620	56	1060, 170, 1310; по н.г. L=2540
Х3	220, 170, 270, 120; по в.г. L=780	Ск5	1280, 170, 1280; по н.г. L=2730	30	1280, 170, 2060; по н.г. L=3510	40	1000, 170, 2360; по н.г. L=3530	47	760, 170, 760; по н.г. L=1690	62	760, 170, 760; по н.г. L=1690
Шп1	170, 100, 100; по в.г. L=370	Ск6	200, 170, 200; по н.г. L=570	32	1140, 170, 1980; по н.г. L=3290	42	860, 170, 860; по н.г. L=1890	48	1060, 170, 1060; по н.г. L=2290	18	860, 170, 1630; по н.г. L=2660
Ск2	860, 170, 860; по н.г. L=1890	Ск8	250, 170, 250; по н.г. L=670	35	1140, 170, 1660; по н.г. L=2970	44	1140, 170, 2560; по н.г. L=3870	50	1000, 170, 1060; по н.г. L=2230	64	760, 170, 1360; по н.г. L=2290


Анкеровка

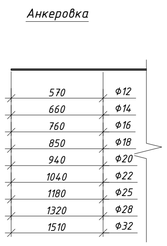


Узел стыковки вертикальной арматуры в нахлест и накладка

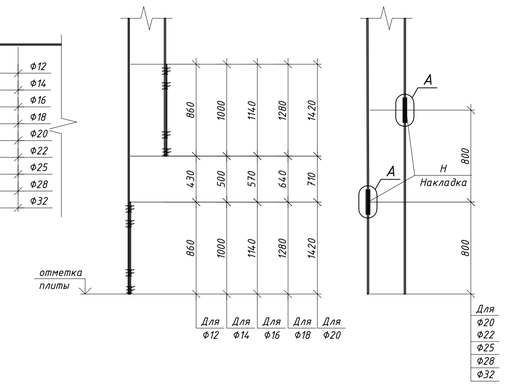

Фрагмент обрамления проема

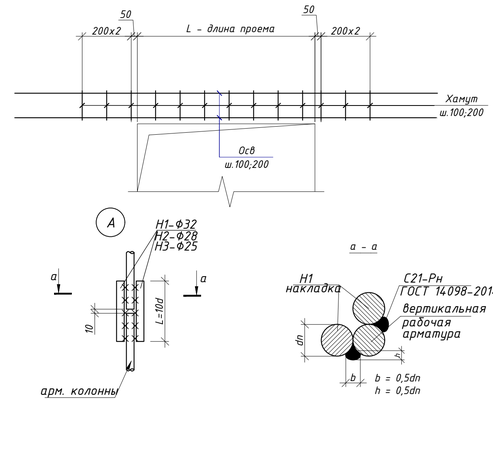

Узел стыковки горизонтальной арматуры в нахлест

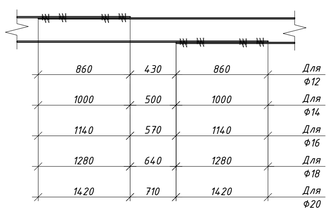

Б

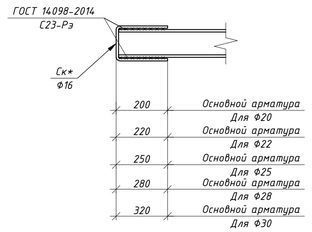


Таблица размеров Накладка

Марка эл-та	dн	L	вес
	мм.		кг.
Н1	32	320	2.01
Н2	28	280	1.35
Н3	25	250	0.96
Н4	22	220	0.66
Н5	20	200	0.49


1. Общие указания см. л. - 1.
2. Данный лист читать совместно с л. КЖ-2.1...2.7 и 5.2 ... 5.6
3. Стыки рабочей арматуры внахлестку без сварки, на скрутках из вязальной проволоки не менее 3 шт. на стык. Длина нахлеста 71d. Стыки располагать враздежку, чтобы площадь рабочей арматуры, стыкуемой в одном сечении, не превышала 50%.
4. Расход арматуры в погонных метрах приведен с учетом нахлеста.
5. Стержни, указанные в "Ведомости деталей", должны гнуться механическим способом в холодном состоянии с радиусом гиба 3d - 5d, где d - диаметр стержня
6. Узел стыковки арматуры нахлеста, анкеровки и Фрагмент обрамления проема смотреть на листе 4

Ведомость расхода стали, кг


Марка элемента	Изделия арматурные											Всего
	Арматура класса											
	А240		А500С									
	ГОСТ 34028-2016(214-210-0101)		ГОСТ 34028-2016(214-210-0502)									
	Ф8	Итого	Ф10	Ф12	Ф14	Ф16	Ф18	Ф20	Ф22	Ф25	Ф28	Итого	
Стена Ст-1	1495.36	1495.36	0.00	607.39	2128.75	5902.76	4309.58	3372.71	1324.44	5784.86	0.00	23430.49	24925.85

Изм.	Кол.уч	Лист	N док.	Подп.	Дата	65П-АИП-2024-1-КЖ			
						Строительство многопрофильной больницы на 250 коек с онкологическим центром и поликлиникой на 350 посещений, по адресу: Медеуский район, г. Алматы			
ГКП	Курал М					"Блок 1 Секция 1"	Стадия	Лист	Листов
Проверил	Кыдырбай А						РП	5.6	
Разраб.	Ауез Б					Спецификация стены Ст-1	АстанаИнжПроект		
Н.контроль	Ешенкулова						Формат А1		


Опалубочный чертеж монолитной стены по оси 4с стена См-2 (тол.250мм)

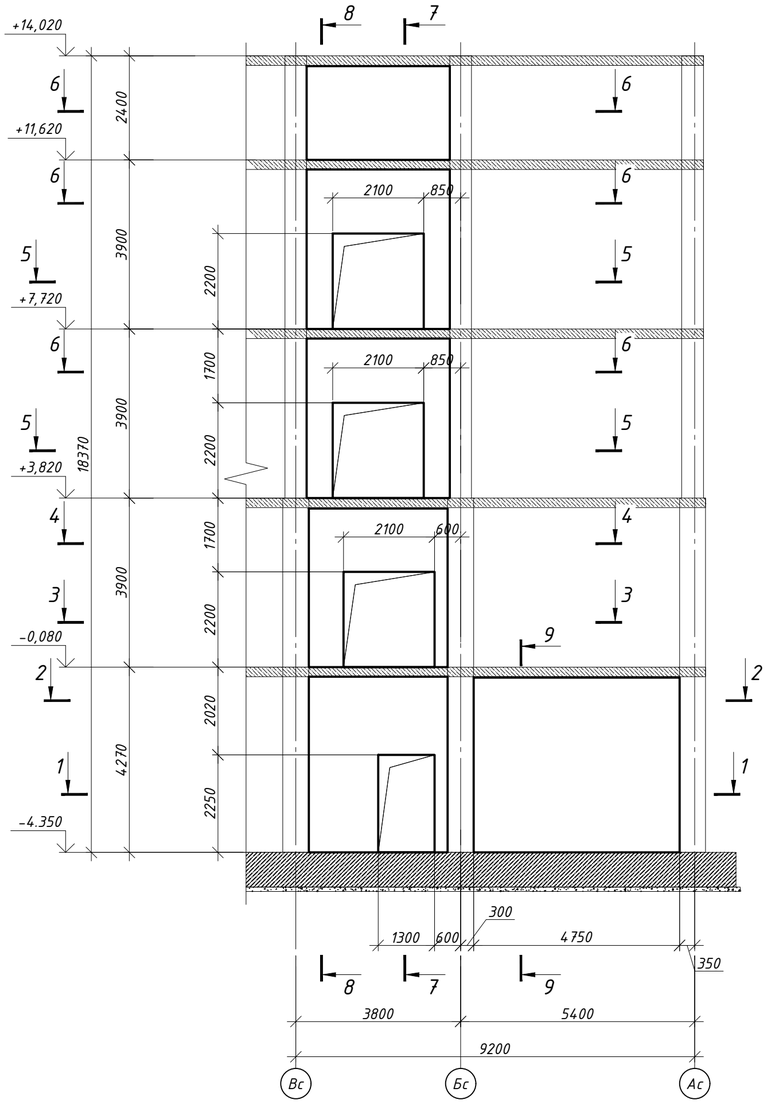


Разрез 7-7(Опалубка)

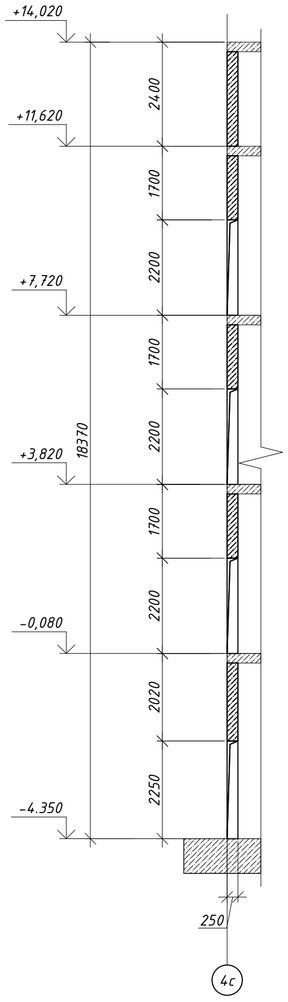

Разрез 8-8 (Опалубка)

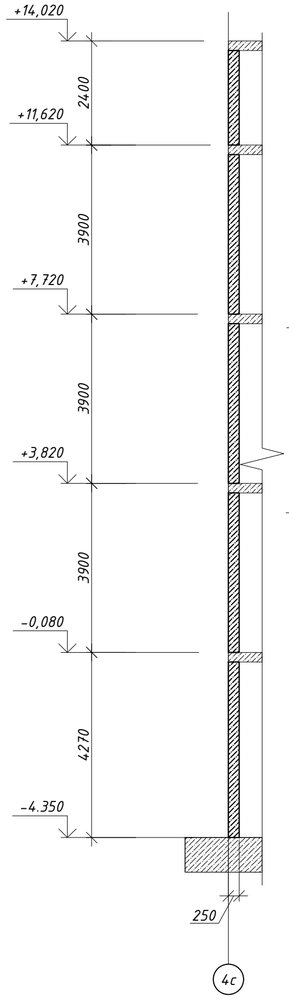


Разрез 9-9 (Опалубка)

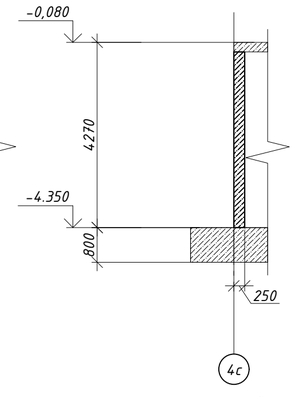


Анкеровка

Узел Т

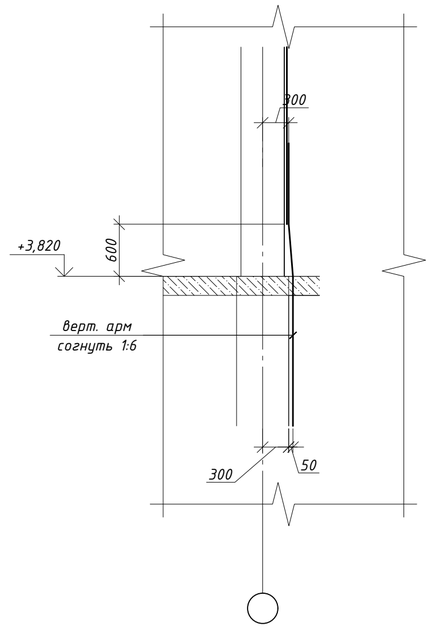


Узел стыковки вертикальной арматуры в нахлест


570	Ф12
660	Ф14
760	Ф16
850	Ф18
940	Ф20
1040	Ф22
1180	Ф25
1320	Ф28
1510	Ф32

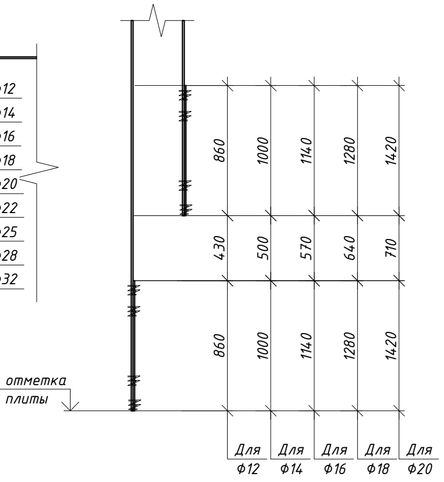


Разрез 1-1 (Опалубка) М 1:100

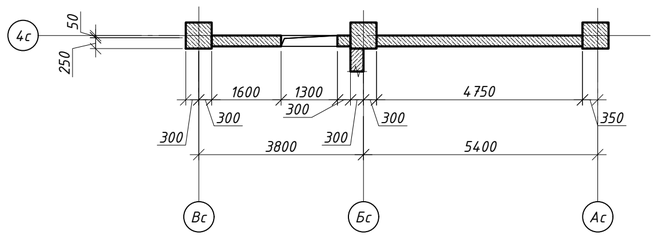


Разрез 2-2 (Опалубка) М 1:100

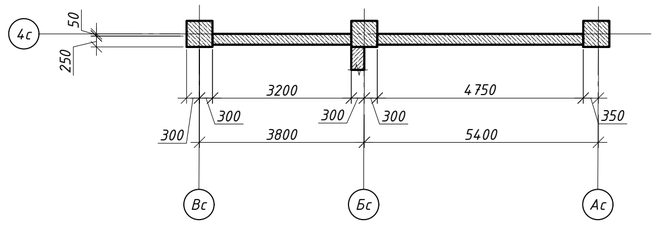


Разрез 3-3 (Опалубка) М 1:100

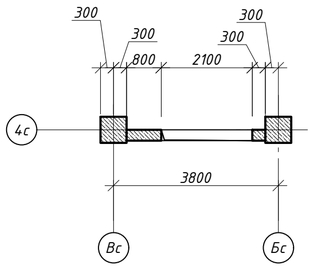


Разрез 4-4 (Опалубка) М 1:100

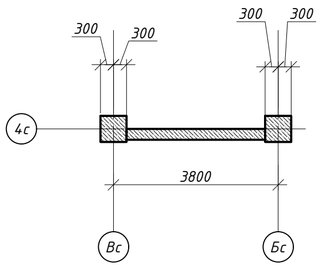

Разрез 5-5 (Опалубка) М 1:100

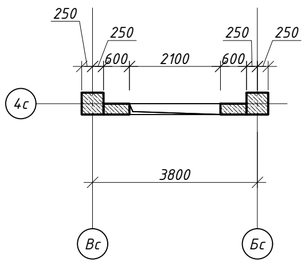


Разрез 6-6 (Опалубка) М 1:100

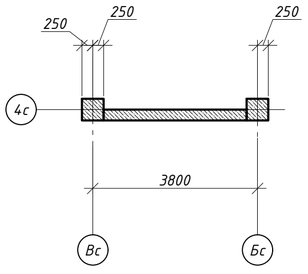


1. Общие указания см. л. - 1.
2. Данный лист читать совместно с л. КЖ-2.1....2.7 и 5.7 ... 5.10
3. Стыки рабочей арматуры внахлестку без сварки, на скрутках из вязальной проволоки не менее 3 шт. на стык. Длина нахлеста 71d. Стыки располагать вразбежку, чтобы площадь рабочей арматуры, стыкуемой в одном сечении, не превышала 50%.
4. Расход арматуры в погонных метрах приведен с учетом нахлеста.
5. Стержни, указанные в "Ведомости деталей", должны гнуться механическим способом в холодном состоянии с радиусом гиба 3d - 5d, где d - диаметр стержня
6. Узел стыковки арматуры нахлеста, анкеровки и Фрагмент обрамления проема смотреть на листе 4

						65П-АИП-2024-1-КЖ
						Строительство многопрофильной больницы на 250 коек с онкологическим центром и поликлиникой на 350 посещений, по адресу: Медеуский район, г. Алматы
Изм.	Кол.уч.	Лист	N док.	Подп.	Дата	
						"Блок 1 Секция 1" — Стадия: РП; Лист: 5.7; Листов:
ГКП		Курал М				Опалубочный чертеж монолитной стены по оси 4с стена См-2 (тол.250мм)
Проверил		Кыдырбай А				АстанаИнжПроект
Разраб.		Ауез Б				
Н.контроль		Ешенкулова				Формат А2


Основное вертикальное армирование монолитной стены по оси 4с стена См-2 (тол.250мм)

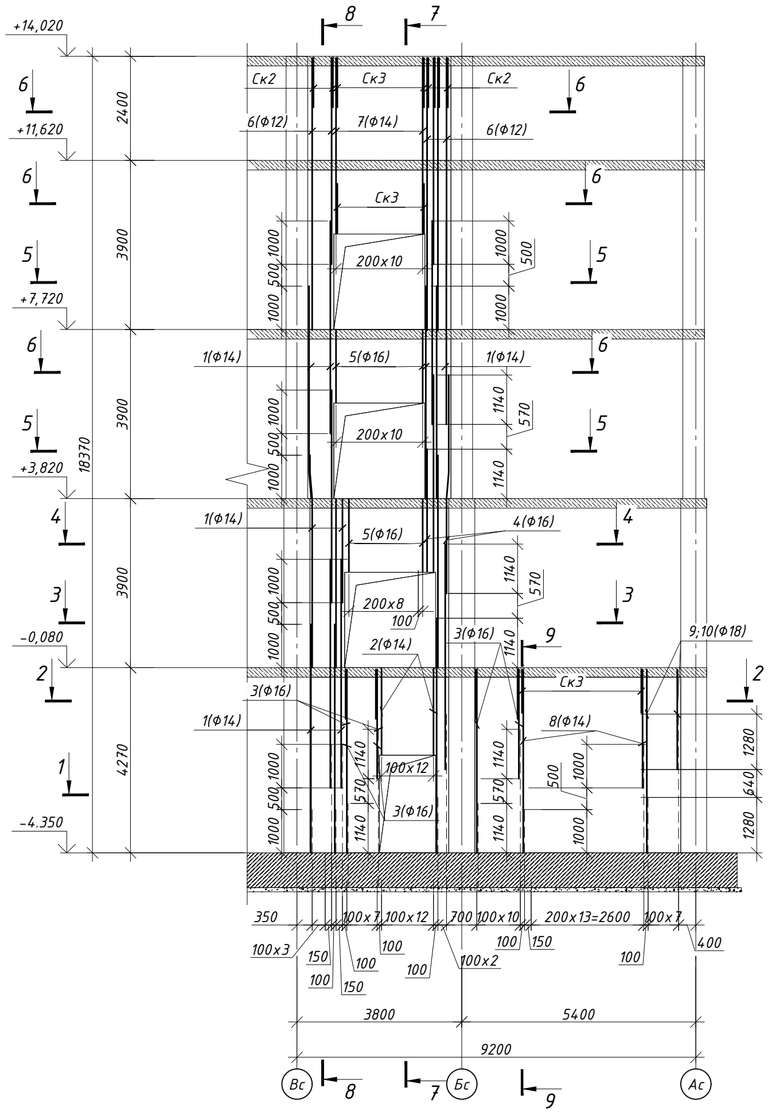


Основное горизонтальное армирование монолитной стены по оси 4с стена См-2 (тол.250мм)

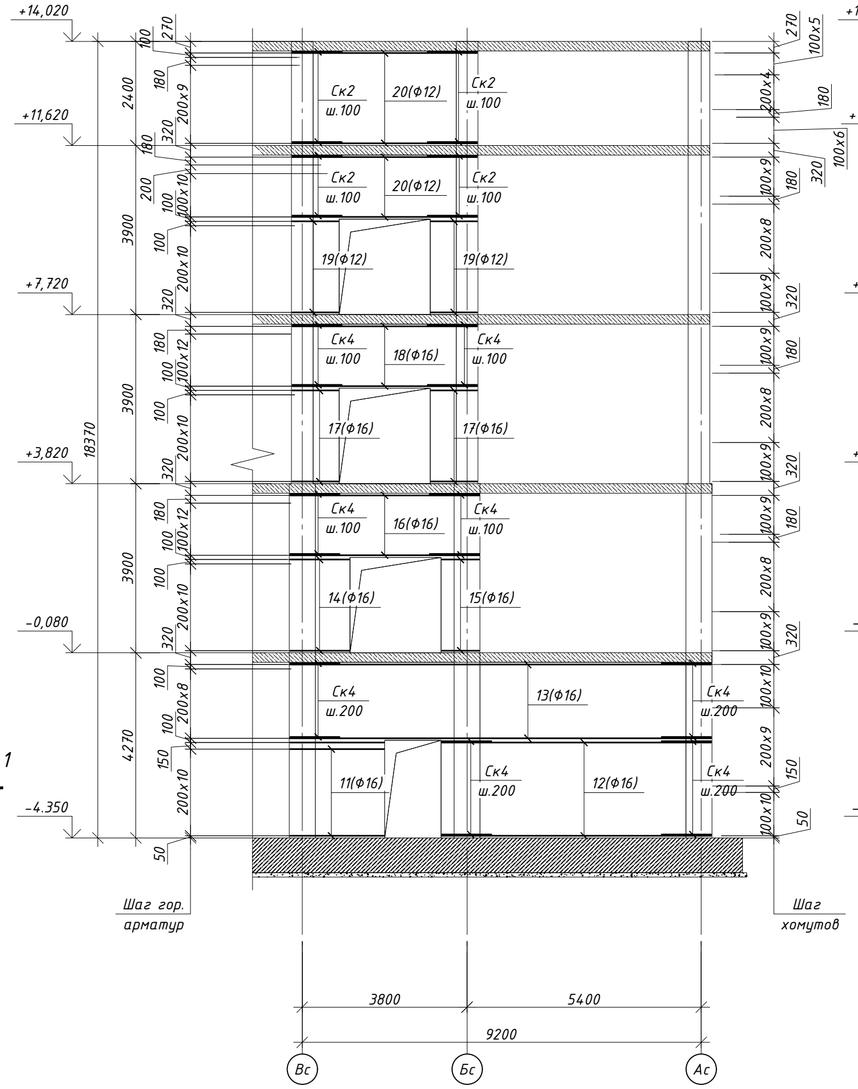


Дополнительное горизонтальное армирование монолитной стены по оси 1с стена См-2 (тол.250мм)

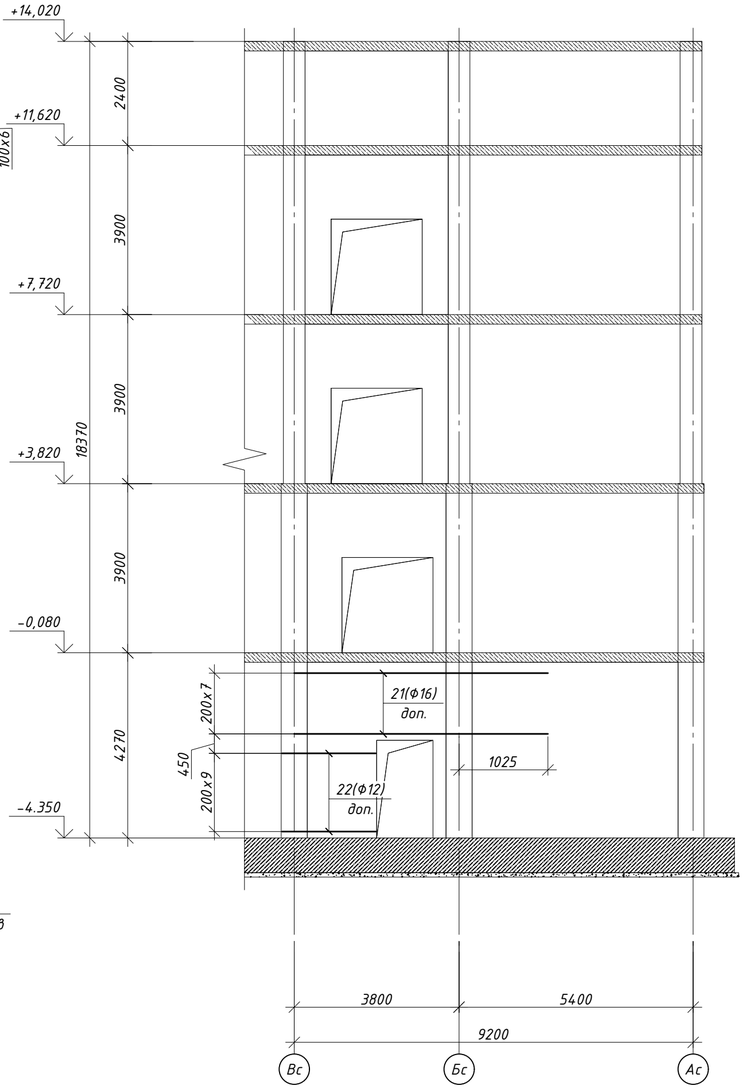


Разрез 1-1 (Армирование) М 1:50

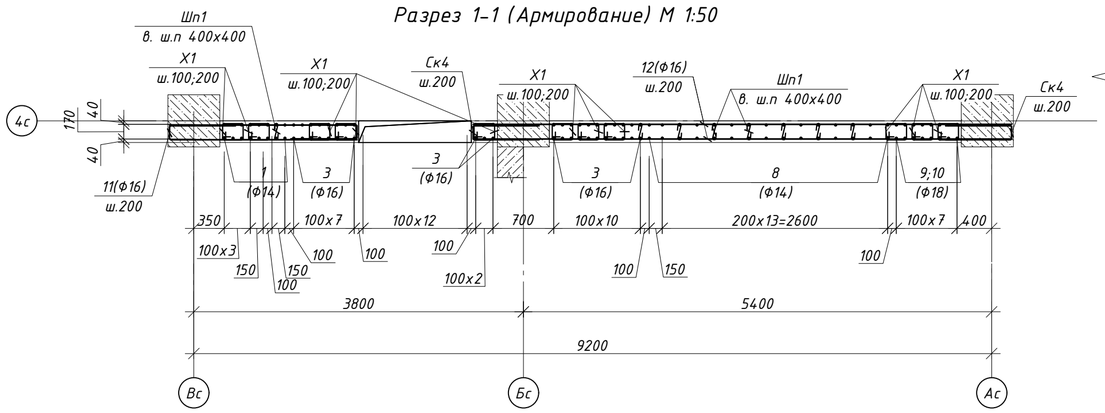

Узел стыковки Горизонтальной арматуры в нахлест

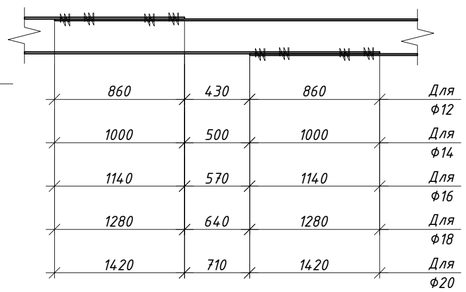


Фрагмент обрамления проема

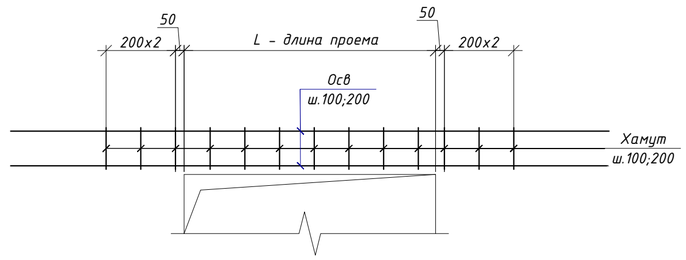


						65П-АИП-2024-1-КЖ
						Строительство многопрофильной больницы на 250 коек с онкологическим центром и поликлиникой на 350 посещений, по адресу: Медеуский район, г. Алматы
Изм.	Кол.уч.	Лист	N док.	Подп.	Дата	
						"Блок 1 Секция 1" — Стадия: РП; Лист: 5.8; Листов:
ГКП		Курал М				
Проверил		Кыдырбай А				Основное армирование монолитной стены по оси 4с стена См-2 (тол.250мм)
Разраб.		Ауез Б				
Н.контроль		Ешенкулова				АстанаИнжПроект

Формат А2


Разрез 2-2 (Армирование) М 1:50

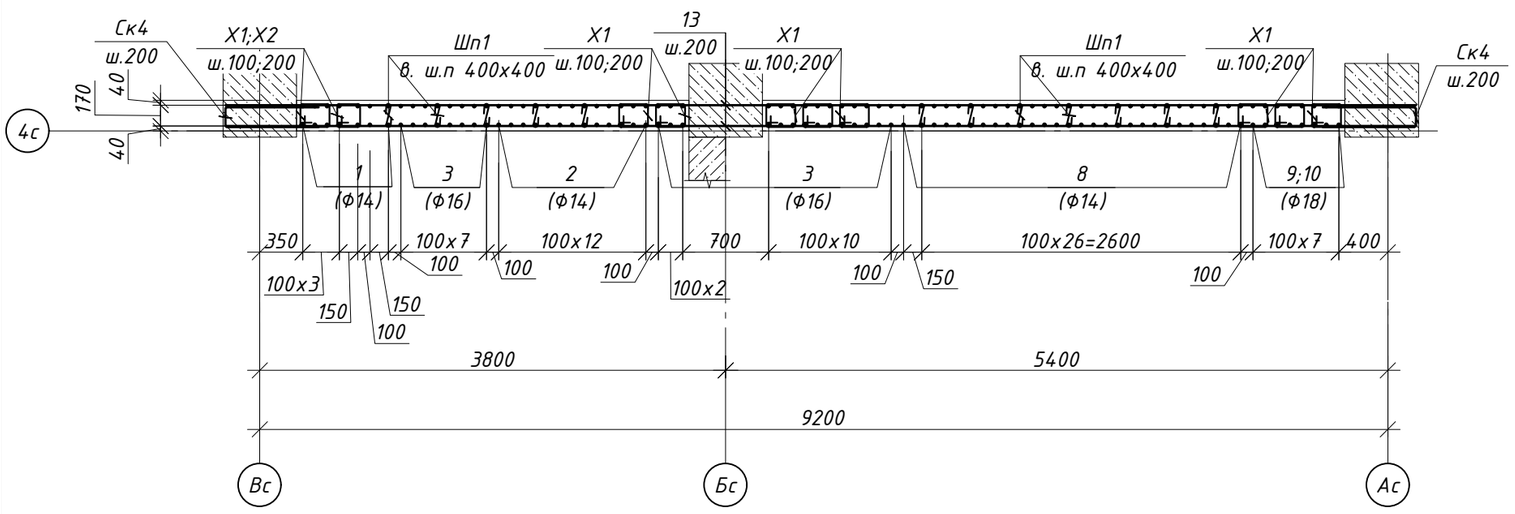


Разрез 3-3 (Армирование) М 1:50

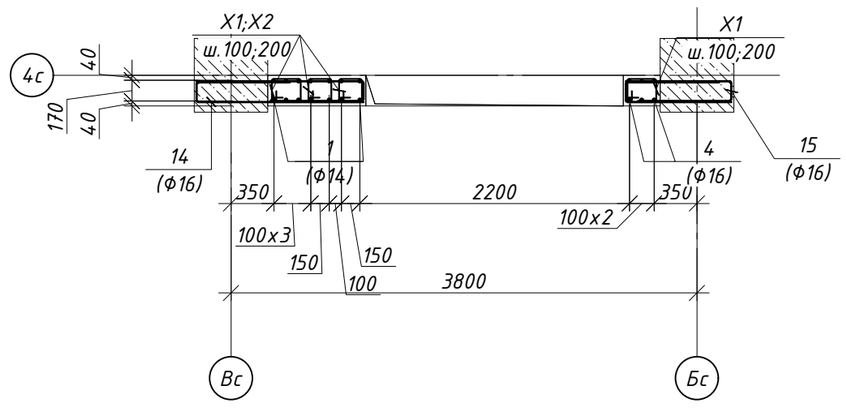

Разрез 4-4 (Армирование) М 1:50

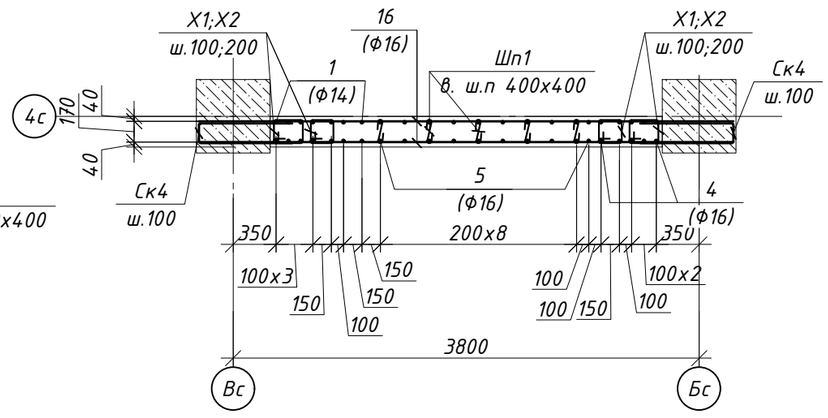


Разрез 5-5 (Армирование) М 1:50

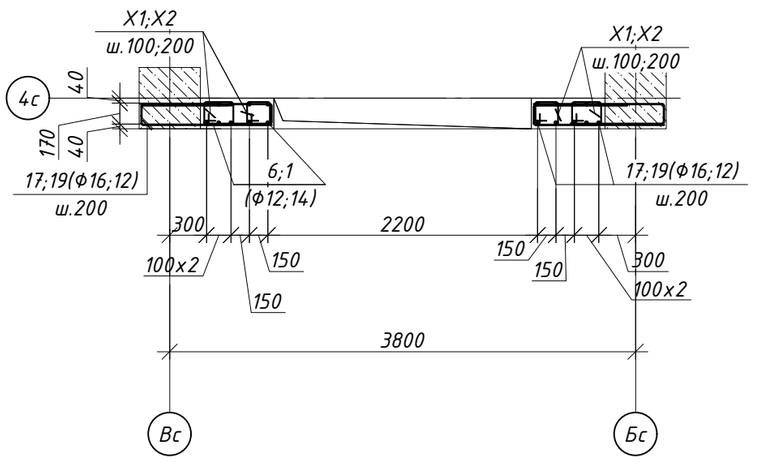


Разрез 6-6 (Армирование) М 1:50


Разрез 7-7 (Армирование) М 1:50

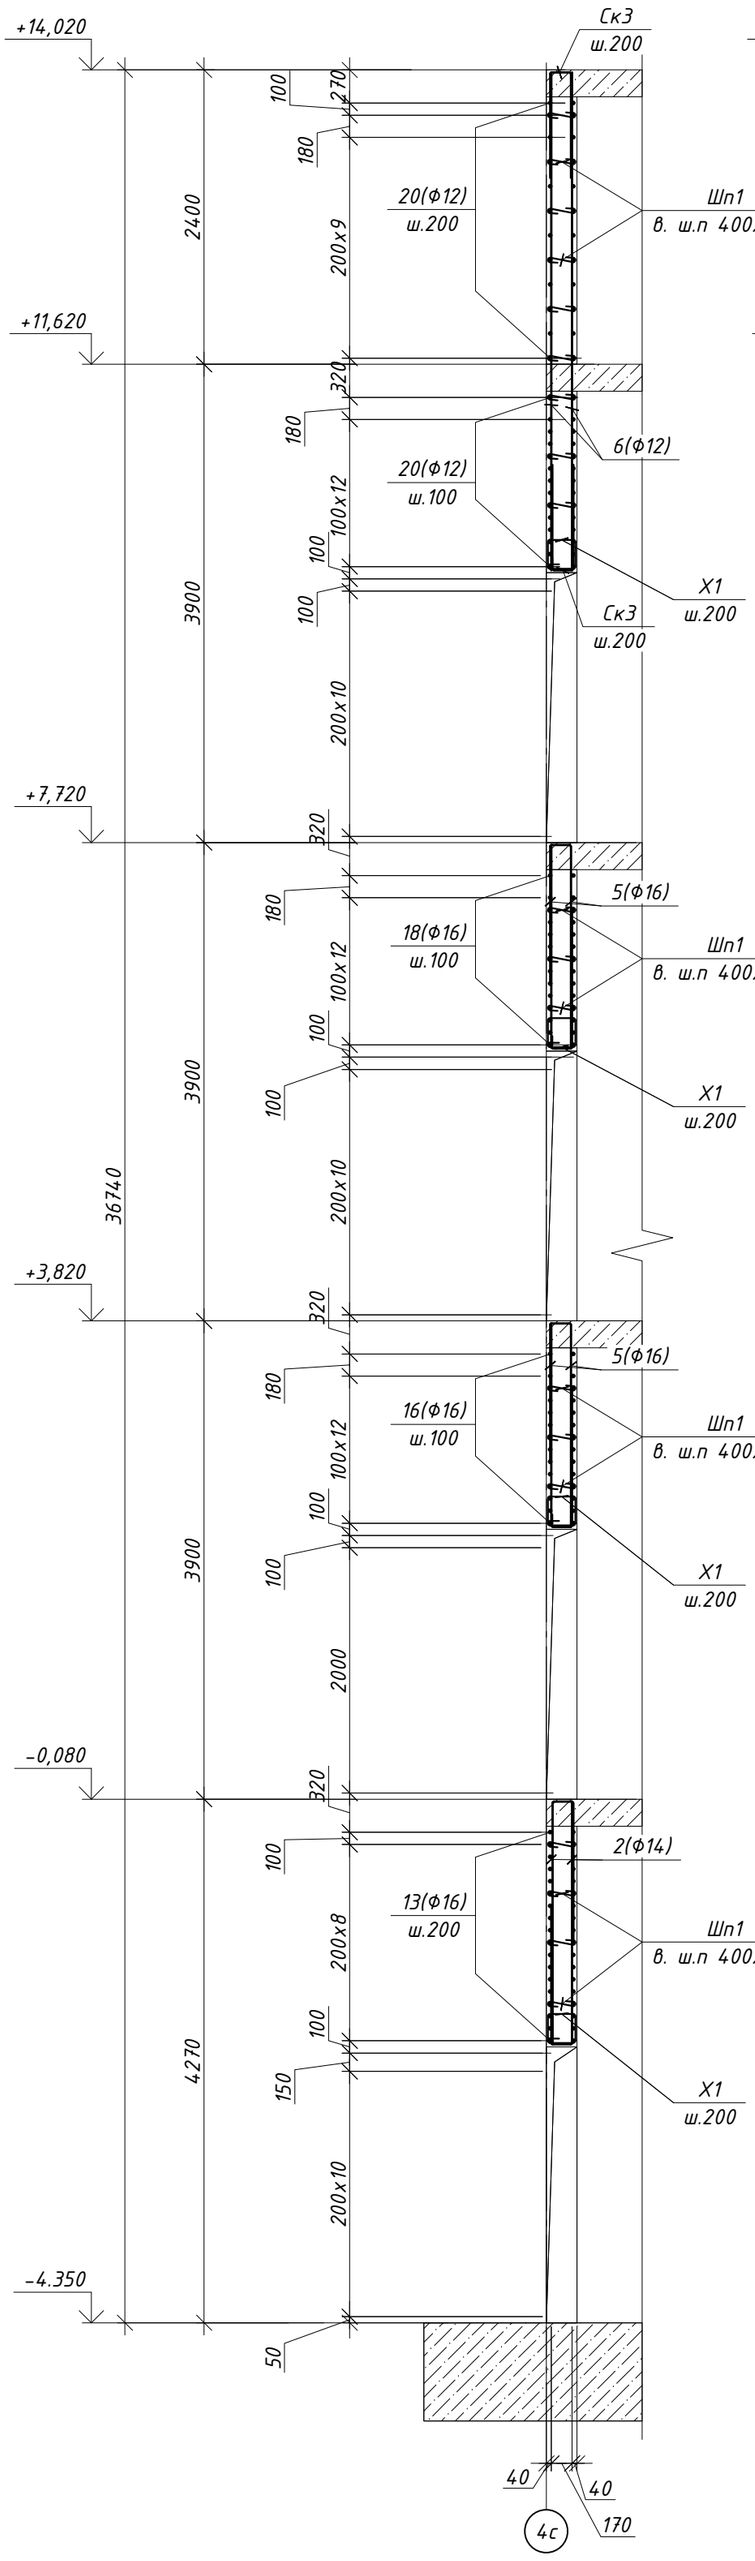

Разрез 8-8 (Армирование) М 1:50

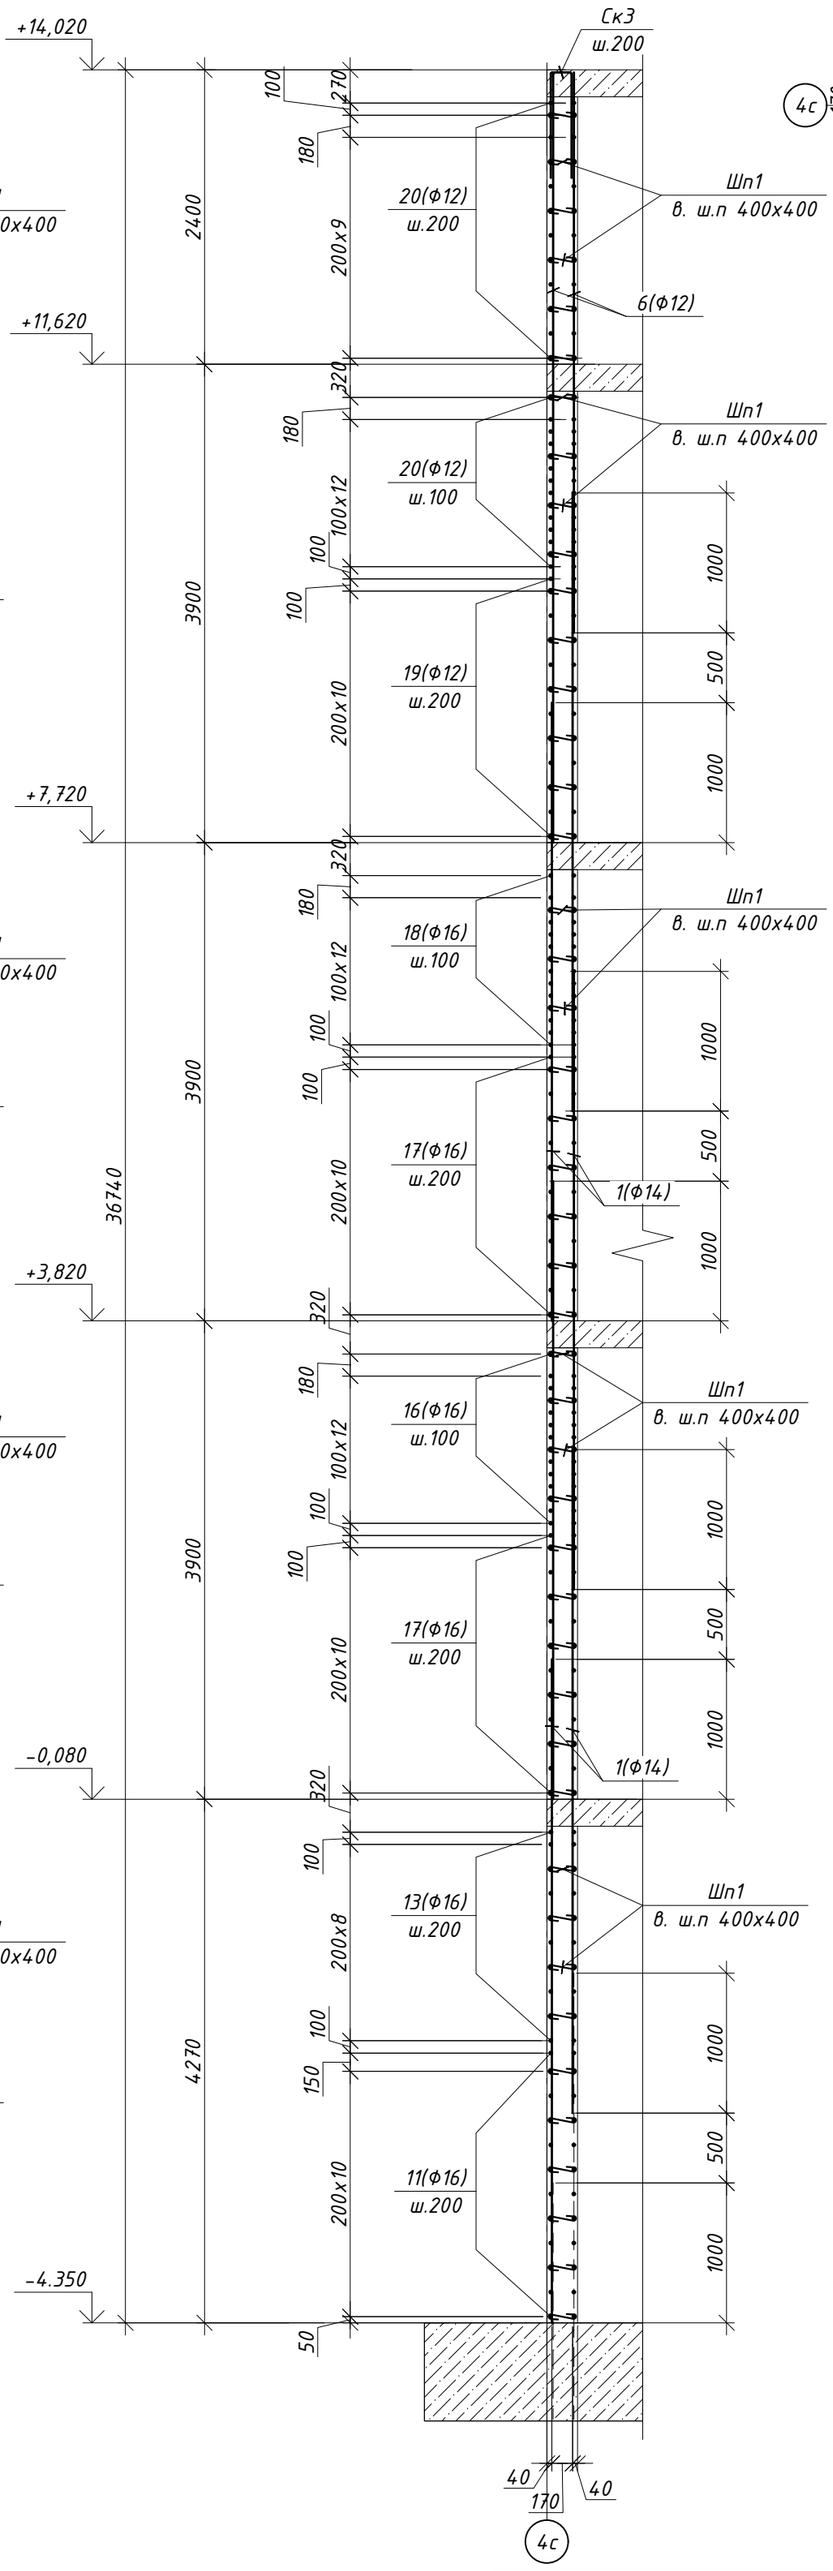

Разрез 9-9 (Армирование) М 1:50

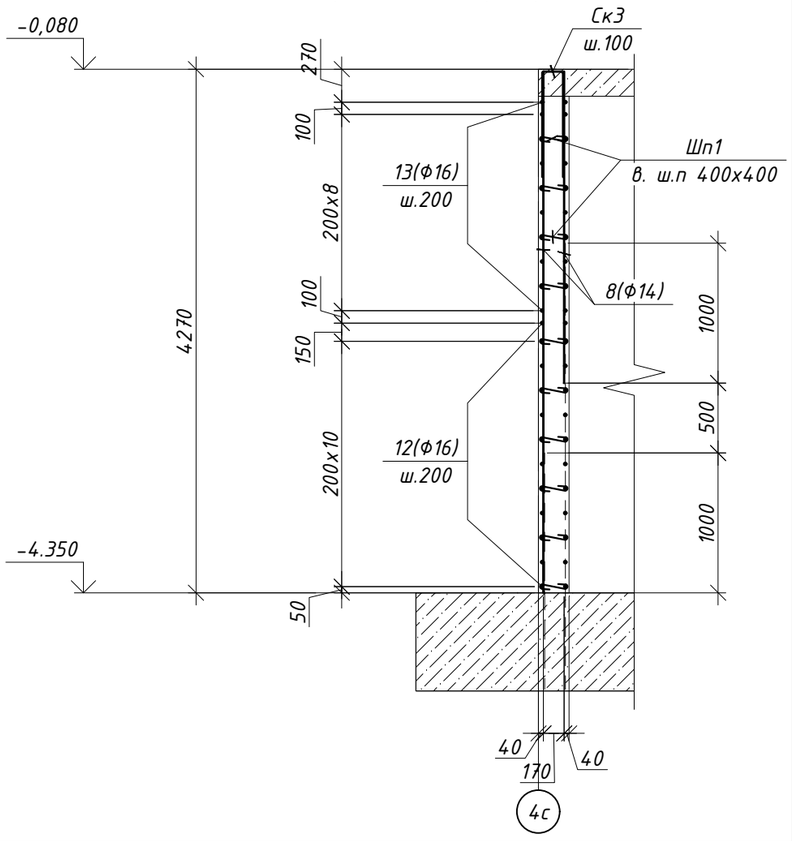

1. Общие указания см. л. – 1.
2. Данный лист читать совместно с л. КЖ-2.1....2.7 и 5.7 ... 5.10
3. Стыки рабочей арматуры внахлестку без сварки, на скрутках из вязальной проволоки не менее 3 шт. на стык. Длина нахлеста 71d. Стыки располагать вразбежку, чтобы площадь рабочей арматуры, стыкуемой в одном сечении, не превышала 50%.
4. Расход арматуры в погонных метрах приведен с учетом нахлеста.
5. Стержни, указанные в "Ведомости деталей", должны гнуться механическим способом в холодном состоянии с радиусом гиба 3d – 5d, где d – диаметр стержня
6. Узел стыковки арматуры нахлеста, анкеровки и Фрагмент обрамления проема смотреть на листе 4

Изм.	Кол.уч.	Лист	N док.	Подп.	Дата	65П-АИП-2024-1-КЖ		
						Строительство многопрофильной больницы на 250 коек с онкологическим центром и поликлиникой на 350 посещений, по адресу: Медеуский район, г. Алматы		
						"Блок 1 Секция 1"	Стадия: РП	Лист: 5.9	Листов:
ГКП		Курал М						
Проверил		Кыдырбай А				Разрезы 2-2;.....9-9.	АстанаИнжПроект	
Разраб.		Ауез Б						
Н.контроль		Ешенкулова						

Формат А2

Спецификация элементов

Поз.	Обозначение	Наименование	Кол.	Масса ед.кг	Примечание
		Стена См-2			4185.65
Х1*	ГОСТ 34028-2016(214-210-0101-0002)	ф 8 А 240 L= 980	522	0.39	201.85
Х2*	ГОСТ 34028-2016(214-210-0101-0002)	ф 8 А 240 L= 880	202	0.35	70.14
Шп1*	ГОСТ 34028-2016(214-210-0101-0002)	ф 8 А 240 L= 370	624	0.15	91.10
Ск2*	ГОСТ 34028-2016(214-210-0502-0001)	ф 12 А500С L= 1890	86	1.68	144.31
Ск3*	ГОСТ 34028-2016(214-210-0502-0002)	ф 14 А500С L= 2170	37	2.62	97.02
Ск4*	ГОСТ 34028-2016(214-210-0502-0003)	ф 16 А500С L= 2450	119	3.87	460.16
1	ГОСТ 34028-2016(214-210-0502-0002)	ф 14 А500С L= пог.м.	236.60	1.21	285.91
2*	ГОСТ 34028-2016(214-210-0502-0002)	ф 14 А500С L= 3150	26	3.81	98.97
3	ГОСТ 34028-2016(214-210-0502-0003)	ф 16 А500С L= пог.м.	129.01	1.58	203.62
5*	ГОСТ 34028-2016(214-210-0502-0003)	ф 16 А500С L= 2970	42	4.69	196.88
6	ГОСТ 34028-2016(214-210-0502-0001)	ф 12 А500С L= пог.м.	103.20	0.89	91.62
7	ГОСТ 34028-2016(214-210-0502-0002)	ф 14 А500С L= 4060	22	4.91	107.94
8	ГОСТ 34028-2016(214-210-0502-0002)	ф 14 А500С L= пог.м.	98.70	1.21	119.27
9	ГОСТ 34028-2016(214-210-0502-0004)	ф 18 А500С L= 2790	8	5.57	44.59
10*	ГОСТ 34028-2016(214-210-0502-0004)	ф 18 А500С L= 3780	8	7.55	60.41
11*	ГОСТ 34028-2016(214-210-0502-0004)	ф 16 А500С L= 3470	24	5.48	131.44
12	ГОСТ 34028-2016(214-210-0502-0003)	ф 16 А500С L= 6210	24	9.80	235.24
13	ГОСТ 34028-2016(214-210-0502-0003)	ф 16 А500С L= 9710	20	15.33	306.51
14*	ГОСТ 34028-2016(214-210-0502-0003)	ф 16 А500С L= 2670	24	4.21	101.14
15*	ГОСТ 34028-2016(214-210-0502-0003)	ф 16 А500С L= 1890	24	2.98	71.59
16	ГОСТ 34028-2016(214-210-0502-0003)	ф 16 А500С L= 2790	28	4.40	123.30
17*	ГОСТ 34028-2016(214-210-0502-0003)	ф 16 А500С L= 2290	48	3.61	173.49
18	ГОСТ 34028-2016(214-210-0502-0003)	ф 16 А500С L= 4260	28	6.72	188.26
19*	ГОСТ 34028-2016(214-210-0502-0001)	ф 12 А500С L= 2090	48	1.86	89.07
20	ГОСТ 34028-2016(214-210-0502-0001)	ф 12 А500С L= 4260	76	3.78	287.44
21	ГОСТ 34028-2016(214-210-0502-0003)	ф 16 А500С L= 5850	16	9.23	147.73
22	ГОСТ 34028-2016(214-210-0502-0001)	ф 12 А500С L= 3190	20	2.83	56.64
		Материалы:			
	(212-101-0901)	Класс бетона С 20/25 (В25)			14.63

Позиции со "*" см. "Ведомость деталей" см. на данном листе.

Ведомость деталей

Поз.	Эскиз	Поз.	Эскиз	Поз.	Эскиз
Х1	320; 170; 270; 220; по в.г. L=980	2	1000; 170; 1980; по н.г. L=3150	17	1060; 170; 1060; по н.г. L=2290
Х2	270; 170; 270; 170; по в.г. L=880	5	1140; 170; 1660; по н.г. L=2970	19	860; 170; 1060; по н.г. L=2090
Шп1	170; 100; 100; по в.г. L=370	10	1280; 170; 2330; по н.г. L=3780		
Ск2	860; 170; 860; по н.г. L=1890	11	1140; 170; 2160; по н.г. L=3470		
Ск3	1000; 170; 1000; по н.г. L=2170	14	1140; 170; 1360; по н.г. L=2670		
Ск4	1140; 170; 1140; по н.г. L=2450	15	860; 170; 860; по н.г. L=1890		


Ведомость расхода стали, кг

Марка элемента	Изделия арматурные									Всего
	Арматура класса									
	А240			А500С						
	ГОСТ 34028-2016(214-210-0101)			ГОСТ 34028-2016(214-210-0502)						
	Ф6	Ф8	Итого	Ф12	Ф14	Ф16	Ф18	Ф20	Итого	
Стена См-2	---	363.10	363.10	669.07	709.11	2339.38	104.99	---	3822.55	4185.65


Изм.	Кол.уч.	Лист	N док.	Подп.	Дата	65П-АИП-2024-1-КЖ			
						Строительство многопрофильной больницы на 250 коек с онкологическим центром и поликлиникой на 350 посещений, по адресу: Медеуский район, г. Алматы			
ГКП		Курал М				"Блок 1 Секция 1"	Стадия	Лист	Листов
Проверил		Кыдырбай А					РП	5.10	
Разраб.		Ауез Б				Спецификация стены См-2	АстанаИнжПроект		
Н.контроль		Ешенкулова							

Формат А3


Опалубочный чертеж монолитной стены по оси 5с стена Ст-3 (тол.250мм)

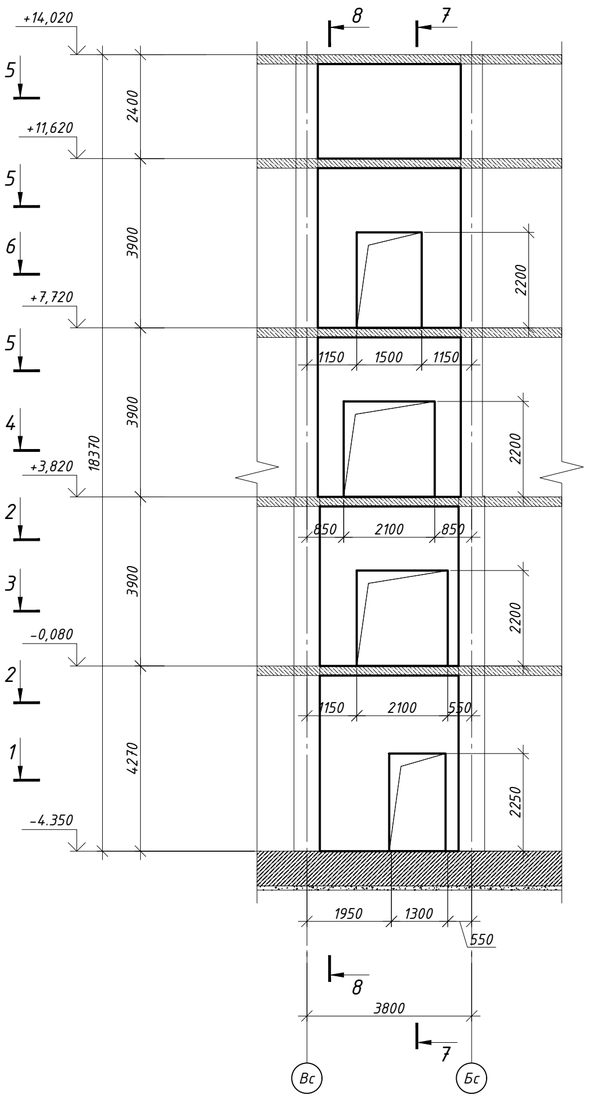


Разрез 1 - 1 (Опалубка) М 1:100

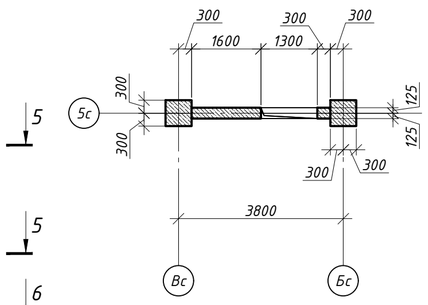


Разрез 2 - 2 (Опалубка) М 1:100

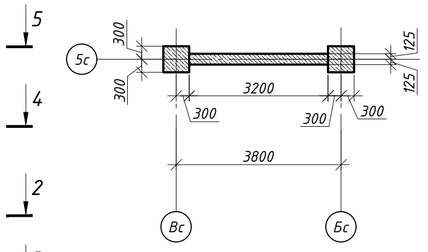


Разрез 3 - 3 (Опалубка) М 1:100

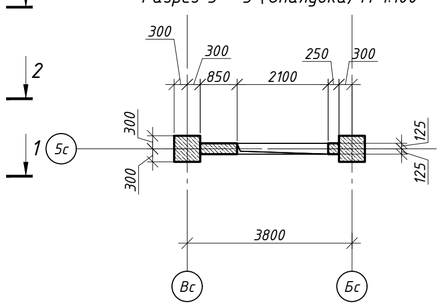


Разрез 4 - 4 (Опалубка) М 1:100

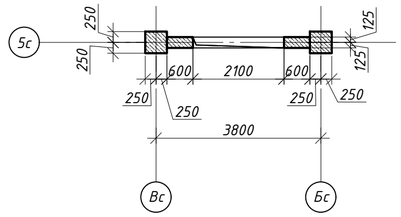


Разрез 5 - 5 (Опалубка) М 1:100

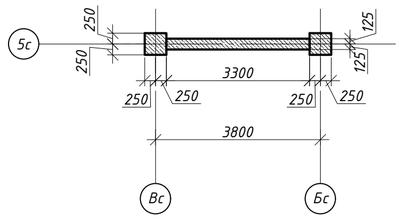


Разрез 6 - 6 (Опалубка) М 1:100

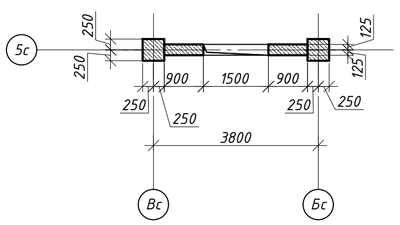


Разрез 7 - 7(Опалубка)

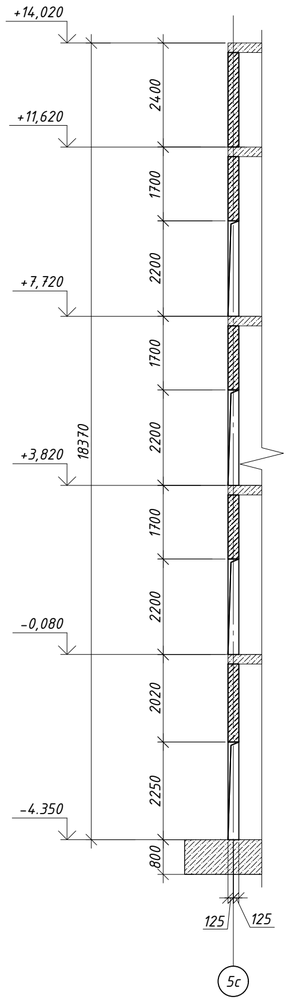

Разрез 8 - 8(Опалубка)

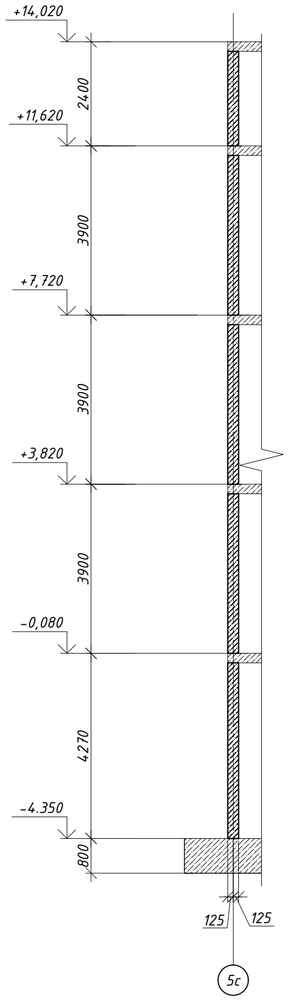



Фрагмент обрамления проема

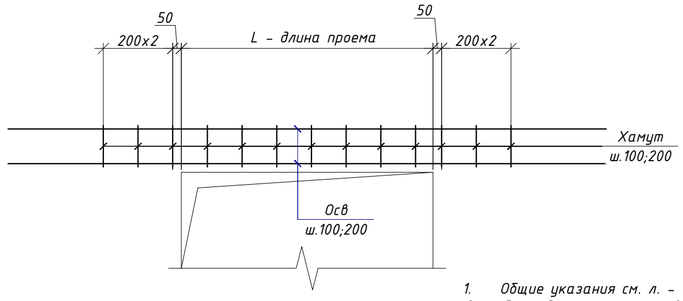


Узел стыковки вертикальной арматуры в нахлест и накладка


Анкеровка

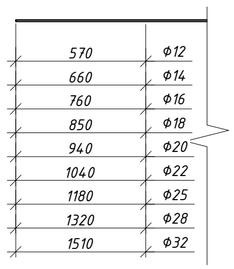

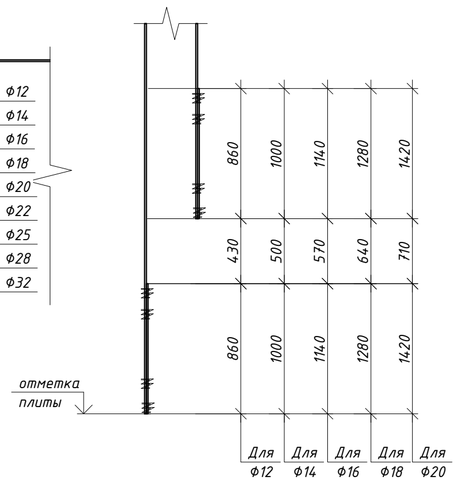

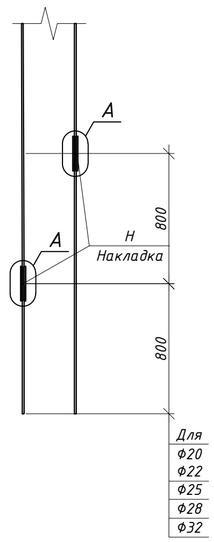

Узел стыковки Горизонтальной арматуры в нахлест

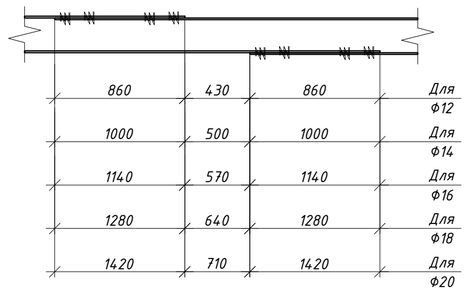


1. Общие указания см. л. - 1.
2. Данный лист читать совместно с л. КЖ-2.1...2.7 и 5.11 ... 5.13
3. Стыки рабочей арматуры внахлестку без сварки, на скрутках из вязальной проволоки не менее 3 шт. на стык. Длина нахлеста 71d. Стыки располагать вразбежку, чтобы площадь рабочей арматуры, стыкуемой в одном сечении, не превышала 50%.
4. Расход арматуры в погонных метрах приведен с учетом нахлеста.
5. Стержни, указанные в "Ведомости деталей", должны гнуться механическим способом в холодном состоянии с радиусом гиба 3d - 5d, где d - диаметр стержня
6. Узел стыковки арматуры нахлеста, анкеровки и Фрагмент обрамления проема смотреть на листе 4


						65П-АИП-2024-1-КЖ
						Строительство многопрофильной больницы на 250 коек с онкологическим центром и поликлиникой на 350 посещений, по адресу: Медеуский район, г. Алматы
Изм.	Кол.уч.	Лист	N док.	Подп.	Дата	
ГКП		Курал М				"Блок 1 Секция 1"
Проверил		Кыдырбай А				Стадия: РП; Лист: 5.11; Листов:
Разраб.		Ауез Б				Опалубочный чертеж монолитной стены по оси 5с стена Ст-3 (тол.250мм)
Н.контроль		Ешенкулова				АстанаИнжПроект

Формат А2


Основное вертикальное армирование монолитной стены по оси 5с стена См-3 (тол.250мм)

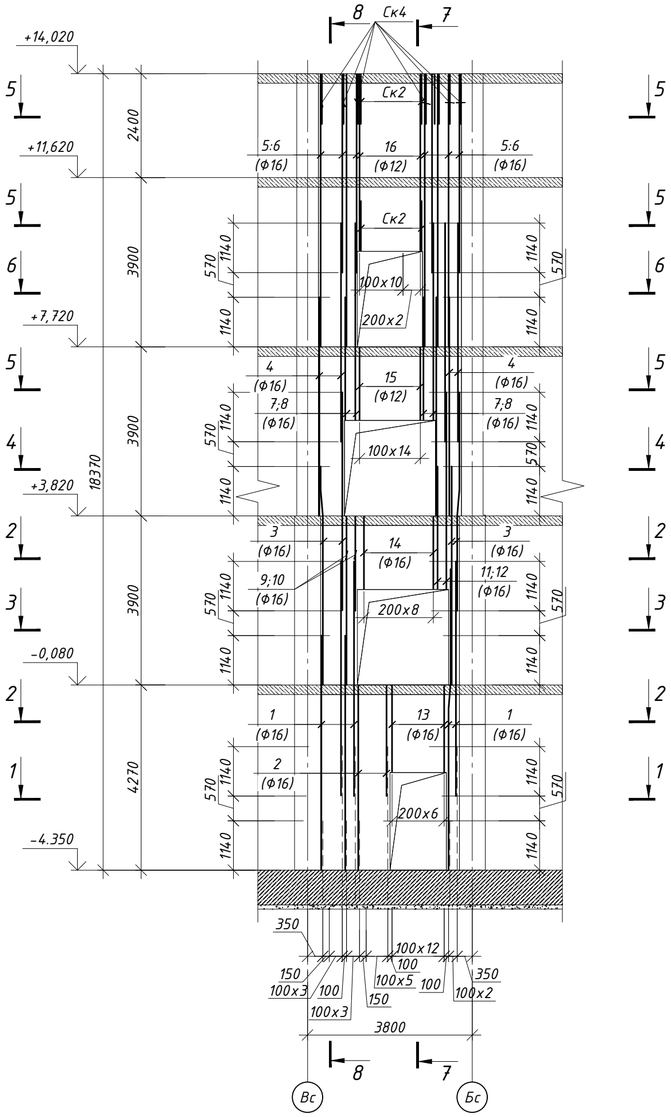


Основное горизонтальное армирование монолитной стены по оси 5с стена См-3 (тол.250мм)

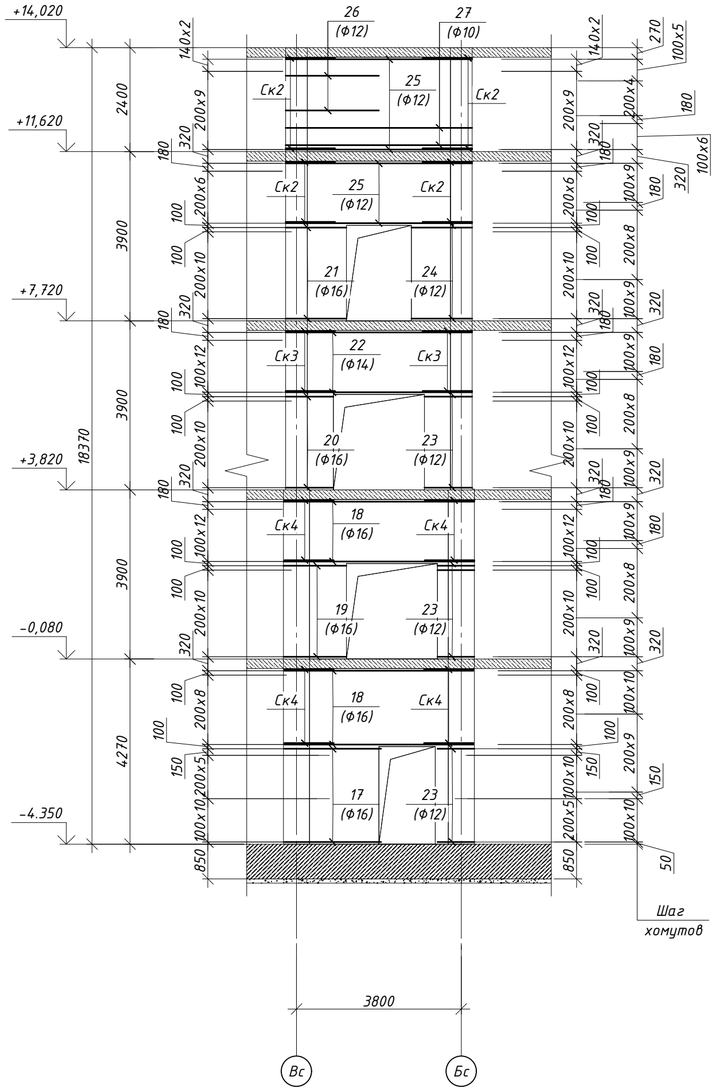


Разрез 3 - 3 (Армирование) М 1:50

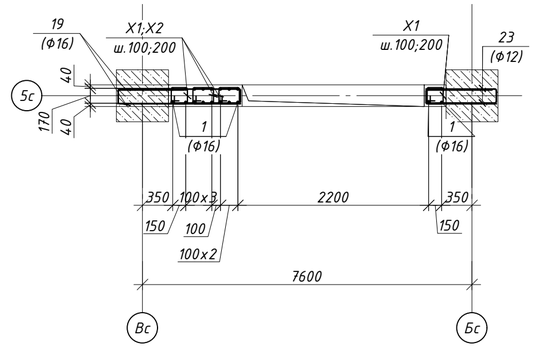


Разрез 4 - 4 (Армирование) М 1:50

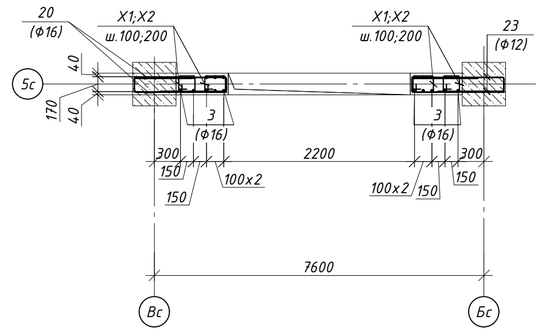


Разрез 5 - 5 (Армирование) М 1:50

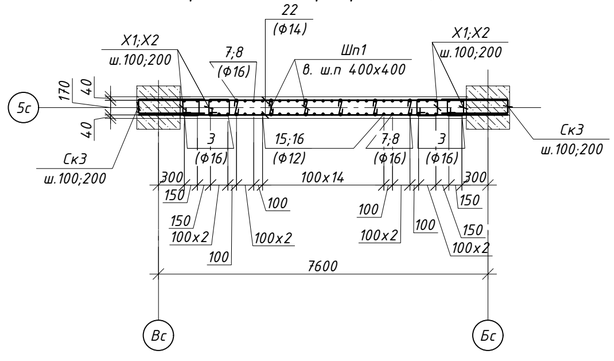

Разрез 1 - 1 (Армирование) М 1:50

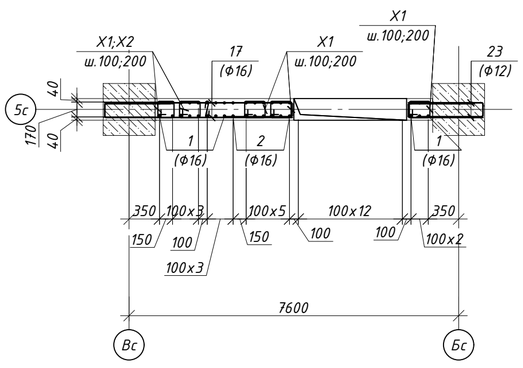


Разрез 2 - 2 (Армирование) М 1:50

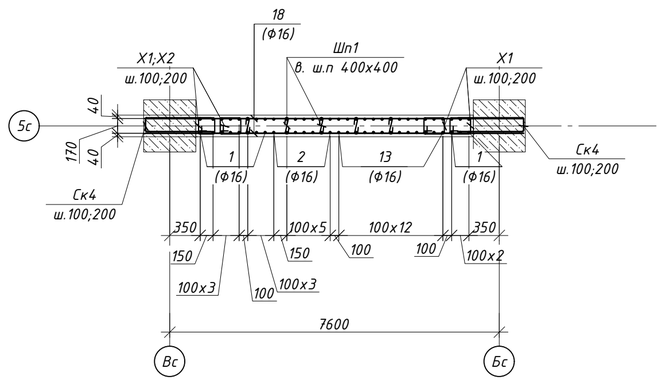


						65П-АИП-2024-1-КЖ	
						Строительство многопрофильной больницы на 250 коек с онкологическим центром и поликлиникой на 350 посещений, по адресу: Медеуский район, г. Алматы	
Изм.	Кол.уч	Лист	N док.	Подп.	Дата		
						"Блок 1 Секция 1"	Стадия: РП; Лист: 5.12; Листов:
ГКП		Курал М					
Проверил		Кыдырбай А				Основное армирование монолитной стены по оси 5с стена См-3 (тол.250мм)	АстанаИнжПроект
Разраб.		Ауез Б					
Н.контроль		Ешенкулова					

Формат А2


Разрез 6 – 6 (Армирование) М 1:50

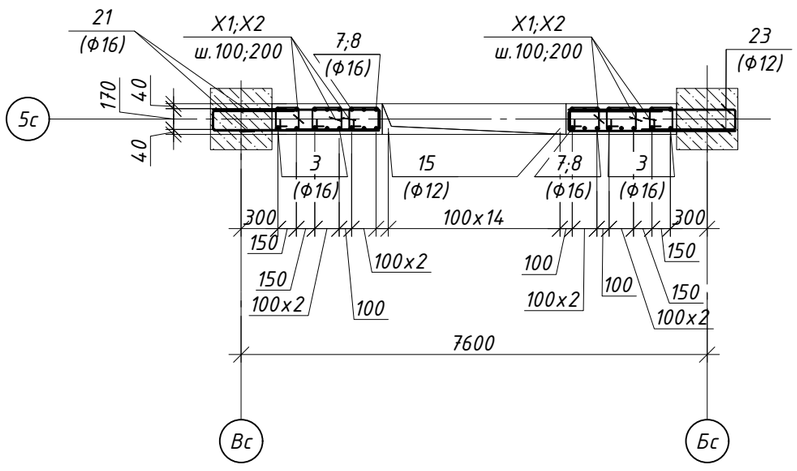

Разрез 7 – 7 (Армирование) М 1:50

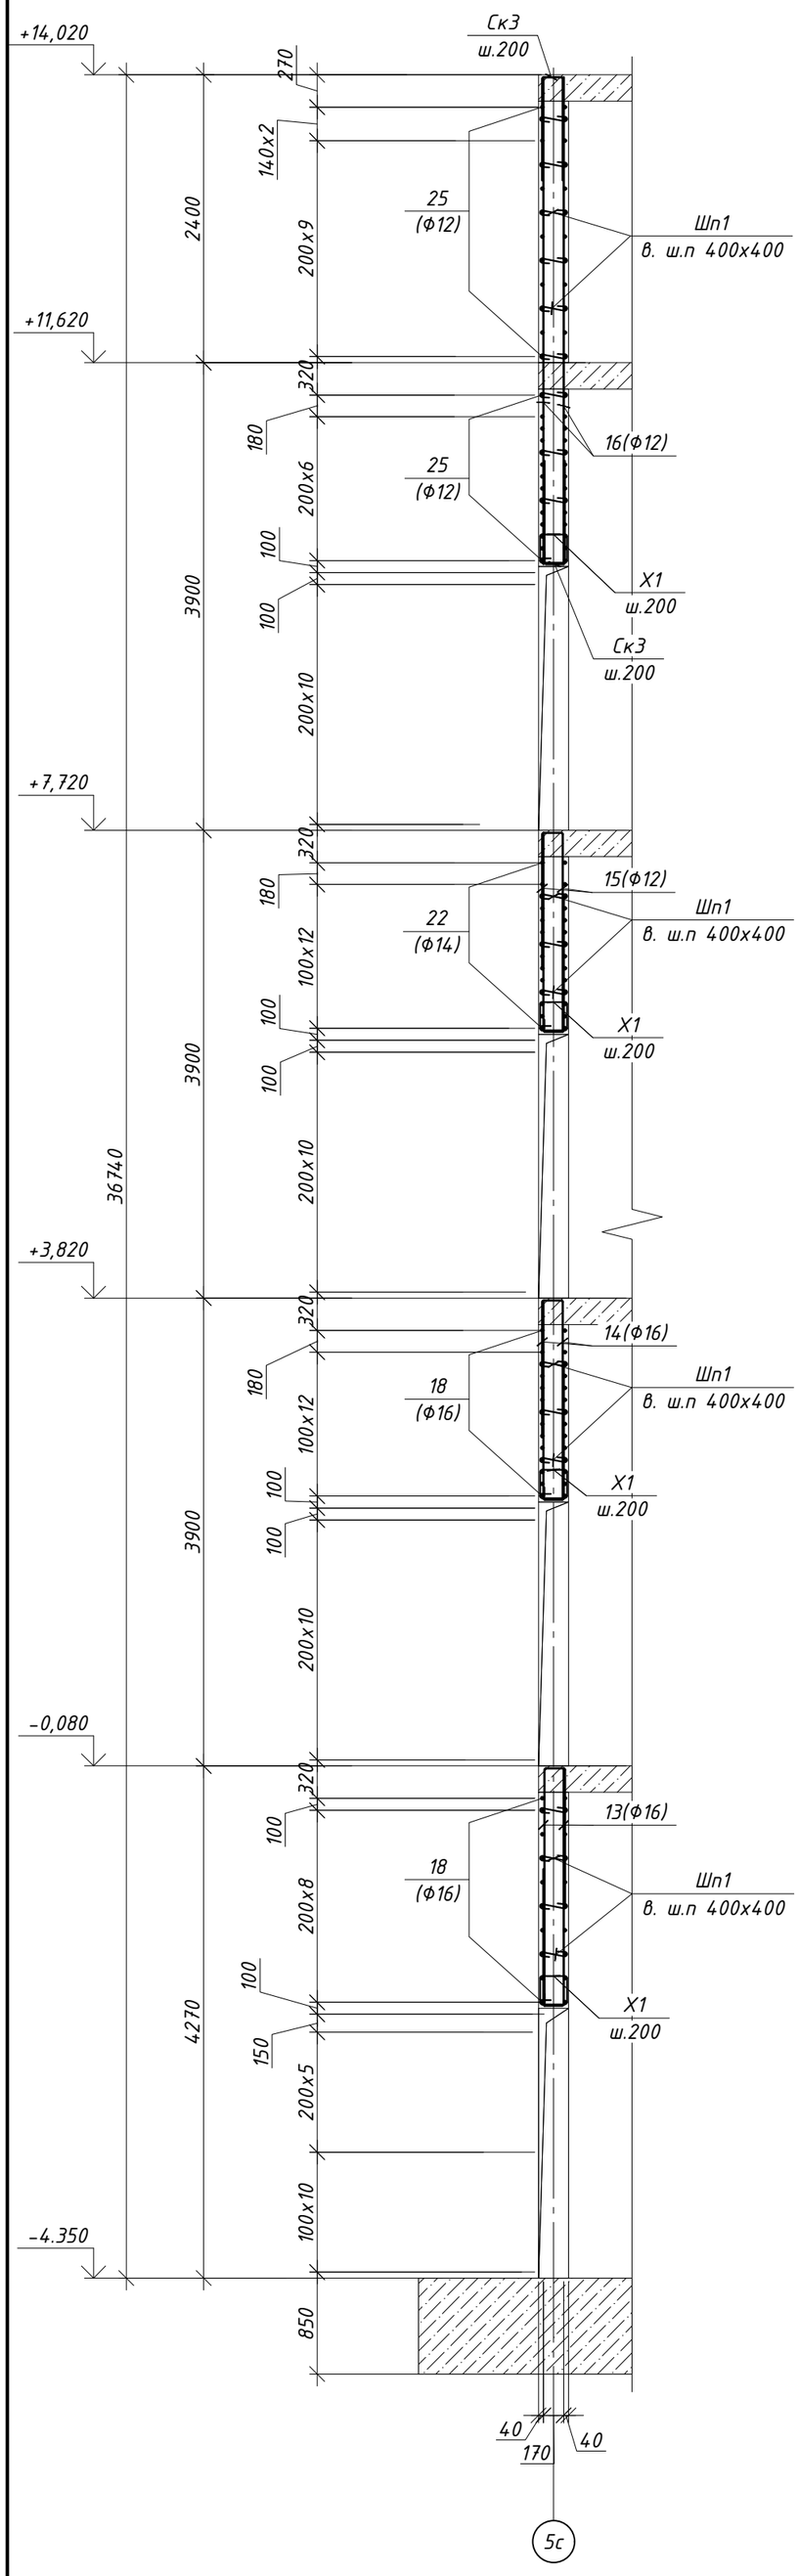

Узел Т

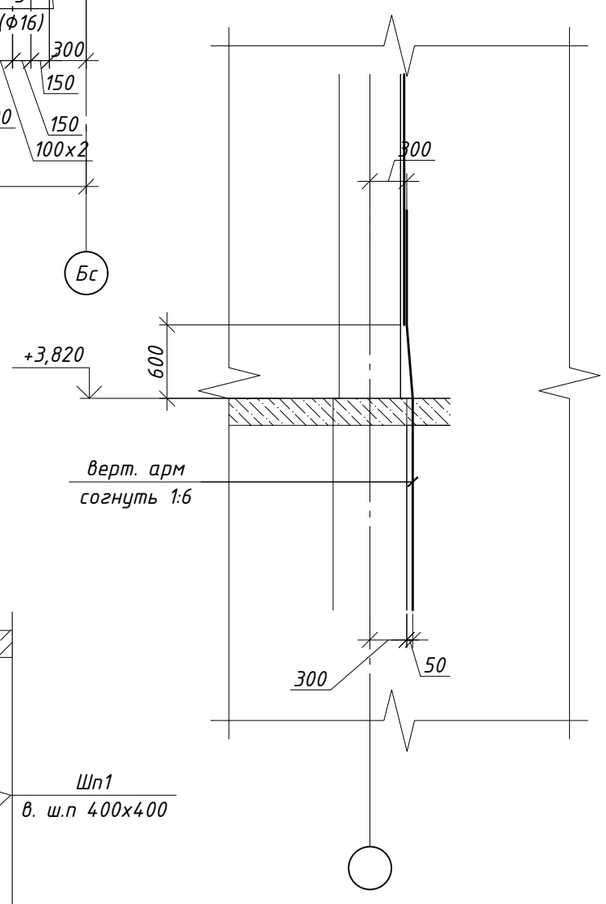

Спецификация элементов

Поз.	Обозначение	Наименование	Кол.	Масса ед.кг	Примечание
		Стена См-3			3085.99
X1*	ГОСТ 34028-2016(214-210-0101-0002)	ф 8 А 240 L= 980	576	0.39	222.73
X2*	ГОСТ 34028-2016(214-210-0101-0002)	ф 8 А 240 L= 880	264	0.35	91.67
Шп1*	ГОСТ 34028-2016(214-210-0101-0002)	ф 8 А 240 L= 370	105	0.15	15.33
Ск2*	ГОСТ 34028-2016(214-210-0502-0001)	ф 12 А500С L= 1890	66	1.68	110.75
Ск3*	ГОСТ 34028-2016(214-210-0502-0002)	ф 14 А500С L= 2170	28	2.62	73.42
Ск4*	ГОСТ 34028-2016(214-210-0502-0003)	ф 16 А500С L= 2450	64	3.87	247.48
1	ГОСТ 34028-2016(214-210-0502-0003)	ф 16 А500С L= 5410	22	8.54	187.85
2	ГОСТ 34028-2016(214-210-0502-0003)	ф 16 А500С L= пог.м.	47.53	1.58	75.02
3	ГОСТ 34028-2016(214-210-0502-0003)	ф 16 А500С L= 5025	20	7.93	158.62
4	ГОСТ 34028-2016(214-210-0502-0003)	ф 16 А500С L= 5040	20	7.95	159.10
5	ГОСТ 34028-2016(214-210-0502-0003)	ф 16 А500С L= 6280	10	9.91	99.12
6	ГОСТ 34028-2016(214-210-0502-0003)	ф 16 А500С L= 4570	10	7.21	72.13
7	ГОСТ 34028-2016(214-210-0502-0003)	ф 16 А500С L= 2820	6	4.45	26.71
8	ГОСТ 34028-2016(214-210-0502-0003)	ф 16 А500С L= 2820	6	4.45	26.71
9	ГОСТ 34028-2016(214-210-0502-0003)	ф 16 А500С L= 3880	3	6.12	18.37
10	ГОСТ 34028-2016(214-210-0502-0003)	ф 16 А500С L= 2170	3	3.42	10.27
11	ГОСТ 34028-2016(214-210-0502-0003)	ф 16 А500С L= 2820	3	4.45	13.35
12	ГОСТ 34028-2016(214-210-0502-0003)	ф 16 А500С L= 4525	3	7.14	21.43
13	ГОСТ 34028-2016(214-210-0502-0003)	ф 16 А500С L= 3150	14	4.97	69.60
14	ГОСТ 34028-2016(214-210-0502-0003)	ф 16 А500С L= 2970	18	4.69	84.38
15	ГОСТ 34028-2016(214-210-0502-0001)	ф 12 А500С L= 2690	30	2.39	71.65
16	ГОСТ 34028-2016(214-210-0502-0001)	ф 12 А500С L= 4060	26	3.60	93.72
17	ГОСТ 34028-2016(214-210-0502-0003)	ф 16 А500С L= 3470	34	5.48	186.21
18	ГОСТ 34028-2016(214-210-0502-0003)	ф 16 А500С L= 4360	20	6.88	137.63
19	ГОСТ 34028-2016(214-210-0502-0003)	ф 16 А500С L= 2720	24	4.29	103.03
20	ГОСТ 34028-2016(214-210-0502-0003)	ф 16 А500С L= 2370	24	3.74	89.78
21	ГОСТ 34028-2016(214-210-0502-0003)	ф 16 А500С L= 2670	24	4.21	101.14
22	ГОСТ 34028-2016(214-210-0502-0002)	ф 14 А500С L= 4260	28	5.15	144.14
23	ГОСТ 34028-2016(214-210-0502-0001)	ф 12 А500С L= 1890	82	1.68	137.59
24	ГОСТ 34028-2016(214-210-0502-0001)	ф 12 А500С L= 2390	24	2.12	50.93
25	ГОСТ 34028-2016(214-210-0502-0001)	ф 12 А500С L= 4260	40	3.78	151.28
26	ГОСТ 34028-2016(214-210-0502-0001)	ф 12 А500С L= 2150	10	1.91	19.09
27	ГОСТ 34028-2016(214-210-0501-0005)	ф 10 А500С L= 4260	6	2.63	15.76
		Материалы:			
	(212-101-0901)	Класс бетона С 20/25 (В25)			10.19

Позиции со "*" см. "Ведомость деталей" см. на данном листе.

Ведомость деталей

Поз.	Эскиз	Поз.	Эскиз	Поз.	Эскиз
X1	320; 170; 270; 220; по в.г. L=980	13	1000; 170; 1980; по н.г. L=3150	21	1140; 170; 1360; по н.г. L=2670
X2	270; 170; 270; 170; по в.г. L=880	14	1140; 170; 1660; по н.г. L=2970	23	860; 170; 860; по н.г. L=1890
Шп1	170; 100; 100; по в.г. L=370	15	860; 170; 1660; по н.г. L=2690	24	860; 170; 1360; по н.г. L=2390
Ск2	860; 170; 860; по н.г. L=1890	17	1140; 170; 2160; по н.г. L=3470		
Ск3	1000; 170; 1000; по н.г. L=2170	19	1140; 170; 1410; по н.г. L=2720		
Ск4	1140; 170; 1140; по н.г. L=2450	20	1140; 170; 1060; по н.г. L=2370		


Ведомость расхода стали, кг

Марка элемента	Изделия арматурные										Всего
	Арматура класса										
	А240			А500С							
	ГОСТ 34028-2016(214-210-0101)			ГОСТ 34028-2016(214-210-0502)(214-210-0501)							
	ф6	ф8	Итого	ф10	ф12	ф14	ф16	ф18	ф20	Итого	
Стена См-3	---	329.73	329.73	15.76	635.00	217.56	1887.93	---	---	2756.26	3085.99


Изм.	Кол.уч.	Лист	N док.	Подп.	Дата	65П-АИП-2024-1-КЖ			
						Строительство многопрофильной больницы на 250 коек с онкологическим центром и поликлиникой на 350 посещений, по адресу: Медеуский район, г. Алматы			
						"Блок 1 Секция 1"	Стадия	Лист	Листов
							РП	5.13	
ГКП		Курал М				Спецификация стены См3	АстанаИнжПроект		
Проверил		Кыдырбай А							
Разраб.		Ауез Б							
Н.контроль		Ешенкулова							

Формат А2


Опалубочный чертеж монолитной стены по оси 6с стена См-4 (тол.250мм)

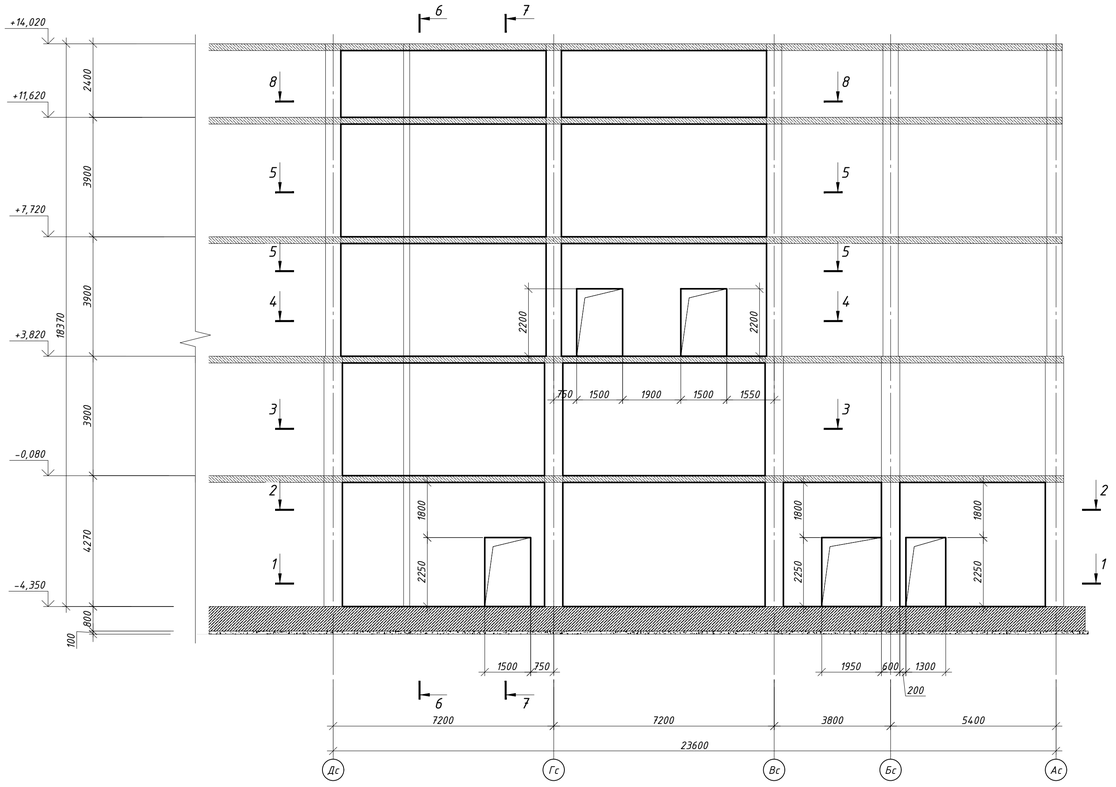


Разрез 6 - 6(Опалубка)

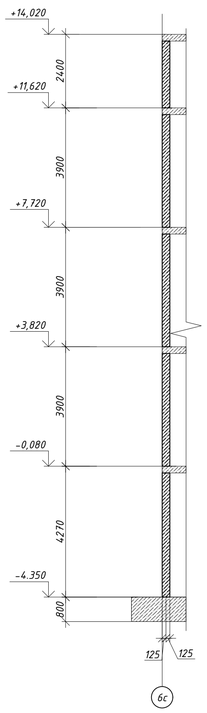

Разрез 7 - 7(Опалубка)

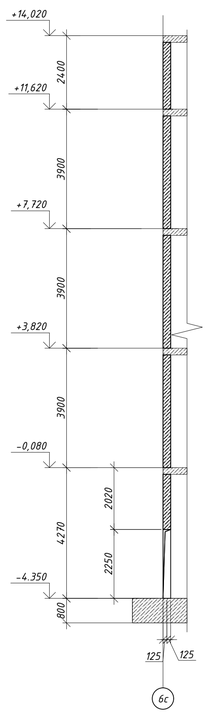


Фрагмент обрамления проема

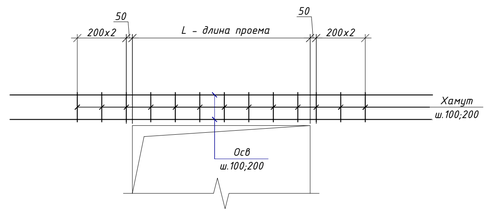


Узел стыковки вертикальной арматуры в нахлест и накладка


Анкеровка

570	Ф12
660	Ф14
760	Ф16
850	Ф18
940	Ф20
1040	Ф22
1180	Ф25
1320	Ф28
1510	Ф32

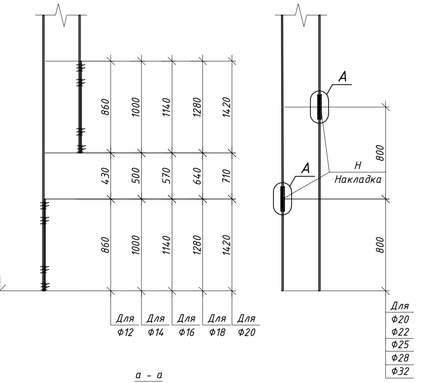


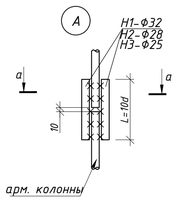


a - a

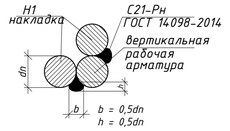


Разрез 1 - 1(Опалубка)

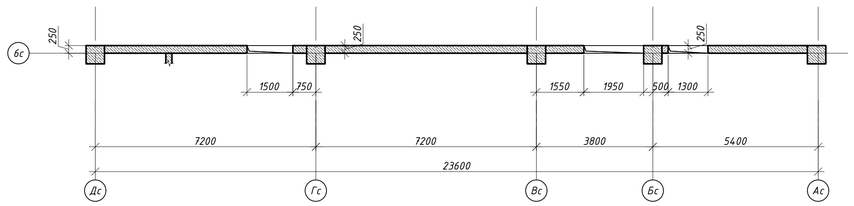


Разрез 2 - 2(Опалубка)

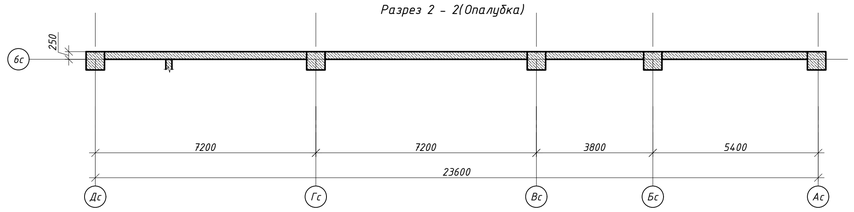


Разрез 3 - 3(Опалубка)

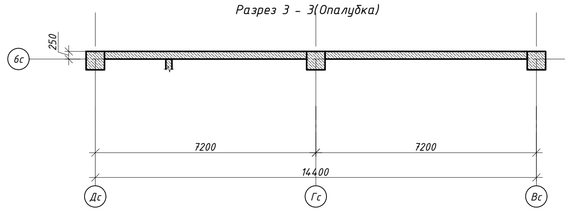


Разрез 4 - 4(Опалубка)

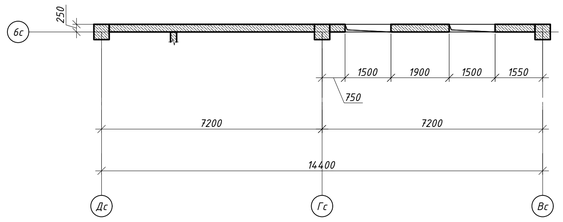

Разрез 5 - 5; 8 - 8 (Опалубка)

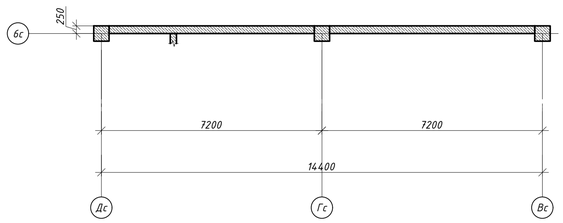

Узел стыковки Горизонтальной арматуры в нахлест

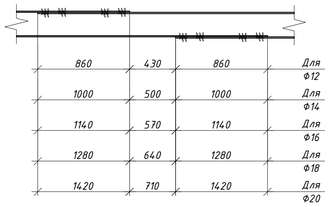

Б

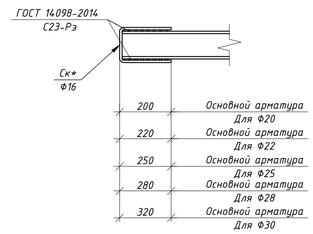


Таблица размеров Накладка


Марка эл-та	d'н	L	вес
	мм.		кг.
H1	32	320	2.01
H2	28	280	1.35
H3	25	250	0.96
H4	22	220	0.66
H5	20	200	0.49

1. Общие указания см. л. - 1.
2. Данный лист читать совместно с л. КЖ-2.1...2.7 и 5.14 ... 5.17
3. Стыки рабочей арматуры внахлестку без сварки, на скрутках из вязальной проволоки не менее 3 шт. на стык. Длина нахлеста 71d. Стыки располагать вразбежку, чтобы площадь рабочей арматуры, стыкуемой в одном сечении, не превышала 50%.
4. Расход арматуры в погонных метрах приведен с учетом нахлеста.
5. Стержни, указанные в "Ведомости деталей", должны гнуться механическим способом в холодном состоянии с радиусом гиба 3d - 5d, где d - диаметр стержня
6. Узел стыковки арматуры нахлеста, анкеровки и Фрагмент обрамления проема смотреть на листе 4


							65П-АИП-2024-1-КЖ
							Строительство многопрофильной больницы на 250 коек с онкологическим центром и поликлиникой на 350 посещений, по адресу: Медеуский район, г. Алматы
Изм.	Кол.уч	Лист	N док.	Подп.	Дата		
						"Блок 1 Секция 1"	Стадия: РП; Лист: 5.14; Листов:
ГКП		Курал М					
Проверил		Кыдырбай А				Опалубочный чертеж монолитной стены по оси 6с стена См-4 (тол.250мм)	АстанаИнжПроект
Разраб.		Ауез Б					
Н.контроль		Ешенкулова					

Формат А1


Основное вертикальное армирование монолитной стены по оси 5с стена См-4 (тол.250мм)

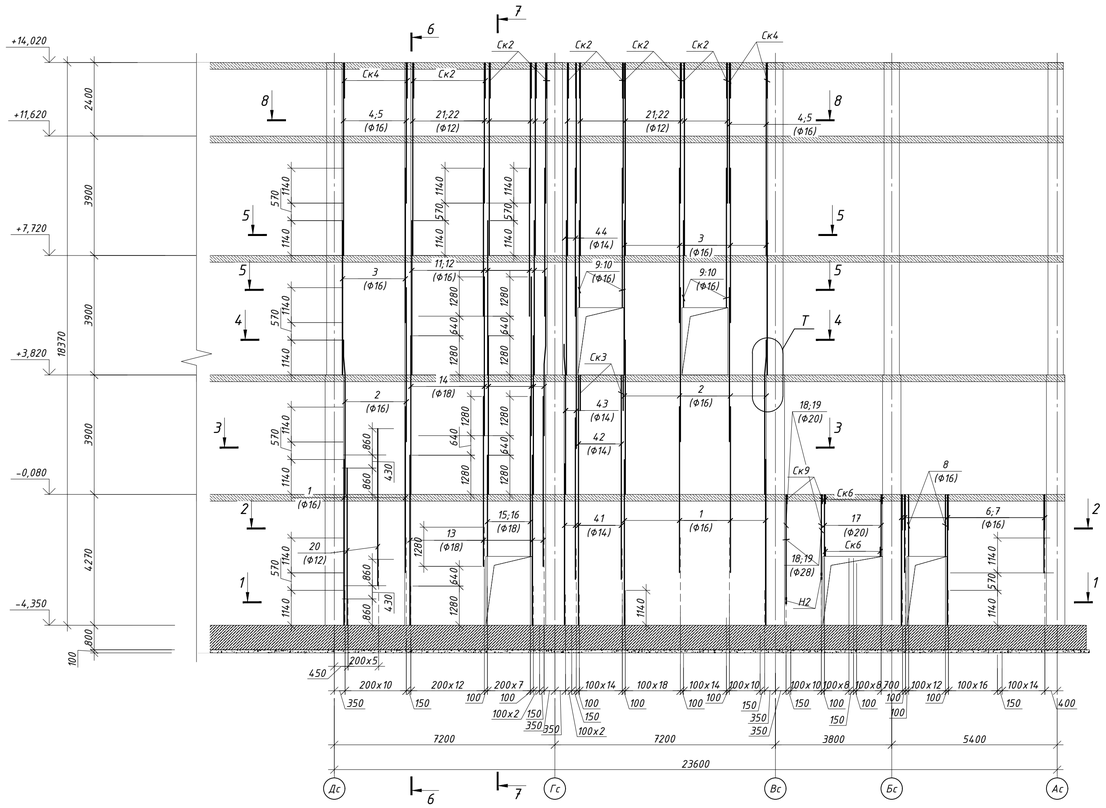


Основное горизонтальное армирование монолитной стены по оси 5с стена См-4 (тол.250мм)

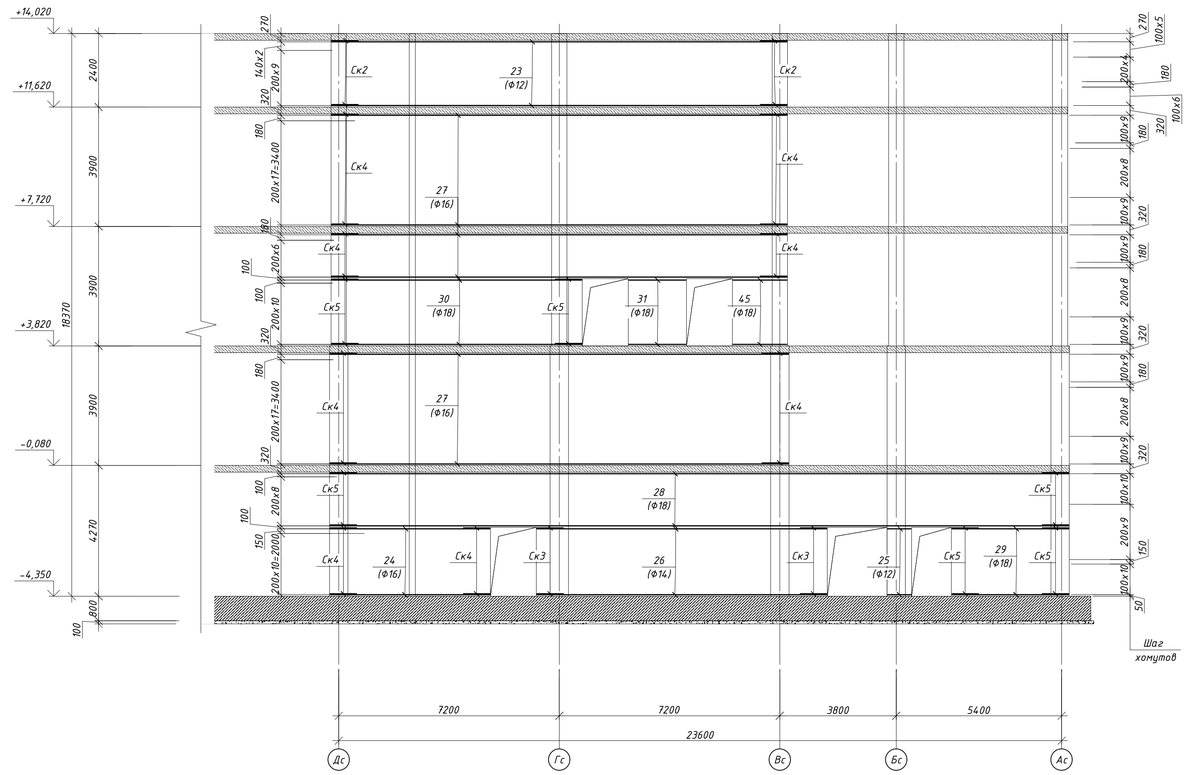

Дополнительное горизонтальное армирование монолитной стены по оси 1с стена См-2 (тол.250мм)

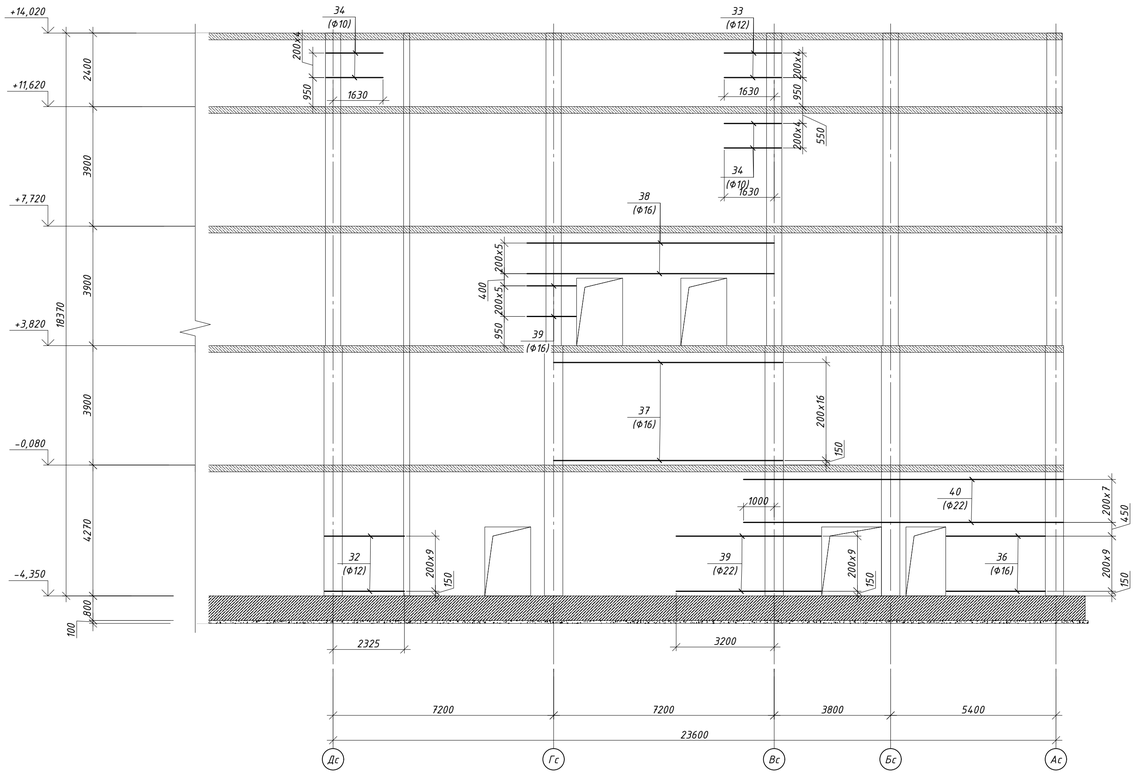


Разрез 3 - 3 (Армирование) М 1:50

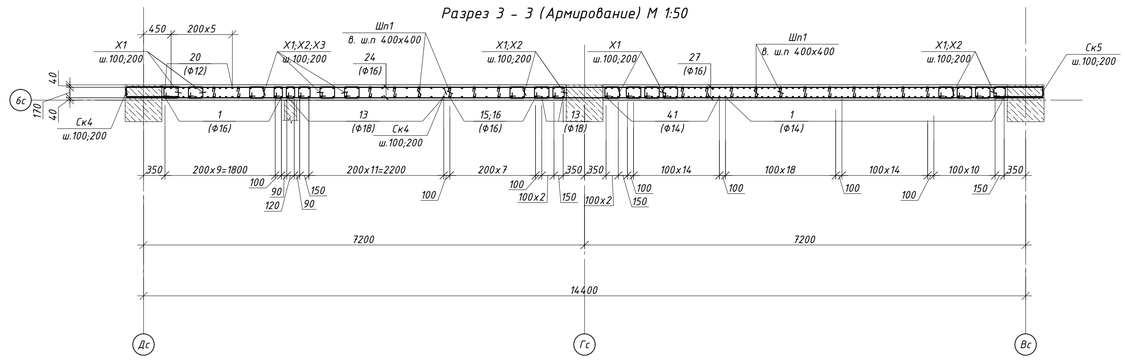


1. Общие указания см. л. - 1.
2. Данный лист читать совместно с л. КЖ-2.1...2.7 и 5.14 ... 5.17
3. Стыки рабочей арматуры внахлестку без сварки, на скрутках из вязальной проволоки не менее 3 шт. на стык. Длина нахлеста 71d. Стыки располагать вразбежку, чтобы площадь рабочей арматуры, стыкуемой в одном сечении, не предышала 50%.
4. Расход арматуры в погонных метрах приведен с учетом нахлеста.
5. Стержни, указанные в "Ведомости деталей", должны гнуться механическим способом в холодном состоянии с радиусом гиба 3d - 5d, где d - диаметр стержня
6. Узел стыковки арматуры нахлеста, анкеровки и Фрагмент обрамления проема смотреть на листе 4

						65П-АИП-2024-1-КЖ
						Строительство многопрофильной больницы на 250 коек с онкологическим центром и поликлиникой на 350 посещений, по адресу: Медеуский район, г. Алматы
Изм.	Кол.уч	Лист	N док.	Подп.	Дата	
						"Блок 1 Секция 1" — Стадия: РП; Лист: 5.15; Листов:
ГКП		Курал М				
Проверил		Кыдырбай А				
Разраб.		Ауез Б				Основное армирование монолитной стены по оси 6с стена См-4 (тол.250мм)
Н.контроль		Ешенкулова				АстанаИнжПроект
						Формат А1


Разрез 1 - 1 (Армирование) М 1:50

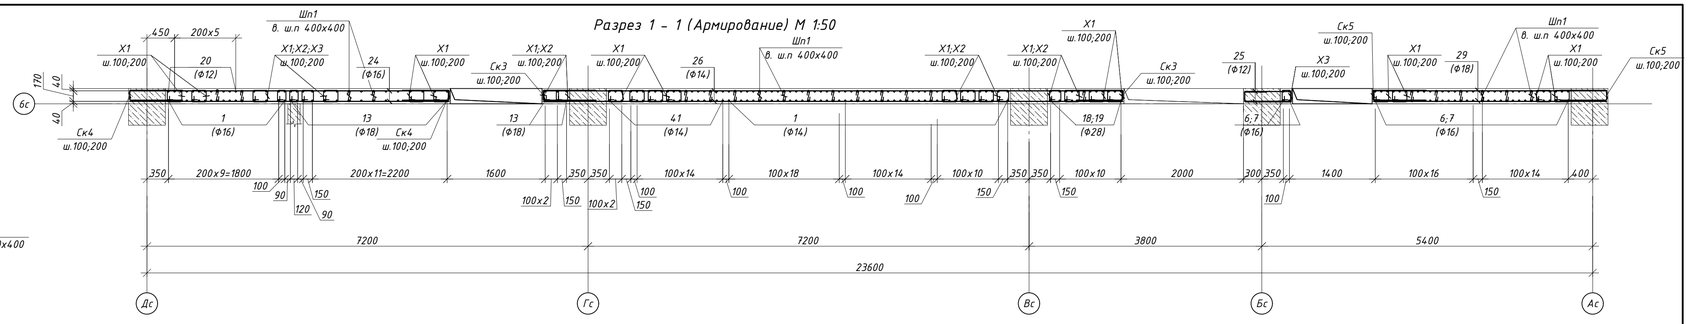


Разрез 2 - 2 (Армирование) М 1:50

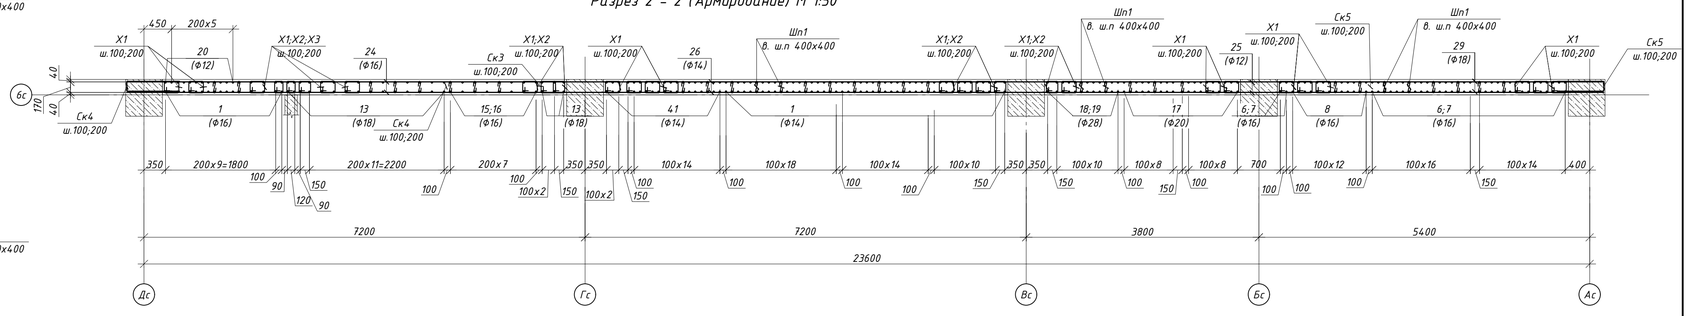


Разрез 4 - 4 (Армирование) М 1:50

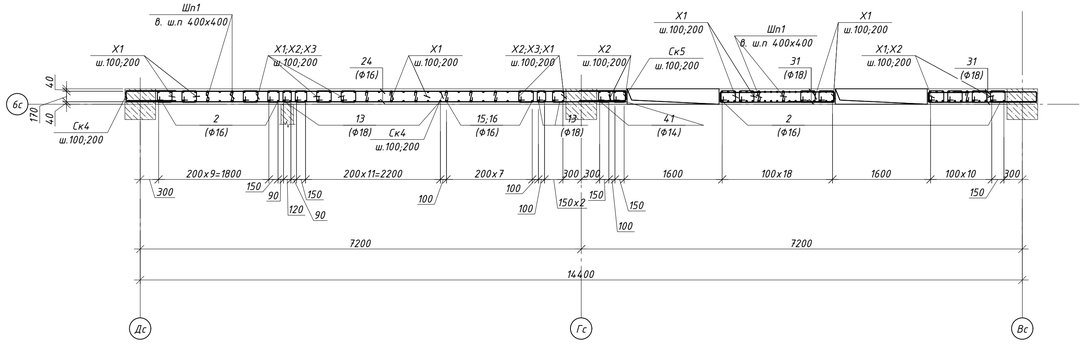


Разрез 5 - 5 (Армирование) М 1:50

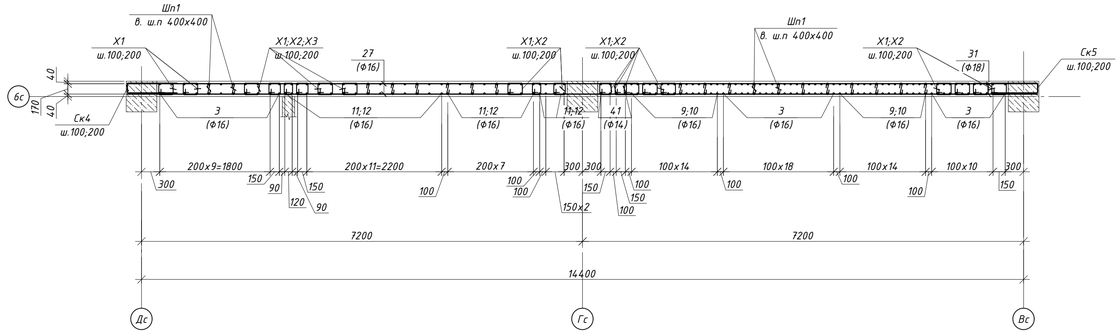


Разрез 6 - 6 (Армирование) М 1:50

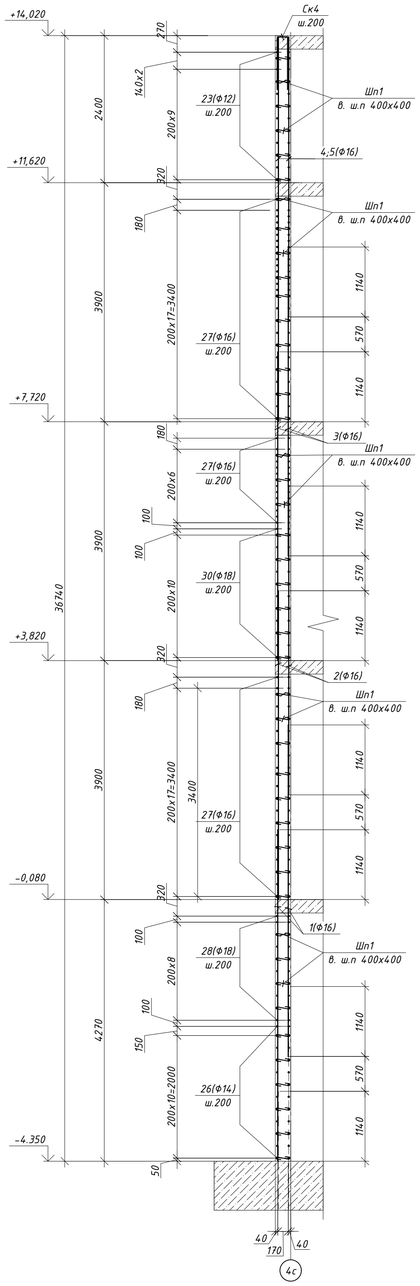


Разрез 7 - 7 (Армирование) М 1:50

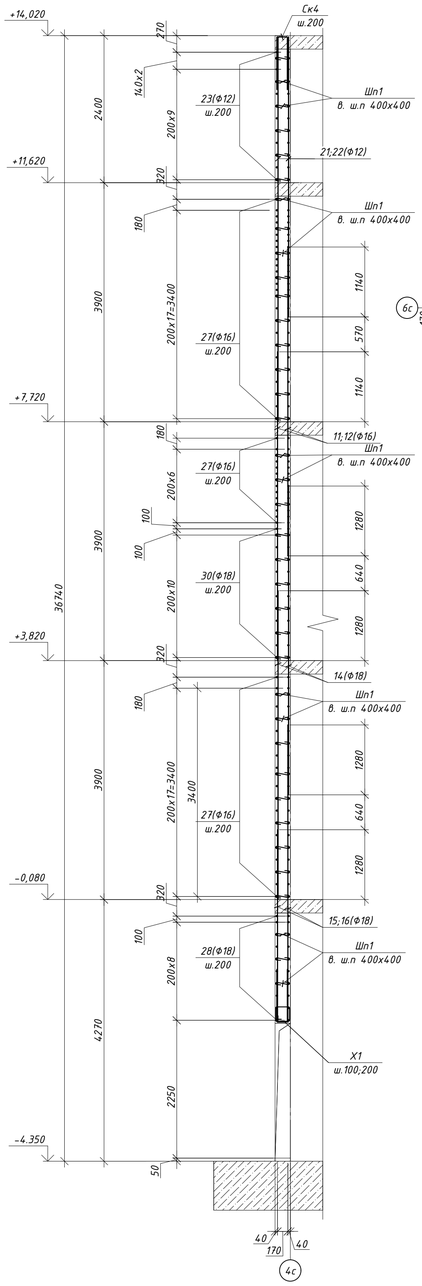

Разрез 8 - 8 (Армирование) М 1:50

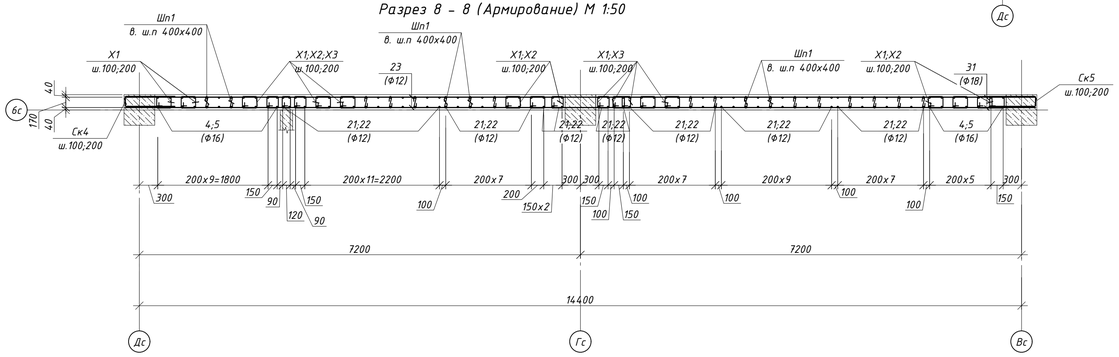

Узел Т

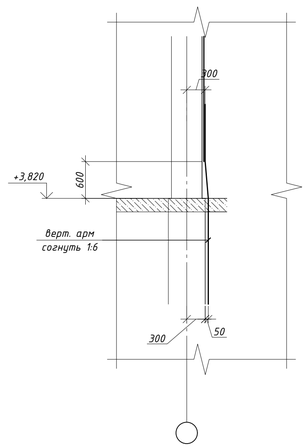

1. Общие указания см. л. - 1.
2. Данный лист читать совместно с л. КЖ-2.1...2.7 и 5.14 ... 5.17
3. Стыки рабочей арматуры внахлестку без сварки, на скрутках из вязальной проволоки не менее 3 шт. на стык. Длина нахлеста 71d. Стыки располагать вразбежку, чтобы площадь рабочей арматуры, стыкуемой в одном сечении, не превышала 50%.
4. Расход арматуры в погонных метрах приведен с учетом нахлеста.
5. Стержни, указанные в "Ведомости деталей", должны гнуться механическим способом в холодном состоянии с радиусом гиба 3d - 5d, где d - диаметр стержня
6. Узел стыковки арматуры нахлеста, анкеровки и Фрагмент обрамления проема смотреть на листе 4

						65П-АИП-2024-1-КЖ	
						Строительство многопрофильной больницы на 250 коек с онкологическим центром и поликлиникой на 350 посещений, по адресу: Медеуский район, г. Алматы	
Изм.	Кол.уч.	Лист	N док.	Подп.	Дата		
						"Блок 1 Секция 1"	Стадия: РП; Лист: 5.16; Листов:
ГКП		Курал М					
Проверил		Кыдырбай А					
Разраб.		Ауез Б				Разрезы 1-1,.....8-8	АстанаИнжПроект
Н.контроль		Ешенкулова					Формат А1

Спецификация элементов

Поз.	Обозначение	Наименование	Кол.	Масса ед.кг	Примечание
		Стена См-4			16214.23
Х1*	ГОСТ 34028-2016(214-210-0101-0002)	ф 8 А 240 L= 980	2017	0.39	779.96
Х2*	ГОСТ 34028-2016(214-210-0101-0002)	ф 8 А 240 L= 880	660	0.35	229.17
Х3*	ГОСТ 34028-2016(214-210-0101-0002)	ф 8 А 240 L= 780	396	0.31	121.88
Шп1*	ГОСТ 34028-2016(214-210-0101-0002)	ф 8 А 240 L= 370	624	0.15	91.10
Ск2*	ГОСТ 34028-2016(214-210-0502-0001)	ф 12 А500С L= 1890	50	1.68	83.90
Ск3*	ГОСТ 34028-2016(214-210-0502-0002)	ф 14 А500С L= 2170	24	2.62	62.93
Ск4*	ГОСТ 34028-2016(214-210-0502-0003)	ф 16 А500С L= 2450	139	3.87	537.50
Ск5*	ГОСТ 34028-2016(214-210-0502-0004)	ф 18 А500С L= 2730	66	5.45	359.92
Ск6*	ГОСТ 34028-2016(214-210-0502-0003)	ф 16 А500С L= 570	38	0.90	34.19
Ск9*	ГОСТ 34028-2016(214-210-0502-0003)	ф 16 А500С L= 730	12	1.15	13.83
1	ГОСТ 34028-2016(214-210-0502-0003)	ф 16 А500С L= 5410	116	8.54	990.50
2	ГОСТ 34028-2016(214-210-0502-0003)	ф 16 А500С L= 5025	116	7.93	920.01
3	ГОСТ 34028-2016(214-210-0502-0003)	ф 16 А500С L= 5040	116	7.95	922.76
4	ГОСТ 34028-2016(214-210-0502-0003)	ф 16 А500С L= 6280	18	9.91	178.42
5	ГОСТ 34028-2016(214-210-0502-0003)	ф 16 А500С L= 4570	18	7.21	129.83
6	ГОСТ 34028-2016(214-210-0502-0003)	ф 16 А500С L= 4250	34	6.71	228.07
7	ГОСТ 34028-2016(214-210-0502-0003)	ф 16 А500С L= 2540	34	4.01	136.31
8	ГОСТ 34028-2016(214-210-0502-0003)	ф 16 А500С L= 3290	26	5.19	135.01
9	ГОСТ 34028-2016(214-210-0502-0003)	ф 16 А500С L= 2820	30	4.45	133.53
10	ГОСТ 34028-2016(214-210-0502-0003)	ф 16 А500С L= 4530	30	7.15	214.50
11	ГОСТ 34028-2016(214-210-0502-0003)	ф 16 А500С L= 5040	26	7.95	206.83
12	ГОСТ 34028-2016(214-210-0502-0003)	ф 16 А500С L= 4830	26	7.62	198.21
13	ГОСТ 34028-2016(214-210-0502-0004)	ф 18 А500С L= 5550	36	11.09	399.12
14	ГОСТ 34028-2016(214-210-0502-0004)	ф 18 А500С L= 5180	54	10.35	558.76
15	ГОСТ 34028-2016(214-210-0502-0004)	ф 18 А500С L= 3280	8	6.55	52.42
16	ГОСТ 34028-2016(214-210-0502-0004)	ф 18 А500С L= 5200	8	10.39	83.10
17	ГОСТ 34028-2016(214-210-0502-0005)	ф 20 А500С L= 1980	38	4.88	185.55
18	ГОСТ 34028-2016(214-210-0502-0007)	ф 28 А500С L= 3450	12	16.68	200.11
19	ГОСТ 34028-2016(214-210-0502-0007)	ф 28 А500С L= 2650	12	12.81	153.71
20	ГОСТ 34028-2016(214-210-0502-0001)	ф 12 А500С L= 5130	12	4.55	54.65
21	ГОСТ 34028-2016(214-210-0502-0001)	ф 12 А500С L= 6280	50	5.58	278.77
22	ГОСТ 34028-2016(214-210-0502-0001)	ф 12 А500С L= 4570	50	4.06	202.87
23	ГОСТ 34028-2016(214-210-0502-0001)	ф 12 А500С L= пог.м.	374.47	0.89	332.46
24	ГОСТ 34028-2016(214-210-0502-0003)	ф 16 А500С L= 5210	24	8.22	197.36
25	ГОСТ 34028-2016(214-210-0502-0001)	ф 12 А500С L= 1690	24	1.50	36.01
26	ГОСТ 34028-2016(214-210-0502-0002)	ф 14 А500С L= 9460	24	11.43	274.36
27	ГОСТ 34028-2016(214-210-0502-0003)	ф 16 А500С L= пог.м.	1445.14	1.58	2280.91
28	ГОСТ 34028-2016(214-210-0502-0004)	ф 18 А500С L= пог.м.	506.31	2.00	1011.40
29	ГОСТ 34028-2016(214-210-0502-0004)	ф 18 А500С L= 3810	24	7.61	182.66
30	ГОСТ 34028-2016(214-210-0502-0004)	ф 18 А500С L= 8160	24	16.30	391.21
31	ГОСТ 34028-2016(214-210-0502-0004)	ф 18 А500С L= 3310	24	6.61	158.69
32	ГОСТ 34028-2016(214-210-0502-0001)	ф 12 А500С L= 2605	20	2.31	46.26
33	ГОСТ 34028-2016(214-210-0502-0001)	ф 12 А500С L= 1860	10	1.65	16.51
34	ГОСТ 34028-2016(214-210-0501-0005)	ф 10 А500С L= 1860	20	1.15	22.94
36	ГОСТ 34028-2016(214-210-0502-0003)	ф 16 А500С L= 3230	20	5.10	101.96
37	ГОСТ 34028-2016(214-210-0502-0003)	ф 16 А500С L= 7480	34	11.81	401.40
38	ГОСТ 34028-2016(214-210-0502-0003)	ф 16 А500С L= 8070	12	12.74	152.85
39	ГОСТ 34028-2016(214-210-0502-0006)	ф 22 А500С L= 4730	20	14.11	282.29
40	ГОСТ 34028-2016(214-210-0502-0008)	ф 28 А500С L= 10430	16	50.42	806.64
41	ГОСТ 34028-2016(214-210-0502-0002)	ф 14 А500С L= 5270	8	6.37	50.95

Позиции со "*" см. "Ведомость деталей" см. на данном листе.

Спецификация элементов

Поз.	Обозначение	Наименование	Кол.	Масса ед.кг	Примечание
42	ГОСТ 34028-2016(214-210-0502-0002)	ф 14 А500С L= пог.м.	222.00	1.21	268.27
43	ГОСТ 34028-2016(214-210-0502-0002)	ф 14 А500С L= 5600	8	6.77	54.14
44	ГОСТ 34028-2016(214-210-0502-0002)	ф 14 А500С L= 5040	8	6.09	48.72
45	ГОСТ 34028-2016(214-210-0502-0004)	ф 18 А500С L= 3210	24	6.41	153.89
Н2	ГОСТ 34028-2016(214-210-0502-0008)	ф 28 А500С L= 280	48	1.35	64.96
		Материалы:			
		Класс бетона С 20/25 (В25) W6 F100, м³			18.75
	(212-101-0901)	Класс бетона С 20/25 (В25), м³			42.50

Позиции со "*" см. "Ведомость деталей" см. на данном листе.

Ведомость деталей

Поз.	Эскиз	Поз.	Эскиз	Поз.	Эскиз
Х1	320; 170; 270; 220; по в.г. L=980	Ск3	1000; 170; 1000; по н.г. L=2170	Ск9	280; 170; 280; по н.г. L=730
Х2	270; 170; 270; 170; по в.г. L=880	Ск4	1140; 170; 1140; по н.г. L=2450	8	1140; 170; 1980; по н.г. L=3290
Х3	220; 170; 270; 120; по в.г. L=780	Ск5	1280; 170; 1280; по н.г. L=2730	25	760; 170; 760; по н.г. L=1690
Шп1	170; 100; 100; по в.г. L=370	Ск6	200; 170; 200; по н.г. L=570	31	1280; 170; 1860; по н.г. L=3310
Ск2	860; 170; 860; по н.г. L=1890	Шп1	170; 100; 100; по в.г. L=370	45	1280; 170; 1760; по н.г. L=3210

Ведомость расхода стали, кг


Марка элемента	Изделия арматурные												Всего
	Арматура класса												
	А240		А500С										
	ГОСТ 34028-2016(214-210-0101)		ГОСТ 34028-2016(214-210-0502)(214-210-0501)										
	Ф8	Итого	Ф10	Ф12	Ф14	Ф16	Ф18	Ф20	Ф22	Ф25	Ф28	Итого	
Стена См-4	1222.11	1222.11	22.94	1051.43	759.37	8113.95	3351.16	185.55	282.29	---	1225.43	14992.12	16214.23

1. Общие указания см. л. - 1.
2. Данный лист читать совместно с л. КЖ-2.1....2.7 и 5.14 ... 5.17
3. Стыки рабочей арматуры внахлестку без сварки, на скрутках из вязальной проволоки не менее 3 шт. на стык. Длина нахлеста 71d. Стыки располагать вразбежку, чтобы площадь рабочей арматуры, стыкуемой в одном сечении, не превышала 50%.
4. Расход арматуры в погонных метрах приведен с учетом нахлеста.
5. Стержни, указанные в "Ведомости деталей", должны гнуться механическим способом в холодном состоянии с радиусом гиба 3d - 5d, где d - диаметр стержня
6. Узел стыковки арматуры нахлеста, анкеровки и Фрагмент обрамления проема смотреть на листе 4


Изм.	Кол.уч.	Лист	N док.	Подп.	Дата	65П-АИП-2024-1-КЖ			
						Строительство многопрофильной больницы на 250 коек с онкологическим центром и поликлиникой на 350 посещений, по адресу: Медеуский район, г. Алматы			
						"Блок 1 Секция 1"	Стадия	Лист	Листов
							РП	5.17	
ГКП		Курал М				Спецификация стены См 4	АстанаИнжПроект		
Проверил		Кыдырбай А							
Разраб.		Ауез Б							
Н.контроль		Ешенкулова							

Формат А2


Опалубочный чертеж монолитной стены по оси Ас стена См-5 (тол.250мм)

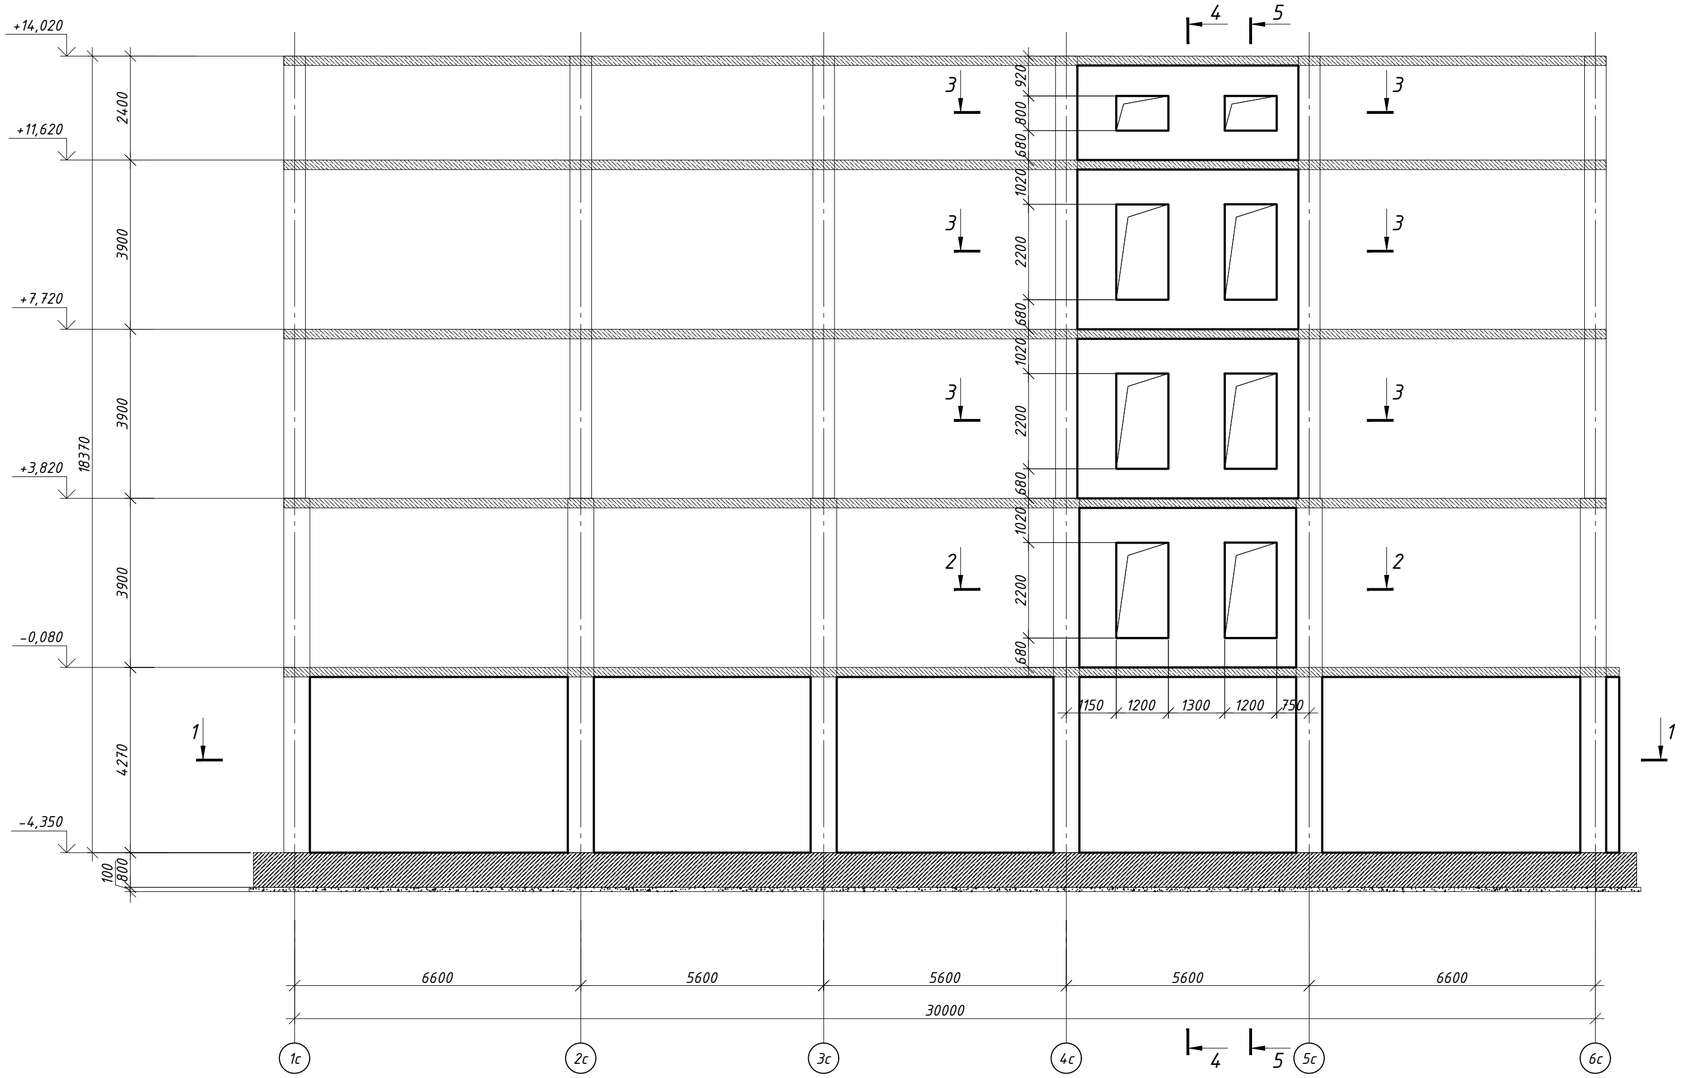


Разрез 4 - 4 (Опалубка) М1:100

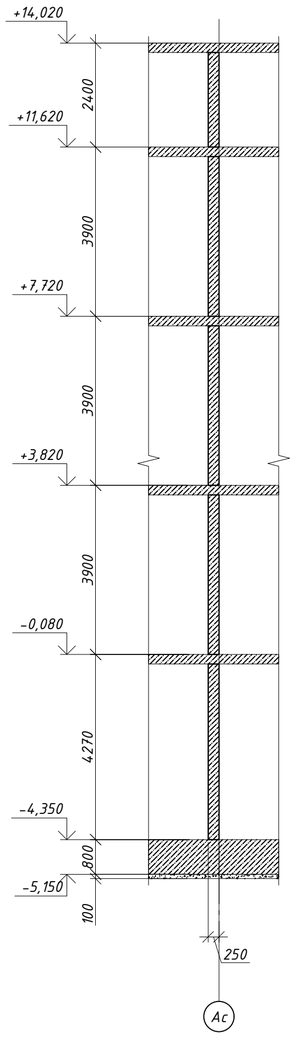


Разрез 5 - 5 (Опалубка) М1:100

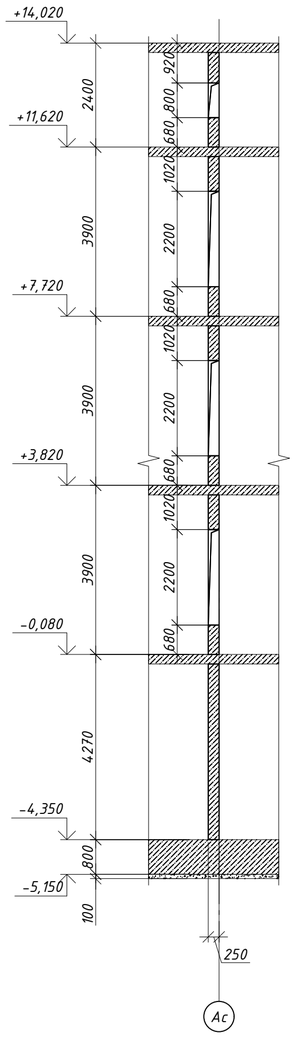


Разрез 1 - 1 (Опалубка) М1:100

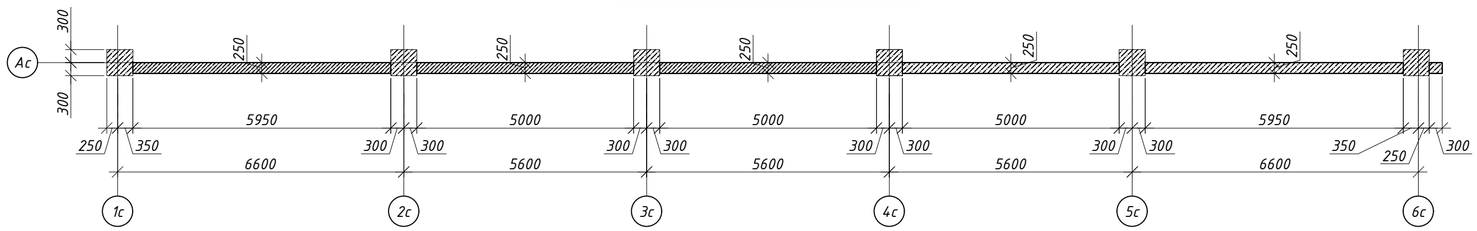

Разрез 2 - 2 (Опалубка) М1:100

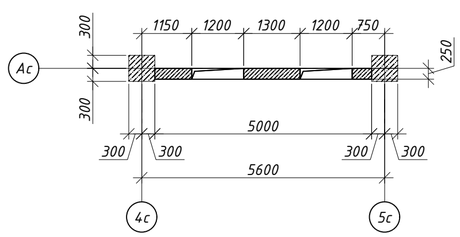

Разрез 3 - 3 (Опалубка) М1:100

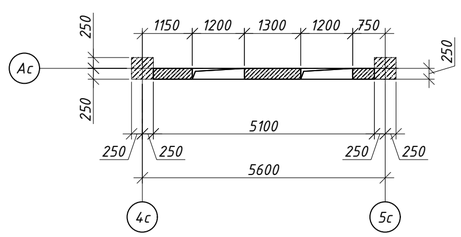

1. Общие указания см. л. - 1.
2. Данный лист читать совместно с л. КЖ-2.1...2.7 и 5.18 ... 5.20
3. Стыки рабочей арматуры внахлестку без сварки, на скрутках из вязальной проволоки не менее 3 шт. на стык. Длина нахлеста 71d. Стыки располагать враздежку, чтобы площадь рабочей арматуры, стыкуемой в одном сечении, не превышала 50%.
4. Расход арматуры в погонных метрах приведен с учетом нахлеста.
5. Стержни, указанные в "Ведомости деталей", должны гнуться механическим способом в холодном состоянии с радиусом гиба 3d - 5d, где d - диаметр стержня
6. Узел стыковки арматуры нахлеста, анкеровки и Фрагмент обрамления проема смотреть на листе 4

						65П-АИП-2024-1-КЖ	
						Строительство многопрофильной больницы на 250 коек с онкологическим центром и поликлиникой на 350 посещений, по адресу: Медеуский район, г. Алматы	
Изм.	Кол.уч	Лист	N док.	Подп.	Дата		
						"Блок 1 Секция 1"	Стадия: РП; Лист: 5.18; Листов:
ГКП		Курал М					
Проверил		Кыдырбай А				Опалубочный чертеж монолитной стены по оси Ас стена См-5 (тол.250мм)	АстанаИнжПроект
Разраб.		Ауез Б					
Н.контроль		Ешенкулова					

Формат А2

Схема расположения основное вертикальное армирование монолитной стены по оси Ac стена Ст-5 (тол.250мм)



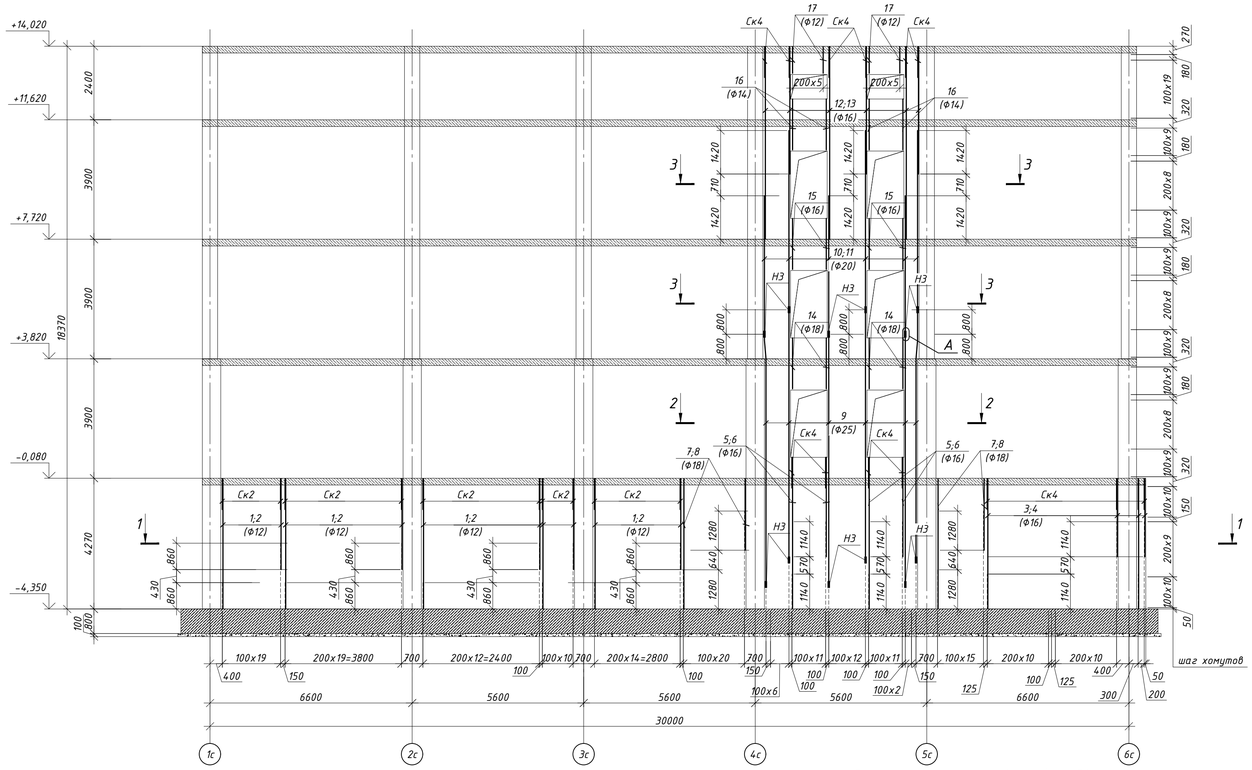



Схема расположения основное горизонтальное армирование монолитной стены по оси Ac стена Ст-5 (тол.250мм)

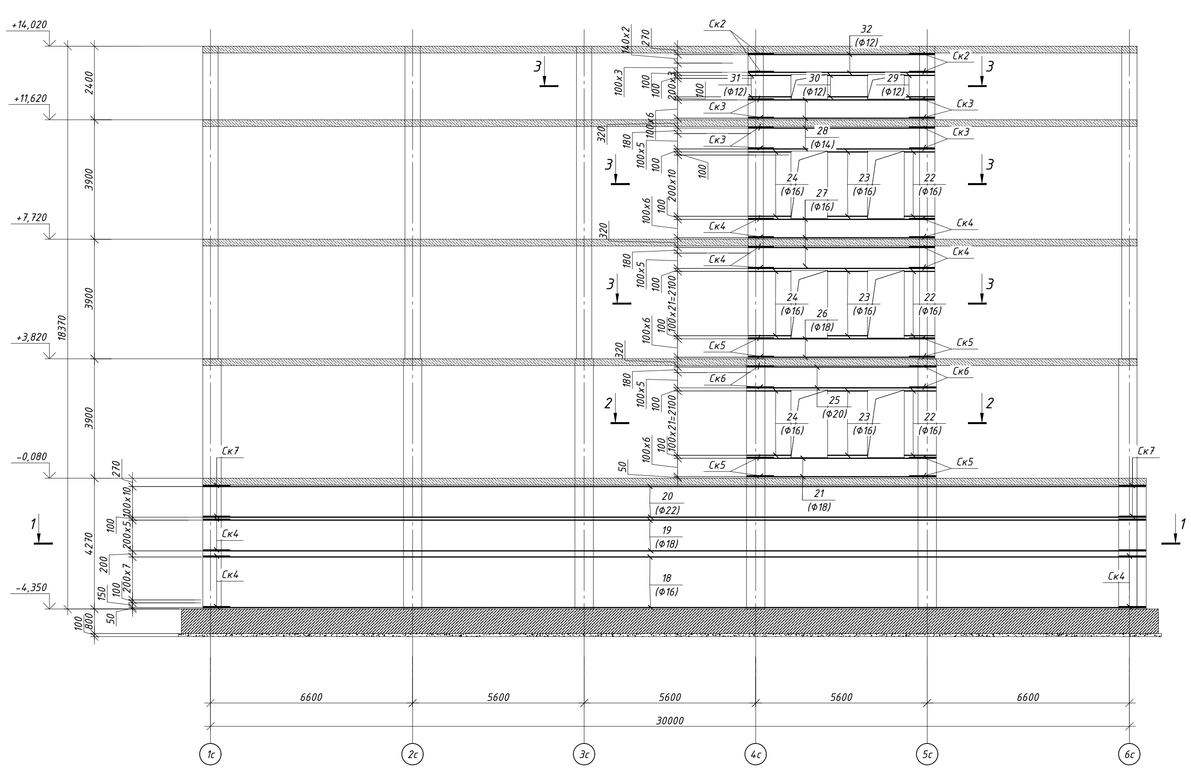


Разрез 1 - 1 (Армирование) М1:50

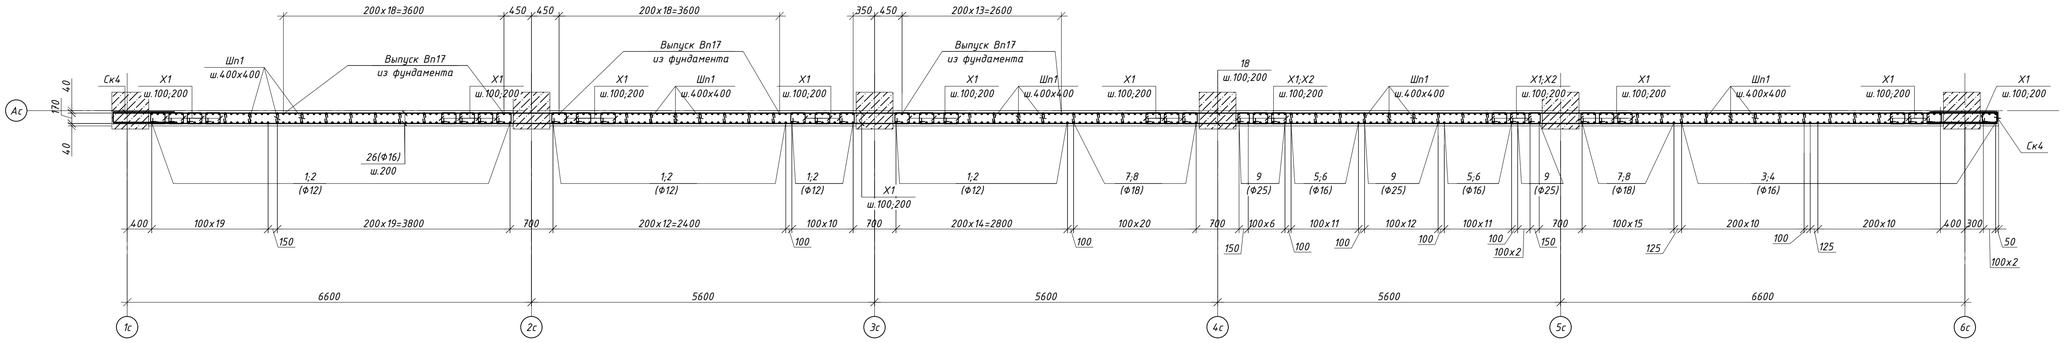


Узел Т

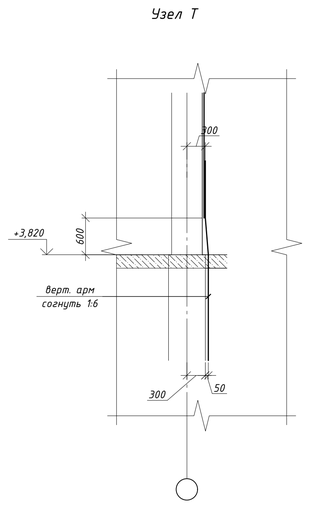

Разрез 2 - 2 (Армирование) М1:50

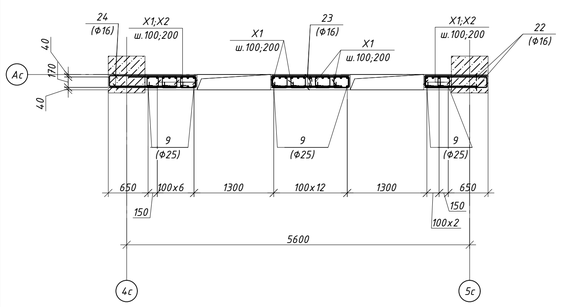

Разрез 3 - 3 (Армирование) М1:50

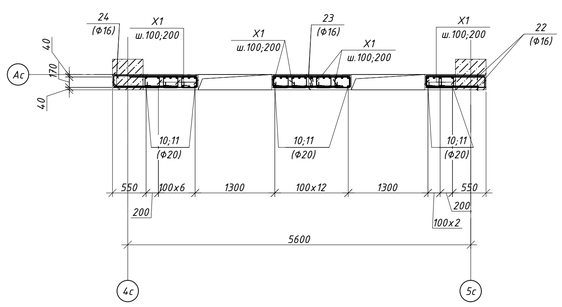


1. Общие указания см. л. - 1.
2. Данный лист читать совместно с л. КЖ-2.1...2.7 и 5.18 ... 5.20
3. Стыки рабочей арматуры внахлестку без сварки, на скрутках из вязальной проволоки не менее 3 шт. на стык. Длина нахлеста 71d. Стыки располагать враздвижку, чтобы площадь рабочей арматуры, стыкуемой в одном сечении, не превышала 50%.
4. Расход арматуры в погонных метрах приведен с учетом нахлеста.
5. Стержни, указанные в "Ведомости деталей", должны гнуться механическим способом в холодном состоянии с радиусом гиба 3d - 5d, где d - диаметр стержня
6. Узел стыковки арматуры нахлеста, анкеровки и Фрагмент обрамления проема смотреть на листе 4


							65П-АИП-2024-1-КЖ
							Строительство многопрофильной больницы на 250 коек с онкологическим центром и поликлиникой на 350 посещений, по адресу: Медеуский район, г. Алматы
Изм.	Кол.уч	Лист	N док.	Подп.	Дата		
						"Блок 1 Секция 1"	Стадия: РП; Лист: 5.19; Листов:
ГКП		Курал М				Основное армирование монолитной стены по оси Ac стена Ст-5 (тол.250мм)	АстанаИнжПроект
Проверил		Кыдырбай А					
Разраб.		Ауез Б					
Н.контроль		Ешенкулова					

Формат А1


Разрез 4 - 4 (Армирование) М 1:50

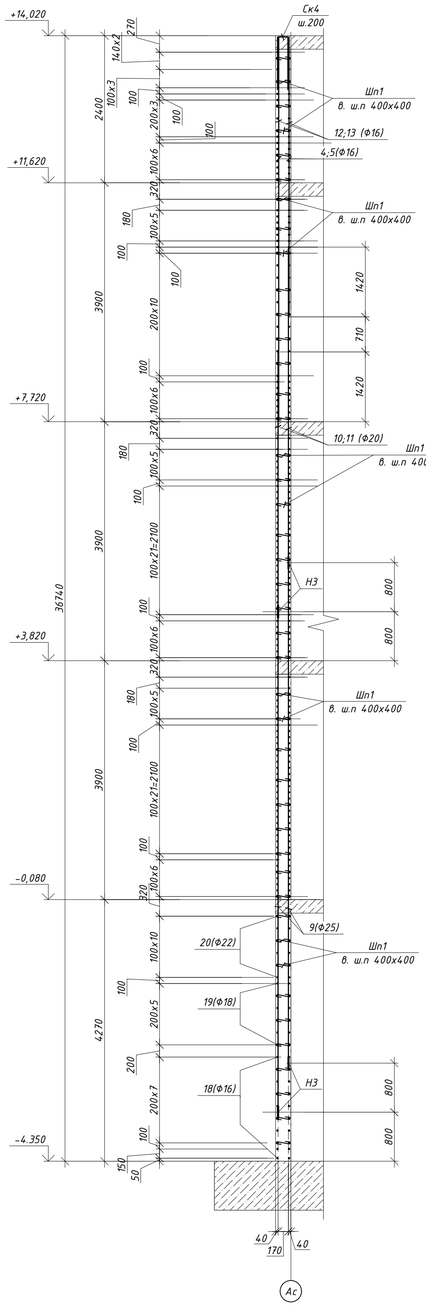


Разрез 5 - 5 (Армирование) М 1:50

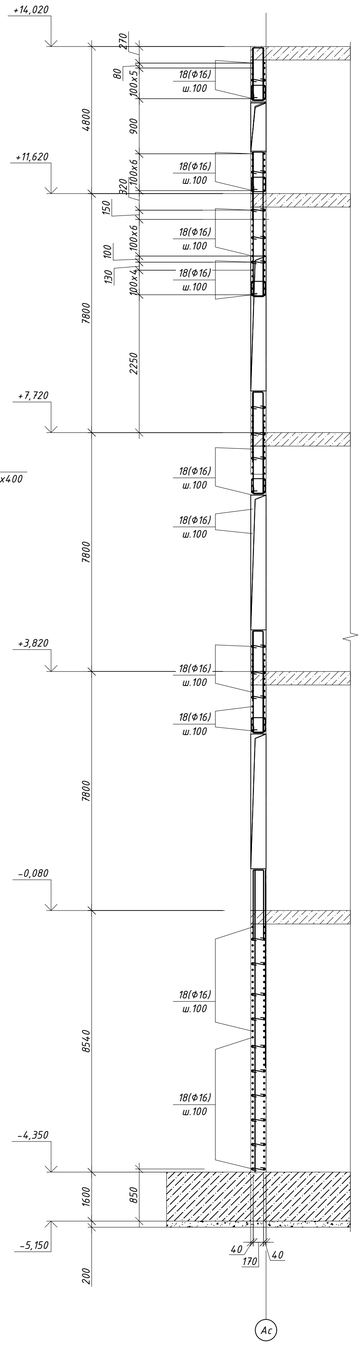



Анкеровка

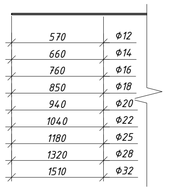


Узел стыковки вертикальной арматуры в нахлест и накладка

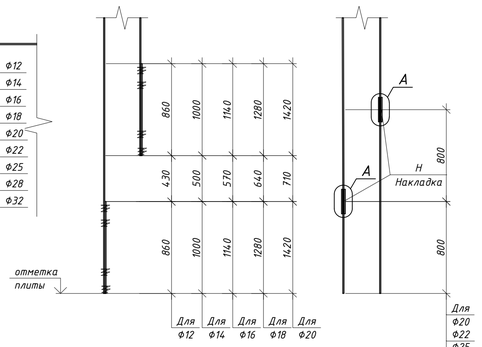


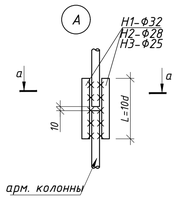

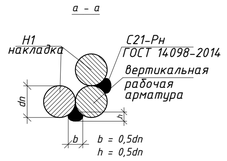


Узел стыковки Горизонтальной арматуры в нахлест

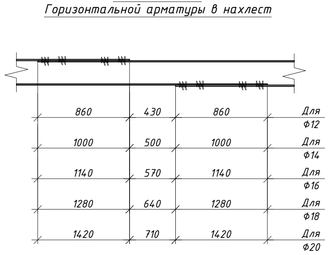

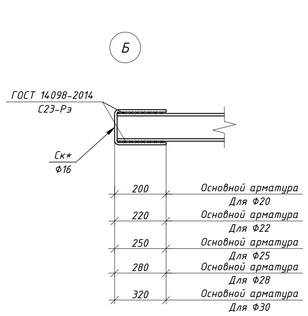

Фрагмент обрамления проема

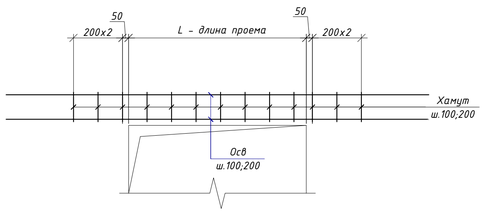

Ведомость деталей

Поз.	Эскиз	Поз.	Эскиз
Х1	320, 170, 270, 220; по в.г. L=980	14	1280, 170, 1660; по н.г. L=3110
Х2	270, 170, 270, 170; по в.г. L=880	15	1140, 170, 1660; по н.г. L=2970
Шп1	170, 100, 100; по в.г. L=370	16	1000, 170, 1660; по н.г. L=2830
Ск2 (17)	860, 170, 860; по н.г. L=1890	22	960, 170, 960; по н.г. L=2090
Ск3	1000, 170, 1000; по н.г. L=2170	23	1260, 170, 1140; по н.г. L=2570
Ск4	1140, 170, 1140; по н.г. L=2450	24	1360, 170, 1140; по н.г. L=2670
Ск5	1280, 170, 1280; по н.г. L=2730	29	860, 170, 960; по н.г. L=1990
Ск6	200, 170, 200; по н.г. L=570	30	1260, 170, 860; по н.г. L=2290
Ск7	220, 170, 220; по н.г. L=610	31	1360, 170, 860; по н.г. L=2390
8	1280, 170, 2330; по н.г. L=3780		

Таблица размеров Накладка

Марка эл-та	dн	L	вес
	мм.		кг.
Н1	32	320	2.01
Н2	28	280	1.35
Н3	25	250	0.96
Н4	22	220	0.66
Н5	20	200	0.49

Спецификация элементов

Поз.	Обозначение	Наименование	Кол.	Масса ед.кг	Примечание
		Стена Ст-4			13455.50
Х1*	ГОСТ 34028-2016(214-210-0101-0002)	Ф 8 А 240 L= 980	2073	0.39	801.61
Х2*	ГОСТ 34028-2016(214-210-0101-0002)	Ф 8 А 240 L= 880	180	0.35	62.50
Шп1*	ГОСТ 34028-2016(214-210-0101-0002)	Ф 8 А 240 L= 370	903	0.15	131.83
Ск2*	ГОСТ 34028-2016(214-210-0502-0001)	Ф 12 А500С L= 1890	170	1.68	285.25
Ск3*	ГОСТ 34028-2016(214-210-0502-0002)	Ф 14 А500С L= 2170	28	2.62	73.42
Ск4*	ГОСТ 34028-2016(214-210-0502-0003)	Ф 16 А500С L= 2450	176	3.87	680.58
Ск5*	ГОСТ 34028-2016(214-210-0502-0004)	Ф 18 А500С L= 2730	40	5.45	218.14
Ск6*	ГОСТ 34028-2016(214-210-0502-0003)	Ф 16 А500С L= 570	14	0.90	12.60
Ск7*	ГОСТ 34028-2016(214-210-0502-0003)	Ф 16 А500С L= 610	22	0.96	21.18
1	ГОСТ 34028-2016(214-210-0502-0001)	Ф 12 А500С L= 4250	79	3.77	298.08
2	ГОСТ 34028-2016(214-210-0502-0001)	Ф 12 А500С L= 2960	79	2.63	207.61
3	ГОСТ 34028-2016(214-210-0502-0003)	Ф 16 А500С L= 4250	25	6.71	167.70
4	ГОСТ 34028-2016(214-210-0502-0003)	Ф 16 А500С L= 2540	25	4.01	100.22
5	ГОСТ 34028-2016(214-210-0502-0003)	Ф 16 А500С L= 4950	24	7.81	187.51
6	ГОСТ 34028-2016(214-210-0502-0003)	Ф 16 А500С L= 3240	24	5.11	122.73
7	ГОСТ 34028-2016(214-210-0502-0004)	Ф 18 А500С L= 4250	37	8.49	314.12
8	ГОСТ 34028-2016(214-210-0502-0004)	Ф 18 А500С L= 3780	37	7.55	279.38
9	ГОСТ 34028-2016(214-210-0502-0007)	Ф 25 А500С L= 8170	50	31.48	1574.10
10	ГОСТ 34028-2016(214-210-0502-0005)	Ф 20 А500С L= 4520	25	11.15	278.67
11	ГОСТ 34028-2016(214-210-0502-0005)	Ф 20 А500С L= 5850	25	14.43	360.67
12	ГОСТ 34028-2016(214-210-0502-0002)	Ф 14 А500С L= 6280	15	7.59	113.83
13	ГОСТ 34028-2016(214-210-0502-0002)	Ф 14 А500С L= 4150	15	5.01	75.22
14	ГОСТ 34028-2016(214-210-0502-0004)	Ф 18 А500С L= 3110	48	6.21	298.20
15	ГОСТ 34028-2016(214-210-0502-0003)	Ф 16 А500С L= 2970	48	4.69	225.01
16	ГОСТ 34028-2016(214-210-0502-0002)	Ф 14 А500С L= 2830	48	3.42	164.15
17	ГОСТ 34028-2016(214-210-0502-0001)	Ф 12 А500С L= 1890	24	1.68	40.27
18	ГОСТ 34028-2016(214-210-0502-0003)	Ф 16 А500С L= пог.м.	645.96	1.58	1019.54
19	ГОСТ 34028-2016(214-210-0502-0004)	Ф 18 А500С L= пог.м.	387.58	2.00	774.21
20	ГОСТ 34028-2016(214-210-0502-0006)	Ф 22 А500С L= пог.м.	710.56	2.98	2120.33
21	ГОСТ 34028-2016(214-210-0502-0004)	Ф 18 А500С L= 6160	14	12.31	172.27
22	ГОСТ 34028-2016(214-210-0502-0003)	Ф 16 А500С L= 2090	112	3.30	369.46
23	ГОСТ 34028-2016(214-210-0502-0003)	Ф 16 А500С L= 2570	112	4.06	454.31
24	ГОСТ 34028-2016(214-210-0502-0003)	Ф 16 А500С L= 2670	112	4.21	471.99
25	ГОСТ 34028-2016(214-210-0502-0005)	Ф 20 А500С L= 6160	14	15.19	212.68
26	ГОСТ 34028-2016(214-210-0502-0004)	Ф 18 А500С L= 6060	14	12.11	169.47
27	ГОСТ 34028-2016(214-210-0502-0003)	Ф 16 А500С L= 6060	28	9.56	267.81
28	ГОСТ 34028-2016(214-210-0502-0002)	Ф 14 А500С L= 6060	28	7.32	205.04
29	ГОСТ 34028-2016(214-210-0502-0001)	Ф 12 А500С L= 1990	10	1.77	17.67
30	ГОСТ 34028-2016(214-210-0502-0001)	Ф 12 А500С L= 2290	10	2.03	20.33
31	ГОСТ 34028-2016(214-210-0502-0001)	Ф 12 А500С L= 2390	10	2.12	21.22
32	ГОСТ 34028-2016(214-210-0502-0001)	Ф 12 А500С L= 6060	12	5.38	64.56
		Материалы:			
		Класс бетона С 20/25 (В25) W6 F100, м³			27.54
	(212-101-0901)	Класс бетона С 20/25 (В25), м³			12.46

Позиции со "*" см. "Ведомость деталей" см. на данном листе.

Ведомость расхода стали, кг

Марка элемента	Изделия арматурные												Всего
	Арматура класса												
	А240		А500С										
	ГОСТ 34028-2016(214-210-0101)		ГОСТ 34028-2016(214-210-0502)										
	Ф8	Итого	Ф10	Ф12	Ф14	Ф16	Ф18	Ф20	Ф22	Ф25	Ф28	Итого	
Стена Ст-5	995.95	995.95	---	954.99	631.67	4100.63	2225.80	852.03	2120.33	1574.10	---	12459.55	13455.50

1. Общие указания см. л. - 1.
2. Данный лист читать совместно с л. КЖ-2.1...2.7 и 5.18 ... 5.20
3. Стыки рабочей арматуры внахлестку без сварки, на скрутках из вязальной проволоки не менее 3 шт. на стык. Длина нахлеста 71d. Стыки располагать вразбежку, чтобы площадь рабочей арматуры, стыкуемой в одном сечении, не превышала 50%.
4. Расход арматуры в погонных метрах приведен с учетом нахлеста.
5. Стержни, указанные в "Ведомости деталей", должны гнуться механическим способом в холодном состоянии с радиусом гиба 3d - 5d, где d - диаметр стержня
6. Узел стыковки арматуры нахлеста, анкеровки и Фрагмент обрамления проема смотреть на листе 4

						65П-АИП-2024-1-КЖ	
						Строительство многопрофильной больницы на 250 коек с онкологическим центром и поликлиникой на 350 посещений, по адресу: Медеуский район, г. Алматы	
Изм.	Кол.уч	Лист	N док.	Подп.	Дата		
						"Блок 1 Секция 1"	Стадия: РП; Лист: 5.20; Листов:
ГКП		Курал М					
Проверил		Кыдырбай А				Спецификация монолитной стены по оси Ас стена Ст-5 (тол.250мм)	АстанаИнжПроект
Разраб.		Ауез Б					
Н.контроль		Ешенкулова					Формат А1