


Схема расположения опалубочный чертеж монолитной стены по оси Бс стена См-6 (тол.250мм)

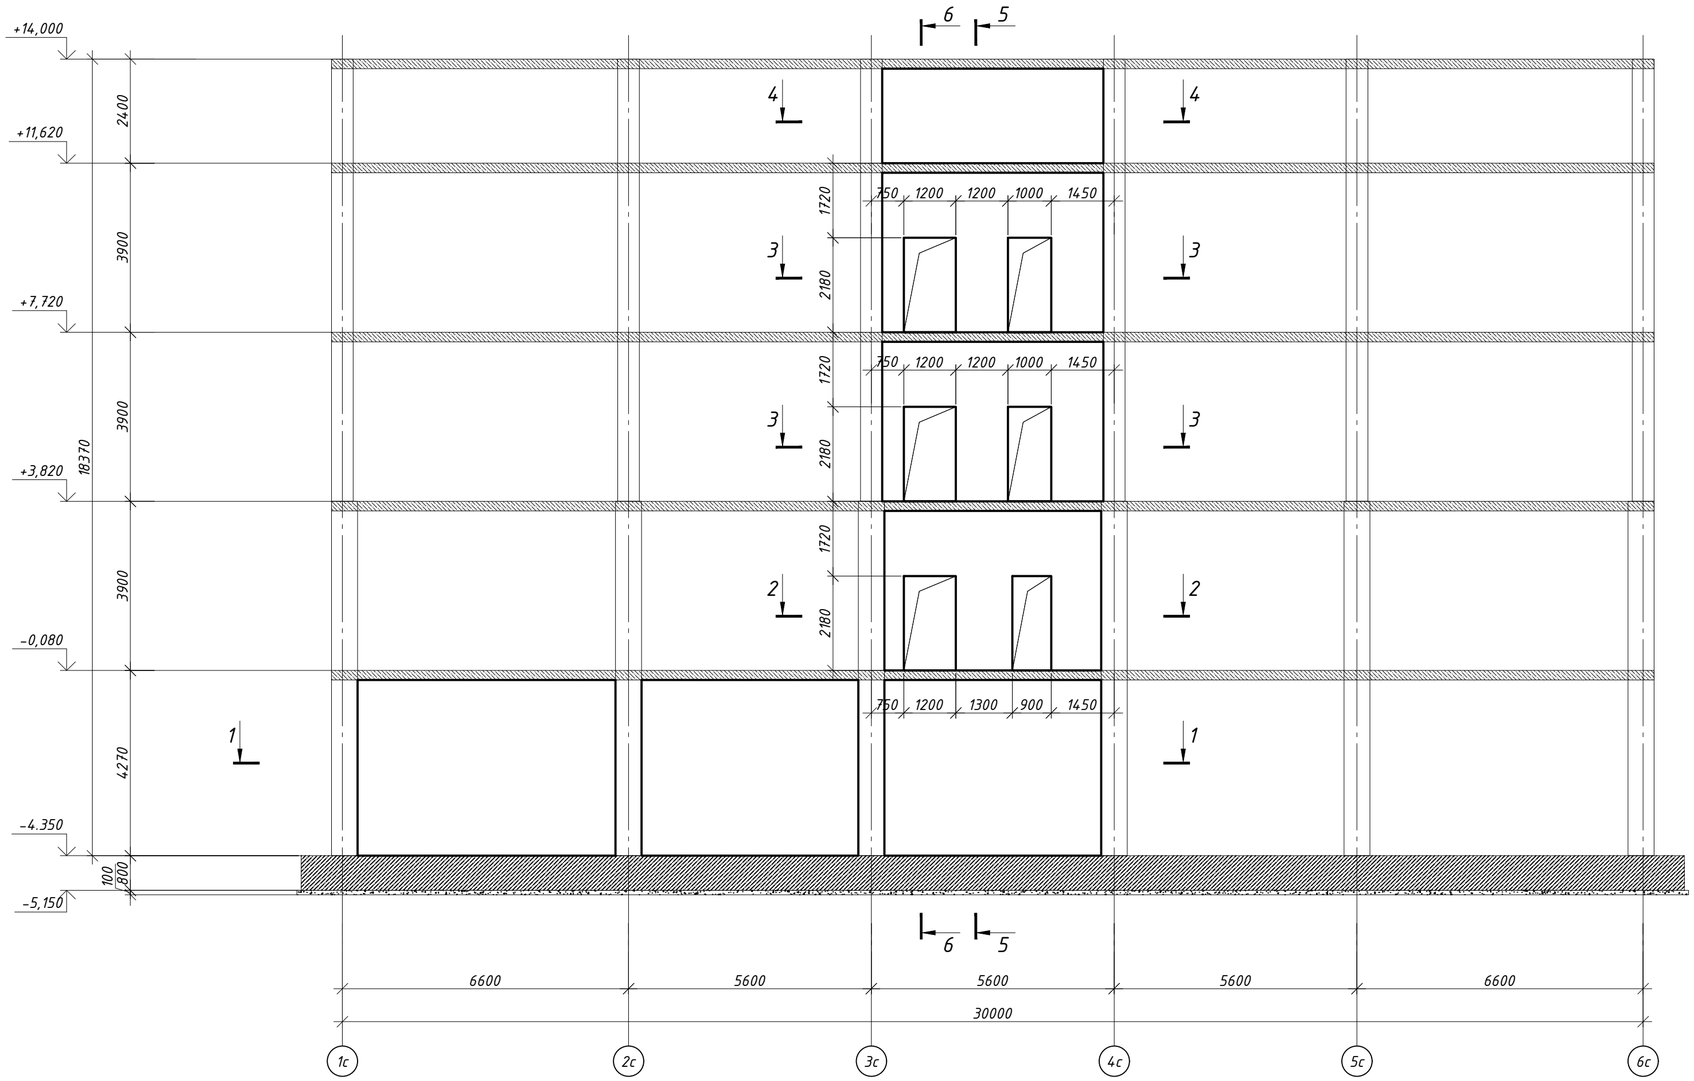


Разрез 5 - 5 (Опалубка) М1:100

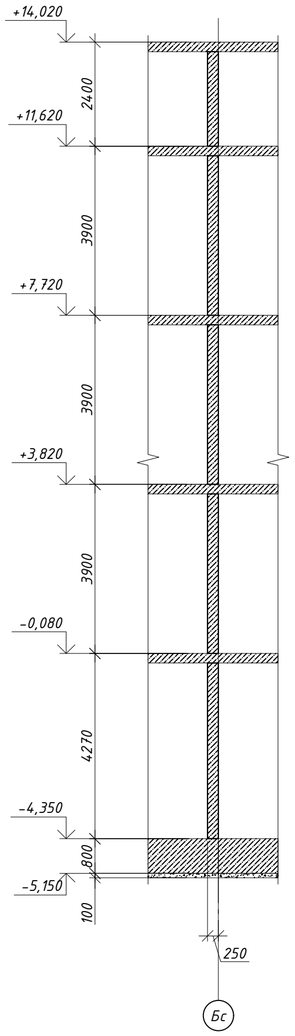


Разрез 6 - 6 (Опалубка) М1:100

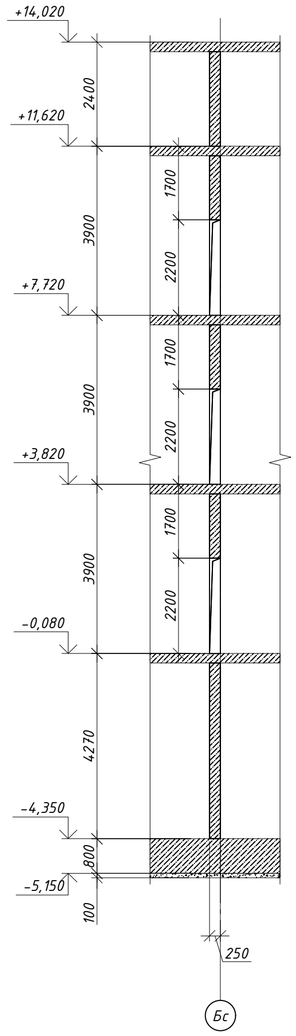


Разрез 1 - 1 (Опалубка) М1:100

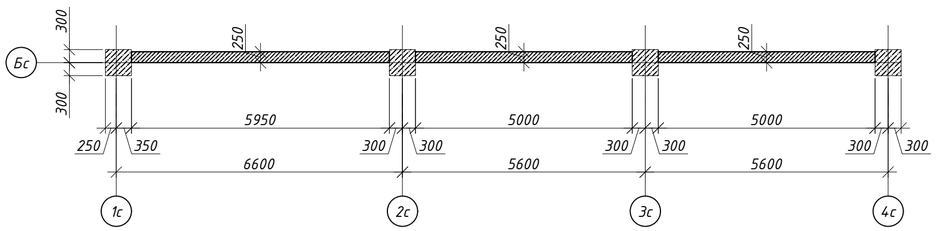


Разрез 2 - 2 (Опалубка) М1:100

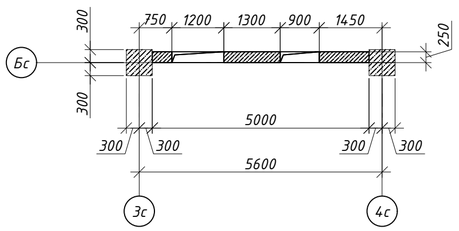

Разрез 3 - 3 (Опалубка) М1:100

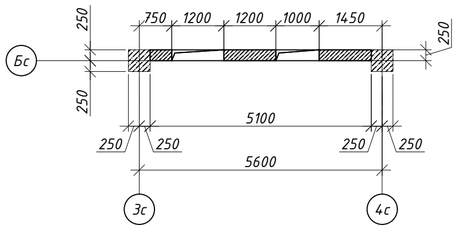

Разрез 4 - 4 (Опалубка) М1:100

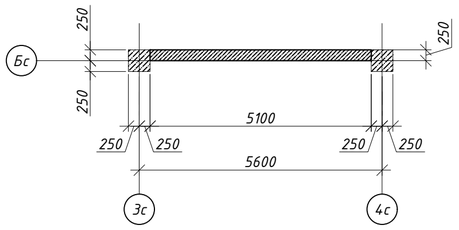

1. Общие указания см. л. - 1.
2. Данный лист читать совместно с л. КЖ-5.22 ... 5.24
3. Стыки рабочей арматуры внахлестку без сварки, на скрутках из вязальной проволоки не менее 3 шт. на стык. Длина нахлеста 71d. Стыки располагать вразбежку, чтобы площадь рабочей арматуры, стыкуемой в одном сечении, не превышала 50%.
4. Расход арматуры в погонных метрах приведен с учетом нахлеста.
5. Стержни, указанные в "Ведомости деталей", должны гнуться механическим способом в холодном состоянии с радиусом гиба 3d - 5d, где d - диаметр стержня
6. Узел стыковки арматуры нахлеста и анкеровки смотреть на листе 5.1

						65П-АИП-2024-1-КЖ
						Строительство многопрофильной больницы на 250 коек с онкологическим центром и поликлиникой на 350 посещений, по адресу: Медеуский район, г. Алматы
Изм.	Кол.уч	Лист	N док.	Подп.	Дата	
						"Блок 1 Секция 1"
ГКП		Курал М				Стадия: РП; Лист: 5.22; Листов:
Проверил		Кыдырбай А				
Разраб.		Ауез Б				Схема расположения опалубочный чертеж монолитной стены по оси Бс стена См-6 (тол.250мм)
Н.контроль		Ешенкулова				АстанаИнжПроект

Формат А2

Схема расположения основное вертикальное армирование монолитной стены по оси Бс стена См-6 (тол.250мм)



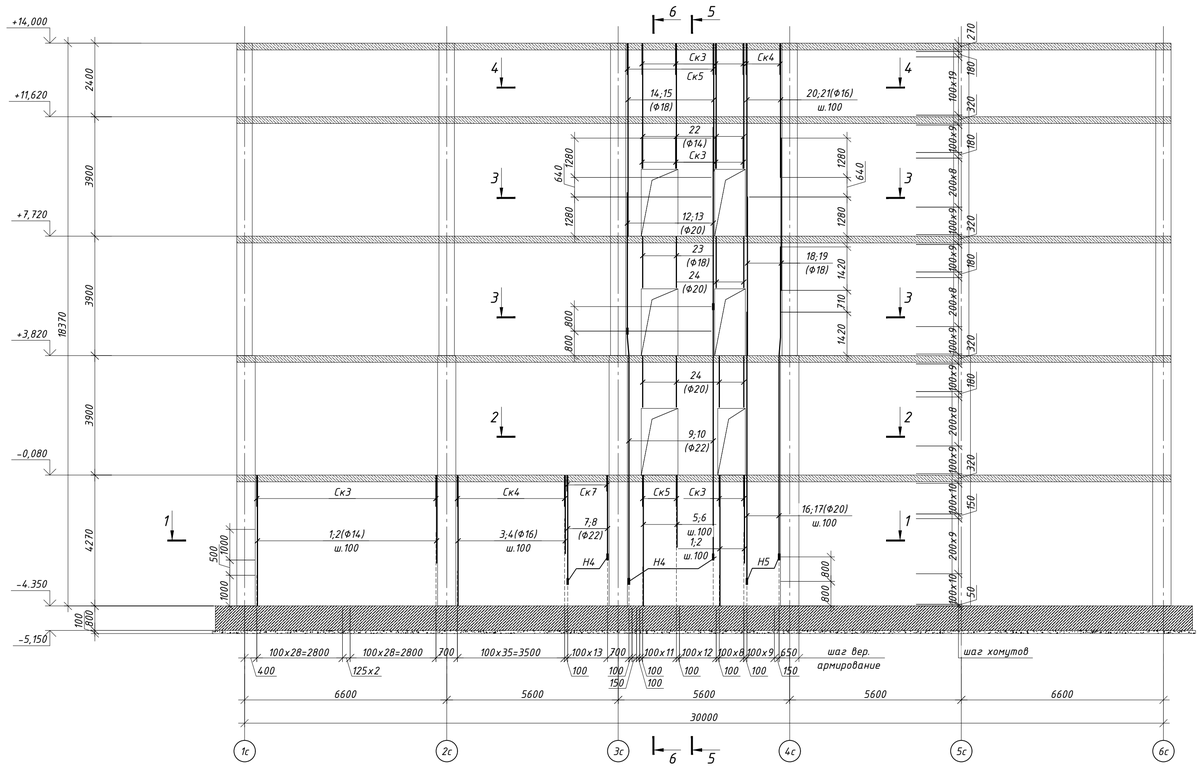



Схема расположения основное горизонтальное армирование монолитной стены по оси Бс стена См-6 (тол.250мм)

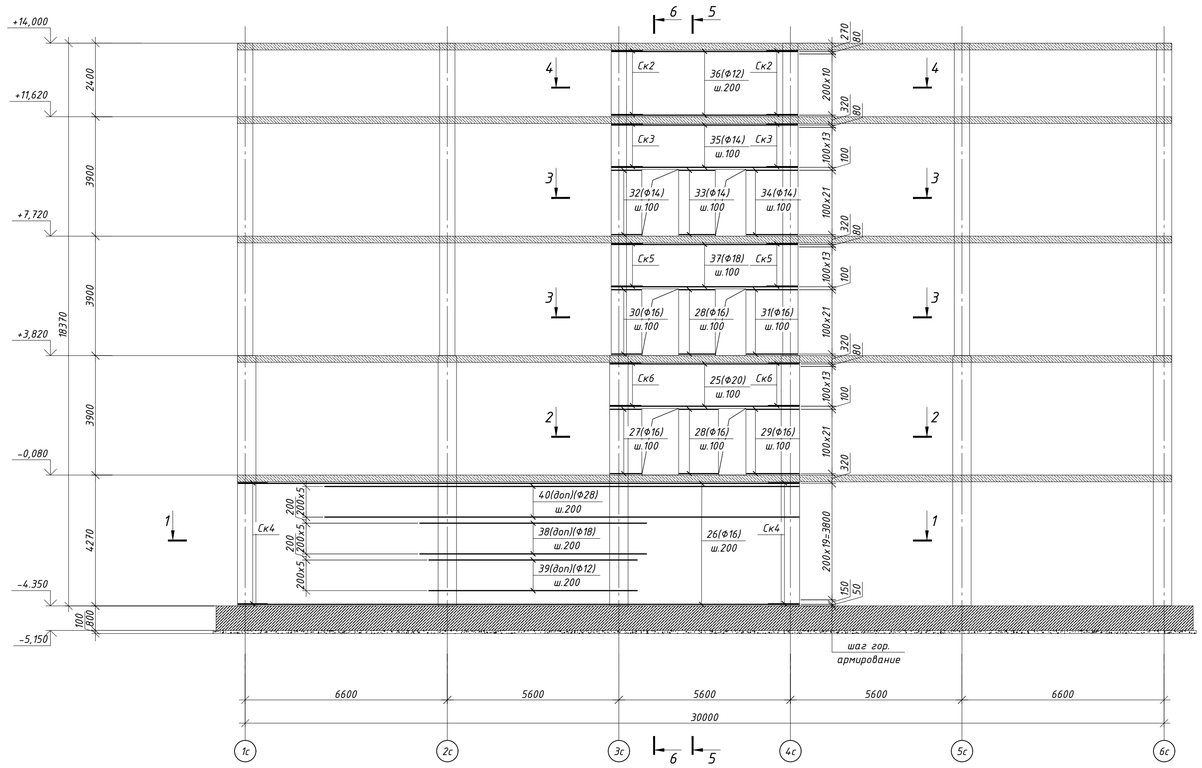


Разрез 1 - 1 (Армирование) М1:50

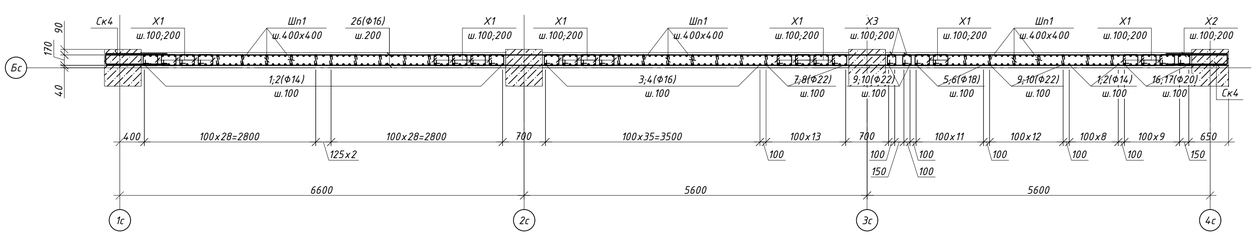


Разрез 2 - 2 (Армирование) М1:50

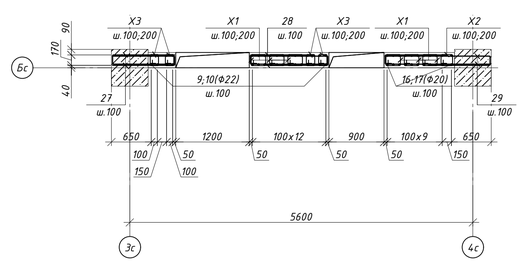


Разрез 3 - 3 (Армирование) М1:50

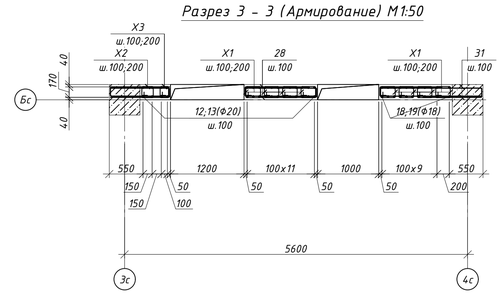


Разрез 4 - 4 (Армирование) М1:50

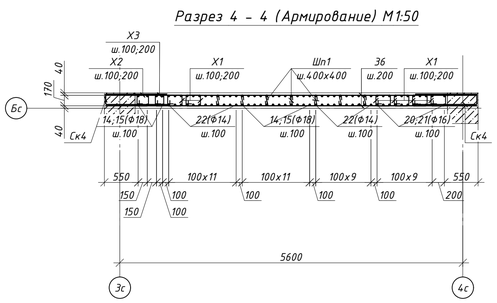


Фрагмент обрамления проема

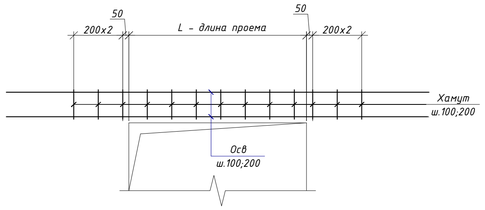

Анкеровка

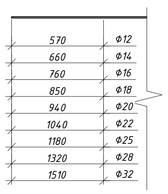

Узел Т

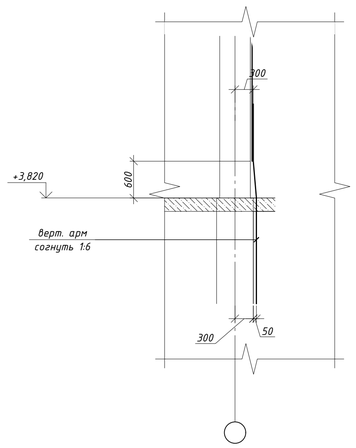


1. Общие указания см. л. - 1.
2. Данный лист читать совместно с л. КЖ-5.22 ... 5.24
3. Стыки рабочей арматуры внахлестку без сварки, на скрутках из вязальной проволоки не менее 3 шт. на стык. Длина нахлеста 71d. Стыки располагать вразбежку, чтобы площадь рабочей арматуры, стыкуемой в одном сечении, не превышала 50%.
4. Расход арматуры в погонных метрах приведен с учетом нахлеста.
5. Стержни, указанные в "Ведомости деталей", должны гнуться механическим способом в холодном состоянии с радиусом гиба 3d - 5d, где d - диаметр стержня
6. Узел стыковки арматуры нахлеста и анкеровки смотреть на листе 5.1


						65П-АИП-2024-1-КЖ	
						Строительство многопрофильной больницы на 250 коек с онкологическим центром и поликлиникой на 350 посещений, по адресу: Медеуский район, г. Алматы	
Изм.	Кол.уч	Лист	N док	Подп.	Дата		
						"Блок 1 Секция 1"	Стадия: РП; Лист: 5.23; Листов:
ГКП		Курал М				Схема расположения основное армирование монолитной стены по оси Бс стена См-6 (тол.250мм)	АстанаИнжПроект
Проверил		Кыдырбай А					
Разраб.		Ауез Б					
Н.контроль		Ешенкулова					

Формат А1

Разрез 5 – 5 (Армирование) М1:50

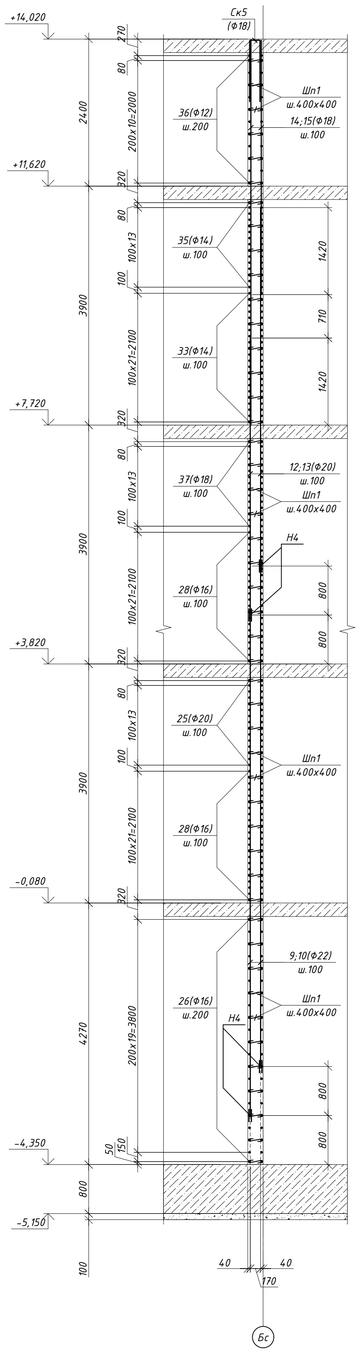

Разрез 6 – 6 (Армироование) М1:50

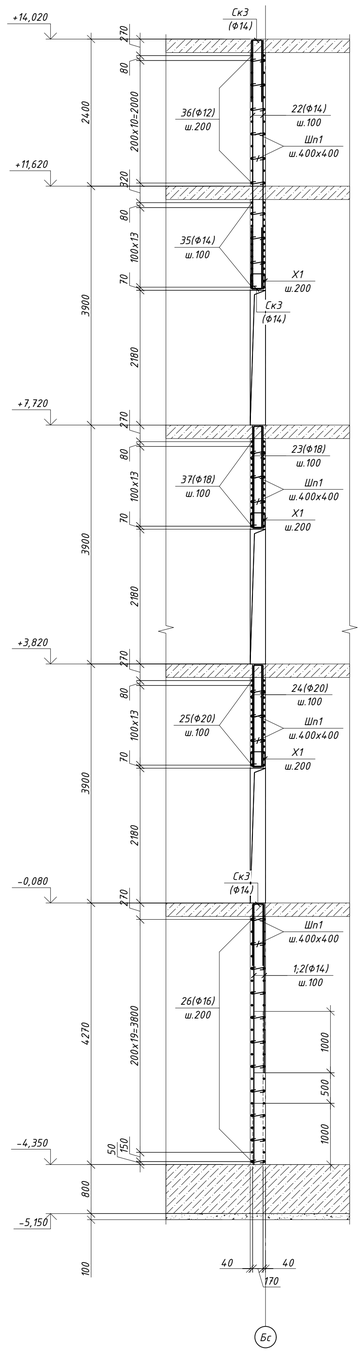

Ведомость деталей

Поз.	Эскиз	Поз.	Эскиз	Поз.	Эскиз
Шп1	170, 100, 100; по в.г. L=370	Ск5	1280, 170, 1280; по н.г. L=2730	29*	1710, 170, 1140; по н.г. L=3020
Х1	320, 170, 270, 220; по в.г. L=980	Ск6	200, 170, 200; по н.г. L=570	30*	960, 170, 960; по н.г. L=2090
Х2	270, 170, 270, 170; по в.г. L=880	Ск7	220, 170, 220; по н.г. L=610	31*	1660, 170, 1140; по н.г. L=2970
Х3	220, 170, 270, 120; по в.г. L=780	23*	1660, 170, 1280; по н.г. L=3110	32*	960, 170, 960; по н.г. L=2090
Ск2	860, 170, 860; по н.г. L=1890	24*	1660, 170, 1420; по н.г. L=3250	33*	1160, 170, 1000; по н.г. L=2330
Ск3	1000, 170, 1000; по н.г. L=2170	27*	1010, 170, 1010; по н.г. L=2190	34*	1660, 170, 1000; по н.г. L=2830
Ск4	1140, 170, 1140; по н.г. L=2450	28*	1160, 170, 1140; по н.г. L=2470		

Ведомость расхода стали, кг


Марка элемента	Изделия арматурные												Всего
	Арматура класса												
	А240			А500С									
	ГОСТ 34028-2016(214-210-0101)			ГОСТ 34028-2016(214-210-0502)									
	Ф6	Ф8	Итого	Ф12	Ф14	Ф16	Ф18	Ф20	Ф22	Ф25	Ф28	Итого	
По оси Бс стена Ск-6	---	805.30	805.30	231.08	1796.57	3246.27	1746.35	1936.94	1235.27	---	947.40	11139.88	11945.18


Спецификация элементов


Поз.	Обозначение	Наименование	Кол.	Масса ед.кг	Примечание
		По оси Бс стена Ск-6			11945.18
Шп1	ГОСТ 34028-2016(214-210-0101-0082)	Ф 8 А500С L= 370	735	0.15	107.31
Х1	ГОСТ 34028-2016(214-210-0101-0002)	Ф 8 А500С L= 980	1394	0.39	539.05
Х2	ГОСТ 34028-2016(214-210-0101-0002)	Ф 8 А500С L= 880	136	0.35	47.22
Х3	ГОСТ 34028-2016(214-210-0101-0002)	Ф 8 А500С L= 780	363	0.31	111.72
Ск2	ГОСТ 34028-2016(214-210-0502-0001)	Ф 12 А500С L= 1890	24	1.68	40.27
Ск3	ГОСТ 34028-2016(214-210-0502-0002)	Ф 14 А500С L= 2170	150	2.62	393.34
Ск4	ГОСТ 34028-2016(214-210-0502-0003)	Ф 16 А500С L= 2450	89	3.87	344.16
Ск5	ГОСТ 34028-2016(214-210-0502-0004)	Ф 18 А500С L= 2730	59	5.45	321.75
Ск6	ГОСТ 34028-2016(214-210-0502-0005)	Ф 20 А500С L= 570	30	1.41	42.17
Ск7	ГОСТ 34028-2016(214-210-0502-0006)	Ф 22 А500С L= 610	14	1.82	25.48
1	ГОСТ 34028-2016(214-210-0502-0002)	Ф 14 А500С L= 4250	69	5.14	354.37
2	ГОСТ 34028-2016(214-210-0502-0002)	Ф 14 А500С L= 2850	69	3.44	237.63
3	ГОСТ 34028-2016(214-210-0502-000)	Ф 16 А500С L= 4250	36	6.71	241.49
4	ГОСТ 34028-2016(214-210-0502-0003)	Ф 16 А500С L= 2540	36	4.01	144.32
5	ГОСТ 34028-2016(214-210-0502-0004)	Ф 18 А500С L= 4250	12	8.49	101.88
6	ГОСТ 34028-2016(214-210-0502-0004)	Ф 18 А500С L= 2330	12	4.65	55.85
7	ГОСТ 34028-2016(214-210-0502-0006)	Ф 22 А500С L= 3450	14	10.29	144.13
8	ГОСТ 34028-2016(214-210-0502-0006)	Ф 22 А500С L= 2650	14	7.91	110.71
9	ГОСТ 34028-2016(214-210-0502-0006)	Ф 22 А500С L= 8170	17	24.38	414.45
10	ГОСТ 34028-2016(214-210-0502-0006)	Ф 22 А500С L= 8170	17	24.38	414.45
Н4	ГОСТ 34028-2016(214-210-0502-0006)	Ф 22 А500С L= 220	192	0.66	126.05
12	ГОСТ 34028-2016(214-210-0502-0005)	Ф 20 А500С L= 4250	17	10.48	178.18
13	ГОСТ 34028-2016(214-210-0502-0005)	Ф 20 А500С L= 5850	17	14.43	245.26
14	ГОСТ 34028-2016(214-210-0502-0004)	Ф 18 А500С L= 6280	17	12.54	213.26
15	ГОСТ 34028-2016(214-210-0502-0004)	Ф 18 А500С L= 4150	17	8.29	140.93
16	ГОСТ 34028-2016(214-210-0502-0005)	Ф 20 А500С L= 8790	11	21.68	238.45
17	ГОСТ 34028-2016(214-210-0502-0005)	Ф 20 А500С L= 10120	11	24.96	274.53
Н5	ГОСТ 34028-2016(214-210-0502-0005)	Ф 20 А500С L= 200	44	0.49	21.70
18	ГОСТ 34028-2016(214-210-0502-0004)	Ф 18 А500С L= 5180	11	10.35	113.82
19	ГОСТ 34028-2016(214-210-0502-0004)	Ф 18 А500С L= 4970	11	9.93	109.21
20	ГОСТ 34028-2016(214-210-0502-0003)	Ф 16 А500С L= 6280	11	9.91	109.03
21	ГОСТ 34028-2016(214-210-0502-0003)	Ф 16 А500С L= 4360	11	6.88	75.70
22	ГОСТ 34028-2016(214-210-0502-0002)	Ф 14 А500С L= 4060	42	4.91	206.06
23*	ГОСТ 34028-2016(214-210-0502-0004)	Ф 18 А500С L= 3110	24	6.21	149.10
24*	ГОСТ 34028-2016(214-210-0502-0005)	Ф 20 А500С L= 3250	60	8.01	480.90
25	ГОСТ 34028-2016(214-210-0502-0005)	Ф 20 А500С L= 6160	30	15.19	455.74
26	ГОСТ 34028-2016(214-210-0502-0003)	Ф 16 А500С L= пог.м.	808	1.58	1275.30
27*	ГОСТ 34028-2016(214-210-0502-0003)	Ф 16 А500С L= 2190	44	3.46	152.09
28*	ГОСТ 34028-2016(214-210-0502-0003)	Ф 16 А500С L= 2470	88	3.90	343.07
29*	ГОСТ 34028-2016(214-210-0502-0003)	Ф 16 А500С L= 3020	44	4.77	209.73
30*	ГОСТ 34028-2016(214-210-0502-0003)	Ф 16 А500С L= 2090	44	3.30	145.14
31*	ГОСТ 34028-2016(214-210-0502-0003)	Ф 16 А500С L= 2970	44	4.69	206.26
32*	ГОСТ 34028-2016(214-210-0502-0002)	Ф 14 А500С L= 2090	44	2.53	111.13
33*	ГОСТ 34028-2016(214-210-0502-0002)	Ф 14 А500С L= 2330	44	2.82	123.89
34*	ГОСТ 34028-2016(214-210-0502-0002)	Ф 14 А500С L= 2830	44	3.42	150.47
35	ГОСТ 34028-2016(214-210-0502-0002)	Ф 14 А500С L= 6060	30	7.32	219.69
36	ГОСТ 34028-2016(214-210-0502-0001)	Ф 12 А500С L= 6060	22	5.38	118.36
37	ГОСТ 34028-2016(214-210-0502-0004)	Ф 18 А500С L= 6060	30	12.11	363.16
38	ГОСТ 34028-2016(214-210-0502-0004)	Ф 18 А500С L= 7400	12	14.78	177.39
39	ГОСТ 34028-2016(214-210-0502-0001)	Ф 12 А500С L= 6800	12	6.04	72.45
40	ГОСТ 34028-2016(214-210-0502-0009)	Ф 28 А500С L= пог.м.	196	4.83	947.40
		Материалы:			
		Класс бетона С 20/25 (В25), м³			29.37

Позиции со "*" см. "Ведомость деталей" см. на данном листе.


Узел стыковки вертикальной арматуры в нахлест и накладка

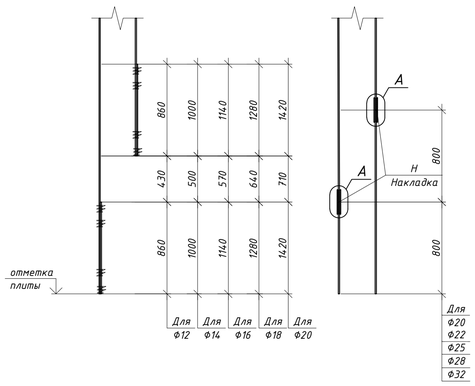

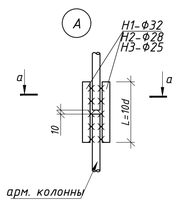

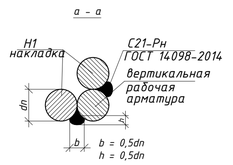

Узел стыковки горизонтальной арматуры в нахлест

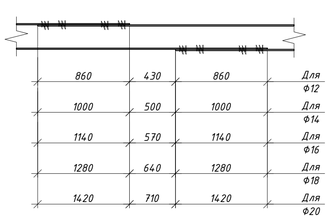

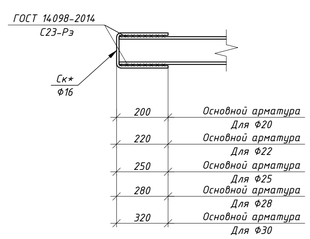



Таблица размеров Накладка

Марка эл-та	dн	L	вес
	мм.		кг.
Н1	32	320	2.01
Н2	28	280	1.35
Н3	25	250	0.96
Н4	22	220	0.66
Н5	20	200	0.49


1. Общие указания см. л. – 1.
2. Данный лист читать совместно с л. КЖ-5.22 ... 5.24
3. Стыки рабочей арматуры внахлестку без сварки, на скрутках из вязальной проволоки не менее 3 шт. на стык. Длина нахлеста 71d. Стыки располагать вразбежку, чтобы площадь рабочей арматуры, стыкуемой в одном сечении, не превышала 50%.
4. Расход арматуры в погонных метрах приведен с учетом нахлеста.
5. Стержни, указанные в "Ведомости деталей", должны гнуться механическим способом в холодном состоянии с радиусом гиба 3d – 5d, где d – диаметр стержня
6. Узел стыковки арматуры нахлеста и анкеровки смотреть на листе 5.1

						65П-АИП-2024-1-КЖ	
						Строительство многопрофильной больницы на 250 коек с онкологическим центром и поликлиникой на 350 посещений, по адресу: Медеуский район, г. Алматы	
Изм.	Кол.уч.	Лист	N док.	Подп.	Дата		
						"Блок 1 Секция 1"	Стадия: РП; Лист: 5.24; Листов:
ГКП		Курал М					
Проверил		Кыдырбай А				Спецификация монолитной стены по оси Бс стена Ск-6 (тол.250мм)	АстанаИнжПроект
Разраб.		Ауез Б					
Н.контроль		Ешенкулова					Формат А1


Схема расположения опалубочный чертеж монолитной стены по оси Гс стена См-7 (тол.250мм)

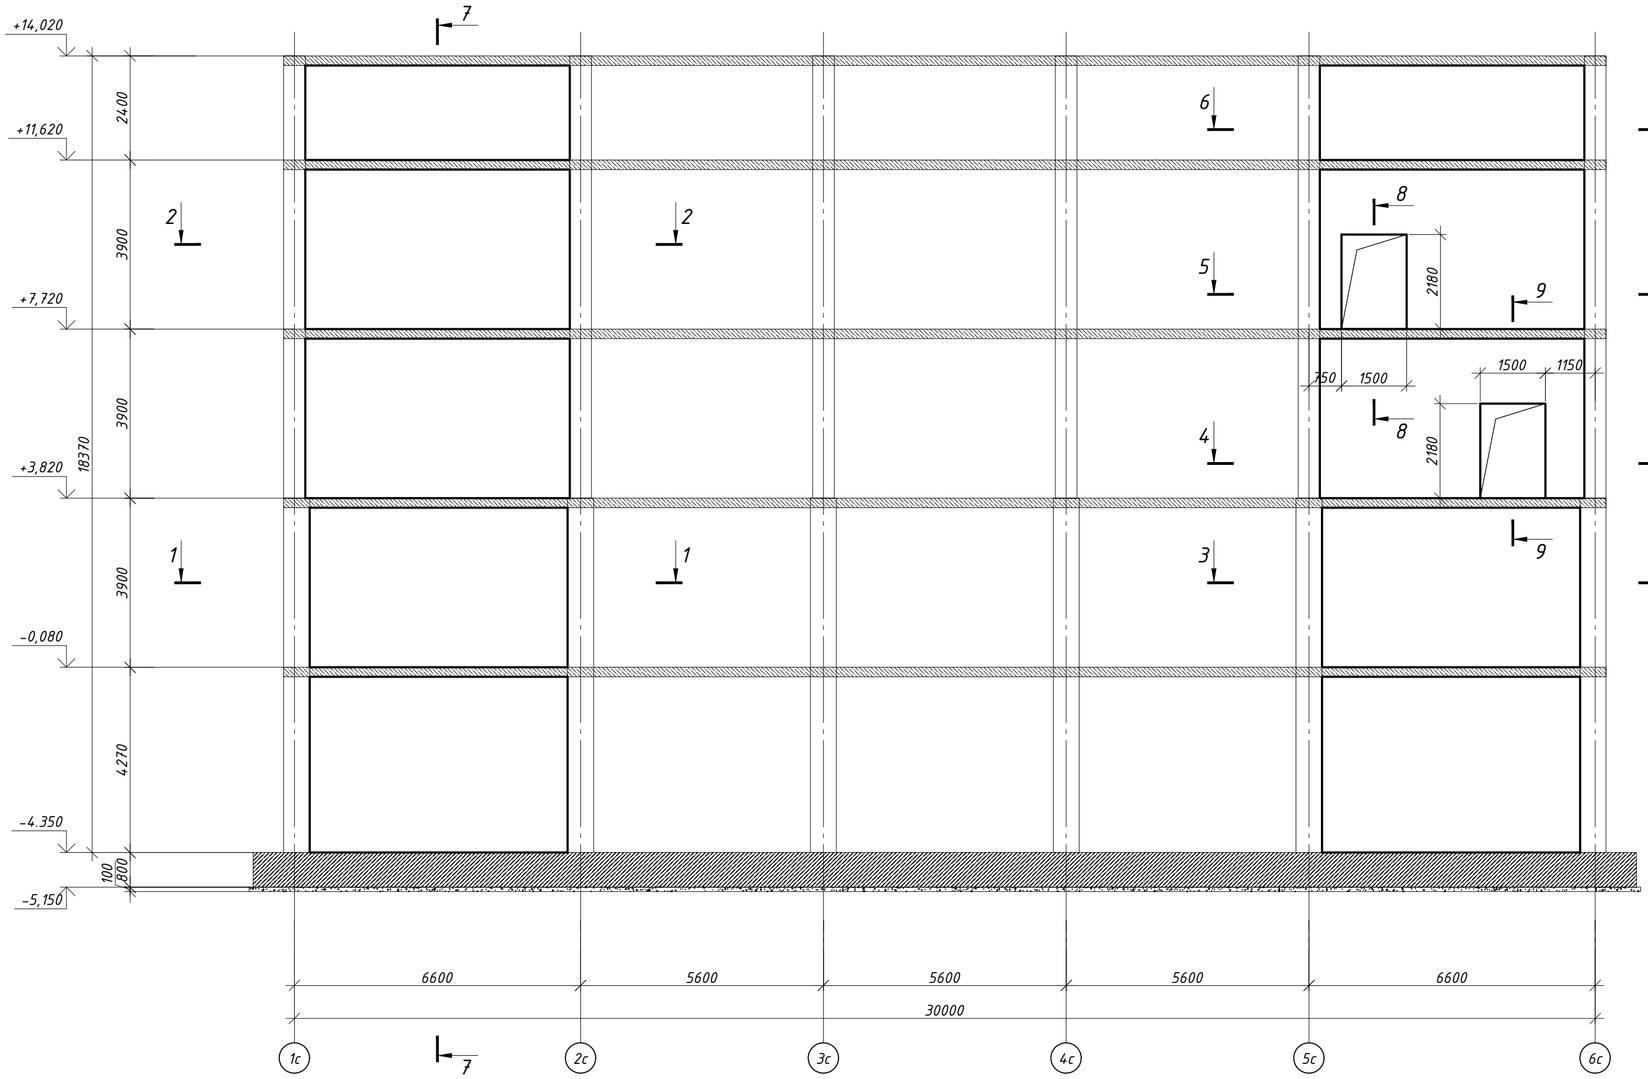


Разрез 7 – 7 (Опалубка) М1:100

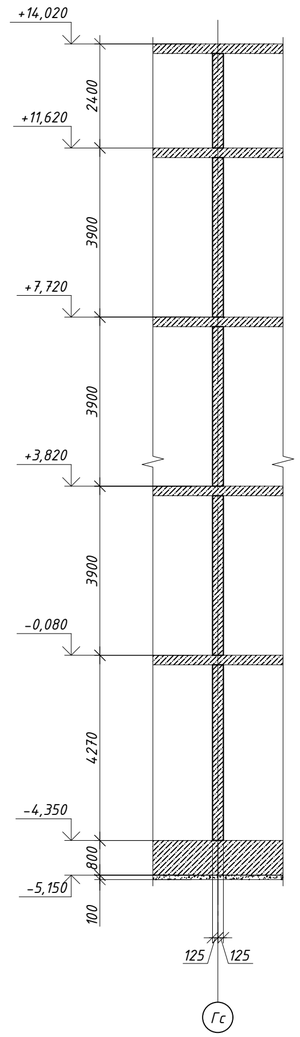


Разрез 8 – 8 (Опалубка) М1:100

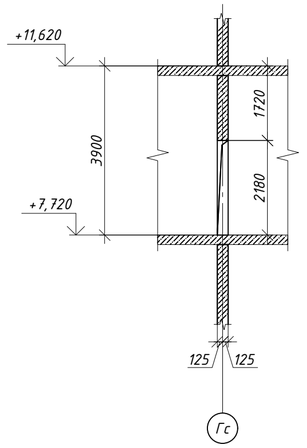


Разрез 9 – 9 (Опалубка) М1:100

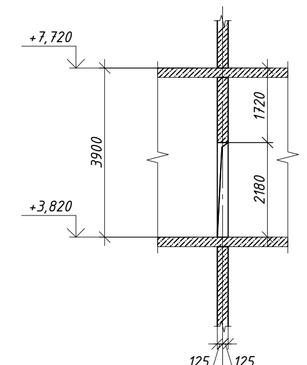


Анкеровка

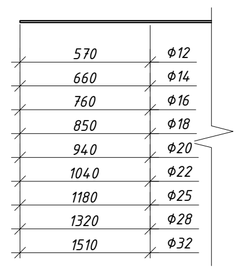


Разрез 1 – 1 (Опалубка) М1:100

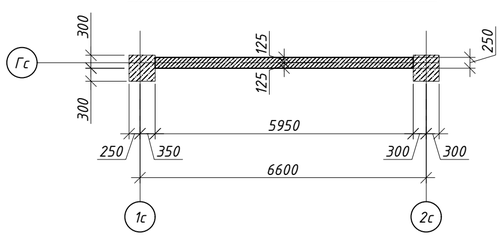


Разрез 3 – 3 (Опалубка) М1:100

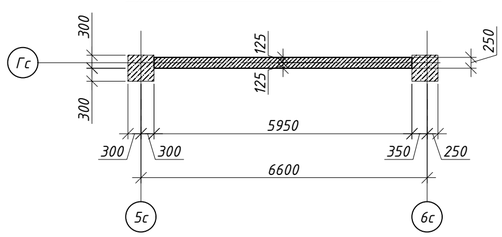


Разрез 4 – 4 (Опалубка) М1:100

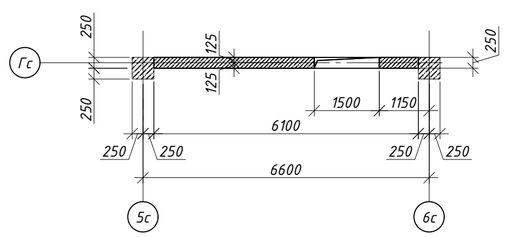


Разрез 2 – 2 (Опалубка) М1:100

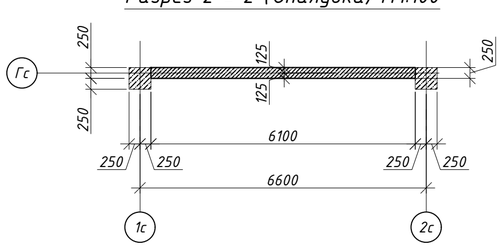

Разрез 6 – 6 (Опалубка) М1:100

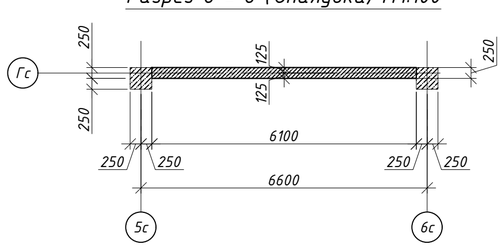

Разрез 5 – 5 (Опалубка) М1:100

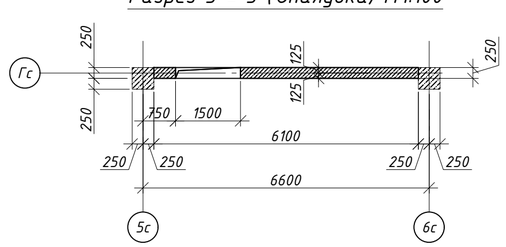

1. Общие указания см. л. – 1.
2. Данный лист читать совместно с л. КЖ-5.25 ... 5.27
3. Стыки рабочей арматуры внахлестку без сварки, на скрутках из вязальной проволоки не менее 3 шт. на стык. Длина нахлеста 71d. Стыки располагать вразбежку, чтобы площадь рабочей арматуры, стыкуемой в одном сечении, не превышала 50%.
4. Расход арматуры в погонных метрах приведен с учетом нахлеста.
5. Стержни, указанные в "Ведомости деталей", должны гнуться механическим способом в холодном состоянии с радиусом гиба 3d – 5d, где d – диаметр стержня
6. Узел стыковки арматуры нахлеста и анкеровки смотреть на листе 5.1

						65П-АИП-2024-1-КЖ	
						Строительство многопрофильной больницы на 250 коек с онкологическим центром и поликлиникой на 350 посещений, по адресу: Медеуский район, г. Алматы	
Изм.	Кол.уч	Лист	N док.	Подп.	Дата		
						"Блок 1 Секция 1"	Стадия: РП; Лист: 5.25; Листов:
ГКП		Курал М				Схема расположения опалубочный чертеж монолитной стены по оси Гс стена См-7 (тол.250мм)	АстанаИнжПроект
Проверил		Кыдырбай А					
Разраб.		Ауез Б					
Н.контроль		Ешенкулова					

Формат А2

Схема расположения основное вертикальное армирование монолитной стены по оси Гс стена См-7 (тол.250мм)



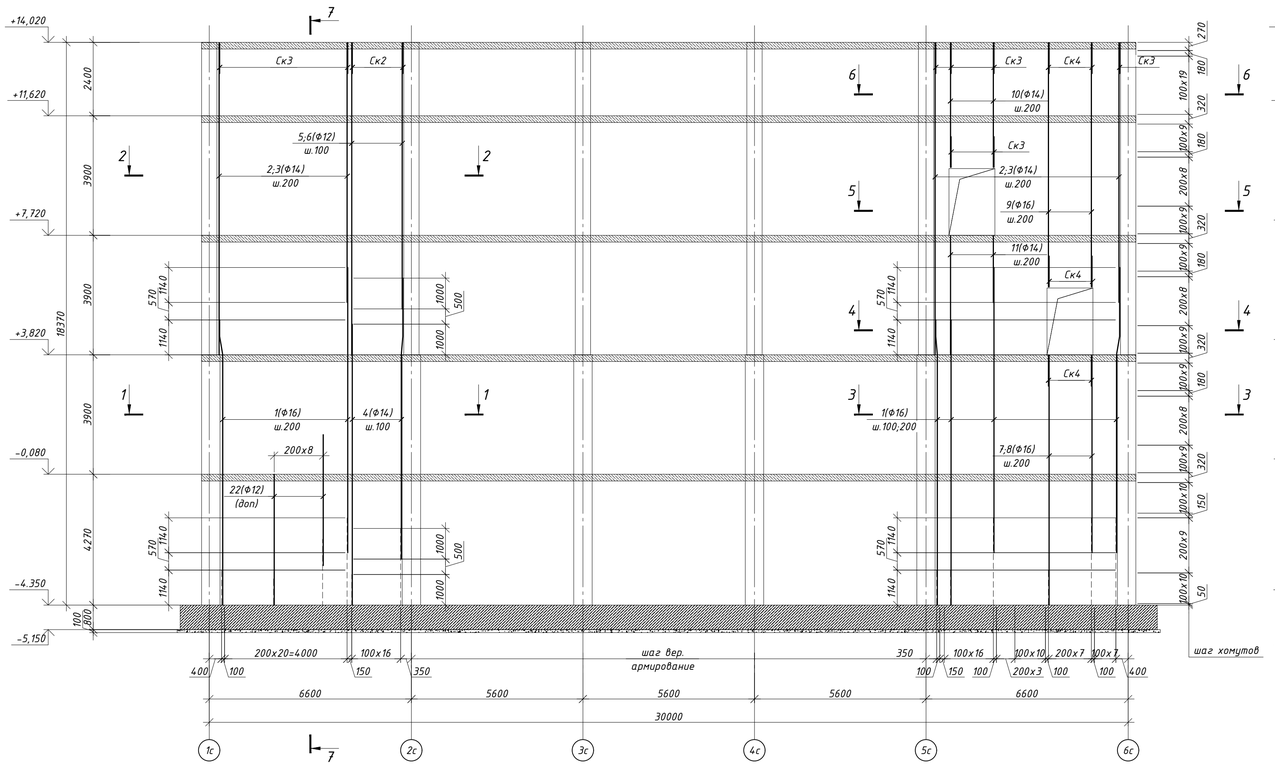


Схема расположения основное горизонтальное армирование монолитной стены по оси Гс стена См-7 (тол.250мм)

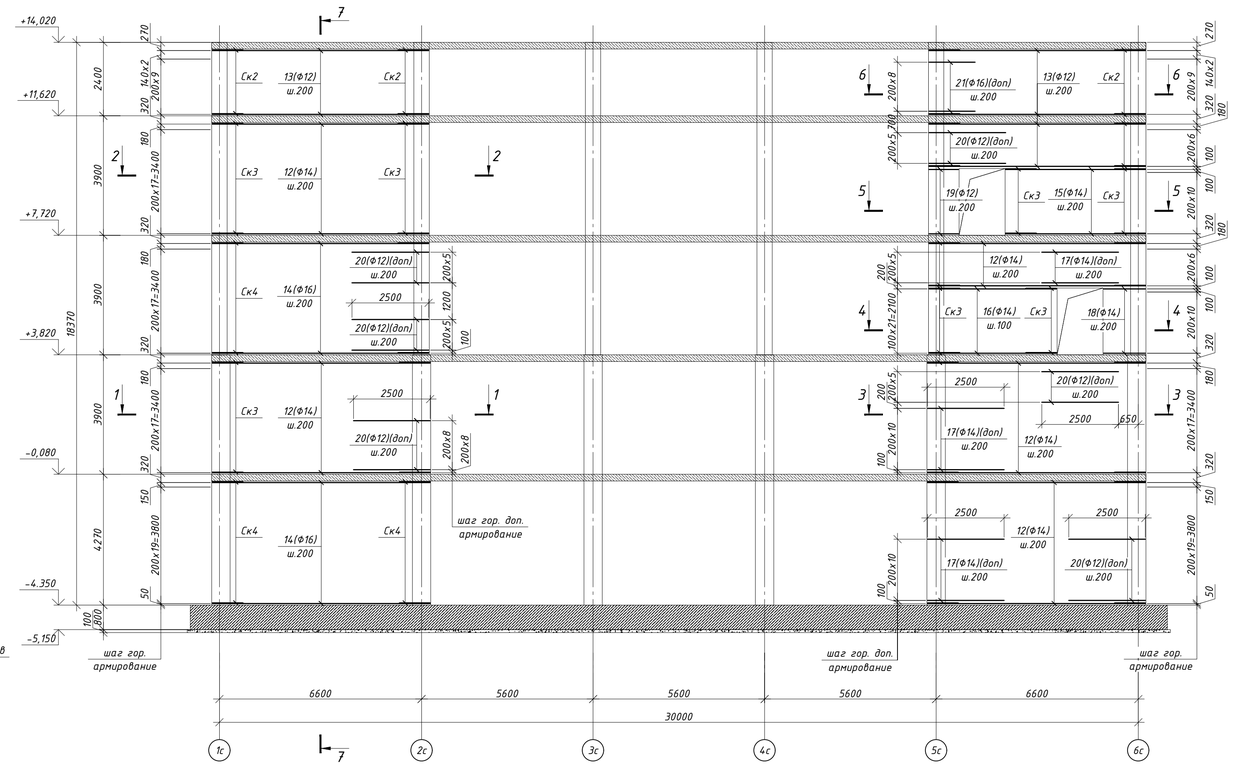


Узел стыковки вертикальной арматуры в нахлест


Разрез 1 - 1 (Армирование) М1:50

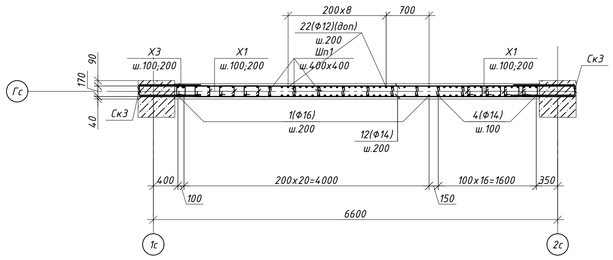


Разрез 4 - 4 (Армирование) М1:50

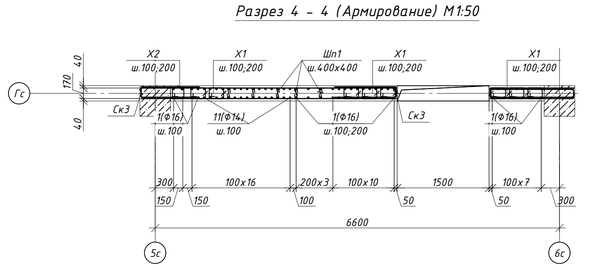


Разрез 8 - 8 (Армирование) М1:50

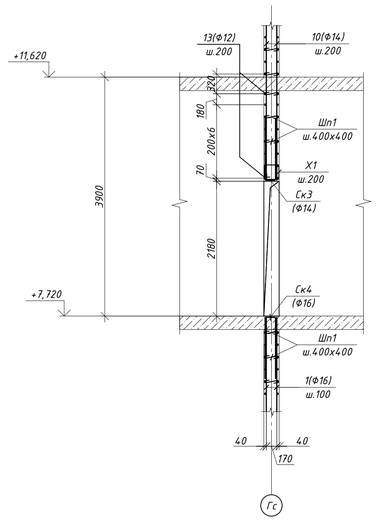


Разрез 9 - 9 (Армирование) М1:50

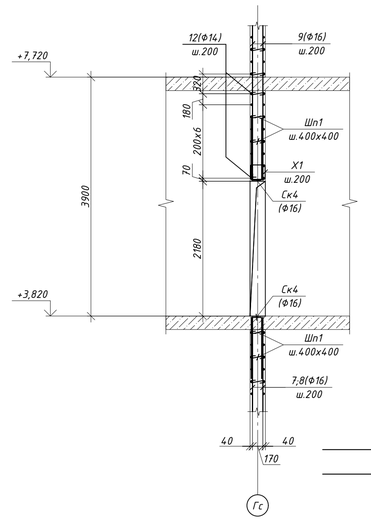


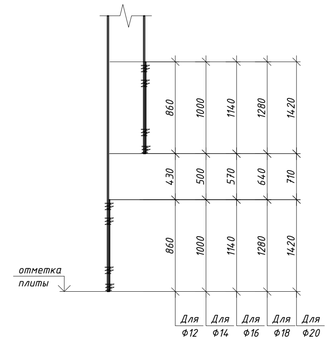


Фрагмент обрамления проема

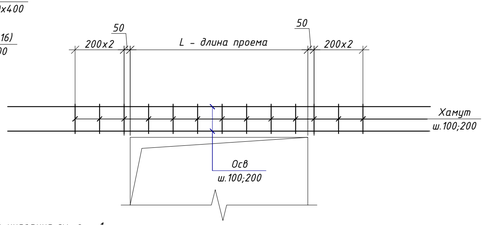


Разрез 2 - 2 (Армирование) М1:50

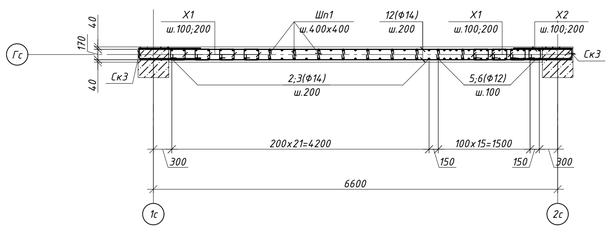


Разрез 5 - 5 (Армирование) М1:50

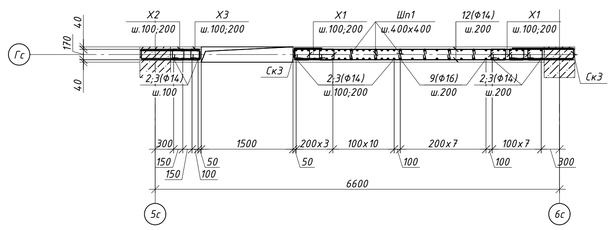


Узел стыковки Горизонтальной арматуры в нахлест

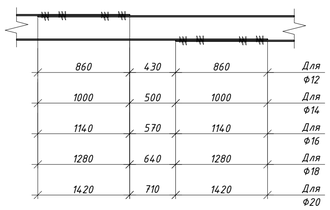

Разрез 3 - 3 (Армирование) М1:50

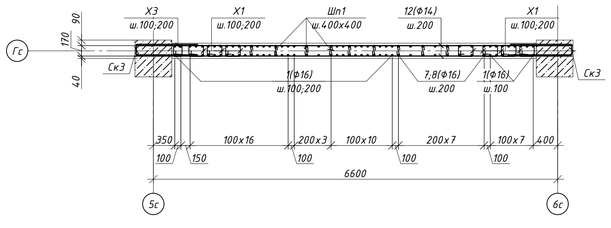


Разрез 6 - 6 (Армирование) М1:50

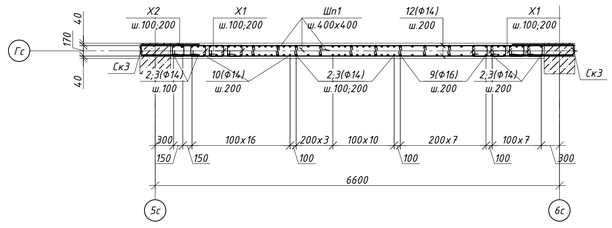

1. Общие указания см. л. - 1.
2. Данный лист читать совместно с л. КЖ-5.25 ... 5.27
3. Стыки рабочей арматуры внахлестку без сварки, на скрутках из вязальной проволоки не менее 3 шт. на стык. Длина нахлеста 71d. Стыки располагать вразбежку, чтобы площадь рабочей арматуры, стыкуемой в одном сечении, не превышала 50%.
4. Расход арматуры в погонных метрах приведен с учетом нахлеста.
5. Стержни, указанные в "Ведомости деталей", должны гнуться механическим способом в холодном состоянии с радиусом гиба 3d - 5d, где d - диаметр стержня
6. Узел стыковки арматуры нахлеста и анкеровки смотреть на листе 5.1

						65П-АИП-2024-1-КЖ	
						Строительство многопрофильной больницы на 250 коек с онкологическим центром и поликлиникой на 350 посещений, по адресу: Медеуский район, г. Алматы	
Изм.	Кол.уч	Лист	N док.	Подп.	Дата		
						"Блок 1 Секция 1"	Стадия: РП; Лист: 5.26; Листов:
ГКП		Курал М				Схема расположения основное армирование монолитной стены по оси Гс стена См-7 (тол.250мм)	АстанаИнжПроект
Проверил		Кыдырбай А					
Разраб.		Ауез Б					
Н.контроль		Ешенкулова					Формат А1

Разрез 7 – 7 (Армирование) М1:50

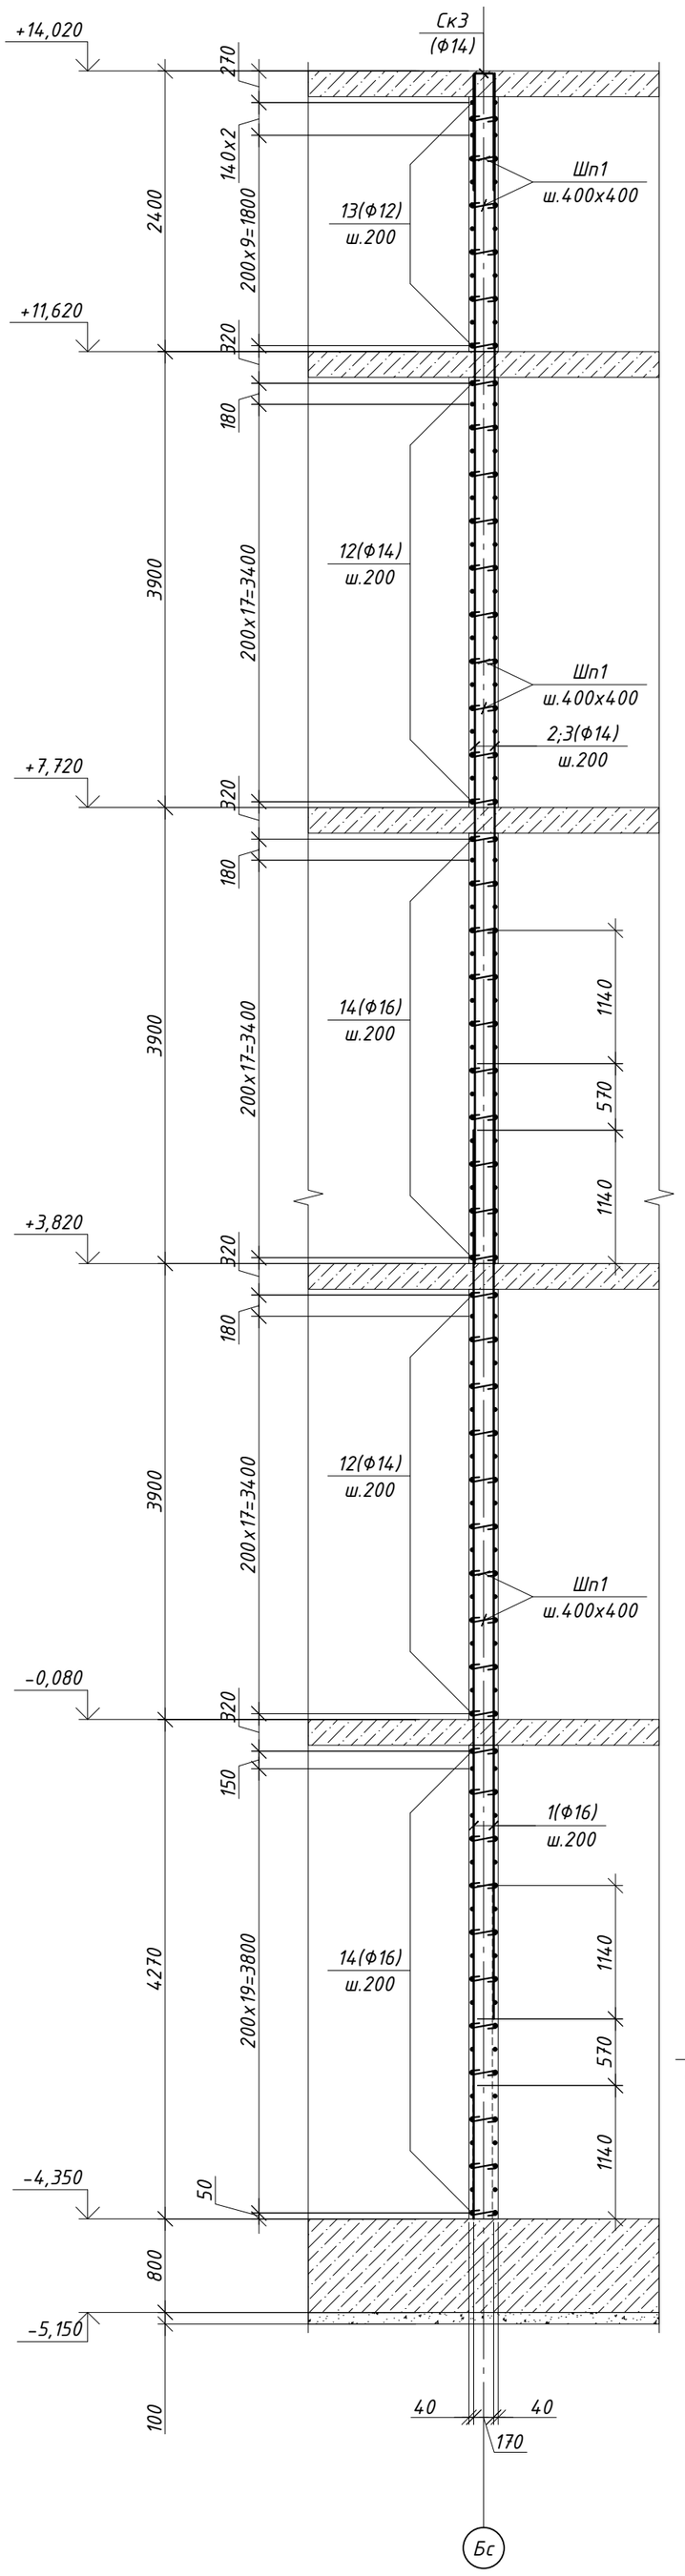


Спецификация элементов

Поз.	Обозначение	Наименование	Кол.	Масса ед.кг	Примечание
		По оси Гс стена См-7			10092.65
Шп1	ГОСТ 34028-2016(214-210-0101-0002)	ф 8 А500С L= 370	1620	0.15	236.51
Х1	ГОСТ 34028-2016(214-210-0101-0002)	ф 8 А500С L= 980	1883	0.39	728.14
Х2	ГОСТ 34028-2016(214-210-0101-0002)	ф 8 А500С L= 880	158	0.35	54.86
Х3	ГОСТ 34028-2016(214-210-0101-0002)	ф 8 А500С L= 780	146	0.31	44.94
Ск2	ГОСТ 34028-2016(214-210-0502-0001)	ф 12 А500С L= 1890	81	1.68	135.92
Ск3	ГОСТ 34028-2016(214-210-0502-0002)	ф 14 А500С L= 2170	333	2.62	873.21
Ск4	ГОСТ 34028-2016(214-210-0502-0003)	ф 16 А500С L= 2450	128	3.87	494.97
1	ГОСТ 34028-2016(214-210-0502-0003)	ф 16 А500С L= 9310	144	14.69	2115.98
2	ГОСТ 34028-2016(214-210-0502-0002)	ф 14 А500С L= 10180	51	12.30	627.38
3	ГОСТ 34028-2016(214-210-0502-0002)	ф 14 А500С L= 8470	51	10.24	522.00
4	ГОСТ 34028-2016(214-210-0502-0002)	ф 14 А500С L= 9170	34	11.08	376.76
5	ГОСТ 34028-2016(214-210-0502-0001)	ф 12 А500С L= 10180	17	9.04	153.65
6	ГОСТ 34028-2016(214-210-0502-0001)	ф 12 А500С L= 8680	17	7.71	131.01
7	ГОСТ 34028-2016(214-210-0502-0003)	ф 16 А500С L= 8150	8	12.86	102.91
8	ГОСТ 34028-2016(214-210-0502-0003)	ф 16 А500С L= 6440	8	10.16	81.32
9	ГОСТ 34028-2016(214-210-0502-0003)	ф 16 А500С L= 7960	16	12.56	201.02
10	ГОСТ 34028-2016(214-210-0502-0002)	ф 14 А500С L= 4060	22	4.91	107.94
11*	ГОСТ 34028-2016(214-210-0502-0002)	ф 14 А500С L= 6220	15	7.52	112.74
12	ГОСТ 34028-2016(214-210-0502-0002)	ф 14 А500С L= пог.м.	566	1.21	683.96
13	ГОСТ 34028-2016(214-210-0502-0001)	ф 12 А500С L= пог.м.	475	0.89	421.71
14	ГОСТ 34028-2016(214-210-0502-0003)	ф 16 А500С L= пог.м.	596	1.58	940.69
15	ГОСТ 34028-2016(214-210-0502-0002)	ф 14 А500С L= 4560	24	5.51	132.25
16	ГОСТ 34028-2016(214-210-0502-0002)	ф 14 А500С L= 4160	44	5.03	221.19
17	ГОСТ 34028-2016(214-210-0502-0002)	ф 14 А500С L= 2500	56	3.02	169.18
18*	ГОСТ 34028-2016(214-210-0502-0002)	ф 14 А500С L= 2530	24	3.06	73.37
19*	ГОСТ 34028-2016(214-210-0502-0001)	ф 12 А500С L= 1990	24	1.77	42.40
20	ГОСТ 34028-2016(214-210-0502-0001)	ф 12 А500С L= 2500	88	2.22	195.32
21	ГОСТ 34028-2016(214-210-0502-0003)	ф 16 А500С L= 1500	18	2.37	42.62
22	ГОСТ 34028-2016(214-210-0502-0001)	ф 12 А500С L= 4300	18	3.82	68.72
		Материалы:			
		Класс бетона С 20/25 (В25), м³			50.46

Позиции со "*" см. "Ведомость деталей" см. на данном листе.

Узел Т

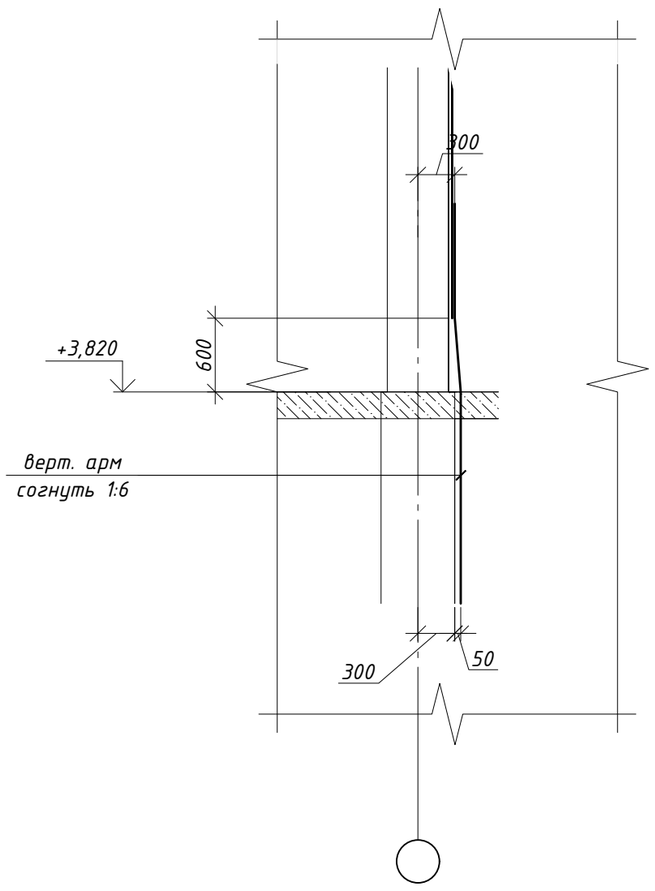

Ведомость расхода стали, кг

Марка элемента	Изделия арматурные							Всего
	Арматура класса							
	А240			А500С				
	ГОСТ 34028-2016(214-210-0101)			ГОСТ 34028-2016(214-210-0502)				
	ф6	ф8	Итого	ф12	ф14	ф16	Итого	
По оси Гс стена См-7	---	1064.45	1064.45	1148.72	3899.99	3979.49	9028.19	10092.65

Ведомость деталей


Поз.	Эскиз	Поз.	Эскиз
Шп1	170, 100, 100 — по в.г. L=370	Ск3	1000, 170, 1000 — по н.г. L=2170
Х1	320, 170, 270, 220 — по в.г. L=980	Ск4	1140, 170, 1140 — по н.г. L=2450
Х2	270, 170, 270, 170 — по в.г. L=880	11*	3880, 170, 2170 — по н.г. L=6220
Х3	220, 170, 270, 120 — по в.г. L=780	18*	1360, 170, 1000 — по н.г. L=2530
Ск2	860, 170, 860 — по н.г. L=1890	19*	960, 170, 860 — по н.г. L=1990

1. Общие указания см. л. – 1.
2. Данный лист читать совместно с л. КЖ-5.25 ... 5.27
3. Стыки рабочей арматуры внахлестку без сварки, на скрутках из вязальной проволоки не менее 3 шт. на стык. Длина нахлеста 71d. Стыки располагать вразбежку, чтобы площадь рабочей арматуры, стыкуемой в одном сечении, не превышала 50%.
4. Расход арматуры в погонных метрах приведен с учетом нахлеста.
5. Стержни, указанные в "Ведомости деталей", должны гнуться механическим способом в холодном состоянии с радиусом гиба 3d – 5d, где d – диаметр стержня
6. Узел стыковки арматуры нахлеста и анкеровки смотреть на листе 5.1


Изм.	Кол.уч.	Лист	N док.	Подп.	Дата		
						65П-АИП-2024-1-КЖ	
						Строительство многопрофильной больницы на 250 коек с онкологическим центром и поликлиникой на 350 посещений, по адресу: Медеуский район, г. Алматы	
						"Блок 1 Секция 1"	Стадия: РП; Лист: 5.27; Листов:
ГКП		Курал М				Спецификация монолитной стены по оси Гс стена См-7 (тол.250мм)	АстанаИнжПроект
Проверил		Кыдырбай А					
Разраб.		Ауез Б					
Н.контроль		Ешенкулова					

Формат А2


Схема расположения опалубочный чертеж монолитной стены по оси Дс стена См-8 (тол.250мм)

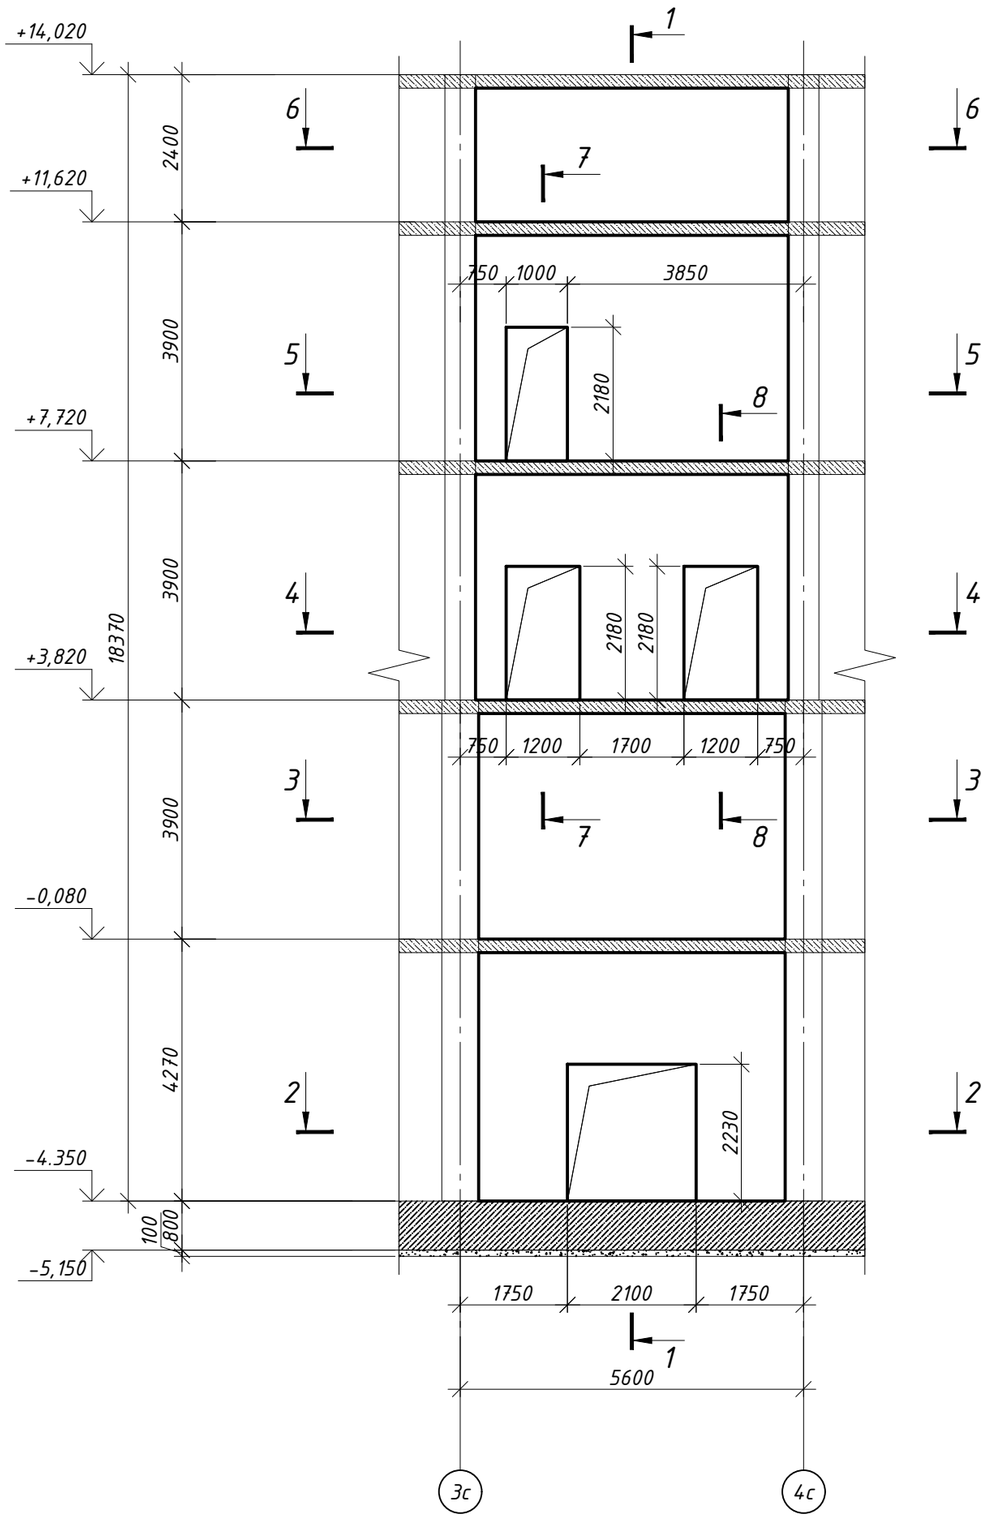


Разрез 1 - 1 (Опалубка) М1:100

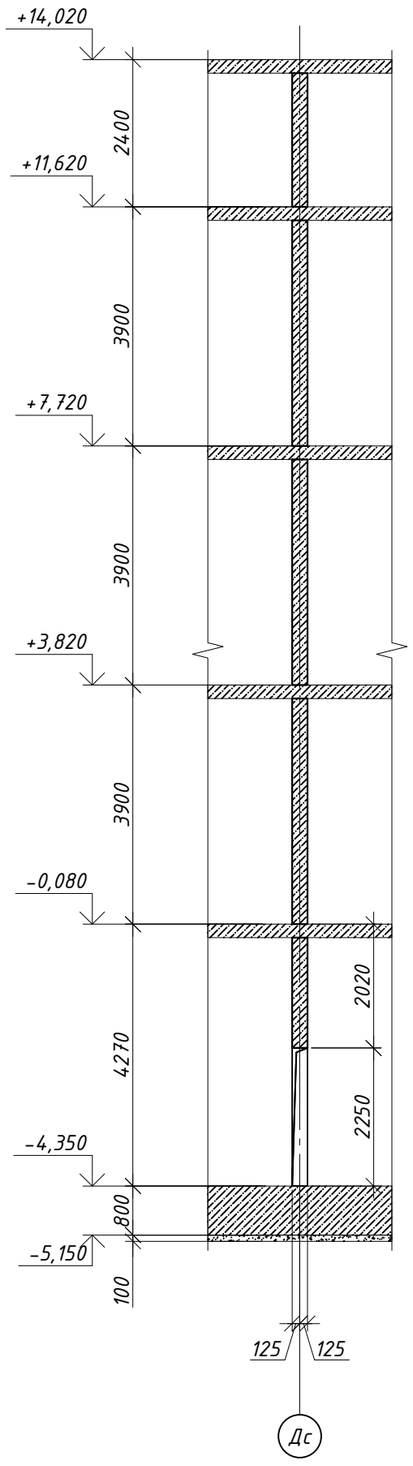


Разрез 2 - 2 (Опалубка) М1:100

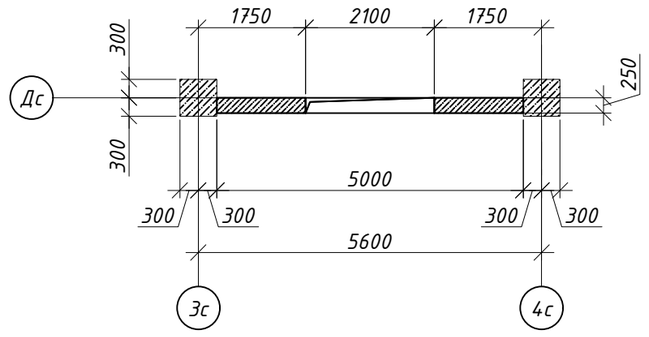


Разрез 3 - 3 (Опалубка) М1:100

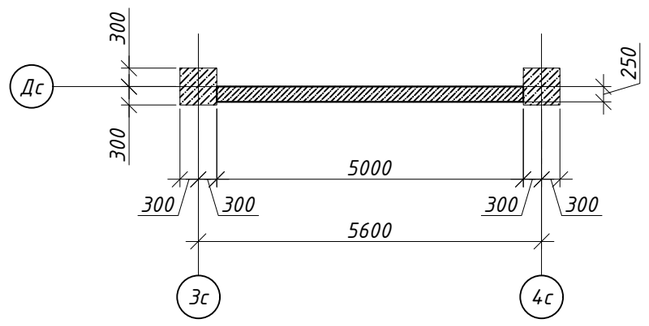


Разрез 4 - 4 (Опалубка) М1:100

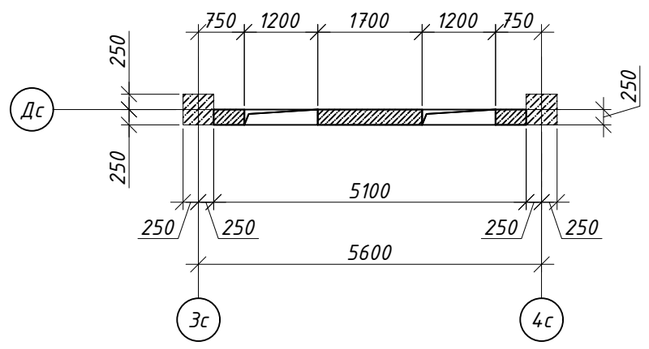


Разрез 5 - 5 (Опалубка) М1:100

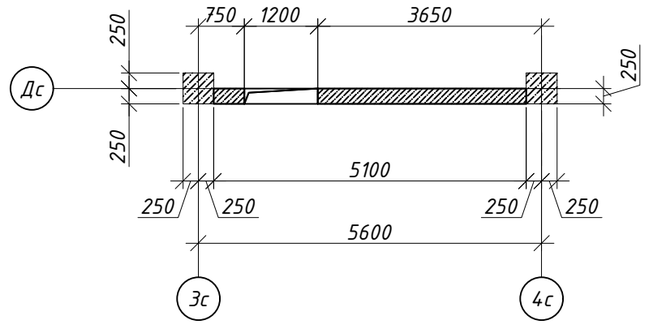


Разрез 6 - 6 (Опалубка) М1:100

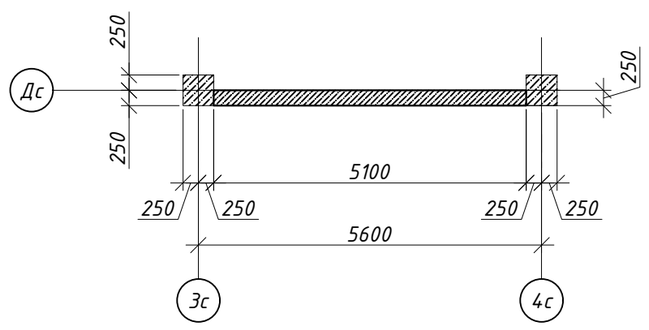


Разрез 7 - 7 (Опалубка) М1:100

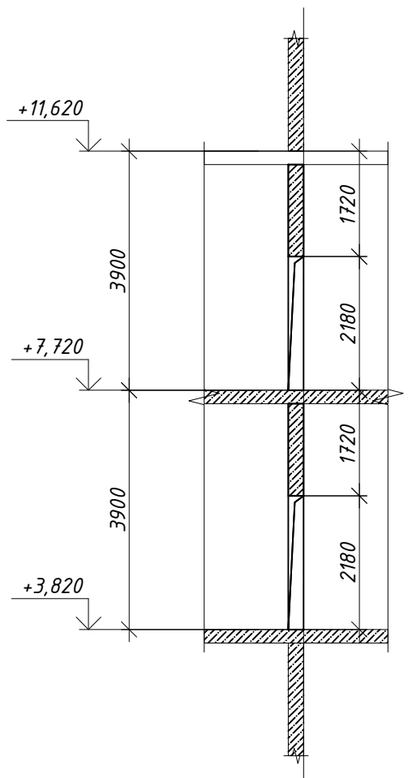

Разрез 8 - 8 (Опалубка) М1:100

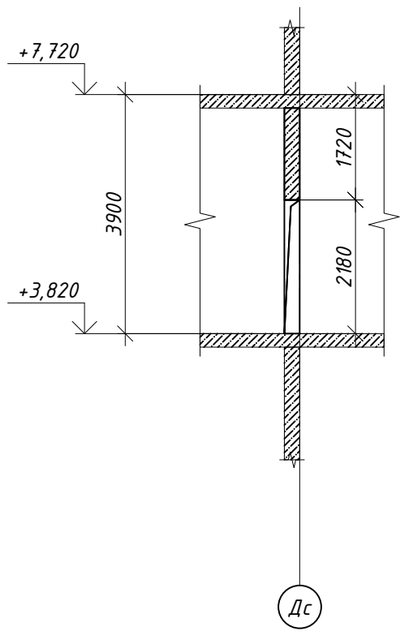

Узел Т

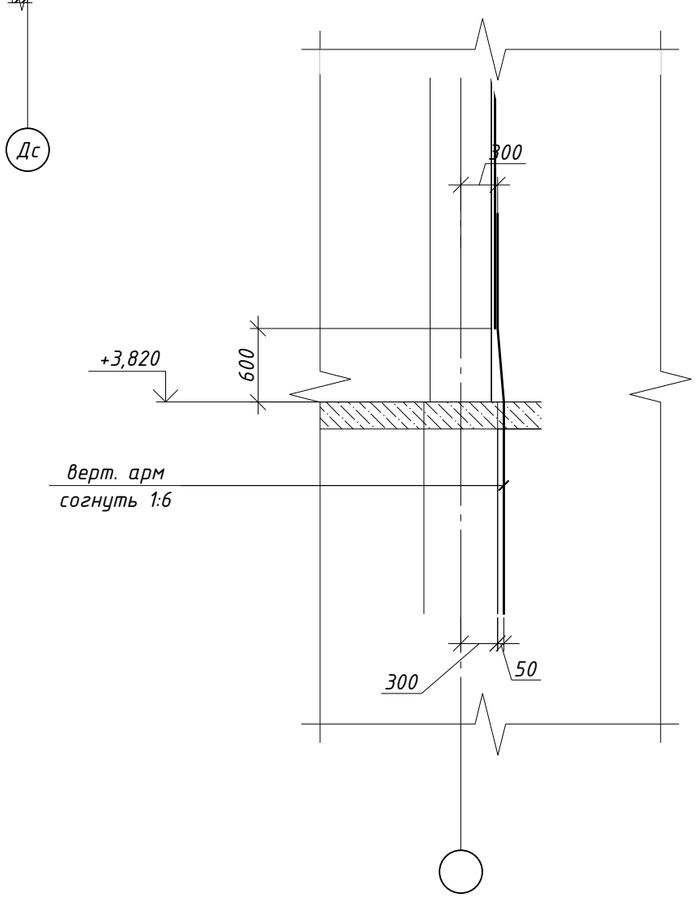

1. Общие указания см. л. - 1.
2. Данный лист читать совместно с л. КЖ-5.28 ... 5.30
3. Стыки рабочей арматуры внахлестку без сварки, на скрутках из вязальной проволоки не менее 3 шт. на стык. Длина нахлеста 71d. Стыки располагать вразбежку, чтобы площадь рабочей арматуры, стыкуемой в одном сечении, не превышала 50%.
4. Расход арматуры в погонных метрах приведен с учетом нахлеста.
5. Стержни, указанные в "Ведомости деталей", должны гнуться механическим способом в холодном состоянии с радиусом гиба 3d - 5d, где d - диаметр стержня
6. Узел стыковки арматуры нахлеста и анкеровки смотреть на листе 5.1

						65П-АИП-2024-1-КЖ		
						Строительство многопрофильной больницы на 250 коек с онкологическим центром и поликлиникой на 350 посещений, по адресу: Медеуский район, г. Алматы		
Изм.	Кол.уч.	Лист	N док.	Подп.	Дата			
						"Блок 1 Секция 1"	Стадия	Лист	Листов
							РП	5.28	
ГКП		Курал М				Схема расположения опалубочный чертеж монолитной стены по оси Дс стена См-8 (тол.250мм)	АстанаИнжПроект		
Проверил		Кыдырбай А							
Разраб.		Ауез Б							
Н.контроль		Ешенкулова							

Формат А2

Схема расположения основное вертикальное армирование монолитной стены по оси Дс стена См-8 (тол.250мм)



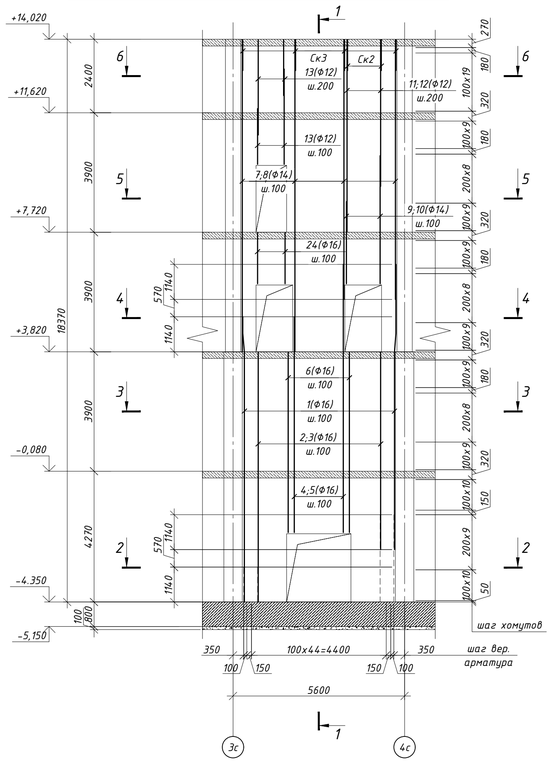



Схема расположения основное горизонтальное армирование монолитной стены по оси Дс стена См-8 (тол.250мм)

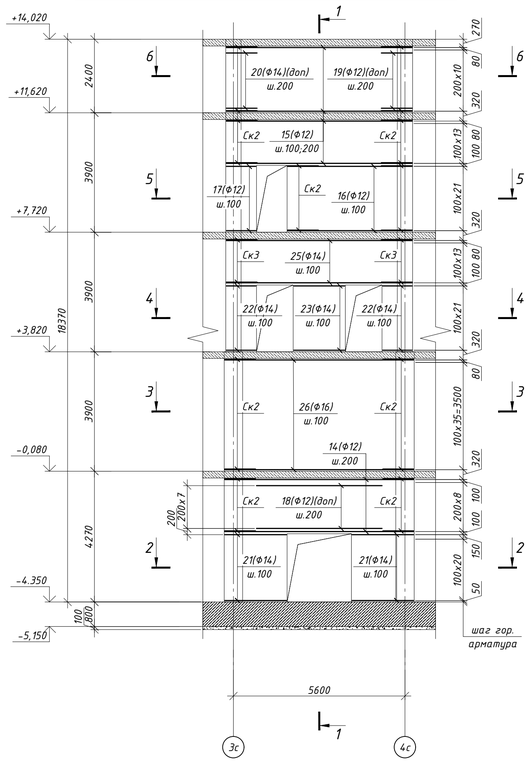


Разрез 1 - 1 (Армирование) М1:50

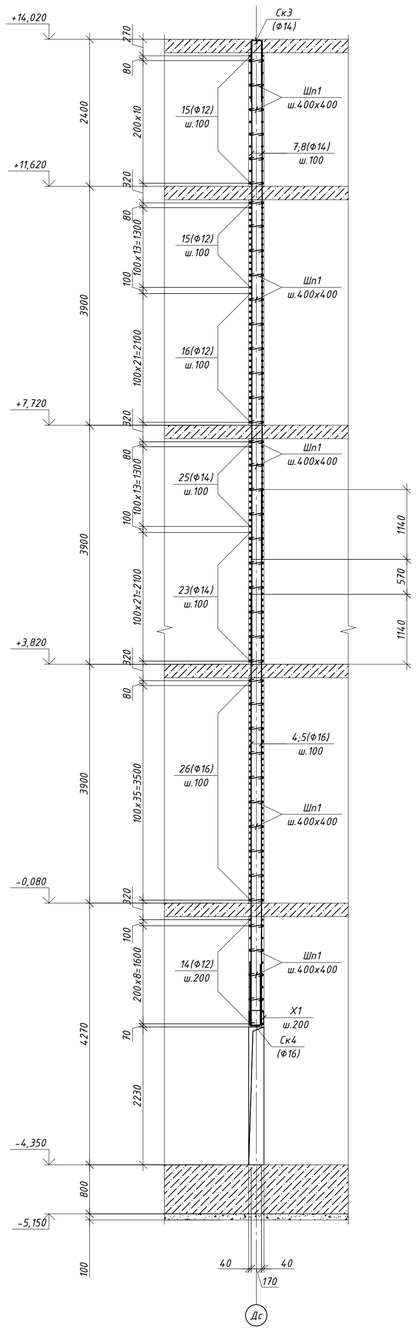


Разрез 2 - 2 (Армирование) М1:50

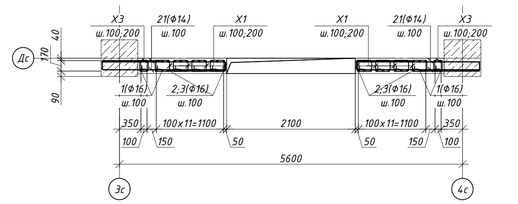


Разрез 3 - 3 (Армирование) М1:50

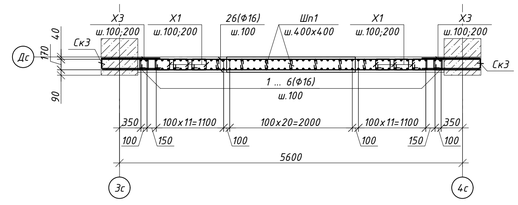


Разрез 4 - 4 (Армирование) М1:50

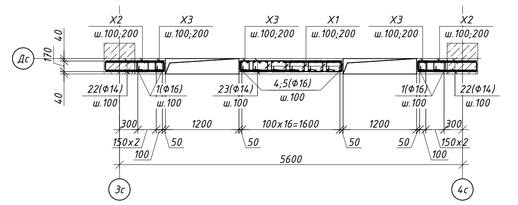


Разрез 5 - 5 (Армирование) М1:50

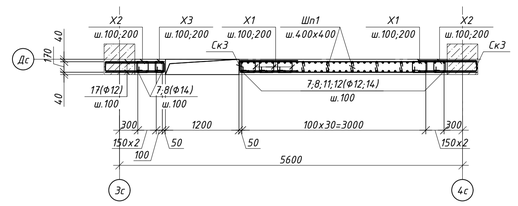


Разрез 6 - 6 (Армирование) М1:50

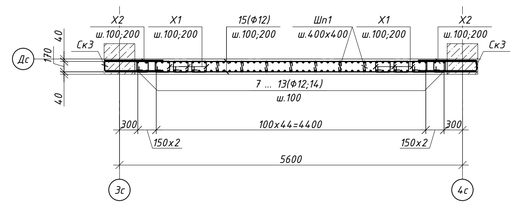


Разрез 8 - 8 (Армирование) М1:50

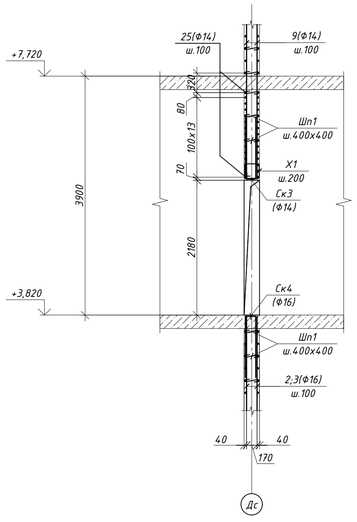


Разрез 9 - 9 (Армирование) М1:50

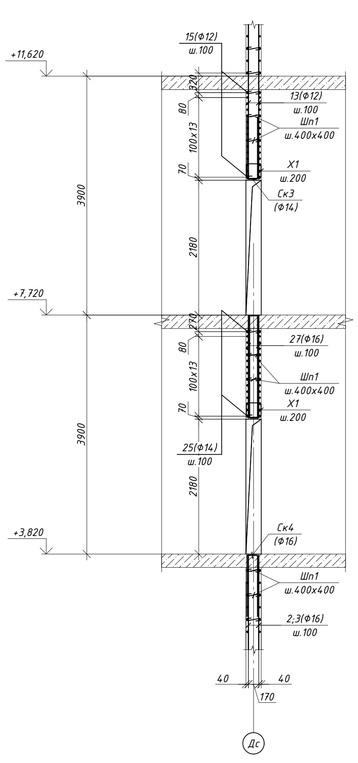

Фрагмент обрамления проема

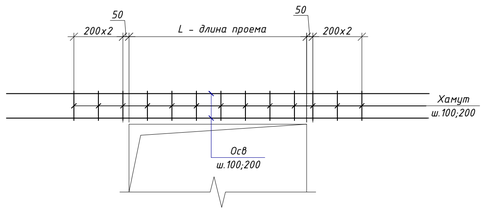

Узел стыковки Горизонтальной арматуры в нахлест

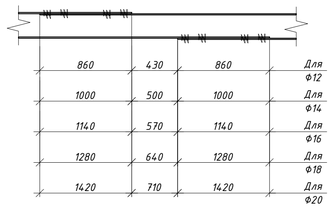

1. Общие указания см. л. - 1.
2. Данный лист читать совместно с л. КЖ-5.28 ... 5.30
3. Стыки рабочей арматуры внахлестку без сварки, на скрутках из вязальной проволоки не менее 3 шт. на стык. Длина нахлеста 71d. Стыки располагать вразбежку, чтобы площадь рабочей арматуры, стыкуемой в одном сечении, не превышала 50%.
4. Расход арматуры в погонных метрах приведен с учетом нахлеста.
5. Стержни, указанные в "Ведомости деталей", должны гнуться механическим способом в холодном состоянии с радиусом гиба 3d - 5d, где d - диаметр стержня
6. Узел стыковки арматуры нахлеста и анкеровки смотреть на листе 5.1


						65П-АИП-2024-1-КЖ	
						Строительство многопрофильной больницы на 250 коек с онкологическим центром и поликлиникой на 350 посещений, по адресу: Медеуский район, г. Алматы	
Изм.	Кол.уч	Лист	N док.	Подп.	Дата		
						"Блок 1 Секция 1"	Стадия: РП; Лист: 5.29; Листов:
ГКП		Курал М					
Проверил		Кыдырбай А				Схема расположения основное армирование монолитной стены по оси Дс стена См-8 (тол.250мм)	АстанаИнжПроект
Разраб.		Ауез Б					
Н.контроль		Ешенкулова					


Формат А1

Ведомость деталей

Поз.	Эскиз	Поз.	Эскиз
Шп1	170, 100, 100; по в.г. L=370	13*	3105, 170, 1815; по н.г. L=5090
Х1	320, 170, 270, 220; по в.г. L=980	17*	960, 170, 860; по н.г. L=1990
Х2	270, 170, 270, 170; по в.г. L=880	21*	2010, 170, 1000; по н.г. L=3180
Х3	220, 170, 270, 120; по в.г. L=780	22*	960, 170, 960; по н.г. L=2090
Ск2	860, 170, 860; по н.г. L=1890	23*	1660, 170, 1000; по н.г. L=2830
Ск3	1000, 170, 1000; по н.г. L=2170	24*	1660, 170, 1140; по н.г. L=2970
Ск4	1140, 170, 1140; по н.г. L=2450		

Узел стыковки вертикальной арматуры в нахлест и накладка

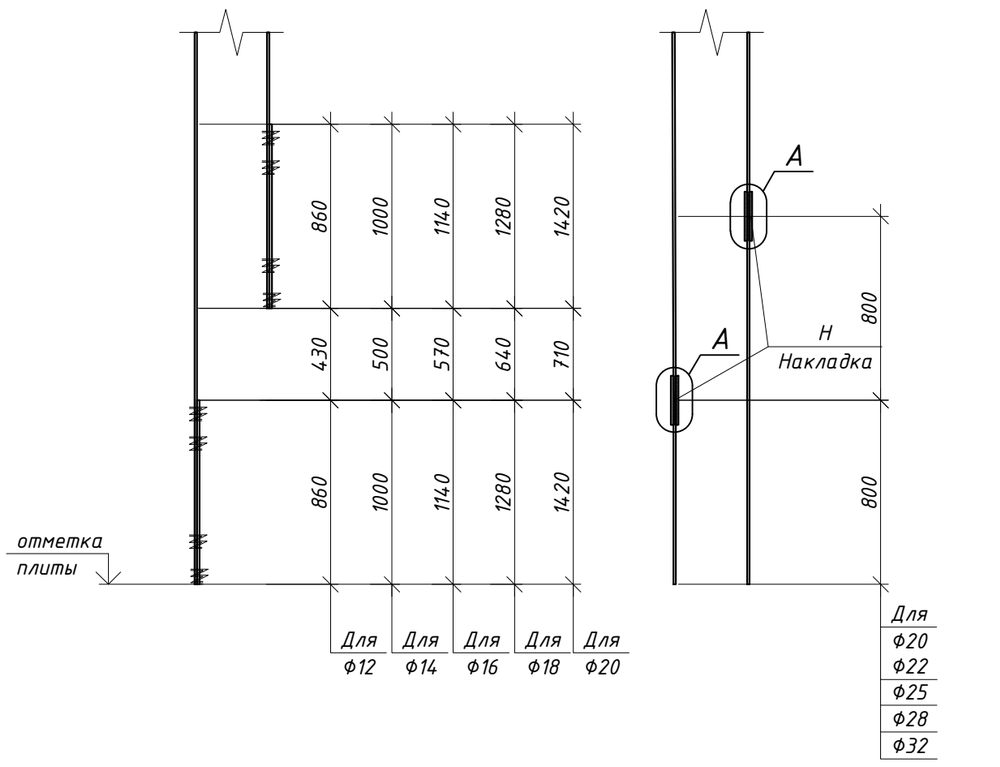

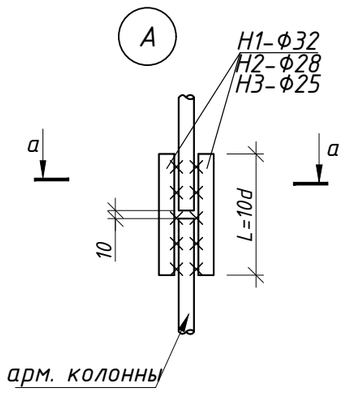

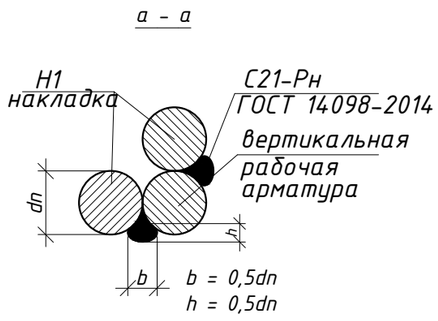


Таблица размеров Накладка

Марка эл-та	dн	L	вес
	мм.		кг.
H1	32	320	2.01
H2	28	280	1.35
H3	25	250	0.96
H4	22	220	0.66
H5	20	200	0.49

Спецификация элементов

Поз.	Обозначение	Наименование	Кол.	Масса ед.кг	Примечание
		По оси Дс стена См-8			5147.73
Шп1	ГОСТ 34028-2016(214-210-0101-0002)	ф 8 А500С L= 370	294	0.15	42.92
Х1	ГОСТ 34028-2016(214-210-0101-0002)	ф 8 А500С L= 980	809	0.39	312.83
Х2	ГОСТ 34028-2016(214-210-0101-0002)	ф 8 А500С L= 880	158	0.35	54.86
Х3	ГОСТ 34028-2016(214-210-0101-0002)	ф 8 А500С L= 780	236	0.31	72.64
Ск2	ГОСТ 34028-2016(214-210-0502-0001)	ф 12 А500С L= 1890	132	1.68	221.49
Ск3	ГОСТ 34028-2016(214-210-0502-0002)	ф 14 А500С L= 2170	55	2.62	144.22
Ск4	ГОСТ 34028-2016(214-210-0502-0003)	ф 16 А500С L= 2450	96	3.87	371.22
1	ГОСТ 34028-2016(214-210-0502-0003)	ф 16 А500С L= 9310	16	14.69	235.11
2	ГОСТ 34028-2016(214-210-0502-0003)	ф 16 А500С L= 8150	20	12.86	257.27
3	ГОСТ 34028-2016(214-210-0502-0003)	ф 16 А500С L= 6440	20	10.16	203.29
4	ГОСТ 34028-2016(214-210-0502-0003)	ф 16 А500С L= 7040	9	11.11	100.00
5	ГОСТ 34028-2016(214-210-0502-0003)	ф 16 А500С L= 8750	9	13.81	124.29
6	ГОСТ 34028-2016(214-210-0502-0003)	ф 16 А500С L= 5880	8	9.28	74.24
7	ГОСТ 34028-2016(214-210-0502-0002)	ф 14 А500С L= 10180	8	12.30	98.41
8	ГОСТ 34028-2016(214-210-0502-0002)	ф 14 А500С L= 8470	8	10.24	81.88
9	ГОСТ 34028-2016(214-210-0502-0002)	ф 14 А500С L= 2680	12	3.24	38.86
10	ГОСТ 34028-2016(214-210-0502-0002)	ф 14 А500С L= 4180	12	5.05	60.61
11	ГОСТ 34028-2016(214-210-0502-0001)	ф 12 А500С L= 6280	7	5.58	39.03
12	ГОСТ 34028-2016(214-210-0502-0001)	ф 12 А500С L= 4780	7	4.24	29.71
13*	ГОСТ 34028-2016(214-210-0502-0001)	ф 12 А500С L= 5090	19	4.52	85.86
14	ГОСТ 34028-2016(214-210-0502-0001)	ф 12 А500С L= 6160	20	5.47	109.38
15	ГОСТ 34028-2016(214-210-0502-0001)	ф 12 А500С L= 6060	54	5.38	290.53
16	ГОСТ 34028-2016(214-210-0502-0001)	ф 12 А500С L= 4060	44	3.60	158.60
17*	ГОСТ 34028-2016(214-210-0502-0001)	ф 12 А500С L= 1990	44	1.77	77.74
18	ГОСТ 34028-2016(214-210-0502-0001)	ф 12 А500С L= 4100	16	3.64	58.24
19	ГОСТ 34028-2016(214-210-0502-0001)	ф 12 А500С L= 1000	20	0.89	17.76
20	ГОСТ 34028-2016(214-210-0502-0002)	ф 14 А500С L= 1000	20	1.21	24.17
21*	ГОСТ 34028-2016(214-210-0502-0002)	ф 14 А500С L= 3180	88	3.84	338.16
22*	ГОСТ 34028-2016(214-210-0502-0002)	ф 14 А500С L= 2090	88	2.53	222.25
23*	ГОСТ 34028-2016(214-210-0502-0002)	ф 14 А500С L= 2830	44	3.42	150.47
24*	ГОСТ 34028-2016(214-210-0502-0003)	ф 16 А500С L= 2970	24	4.69	112.50
25	ГОСТ 34028-2016(214-210-0502-0002)	ф 14 А500С L= 6060	30	7.32	219.69
26	ГОСТ 34028-2016(214-210-0502-0003)	ф 16 А500С L= 6160	74	9.72	719.47
		Материалы:			
		Класс бетона С 20/25 (В25), м³			18.80

Позиции со "*" см. "Ведомость деталей" см. на данном листе.

Ведомость расхода стали, кг

Марка элемента	Изделия арматурные							Всего
	Арматура класса							
	А240			А500С				
	ГОСТ 34028-2016(214-210-0101)			ГОСТ 34028-2016(214-210-0502)				
	ф6	ф8	Итого	ф12	ф14	ф16	Итого	
По оси Дс стена См-8	---	483.25	483.25	1088.33	1378.74	2197.41	4664.47	5147.73

1. Общие указания см. л. - 1.
2. Данный лист читать совместно с л. КЖ-5.28 ... 5.30
3. Стыки рабочей арматуры внахлестку без сварки, на скрутках из вязальной проволоки не менее 3 шт. на стык. Длина нахлеста 71d. Стыки располагать вразбежку, чтобы площадь рабочей арматуры, стыкуемой в одном сечении, не превышала 50%.
4. Расход арматуры в погонных метрах приведен с учетом нахлеста.
5. Стержни, указанные в "Ведомости деталей", должны гнуться механическим способом в холодном состоянии с радиусом гиба 3d - 5d, где d - диаметр стержня
6. Узел стыковки арматуры нахлеста и анкеровки смотреть на листе 5.1

Изм.	Кол.уч.	Лист	N док.	Подп.	Дата	65П-АИП-2024-1-КЖ			
						Строительство многопрофильной больницы на 250 коек с онкологическим центром и поликлиникой на 350 посещений, по адресу: Медеуский район, г. Алматы			
ГКП		Курал М				"Блок 1 Секция 1"	Стадия	Лист	Листов
Проверил		Кыдырбай А					РП	5.30	
Разраб.		Ауез Б				Спецификация монолитной стены по оси Дс стена См-8 (тол.250мм)	АстанаИнжПроект		
Н.контроль		Ешенкулова							

Формат А2