


Опалубочный чертеж монолитной стены по оси Ес стена См-9 (тол.250мм)

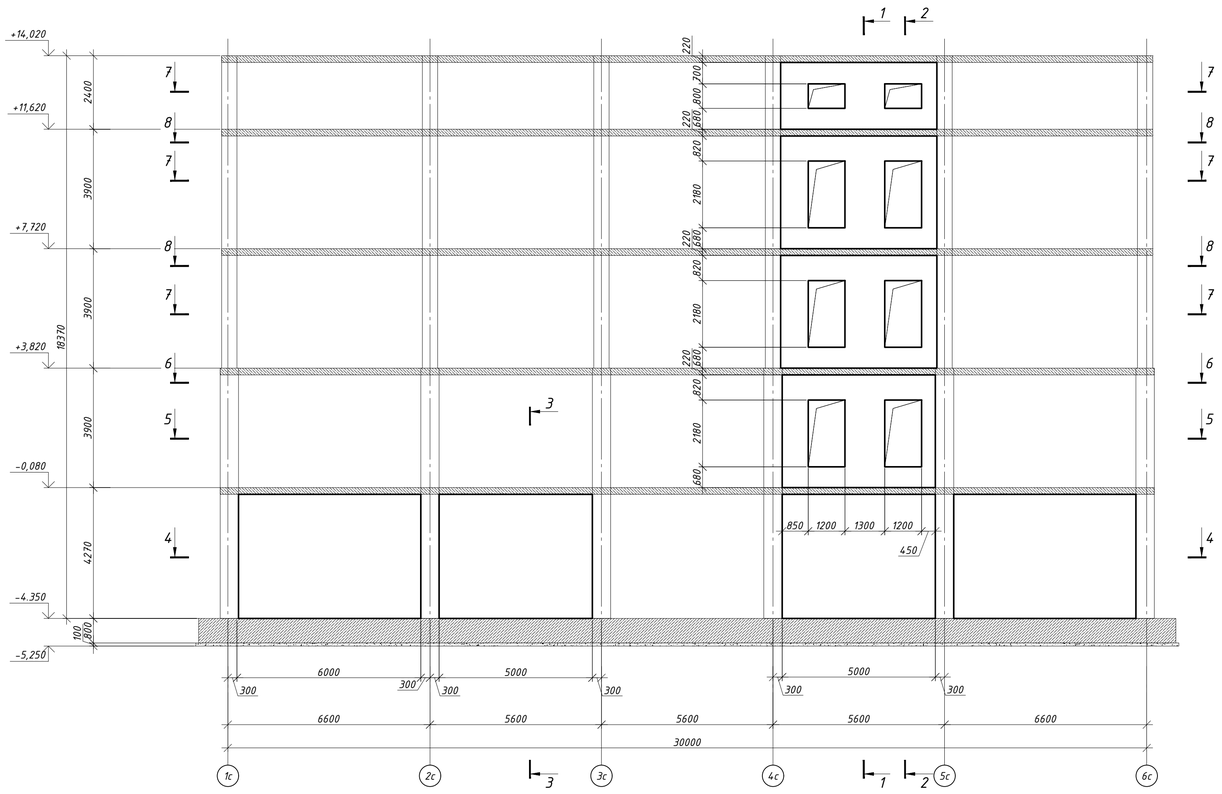


Разрез 1 - 1 (Опалубка)

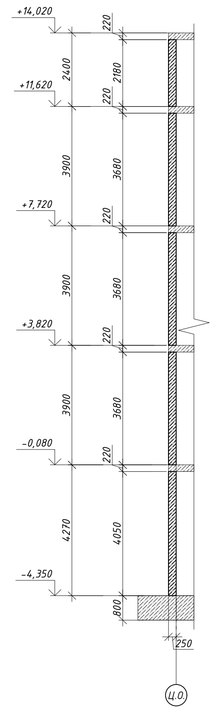


Разрез 2 - 2 (Опалубка)

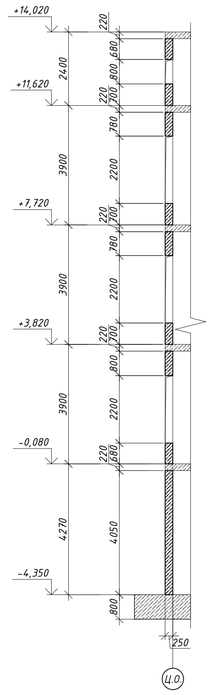


Разрез 3 - 3 (Опалубка)

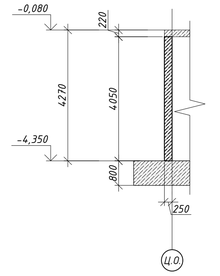


Разрез 4 - 4 (Опалубка)

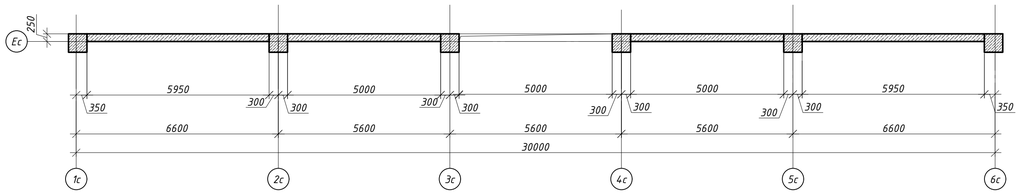


Разрез 5 - 5 (Опалубка)

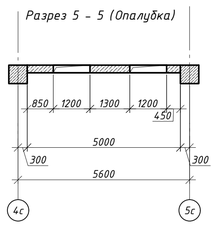


Разрез 6 - 6 (Опалубка)

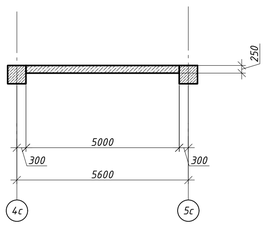


Разрез 7 - 7 (Опалубка)

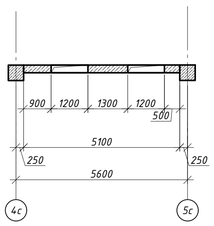

Разрез 8 - 8; 9 - 9 (Опалубка)

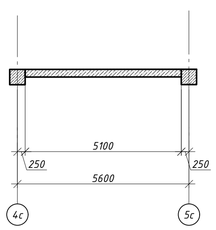



Фрагмент обрамления проема

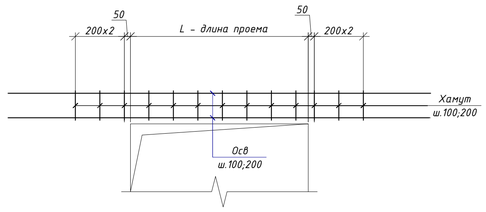


Узел стыковки вертикальной арматуры в нахлест и накладка


Анкеровка

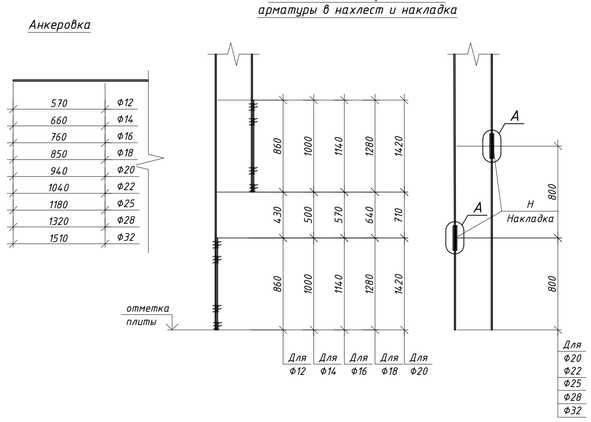

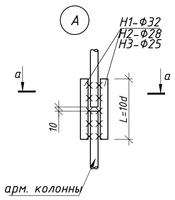

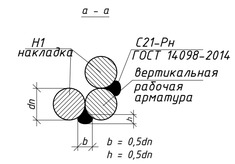

Узел стыковки Горизонтальной арматуры в нахлест

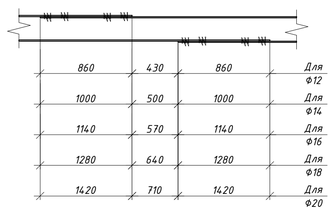

Б

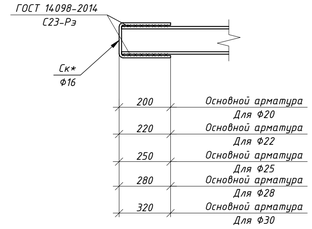


Таблица размеров Накладка

Марка эл-та	dн	L	вес
	мм.		кг.
H1	32	320	2.01
H2	28	280	1.35
H3	25	250	0.96
H4	22	220	0.66
H5	20	200	0.49

1. Общие указания см. л. - 1.
2. Данный лист читать совместно с л. КЖ- 2.1 ... 2.7; 5.31 ... 5.34
3. Стыки рабочей арматуры внахлестку без сварки, на скрутках из вязальной проволоки не менее 3 шт. на стык. Длина нахлеста 71d. Стыки располагать вразбежку, чтобы площадь рабочей арматуры, стыкуемой в одном сечении, не превышала 50%.
4. Расход арматуры в погонных метрах приведен с учетом нахлеста.
5. Стержни, указанные в "Ведомости деталей", должны гнуться механическим способом в холодном состоянии с радиусом гиба 3d - 5d, где d - диаметр стержня
6. Узел стыковки арматуры нахлеста и анкеровки смотреть на листе 5.1

Изм.	Кол.уч	Лист	N док.	Подп.	Дата
ГКП		Курал М			
Проверил		Кыдырбай А			
Разраб.		Ауез Б			
Н.контроль		Ешенкулова			

65П-АИП-2024-1-КЖ

Строительство многопрофильной больницы на 250 коек с онкологическим центром и поликлиникой на 350 посещений, по адресу: Медеуский район, г. Алматы

"Блок 1 Секция 1"

Стадия	Лист	Листов
РП	5.31	

Опалубочный чертеж монолитной стены по оси Ес стена См-9 (тол.250мм)

АстанаИнжПроект

Формат А1

Схема расположения основное вертикальное армирование монолитной стены по оси Ес стена Ст-9 (тол.250мм)



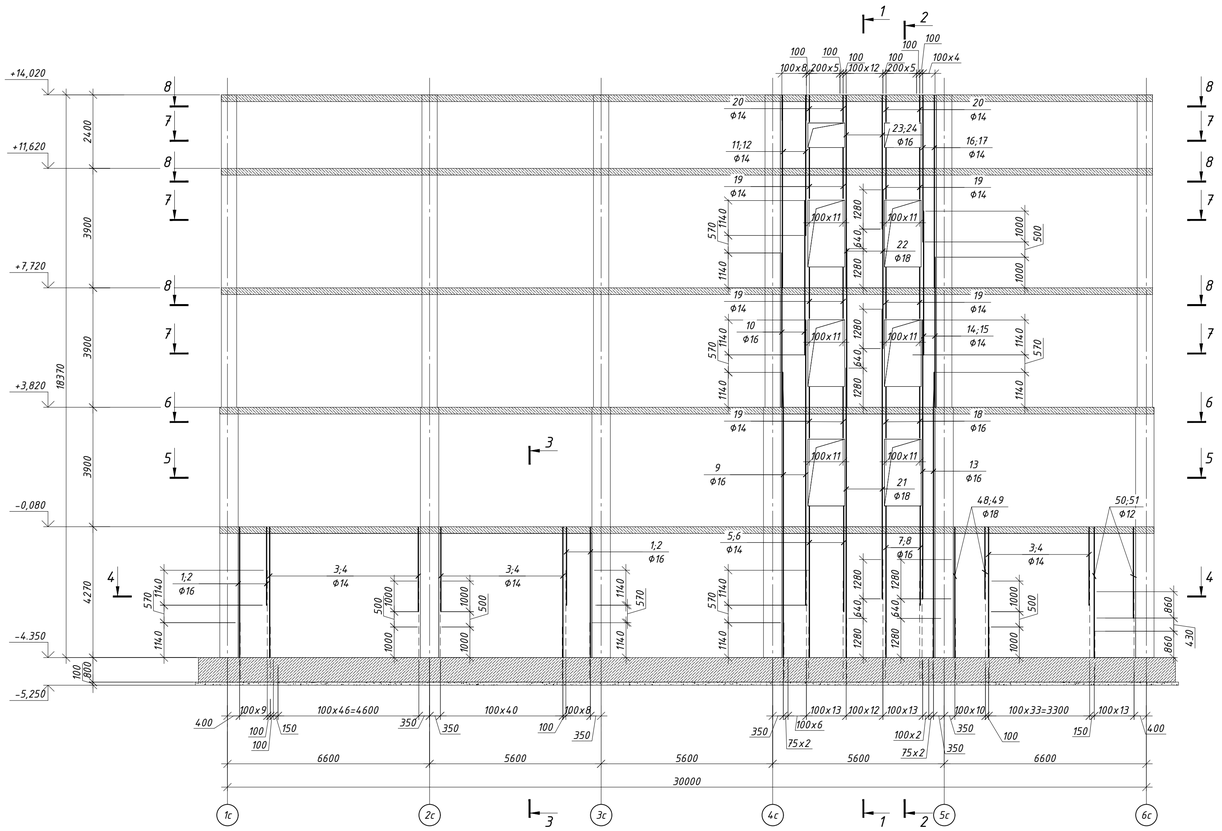



Схема расположения основное горизонтальное армирование монолитной стены по оси Ес стена Ст-9 (тол.250мм)

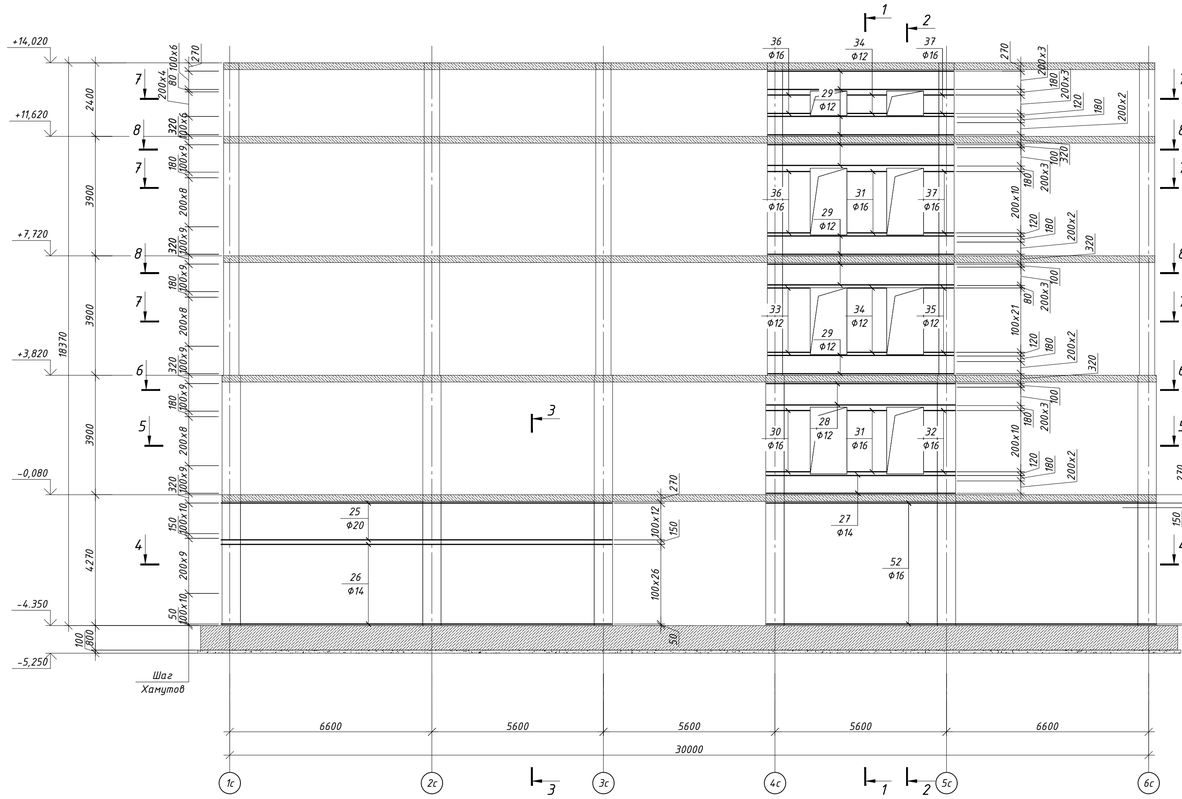


Разрез 4 - 4 (армирование)

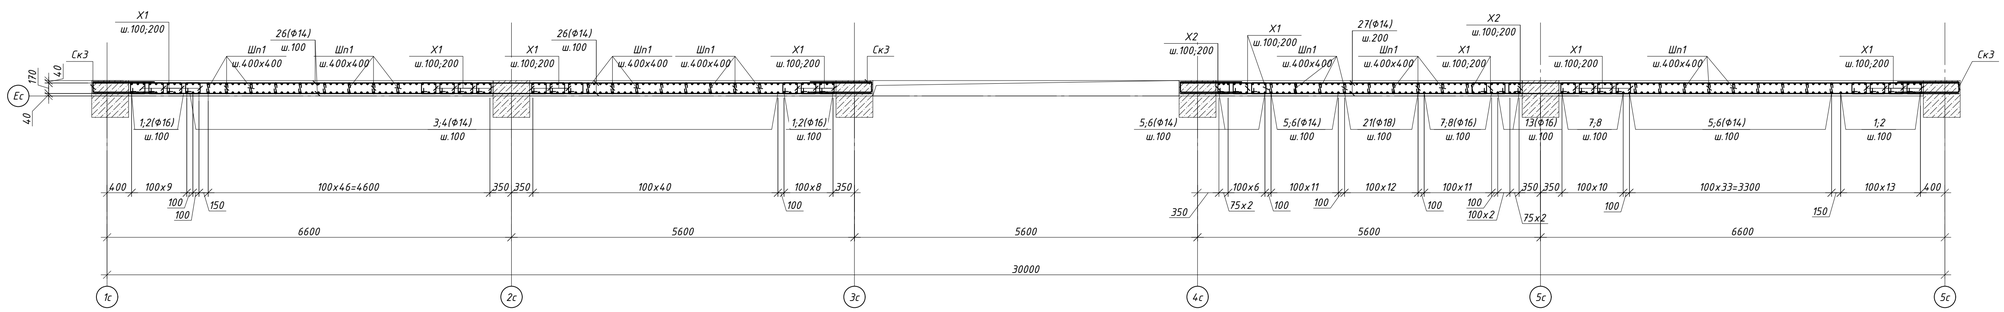


Узел Т

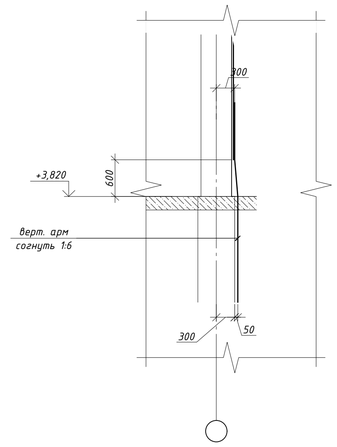

Разрез 5 - 5 (армирование)

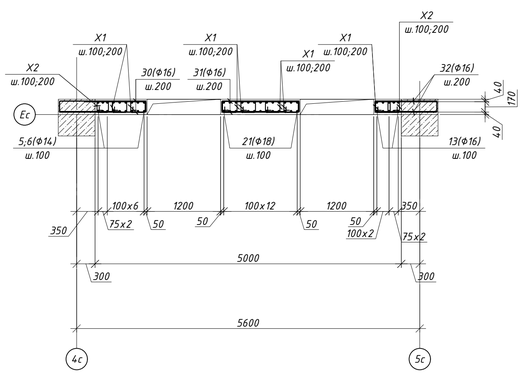

Разрез 6 - 6 (армирование)

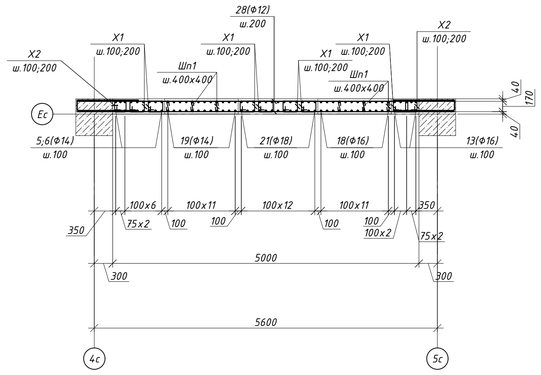


1. Общие указания см. л. - 1.
2. Данный лист читать совместно с л. КЖ- 2.1 ... 2.7; 5.31 ... 5.34
3. Стыки рабочей арматуры внахлестку без сварки, на скрутках из вязальной проволоки не менее 3 шт. на стык. Длина нахлеста 71d. Стыки располагать вразбежку, чтобы площадь рабочей арматуры, стыкуемой в одном сечении, не превышала 50%.
4. Расход арматуры в погонных метрах приведен с учетом нахлеста.
5. Стержни, указанные в "Ведомости деталей", должны гнуться механическим способом в холодном состоянии с радиусом гиба 3d - 5d, где d - диаметр стержня
6. Узел стыковки арматуры нахлеста и анкеровки смотреть на листе 5.1


						65П-АИП-2024-1-КЖ	
						Строительство многопрофильной больницы на 250 коек с онкологическим центром и поликлиникой на 350 посещений, по адресу: Медеуский район, г. Алматы	
Изм.	Кол.уч	Лист	N док.	Подп.	Дата		
						"Блок 1 Секция 1"	Стадия: РП; Лист: 5.32; Листов:
ГКП		Курал М				Опалубочный чертеж монолитной стены по оси Ес стена Ст-9 (тол.250мм)	АстанаИнжПроект
Проверил		Кыдырбай А					
Разраб.		Ауез Б					
Н.контроль		Ешенкулова					

Формат А1


Схема расположения дополнительное горизонтальное армирование монолитной стены по оси Ес стена Ст-9 (тол.250мм)

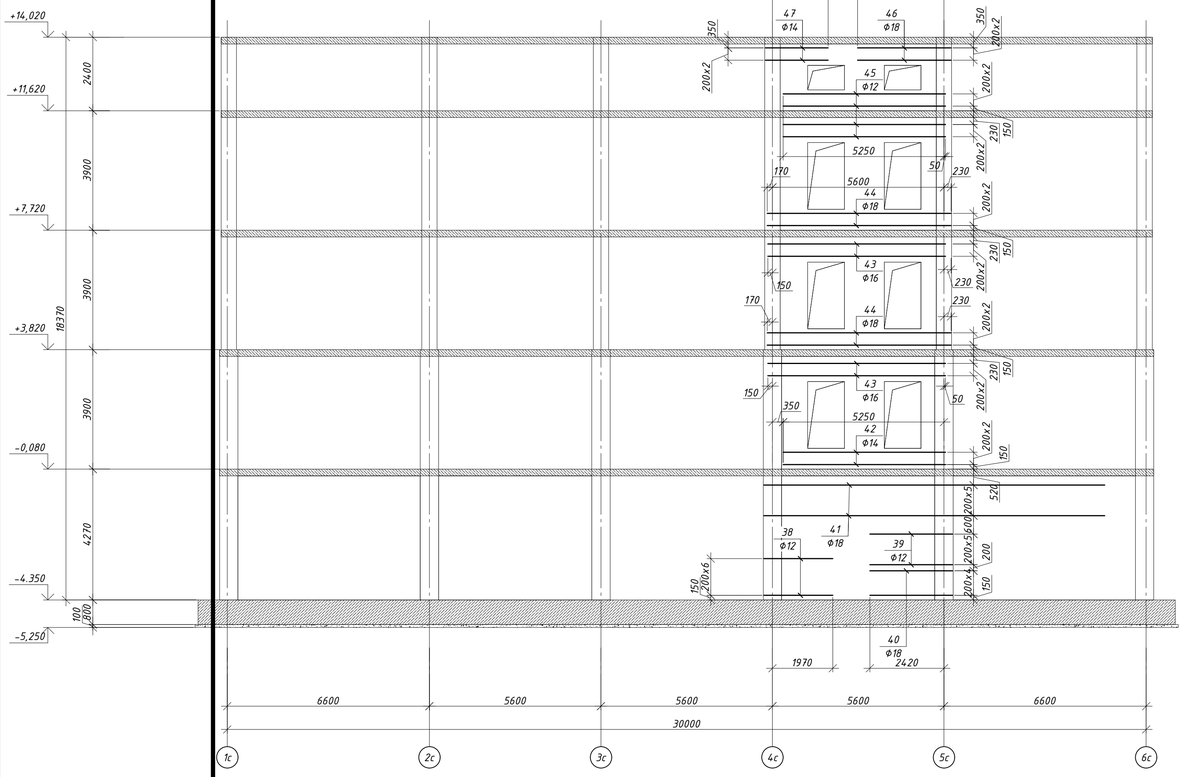


Разрез 1 - 1 (армирование)

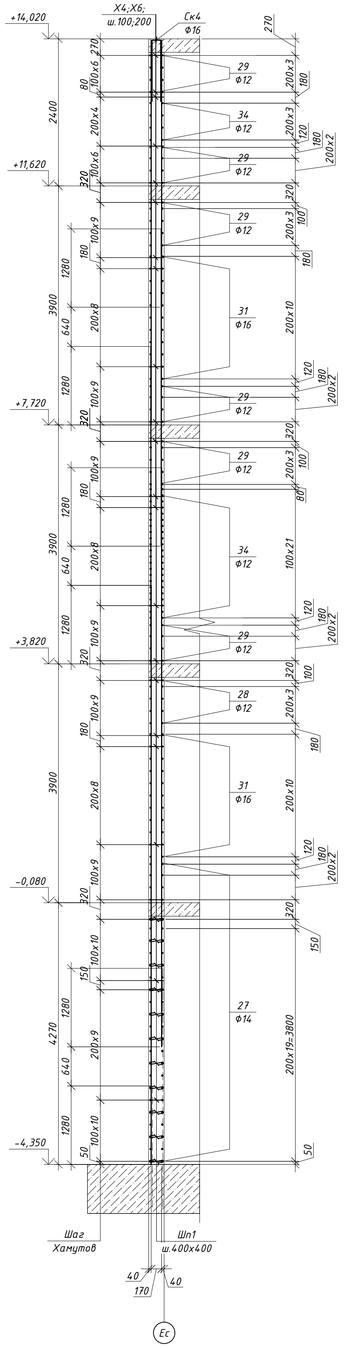


Разрез 2 - 2 (армирование)

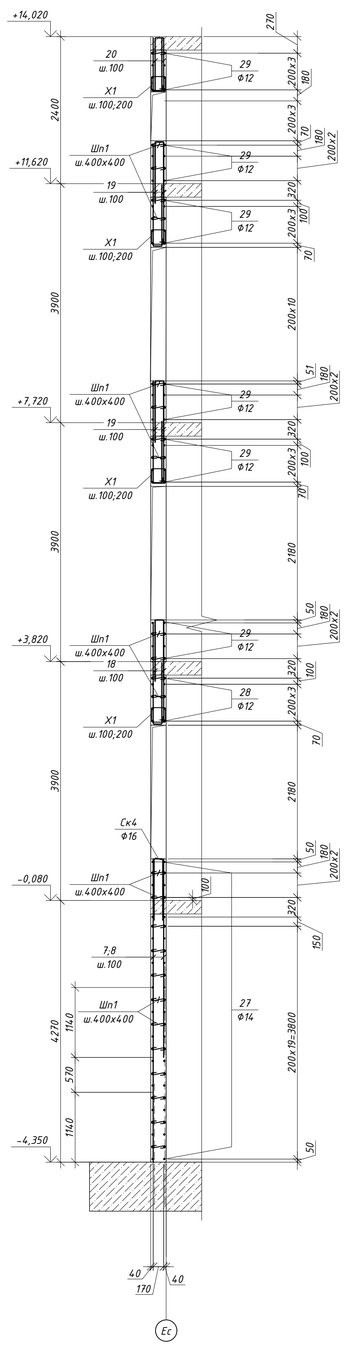


Разрез 3 - 3 (армирование)

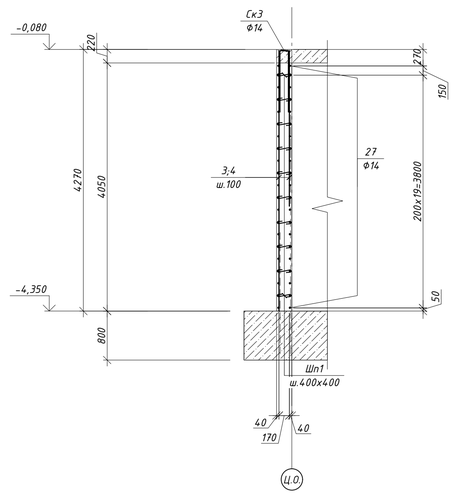

Разрез 7 - 7 (армирование)

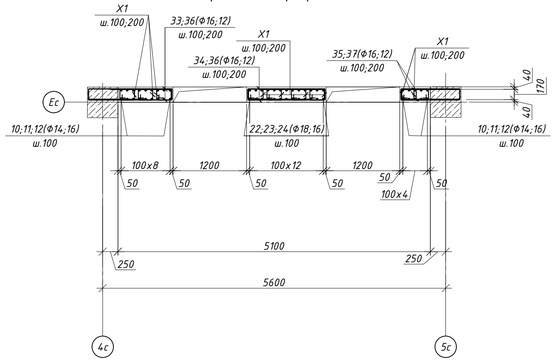

Разрез 8 - 8 (армирование)

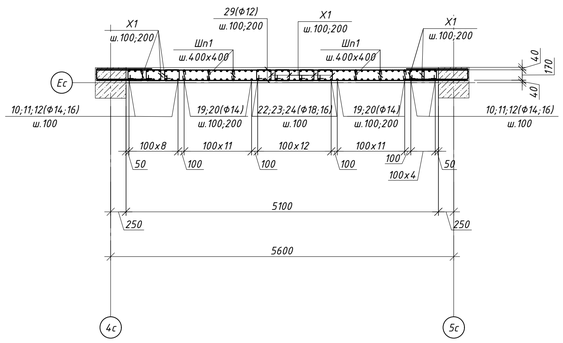

1. Общие указания см. л. - 1.
2. Данный лист читать совместно с л. КЖ- 2.1 ... 2.7; 5.31 ... 5.34
3. Стыки рабочей арматуры внахлестку без сварки, на скрутках из вязальной проволоки не менее 3 шт. на стык. Длина нахлеста 71d. Стыки располагать вразбежку, чтобы площадь рабочей арматуры, стыкуемой в одном сечении, не превышала 50%.
4. Расход арматуры в погонных метрах приведен с учетом нахлеста.
5. Стержни, указанные в "Ведомости деталей", должны гнуться механическим способом в холодном состоянии с радиусом гиба 3d - 5d, где d - диаметр стержня
6. Узел стыковки арматуры нахлеста и анкеровки смотреть на листе 5.1

						65П-АИП-2024-1-КЖ	
						Строительство многопрофильной больницы на 250 коек с онкологическим центром и поликлиникой на 350 посещений, по адресу: Медеуский район, г. Алматы	
Изм.	Кол.уч	Лист	N док.	Подп.	Дата		
						"Блок 1 Секция 1"	Стадия: РП; Лист: 5.33; Листов:
ГКП		Курал М					
Проверил		Кыдырбай А				Опалубочный чертеж монолитной стены по оси Ес стена Ст-9 (тол.250мм)	АстанаИнжПроект
Разраб.		Ауез Б					
Н.контроль		Ешенкулова					

Формат А1

Спецификация элементов

Поз.	Обозначение	Наименование	Кол.	Масса ед.кг	Примечание
		По оси Ес стена См-9			10690.77
Шп1	ГОСТ 34028-2016(214-210-0101-0002)	ф 8 А 240 L= 370	932	0.15	136.07
Х1	ГОСТ 34028-2016(214-210-0101-0002)	ф 8 А 240 L= 980	1836	0.39	709.97
Х2	ГОСТ 34028-2016(214-210-0101-0002)	ф 8 А 240 L= 880	118	0.35	40.97
Ск2	ГОСТ 34028-2016(214-210-0502-0001)	ф 12 А500С L= 1890	62	1.68	104.03
Ск3	ГОСТ 34028-2016(214-210-0502-0002)	ф 14 А500С L= 2170	198	2.62	519.21
Ск4	ГОСТ 34028-2016(214-210-0502-0003)	ф 16 А500С L= 2450	46	3.87	177.88
Ск6	ГОСТ 34028-2016(214-210-0502-0003)	ф 16 А500С L= 570	26	0.90	23.39
1	ГОСТ 34028-2016(214-210-0502-0003)	ф 16 А500С L= 4250	19	6.71	127.45
2	ГОСТ 34028-2016(214-210-0502-0003)	ф 16 А500С L= 2540	19	4.01	76.17
3	ГОСТ 34028-2016(214-210-0502-0002)	ф 14 А500С L= 4250	125	5.14	641.97
4	ГОСТ 34028-2016(214-210-0502-0002)	ф 14 А500С L= 2750	125	3.32	415.39
5	ГОСТ 34028-2016(214-210-0502-0002)	ф 14 А500С L= 4950	12	5.98	71.78
6	ГОСТ 34028-2016(214-210-0502-0002)	ф 14 А500С L= 3450	12	4.17	50.03
7	ГОСТ 34028-2016(214-210-0502-0003)	ф 16 А500С L= 4950	12	7.81	93.75
8	ГОСТ 34028-2016(214-210-0502-0003)	ф 16 А500С L= 3240	12	5.11	61.37
9	ГОСТ 34028-2016(214-210-0502-0003)	ф 16 А500С L= 9310	18	14.69	264.50
10	ГОСТ 34028-2016(214-210-0502-0003)	ф 16 А500С L= 5040	18	7.95	143.19
11	ГОСТ 34028-2016(214-210-0502-0002)	ф 14 А500С L= 6280	9	7.59	68.30
12	ГОСТ 34028-2016(214-210-0502-0002)	ф 14 А500С L= 4570	9	5.52	49.70
13	ГОСТ 34028-2016(214-210-0502-0003)	ф 16 А500С L= 9100	10	14.36	143.63
14	ГОСТ 34028-2016(214-210-0502-0002)	ф 14 А500С L= 4900	5	5.92	29.61
15	ГОСТ 34028-2016(214-210-0502-0002)	ф 14 А500С L= 4690	5	5.67	28.34
16	ГОСТ 34028-2016(214-210-0502-0002)	ф 14 А500С L= 6280	5	7.59	37.94
17	ГОСТ 34028-2016(214-210-0502-0002)	ф 14 А500С L= 4780	5	5.78	28.88
18*	ГОСТ 34028-2016(214-210-0502-0003)	ф 16 А500С L= 2990	24	4.72	113.26
19*	ГОСТ 34028-2016(214-210-0502-0002)	ф 14 А500С L= 2850	120	3.44	413.28
20*	ГОСТ 34028-2016(214-210-0502-0002)	ф 14 А500С L= 1890	28	2.28	63.95
21	ГОСТ 34028-2016(214-210-0502-0004)	ф 18 А500С L= 9450	26	18.88	490.81
22	ГОСТ 34028-2016(214-210-0502-0004)	ф 18 А500С L= 5180	26	10.35	269.03
23	ГОСТ 34028-2016(214-210-0502-0003)	ф 16 А500С L= 6280	13	9.91	128.86
24	ГОСТ 34028-2016(214-210-0502-0003)	ф 16 А500С L= 4360	13	6.88	89.46
25	ГОСТ 34028-2016(214-210-0502-0005)	ф 20 А500С L= пог.м.	348.35	2.47	859.08
26	ГОСТ 34028-2016(214-210-0502-0002)	ф 14 А500С L= пог.м.	723.49	1.21	874.28
27	ГОСТ 34028-2016(214-210-0502-0002)	ф 14 А500С L= 6160	8	7.44	59.55
28	ГОСТ 34028-2016(214-210-0502-0001)	ф 12 А500С L= 6160	10	5.47	54.69
29	ГОСТ 34028-2016(214-210-0502-0001)	ф 12 А500С L= 6060	52	5.38	279.77
30*	ГОСТ 34028-2016(214-210-0502-0003)	ф 16 А500С L= 2720	22	4.29	94.45
31*	ГОСТ 34028-2016(214-210-0502-0003)	ф 16 А500С L= 2570	44	4.06	178.48
32*	ГОСТ 34028-2016(214-210-0502-0003)	ф 16 А500С L= 2390	22	3.77	82.99
33*	ГОСТ 34028-2016(214-210-0502-0003)	ф 16 А500С L= 2390	44	3.77	165.98
34*	ГОСТ 34028-2016(214-210-0502-0003)	ф 16 А500С L= 2290	52	3.61	187.95
35*	ГОСТ 34028-2016(214-210-0502-0001)	ф 12 А500С L= 1990	44	1.77	77.74
36*	ГОСТ 34028-2016(214-210-0502-0003)	ф 16 А500С L= 2670	30	4.21	126.42
37*	ГОСТ 34028-2016(214-210-0502-0003)	ф 16 А500С L= 2090	30	3.30	98.96
38	ГОСТ 34028-2016(214-210-0502-0001)	ф 12 А500С L= 2250	14	2.00	27.97
39	ГОСТ 34028-2016(214-210-0502-0001)	ф 12 А500С L= 2700	12	2.40	28.77
40	ГОСТ 34028-2016(214-210-0502-0004)	ф 18 А500С L= 2700	10	5.39	53.93
41	ГОСТ 34028-2016(214-210-0502-0004)	ф 18 А500С L= 11130	12	22.23	266.80
42	ГОСТ 34028-2016(214-210-0502-0002)	ф 14 А500С L= 5300	6	6.40	38.43
43	ГОСТ 34028-2016(214-210-0502-0003)	ф 16 А500С L= 5800	12	9.15	109.85
44	ГОСТ 34028-2016(214-210-0502-0004)	ф 18 А500С L= 6000	12	11.99	143.83
45	ГОСТ 34028-2016(214-210-0502-0001)	ф 12 А500С L= 5300	12	4.71	56.46
46	ГОСТ 34028-2016(214-210-0502-0004)	ф 18 А500С L= 3050	6	6.09	36.56
47	ГОСТ 34028-2016(214-210-0502-0002)	ф 14 А500С L= 2050	6	2.48	14.86
48	ГОСТ 34028-2016(214-210-0502-0004)	ф 18 А500С L= 4250	11	8.49	93.39
49	ГОСТ 34028-2016(214-210-0502-0004)	ф 18 А500С L= 3780	11	7.55	83.06
50	ГОСТ 34028-2016(214-210-0502-0001)	ф 12 А500С L= 4950	14	4.39	61.53
51	ГОСТ 34028-2016(214-210-0502-0001)	ф 12 А500С L= 2960	14	2.63	36.79
52	ГОСТ 34028-2016(214-210-0502-0003)	ф 16 А500С L= пог.м.	561.39	1.58	886.07
		Материалы:			
	(212-101-0902)	Класс бетона С 20/25 (B25) W6 F100, м^3			22.18
	(212-101-0901)	Класс бетона С 20/25 (B25), м^3			12.37

Позиции со "*" см. "Ведомость деталей" см. на данном листе.

1. Общие указания см. л. - 1.
2. Данный лист читать совместно с л. КЖ- 2.1 ... 2.7; 5.31 ... 5.34
3. Стыки рабочей арматуры внахлестку без сварки, на скрутках из вязальной проволоки не менее 3 шт. на стык. Длина нахлеста 71d. Стыки располагать вразбежку, чтобы площадь рабочей арматуры, стыкуемой в одном сечении, не превышала 50%.
4. Расход арматуры в погонных метрах приведен с учетом нахлеста.
5. Стержни, указанные в "Ведомости деталей", должны гнуться механическим способом в холодном состоянии с радиусом гиба 3d - 5d, где d - диаметр стержня
6. Узел стыковки арматуры нахлеста и анкеровки смотреть на листе 5.1

Ведомость деталей

Поз.	Эскиз	Поз.	Эскиз	Поз.	Эскиз
Шп1	170, 100, 100; по в.г. L=370	18*	1680, 170, 1140; по н.г. L=2990	34*	1260, 170, 860; по н.г. L=2290
Х1	320, 170, 270, 220; по в.г. L=980	19*	1680, 170, 1000; по н.г. L=2850	35*	960, 170, 860; по н.г. L=1990
Х2	270, 170, 270, 170; по в.г. L=880	20*	860, 170, 860; по н.г. L=1890	36*	1360, 170, 1140; по н.г. L=2670
Ск2	860, 170, 860; по н.г. L=1890	30*	1410, 170, 1140; по н.г. L=2720	37*	960, 170, 960; по н.г. L=2090
Ск3	1000, 170, 1000; по н.г. L=2170	31*	1260, 170, 1140; по н.г. L=2570	49*	1280, 170, 2330; по н.г. L=3780
Ск4	1140, 170, 1140; по н.г. L=2450	32*	1110, 170, 1110; по н.г. L=2390		
Ск6	200, 170, 200; по н.г. L=570	33*	1360, 170, 860; по н.г. L=2390		

Ведомость расхода стали, кг


Марка элемента	Изделия арматурные									Всего
	Арматура класса									
	А240 ГОСТ 34028-2016(214-210-0101)		А500С ГОСТ 34028-2016(214-210-0502)(214-210-0501)							
	ф8	Итого	ф10	ф12	ф14	ф16	ф18	ф20	Итого	
По оси Ес стена См-9	887.01	887.01	266.80	727.74	3405.49	3374.05	1170.60	859.08	9803.76	10690.77


							65П-АИП-2024-1-КЖ
							Строительство многопрофильной больницы на 250 коек с онкологическим центром и поликлиникой на 350 посещений, по адресу: Медеуский район, г. Алматы
Изм.	Кол.уч.	Лист	N док.	Подп.	Дата		
						"Блок 1 Секция 1"	Стадия: РП; Лист: 5.34; Листов:
ГКП		Курал М					
Проверил		Кыдырбай А				Спецификация стены См-9 (тол.200мм)	АстанаИнжПроект
Разраб.		Ауез Б					
Н.контроль		Ешенкулова					

Формат А2


Опалубочный чертеж монолитной стена См-10 (тол.200мм)

Разрез 1 - 1 (Опалубка)

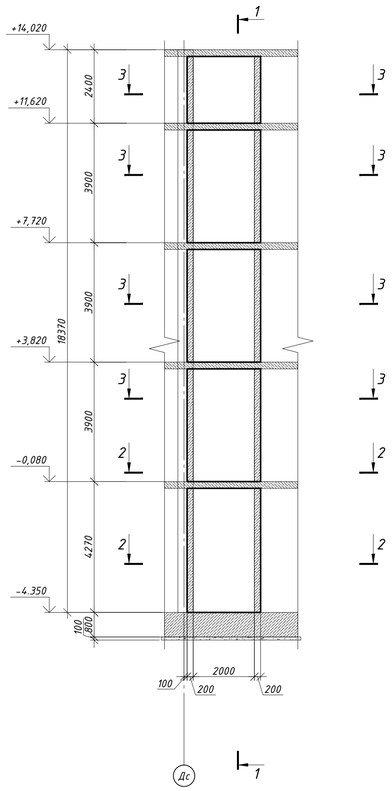


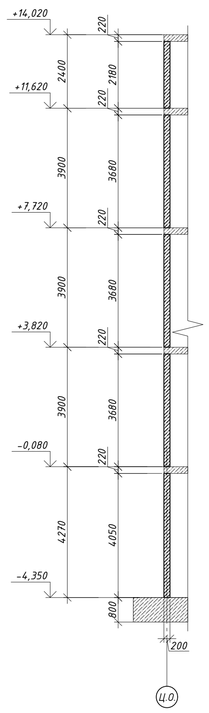


Основное вертикальное армирование монолитной стены См-10 (тол.200мм)

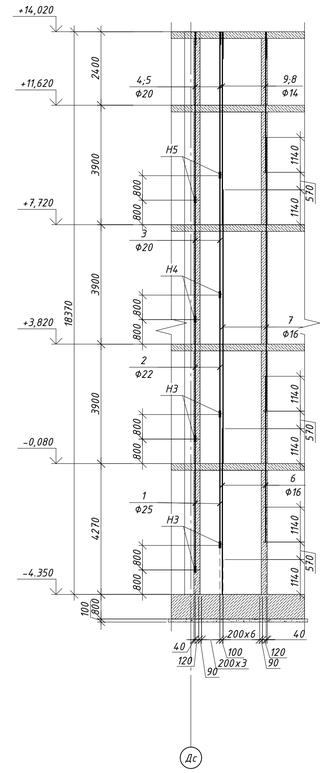


Дополнительное вертикальное армирование монолитной стены См-10 (тол.200мм)

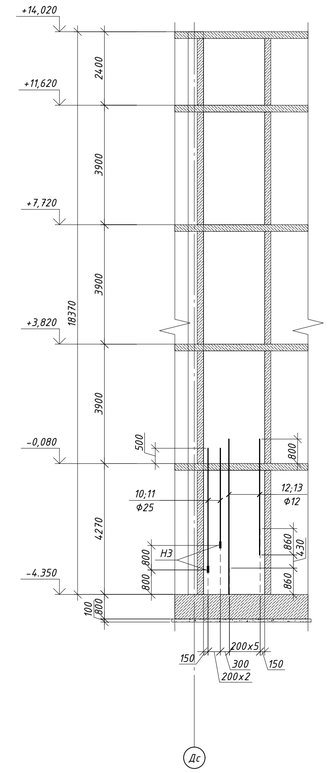


Основное горизонтальное армирование монолитной стены См-10 (тол.200мм)

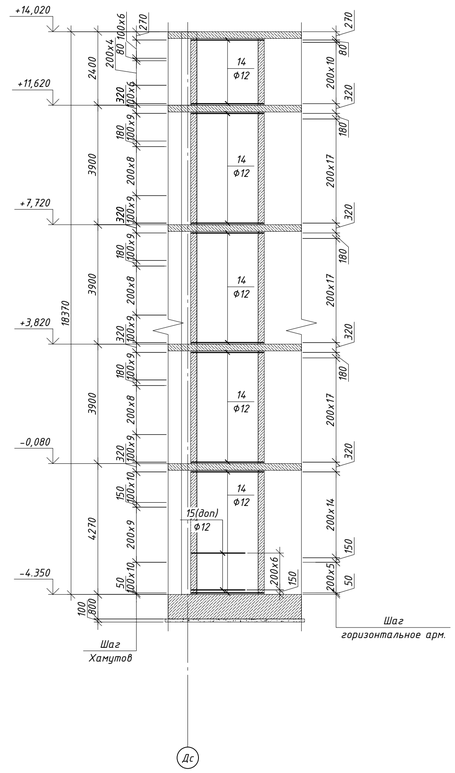


Разрез 2 - 2; 3 - 3; (Опалубка)

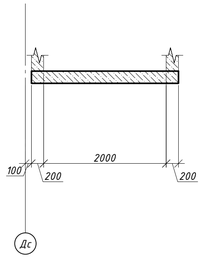


Разрез 3 - 3 (армирование)

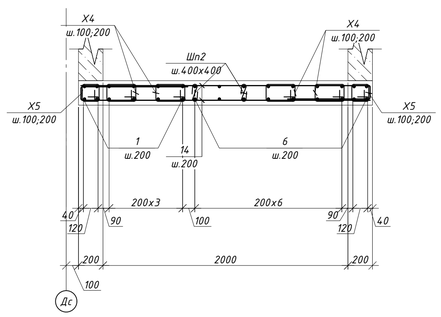


Анкеровка

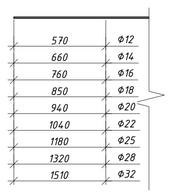

Узел стыковки вертикальной арматуры в нахлест и накладка

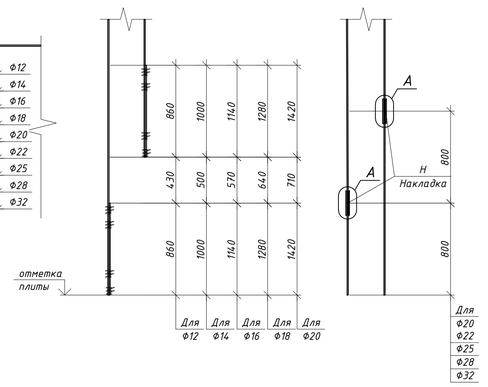

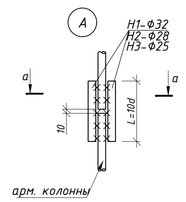


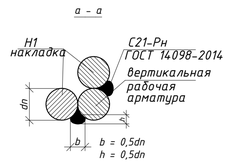



Таблица размеров Накладка

Марка эл-та	dн	L	вес
	мм.		кг.
H1	32	320	2.01
H2	28	280	1.35
H3	25	250	0.96
H4	22	220	0.66
H5	20	200	0.49


Разрез 2 - 2 (армирование)

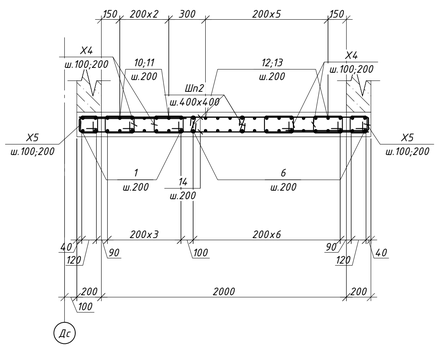


Фрагмент обрамления проема

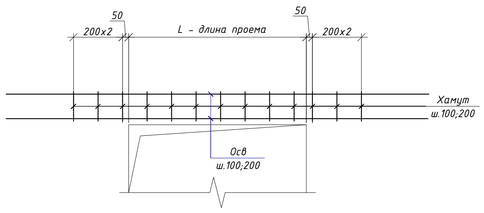

Узел стыковки Горизонтальной арматуры в нахлест

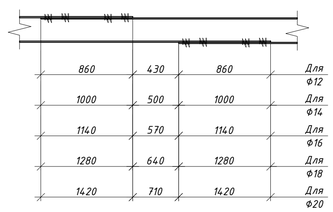


Б

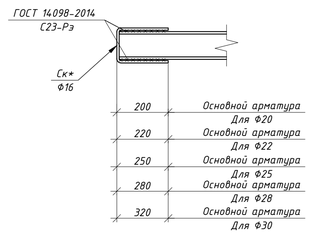

1. Общие указания см. л. - 1.
2. Данный лист читать совместно с л. КЖ- 2.1 ... 2.7; 5.35 ... 5.36
3. Стыки рабочей арматуры внахлестку без сварки, на скрутках из вязальной проволоки не менее 3 шт. на стык. Длина нахлеста 71d. Стыки располагать вразбежку, чтобы площадь рабочей арматуры, стыкуемой в одном сечении, не превышала 50%.
4. Расход арматуры в погонных метрах приведен с учетом нахлеста.
5. Стержни, указанные в "Ведомости деталей", должны гнуться механическим способом в холодном состоянии с радиусом гиба 3d - 5d, где d - диаметр стержня
6. Узел стыковки арматуры нахлеста и анкеровки смотреть на листе 5.1

						65П-АИП-2024-1-КЖ	
						Строительство многопрофильной больницы на 250 коек с онкологическим центром и поликлиникой на 350 посещений, по адресу: Медеуский район, г. Алматы	
Изм.	Кол.уч	Лист	N док.	Подп.	Дата		
						"Блок 1 Секция 1"	Стадия: РП; Лист: 5.35; Листов:
ГКП		Курал М					
Проверил		Кыдырбай А					
Разраб.		Ауез Б				Спецификация стены См-10 (тол.200мм)	АстанаИнжПроект
Н.контроль		Ешенкулова					Формат А1

Разрез 1 – 1 (армирование)

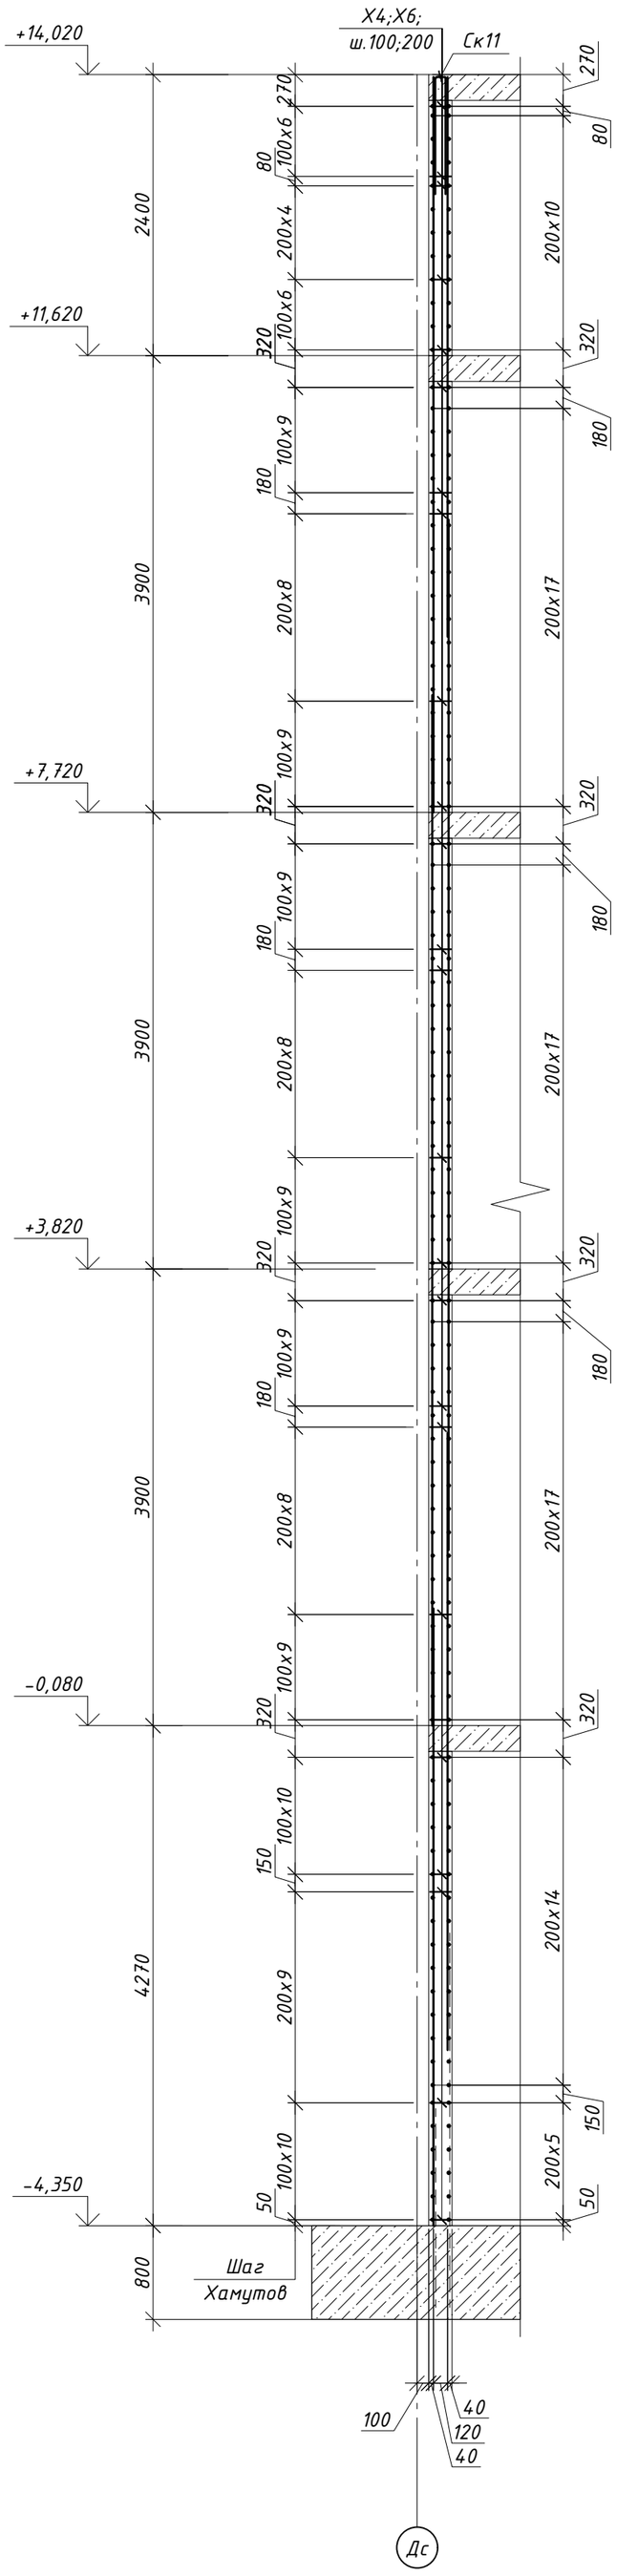

Спецификация элементов

Поз.	Обозначение	Наименование	Кол.	Масса ед.кг	Примечание
		Стена См-10			2207.30
X4*	ГОСТ 34028-2016(214-210-0101-0002)	ф 8 А 240 L= 880	532	0.35	184.73
X5*	ГОСТ 34028-2016(214-210-0101-0002)	ф 8 А 240 L= 740	266	0.29	77.67
Ск12*	ГОСТ 34028-2016(214-210-0502-0001)	ф 12 А500С L= 2120	6	1.88	11.29
Ск15*	ГОСТ 34028-2016(214-210-0502-0003)	ф 16 А500С L= 520	9	0.82	7.39
1	ГОСТ 34028-2016(214-210-0502-0007)	ф 25 А500С L= 4270	12	16.45	197.45
2	ГОСТ 34028-2016(214-210-0502-0006)	ф 22 А500С L= 3900	12	11.64	139.65
3	ГОСТ 34028-2016(214-210-0502-0005)	ф 20 А500С L= 3900	12	9.62	115.42
4	ГОСТ 34028-2016(214-210-0502-0005)	ф 20 А500С L= 5480	6	13.51	81.09
5	ГОСТ 34028-2016(214-210-0502-0005)	ф 20 А500С L= 5850	6	14.43	86.56
6	ГОСТ 34028-2016(214-210-0502-0003)	ф 16 А500С L= 5410	18	8.54	153.70
7	ГОСТ 34028-2016(214-210-0502-0003)	ф 16 А500С L= 8940	18	14.11	253.99
8	ГОСТ 34028-2016(214-210-0502-0002)	ф 14 А500С L= 6280	9	7.59	68.30
9	ГОСТ 34028-2016(214-210-0502-0002)	ф 14 А500С L= 5470	9	6.61	59.49
10	ГОСТ 34028-2016(214-210-0502-0007)	ф 25 А500С L= 3970	3	15.30	45.89
11	ГОСТ 34028-2016(214-210-0502-0007)	ф 25 А500С L= 3170	3	12.22	36.65
12	ГОСТ 34028-2016(214-210-0502-0001)	ф 12 А500С L= 5070	6	4.50	27.01
13	ГОСТ 34028-2016(214-210-0502-0001)	ф 12 А500С L= 3780	6	3.36	20.14
14*	ГОСТ 34028-2016(214-210-0502-0001)	ф 12 А500С L= 3340	180	2.97	533.75
15	ГОСТ 34028-2016(214-210-0502-0001)	ф 12 А500С L= 1750	14	1.55	21.75
Н3	ГОСТ 34028-2016(214-210-0502-0007)	ф 25 А500С L= 250	60	0.96	57.80
Н4	ГОСТ 34028-2016(214-210-0502-0006)	ф 22 А500С L= 220	24	0.66	15.76
Н5	ГОСТ 34028-2016(214-210-0502-0005)	ф 20 А500С L= 200	24	0.49	11.84
		Материалы:			
	(212-101-0901)	Класс бетона С 20/25 (В25), м³			8.29

Позиции со "*" см. "Ведомость деталей" см. на данном листе.

Ведомость деталей

Поз.	Эскиз	Поз.	Эскиз
X4	320; 120; 220; 220; по в.г. L=880	16	2360; 120; 860; по н.г. L=3340
X5	220; 120; 220; 120; по в.г. L=680	Ск11	860; 120; 860; по н.г. L=1840
		Ск15	200; 120; 200; по н.г. L=520

Ведомость расхода стали, кг

Марка элемента	Изделия арматурные											Всего
	Арматура класса											
	А240		А500С									
	ГОСТ 34028-2016(214-210-0101)		ГОСТ 34028-2016(214-210-0502)									
	ф8	Итого	ф10	ф12	ф14	ф16	ф18	ф20	ф22	ф25	Итого	
Стена См-10	262.40	262.40	0.00	613.94	127.79	415.07	0.00	294.90	155.41	337.79	1944.90	2207.30


1. Общие указания см. л. – 1.
2. Данный лист читать совместно с л. КЖ– 2.1 ... 2.7; 5.35 ... 5.36
3. Стыки рабочей арматуры внахлестку без сварки, на скрутках из вязальной проволоки не менее 3 шт. на стык. Длина нахлеста 71d. Стыки располагать вразбежку, чтобы площадь рабочей арматуры, стыкуемой в одном сечении, не превышала 50%.
4. Расход арматуры в погонных метрах приведен с учетом нахлеста.
5. Стержни, указанные в "Ведомости деталей", должны гнуться механическим способом в холодном состоянии с радиусом гиба 3d – 5d, где d – диаметр стержня
6. Узел стыковки арматуры нахлеста и анкеровки смотреть на листе 5.1

Изм.	Кол.уч.	Лист	N док.	Подп.	Дата	65П-АИП-2024-1-КЖ		
						Строительство многопрофильной больницы на 250 коек с онкологическим центром и поликлиникой на 350 посещений, по адресу: Медеуский район, г. Алматы		
ГКП		Курал М				"Блок 1 Секция 1"	Стадия: РП	Лист: 5.36 / Листов:
Проверил		Кыдырбай А				Стена См-10 (тол.200мм)	АстанаИнжПроект	
Разраб.		Ауез Б						
Н.контроль		Ешенкулова						


Формат А2


Опалубочный чертеж монолитной стена См-11 (тол.200мм)

Разрез 1 - 1 (Опалубка)

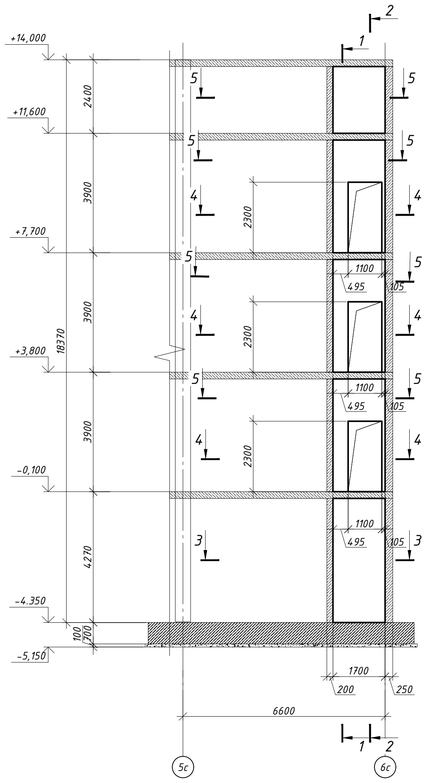


Разрез 1 - 1 (Опалубка)

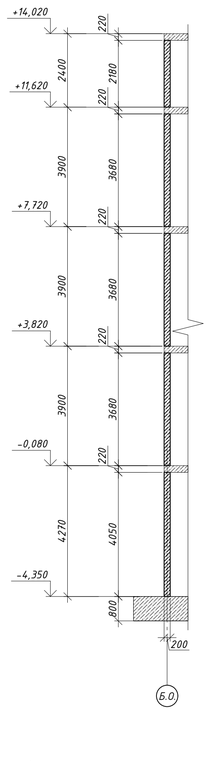


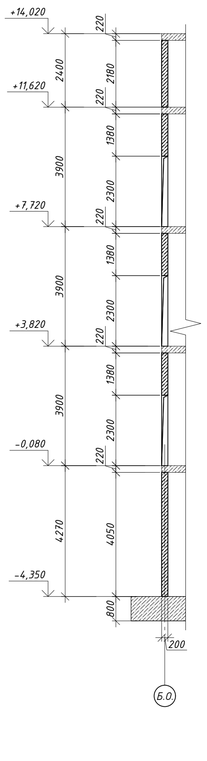


Основное вертикальное армирование монолитной стены См-11 (тол.200мм)

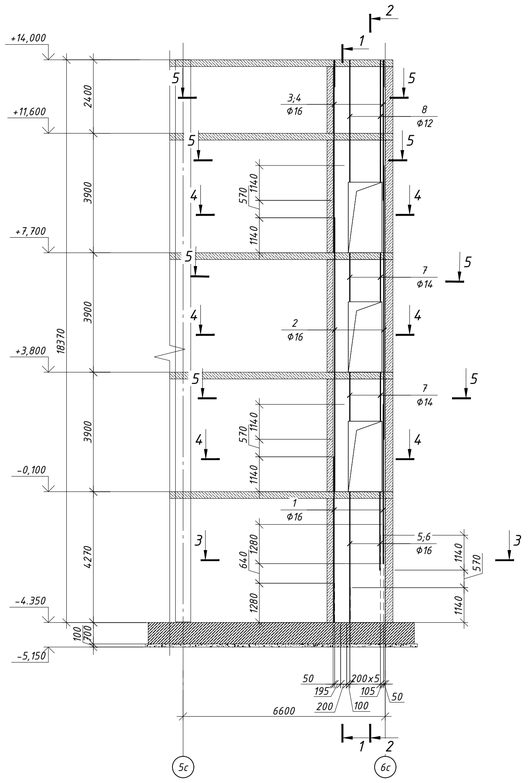


Основное горизонтальное армирование монолитной стены См-12 (тол.200мм)

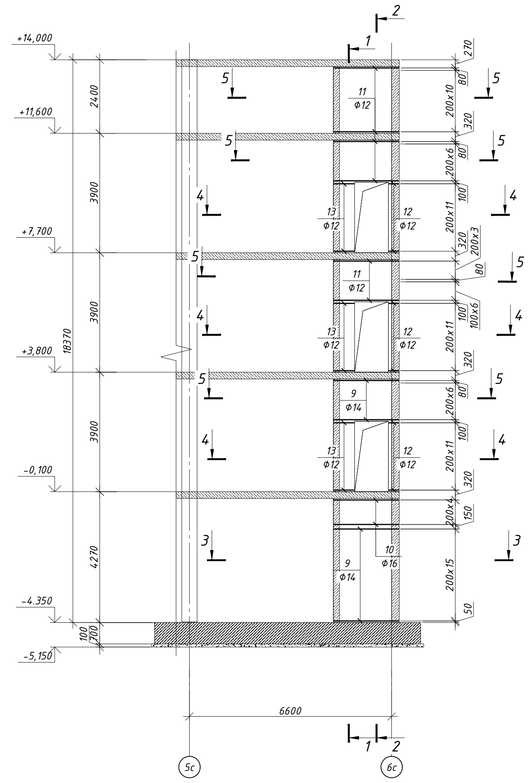


Разрез 3 - 3; 5 - 5; (Опалубка)

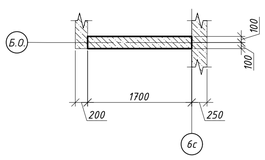


Разрез 4 - 4; (Опалубка)

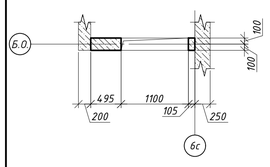


Разрез 4 - 4 (армирование)

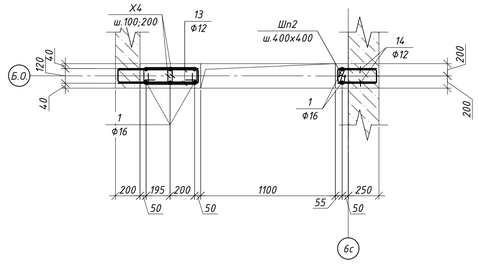

Разрез 3 - 3 (армирование)

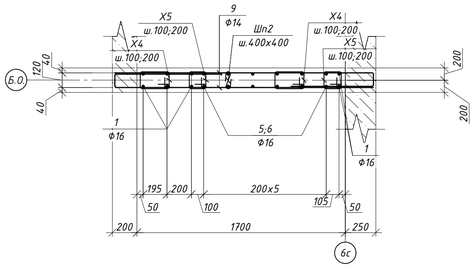


Разрез 5 - 5 (армирование)

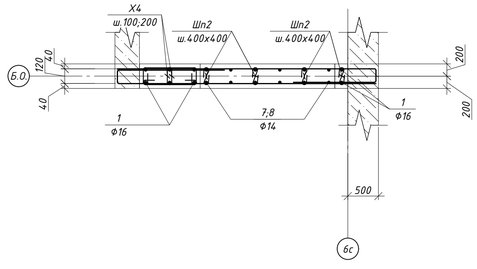


Анкеровка


570	Ф12
660	Ф14
760	Ф16
850	Ф18
940	Ф20
1040	Ф22
1180	Ф25
1320	Ф28
1510	Ф32

Узел стыковки вертикальной арматуры в нахлест и накладка

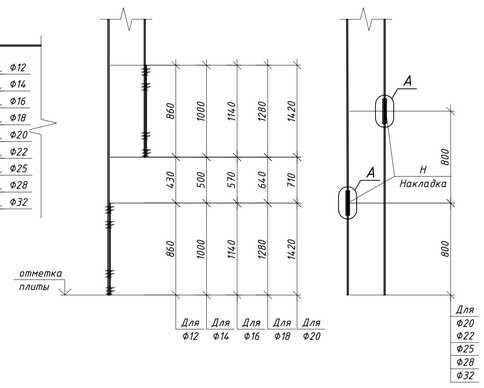


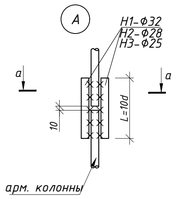


Узел стыковки горизонтальной арматуры в нахлест

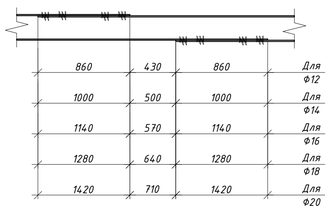

Б

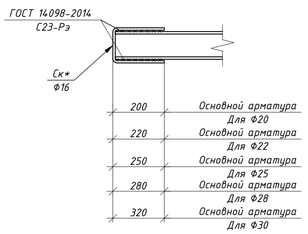

Фрагмент обрамления проема

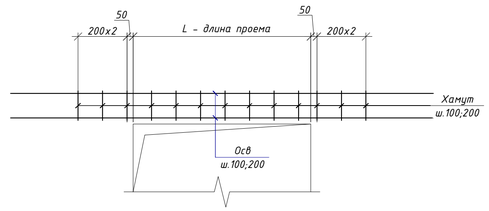

a - a

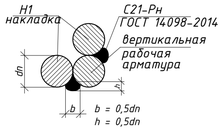


Таблица размеров Накладка

Марка эл-та	dн	L	вес
	мм.		кг.
H1	32	320	2.01
H2	28	280	1.35
H3	25	250	0.96
H4	22	220	0.66
H5	20	200	0.49

1. Общие указания см. л. - 1.
2. Данный лист читать совместно с л. КЖ- 2.1 ... 2.7; 5.37 ... 5.38
3. Стыки рабочей арматуры внахлестку без сварки, на скруткох из вязальной проволоки не менее 3 шт. на стык. Длина нахлеста 71d. Стыки располагать вразбежку, чтобы площадь рабочей арматуры, стыкуемой в одном сечении, не превышала 50%.
4. Расход арматуры в погонных метрах приведен с учетом нахлеста.
5. Стержни, указанные в "Ведомости деталей", должны гнуться механическим способом в холодном состоянии с радиусом гиба 3d - 5d, где d - диаметр стержня
6. Узел стыковки арматуры нахлеста и анкеровки смотреть на листе 5.1


							65П-АИП-2024-1-КЖ
							Строительство многопрофильной больницы на 250 коек с онкологическим центром и поликлиникой на 350 посещений, по адресу: Медеуский район, г. Алматы
Изм.	Колич	Лист	N док.	Подп.	Дата		
							"Блок 1 Секция 1"
ГКП		Курал М					
Проверил		Кыдырбай А					
Разраб.		Ауез Б					Стена См-11 (тол.200мм)
Н.контроль		Ешенкулова					

Стадия	Лист	Листов
РП	5.37	


АстанаИнжПроект

Формат А1

Разрез 1 – 1 (армирование)

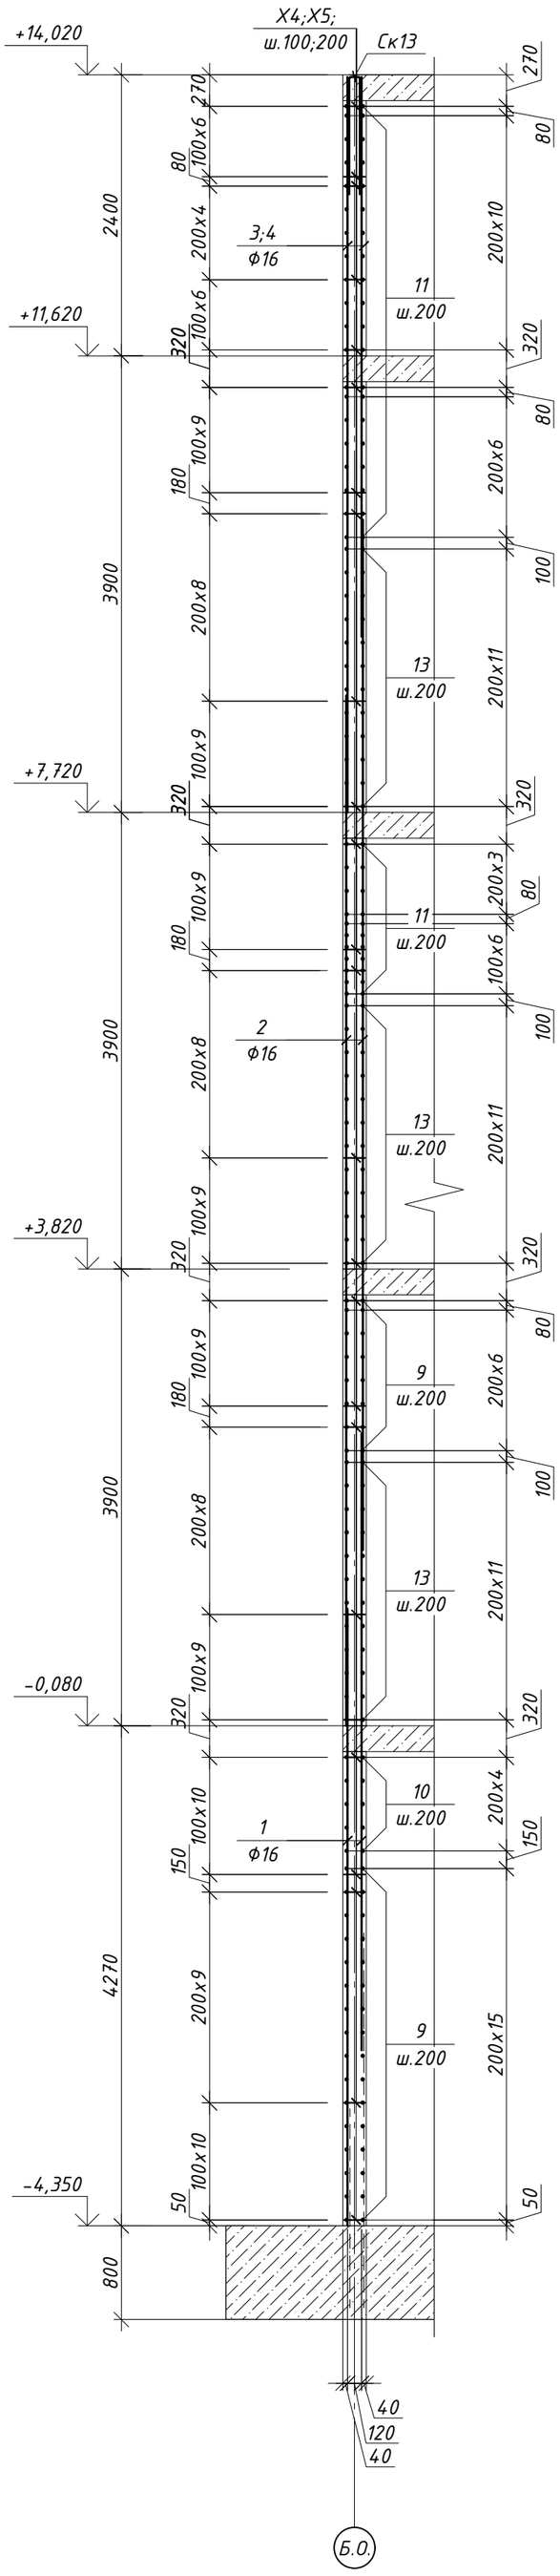

Разрез 2 – 2 (армирование)

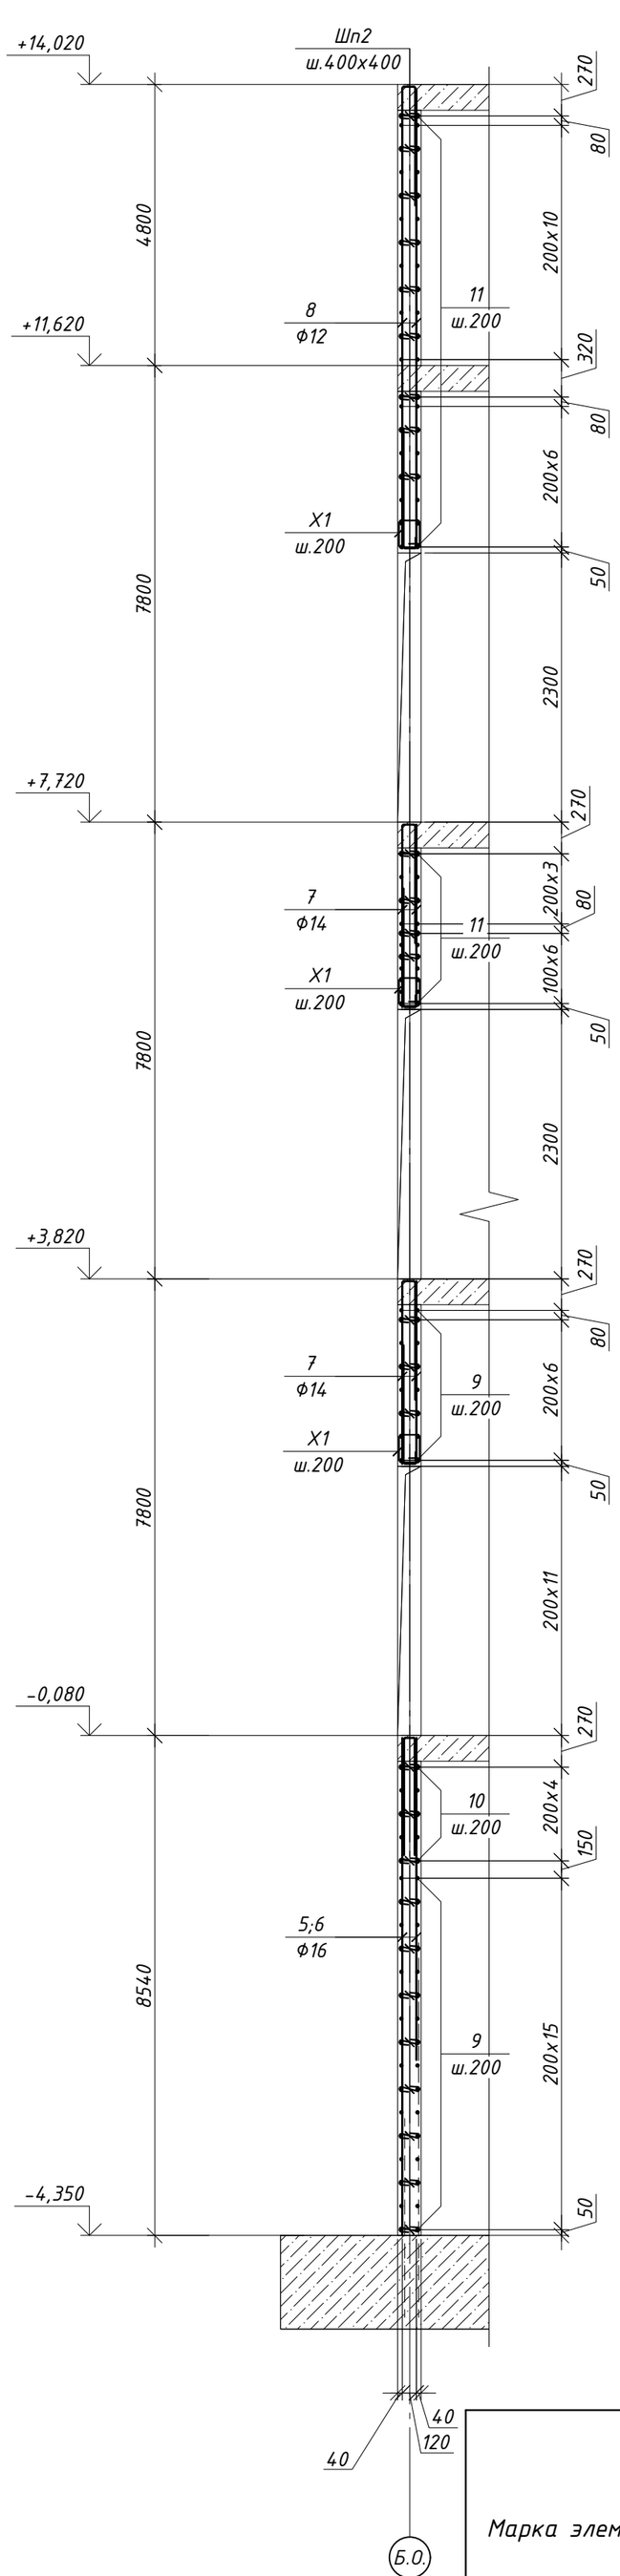

Спецификация элементов

Поз.	Обозначение	Наименование	Кол.	Масса ед.кг	Примечание
		Стена См-11			1161.16
X4*	ГОСТ 34028-2016(214-210-0101-0002)	ф 8 A 240 L= 880	310	0.35	107.64
X5*	ГОСТ 34028-2016(214-210-0101-0002)	ф 8 A 240 L= 740	60	0.29	17.52
Шп1*	ГОСТ 34028-2016(214-210-0101-0002)	ф 8 A 240 L= 320	180	0.13	22.73
Ск13*	ГОСТ 34028-2016(214-210-0502-0003)	ф 16 A500C L= 2400	5	3.79	18.94
1	ГОСТ 34028-2016(214-210-0502-0003)	ф 16 A500C L= 5410	8	8.54	68.31
2	ГОСТ 34028-2016(214-210-0502-0003)	ф 16 A500C L= 8940	8	14.11	112.88
3	ГОСТ 34028-2016(214-210-0502-0003)	ф 16 A500C L= 6280	4	9.91	39.65
4	ГОСТ 34028-2016(214-210-0502-0003)	ф 16 A500C L= 4570	4	7.21	28.85
5	ГОСТ 34028-2016(214-210-0502-0003)	ф 16 A500C L= 4250	6	6.71	40.25
6	ГОСТ 34028-2016(214-210-0502-0003)	ф 16 A500C L= 2540	6	4.01	24.05
7*	ГОСТ 34028-2016(214-210-0502-0002)	ф 14 A500C L= 2680	24	3.24	77.73
8*	ГОСТ 34028-2016(214-210-0502-0001)	ф 12 A500C L= 4940	12	4.39	52.63
9*	ГОСТ 34028-2016(214-210-0502-0002)	ф 14 A500C L= 3230	48	3.90	187.35
10*	ГОСТ 34028-2016(214-210-0502-0003)	ф 16 A500C L= 3370	10	5.32	53.19
11*	ГОСТ 34028-2016(214-210-0502-0001)	ф 12 A500C L= 3090	62	2.74	170.09
12*	ГОСТ 34028-2016(214-210-0502-0001)	ф 12 A500C L= 750	72	0.67	47.94
13*	ГОСТ 34028-2016(214-210-0502-0001)	ф 12 A500C L= 1430	72	1.27	91.41
		Материалы:			
	(212-101-0901)	Класс бетона С 20/25 (В25), м³			4.35

Позиции со "*" см. "Ведомость деталей" см. на данном листе.

Ведомость деталей

Поз.	Эскиз	Поз.	Эскиз
X4	320; 120; 220; 220; по в.г. L=880	7	1560; 120; 1000; по н.г. L=2680
X5	220; 120; 220; 120; по в.г. L=680	8	3960; 120; 860; по н.г. L=4940
Ск13	1140; 120; 1140; по н.г. L=2400	9	2110; 120; 1000; по н.г. L=3230
10	2110; 120; 1140; по н.г. L=3370	11	2110; 120; 860; по н.г. L=3090
12	315; 120; 315; по н.г. L=750	13	655; 120; 655; по н.г. L=1430

Ведомость расхода стали, кг

Марка элемента	Изделия арматурные								Всего
	Арматура класса								
	A240		A500C						
	ГОСТ 34028-2016(214-210-0101)		ГОСТ 34028-2016(214-210-0502)						
	ф8	Итого	ф10	ф12	ф14	ф16	ф18	Итого	
Стена См-11	147.89	147.89	0.00	362.07	265.08	386.12	0.00	1013.27	1161.16


1. Общие указания см. л. – 1.
2. Данный лист читать совместно с л. КЖ- 2.1 ... 2.7; 5.37 ... 5.38
3. Стыки рабочей арматуры внахлестку без сварки, на скрутках из вязальной проволоки не менее 3 шт. на стык. Длина нахлеста 71d. Стыки располагать вразбежку, чтобы площадь рабочей арматуры, стыкуемой в одном сечении, не превышала 50%.
4. Расход арматуры в погонных метрах приведен с учетом нахлеста.
5. Стержни, указанные в "Ведомости деталей", должны гнуться механическим способом в холодном состоянии с радиусом гиба 3d – 5d, где d – диаметр стержня
6. Узел стыковки арматуры нахлеста и анкеровки смотреть на листе 5.1

						65П-АИП-2024-1-КЖ
						Строительство многопрофильной больницы на 250 коек с онкологическим центром и поликлиникой на 350 посещений, по адресу: Медеуский район, г. Алматы
Изм.	Кол.уч.	Лист	N док.	Подп.	Дата	
ГКП		Курал М				"Блок 1 Секция 1"
Проверил		Кыдырбай А				Стадия: РП; Лист: 5.38; Листов:
Разраб.		Ауез Б				Стена См-11 (тол.200мм)
Н.контроль		Ешенкулова				АстанаИнжПроект


Формат А2

Опалубочный чертеж монолитной стена См-12 (тол.200мм)


Разрез 1 - 1 (Опалубка)

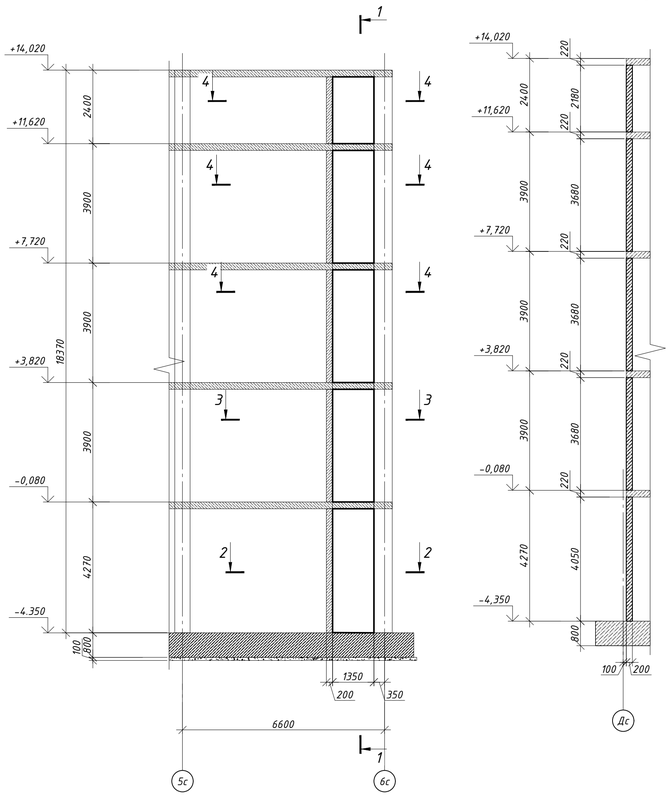


Основное вертикальное армирование монолитной стены См-12 (тол.200мм)

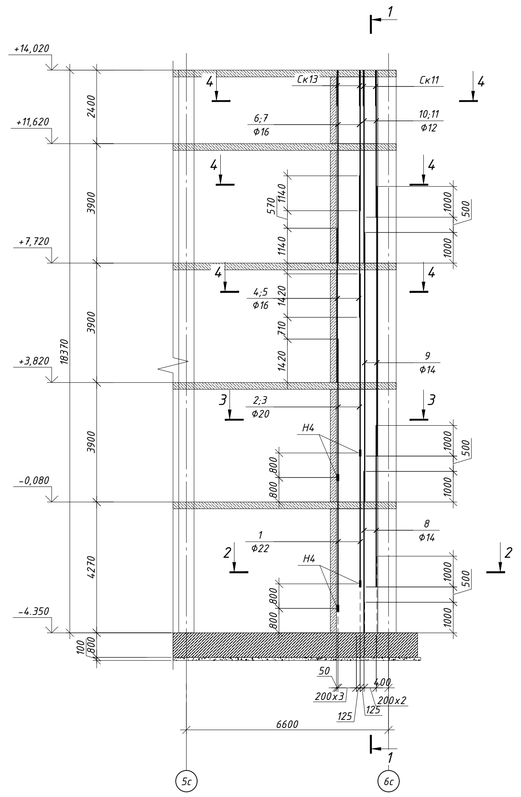


Дополнительное вертикальное армирование монолитной стены См-12 (тол.200мм)

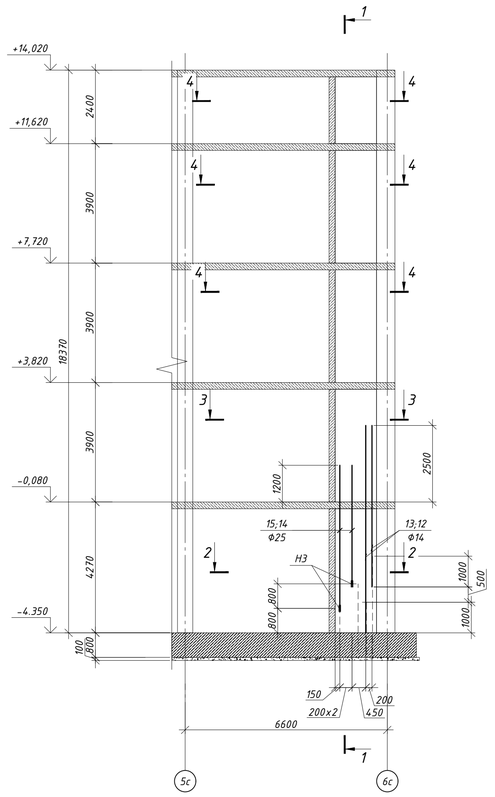


Основное горизонтальное армирование монолитной стены См-12 (тол.200мм)

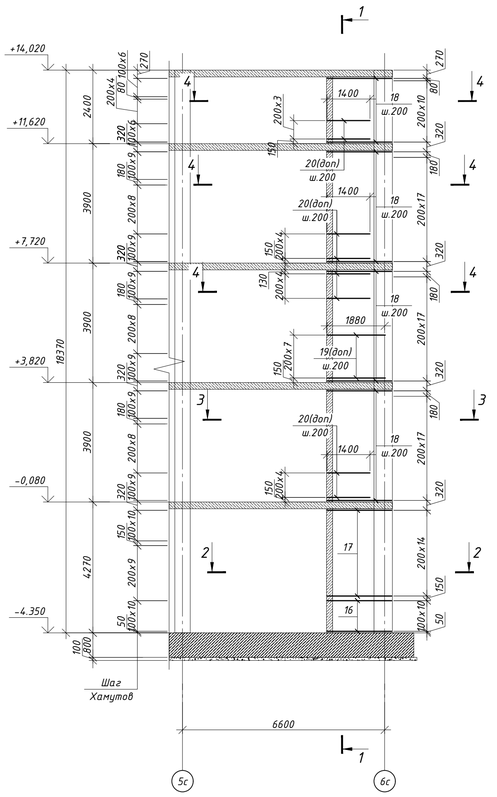


Разрез 2 - 2; 3 - 3; 4 - 4; (Опалубка)

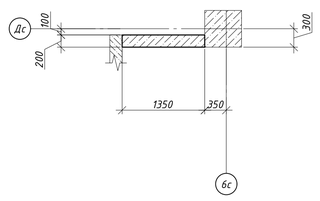


Разрез 2 - 2 (армирование)

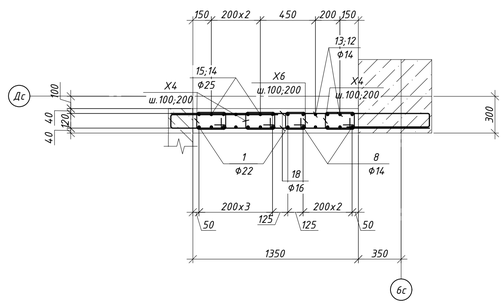


Разрез 3 - 3 (армирование)

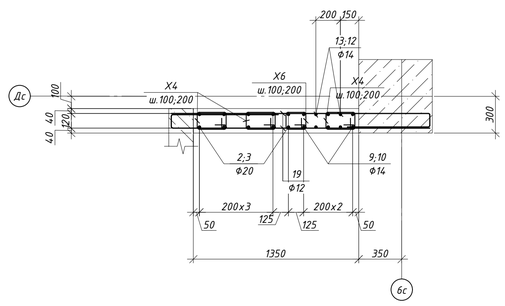


Разрез 4 - 4 (армирование)

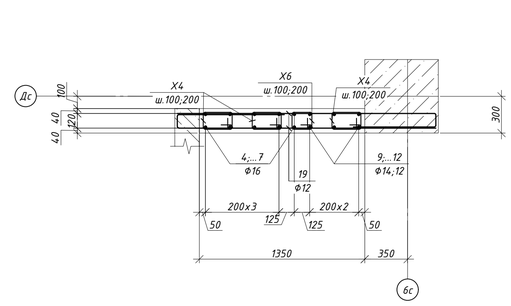


Анкеровка

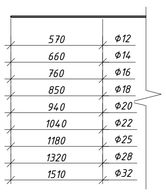


Узел стыковки вертикальной арматуры в нахлест и накладка

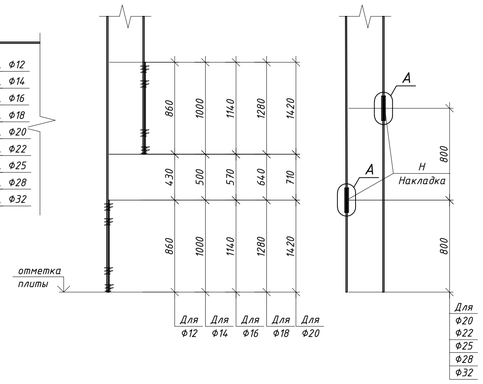

Узел стыковки Горизонтальной арматуры в нахлест

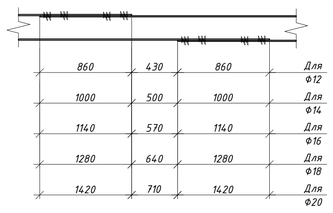

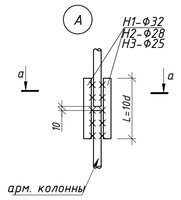

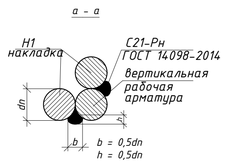



Таблица размеров Накладка

Марка эл-та	dн	L	вес
	мм.		кг.
Н1	32	320	2.01
Н2	28	280	1.35
Н3	25	250	0.96
Н4	22	220	0.66
Н5	20	200	0.49

1. Общие указания см. л. - 1.
2. Данный лист читать совместно с л. КЖ- 2.1 ... 2.7; 5.39 ... 5.40
3. Стыки рабочей арматуры внахлестку без сварки, на скруткаx из вязальной проволоки не менее 3 шт. на стык. Длина нахлеста 71d. Стыки располагать вразбежку, чтобы площадь рабочей арматуры, стыкуемой в одном сечении, не превышала 50%.
4. Расход арматуры в погонных метрах приведен с учетом нахлеста.
5. Стержни, указанные в "Ведомости деталей", должны гнуться механическим способом в холодном состоянии с радиусом гиба 3d - 5d, где d - диаметр стержня
6. Узел стыковки арматуры нахлеста и анкеровки смотреть на листе 5.1

Изм.	Колич.	Лист	N док.	Подп.	Дата	65П-АИП-2024-1-КЖ			
						Строительство многопрофильной больницы на 250 коек с онкологическим центром и поликлиникой на 350 посещений, по адресу: Медеуский район, г. Алматы			
						"Блок 1 Секция 1"	Стадия	Лист	Листов
							РП	5.39	
ГКП		Курал М				Стена См-12 (тол.200мм)	АстанаИнжПроект		
Проверил		Кыдырбай А							
Разраб.		Ауез Б							
Н.контроль		Ешенкулова					Формат	А1	

Разрез 1 – 1 (армирование)

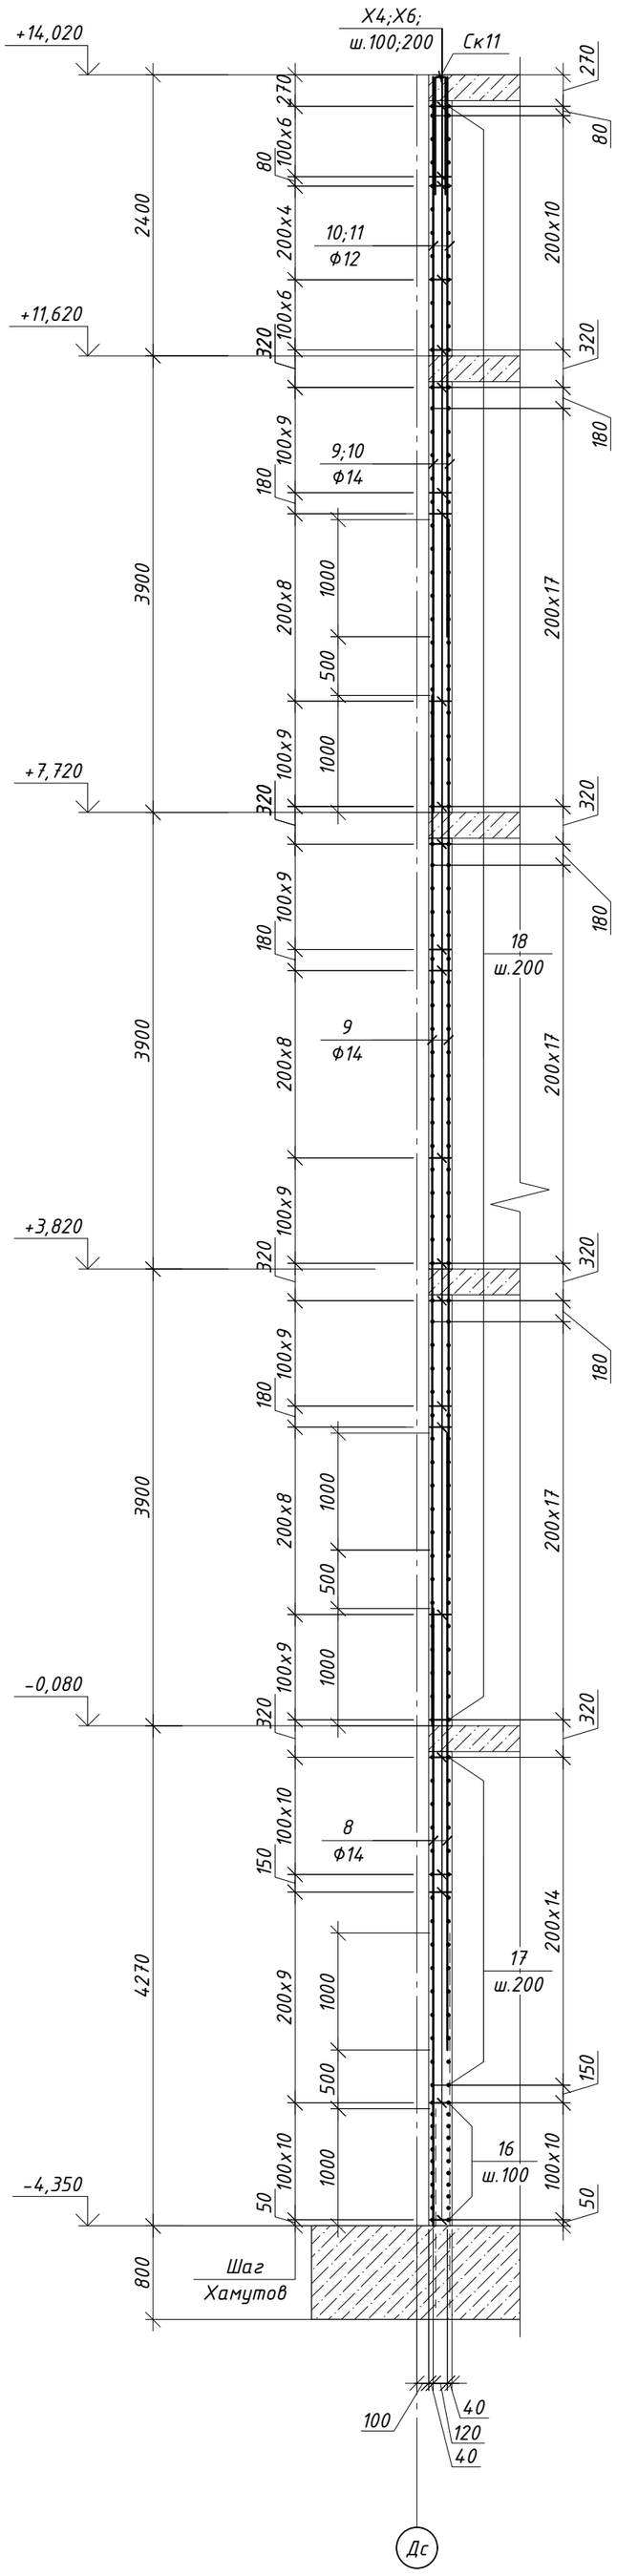

Спецификация элементов

Поз.	Обозначение	Наименование	Кол.	Масса ед.кг	Примечание
		Стена См-12			1578.26
X4*	ГОСТ 34028-2016(214-210-0101-0002)	ф 8 A 240 L= 880	400	0.35	138.89
X6*	ГОСТ 34028-2016(214-210-0101-0002)	ф 8 A 240 L= 740	133	0.29	38.83
Ск11*	ГОСТ 34028-2016(214-210-0502-0001)	ф 12 A500C L= 1840	3	1.63	4.90
Ск13*	ГОСТ 34028-2016(214-210-0502-0003)	ф 16 A500C L= 2400	5	3.79	18.94
Н3	ГОСТ 34028-2016(214-210-0502-0007)	ф 25 A500C L= 250	12	0.96	11.56
Н4	ГОСТ 34028-2016(214-210-0502-0006)	ф 22 A500C L= 220	20	0.66	13.13
1	ГОСТ 34028-2016(214-210-0502-0006)	ф 22 A500C L= 4270	10	12.74	127.42
2	ГОСТ 34028-2016(214-210-0502-0006)	ф 20 A500C L= 4520	5	11.15	55.73
3	ГОСТ 34028-2016(214-210-0502-0006)	ф 20 A500C L= 5850	5	14.43	72.13
4	ГОСТ 34028-2016(214-210-0502-0003)	ф 16 A500C L= 5040	5	7.95	39.77
5	ГОСТ 34028-2016(214-210-0502-0003)	ф 16 A500C L= 4620	5	7.29	36.46
6	ГОСТ 34028-2016(214-210-0502-0003)	ф 16 A500C L= 6280	5	9.91	49.56
7	ГОСТ 34028-2016(214-210-0502-0003)	ф 16 A500C L= 4570	5	7.21	36.06
8	ГОСТ 34028-2016(214-210-0502-0002)	ф 14 A500C L= 5270	6	6.37	38.21
9	ГОСТ 34028-2016(214-210-0502-0002)	ф 14 A500C L= 8800	6	10.63	63.80
10	ГОСТ 34028-2016(214-210-0502-0001)	ф 12 A500C L= 6280	3	5.58	16.73
11	ГОСТ 34028-2016(214-210-0502-0001)	ф 12 A500C L= 4780	3	4.24	12.73
12	ГОСТ 34028-2016(214-210-0502-0002)	ф 14 A500C L= 6770	2	8.18	16.36
13	ГОСТ 34028-2016(214-210-0502-0002)	ф 14 A500C L= 5270	2	6.37	12.74
14	ГОСТ 34028-2016(214-210-0502-0007)	ф 25 A500C L= 4670	3	18.00	53.99
15	ГОСТ 34028-2016(214-210-0502-0007)	ф 25 A500C L= 3870	3	14.91	44.74
16*	ГОСТ 34028-2016(214-210-0502-0002)	ф 14 A500C L= 3230	22	3.90	85.87
17*	ГОСТ 34028-2016(214-210-0502-0003)	ф 16 A500C L= 3370	30	5.32	159.57
18*	ГОСТ 34028-2016(214-210-0502-0001)	ф 12 A500C L= 3090	138	2.74	378.58
19	ГОСТ 34028-2016(214-210-0501-0005)	ф 10 A500C L= 1900	16	1.17	18.74
20	ГОСТ 34028-2016(214-210-0501-0005)	ф 10 A500C L= 1400	38	0.86	32.80
		Материалы:			
	(212-101-0901)	Класс бетона С 20/25 (В25), м³			4.66

Позиции со "*" см. "Ведомость деталей" см. на данном листе.

Ведомость деталей

Поз.	Эскиз	Поз.	Эскиз
X4	320; 120; 220; 220; по в.г. L=880	16	2110; 120; 1000; по н.г. L=3230
X5	220; 120; 220; 120; по в.г. L=680	17	2110; 120; 1140; по н.г. L=3370
Ск11	860; 120; 860; по н.г. L=1840	18	2110; 120; 860; по н.г. L=3090
Ск13	1140; 120; 1140; по н.г. L=2400		

Ведомость расхода стали, кг


Марка элемента	Изделия арматурные											Всего
	Арматура класса											
	A240		A500C									
	ГОСТ 34028-2016(214-210-0101)		ГОСТ 34028-2016(214-210-0502)(214-210-0501)									
	ф8	Итого	ф10	ф12	ф14	ф16	ф18	ф20	ф22	ф20	Итого	
Стена См-12	177.73	177.73	51.54	412.94	216.98	340.37	0.00	127.87	140.55	110.28	1400.53	1578.26

1. Общие указания см. л. – 1.
2. Данный лист читать совместно с л. КЖ- 2.1 ... 2.7; 5.39 ... 5.40
3. Стыки рабочей арматуры внахлестку без сварки, на скрутках из вязальной проволоки не менее 3 шт. на стык. Длина нахлеста 71d. Стыки располагать вразбежку, чтобы площадь рабочей арматуры, стыкуемой в одном сечении, не превышала 50%.
4. Расход арматуры в погонных метрах приведен с учетом нахлеста.
5. Стержни, указанные в "Ведомости деталей", должны гнуться механическим способом в холодном состоянии с радиусом гиба 3d – 5d, где d – диаметр стержня
6. Узел стыковки арматуры нахлеста и анкеровки смотреть на листе 5.1


Изм.	Кол.уч.	Лист	N док.	Подп.	Дата	65П-АИП-2024-1-КЖ		
						Строительство многопрофильной больницы на 250 коек с онкологическим центром и поликлиникой на 350 посещений, по адресу: Медеуский район, г. Алматы		
ГКП		Курал М				"Блок 1 Секция 1"	Стадия: РП	Лист: 5.40 / Листов:
Проверил		Кыдырбай А				Стена См-12 (тол.200мм)	АстанаИнжПроект	
Разраб.		Ауез Б						
Н.контроль		Ешенкулова						

Формат А2


Опалубочный чертеж монолитной стена Ст-13 (тол.200мм)

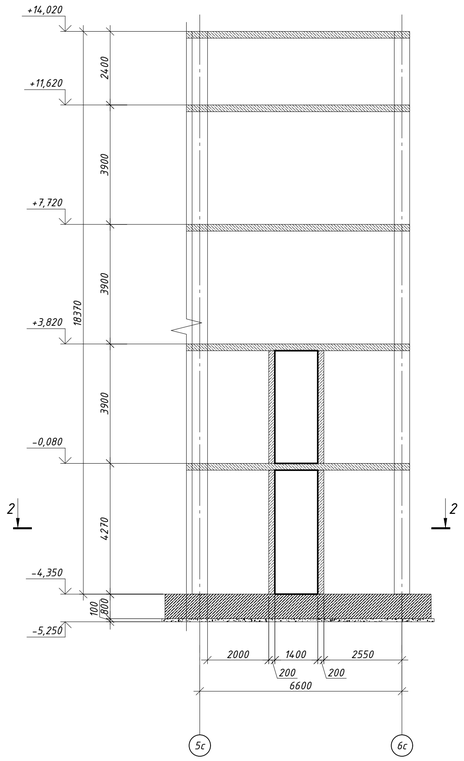

Разрез 1 - 1 (Опалубка)

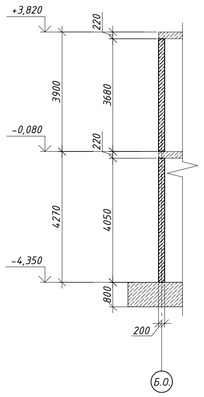


Разрез 2 - 2 (Опалубка)

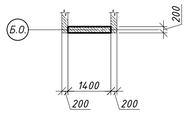


Разрез 2 - 2 (армирование)

Основное вертикальное армирование монолитной стены Ст-13 (тол.200мм)

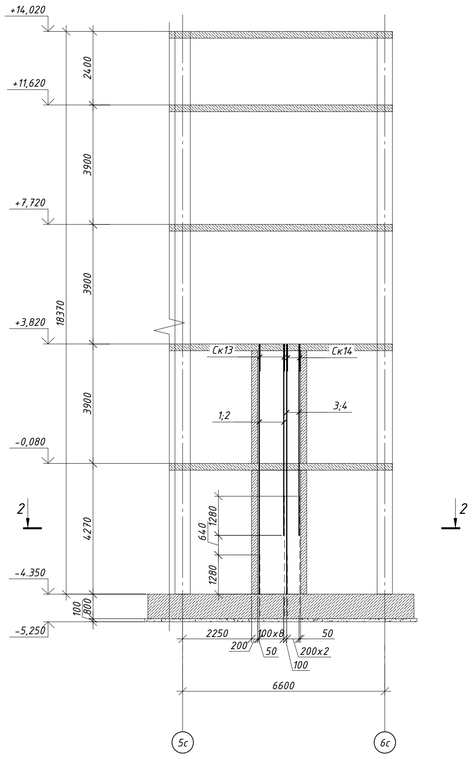


Основное горизонтальное армирование монолитной стены Ст-13 (тол.200мм)

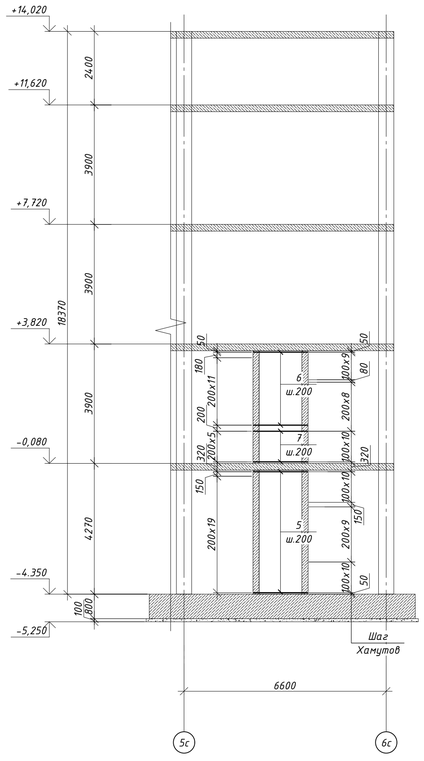


Ведомость деталей


Поз.	Эскиз
Х4	320, 120, 220 — по в.г. L=880
Шп2	120, 100, 100 — по в.г. L=320
Ск14	1280, 120, 1280 — по н.г. L=2680
Ск13	1140, 120, 1140 — по н.г. L=2400
5	1760, 120, 860 — по н.г. L=2740
6	1760, 120, 1000 — по н.г. L=2880
7	1760, 120, 1140 — по н.г. L=3020

Разрез 1 - 1 (армирование)

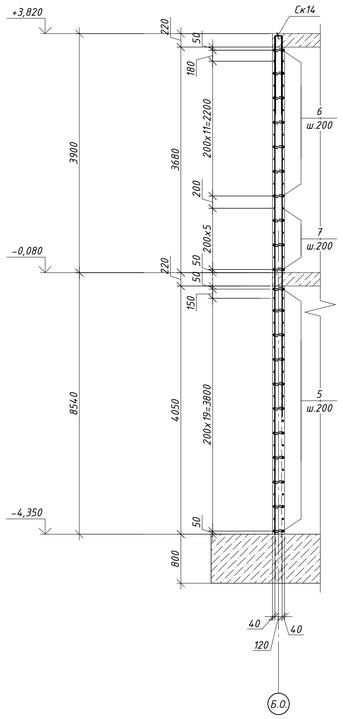


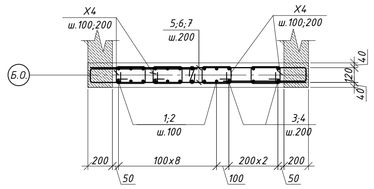


Анкеровка

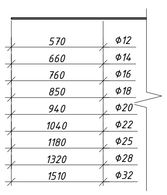

Узел стыковки вертикальной арматуры в нахлест и накладка

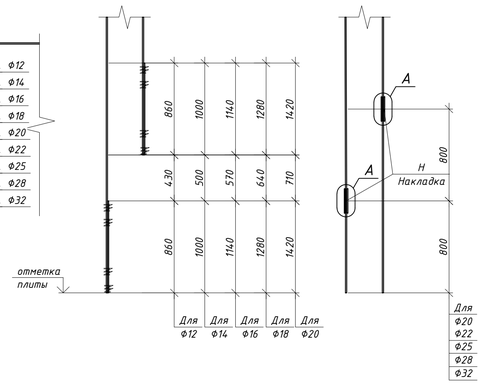

Узел стыковки Горизонтальной арматуры в нахлест

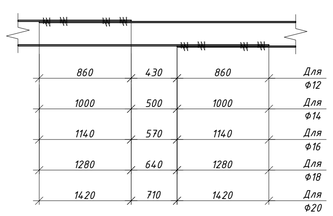

Спецификация элементов

Поз.	Обозначение	Наименование	Кол.	Масса ед.кг	Примечание
		Стена Ст-13			686.97
Х4*	ГОСТ 34028-2016(214-210-0101-0002)	Ф 8 А 240 L= 880	240	0.35	83.34
Шп1*	ГОСТ 34028-2016(214-210-0101-0002)	Ф 8 А 240 L= 320	30	0.13	3.79
Ск14*	ГОСТ 34028-2016(214-210-0502-0004)	Ф 18 А500С L= 2680	9	5.35	48.18
Ск13*	ГОСТ 34028-2016(214-210-0502-0003)	Ф 16 А500С L= 2400	3	3.79	11.36
1	ГОСТ 34028-2016(214-210-0502-0003)	Ф 16 А500С L= 8150	9	12.86	115.77
2	ГОСТ 34028-2016(214-210-0502-0003)	Ф 16 А500С L= 6230	9	9.83	88.50
3	ГОСТ 34028-2016(214-210-0502-0004)	Ф 18 А500С L= 8150	3	16.28	48.84
4	ГОСТ 34028-2016(214-210-0502-0004)	Ф 18 А500С L= 6230	3	12.44	37.33
5*	ГОСТ 34028-2016(214-210-0502-0001)	Ф 12 А500С L= 2740	42	2.43	102.17
6*	ГОСТ 34028-2016(214-210-0502-0002)	Ф 14 А500С L= 2880	26	3.48	90.49
7*	ГОСТ 34028-2016(214-210-0502-0003)	Ф 16 А500С L= 3020	12	4.77	57.20
		Материалы:			
	(212-101-0901)	Класс бетона С 20/25 (В25), м³			2.18

Позиции со "*" см. "Ведомость деталей" см. на данном листе.


Ведомость расхода стали, кг

Марка элемента	Изделия арматурные									Всего
	Арматура класса									
	А240 ГОСТ 34028-2016(214-210-0101)		А500С ГОСТ 34028-2016(214-210-0502)							
	Ø8	Итого	Ø10	Ø12	Ø14	Ø16	Ø18	Ø25	Итого	
Стена Ст-13	87.12	87.12	0.00	102.17	90.49	272.83	134.36	0.00	599.84	686.97


1. Общие указания см. л. - 1.
2. Данный лист читать совместно с л. КЖ-5.41 ... 5.42;
3. Стыки рабочей арматуры внахлестку без сварки, на скрутках из вязальной проволоки не менее 3 шт. на стык. Длина нахлеста 71d. Стыки располагать вразбежку, чтобы площадь рабочей арматуры, стыкуемой в одном сечении, не превышала 50%.
4. Расход арматуры в погонных метрах приведен с учетом нахлеста.
5. Стержни, указанные в "Ведомости деталей", должны гнуться механическим способом в холодном состоянии с радиусом гиба 3d - 5d, где d - диаметр стержня
6. Узел стыковки арматуры нахлеста и анкеровки смотреть на листе 5.1

							65П-АИП-2024-1-КЖ
Изм.	Кол.уч	Лист	N док.	Подп.	Дата		Строительство многопрофильной больницы на 250 коек с онкологическим центром и поликлиникой на 350 посещений, по адресу: Медеуский район, г. Алматы
ГКП		Курал М				"Блок 1 Секция 1"	Стадия: РП; Лист: 5.41; Листов:
Проверил		Кыдырбай А				Стена Ст-13 (тол.200мм)	АстанаИнжПроект
Разраб.		Ауез Б					Формат А1
Н.контроль		Ешенкулова					


Опалубочный чертеж монолитной стена См-14 (тол.250мм)

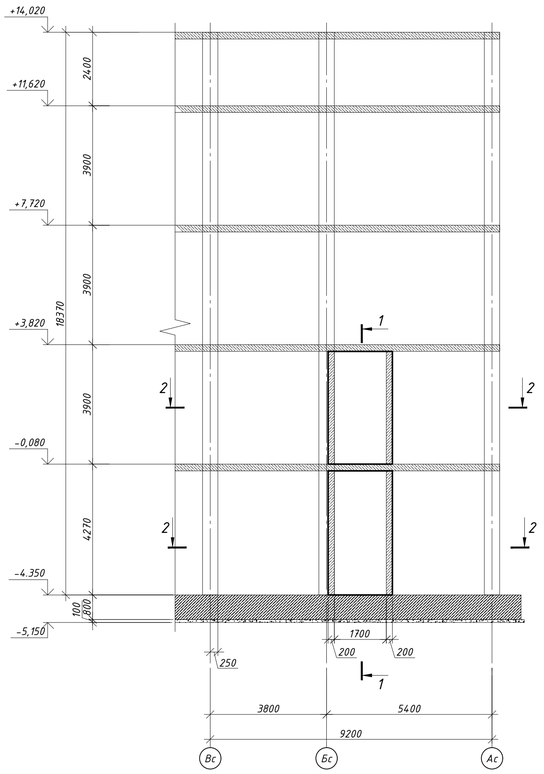


Разрез 1 - 1 (Опалубка)

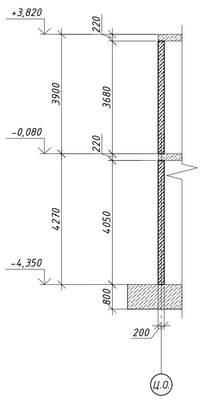


Разрез 2 - 2 (Опалубка)

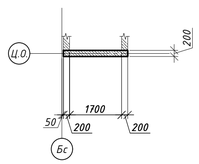


Разрез 2 - 2 (армирование)

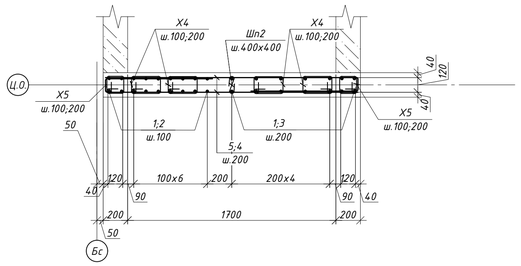


Разрез 1 - 1 (армирование)

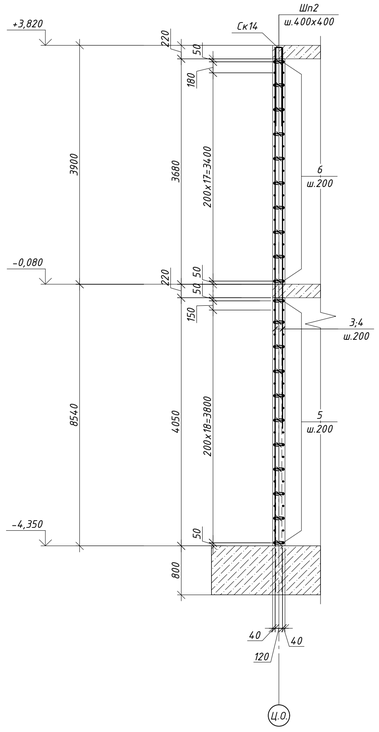


Основное вертикальное армирование монолитной стены См-14 (тол.200мм)

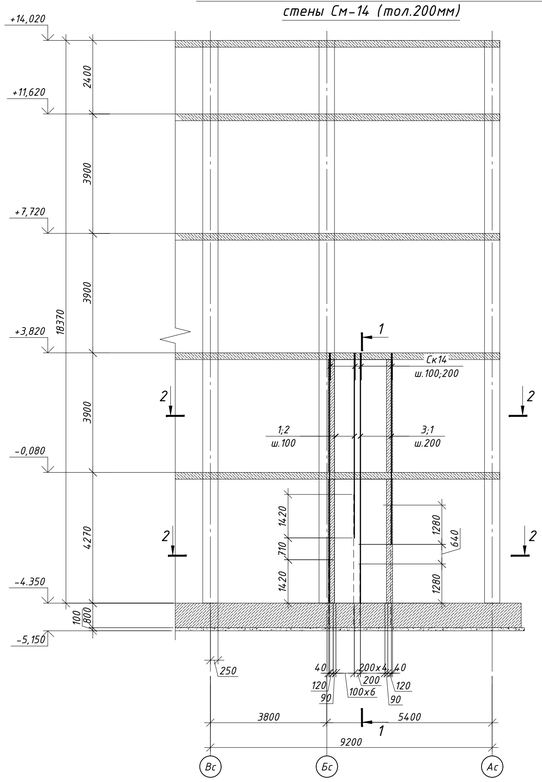


Основное горизонтальное армирование монолитной стены См-14 (тол.200мм)

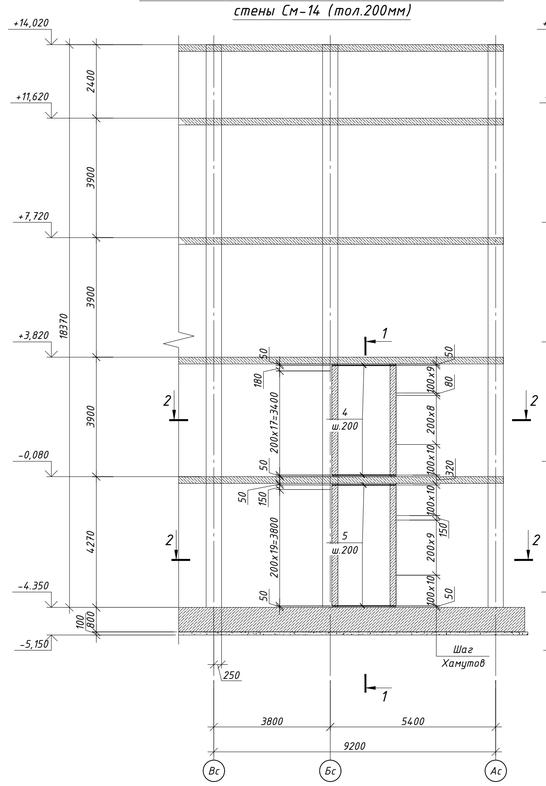


Дополнительное горизонтальное армирование монолитной стены См-14 (тол.200мм)

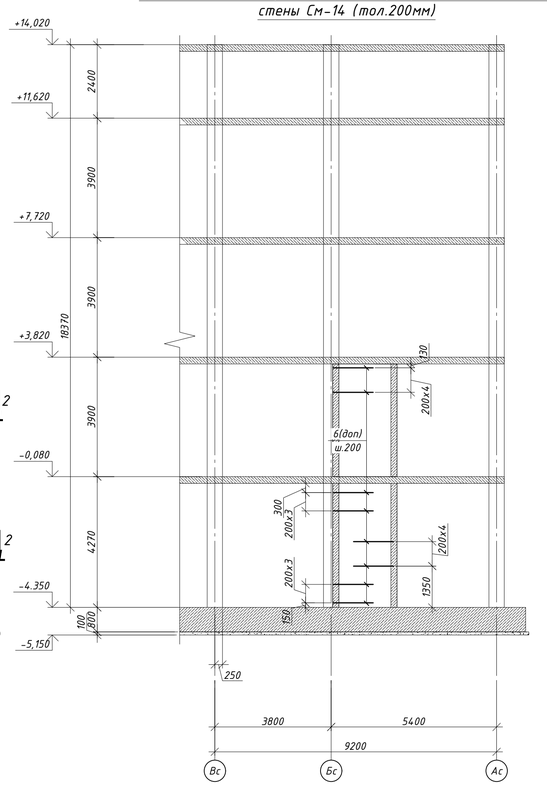


Анкеровка

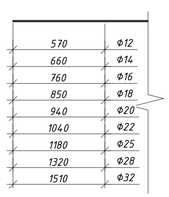

Узел стыковки вертикальной арматуры в нахлест и накладка

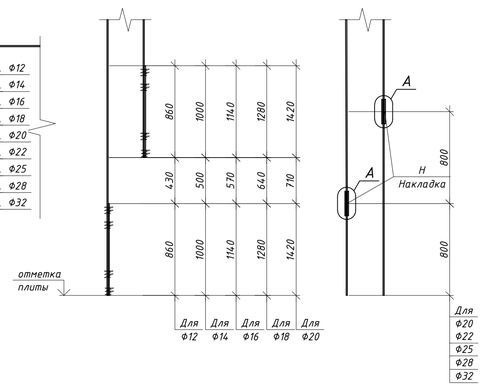

Узел стыковки Горизонтальной арматуры в нахлест

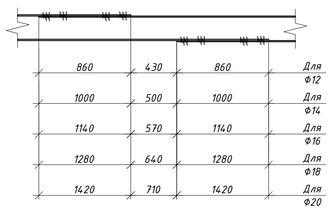

Ведомость деталей

Поз.	Эскиз
X4	320, 120, 220, 220; по в.г. L=880
X5	220, 120, 220, 120; по в.г. L=680
Шп2	120, 100, 100; по в.г. L=320
Ск14	1280, 120, 1280; по н.г. L=2680
5	2060, 120, 860; по н.г. L=3040
4	2060, 120, 1000; по н.г. L=3180

Спецификация элементов

Поз.	Обозначение	Наименование	Кол.	Масса ед.кг	Примечание
		Стена См-14			951.23
X4*	ГОСТ 34028-2016(214-210-0101-0002)	Ф 8 A 240 L= 880	240	0.35	83.34
X5*	ГОСТ 34028-2016(214-210-0101-0002)	Ф 8 A 240 L= 680	120	0.27	32.20
Шп1*	ГОСТ 34028-2016(214-210-0101-0002)	Ф 8 A 240 L= 320	60	0.13	7.58
Ск14*	ГОСТ 34028-2016(214-210-0502-0004)	Ф 18 A500C L= 2680	16	5.35	85.66
1	ГОСТ 34028-2016(214-210-0502-0004)	Ф 18 A500C L= 8150	16	16.28	260.48
2	ГОСТ 34028-2016(214-210-0502-0004)	Ф 18 A500C L= 6020	9	12.03	108.23
3	ГОСТ 34028-2016(214-210-0502-0004)	Ф 18 A500C L= 6230	7	12.44	87.11
4*	ГОСТ 34028-2016(214-210-0502-0002)	Ф 14 A500C L= 3180	38	3.84	146.02
5*	ГОСТ 34028-2016(214-210-0502-0001)	Ф 12 A500C L= 3040	42	2.70	113.36
6	ГОСТ 34028-2016(214-210-0501-0005)	Ф 10 A500C L= 1300	34	0.80	27.25
		Материалы:			
	(212-101-0901)	Класс бетона С 20/25 (B25)			3.24

Позиции со "*" см. "Ведомость деталей" см. на данном листе.

Ведомость расхода стали, кг


Марка элемента	Изделия арматурные									Всего
	Арматура класса									
	A240 ГОСТ 34028-2016(214-210-0101)		A500C ГОСТ 34028-2016(214-210-0502)(214-210-0501)							
	Ф8	Итого	Ф10	Ф12	Ф14	Ф16	Ф18	Ф25	Итого	
Стена См-14	123.11	123.11	27.25	113.36	146.02	0.00	541.48	0.00	828.12	951.23

1. Общие указания см. л. - 1.
2. Данный лист читать совместно с л. КЖ-5.41 ...5.42;
3. Стыки рабочей арматуры внахлестку без сварки, на скрутках из вязальной проволоки не менее 3 шт. на стык. Длина нахлеста 71d. Стыки располагать вразбежку, чтобы площадь рабочей арматуры, стыкуемой в одном сечении, не предышала 50%.
4. Расход арматуры в погонных метрах приведен с учетом нахлеста.
5. Стержни, указанные в "Ведомости деталей", должны гнуться механическим способом в холодном состоянии с радиусом гиба 3d - 5d, где d - диаметр стержня
6. Узел стыковки арматуры нахлеста и анкеровки смотреть на листе 5.1


						65П-АИП-2024-1-КЖ
						Строительство многопрофильной больницы на 250 коек с онкологическим центром и поликлиникой на 350 посещений, по адресу: Медеуский район, г. Алматы
Изм.	Кол.уч	Лист	N док.	Подп.	Дата	
ГКП	Курал М					"Блок 1 Секция 1"
Проверил	Кыдырбай А					Стадия: РП; Лист: 5.42; Листов:
Разраб.	Ауез Б					Стена См-14 (тол.200мм)
Н.контроль	Ешенкулова					АстанаИнжПроект

Формат А1


Опалубочный чертеж монолитной стена См-15 (тол.200мм)

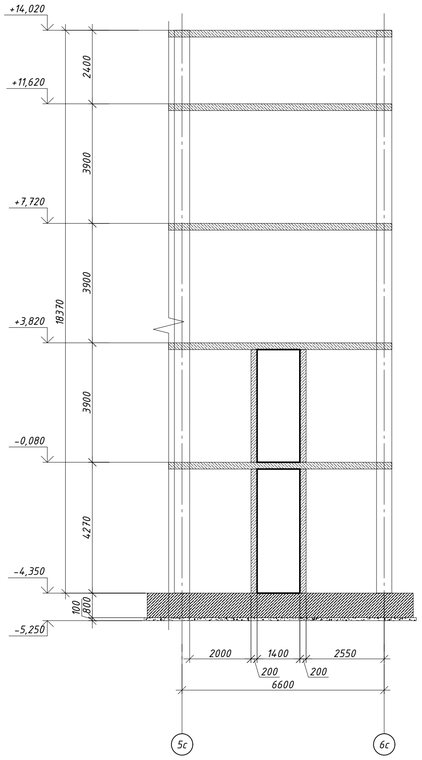


Разрез 1 - 1 (Опалубка)

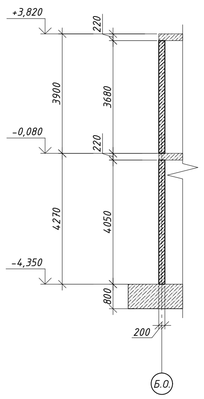


Разрез 2 - 2 (Опалубка)

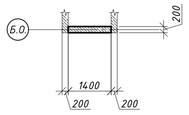

Основное вертикальное армирование монолитной стены См-15 (тол.200мм)

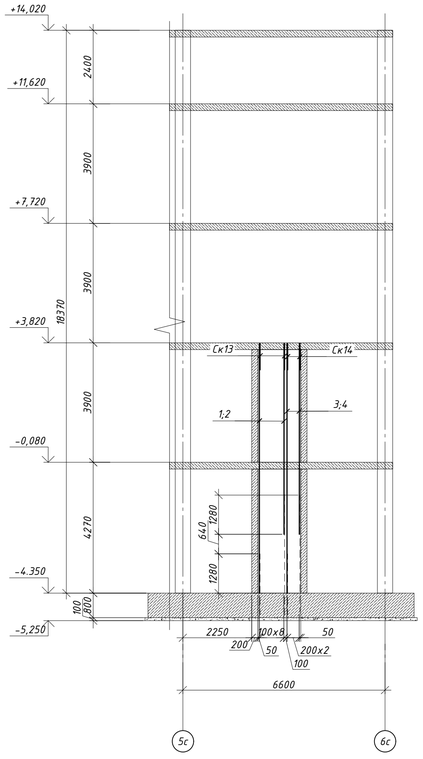


Основное горизонтальное армирование монолитной стены См-15 (тол.200мм)

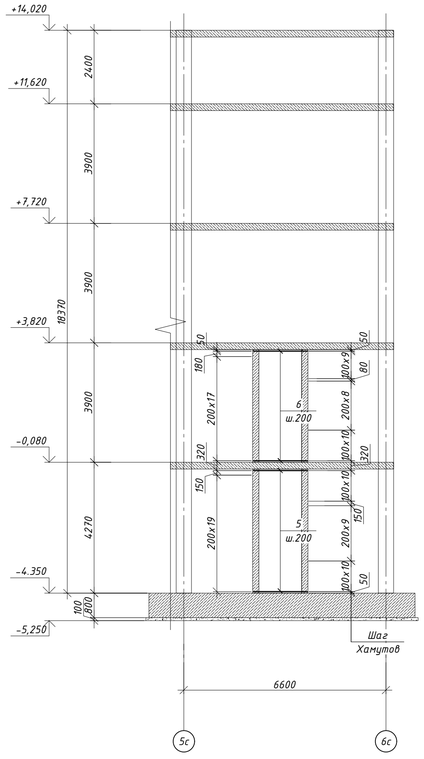


Ведомость деталей

Поз.	Эскиз
Х4	320, 120, 220, 220; по в.г. L=880
Шп2	120, 100, 100; по в.г. L=320
Ск1	1280, 120, 1280; по н.г. L=2680
Ск2	1140, 120, 1140; по н.г. L=2400
5	1760, 120, 860; по н.г. L=2740
6	1760, 120, 1000; по н.г. L=2880

Разрез 1 - 1 (армирование)

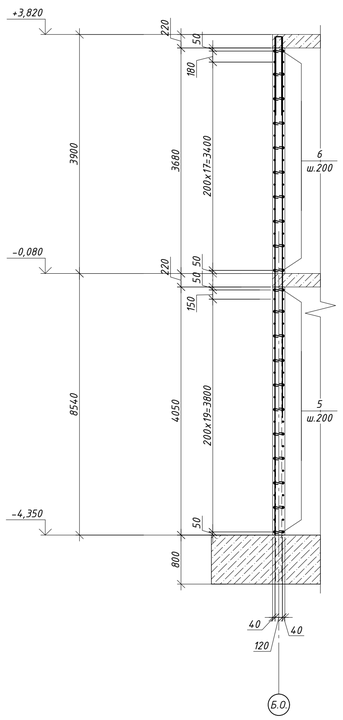


Разрез 2 - 2 (армирование)

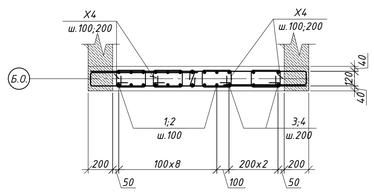


Узел стыковки вертикальной арматуры в нахлест и накладка

Анкеровка

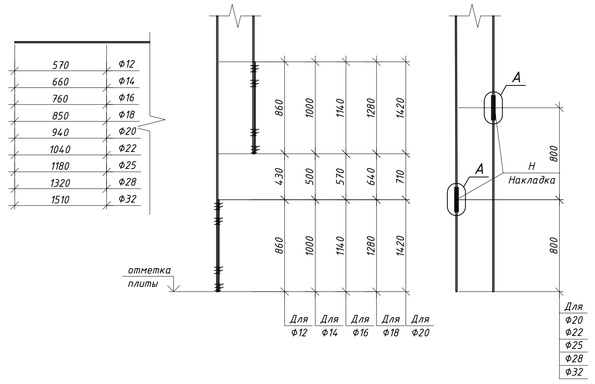

Узел стыковки Горизонтальной арматуры в нахлест

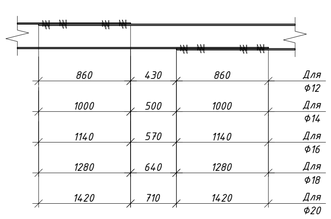

Спецификация элементов

Поз.	Обозначение	Наименование	Кол.	Масса ед.кг	Примечание
		Стена См-15			671.53
Х4*	ГОСТ 34028-2016(214-210-0101-0002)	Ф 8 А 240 L= 880	240	0.35	83.34
Шп1*	ГОСТ 34028-2016(214-210-0101-0002)	Ф 8 А 240 L= 320	30	0.13	3.79
Ск14*	ГОСТ 34028-2016(214-210-0502-0004)	Ф 18 А500С L= 2680	9	5.35	48.18
Ск13*	ГОСТ 34028-2016(214-210-0502-0003)	Ф 16 А500С L= 2400	3	3.79	11.36
1	ГОСТ 34028-2016(214-210-0502-0003)	Ф 16 А500С L= 8150	9	12.86	115.77
2	ГОСТ 34028-2016(214-210-0502-0003)	Ф 16 А500С L= 6230	9	9.83	88.50
3	ГОСТ 34028-2016(214-210-0502-0004)	Ф 18 А500С L= 8150	3	16.28	48.84
4	ГОСТ 34028-2016(214-210-0502-0004)	Ф 18 А500С L= 6230	3	12.44	37.33
5*	ГОСТ 34028-2016(214-210-0502-0001)	Ф 12 А500С L= 2740	42	2.43	102.17
6*	ГОСТ 34028-2016(214-210-0502-0002)	Ф 14 А500С L= 2880	38	3.48	132.25
		Материалы:			
	(212-101-0901)	Класс бетона С 20/25 (В25), м³			2.18

Позиции со "*" см. "Ведомость деталей" см. на данном листе.

Ведомость расхода стали, кг


Марка элемента	Изделия арматурные									Всего
	Арматура класса									
	А240 ГОСТ 34028-2016(214-210-0101)		А500С ГОСТ 34028-2016(214-210-0502)							
	Ф8	Итого	Ф10	Ф12	Ф14	Ф16	Ф18	Ф25	Итого	
Стена См-15	87.12	87.12	0.00	102.17	132.25	215.63	134.36	0.00	584.41	671.53

1. Общие указания см. л. - 1.
2. Данный лист читать совместно с л. КЖ-5.43;
3. Стыки рабочей арматуры внахлестку без сварки, на скрутках из вязальной проволоки не менее 3 шт. на стык. Длина нахлеста 71d. Стыки располагать вразбежку, чтобы площадь рабочей арматуры, стыкуемой в одном сечении, не превышала 50%.
4. Расход арматуры в погонных метрах приведен с учетом нахлеста.
5. Стержни, указанные в "Ведомости деталей", должны гнуться механическим способом в холодном состоянии с радиусом гиба 3d - 5d, где d - диаметр стержня
6. Узел стыковки арматуры нахлеста и анкеровки смотреть на листе 5.1


Изм.	Кол.уч	Лист	N док.	Подп.	Дата	65П-АИП-2024-1-КЖ			
						Строительство многопрофильной больницы на 250 коек с онкологическим центром и поликлиникой на 350 посещений, по адресу: Медеуский район, г. Алматы			
ГКП	Курал М					"Блок 1 Секция 1"	Стадия	Лист	Листов
Проверил	Кыдырбай А						РП	5.43	
Разраб.	Ауез Б					Стена См-15 (тол.200мм)	АстанаИнжПроект		
Н.контроль	Ешенкулова								

Формат А1


Опалубочный чертеж монолитной стена См-16 (тол.200мм)

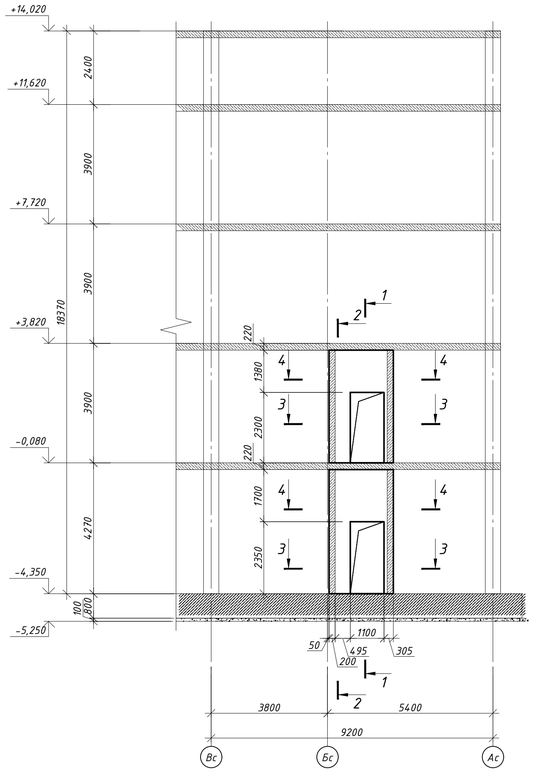


Разрез 1 - 1 (Опалубка)

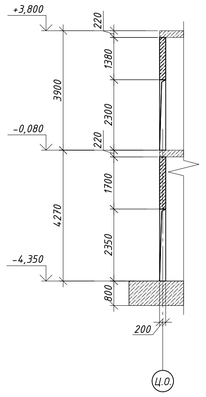


Разрез 2 - 2 (Опалубка)

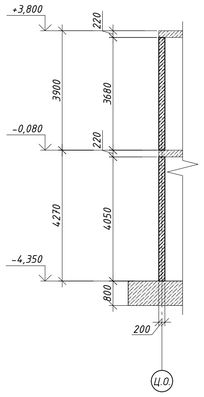


Разрез 3 - 3 (Опалубка)

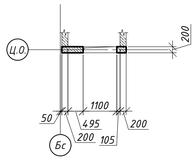


Разрез 4 - 4 (Опалубка)

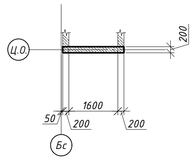

Основное вертикальное армирование монолитной стены См-16 (тол.200мм)

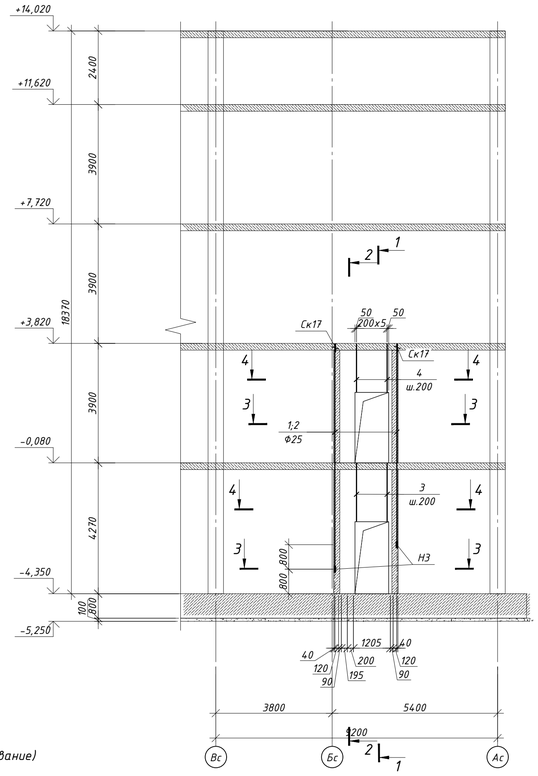


Основное горизонтальное армирование монолитной стены См-16 (тол.200мм)

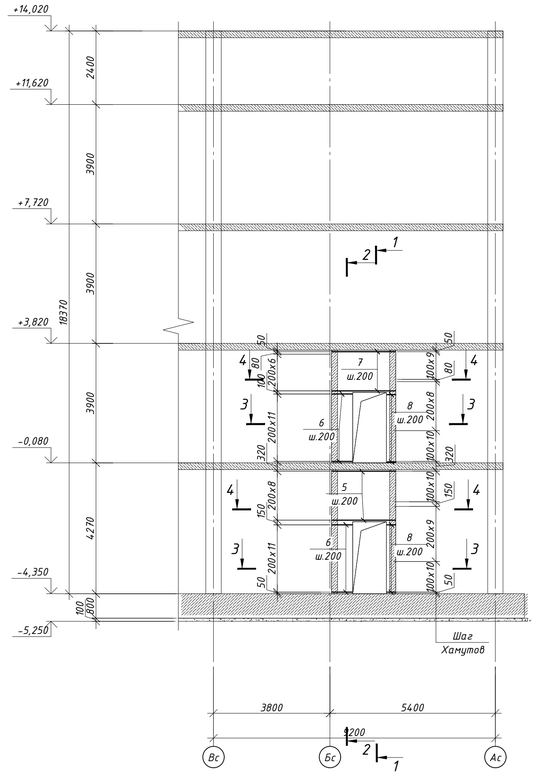


Разрез 3 - 3 (армирование)


Разрез 1 - 1 (армирование)

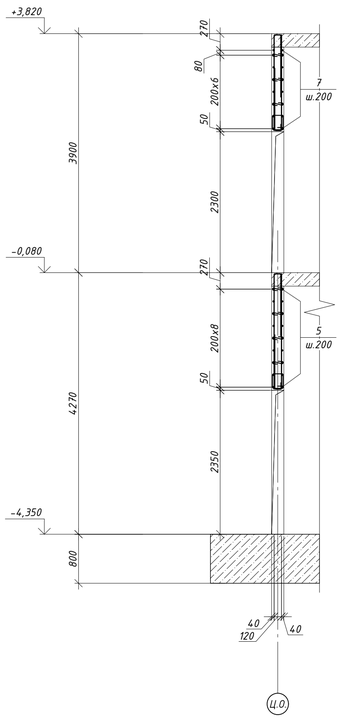

Разрез 2 - 2 (армирование)

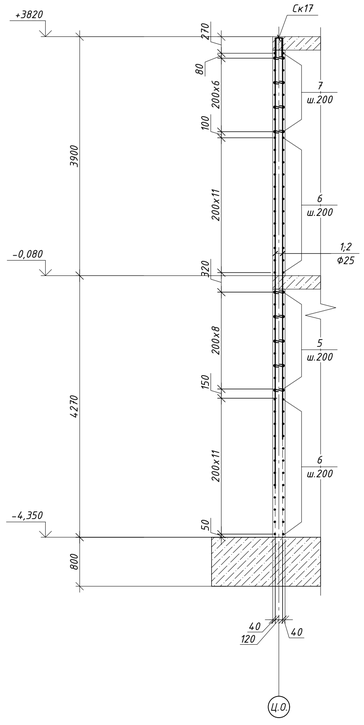


Разрез 4 - 4 (армирование)

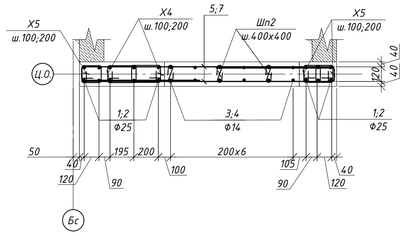


Узел стыковки вертикальной арматуры в нахлест и накладка

Анкеровка

570	Ф12
660	Ф14
760	Ф16
850	Ф18
940	Ф20
1040	Ф22
1180	Ф25
1320	Ф28
1510	Ф32

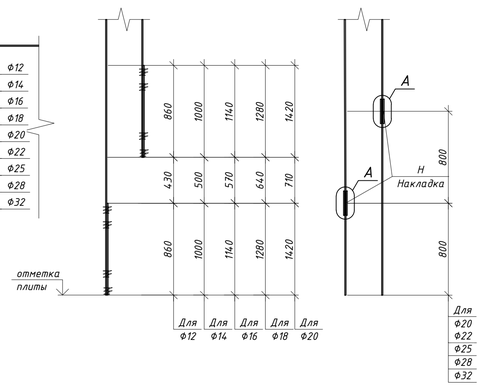











Узел стыковки Горизонтальной арматуры в нахлест

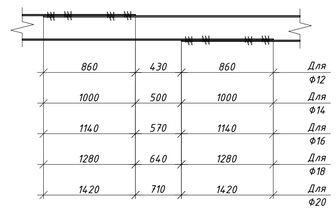

1. Общие указания см. л. - 1.
2. Данный лист читать совместно с л. КЖ-2.1 ... 2.7; и5.44; ... 5.45;
3. Стыки рабочей арматуры внахлестку без сварки, на скрутках из вязальной проволоки не менее 3 шт. на стык. Длина нахлеста 71d. Стыки располагать вразбежку, чтобы площадь рабочей арматуры, стыкуемой в одном сечении, не превышала 50%.
4. Расход арматуры в погонных метрах приведен с учетом нахлеста.
5. Стержни, указанные в "Ведомости деталей", должны гнуться механическим способом в холодном состоянии с радиусом гиба 3d - 5d, где d - диаметр стержня
6. Узел стыковки арматуры нахлеста и анкеровки смотреть на листе 5.1

							65П-АИП-2024-1-КЖ
							Строительство многопрофильной больницы на 250 коек с онкологическим центром и поликлиникой на 350 посещений, по адресу: Медеуский район, г. Алматы
Изм.	Кол.уч	Лист	N док.	Подп.	Дата		
ГКП		Курал М				"Блок 1 Секция 1"	Стадия: РП; Лист: 5.44; Листов:
Проверил		Кыдырбай А					
Разраб.		Ауез Б				Стена См-16 (тол.200мм)	АстанаИнжПроект
Н.контроль		Ешенкулова					Формат А1

Ведомость деталей

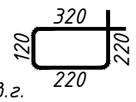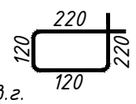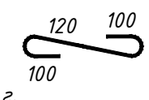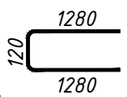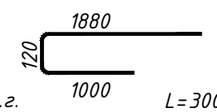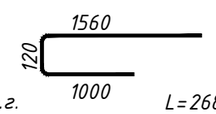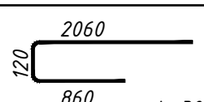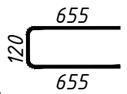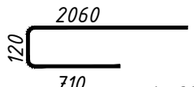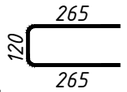Поз.	Эскиз
Х4	
Х5	
Шп2	
Ск14	
3	
4	
5	
6	
7	
8	

Ведомость расхода стали, кг

Марка элемента	Изделия арматурные									Всего
	Арматура класса									
	А240		А500С							
	ГОСТ 34028-2016(214-210-0101)		ГОСТ 34028-2016(214-210-0502)(214-210-0501)							
	Ф8	Итого	Ф10	Ф12	Ф14	Ф16	Ф18	Ф25	Итого	
Стена См-16	106.19	106.19	90.06	48.58	82.37	7.83	0.00	459.32	688.16	794.35

Спецификация элементов

Поз.	Обозначение	Наименование	Кол.	Масса ед.кг	Примечание
		Стена См-16			794.35
Х4*	ГОСТ 34028-2016(214-210-0101-0002)	ф 8 А 240 L= 880	150	0.35	52.09
Х5*	ГОСТ 34028-2016(214-210-0101-0002)	ф 8 А 240 L= 680	180	0.27	48.30
Шп2*	ГОСТ 34028-2016(214-210-0101-0002)	ф 8 А 240 L= 320	46	0.13	5.81
Ск17*	ГОСТ 34028-2016(214-210-0502-0003)	ф 16 А500С L= 620	8	0.98	7.83
НЗ	ГОСТ 34028-2016(214-210-0502-0007)	ф 25 А500С L= 250	32	0.96	30.83
1	ГОСТ 34028-2016(214-210-0502-0007)	ф 25 А500С L= 7350	8	28.32	226.58
2	ГОСТ 34028-2016(214-210-0502-0007)	ф 25 А500С L= 6550	8	25.24	201.92
3*	ГОСТ 34028-2016(214-210-0502-0002)	ф 14 А500С L= 3000	12	3.63	43.50
4*	ГОСТ 34028-2016(214-210-0502-0002)	ф 14 А500С L= 2680	12	3.24	38.86
5*	ГОСТ 34028-2016(214-210-0502-0001)	ф 12 А500С L= 3040	18	2.70	48.58
6*	ГОСТ 34028-2016(214-210-0501-0005)	ф 10 А500С L= 1430	48	0.88	42.32
7*	ГОСТ 34028-2016(214-210-0501-0005)	ф 10 А500С L= 2890	16	1.78	28.51
8*	ГОСТ 34028-2016(214-210-0501-0005)	ф 10 А500С L= 650	48	0.40	19.24
		Материалы:			
	(212-101-0901)	Класс бетона С 20/25			2.22


Позиции со "*" см. "Ведомость деталей" см. на данном листе.

1. Общие указания см. л. - 1.
2. Данный лист читать совместно с л. КЖ-2.1 ... 2.7; и5.44; ... 5.45;
3. Стыки рабочей арматуры внахлестку без сварки, на скрутках из вязальной проволоки не менее 3 шт. на стык. Длина нахлеста 71d. Стыки располагать вразбежку, чтобы площадь рабочей арматуры, стыкуемой в одном сечении, не превышала 50%.
4. Расход арматуры в погонных метрах приведен с учетом нахлеста.
5. Стержни, указанные в "Ведомости деталей", должны гнуться механическим способом в холодном состоянии с радиусом гиба 3d - 5d, где d - диаметр стержня
6. Узел стыковки арматуры нахлеста и анкеровки смотреть на листе 5.1


Изм.	Кол.уч.	Лист	N док.	Подп.	Дата	65П-АИП-2024-1-КЖ			
						Строительство многопрофильной больницы на 250 коек с онкологическим центром и поликлиникой на 350 посещений, по адресу: Медеуский район, г. Алматы			
						"Блок 1 Секция 1"	Стадия	Лист	Листов
							РП	5.45	
ГКП		Курал М				Спецификация стены См-16 (тол.200мм)	АстанаИнжПроект		
Проверил		Кыдырбай А							
Разраб.		Ауез Б							
Н.контроль		Ешенкулова							

Формат А3


Опалубочный чертеж монолитной стена См-17 (тол.250мм)

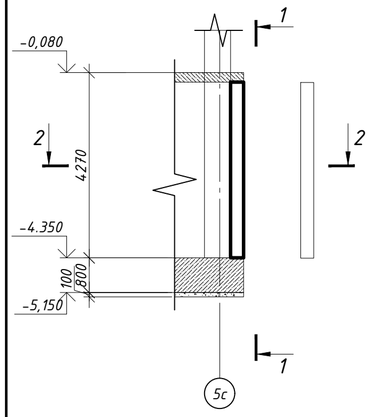


Разрез 1 - 1 (Опалубка) М1:100

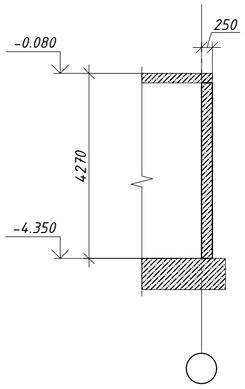


Основное вертикальное армирование монолитной стены См-17;(тол.250мм)

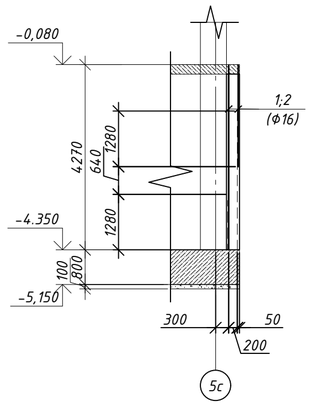


Основное горизонтальное армирование монолитной стены См-17 (тол.250мм)

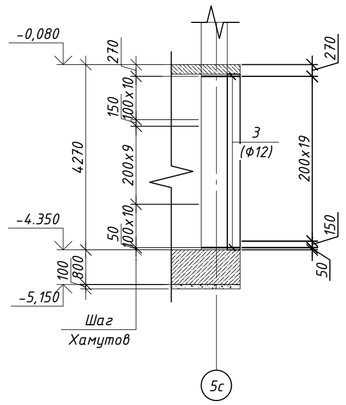


Разрез 1 - 1 (армирование)

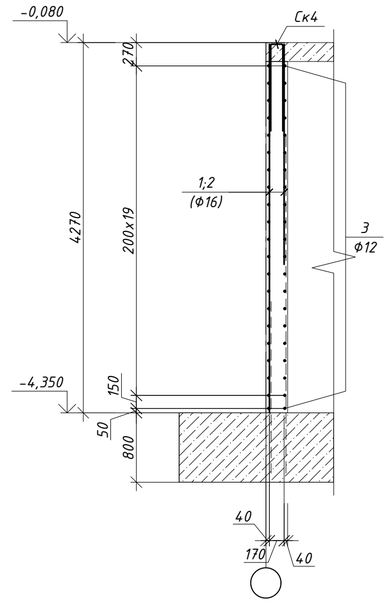

Разрез 2 - 2 (Опалубка)

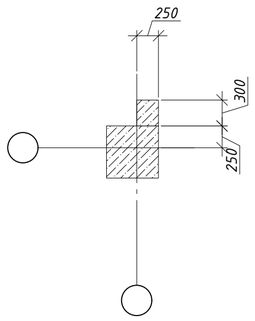

Разрез 2 - 2 (армирование)

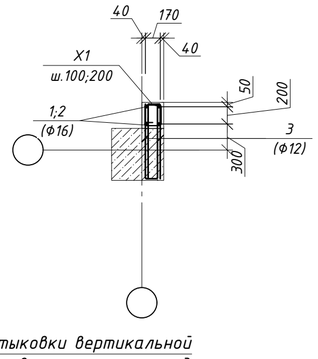

Ведомость деталей


Поз.	Эскиз
X1	320, 170, 270, 220 по в.г. L=980
Ск4	1140, 170, 1140 по н.г. L=2450
3	860, 170, 860 по н.г. L=1890

Спецификация элементов


Поз.	Обозначение	Наименование	Кол.	Масса ед.кг	Примечание
		Стена См-17			109.74
X1	ГОСТ 34028-2016(214-210-0101-0002)	Ф 8 А 240 L= 880	31	0.35	10.76
Ск4	ГОСТ 34028-2016(214-210-0502-0003)	Ф 16 А500С L= 2450	2	3.87	7.73
1	ГОСТ 34028-2016(214-210-0502-0003)	Ф 16 А500С L= 4250	2	6.71	13.42
2	ГОСТ 34028-2016(214-210-0502-0003)	Ф 16 А500С L= 2330	2	3.68	7.36
3	ГОСТ 34028-2016(214-210-0502-0001)	Ф 12 А500С L= 1890	42	1.68	70.47
		Материалы:			
	(212-101-0901)	Класс бетона С 20/25 (В25), м³			0.31

Позиции со "*" см. "Ведомость деталей" см. на данном листе.


Анкеровка

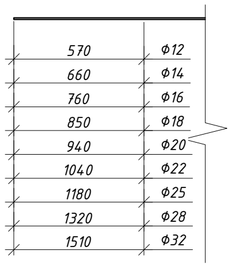

Узел стыковки вертикальной арматуры в нахлест и накладка

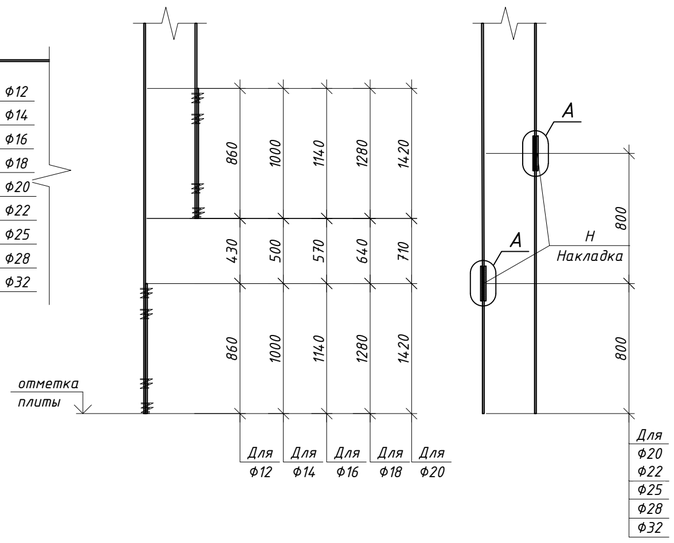

Узел стыковки Горизонтальной арматуры в нахлест

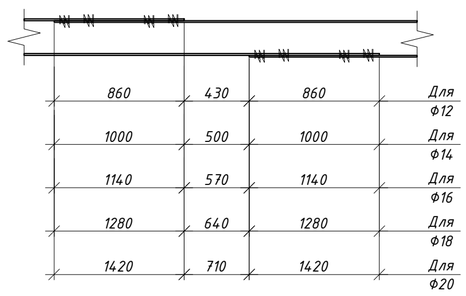

Ведомость расхода стали, кг

Марка элемента	Изделия арматурные									Всего
	Арматура класса									
	А240 ГОСТ 34028-2016(214-210-0101)		А500С ГОСТ 34028-2016(214-210-0502)							
	Ф8	Итого	Ф10	Ф12	Ф14	Ф16	Ф18	Ф20	Итого	
Стена См-20	10.76	10.76	0.00	70.47	0.00	28.50	0.00	0.00	98.98	109.74

1. Общие указания см. л. - 1.
2. Данный лист читать совместно с л. КЖ-5.46
3. Стыки рабочей арматуры внахлестку без сварки, на скрутках из вязальной проволоки не менее 3 шт. на стык. Длина нахлеста 71d. Стыки располагать вразбежку, чтобы площадь рабочей арматуры, стыкуемой в одном сечении, не превышала 50%.
4. Расход арматуры в погонных метрах приведен с учетом нахлеста.
5. Стержни, указанные в "Ведомости деталей", должны гнуться механическим способом в холодном состоянии с радиусом гиба 3d - 5d, где d - диаметр стержня
6. Узел стыковки арматуры нахлеста и анкеровки смотреть на листе 5.1

Изм.	Кол.уч	Лист	N док.	Подп.	Дата	65П-АИП-2024-1-КЖ		
						Строительство многопрофильной больницы на 250 коек с онкологическим центром и поликлиникой на 350 посещений, по адресу: Медеуский район, г. Алматы		
ГКП		Курал М				"Блок 1 Секция 1"	Стадия: РП	Лист: 5.46
Проверил		Кыдырбай А						
Разраб.		Ауез Б				Спецификация монолитной стены по оси 5с стена См-17 (тол.250мм)	АстанаИнжПроект	
Н.контроль		Ешенкулова						

Согласовано

Взам. инв. №

Подп. и дата

Инв. № подл.

Формат А2