

Ригель Рм-1

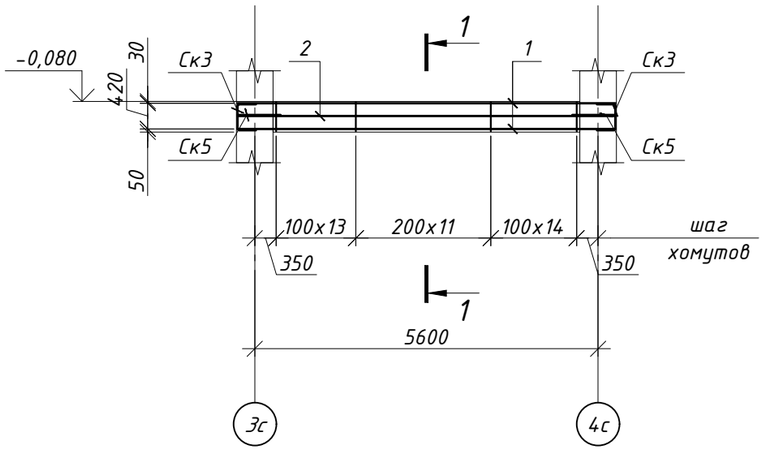

Разрез 1 - 1

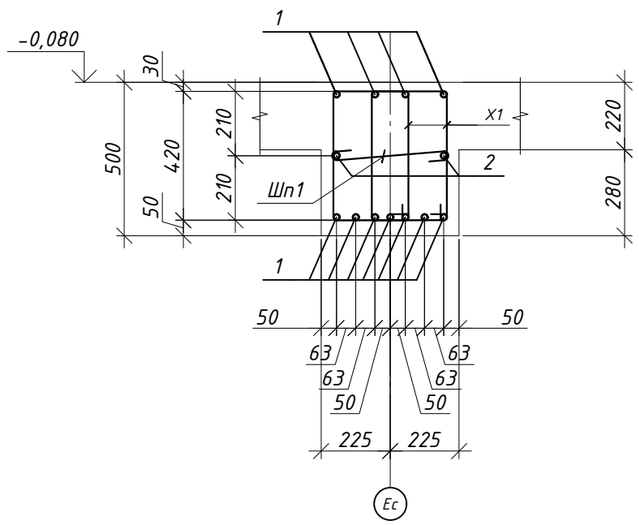

Спецификация элементов

Поз.	Обозначение	Наименование	Кол.	Масса ед.кг	Примечание
		Ригель Рм-1			349.76
X1	ГОСТ 34028-2016(214-210-0101-0002)	ф 8 A 240 L= 1530	78	0.60	47.09
Ск3	ГОСТ 34028-2016(214-210-0502-0005)	ф 20 A500C L= 920	8	2.27	18.15
Ск5	ГОСТ 34028-2016(214-210-0502-0001)	ф 12 A500C L= 2090	2	1.86	3.71
1	ГОСТ 34028-2016(214-210-0502-0007)	ф 25 A500C L= 6160	11	23.74	261.10
2	ГОСТ 34028-2016(214-210-0502-0001)	ф 12 A500C L= 6160	2	5.47	10.94
Шп1	ГОСТ 34028-2016(214-210-0101-0002)	ф 8 A 240 L= 570	39	0.22	8.77
		Материалы:			
	(212-101-0901)	Класс бетона С 20/25 (В25), м³			0.63


Позиции со "*" см. "Ведомость деталей" см. на данном листе.

Ведомость расхода стали, кг

Марка элемента	Изделия арматурные						Всего
	Арматура класса						
	A240		A500C				
	ГОСТ 34028-2016(214-210-0101)		ГОСТ 34028-2016(214-210-0502)				
	ф8	Итого	ф12	ф20	ф25	Итого	
Ригель Рм-1	55.86	55.86	14.65	18.15	261.10	293.90	349.76

Ведомость деталей

Поз.	Эскиз	Поз.	Эскиз
X1	520, 245, 345, 420; по в.г. L=1530	Ск3	250, 420, 250; по н.г. L=920
Шп1	370, 100, 100; по в.г. L=570	Ск5	860, 370, 860; по н.г. L=2090

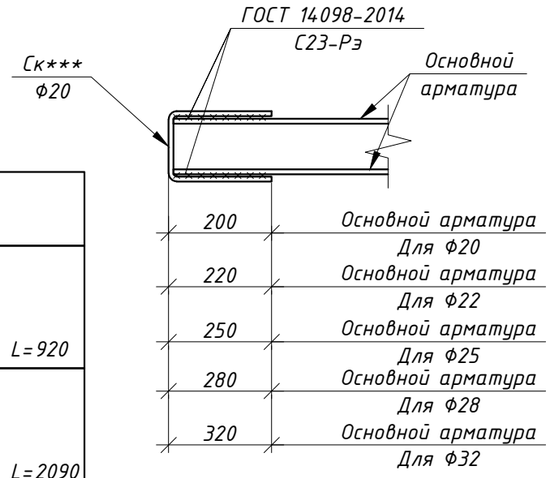

1. Общие указания см. л. - 1.
2. Данный лист читать совместно с л. КЖ-2.2 ... 2.7
3. Стержни, указанные в "Ведомости деталей", должны гнуться механическим способом в холодном состоянии с радиусом гиба 3d - 5d, где d - диаметр стержня

Изм.	Кол.уч.	Лист	N док.	Подп.	Дата
ГКП		Курал М			
Проверил		Кыдырбай А			
Разраб.		Ауез Б			
Н.контроль		Ешенкулова			

65П-АИП-2024-1-КЖ

Строительство многопрофильной больницы на 250 коек с онкологическим центром и поликлиникой на 350 посещений, по адресу: Медеуский район, г. Алматы

"Блок 1 Секция 1"


Стадия	Лист	Листов
РП	6.1	

Ригель Рм-1


АстанаИнжПроект

Формат А3

Ригель Рм-2

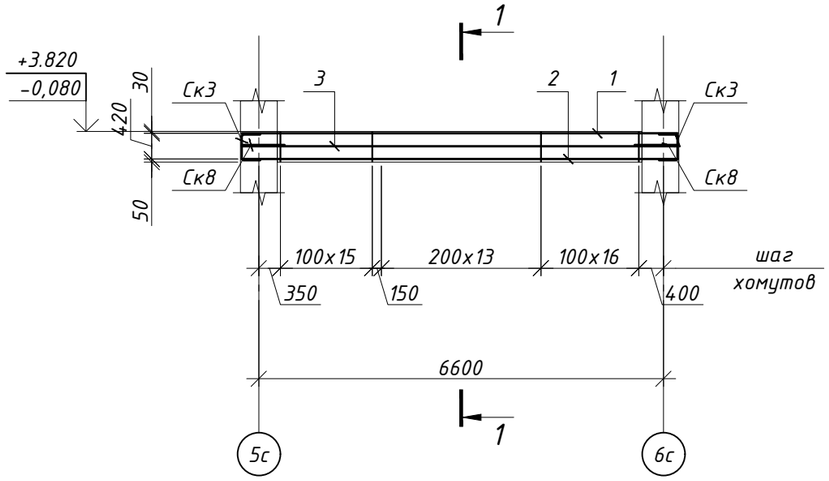

Разрез 1 - 1

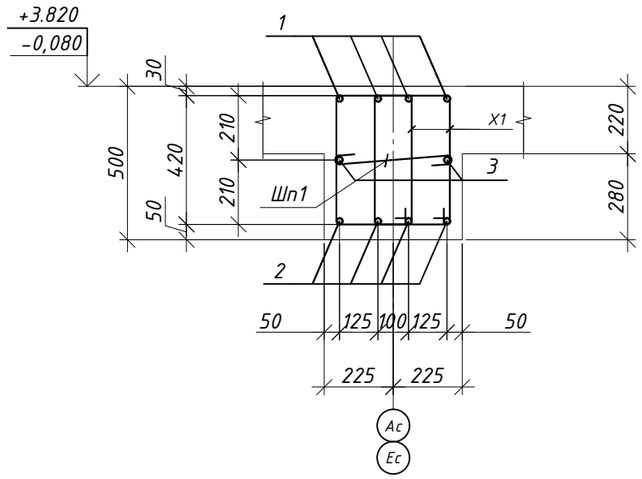

Спецификация элементов





Поз.	Обозначение	Наименование	Кол.	Масса ед.кг	Примечание
		Ригель Рм-2	3		382.89
X1	ГОСТ 34028-2016(214-210-0101-0003)	ф 10 А 240 L= 1530	92	0.94	86.78
Ск3	ГОСТ 34028-2016(214-210-0502-0005)	ф 20 А500С L= 920	8	2.27	18.15
Ск8	ГОСТ 34028-2016(214-210-0502-0004)	ф 18 А500С L= 2930	2	5.85	11.71
1	ГОСТ 34028-2016(214-210-0502-0007)	ф 25 А500С L= 7110	4	27.40	109.59
2	ГОСТ 34028-2016(214-210-0502-0006)	ф 22 А500С L= 7110	4	21.22	84.87
3	ГОСТ 34028-2016(214-210-0502-0004)	ф 18 А500С L= 7110	2	14.20	28.41
Шп1	ГОСТ 34028-2016(214-210-0101-0003)	ф 10 А 240 L= 1530	46	0.94	43.39
		Материалы:			
	(212-101-0901)	Класс бетона С 20/25 (В25), м³			0.75


Позиции со "*" см. "Ведомость деталей" см. на данном листе.

Ведомость расхода стали, кг

Марка элемента	Изделия арматурные								Всего
	Арматура класса								
	А240			А500С					
	ГОСТ 34028-2016(214-210-0101)			ГОСТ 34028-2016(214-210-0502)					
	ф8	ф10	Итого	ф18	ф20	ф22	ф25	Итого	
Ригель Рм-2	0.00	130.18	130.18	40.11	18.15	84.87	109.59	252.72	382.89

Ведомость деталей

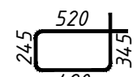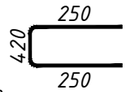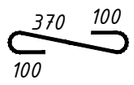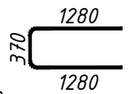Поз.	Эскиз	Поз.	Эскиз
X1	 по в.г. L=1530	Ск3	 по н.г. L=920
Шп1	 по в.г. L=570	Ск8	 по н.г. L=2930

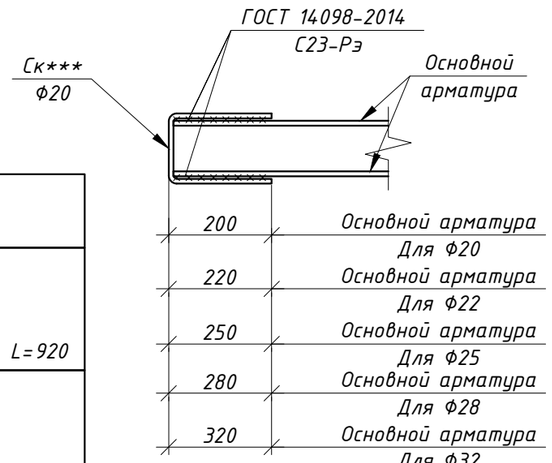


1. Общие указания см. л. - 1.
2. Данный лист читать совместно с л. КЖ-2.2 ... 2.7
3. Стержни, указанные в "Ведомости деталей", должны гнуться механическим способом в холодном состоянии с радиусом гиба 3d - 5d, где d - диаметр стержня


Изм.	Кол.уч.	Лист	N док.	Подп.	Дата	65П-АИП-2024-1-КЖ			
						Строительство многопрофильной больницы на 250 коек с онкологическим центром и поликлиникой на 350 посещений, по адресу: Медеуский район, г. Алматы			
						"Блок 1 Секция 1"	Стадия	Лист	Листов
							РП	6.2	
ГКП		Курал М				Ригель Рм-2	АстанаИнжПроект		
Проверил		Кыдырбай А							
Разраб.		Ауез Б							
Н.контроль		Ешенкулова							

Формат А3


Ригель Рм-3

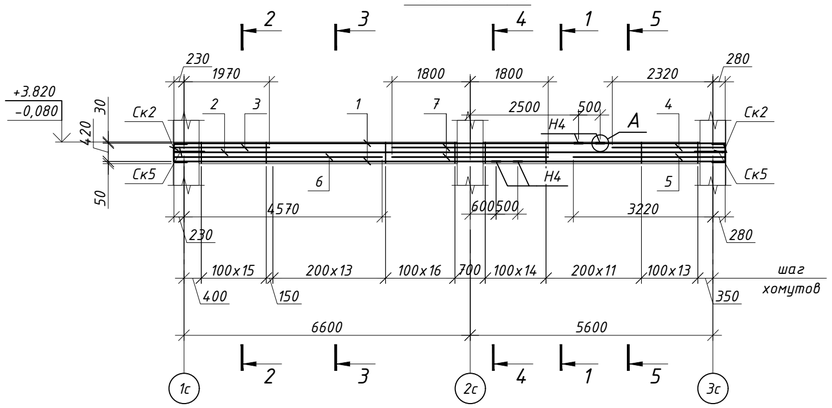


Разрез 1 - 1

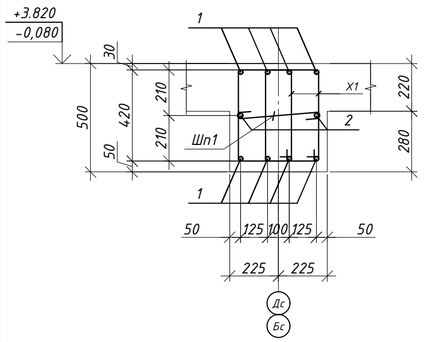


Разрез 4 - 4

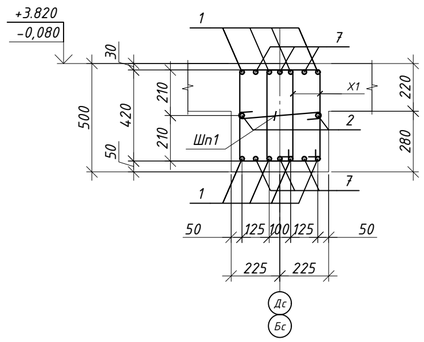


Разрез 2 - 2

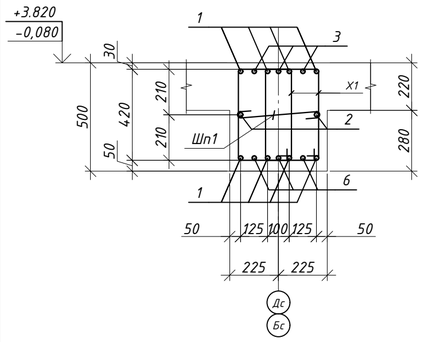

Разрез 5 - 5

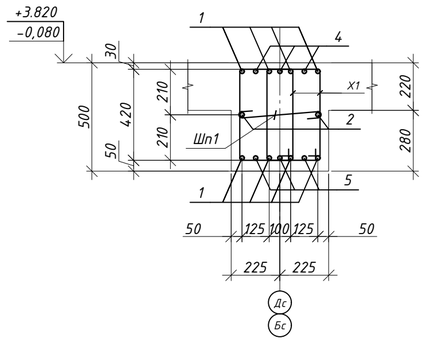

Разрез 3 - 3

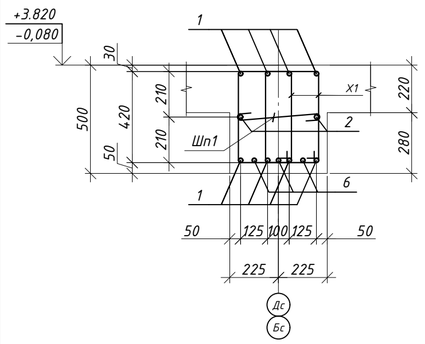

Ведомость деталей

Поз.	Эскиз	
Х1	520, 245, 345, 420	по в.г. L=1530
Ск2	220, 420, 220	по н.г. L=860
Ск5	860, 370, 860	по н.г. L=2090
Шп1	370, 100, 100	по в.г. L=570

Спецификация элементов

Поз.	Обозначение	Наименование	Кол.	Масса ед.кг	Примечание
		Ригель Рм-3	3		682.51
Х1	ГОСТ 34028-2016(214-210-0101-0003)	ф 10 А 240 L= 1530	170	0.94	160.36
Ск2	ГОСТ 34028-2016(214-210-0502-0005)	ф 20 А500С L= 860	8	2.12	16.97
Ск5	ГОСТ 34028-2016(214-210-0502-0001)	ф 12 А500С L= 2090	2	1.86	3.71
1	ГОСТ 34028-2016(214-210-0502-0006)	ф 22 А500С L= пог.м.	107	2.98	319.29
Н4	ГОСТ 34028-2016(214-210-0502-0006)	ф 22 А500С L= 220	16	0.66	10.50
2	ГОСТ 34028-2016(214-210-0502-0001)	ф 12 А500С L= пог.м.	27	0.89	23.97
3	ГОСТ 34028-2016(214-210-0502-0001)	ф 12 А500С L= 2200	3	1.95	5.86
4	ГОСТ 34028-2016(214-210-0502-0003)	ф 16 А500С L= 2600	3	4.10	12.31
5	ГОСТ 34028-2016(214-210-0502-0008)	ф 28 А500С L= 3500	3	16.92	50.75
6	ГОСТ 34028-2016(214-210-0502-0001)	ф 12 А500С L= 4800	6	4.26	25.57
7	ГОСТ 34028-2016(214-210-0502-0003)	ф 16 А500С L= 3600	6	5.68	34.09
Шп1	ГОСТ 34028-2016(214-210-0101-0002)	ф 8 А 240 L= 570	85	0.22	19.12
		Материалы:			
	(212-101-0901)	Класс бетона С 20/25 (В25), м³			1.38


Позиции со "*" см. "Ведомость деталей" см. на данном листе.


Ведомость расхода стали, кг


Марка элемента	Изделия арматурные									Всего
	Арматура класса									
	А240			А500С						
	ГОСТ 34028-2016(214-210-0101)			ГОСТ 34028-2016(214-210-0502)						
	ф8	ф10	Итого	ф12	ф16	ф20	ф22	ф28	Итого	
Ригель Рм-3	19.12	160.36	179.48	59.11	46.40	16.97	329.80	50.75	503.03	682.51

Таблица размеров накладок

Марка эл-та	dн	L	вес
	мм.		кг.
Н1	32	320	2.01
Н2	28	280	1.35
Н3	25	250	0.96
Н4	22	220	0.66
Н5	20	200	0.49

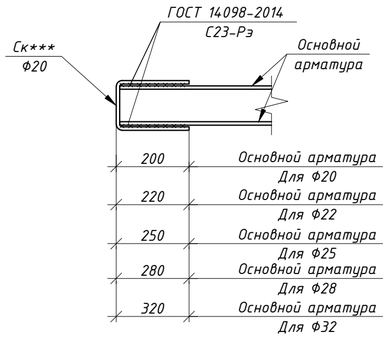

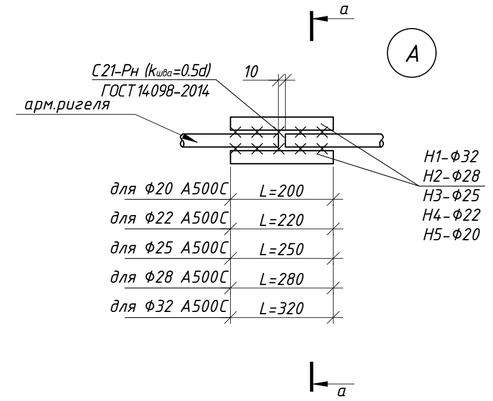

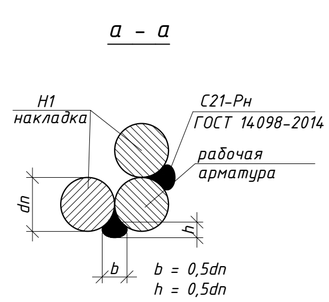


1. Общие указания см. л. - 1.
2. Данный лист читать совместно с л. КЖ-2.2 ... 2.7
3. Стержни, указанные в "Ведомости деталей", должны гнуться механическим способом в холодном состоянии с радиусом гиба 3d - 5d, где d - диаметр стержня


							65П-АИП-2024-1-КЖ
							Строительство многопрофильной больницы на 250 коек с онкологическим центром и поликлиникой на 350 посещений, по адресу: Медеуский район, г. Алматы
Изм.	Кол.уч.	Лист	N док.	Подп.	Дата		
ГКП		Курал М				"Блок 1 Секция 1"	Стадия: РП; Лист: 6.3; Листов:
Проверил		Кыдырбай А				Ригель Рм-3	АстанаИнжПроект
Разраб.		Ауез Б					
Н.контроль		Ешенкулова					

Формат А2


Ригель Рм-4

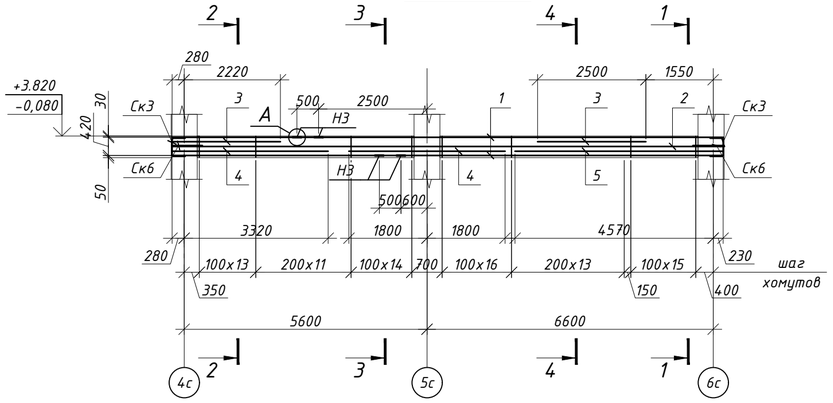


Разрез 1 - 1

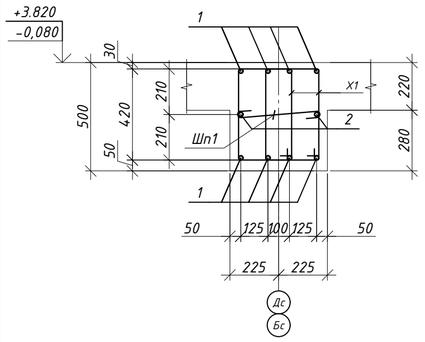


Разрез 4 - 4

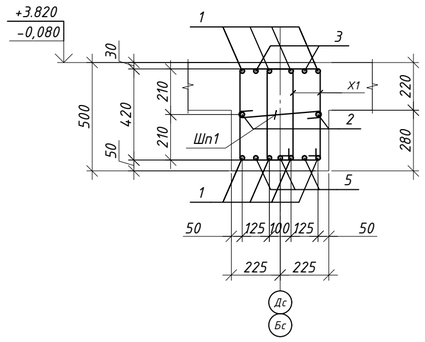

Разрез 2 - 2

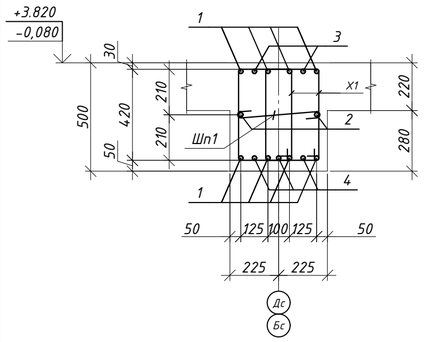

Разрез 3 - 3

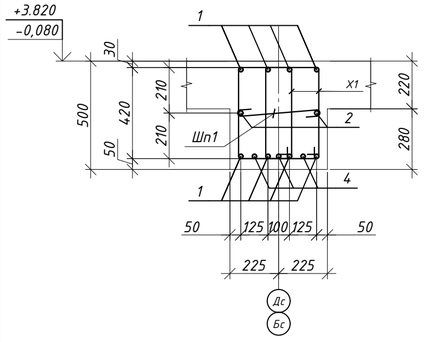

Ведомость деталей

Поз.	Эскиз	
Х1	520, 245, 345, 420 — по в.г.	L=1530
Ск3	250, 420, 250 — по н.г.	L=920
Ск6	1000, 370, 1000 — по н.г.	L=2370
Шп1	370, 100, 100 — по в.г.	L=570

Таблица размеров накладок

Марка эл-та	dн	L	вес
	мм.		кг.
Н1	32	320	2.01
Н2	28	280	1.35
Н3	25	250	0.96
Н4	22	220	0.66
Н5	20	200	0.49


Спецификация элементов

Поз.	Обозначение	Наименование	Кол.	Масса ед.кг	Примечание
		Ригель Рм-4	4		793.57
Х1	ГОСТ 34028-2016(214-210-0101-0003)	ф 10 А 240 L= 1530	170	0.94	160.36
Ск3	ГОСТ 34028-2016(214-210-0502-0005)	ф 20 А500С L= 920	8	2.27	18.15
Ск6	ГОСТ 34028-2016(214-210-0502-0002)	ф 14 А500С L= 2370	2	2.86	5.73
1	ГОСТ 34028-2016(214-210-0502-0007)	ф 25 А500С L= пог.м.	107	3.85	412.31
НЗ	ГОСТ 34028-2016(214-210-0502-0007)	ф 25 А500С L= 250	16	0.96	15.41
2	ГОСТ 34028-2016(214-210-0502-0002)	ф 14 А500С L= пог.м.	27	1.21	32.63
3	ГОСТ 34028-2016(214-210-0502-0001)	ф 12 А500С L= 2500	4	2.22	8.88
4	ГОСТ 34028-2016(214-210-0502-0005)	ф 20 А500С L= 3600	6	8.88	53.27
5	ГОСТ 34028-2016(214-210-0502-0005)	ф 20 А500С L= 4800	3	11.84	35.51
Шп1	ГОСТ 34028-2016(214-210-0101-0002)	ф 8 А 240 L= 1530	85	0.60	51.32
		Материалы:			
	(212-101-0901)	Класс бетона С 20/25 (В25), м³			1.38


Позиции со "*" см. "Ведомость деталей" см. на данном листе.


Ведомость расхода стали, кг

Марка элемента	Изделия арматурные								Всего
	Арматура класса								
	А240			А500С					
	ГОСТ 34028-2016(214-210-0101)			ГОСТ 34028-2016(214-210-0502)					
	ф8	ф10	Итого	ф12	ф14	ф20	ф25	Итого	
Ригель Рм-4	51.32	160.36	211.68	8.88	38.36	106.93	427.72	581.89	793.57

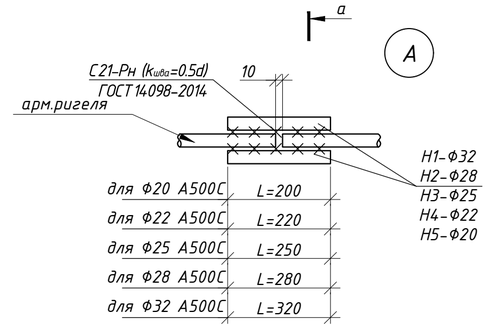

а - а

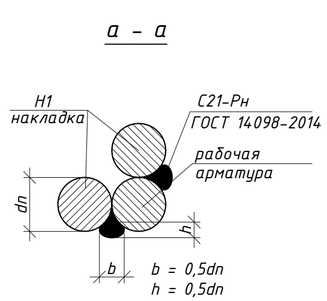

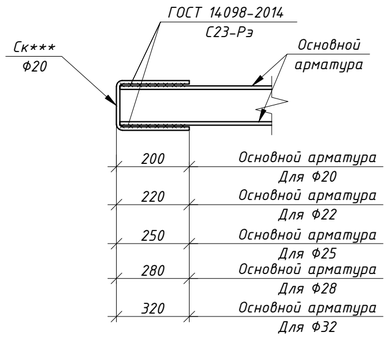


1. Общие указания см. л. - 1.
2. Данный лист читать совместно с л. КЖ-2.2 ... 2.7
3. Стержни, указанные в "Ведомости деталей", должны гнуться механическим способом в холодном состоянии с радиусом гиба 3d - 5d, где d - диаметр стержня


Изм.	Кол.уч.	Лист	N док.	Подп.	Дата	65П-АИП-2024-1-КЖ			
						Строительство многопрофильной больницы на 250 коек с онкологическим центром и поликлиникой на 350 посещений, по адресу: Медеуский район, г. Алматы			
ГКП		Курал М				"Блок 1 Секция 1"	Стадия	Лист	Листов
Проверил		Кыдырбай А					РП	6.4	
Разраб.		Ауез Б				Ригель Рм-4	АстанаИнжПроект		
Н.контроль		Ешенкулова							

Формат А2


Ригель Рм-5

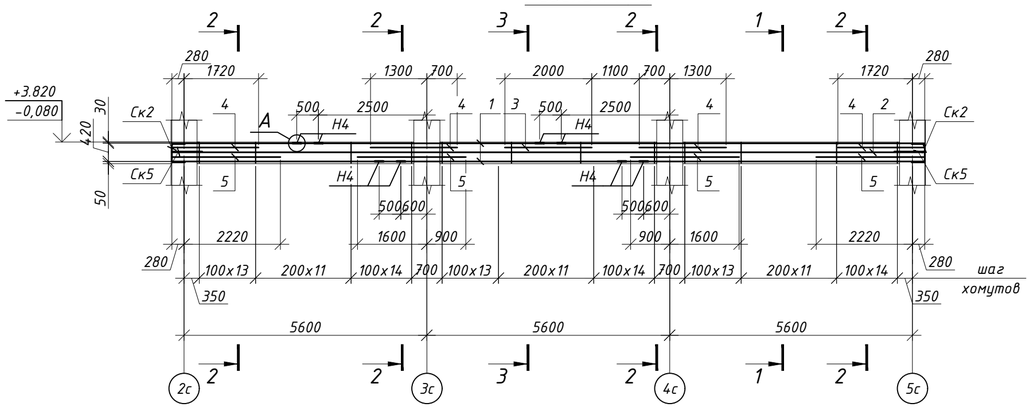


Разрез 1 - 1

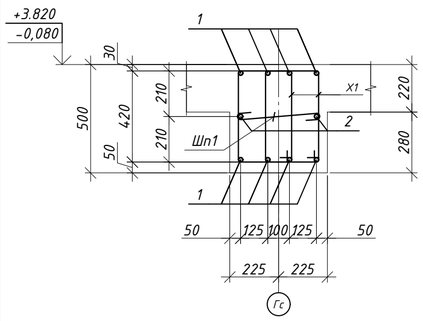

Разрез 2 - 2

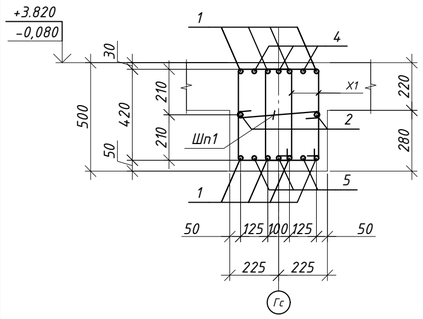

Разрез 3 - 3

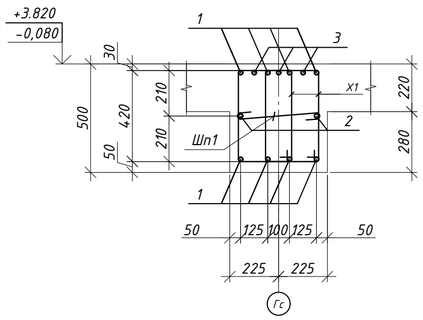


Ведомость деталей

Поз.	Эскиз
Х1	520; 245; 345; 420; по в.г. L=1530
Ск2	220; 420; 220; по н.г. L=860
Ск5	860; 370; 860; по н.г. L=2090
Шп1	370; 100; 100; по в.г. L=570

Таблица размеров накладок

Марка эл-та	dн	L	Вес
	мм.		кг.
Н1	32	320	2.01
Н2	28	280	1.35
Н3	25	250	0.96
Н4	22	220	0.66
Н5	20	200	0.49

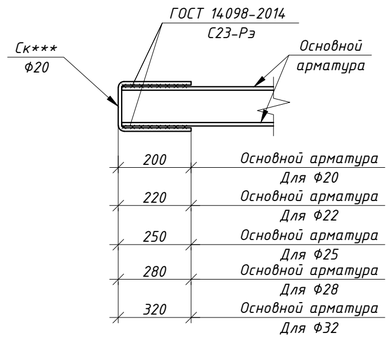


Спецификация элементов


Поз.	Обозначение	Наименование	Кол.	Масса ед.кг	Примечание
		Ригель Рм-5	2		852.69
Х1	ГОСТ 34028-2016(214-210-0101-0003)	Ф 10 А 240 L= 1530	234	0.94	220.73
Ск2	ГОСТ 34028-2016(214-210-0502-0005)	Ф 20 А500С L= 920	8	2.27	18.15
Ск5	ГОСТ 34028-2016(214-210-0502-0001)	Ф 12 А500С L= 2090	2	1.86	3.71
1	ГОСТ 34028-2016(214-210-0502-0006)	Ф 22 А500С L= пог.м.	146	2.98	435.67
Н4	ГОСТ 34028-2016(214-210-0502-0006)	Ф 22 А500С L= 220	32	0.66	21.01
2	ГОСТ 34028-2016(214-210-0502-0001)	Ф 12 А500С L= пог.м.	37	0.89	32.85
3	ГОСТ 34028-2016(214-210-0502-0001)	Ф 12 А500С L= 2000	3	1.78	5.33
4	ГОСТ 34028-2016(214-210-0502-0002)	Ф 14 А500С L= 2000	12	2.42	29.00
5	ГОСТ 34028-2016(214-210-0502-0004)	Ф 18 А500С L= 2500	12	4.99	59.93
Шп1	ГОСТ 34028-2016(214-210-0101-0002)	Ф 8 А 240 L= 570	117	0.22	26.31
		Материалы:			
	(212-101-0901)	Класс бетона С 20/25 (В25), м³			1.89

Позиции со "*" см. "Ведомость деталей" см. на данном листе.

Ведомость расхода стали, кг

Марка элемента	Изделия арматурные									Всего
	Арматура класса									
	А240			А500С						
	ГОСТ 34028-2016(214-210-0101)			ГОСТ 34028-2016(214-210-0502)						
	Ф8	Ф10	Итого	Ф12	Ф14	Ф18	Ф20	Ф22	Итого	
Ригель Рм-5	26.31	220.73	247.05	41.89	29.00	59.93	18.15	456.68	605.65	852.69

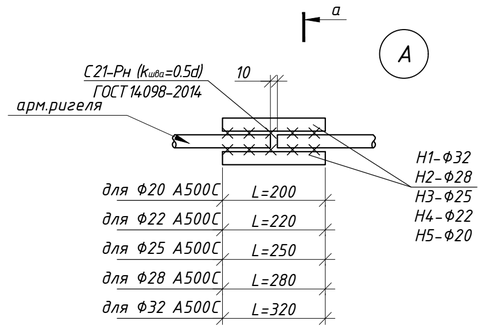

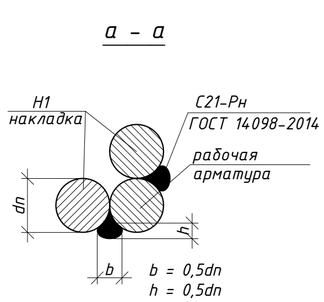


1. Общие указания см. л. - 1.
2. Данный лист читать совместно с л. КЖ-2.2 ... 2.7
3. Стержни, указанные в "Ведомости деталей", должны гнуться механическим способом в холодном состоянии с радиусом гиба 3d - 5d, где d - диаметр стержня


						65П-АИП-2024-1-КЖ	
						Строительство многопрофильной больницы на 250 коек с онкологическим центром и поликлиникой на 350 посещений, по адресу: Медеуский район, г. Алматы	
Изм.	Кол.уч.	Лист	N док.	Подп.	Дата		
						"Блок 1 Секция 1"	Стадия: РП; Лист: 6.5; Листов:
ГКП		Курал М					
Проверил		Кыдырбай А				Ригель Рм-5	АстанаИнжПроект
Разраб.		Ауез Б					
Н.контроль		Ешенкулова					

Формат А2


Ригель Рм-6

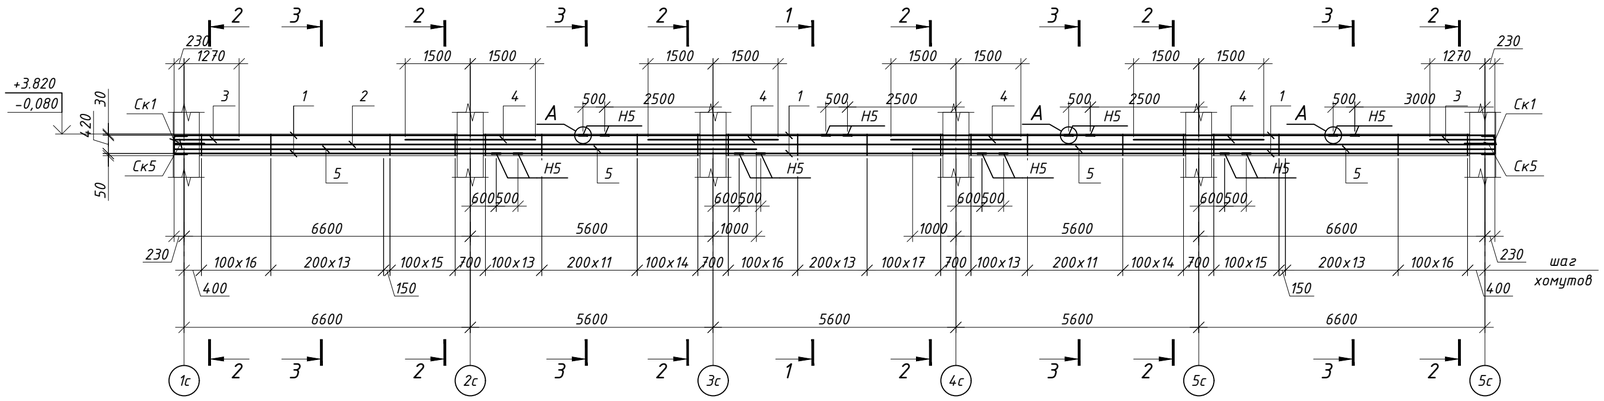


Разрез 1 - 1

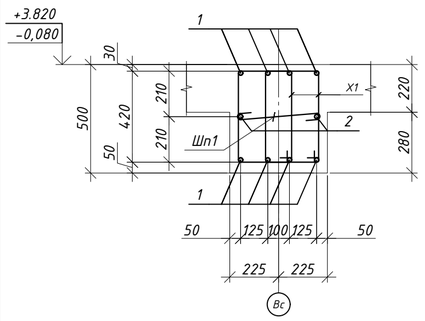

Разрез 2 - 2

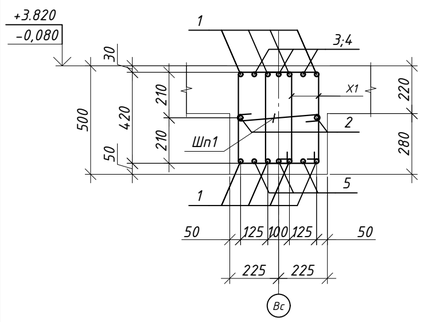

Разрез 3 - 3

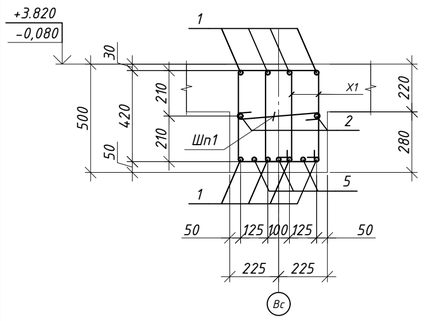

Спецификация элементов

Поз.	Обозначение	Наименование	Кол.	Масса ед.кг	Примечание
		Ригель Рм-6	2		1355.03
Х1	ГОСТ 34028-2016(214-210-0101-0003)	ф 10 А 240 L= 1530	418	0.94	394.30
Ск1	ГОСТ 34028-2016(214-210-0502-0005)	ф 20 А500С L= 820	8	2.02	16.18
Ск5	ГОСТ 34028-2016(214-210-0502-0001)	ф 12 А500С L= 2090	2	1.86	3.71
1	ГОСТ 34028-2016(214-210-0502-0005)	ф 20 А500С L= пог.м.	256	2.47	631.33
Н5	ГОСТ 34028-2016(214-210-0502-0005)	ф 20 А500С L= 200	64	0.49	31.57
2	ГОСТ 34028-2016(214-210-0502-0001)	ф 12 А500С L= пог.м.	64	0.89	56.82
3	ГОСТ 34028-2016(214-210-0502-0001)	ф 12 А500С L= 1500	6	1.33	7.99
4	ГОСТ 34028-2016(214-210-0502-0001)	ф 12 А500С L= 3000	12	2.66	31.96
5	ГОСТ 34028-2016(214-210-0502-0003)	ф 16 А500С L= пог.м.	85	1.58	134.16
Шп1	ГОСТ 34028-2016(214-210-0101-0002)	ф 8 А 240 L= 570	209	0.22	47.01
		Материалы:			
	(212-101-0901)	Класс бетона С 20/25 (В25), м³			3.39

Позиции со "*" см. "Ведомость деталей" см. на данном листе.

Ведомость расхода стали, кг


Марка элемента	Изделия арматурные								Всего
	Арматура класса								
	А240			А500С					
	ГОСТ 34028-2016(214-210-0101)			ГОСТ 34028-2016(214-210-0502)					
	ф8	ф10	Итого	ф12	ф16	ф20	ф22	Итого	
Ригель Рм-6	47.01	394.30	441.31	100.48	134.16	679.08	0.00	913.72	1355.03


Ведомость деталей


Поз.	Эскиз
Х1	520, 245, 345, 420, по в.г., L=1530
Ск1	200, 420, 200, по н.г., L=820
Ск5	860, 370, 860, по н.г., L=2090
Шп1	370, 100, 100, по в.г., L=570

Таблица размеров накладок

Марка эл-та	dн	L	Вес
	мм.		кг.
Н1	32	320	2.01
Н2	28	280	1.35
Н3	25	250	0.96
Н4	22	220	0.66
Н5	20	200	0.49

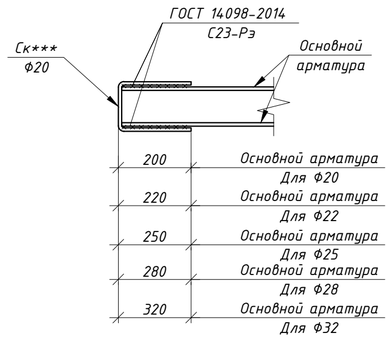

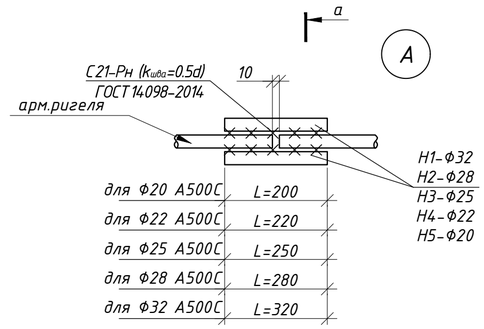

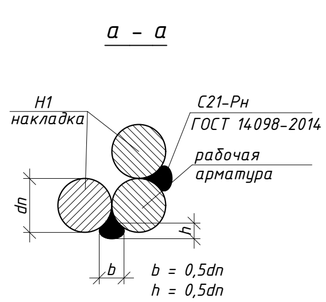


1. Общие указания см. л. - 1.
2. Данный лист читать совместно с л. КЖ-2.2 ... 2.7
3. Стержни, указанные в "Ведомости деталей", должны гнуться механическим способом в холодном состоянии с радиусом гиба 3d - 5d, где d - диаметр стержня


Изм.	Кол.уч.	Лист	N док.	Подп.	Дата	65П-АИП-2024-1-КЖ			
						Строительство многопрофильной больницы на 250 коек с онкологическим центром и поликлиникой на 350 посещений, по адресу: Медеуский район, г. Алматы			
ГКП		Курал М				"Блок 1 Секция 1"	Стадия	Лист	Листов
Проверил		Кыдырбай А					РП	6.6	
Разраб.		Ауез Б				Ригель Рм-6	АстанаИнжПроект		
Н.контроль		Ешенкулова							

Формат А2


Ригель Рм-7

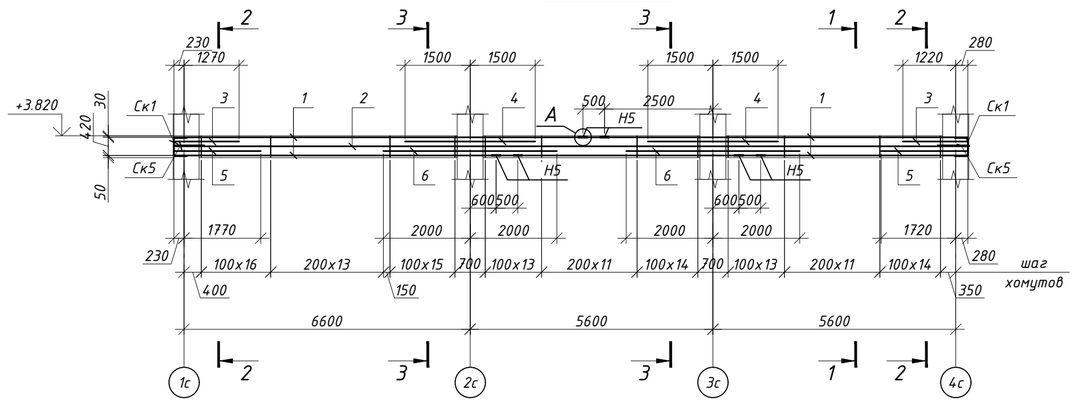


Разрез 1 - 1

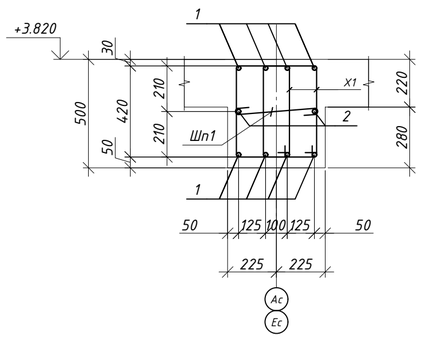

Разрез 2 - 2

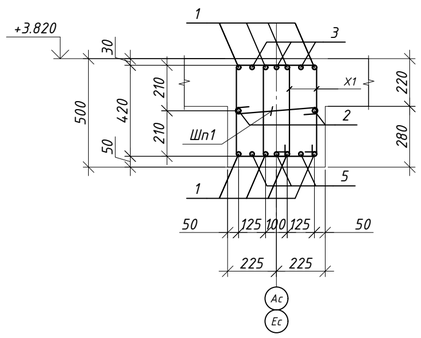

Разрез 3 - 3

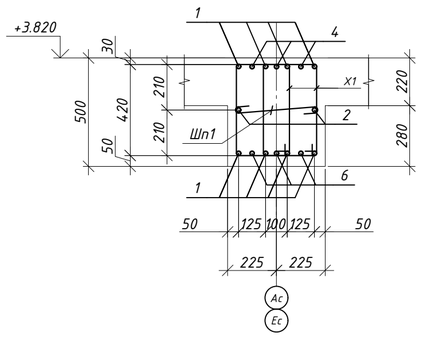

Спецификация элементов

Поз.	Обозначение	Наименование	Кол.	Масса ед.кг	Примечание
		Ригель Рм-7	2		722.07
Х1	ГОСТ 34028-2016(214-210-0101-0002)	Ф 8 А 240 L= 1530	248	0.60	149.72
Ск1	ГОСТ 34028-2016(214-210-0502-0005)	Ф 20 А500С L= 820	8	2.02	16.18
Ск5	ГОСТ 34028-2016(214-210-0502-0001)	Ф 12 А500С L= 2090	2	1.86	3.71
1	ГОСТ 34028-2016(214-210-0502-0005)	Ф 20 А500С L= пог.м.	154	2.47	379.79
Н5	ГОСТ 34028-2016(214-210-0502-0005)	Ф 20 А500С L= 200	24	0.49	11.84
2	ГОСТ 34028-2016(214-210-0502-0001)	Ф 12 А500С L= пог.м.	49	0.89	43.50
3	ГОСТ 34028-2016(214-210-0502-0002)	Ф 14 А500С L= 1500	6	1.81	10.88
4	ГОСТ 34028-2016(214-210-0502-0002)	Ф 14 А500С L= 3000	6	3.63	21.75
5	ГОСТ 34028-2016(214-210-0502-0003)	Ф 16 А500С L= 2000	6	3.16	18.94
6	ГОСТ 34028-2016(214-210-0502-0003)	Ф 16 А500С L= 4000	6	6.31	37.88
Шп1	ГОСТ 34028-2016(214-210-0101-0002)	Ф 8 А 240 L= 570	124	0.22	27.89
		Материалы:			
	(212-101-0901)	Класс бетона С 20/25 (В25), м³			2.01

Позиции со "*" см. "Ведомость деталей" см. на данном листе.

Ведомость расхода стали, кг


Марка элемента	Изделия арматурные							Всего
	Арматура класса							
	А240		А500С					
	ГОСТ 34028-2016(214-210-0101)		ГОСТ 34028-2016(214-210-0502)					
	Ф8	Итого	Ф12	Ф14	Ф16	Ф20	Итого	
Ригель Рм-7	177.61	177.61	47.21	32.63	56.82	407.80	544.46	722.07


Ведомость деталей


Поз.	Эскиз
Х1	520, 245, 345, 420 — по в.г. — L=1530
Ск1	200, 420, 200 — по н.г. — L=820
Ск5	860, 370, 860 — по н.г. — L=2090
Шп1	370, 100, 100 — по в.г. — L=570

Таблица размеров накладок

Марка эл-та	dн	L	вес
	мм.		кг.
Н1	32	320	2.01
Н2	28	280	1.35
Н3	25	250	0.96
Н4	22	220	0.66
Н5	20	200	0.49

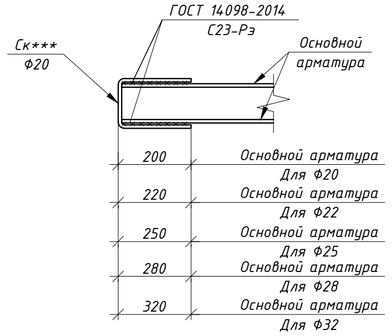

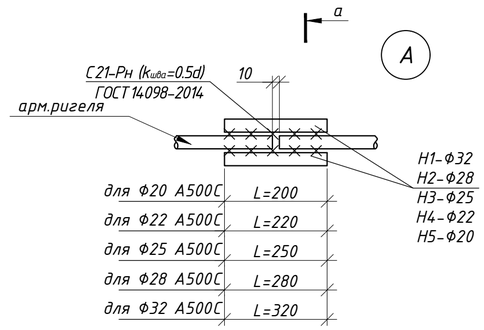

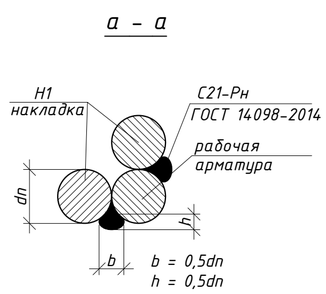


1. Общие указания см. л. - 1.
2. Данный лист читать совместно с л. КЖ-2.2 ... 2.7
3. Стержни, указанные в "Ведомости деталей", должны гнуться механическим способом в холодном состоянии с радиусом гиба 3d - 5d, где d - диаметр стержня


Изм.	Кол.уч.	Лист	N док.	Подп.	Дата	65П-АИП-2024-1-КЖ			
						Строительство многопрофильной больницы на 250 коек с онкологическим центром и поликлиникой на 350 посещений, по адресу: Медеуский район, г. Алматы			
						"Блок 1 Секция 1"	Стадия	Лист	Листов
							РП	6.7	
ГКП		Курал М				Ригель Рм-7	АстанаИнжПроект		
Проверил		Кыдырбай А							
Разраб.		Ауез Б							
Н.контроль		Ешенкулова							

Формат А2


Ригель Рм-8

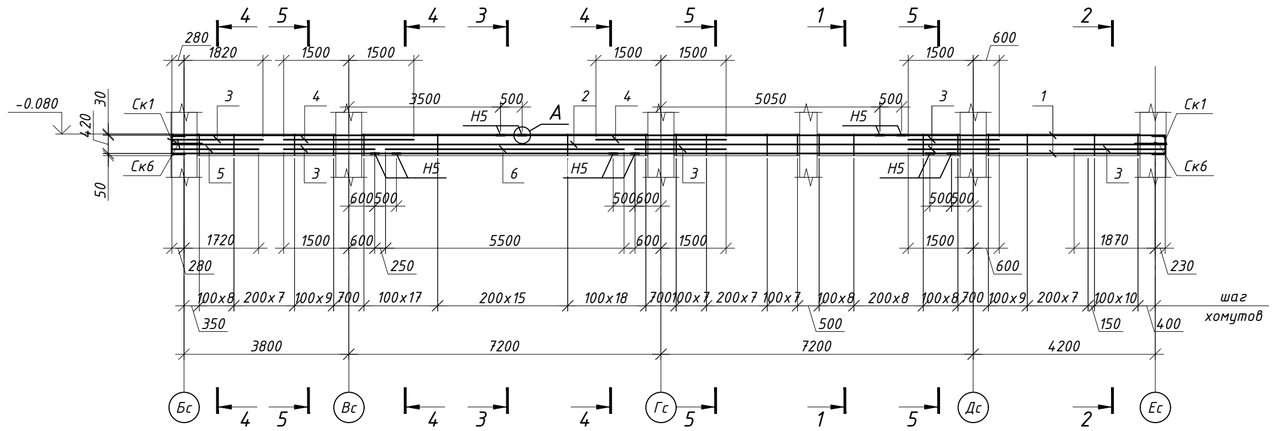


Разрез 1 - 1

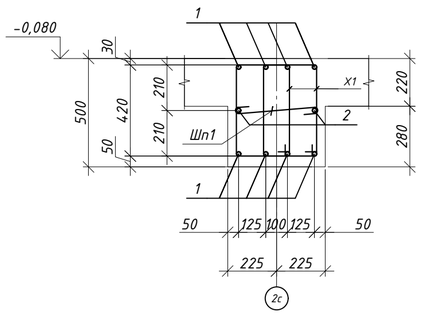


Разрез 4 - 4

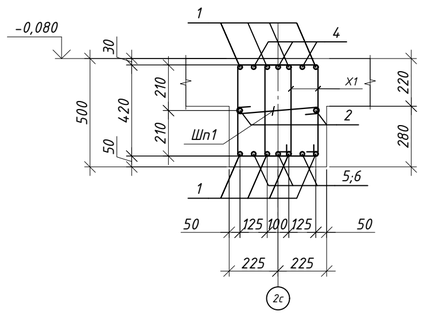


Разрез 2 - 2

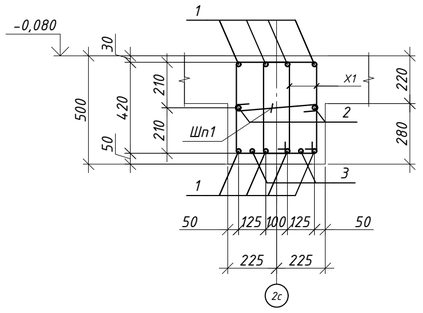

Разрез 5 - 5

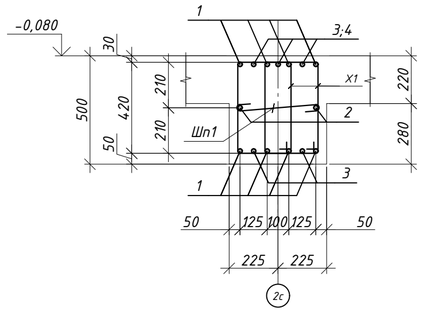

Разрез 3 - 3

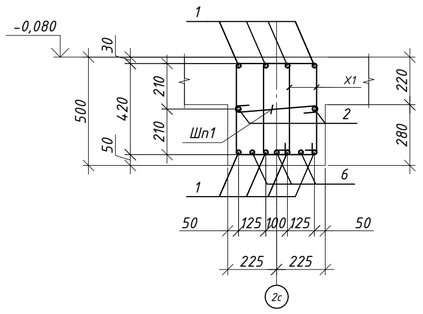


Ведомость деталей

Поз.	Эскиз
X1	520, 245, 345, 420 — по в.г. — L=1530
Ск1	200, 420, 200 — по н.г. — L=820
Ск6	1000, 370, 1000 — по н.г. — L=2370
Шп1	370, 100, 100 — по в.г. — L=570

Таблица размеров накладок

Марка эл-та	dн	L	Вес
	мм.		кг.
Н1	32	320	2.01
Н2	28	280	1.35
Н3	25	250	0.96
Н4	22	220	0.66
Н5	20	200	0.49

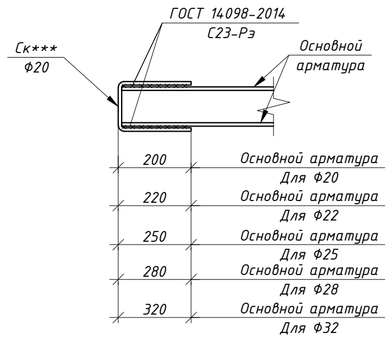


Спецификация элементов


Поз.	Обозначение	Наименование	Кол.	Масса ед.кг	Примечание
		Ригель Рм-8			999.92
X1	ГОСТ 34028-2016(214-210-0101-0003)	Ф 10 А 240 L= 1530	304	0.94	286.76
Ск1	ГОСТ 34028-2016(214-210-0502-0005)	Ф 20 А500С L= 820	8	2.02	16.18
Ск6	ГОСТ 34028-2016(214-210-0502-0002)	Ф 14 А500С L= 2370	2	2.86	5.73
1	ГОСТ 34028-2016(214-210-0502-0005)	Ф 20 А500С L= пог.м.	193	2.47	475.97
Н5	ГОСТ 34028-2016(214-210-0502-0005)	Ф 20 А500С L= 200	40	0.49	19.73
2	ГОСТ 34028-2016(214-210-0502-0002)	Ф 14 А500С L= пог.м.	49	1.21	59.21
3	ГОСТ 34028-2016(214-210-0502-0001)	Ф 12 А500С L= 2100	14	1.86	26.10
4	ГОСТ 34028-2016(214-210-0502-0001)	Ф 12 А500С L= 3000	6	2.66	15.98
5	ГОСТ 34028-2016(214-210-0502-0005)	Ф 20 А500С L= 2000	3	4.93	14.80
6	ГОСТ 34028-2016(214-210-0502-0003)	Ф 16 А500С L= 5500	3	8.68	26.04
Шп1	ГОСТ 34028-2016(214-210-0101-0003)	Ф 10 А 240 L= 570	152	0.35	53.42
		Материалы:			
	(212-101-0901)	Класс бетона С 20/25 (В25), м³			2.46

Позиции со "*" см. "Ведомость деталей" см. на данном листе.

Ведомость расхода стали, кг

Марка элемента	Изделия арматурные							Всего
	Арматура класса							
	А240		А500С					
	ГОСТ 34028-2016(214-210-0101)		ГОСТ 34028-2016(214-210-0502)					
	Ф10	Итого	Ф12	Ф14	Ф16	Ф20	Итого	
Ригель Рм-8	340.18	340.18	42.08	64.94	26.04	526.67	659.74	999.92

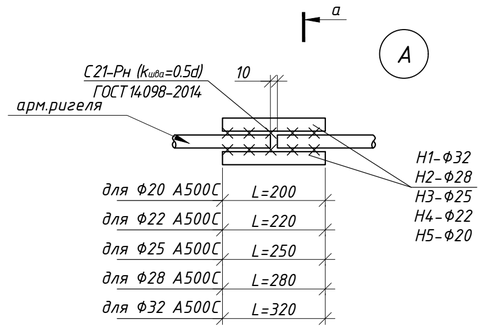

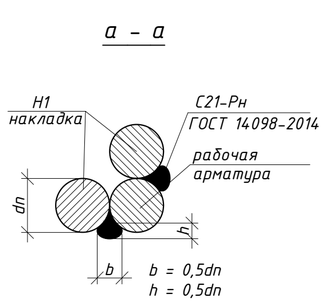


1. Общие указания см. л. - 1.
2. Данный лист читать совместно с л. КЖ-2.2 ... 2.7
3. Стержни, указанные в "Ведомости деталей", должны гнуться механическим способом в холодном состоянии с радиусом гиба 3d - 5d, где d - диаметр стержня


Изм.	Кол.уч.	Лист	N док.	Подп.	Дата	65П-АИП-2024-1-КЖ			
						Строительство многопрофильной больницы на 250 коек с онкологическим центром и поликлиникой на 350 посещений, по адресу: Медеуский район, г. Алматы			
ГКП		Курал М				"Блок 1 Секция 1"	Стадия	Лист	Листов
Проверил		Кыдырбай А					РП	6.8	
Разраб.		Ауез Б				Ригель Рм-8	АстанаИнжПроект		
Н.контроль		Ешенкулова							

Формат А2


Ригель Рм-9

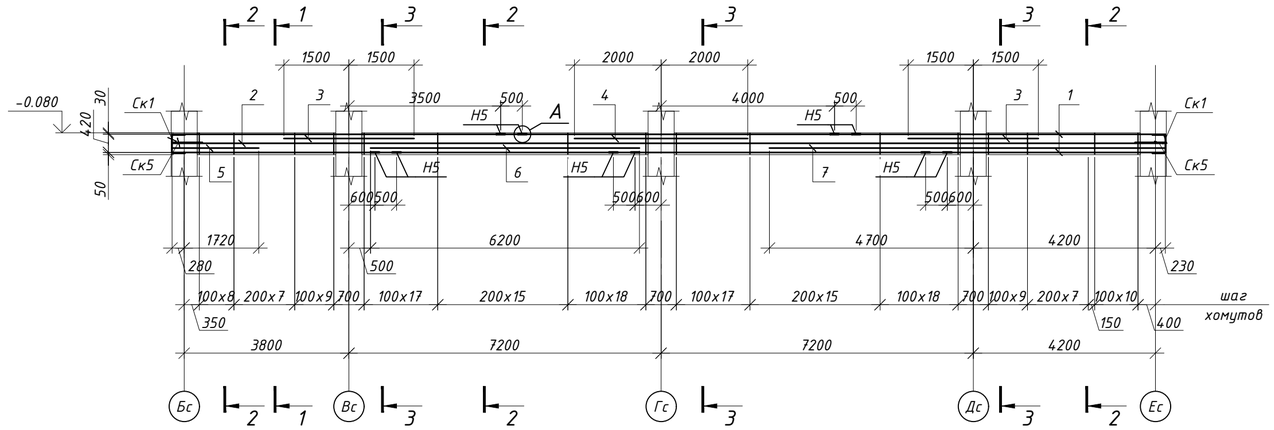


Разрез 1 - 1

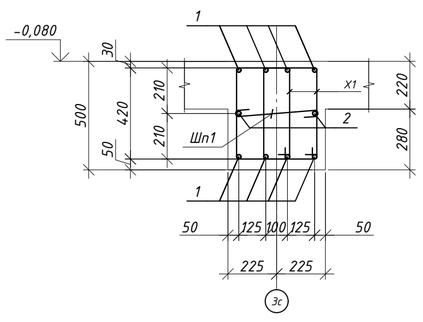

Разрез 2 - 2

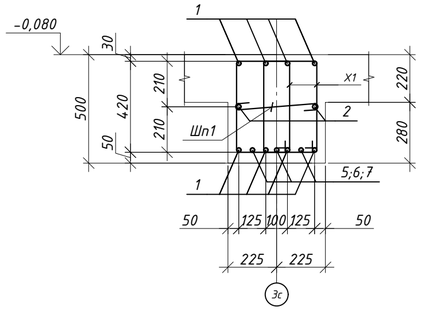

Разрез 3 - 3

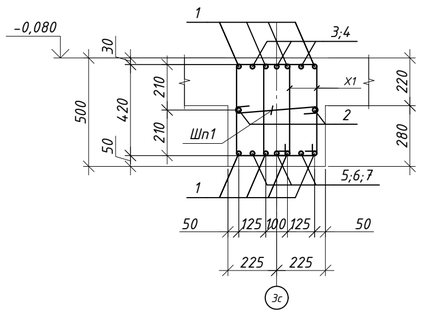


Ведомость деталей

Поз.	Эскиз	
Х1	520, 245, 345, 420	по в.г. L=1530
Ск1	200, 420, 200	по н.г. L=820
Ск5	860, 370, 860	по н.г. L=2090
Шп1	370, 100, 100	по в.г. L=570

Таблица размеров накладок

Марка эл-та	dн	L	вес
	мм.		кг.
Н1	32	320	2.01
Н2	28	280	1.35
Н3	25	250	0.96
Н4	22	220	0.66
Н5	20	200	0.49

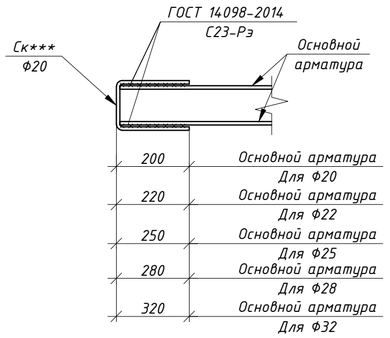


Спецификация элементов


Поз.	Обозначение	Наименование	Кол.	Масса ед.кг	Примечание
		Ригель Рм-9			1161.83
Х1	ГОСТ 34028-2016(214-210-0101-0004)	ф 12 А 240 L= 1530	312	1.36	423.81
Ск1	ГОСТ 34028-2016(214-210-0502-0005)	ф 20 А500С L= 820	8	2.02	16.18
Ск5	ГОСТ 34028-2016(214-210-0502-0001)	ф 12 А500С L= 2090	2	1.86	3.71
1	ГОСТ 34028-2016(214-210-0502-0005)	ф 20 А500С L= пог.м.	193	2.47	475.97
Н5	ГОСТ 34028-2016(214-210-0502-0005)	ф 20 А500С L= 200	40	0.49	19.73
2	ГОСТ 34028-2016(214-210-0502-0001)	ф 12 А500С L= пог.м.	49	0.89	43.50
3	ГОСТ 34028-2016(214-210-0502-0001)	ф 12 А500С L= 3000	6	2.66	15.98
4	ГОСТ 34028-2016(214-210-0502-0004)	ф 18 А500С L= 4000	3	7.99	23.97
5	ГОСТ 34028-2016(214-210-0502-0005)	ф 20 А500С L= 2000	3	4.93	14.80
6	ГОСТ 34028-2016(214-210-0502-0005)	ф 20 А500С L= 6200	3	15.29	45.87
7	ГОСТ 34028-2016(214-210-0502-0003)	ф 16 А500С L= 9130	3	14.41	43.23
Шп1	ГОСТ 34028-2016(214-210-0101-0002)	ф 8 А 240 L= 570	156	0.22	35.09
		Материалы:			
	(212-101-0901)	Класс бетона С 20/25 (В25), м³			2.51

Позиции со "*" см. "Ведомость деталей" см. на данном листе.

Ведомость расхода стали, кг

Марка элемента	Изделия арматурные								Всего
	Арматура класса								
	А240			А500С					
	ГОСТ 34028-2016(214-210-0101)			ГОСТ 34028-2016(214-210-0502)					
	ф8	ф12	Итого	ф12	ф16	ф18	ф20	Итого	
Ригель Рм-9	35.09	423.81	458.89	63.19	43.23	23.97	572.54	702.94	1161.83

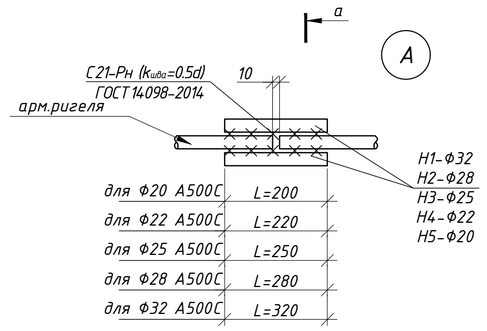

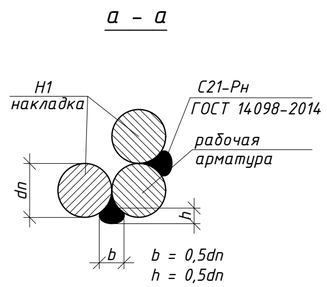


1. Общие указания см. л. - 1.
2. Данный лист читать совместно с л. КЖ-2.2 ... 2.7
3. Стержни, указанные в "Ведомости деталей", должны гнуться механическим способом в холодном состоянии с радиусом гиба 3d - 5d, где d - диаметр стержня


						65П-АИП-2024-1-КЖ	
						Строительство многопрофильной больницы на 250 коек с онкологическим центром и поликлиникой на 350 посещений, по адресу: Медеуский район, г. Алматы	
Изм.	Кол.уч.	Лист	N док.	Подп.	Дата		
						"Блок 1 Секция 1"	Стадия: РП; Лист: 6.9; Листов:
ГКП		Курал М					
Проверил		Кыдырбай А				Ригель Рм-9	АстанаИнжПроект
Разраб.		Ауез Б					
Н.контроль		Ешенкулова					

Формат А2


Ригель Рм-10

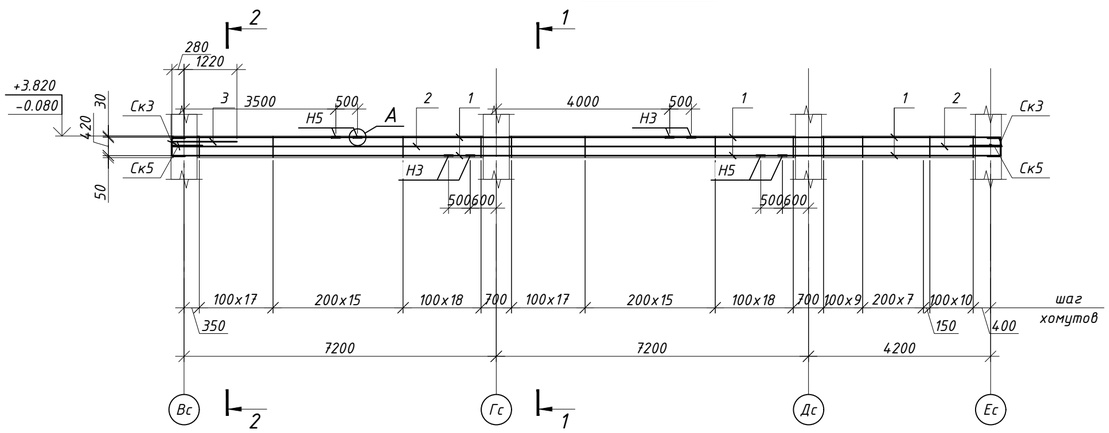

Разрез 1 - 1

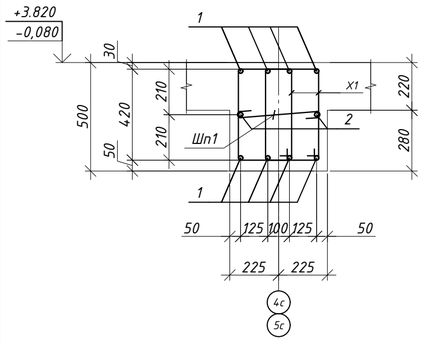

Разрез 2 - 2

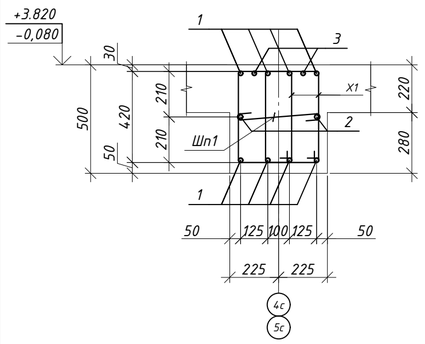

Спецификация элементов

Поз.	Обозначение	Наименование	Кол.	Масса ед.кг	Примечание
		Ригель Рм-10	4		1097.50
Х1	ГОСТ 34028-2016(214-210-0101-0004)	ф 12 А 240 L= 1530	262	1.36	355.89
Ск3	ГОСТ 34028-2016(214-210-0502-0005)	ф 20 А500С L= 920	8	2.27	18.15
Ск5	ГОСТ 34028-2016(214-210-0502-0001)	ф 12 А500С L= 2090	2	1.86	3.71
1	ГОСТ 34028-2016(214-210-0502-0007)	ф 25 А500С L= пог.м.	161	3.85	620.39
Н5	ГОСТ 34028-2016(214-210-0502-0007)	ф 25 А500С L= 250	32	0.96	30.83
2	ГОСТ 34028-2016(214-210-0502-0001)	ф 12 А500С L= пог.м.	41	0.89	36.40
3	ГОСТ 34028-2016(214-210-0502-0001)	ф 12 А500С L= 1500	2	1.33	2.66
Шп1	ГОСТ 34028-2016(214-210-0101-0002)	ф 8 А 240 L= 570	131	0.22	29.46
		Материалы:			
	(212-101-0901)	Класс бетона С 20/25 (В25), м³			2.11

Позиции со "*" см. "Ведомость деталей" см. на данном листе.

Ведомость расхода стали, кг


Марка элемента	Изделия арматурные								Всего
	Арматура класса								
	А240			А500С					
	ГОСТ 34028-2016(214-210-0101)			ГОСТ 34028-2016(214-210-0502)					
	ф8	ф12	Итого	ф12	ф16	ф20	ф25	Итого	
Ригель Рм-10	29.46	355.89	385.35	42.77	0.00	18.15	651.22	712.14	1097.50


Ведомость деталей


Поз.	Эскиз
Х1	520, 24.5, 34.5, 420; по в.г. L=1530
Ск3	250, 420, 250; по н.г. L=920
Ск5	860, 370, 860; по н.г. L=2090
Шп1	370, 100, 100; по в.г. L=570

Таблица размеров накладок

Марка эл-та	dн	L	вес
	мм.		кг.
Н1	32	320	2.01
Н2	28	280	1.35
Н3	25	250	0.96
Н4	22	220	0.66
Н5	20	200	0.49

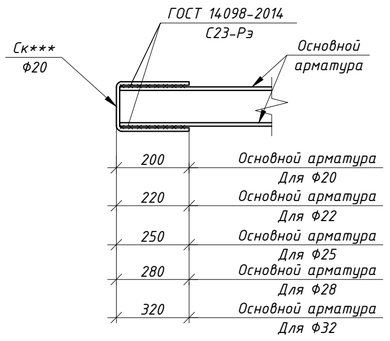

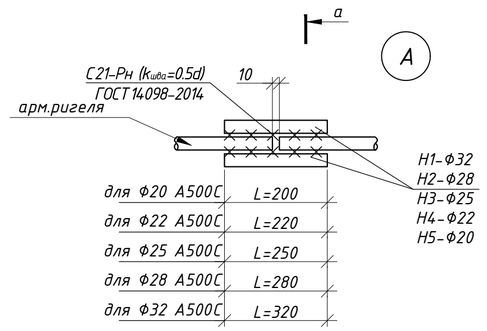

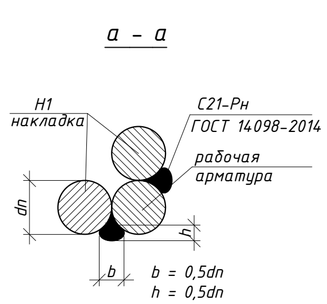


1. Общие указания см. л. - 1.
2. Данный лист читать совместно с л. КЖ-2.2 ... 2.7
3. Стержни, указанные в "Ведомости деталей", должны гнуться механическим способом в холодном состоянии с радиусом гиба 3d - 5d, где d - диаметр стержня


Изм.	Кол.уч.	Лист	N док.	Подп.	Дата	65П-АИП-2024-1-КЖ			
						Строительство многопрофильной больницы на 250 коек с онкологическим центром и поликлиникой на 350 посещений, по адресу: Медеуский район, г. Алматы			
ГКП		Курал М				"Блок 1 Секция 1"	Стадия	Лист	Листов
Проверил		Кыдырбай А					РП	6.10	
Разраб.		Ауез Б				Ригель Рм-10	АстанаИнжПроект		
Н.контроль		Ешенкулова							

Формат А2

Ригель Рм-11

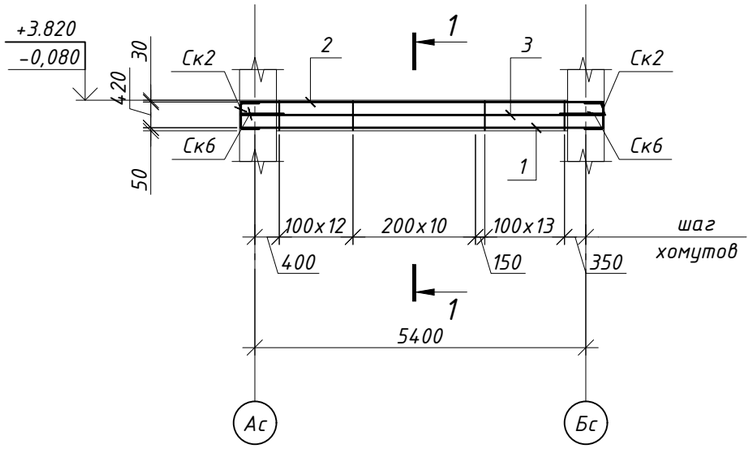

Разрез 1 - 1

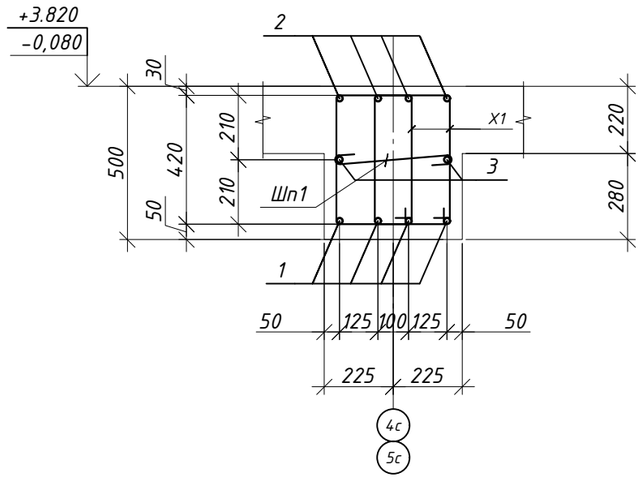

Спецификация элементов





Поз.	Обозначение	Наименование	Кол.	Масса ед.кг	Примечание
		Ригель Рм-11	3		220.25
X1	ГОСТ 34028-2016(214-210-0101-0002)	ф 8 А 240 L= 1530	76	0.60	45.88
Ск2	ГОСТ 34028-2016(214-210-0502-0005)	ф 20 А500С L= 860	8	2.12	16.97
Ск6	ГОСТ 34028-2016(214-210-0502-0002)	ф 14 А500С L= 2370	2	2.86	5.73
1	ГОСТ 34028-2016(214-210-0502-0006)	ф 22 А500С L= 5910	4	17.64	70.54
2	ГОСТ 34028-2016(214-210-0502-0005)	ф 20 А500С L= 5910	4	14.57	58.30
3	ГОСТ 34028-2016(214-210-0502-0002)	ф 14 А500С L= 5910	2	7.14	14.28
Шп1	ГОСТ 34028-2016(214-210-0101-0002)	ф 8 А 240 L= 570	38	0.22	8.55
		Материалы:			
	(212-101-0901)	Класс бетона С 20/25 (В25), м³			0.60


Позиции со "*" см. "Ведомость деталей" см. на данном листе.

Ведомость расхода стали, кг

Марка элемента	Изделия арматурные						Всего
	Арматура класса						
	А240		А500С				
	ГОСТ 34028-2016(214-210-0101)		ГОСТ 34028-2016(214-210-0502)				
	ф8	Итого	ф14	ф20	ф22	Итого	
Ригель Рм-11	54.43	54.43	20.01	75.27	70.54	165.82	220.25

Ведомость деталей

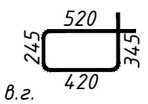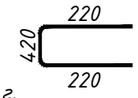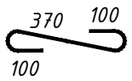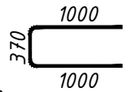Поз.	Эскиз	Поз.	Эскиз
X1	 по в.г. L=1530	Ск2	 по н.г. L=860
Шп1	 по в.г. L=570	Ск6	 по н.г. L=2370

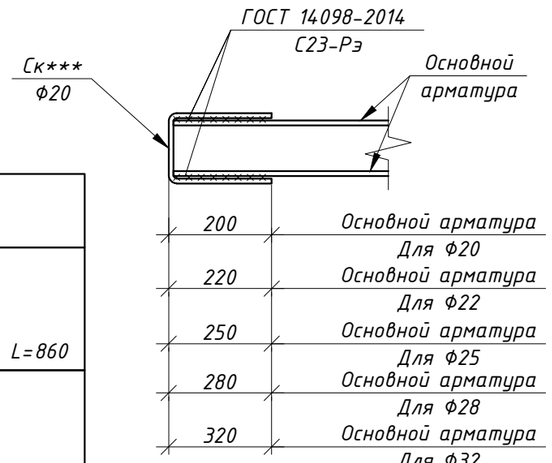


1. Общие указания см. л. - 1.
2. Данный лист читать совместно с л. КЖ-2.2 ... 2.7
3. Стержни, указанные в "Ведомости деталей", должны гнуться механическим способом в холодном состоянии с радиусом гиба 3d - 5d, где d - диаметр стержня


Изм.	Кол.уч.	Лист	N док.	Подп.	Дата	65П-АИП-2024-1-КЖ			
						Строительство многопрофильной больницы на 250 коек с онкологическим центром и поликлиникой на 350 посещений, по адресу: Медеуский район, г. Алматы			
						"Блок 1 Секция 1"	Стадия	Лист	Листов
							РП	6.11	
ГКП		Курал М				Ригель Рм-11	АстанаИнжПроект		
Проверил		Кыдырбай А							
Разраб.		Ауез Б							
Н.контроль		Ешенкулова							

Формат А3

Ригель Рм-12

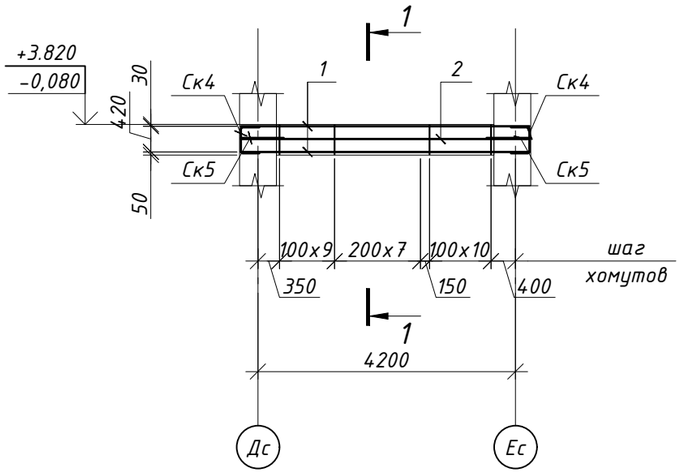

Разрез 1 - 1

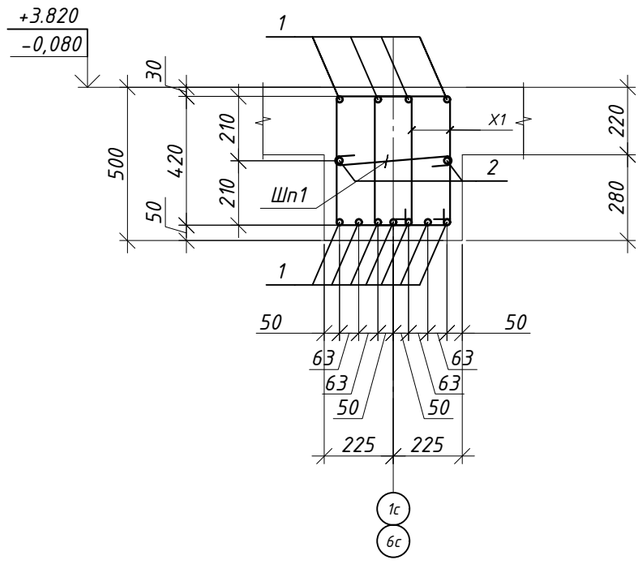

Спецификация элементов

Поз.	Обозначение	Наименование	Кол.	Масса ед.кг	Примечание
		Ригель Рм-12	3		315.07
X1	ГОСТ 34028-2016(214-210-0101-0002)	ф 8 A 240 L= 1530	58	0.60	35.02
Ск4	ГОСТ 34028-2016(214-210-0502-0005)	ф 20 A500C L= 980	8	2.42	19.33
Ск5	ГОСТ 34028-2016(214-210-0502-0001)	ф 12 A500C L= 2090	2	1.86	3.71
1	ГОСТ 34028-2016(214-210-0502-0008)	ф 28 A500C L= 4170	11	20.16	221.72
2	ГОСТ 34028-2016(214-210-0502-0001)	ф 12 A500C L= 4170	2	3.70	7.40
Шп1	ГОСТ 34028-2016(214-210-0101-0002)	ф 8 A 240 L= 570	124	0.22	27.89
		Материалы:			
	(212-101-0901)	Класс бетона С 20/25 (В25), м^3			0.45


Позиции со "*" см. "Ведомость деталей" см. на данном листе.

Ведомость расхода стали, кг

Марка элемента	Изделия арматурные						Всего
	Арматура класса						
	A240		A500C				
	ГОСТ 34028-2016(214-210-0101)		ГОСТ 34028-2016(214-210-0502)				
	ф8	Итого	ф12	ф20	ф28	Итого	
Ригель Рм-12	62.90	62.90	11.12	19.33	221.72	252.17	315.07

Ведомость деталей

Поз.	Эскиз	Поз.	Эскиз
X1	520, 245, 345, 420; по в.г. L=1530	Ск4	280, 420, 280; по н.г. L=980
Шп1	370, 100, 100; по в.г. L=570	Ск5	860, 370, 860; по н.г. L=2090

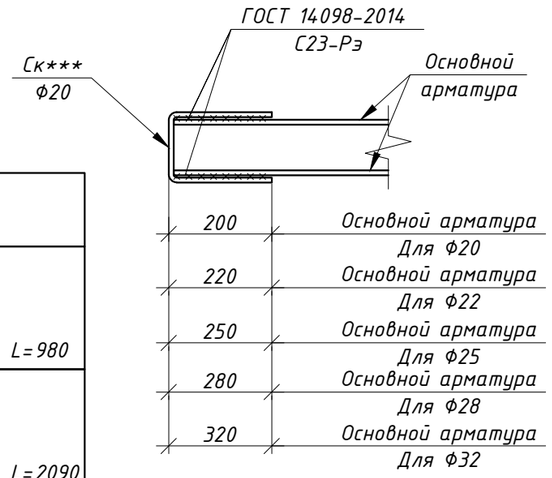


1. Общие указания см. л. - 1.
2. Данный лист читать совместно с л. КЖ-2.2 ... 2.7
3. Стержни, указанные в "Ведомости деталей", должны гнуться механическим способом в холодном состоянии с радиусом гиба 3d - 5d, где d - диаметр стержня

Изм.	Кол.уч.	Лист	N док.	Подп.	Дата	65П-АИП-2024-1-КЖ		
						Строительство многопрофильной больницы на 250 коек с онкологическим центром и поликлиникой на 350 посещений, по адресу: Медеуский район, г. Алматы		
						"Блок 1 Секция 1"	Стадия: РП	Лист: 6.12 / Листов:
ГКП		Курал М				Ригель Рм-12	АстанаИнжПроект	
Проверил		Кыдырбай А						
Разраб.		Ауез Б						
Н.контроль		Ешенкулова						

Формат А3

Ригель Рм-13

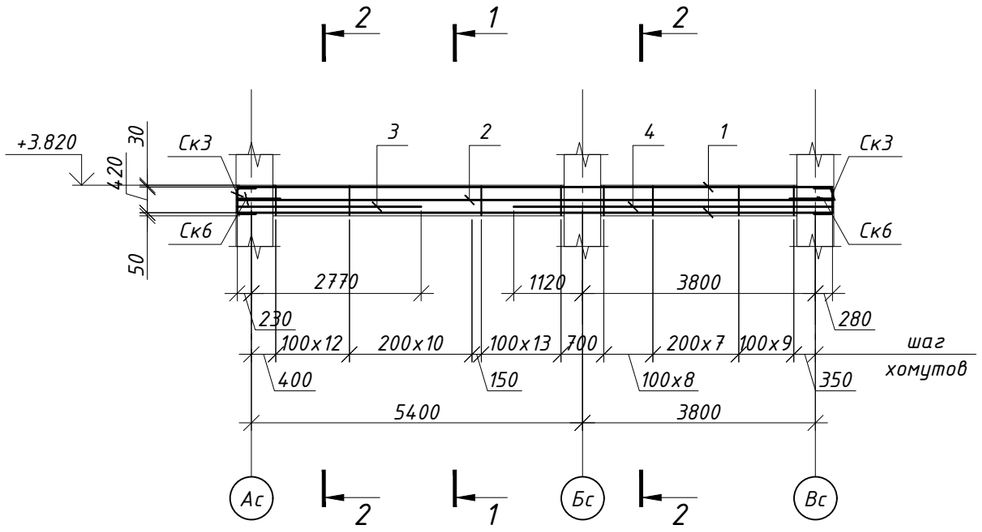


Спецификация элементов


Поз.	Обозначение	Наименование	Кол.	Масса ед.кг	Примечание
		Ригель Рм-13	2		553.11
Х1	ГОСТ 34028-2016(214-210-0101-0003)	ф 10 А 240 L= 1530	126	0.94	118.86
СкЗ	ГОСТ 34028-2016(214-210-0502-0005)	ф 20 А500С L= 920	8	2.27	18.15
Ск6	ГОСТ 34028-2016(214-210-0502-0002)	ф 14 А500С L= 2370	2	2.86	5.73
1	ГОСТ 34028-2016(214-210-0502-0007)	ф 25 А500С L= 9710	8	37.42	299.33
2	ГОСТ 34028-2016(214-210-0502-0002)	ф 14 А500С L= 9710	2	11.73	23.47
3	ГОСТ 34028-2016(214-210-0502-0006)	ф 22 А500С L= 3000	3	8.95	26.86
4	ГОСТ 34028-2016(214-210-0502-0006)	ф 22 А500С L= 5200	3	15.52	46.55
Шп1	ГОСТ 34028-2016(214-210-0101-0002)	ф 8 А 240 L= 570	63	0.22	14.17
		Материалы:			
	(212-101-0901)	Класс бетона С 20/25 (В25), м³			1.00

Позиции со "*" см. "Ведомость деталей" см. на данном листе.

Разрез 1 - 1

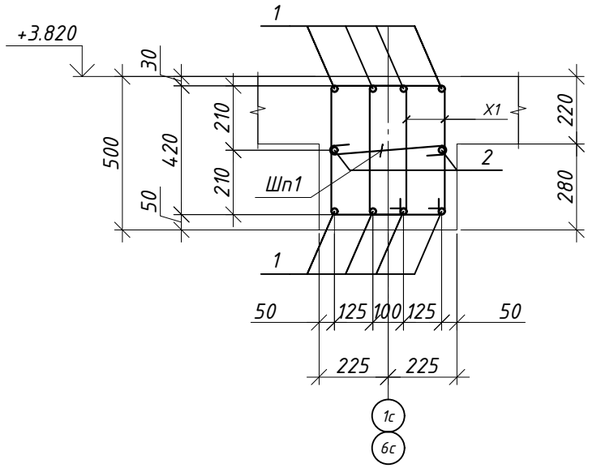


Разрез 2 - 2

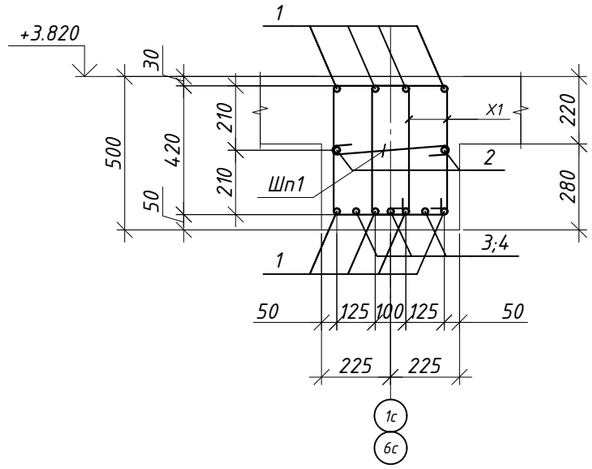

Ведомость деталей

Поз.	Эскиз	Поз.	Эскиз
Х1	520, 245, 345, 420; по в.г. L=1530	СкЗ	250, 420, 250; по н.г. L=920
Шп1	370, 100, 100; по в.г. L=570	Ск6	1000, 370, 1000; по н.г. L=2370

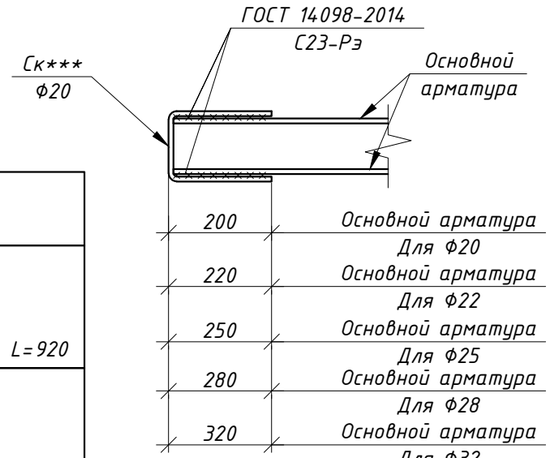

Ведомость расхода стали, кг


Марка элемента	Изделия арматурные								Всего
	Арматура класса								
	А240			А500С					
	ГОСТ 34028-2016(214-210-0101)			ГОСТ 34028-2016(214-210-0502)					
	ф8	ф10	Итого	ф14	ф20	ф22	ф25	Итого	
Ригель Рм-13	14.17	118.86	133.03	29.20	18.15	73.41	299.33	420.08	553.11

1. Общие указания см. л. - 1.
2. Данный лист читать совместно с л. КЖ-2.2 ... 2.7
3. Стержни, указанные в "Ведомости деталей", должны гнуться механическим способом в холодном состоянии с радиусом гиба 3d - 5d, где d - диаметр стержня


Изм.	Кол.уч.	Лист	N док.	Подп.	Дата	65П-АИП-2024-1-КЖ			
						Строительство многопрофильной больницы на 250 коек с онкологическим центром и поликлиникой на 350 посещений, по адресу: Медеуский район, г. Алматы			
ГКП		Курал М				"Блок 1 Секция 1"	Стадия	Лист	Листов
Проверил		Кыдырбай А					РП	6.13	
Разраб.		Ауез Б				Ригель Рм-13	АстанаИнжПроект		
Н.контроль		Ешенкулова							

Формат А3


Ригель Рм-14

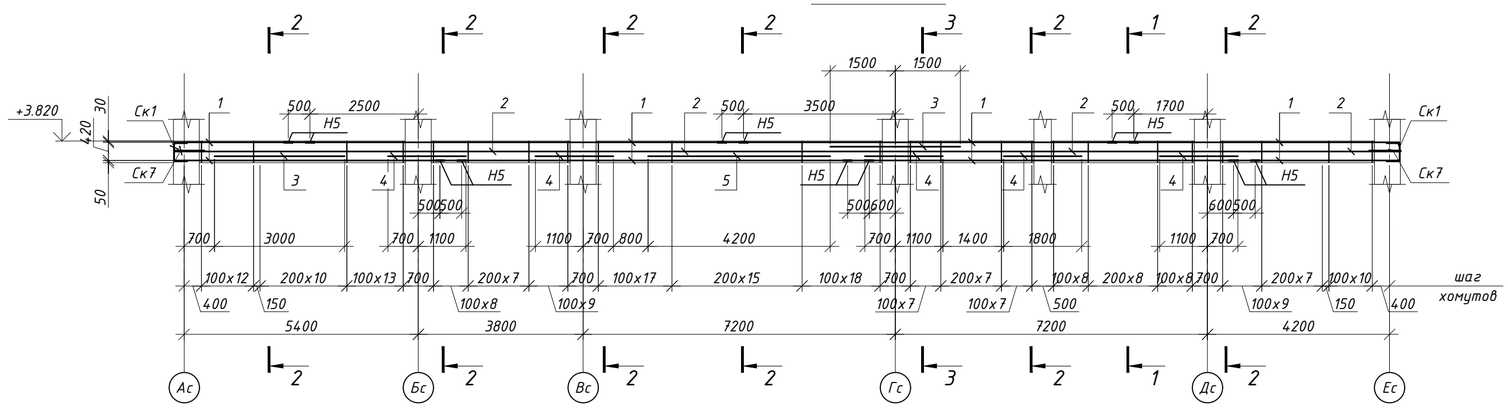


Разрез 1 - 1

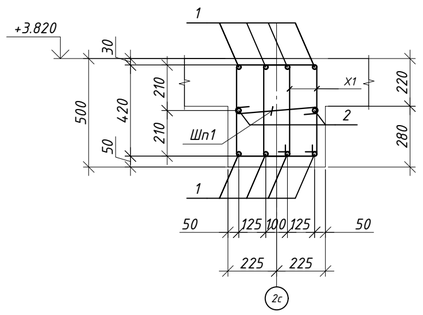

Разрез 2 - 2

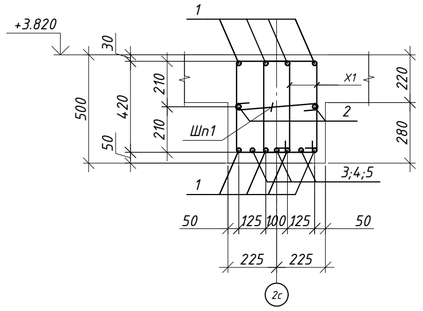

Разрез 3 - 3

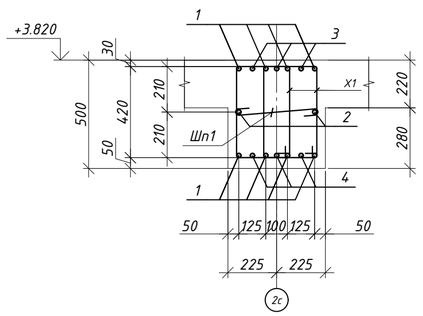

Спецификация элементов

Поз.	Обозначение	Наименование	Кол.	Масса ед.кг	Примечание
		Ригель Рм-14			1390.10
X1	ГОСТ 34028-2016(214-210-0101-0004)	Ф 12 А 240 L= 1530	378	1.36	513.46
Ск1	ГОСТ 34028-2016(214-210-0502-0005)	Ф 20 А500С L= 820	8	2.02	16.18
Ск7	ГОСТ 34028-2016(214-210-0502-0003)	Ф 16 А500С L= 2650	2	4.18	8.37
1	ГОСТ 34028-2016(214-210-0502-0005)	Ф 20 А500С L= пог.м.	238	2.47	586.94
Н5	ГОСТ 34028-2016(214-210-0502-0005)	Ф 20 А500С L= 200	48	0.49	23.68
2	ГОСТ 34028-2016(214-210-0502-0003)	Ф 16 А500С L= пог.м.	60	1.58	94.70
3	ГОСТ 34028-2016(214-210-0502-0001)	Ф 12 А500С L= 3000	6	2.66	15.98
4	ГОСТ 34028-2016(214-210-0502-0001)	Ф 12 А500С L= 1800	15	1.60	23.97
5	ГОСТ 34028-2016(214-210-0502-0001)	Ф 12 А500С L= 4200	3	3.73	11.19
Шп1	ГОСТ 34028-2016(214-210-0502-0001)	Ф 12 А 240 L= 570	189	0.51	95.64
		Материалы:			
	(212-101-0901)	Класс бетона С 20/25 (В25), м³			3.06

Позиции со "*" см. "Ведомость деталей" см. на данном листе.

Ведомость расхода стали, кг

Марка элемента	Изделия арматурные							Всего
	Арматура класса							
	А240		А500С					
	ГОСТ 34028-2016(214-210-0101)		ГОСТ 34028-2016(214-210-0502)					
	Ф12	Итого	Ф12	Ф16	Ф18	Ф20	Итого	
Ригель Рм-14	609.10	609.10	51.14	103.07	0.00	626.80	781.00	1390.10


Разрез 3 - 3


Ведомость деталей


Поз.	Эскиз
X1	520, 245, 34.5, 420; по в.г. L=1530
Ск1	200, 420, 200; по н.г. L=820
Ск7	1140, 370, 1140; по н.г. L=2650
Шп1	370, 100, 100; по в.г. L=570

Таблица размеров накладок

Марка эл-та	dн	L	Вес
	мм.		кг.
Н1	32	320	2.01
Н2	28	280	1.35
Н3	25	250	0.96
Н4	22	220	0.66
Н5	20	200	0.49

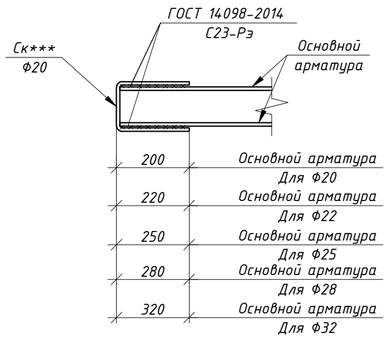

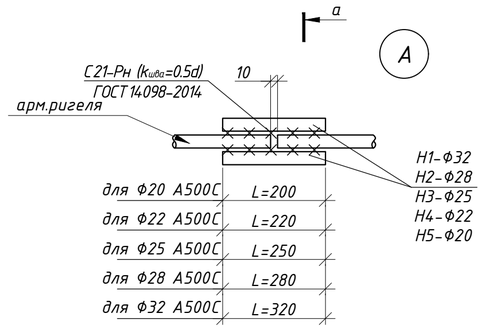


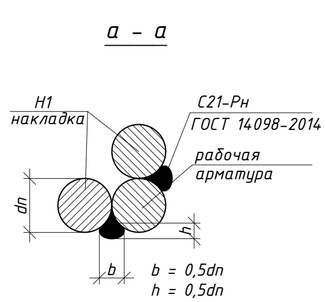


1. Общие указания см. л. - 1.
2. Данный лист читать совместно с л. КЖ-2.2 ... 2.7
3. Стержни, указанные в "Ведомости деталей", должны гнуться механическим способом в холодном состоянии с радиусом гиба 3d - 5d, где d - диаметр стержня

Изм.	Кол.уч.	Лист	N док.	Подп.	Дата	65П-АИП-2024-1-КЖ			
						Строительство многопрофильной больницы на 250 коек с онкологическим центром и поликлиникой на 350 посещений, по адресу: Медеуский район, г. Алматы			
ГКП		Курал М				"Блок 1 Секция 1"	Стадия	Лист	Листов
Проверил		Кыдырбай А					РП	6.14	
Разраб.		Ауез Б				Ригель Рм-14	АстанаИнжПроект		
Н.контроль		Ешенкулова					Формат А2		


Ригель Рм-15

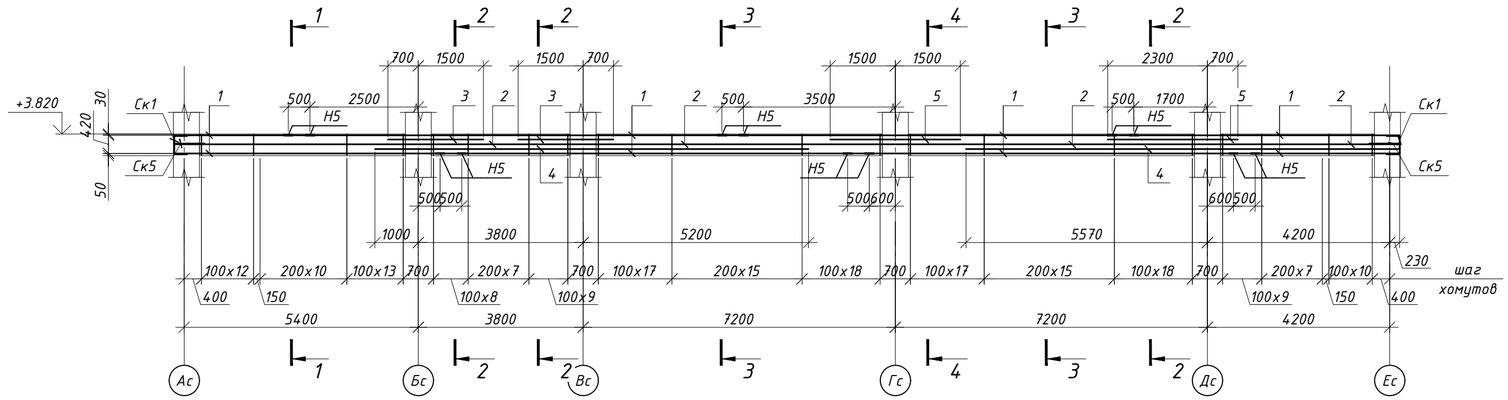


Разрез 1 - 1

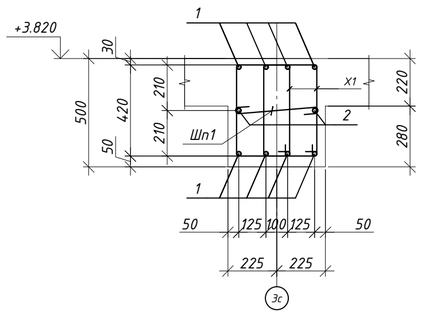


Разрез 4 - 4

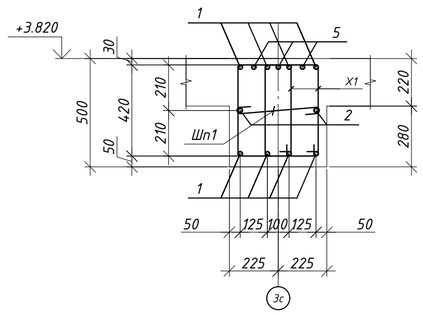

Разрез 2 - 2

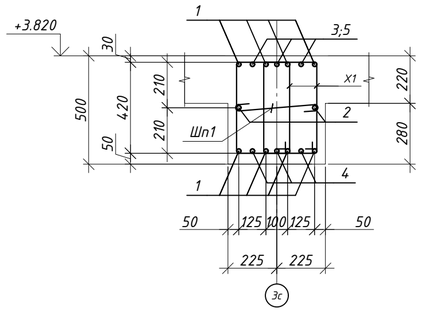

Разрез 3 - 3

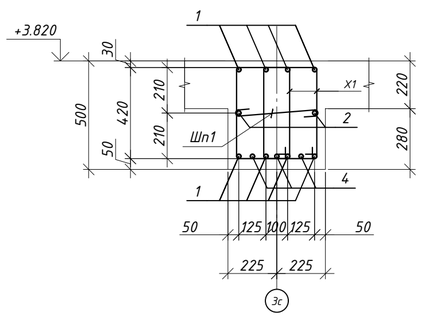

Спецификация элементов

Поз.	Обозначение	Наименование	Кол.	Масса ед.кг	Примечание
		Ригель Рм-15			1361.72
X1	ГОСТ 34028-2016(214-210-0101-0004)	ф 12 А 240 L= 1530	386	1.36	524.33
Ск1	ГОСТ 34028-2016(214-210-0502-0005)	ф 20 А500С L= 820	8	2.02	16.18
Ск5	ГОСТ 34028-2016(214-210-0502-0001)	ф 12 А500С L= 2090	2	1.86	3.71
1	ГОСТ 34028-2016(214-210-0502-0005)	ф 20 А500С L= пог.м.	238	2.47	586.94
Н5	ГОСТ 34028-2016(214-210-0502-0005)	ф 20 А500С L= 200	48	0.49	23.68
2	ГОСТ 34028-2016(214-210-0502-0001)	ф 12 А500С L= пог.м.	60	0.89	53.27
3	ГОСТ 34028-2016(214-210-0502-0002)	ф 14 А500С L= 2200	6	2.66	15.95
4	ГОСТ 34028-2016(214-210-0502-0002)	ф 14 А500С L= 10000	6	12.08	72.50
5	ГОСТ 34028-2016(214-210-0502-0002)	ф 14 А500С L= 3000	6	3.63	21.75
Шп1	ГОСТ 34028-2016(214-210-0101-0002)	ф 8 А 240 L= 570	193	0.22	43.41
		Материалы:			
	(212-101-0901)	Класс бетона С 20/25 (В25), м³			3.11

Позиции со "*" см. "Ведомость деталей" см. на данном листе.

Ведомость расхода стали, кг


Марка элемента	Изделия арматурные								Всего
	Арматура класса								
	А240			А500С					
	ГОСТ 34028-2016(214-210-0101)			ГОСТ 34028-2016(214-210-0502)					
	ф8	ф12	Итого	ф12	ф14	ф18	ф20	Итого	
Ригель Рм-15	43.41	524.33	567.73	56.98	110.21	0.00	626.80	793.98	1361.72


Ведомость деталей


Поз.	Эскиз
X1	520, 245, 34.5, 420; по в.г. L=1530
Ск1	200, 420, 200; по н.г. L=820
Ск5	860, 370, 860; по н.г. L=2090
Шп1	370, 100, 100; по в.г. L=570

Таблица размеров накладок

Марка эл-та	dн	L	Вес
	мм.		кг.
Н1	32	320	2.01
Н2	28	280	1.35
Н3	25	250	0.96
Н4	22	220	0.66
Н5	20	200	0.49

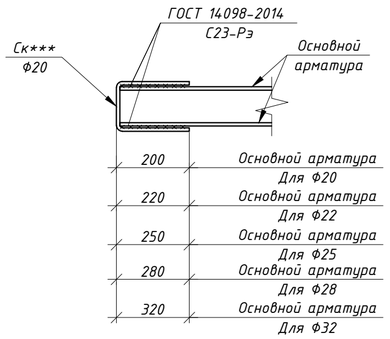

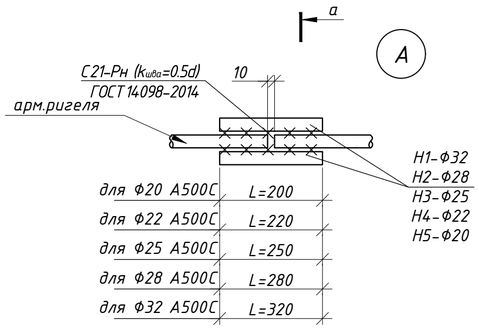

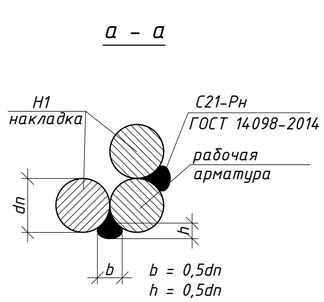


1. Общие указания см. л. - 1.
2. Данный лист читать совместно с л. КЖ-2.2 ... 2.7
3. Стержни, указанные в "Ведомости деталей", должны гнуться механическим способом в холодном состоянии с радиусом гиба 3d - 5d, где d - диаметр стержня


Изм.	Кол.уч.	Лист	N док.	Подп.	Дата	65П-АИП-2024-1-КЖ			
						Строительство многопрофильной больницы на 250 коек с онкологическим центром и поликлиникой на 350 посещений, по адресу: Медеуский район, г. Алматы			
ГКП		Курал М				"Блок 1 Секция 1"	Стадия	Лист	Листов
Проверил		Кыдырбай А					РП	6.15	
Разраб.		Ауез Б				Ригель Рм-15	АстанаИнжПроект		
Н.контроль		Ешенкулова							

Формат А2


Ригель Рм-16

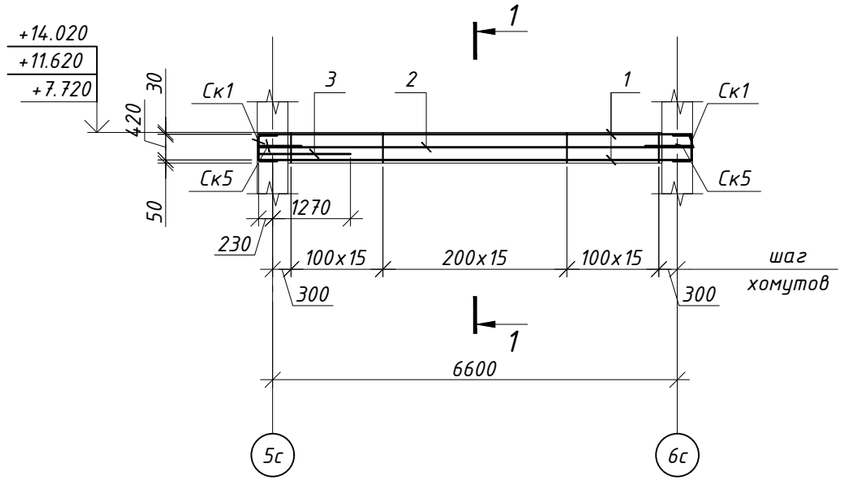

Разрез 1 - 1

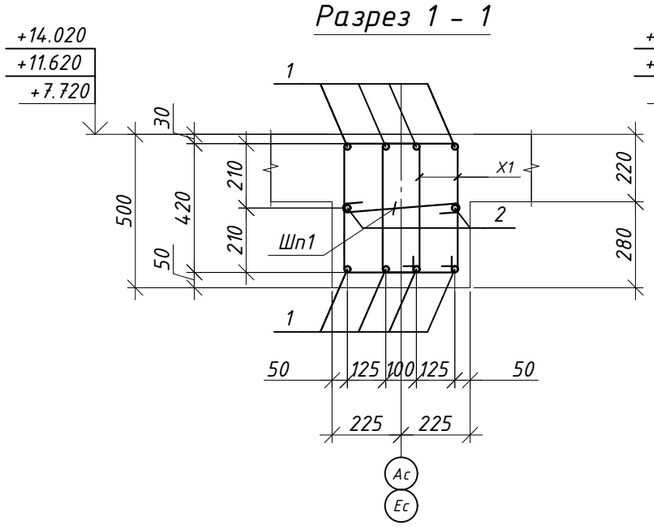

Разрез 2 - 2

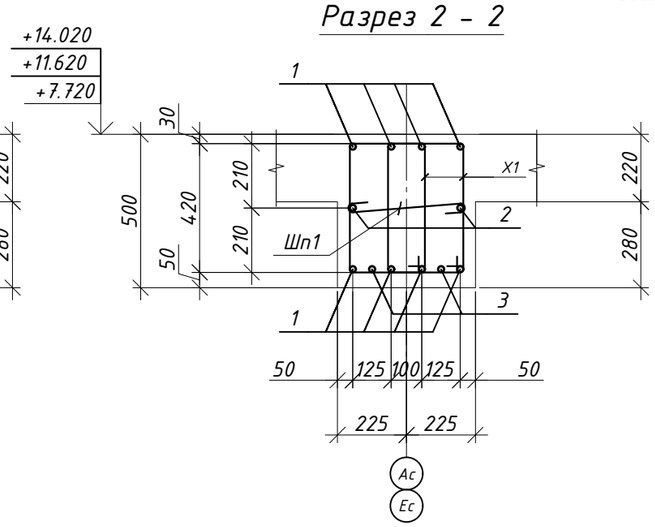

Спецификация элементов

Поз.	Обозначение	Наименование	Кол.	Масса ед.кг	Примечание
		Ригель Рм-16	6		279.56
X1	ГОСТ 34028-2016(214-210-0101-0003)	ф 10 А 240 L= 1530	94	0.94	88.67
Ск1	ГОСТ 34028-2016(214-210-0502-0005)	ф 20 А500С L= 820	8	2.02	16.18
Ск5	ГОСТ 34028-2016(214-210-0502-0001)	ф 12 А500С L= 2090	2	1.86	3.71
1	ГОСТ 34028-2016(214-210-0502-0005)	ф 20 А500С L= 7060	8	17.41	139.29
2	ГОСТ 34028-2016(214-210-0502-0001)	ф 12 А500С L= 7060	2	6.27	12.54
3	ГОСТ 34028-2016(214-210-0502-0001)	ф 12 А500С L= 1500	2	1.33	2.66
Шп1	ГОСТ 34028-2016(214-210-0101-0003)	ф 10 А 240 L= 570	47	0.35	16.52
		Материалы:			
	(212-101-0901)	Класс бетона С 20/25 (В25), м³			0.77


Позиции со "*" см. "Ведомость деталей" см. на данном листе.

Ведомость расхода стали, кг

Марка элемента	Изделия арматурные						Всего
	Арматура класса						
	А240		А500С				
	ГОСТ 34028-2016(214-210-0101)		ГОСТ 34028-2016(214-210-0502)				
	ф10	Итого	ф12	ф20	ф25	Итого	
Ригель Рм-16	105.19	105.19	18.91	155.47	0.00	174.38	279.56

Ведомость деталей

Поз.	Эскиз	Поз.	Эскиз
X1	520, 245, 345, 420; по в.г. L=1530	Ск1	200, 420, 200; по н.г. L=820
Шп1	370, 100, 100; по в.г. L=570	Ск5	860, 370, 860; по н.г. L=2090

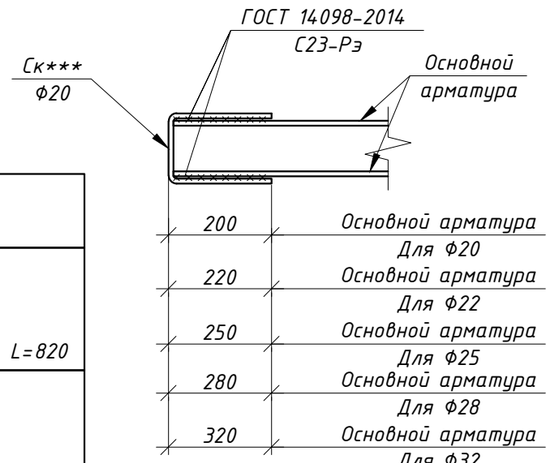


1. Общие указания см. л. - 1.
2. Данный лист читать совместно с л. КЖ-2.2 ... 2.7
3. Стержни, указанные в "Ведомости деталей", должны гнуться механическим способом в холодном состоянии с радиусом гиба 3d - 5d, где d - диаметр стержня


Изм.	Кол.уч.	Лист	N док.	Подп.	Дата	65П-АИП-2024-1-КЖ			
						Строительство многопрофильной больницы на 250 коек с онкологическим центром и поликлиникой на 350 посещений, по адресу: Медеуский район, г. Алматы			
						"Блок 1 Секция 1"	Стадия	Лист	Листов
							РП	6.16	
ГКП		Курал М				Ригель Рм-16	АстанаИнжПроект		
Проверил		Кыдырбай А							
Разраб.		Ауез Б							
Н.контроль		Ешенкулова							

Формат А3


Ригель Рм-17

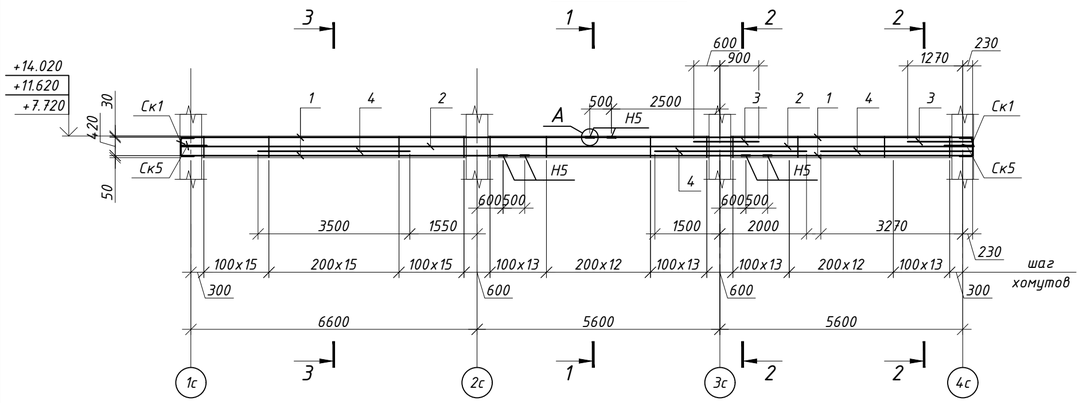


Разрез 1 - 1

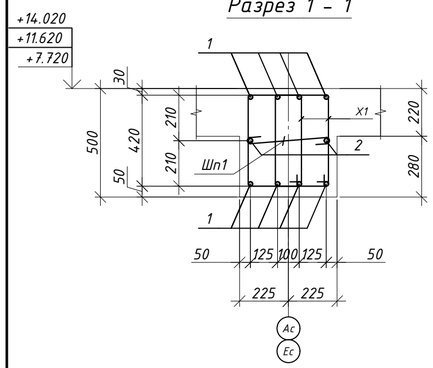

Разрез 2 - 2

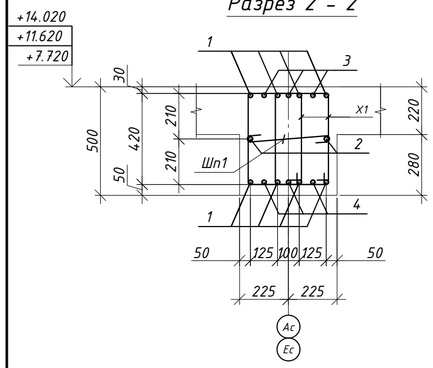

Разрез 3 - 3

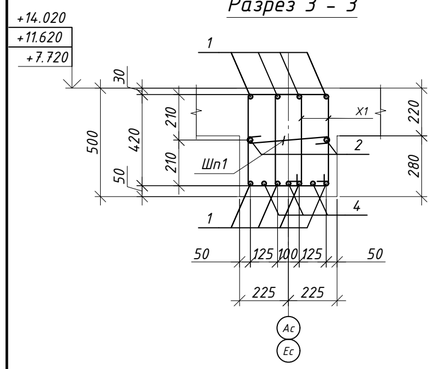

Ведомость деталей

Поз.	Эскиз
Х1	520, 245, 345, 420 — по в.г. — L=1530
Ск1	200, 420, 200 — по н.г. — L=820
Ск5	860, 370, 860 — по н.г. — L=2090
Шп1	370, 100, 100 — по в.г. — L=570

Таблица размеров накладок

Марка эл-та	dн	L	вес
	мм.		кг.
Н1	32	320	2.01
Н2	28	280	1.35
Н3	25	250	0.96
Н4	22	220	0.66
Н5	20	200	0.49


Спецификация элементов


Поз.	Обозначение	Наименование	Кол.	Масса ед.кг	Примечание
		Ригель Рм-17	6		694.66
Х1	ГОСТ 34028-2016(214-210-0101-0002)	Ф 8 А 240 L= 1530	248	0.60	149.72
Ск1	ГОСТ 34028-2016(214-210-0502-0005)	Ф 20 А500С L= 820	8	2.02	16.18
Ск5	ГОСТ 34028-2016(214-210-0502-0001)	Ф 12 А500С L= 2090	2	1.86	3.71
1	ГОСТ 34028-2016(214-210-0502-0005)	Ф 20 А500С L= пог.м.	154	2.47	379.79
Н5	ГОСТ 34028-2016(214-210-0502-0005)	Ф 20 А500С L= 200	24	0.49	11.84
2	ГОСТ 34028-2016(214-210-0502-0001)	Ф 12 А500С L= пог.м.	39	0.89	34.62
3	ГОСТ 34028-2016(214-210-0502-0001)	Ф 12 А500С L= 1500	6	1.33	7.99
4	ГОСТ 34028-2016(214-210-0502-0004)	Ф 18 А500С L= 3500	9	6.99	62.92
Шп1	ГОСТ 34028-2016(214-210-0101-0002)	Ф 8 А 240 L= 570	124	0.22	27.89
		Материалы:			
	(212-101-0901)	Класс бетона С 20/25 (В25), м³			2.05


Позиции со "*" см. "Ведомость деталей" см. на данном листе.

Ведомость расхода стали, кг

Марка элемента	Изделия арматурные							Всего
	Арматура класса							
	А240		А500С					
	ГОСТ 34028-2016(214-210-0101)		ГОСТ 34028-2016(214-210-0502)					
	Ф8	Итого	Ф12	Ф16	Ф18	Ф20	Итого	
Ригель Рм-17	177.61	177.61	46.33	0.00	62.92	407.80	517.05	694.66

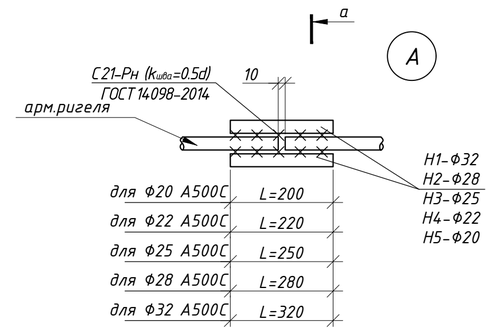

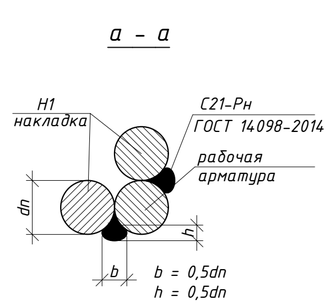

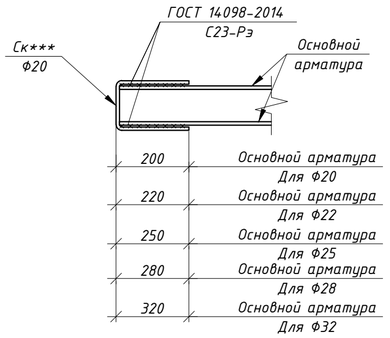


1. Общие указания см. л. - 1.
2. Данный лист читать совместно с л. КЖ-2.2 ... 2.7
3. Стержни, указанные в "Ведомости деталей", должны гнуться механическим способом в холодном состоянии с радиусом гиба 3d - 5d, где d - диаметр стержня


Изм.	Кол.уч.	Лист	N док.	Подп.	Дата	65П-АИП-2024-1-КЖ			
						Строительство многопрофильной больницы на 250 коек с онкологическим центром и поликлиникой на 350 посещений, по адресу: Медеуский район, г. Алматы			
ГКП		Курал М				"Блок 1 Секция 1"	Стадия	Лист	Листов
Проверил		Кыдырбай А					РП	6.17	
Разраб.		Ауез Б				Ригель Рм-17	АстанаИнжПроект		
Н.контроль		Ешенкулова							

Формат А2


Ригель Рм-18

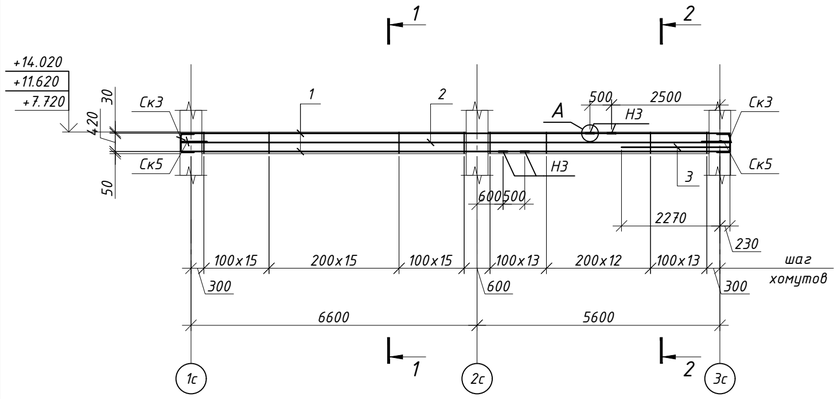

Разрез 1 - 1

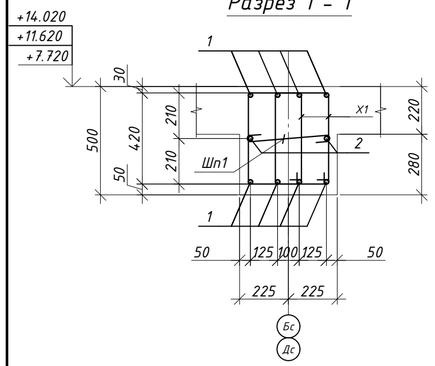

Разрез 2 - 2

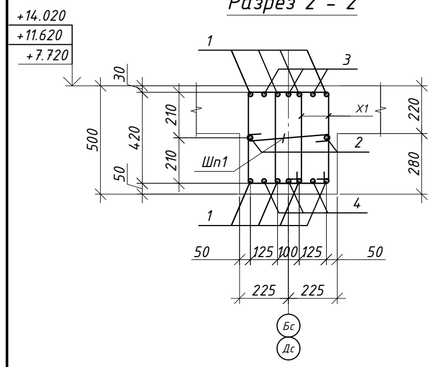

Спецификация элементов

Поз.	Обозначение	Наименование	Кол.	Масса ед.кг	Примечание
		Ригель Рм-18	6		662.02
Х1	ГОСТ 34028-2016(214-210-0101-0003)	Ф 10 А 240 L= 1530	170	0.94	160.36
Ск3	ГОСТ 34028-2016(214-210-0502-0005)	Ф 20 А500С L= 920	8	2.27	18.15
Ск5	ГОСТ 34028-2016(214-210-0502-0001)	Ф 12 А500С L= 2090	2	1.86	3.71
1	ГОСТ 34028-2016(214-210-0502-0007)	Ф 25 А500С L= пог.м.	107	3.85	412.31
НЗ	ГОСТ 34028-2016(214-210-0502-0007)	Ф 25 А500С L= 250	16	0.96	15.41
2	ГОСТ 34028-2016(214-210-0502-0001)	Ф 12 А500С L= пог.м.	27	0.89	23.97
3	ГОСТ 34028-2016(214-210-0502-0004)	Ф 18 А500С L= 1500	3	3.00	8.99
Шп1	ГОСТ 34028-2016(214-210-0101-0002)	Ф 8 А 240 L= 570	85	0.22	19.12
		Материалы:			
	(212-101-0901)	Класс бетона С 20/25 (В25), м^3			1.41

Позиции со "*" см. "Ведомость деталей" см. на данном листе.

Ведомость расхода стали, кг


Марка элемента	Изделия арматурные								Всего
	Арматура класса								
	А240			А500С					
	ГОСТ 34028-2016(214-210-0101)			ГОСТ 34028-2016(214-210-0502)					
	Ф8	Ф10	Итого	Ф12	Ф18	Ф20	Ф25	Итого	
Ригель Рм-18	19.12	160.36	179.48	27.68	8.99	18.15	427.72	482.54	662.02


Ведомость деталей


Поз.	Эскиз
Х1	520, 24.5, 34.5, 420; по в.г. L=1530
Ск3	250, 420, 250; по н.г. L=920
Ск5	860, 370, 860; по н.г. L=2090
Шп1	370, 100, 100; по в.г. L=570

Таблица размеров накладок

Марка эл-та	dн	L	вес
	мм.		кг.
Н1	32	320	2.01
Н2	28	280	1.35
Н3	25	250	0.96
Н4	22	220	0.66
Н5	20	200	0.49

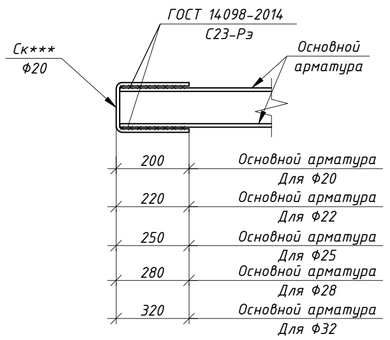

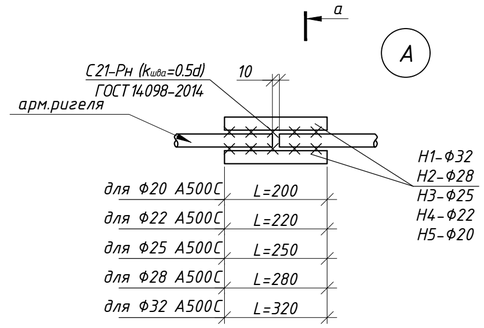

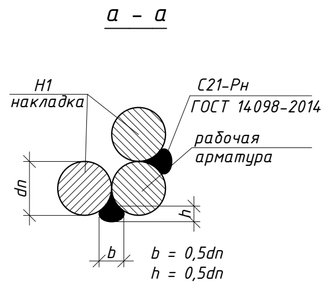


1. Общие указания см. л. - 1.
2. Данный лист читать совместно с л. КЖ-2.2 ... 2.7
3. Стержни, указанные в "Ведомости деталей", должны гнуться механическим способом в холодном состоянии с радиусом гиба 3d - 5d, где d - диаметр стержня


Изм.	Кол.уч.	Лист	N док.	Подп.	Дата	65П-АИП-2024-1-КЖ			
						Строительство многопрофильной больницы на 250 коек с онкологическим центром и поликлиникой на 350 посещений, по адресу: Медеуский район, г. Алматы			
ГКП		Курал М				"Блок 1 Секция 1"	Стадия	Лист	Листов
Проверил		Кыдырбай А					РП	6.18	
Разраб.		Ауез Б				Ригель Рм-18	АстанаИнжПроект		
Н.контроль		Ешенкулова							

Формат А2


Ригель Рм-19

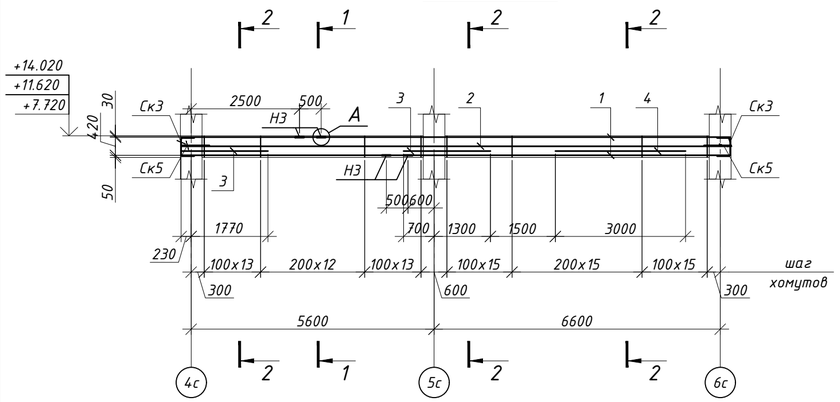

Разрез 1 - 1

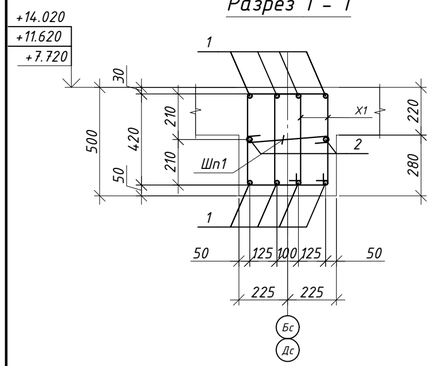

Разрез 2 - 2

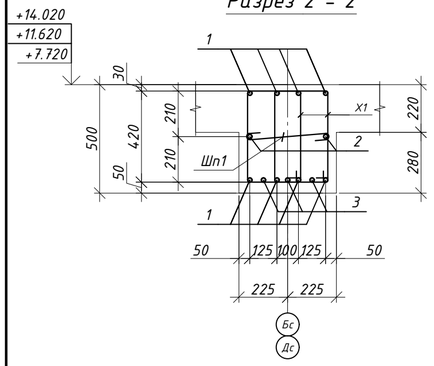

Спецификация элементов

Поз.	Обозначение	Наименование	Кол.	Масса ед.кг	Примечание
		Ригель Рм-19	6		678.41
Х1	ГОСТ 34028-2016(214-210-0101-0003)	Ф 10 А 240 L= 1530	170	0.94	160.36
Ск3	ГОСТ 34028-2016(214-210-0502-0005)	Ф 20 А500С L= 920	8	2.27	18.15
Ск5	ГОСТ 34028-2016(214-210-0502-0001)	Ф 12 А500С L= 2090	2	1.86	3.71
1	ГОСТ 34028-2016(214-210-0502-0007)	Ф 25 А500С L= пог.м.	107	3.85	412.31
Н3	ГОСТ 34028-2016(214-210-0502-0007)	Ф 25 А500С L= 250	16	0.96	15.41
2	ГОСТ 34028-2016(214-210-0502-0001)	Ф 12 А500С L= пог.м.	27	0.89	23.97
3	ГОСТ 34028-2016(214-210-0502-0002)	Ф 14 А500С L= 2000	6	2.42	14.50
4	ГОСТ 34028-2016(214-210-0502-0002)	Ф 14 А500С L= 3000	3	3.63	10.88
Шп1	ГОСТ 34028-2016(214-210-0101-0002)	Ф 8 А 240 L= 570	85	0.22	19.12
		Материалы:			
	(212-101-0901)	Класс бетона С 20/25 (В25), м^3			1.41

Позиции со "*" см. "Ведомость деталей" см. на данном листе.

Ведомость расхода стали, кг


Марка элемента	Изделия арматурные								Всего
	Арматура класса								
	А240			А500С					
	ГОСТ 34028-2016(214-210-0101)			ГОСТ 34028-2016(214-210-0502)					
	Ф8	Ф10	Итого	Ф12	Ф14	Ф20	Ф25	Итого	
Ригель Рм-19	19.12	160.36	179.48	27.68	25.38	18.15	427.72	498.93	678.41


Ведомость деталей


Поз.	Эскиз
Х1	520, 245, 345, 420, по в.г., L=1530
Ск3	250, 420, 250, по н.г., L=920
Ск5	860, 370, 860, по н.г., L=2090
Шп1	370, 100, 100, по в.г., L=570

Таблица размеров накладок

Марка эл-та	dн	L	вес
	мм.		кг.
Н1	32	320	2.01
Н2	28	280	1.35
Н3	25	250	0.96
Н4	22	220	0.66
Н5	20	200	0.49

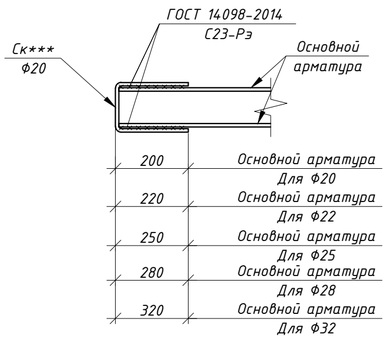

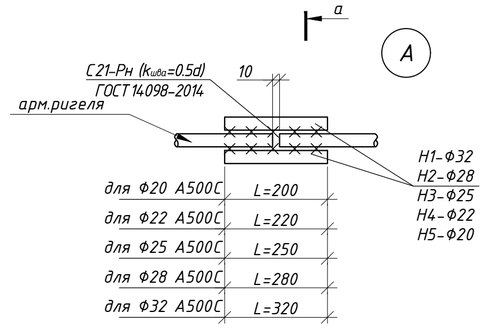

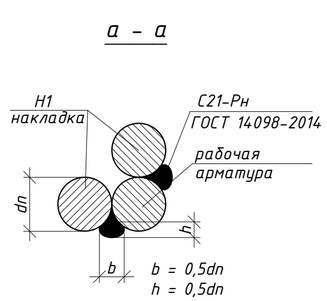


1. Общие указания см. л. - 1.
2. Данный лист читать совместно с л. КЖ-2.2 ... 2.7
3. Стержни, указанные в "Ведомости деталей", должны гнуться механическим способом в холодном состоянии с радиусом гиба 3d - 5d, где d - диаметр стержня


							65П-АИП-2024-1-КЖ
							Строительство многопрофильной больницы на 250 коек с онкологическим центром и поликлиникой на 350 посещений, по адресу: Медеуский район, г. Алматы
Изм.	Кол.уч.	Лист	N док.	Подп.	Дата		
						"Блок 1 Секция 1"	Стадия: РП; Лист: 6.19; Листов:
ГКП		Курал М					
Проверил		Кыдырбай А				Ригель Рм-19	АстанаИнжПроект
Разраб.		Ауез Б					
Н.контроль		Ешенкулова					

Формат А2


Ригель Рм-20

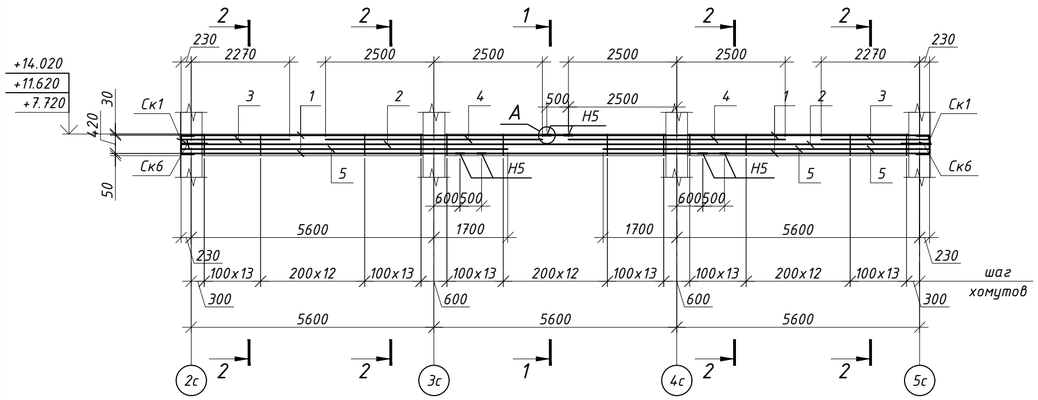

Разрез 1 - 1

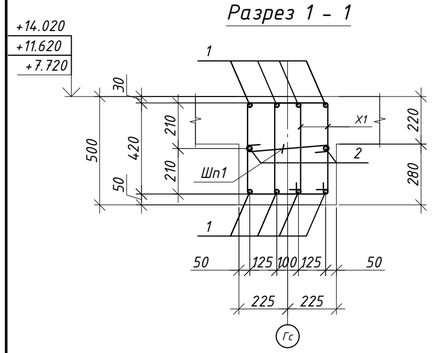

Разрез 2 - 2

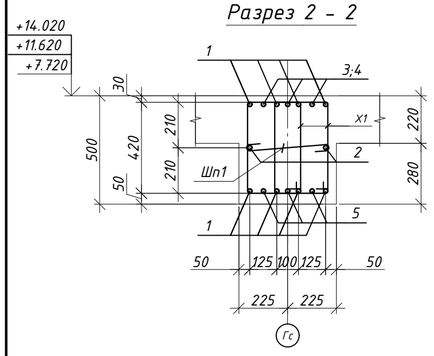

Спецификация элементов

Поз.	Обозначение	Наименование	Кол.	Масса ед.кг	Примечание
		Ригель Рм-20	3		968.17
Х1	ГОСТ 34028-2016(214-210-0101-0003)	ф 10 А 240 L= 1530	234	0.94	220.73
Ск1	ГОСТ 34028-2016(214-210-0502-0005)	ф 20 А500С L= 820	8	2.02	16.18
Ск6	ГОСТ 34028-2016(214-210-0502-0002)	ф 14 А500С L= 2370	2	2.86	5.73
1	ГОСТ 34028-2016(214-210-0502-0005)	ф 20 А500С L= пог.м.	145	2.47	357.59
Н5	ГОСТ 34028-2016(214-210-0502-0005)	ф 20 А500С L= 200	24	0.49	11.84
2	ГОСТ 34028-2016(214-210-0502-0002)	ф 14 А500С L= пог.м.	37	1.21	44.71
3	ГОСТ 34028-2016(214-210-0502-0005)	ф 20 А500С L= 2500	6	6.17	36.99
4	ГОСТ 34028-2016(214-210-0502-0005)	ф 20 А500С L= 5000	6	12.33	73.98
5	ГОСТ 34028-2016(214-210-0502-0007)	ф 25 А500С L= 7530	6	29.02	174.09
Шп1	ГОСТ 34028-2016(214-210-0101-0002)	ф 8 А 240 L= 570	117	0.22	26.31
		Материалы:			
	(212-101-0901)	Класс бетона С 20/25 (В25), м³			1.93

Позиции со "*" см. "Ведомость деталей" см. на данном листе.

Ведомость расхода стали, кг


Марка элемента	Изделия арматурные								Всего
	Арматура класса								
	А240			А500С					
	ГОСТ 34028-2016(214-210-0101)			ГОСТ 34028-2016(214-210-0502)					
	ф8	ф10	Итого	ф14	ф16	ф20	ф25	Итого	
Ригель Рм-20	26.31	220.73	247.05	50.44	0.00	496.58	174.09	721.12	968.17


Ведомость деталей


Поз.	Эскиз
Х1	520; 245; 345; 420; по в.г. L=1530
Ск1	200; 420; 200; по н.г. L=820
Ск6	1000; 370; 1000; по н.г. L=2370
Шп1	370; 100; 100; по в.г. L=570

Таблица размеров накладок

Марка эл-та	dн	L	вес
	мм.		кг.
Н1	32	320	2.01
Н2	28	280	1.35
Н3	25	250	0.96
Н4	22	220	0.66
Н5	20	200	0.49

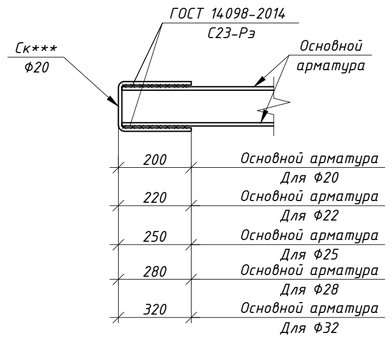

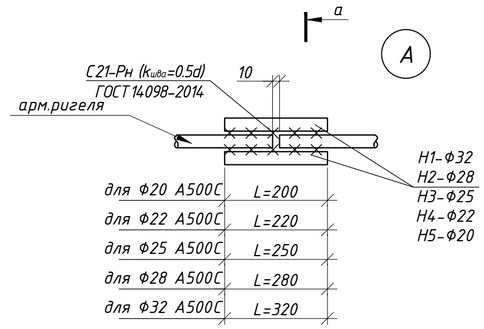

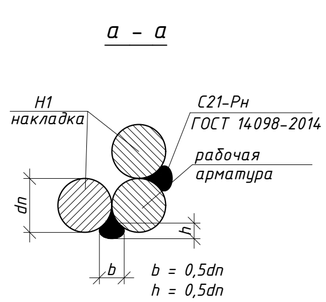


1. Общие указания см. л. - 1.
2. Данный лист читать совместно с л. КЖ-2.2 ... 2.7
3. Стержни, указанные в "Ведомости деталей", должны гнуться механическим способом в холодном состоянии с радиусом гиба 3d - 5d, где d - диаметр стержня


Изм.	Кол.уч.	Лист	N док.	Подп.	Дата	65П-АИП-2024-1-КЖ			
						Строительство многопрофильной больницы на 250 коек с онкологическим центром и поликлиникой на 350 посещений, по адресу: Медеуский район, г. Алматы			
ГКП		Курал М				"Блок 1 Секция 1"	Стадия	Лист	Листов
Проверил		Кыдырбай А					РП	6.20	
Разраб.		Ауез Б				Ригель Рм-20	АстанаИнжПроект		
Н.контроль		Ешенкулова							

Формат А2


Ригель Рм-21

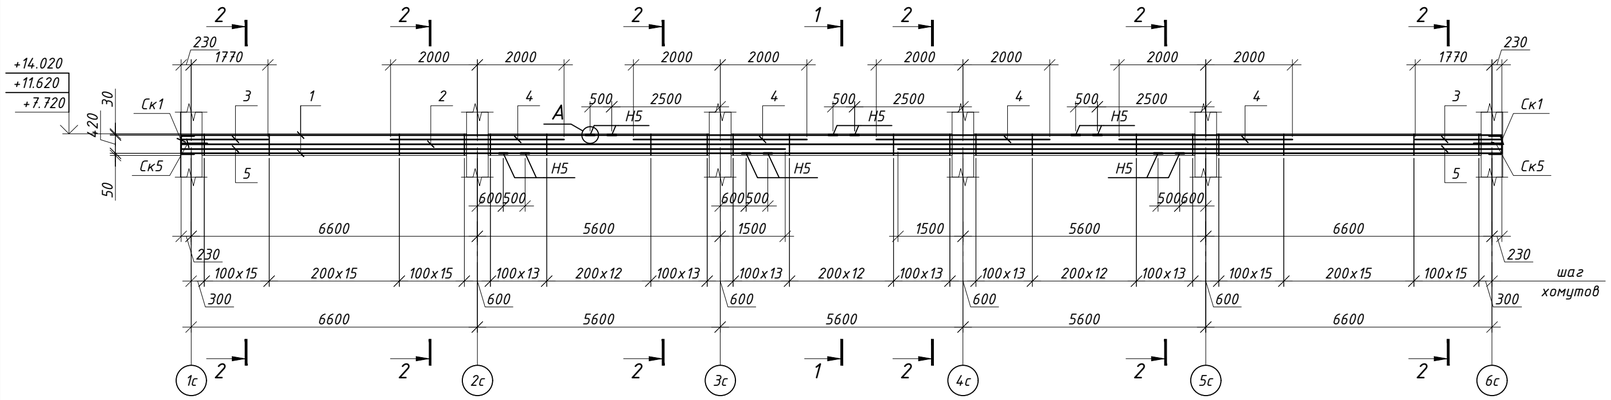

Разрез 1 - 1

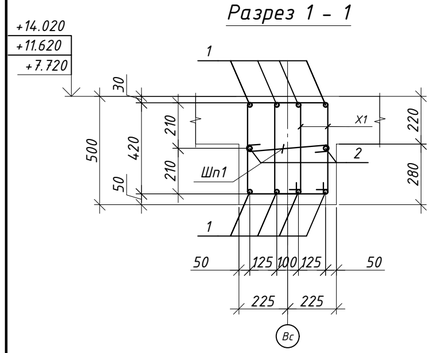

Разрез 2 - 2

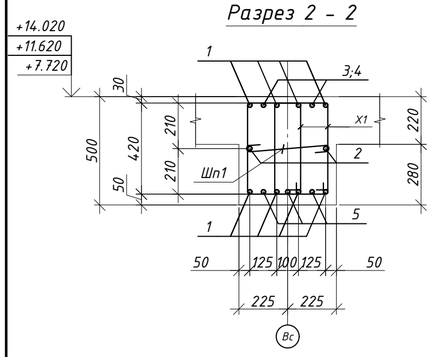

Спецификация элементов

Поз.	Обозначение	Наименование	Кол.	Масса ед.кг	Примечание
		Ригель Рм-21	3		1347.43
Х1	ГОСТ 34028-2016(214-210-0101-0003)	ф 10 А 240 L= 1530	418	0.94	394.30
Ск1	ГОСТ 34028-2016(214-210-0502-0005)	ф 20 А500С L= 820	8	2.02	16.18
Ск5	ГОСТ 34028-2016(214-210-0502-0001)	ф 12 А500С L= 2090	2	1.86	3.71
1	ГОСТ 34028-2016(214-210-0502-0005)	ф 20 А500С L= пог.м.	256	2.47	631.33
Н5	ГОСТ 34028-2016(214-210-0502-0005)	ф 20 А500С L= 200	48	0.49	23.68
2	ГОСТ 34028-2016(214-210-0502-0001)	ф 12 А500С L= пог.м.	64	0.89	56.82
3	ГОСТ 34028-2016(214-210-0502-0001)	ф 12 А500С L= 2000	4	1.78	7.10
4	ГОСТ 34028-2016(214-210-0502-0001)	ф 12 А500С L= 4000	8	3.55	28.41
5	ГОСТ 34028-2016(214-210-0502-0003)	ф 16 А500С L= пог.м.	88	1.58	138.89
Шп1	ГОСТ 34028-2016(214-210-0101-0002)	ф 8 А 240 L= 570	209	0.22	47.01
		Материалы:			
	(212-101-0901)	Класс бетона С 20/25 (В25), м³			3.47

Позиции со "*" см. "Ведомость деталей" см. на данном листе.

Ведомость расхода стали, кг


Марка элемента	Изделия арматурные								Всего
	Арматура класса								
	А240			А500С					
	ГОСТ 34028-2016(214-210-0101)			ГОСТ 34028-2016(214-210-0502)					
	ф8	ф10	Итого	ф12	ф14	ф16	ф20	Итого	
Ригель Рм-21	47.01	394.30	441.31	96.04	0.00	138.89	671.19	906.12	1347.43


Ведомость деталей


Поз.	Эскиз
Х1	520, 245, 345, 420; по в.г. L=1530
Ск1	200, 420, 200; по н.г. L=820
Ск5	860, 370, 860; по н.г. L=2090
Шп1	370, 100, 100; по в.г. L=570

Таблица размеров накладок

Марка эл-та	dн	L	вес
	мм.		кг.
Н1	32	320	2.01
Н2	28	280	1.35
Н3	25	250	0.96
Н4	22	220	0.66
Н5	20	200	0.49

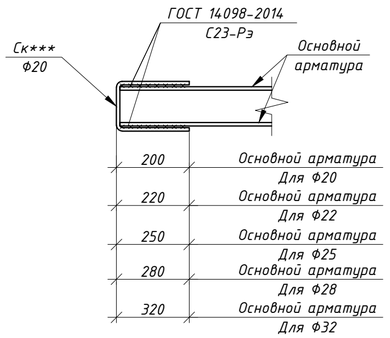

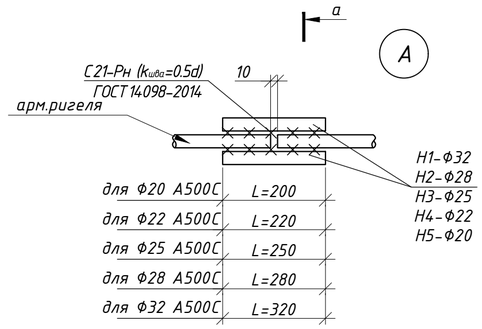

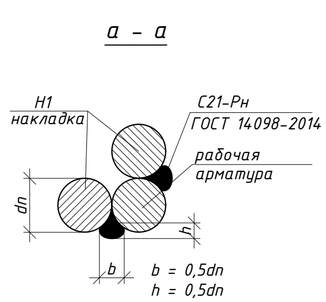


1. Общие указания см. л. - 1.
2. Данный лист читать совместно с л. КЖ-2.2 ... 2.7
3. Стержни, указанные в "Ведомости деталей", должны гнуться механическим способом в холодном состоянии с радиусом гиба 3d - 5d, где d - диаметр стержня


Изм.	Кол.уч.	Лист	N док.	Подп.	Дата	65П-АИП-2024-1-КЖ			
						Строительство многопрофильной больницы на 250 коек с онкологическим центром и поликлиникой на 350 посещений, по адресу: Медеуский район, г. Алматы			
ГКП		Курал М				"Блок 1 Секция 1"	Стадия	Лист	Листов
Проверил		Кыдырбай А					РП	6.21	
Разраб.		Ауез Б				Ригель Рм-21	АстанаИнжПроект		
Н.контроль		Ешенкулова							

Формат А2

Ригель Рм-22

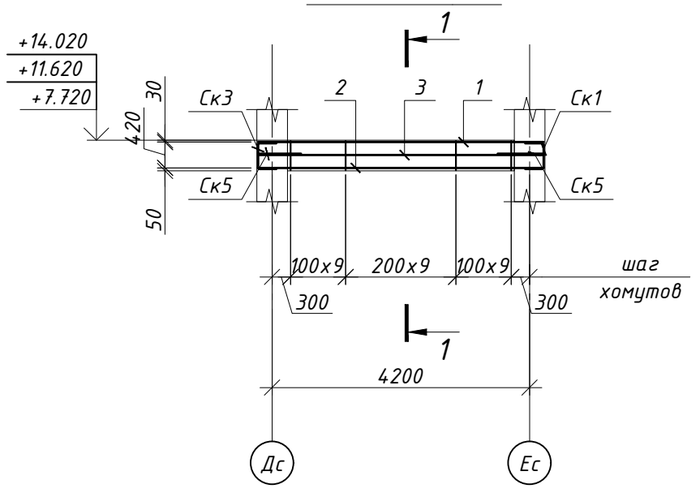

Разрез 1 - 1

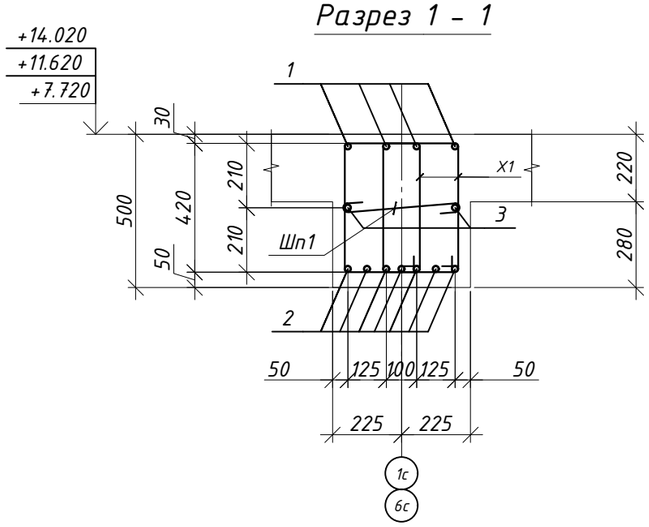

Спецификация элементов

Поз.	Обозначение	Наименование	Кол.	Масса ед.кг	Примечание
		Ригель Рм-22	6		239.41
X1	ГОСТ 34028-2016(214-210-0101-0002)	ф 8 А 240 L= 1530	56	0.60	33.81
Ск3	ГОСТ 34028-2016(214-210-0502-0005)	ф 20 А500С L= 920	8	2.27	18.15
Ск5	ГОСТ 34028-2016(214-210-0502-0001)	ф 12 А500С L= 2090	2	1.86	3.71
1	ГОСТ 34028-2016(214-210-0502-0007)	ф 25 А500С L= 4660	4	17.96	71.83
2	ГОСТ 34028-2016(214-210-0502-0006)	ф 22 А500С L= 4660	7	13.91	97.34
3	ГОСТ 34028-2016(214-210-0502-0001)	ф 12 А500С L= 4660	2	4.14	8.27
Шп1	ГОСТ 34028-2016(214-210-0101-0002)	ф 8 А 240 L= 570	28	0.22	6.30
		Материалы:			
	(212-101-0901)	Класс бетона С 20/25 (В25), м³			0.47


Позиции со "*" см. "Ведомость деталей" см. на данном листе.

Ведомость расхода стали, кг

Марка элемента	Изделия арматурные							Всего
	Арматура класса							
	А240		А500С					
	ГОСТ 34028-2016(214-210-0101)		ГОСТ 34028-2016(214-210-0502)					
	ф8	Итого	ф12	ф20	ф22	ф25	Итого	
Ригель Рм-22	40.11	40.11	11.99	18.15	97.34	71.83	199.30	239.41

Ведомость деталей

Поз.	Эскиз	Поз.	Эскиз
X1	520, 245, 345, 420; по в.г. L=1530	Ск3	250, 420, 250; по н.г. L=920
Шп1	370, 100, 100; по в.г. L=570	Ск5	860, 370, 860; по н.г. L=2090

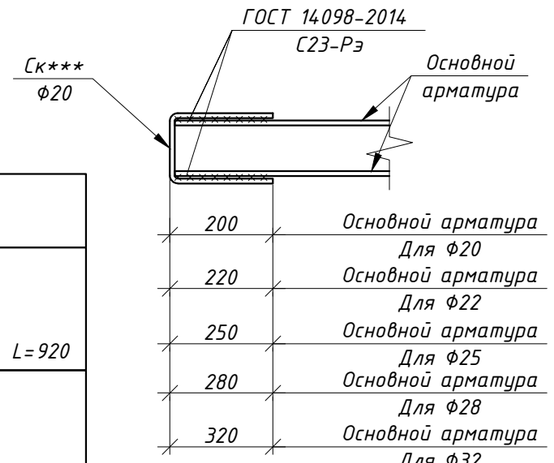


1. Общие указания см. л. - 1.
2. Данный лист читать совместно с л. КЖ-2.2 ... 2.7
3. Стержни, указанные в "Ведомости деталей", должны гнуться механическим способом в холодном состоянии с радиусом гиба 3d - 5d, где d - диаметр стержня


Изм.	Кол.уч.	Лист	N док.	Подп.	Дата	65П-АИП-2024-1-КЖ			
						Строительство многопрофильной больницы на 250 коек с онкологическим центром и поликлиникой на 350 посещений, по адресу: Медеуский район, г. Алматы			
						"Блок 1 Секция 1"	Стадия	Лист	Листов
							РП	6.22	
ГКП		Курал М				Ригель Рм-22	АстанаИнжПроект		
Проверил		Кыдырбай А							
Разраб.		Ауез Б							
Н.контроль		Ешенкулова							

Формат А3

Ригель Рм-23

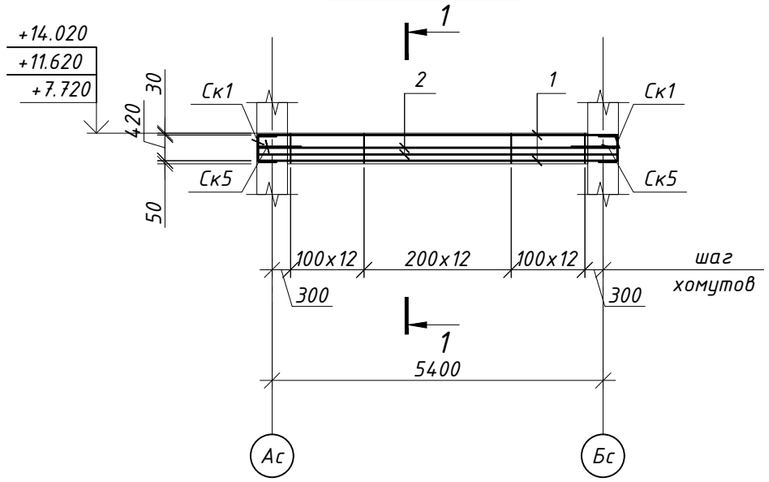

Разрез 1 - 1

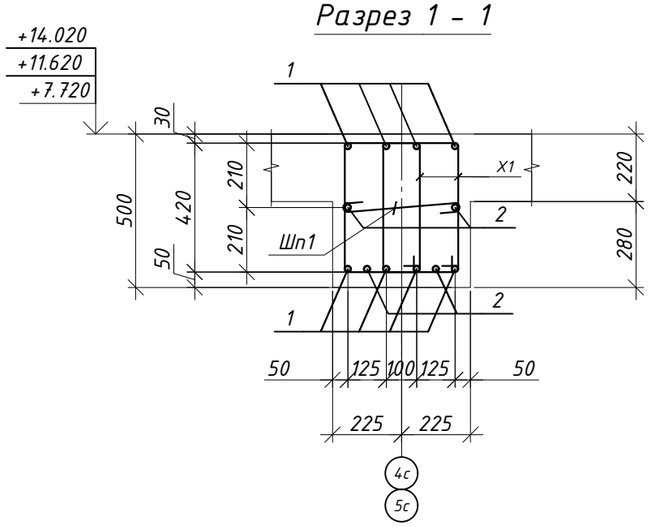

Спецификация элементов

Поз.	Обозначение	Наименование	Кол.	Масса ед.кг	Примечание
		Ригель Рм-23	6		209.31
X1	ГОСТ 34028-2016(214-210-0101-0002)	ф 8 A 240 L= 1530	74	0.60	44.67
Ск1	ГОСТ 34028-2016(214-210-0502-0005)	ф 20 A500C L= 820	8	2.02	16.18
Ск5	ГОСТ 34028-2016(214-210-0502-0001)	ф 12 A500C L= 2090	2	1.86	3.71
1	ГОСТ 34028-2016(214-210-0502-0005)	ф 20 A500C L= 5860	8	14.45	115.61
2	ГОСТ 34028-2016(214-210-0502-0001)	ф 12 A500C L= 5860	4	5.20	20.81
Шп1	ГОСТ 34028-2016(214-210-0101-0002)	ф 8 A 240 L= 570	37	0.22	8.32
		Материалы:			
	(212-101-0901)	Класс бетона С 20/25 (В25), м³			0.62


Позиции со "*" см. "Ведомость деталей" см. на данном листе.

Ведомость расхода стали, кг

Марка элемента	Изделия арматурные						Всего
	Арматура класса						
	A240		A500C				
	ГОСТ 34028-2016(214-210-0101)		ГОСТ 34028-2016(214-210-0502)				
	ф8	Итого	ф12	ф20	ф25	Итого	
Ригель Рм-23	53.00	53.00	24.52	131.79	0.00	156.31	209.31

Ведомость деталей

Поз.	Эскиз	Поз.	Эскиз
X1	520, 245, 345, 420; по в.г. L=1530	Ск1	200, 420, 200; по н.г. L=820
Шп1	370, 100, 100; по в.г. L=570	Ск5	860, 370, 860; по н.г. L=2090

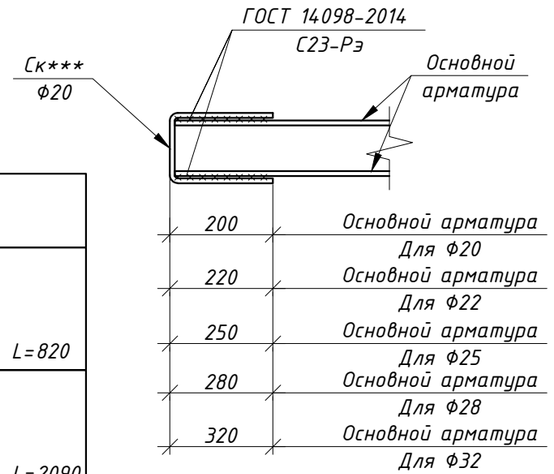


1. Общие указания см. л. - 1.
2. Данный лист читать совместно с л. КЖ-2.2 ... 2.7
3. Стержни, указанные в "Ведомости деталей", должны гнуться механическим способом в холодном состоянии с радиусом гиба 3d - 5d, где d - диаметр стержня


Изм.	Кол.уч.	Лист	N док.	Подп.	Дата	65П-АИП-2024-1-КЖ		
						Строительство многопрофильной больницы на 250 коек с онкологическим центром и поликлиникой на 350 посещений, по адресу: Медеуский район, г. Алматы		
						"Блок 1 Секция 1"	Стадия: РП	Лист: 6.23
ГКП		Курал М						
Проверил		Кыдырбай А				Ригель Рм-23	АстанаИнжПроект	
Разраб.		Ауез Б						
Н.контроль		Ешенкулова						

Формат А3


Ригель Рм-24

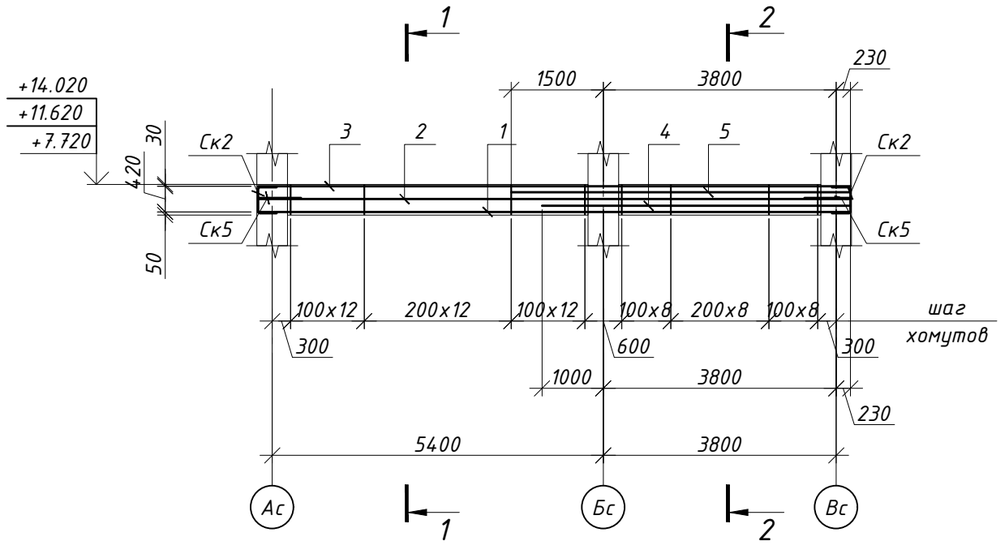

Разрез 1 - 1

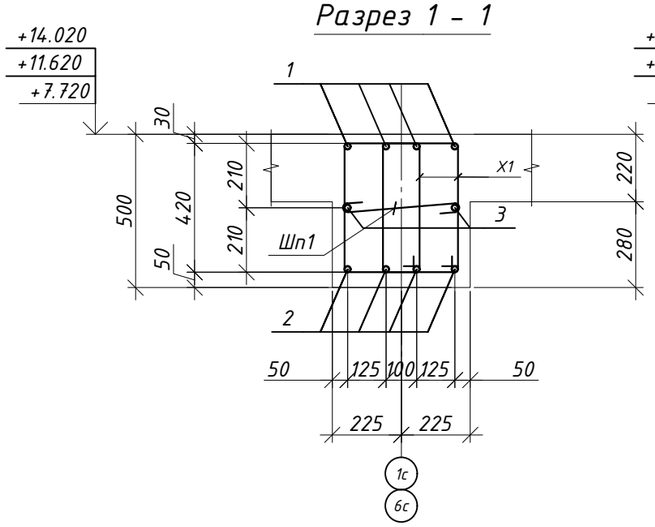

Разрез 2 - 2

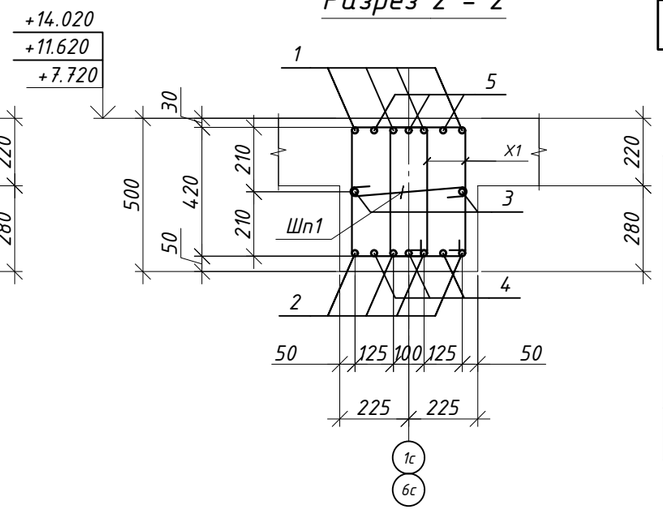

Спецификация элементов

Поз.	Обозначение	Наименование	Кол.	Масса ед.кг	Примечание
		Ригель Рм-24	6		442.74
Х1	ГОСТ 34028-2016(214-210-0101-0003)	ф 10 А 240 L= 1530	124	0.94	116.97
Ск2	ГОСТ 34028-2016(214-210-0502-0005)	ф 20 А500С L= 860	8	2.12	16.97
Ск5	ГОСТ 34028-2016(214-210-0502-0001)	ф 12 А500С L= 2090	2	1.86	3.71
1	ГОСТ 34028-2016(214-210-0502-0006)	ф 22 А500С L= 9660	4	28.83	115.30
2	ГОСТ 34028-2016(214-210-0502-0001)	ф 12 А500С L= 9660	2	8.58	17.15
3	ГОСТ 34028-2016(214-210-0502-0005)	ф 20 А500С L= 9660	4	23.82	95.29
4	ГОСТ 34028-2016(214-210-0502-0005)	ф 20 А500С L= 5030	3	12.40	37.21
5	ГОСТ 34028-2016(214-210-0502-0003)	ф 16 А500С L= 5530	3	8.73	26.18
Шп1	ГОСТ 34028-2016(214-210-0101-0002)	ф 8 А 240 L= 570	62	0.22	13.94
		Материалы:			
	(212-101-0901)	Класс бетона С 20/25 (В25), м³			1.03


Позиции со "*" см. "Ведомость деталей" см. на данном листе.

Ведомость расхода стали, кг

Марка элемента	Изделия арматурные								Всего
	Арматура класса								
	А240			А500С					
	ГОСТ 34028-2016(214-210-0101)			ГОСТ 34028-2016(214-210-0502)					
	ф8	ф10	Итого	ф12	ф16	ф20	ф22	Итого	
Ригель Рм-24	13.94	116.97	130.91	20.86	26.18	149.47	115.30	311.82	442.74

Ведомость деталей

Поз.	Эскиз	Поз.	Эскиз
Х1	520, 245, 345, 420; по в.г. L=1530	Ск2	220, 420, 220; по н.г. L=860
Шп1	370, 100, 100; по в.г. L=570	Ск5	860, 370, 860; по н.г. L=2090

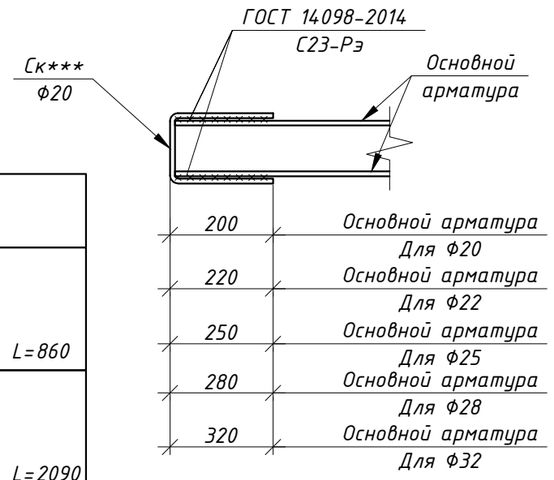


1. Общие указания см. л. - 1.
2. Данный лист читать совместно с л. КЖ-2.2 ... 2.7
3. Стержни, указанные в "Ведомости деталей", должны гнуться механическим способом в холодном состоянии с радиусом гиба 3d - 5d, где d - диаметр стержня


Изм.	Кол.уч	Лист	N док.	Подп.	Дата	65П-АИП-2024-1-КЖ			
						Строительство многопрофильной больницы на 250 коек с онкологическим центром и поликлиникой на 350 посещений, по адресу: Медеуский район, г. Алматы			
						"Блок 1 Секция 1"	Стадия	Лист	Листов
							РП	6.24	
ГКП		Курал М				Ригель Рм-24	АстанаИнжПроект		
Проверил		Кыдырбай А							
Разраб.		Ауез Б							
Н.контроль		Ешенкулова							

Формат А3


Ригель Рм-25

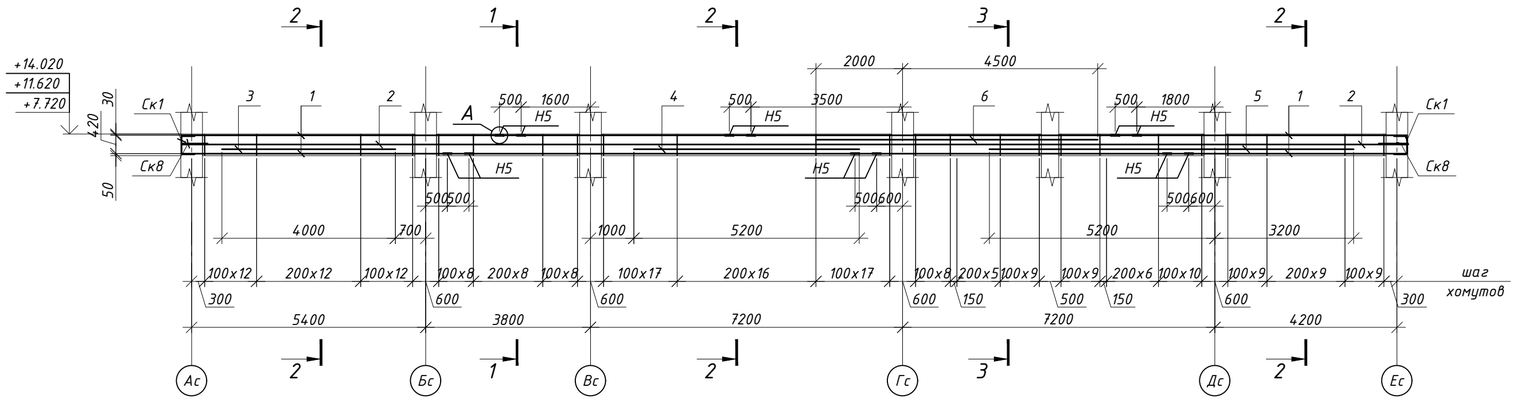


Разрез 1 - 1

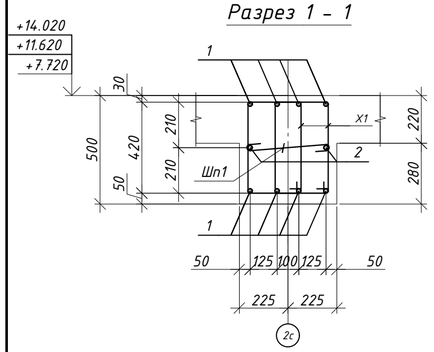

Разрез 2 - 2

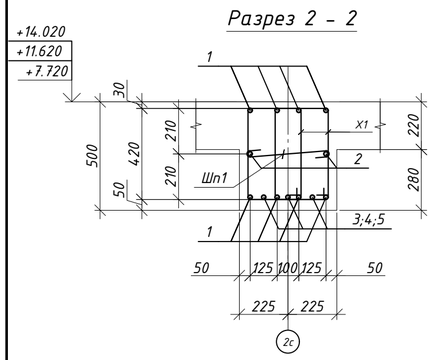

Разрез 3 - 3

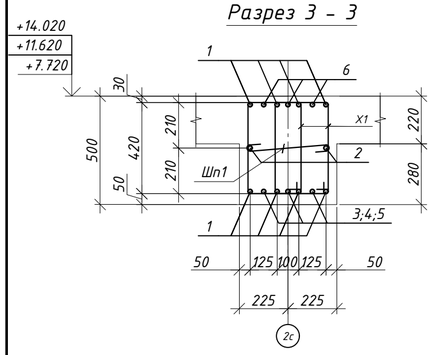

Спецификация элементов

Поз.	Обозначение	Наименование	Кол.	Масса ед.кг	Примечание
		Ригель Рм-25	3		1341.84
Х1	ГОСТ 34028-2016(214-210-0101-0003)	ф 10 А 240 L= 1530	384	0.94	362.23
Ск1	ГОСТ 34028-2016(214-210-0502-0005)	ф 20 А500С L= 820	8	2.02	16.18
Ск8	ГОСТ 34028-2016(214-210-0502-0004)	ф 18 А500С L= 2930	2	5.85	11.71
1	ГОСТ 34028-2016(214-210-0502-0005)	ф 20 А500С L= пог.м.	238	2.47	586.94
Н5	ГОСТ 34028-2016(214-210-0502-0005)	ф 20 А500С L= 200	48	0.49	23.68
2	ГОСТ 34028-2016(214-210-0502-0004)	ф 18 А500С L= пог.м.	60	2.00	119.85
3	ГОСТ 34028-2016(214-210-0502-0005)	ф 20 А500С L= 4000	3	9.86	29.59
4	ГОСТ 34028-2016(214-210-0502-0005)	ф 20 А500С L= 5200	3	12.82	38.47
5	ГОСТ 34028-2016(214-210-0502-0005)	ф 20 А500С L= 8400	3	20.72	62.15
6	ГОСТ 34028-2016(214-210-0502-0002)	ф 14 А500С L= 6500	3	7.85	23.56
Шп1	ГОСТ 34028-2016(214-210-0101-0003)	ф 10 А 240 L= 570	192	0.35	67.47
		Материалы:			
	(212-101-0901)	Класс бетона С 20/25 (В25), м³			3.14

Позиции со "*" см. "Ведомость деталей" см. на данном листе.

Ведомость расхода стали, кг


Марка элемента	Изделия арматурные							Всего
	Арматура класса							
	А240		А500С					
	ГОСТ 34028-2016(214-210-0101)		ГОСТ 34028-2016(214-210-0502)					
	ф10	Итого	ф12	ф14	ф18	ф20	Итого	
Ригель Рм-25	429.70	429.70	0.00	23.56	131.56	757.01	912.13	1341.84


Ведомость деталей


Поз.	Эскиз
Х1	520, 245, 34.5, 420; по в.г. L=1530
Ск1	200, 420, 200; по н.г. L=820
Ск8	1280, 370, 1280; по н.г. L=2930
Шп1	370, 100, 100; по в.г. L=570

Таблица размеров накладок

Марка эл-та	dн	L	вес
	мм.		кг.
Н1	32	320	2.01
Н2	28	280	1.35
Н3	25	250	0.96
Н4	22	220	0.66
Н5	20	200	0.49

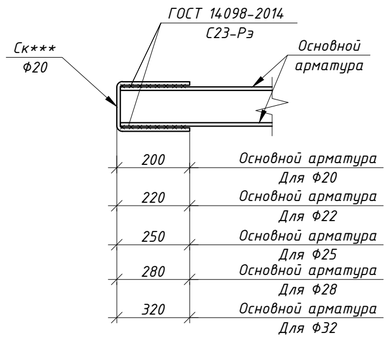

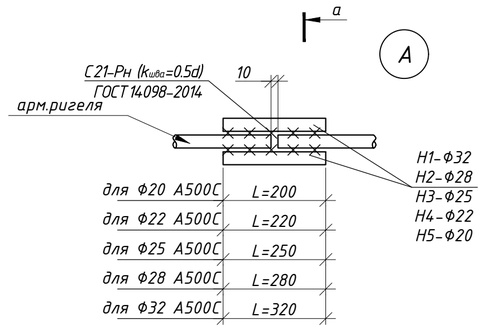

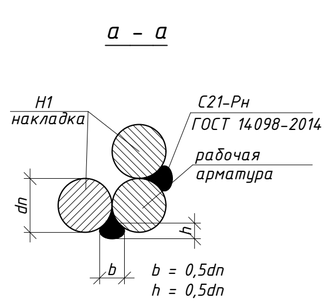


1. Общие указания см. л. - 1.
2. Данный лист читать совместно с л. КЖ-2.2 ... 2.7
3. Стержни, указанные в "Ведомости деталей", должны гнуться механическим способом в холодном состоянии с радиусом гиба 3d - 5d, где d - диаметр стержня


Изм.	Кол.уч	Лист	N док.	Подп.	Дата	65П-АИП-2024-1-КЖ			
						Строительство многопрофильной больницы на 250 коек с онкологическим центром и поликлиникой на 350 посещений, по адресу: Медеуский район, г. Алматы			
ГКП		Курал М				"Блок 1 Секция 1"	Стадия	Лист	Листов
Проверил		Кыдырбай А					РП	6.25	
Разраб.		Ауез Б				Ригель Рм-25	АстанаИнжПроект		
Н.контроль		Ешенкулова							

Формат А2


Ригель Рм-26

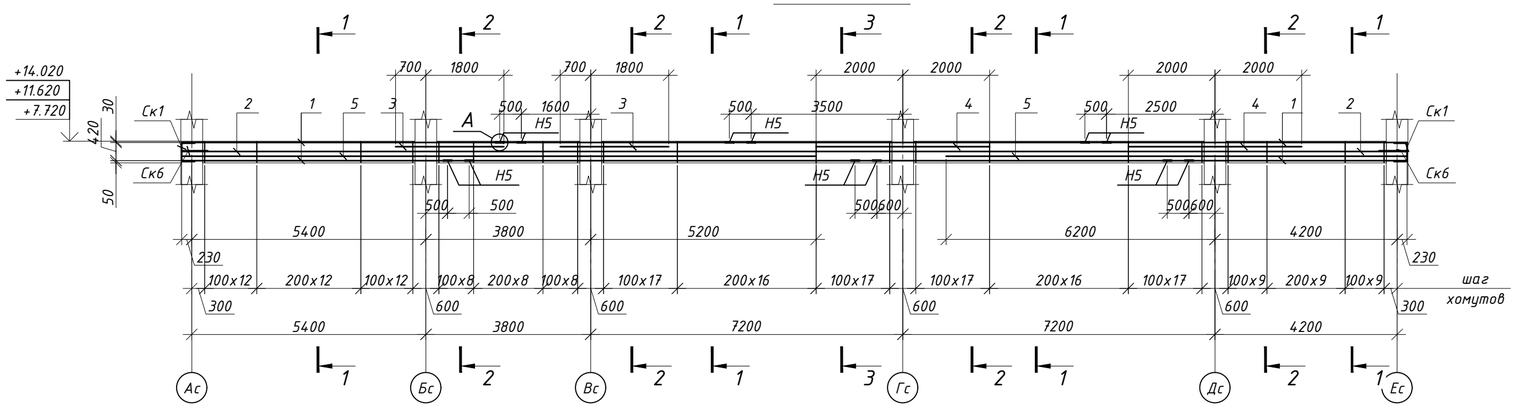


Разрез 1 - 1

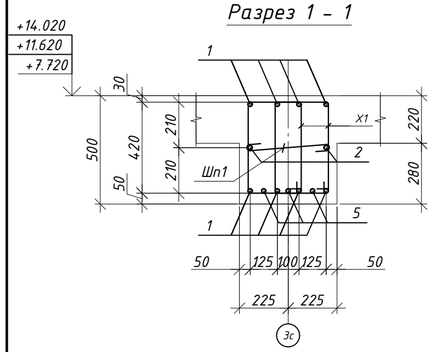

Разрез 2 - 2

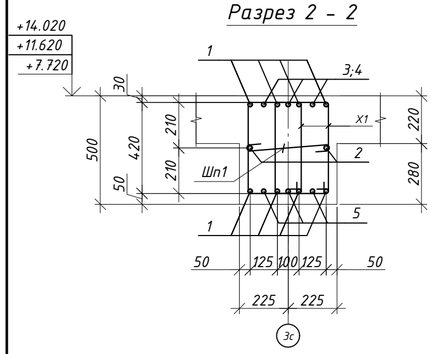

Разрез 3 - 3

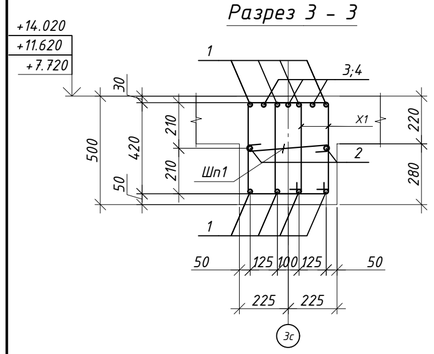

Спецификация элементов

Поз.	Обозначение	Наименование	Кол.	Масса ед.кг	Примечание
		Ригель Рм-26	3		1264.00
Х1	ГОСТ 34028-2016(214-210-0101-0003)	ф 10 А 240 L= 1530	388	0.94	366.00
Ск1	ГОСТ 34028-2016(214-210-0502-0005)	ф 20 А500С L= 820	8	2.02	16.18
Ск6	ГОСТ 34028-2016(214-210-0502-0002)	ф 14 А500С L= 2370	2	2.86	5.73
1	ГОСТ 34028-2016(214-210-0502-0005)	ф 20 А500С L= пог.м.	238	2.47	586.94
Н5	ГОСТ 34028-2016(214-210-0502-0005)	ф 20 А500С L= 200	48	0.49	23.68
2	ГОСТ 34028-2016(214-210-0502-0002)	ф 14 А500С L= пог.м.	60	1.21	72.50
3	ГОСТ 34028-2016(214-210-0502-0002)	ф 14 А500С L= 4000	6	4.83	29.00
4	ГОСТ 34028-2016(214-210-0502-0002)	ф 14 А500С L= 5200	6	6.28	37.70
5	ГОСТ 34028-2016(214-210-0502-0003)	ф 16 А500С L= пог.м.	80	1.58	126.27
Шп1	ГОСТ 34028-2016(214-210-0101-0002)	ф 8 А 240 L= 570	124	0.22	27.89
		Материалы:			
	(212-101-0901)	Класс бетона С 20/25 (В25), м³			3.19

Позиции со "*" см. "Ведомость деталей" см. на данном листе.

Ведомость расхода стали, кг


Марка элемента	Изделия арматурные								Всего
	Арматура класса								
	А240			А500С					
	ГОСТ 34028-2016(214-210-0101)			ГОСТ 34028-2016(214-210-0502)					
	ф8	ф10	Итого	ф12	ф14	ф16	ф20	Итого	
Ригель Рм-26	27.89	366.00	393.89	0.00	144.94	126.27	626.80	898.00	1291.89


Ведомость деталей


Поз.	Эскиз
Х1	520, 245, 345, 420; по в.г. L=1530
Ск1	200, 420, 200; по н.г. L=820
Ск6	1000, 370, 1000; по н.г. L=2370
Шп1	370, 100, 100; по в.г. L=570

Таблица размеров накладок

Марка эл-та	dн	L	вес
	мм.		кг.
Н1	32	320	2.01
Н2	28	280	1.35
Н3	25	250	0.96
Н4	22	220	0.66
Н5	20	200	0.49

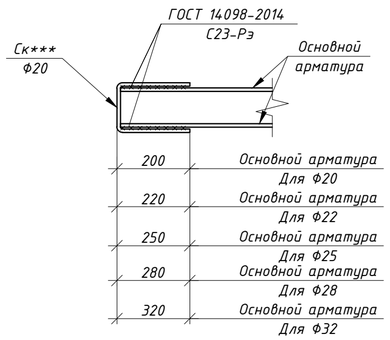

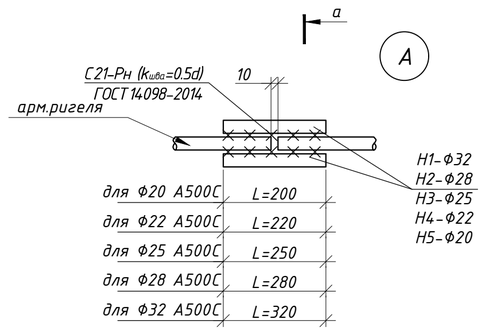

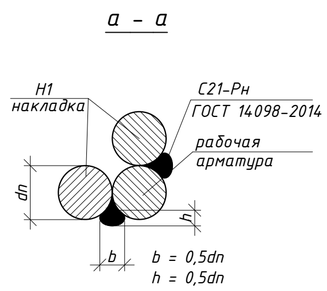


1. Общие указания см. л. - 1.
2. Данный лист читать совместно с л. КЖ-2.2 ... 2.7
3. Стержни, указанные в "Ведомости деталей", должны гнуться механическим способом в холодном состоянии с радиусом гиба 3d - 5d, где d - диаметр стержня


Изм.	Кол.уч	Лист	N док.	Подп.	Дата	65П-АИП-2024-1-КЖ			
						Строительство многопрофильной больницы на 250 коек с онкологическим центром и поликлиникой на 350 посещений, по адресу: Медеуский район, г. Алматы			
ГКП		Курал М				"Блок 1 Секция 1"	Стадия	Лист	Листов
Проверил		Кыдырбай А					РП	6.26	
Разраб.		Ауез Б				Ригель Рм-26	АстанаИнжПроект		
Н.контроль		Ешенкулова							

Формат А2


Ригель Рм-27

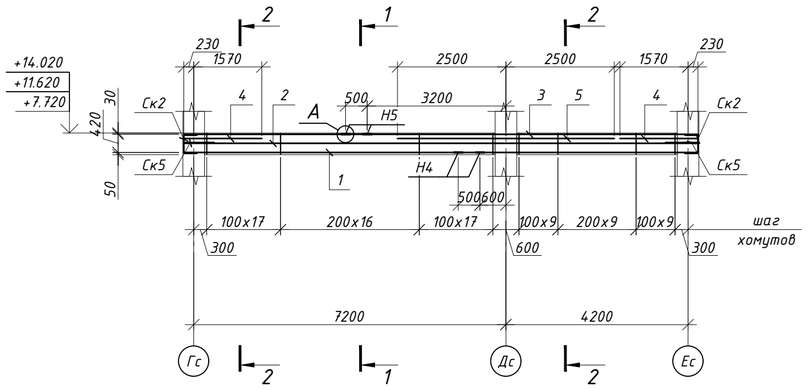

Разрез 1 - 1

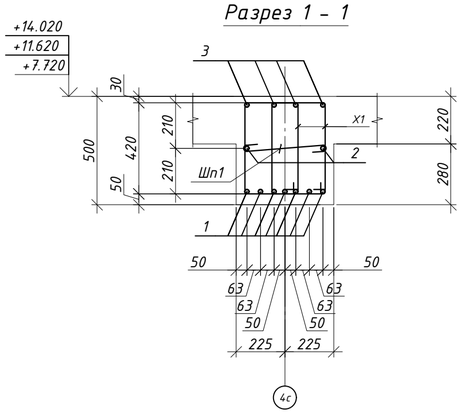

Разрез 2 - 2

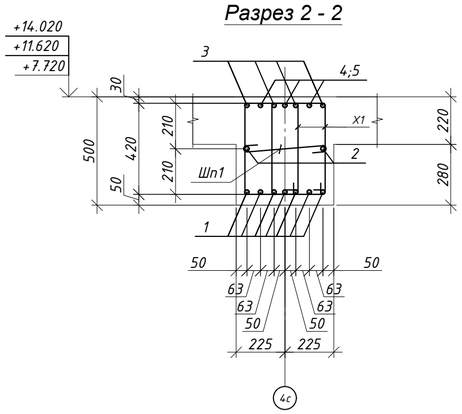

Спецификация элементов

Поз.	Обозначение	Наименование	Кол.	Масса ед.кг	Примечание
		Ригель Рм-27	3		639.90
Х1	ГОСТ 34028-2016(214-210-0101-0003)	ф 10 А 240 L= 1530	158	0.94	149.04
Ск2	ГОСТ 34028-2016(214-210-0502-0005)	ф 20 А500С L= 860	8	2.12	16.97
Ск5	ГОСТ 34028-2016(214-210-0502-0001)	ф 12 А500С L= 2090	2	1.86	3.71
1	ГОСТ 34028-2016(214-210-0502-0006)	ф 22 А500С L= пог.м.	88	2.98	262.60
Н4	ГОСТ 34028-2016(214-210-0502-0006)	ф 22 А500С L= 220	14	0.66	9.19
Н5	ГОСТ 34028-2016(214-210-0502-0005)	ф 20 А500С L= 200	8	0.49	3.95
2	ГОСТ 34028-2016(214-210-0502-0001)	ф 12 А500С L= пог.м.	25	0.89	22.20
3	ГОСТ 34028-2016(214-210-0502-0005)	ф 20 А500С L= пог.м.	50	2.47	123.31
4	ГОСТ 34028-2016(214-210-0502-0002)	ф 14 А500С L= 1800	6	2.18	13.05
5	ГОСТ 34028-2016(214-210-0502-0002)	ф 14 А500С L= 5000	3	6.04	18.13
Шп1	ГОСТ 34028-2016(214-210-0101-0002)	ф 8 А 240 L= 570	79	0.22	17.77
		Материалы:			
	(212-101-0901)	Класс бетона С 20/25 (В25), м³			1.31

Позиции со "*" см. "Ведомость деталей" см. на данном листе.

Ведомость расхода стали, кг


Марка элемента	Изделия арматурные								Всего
	Арматура класса								
	А240			А500С					
	ГОСТ 34028-2016(214-210-0101)			ГОСТ 34028-2016(214-210-0502)					
	ф8	ф10	Итого	ф12	ф14	ф20	ф22	Итого	
Ригель Рм-27	17.77	149.04	166.81	25.91	31.18	144.22	271.79	473.09	639.90


Ведомость деталей


Поз.	Эскиз
Х1	520, 245, 345, 420; по в.г. L=1530
Ск2	220, 420, 220; по н.г. L=860
Ск5	860, 370, 860; по н.г. L=2090
Шп1	370, 100, 100; по в.г. L=570

Таблица размеров накладок

Марка эл-та	dн	L	вес
	мм.		кг.
Н1	32	320	2.01
Н2	28	280	1.35
Н3	25	250	0.96
Н4	22	220	0.66
Н5	20	200	0.49

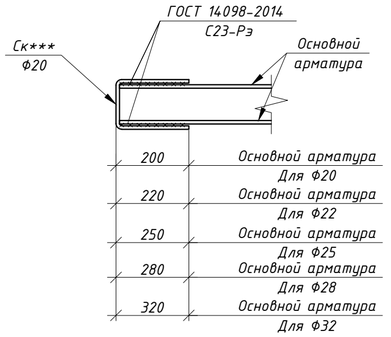

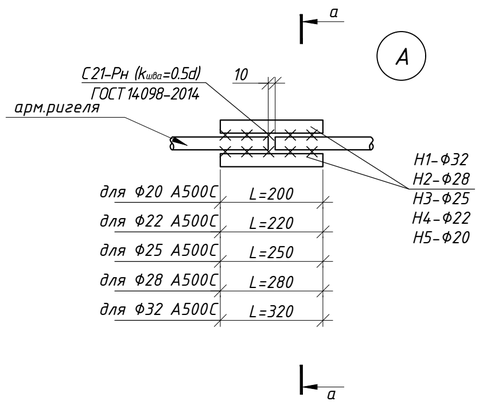

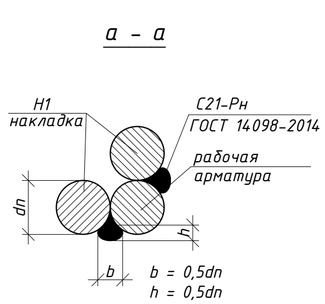


1. Общие указания см. л. - 1.
2. Данный лист читать совместно с л. КЖ-2.2 ... 2.7
3. Стержни, указанные в "Ведомости деталей", должны гнуться механическим способом в холодном состоянии с радиусом гиба 3d - 5d, где d - диаметр стержня


Изм.	Кол.уч.	Лист	N док.	Подп.	Дата	65П-АИП-2024-1-КЖ			
						Строительство многопрофильной больницы на 250 коек с онкологическим центром и поликлиникой на 350 посещений, по адресу: Медеуский район, г. Алматы			
ГКП		Курал М				"Блок 1 Секция 1"	Стадия	Лист	Листов
Проверил		Кыдырбай А					РП	6.27	
Разраб.		Ауез Б				Ригель Рм-27	АстанаИнжПроект		
Н.контроль		Ешенкулова							

Формат А2


Ригель Рм-28

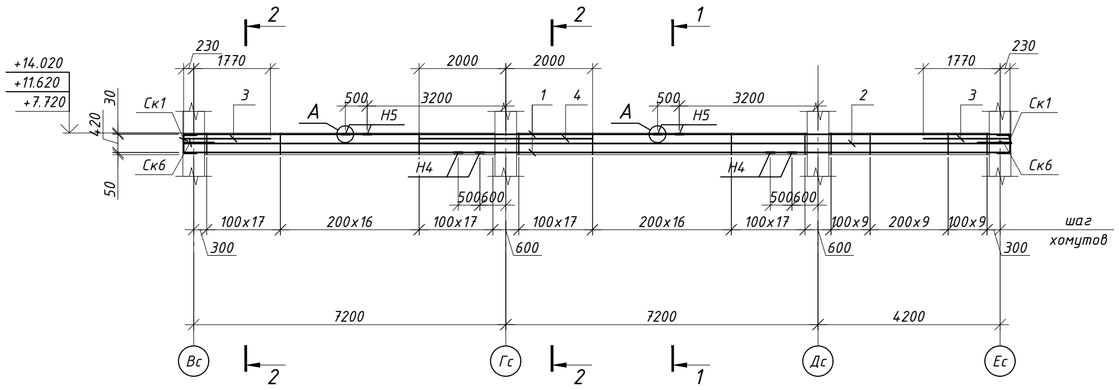

Разрез 1 - 1

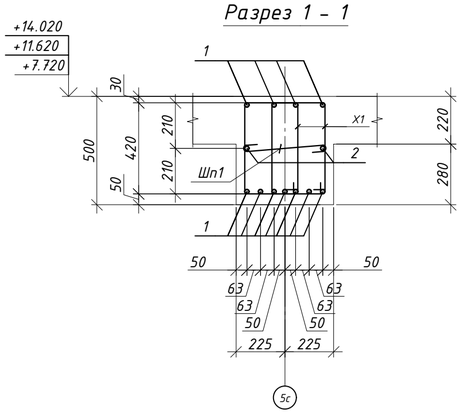

Разрез 2 - 2

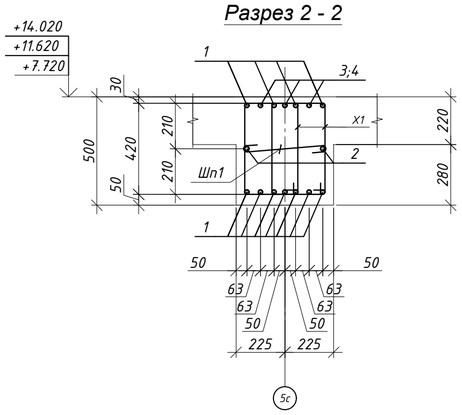

Спецификация элементов

Поз.	Обозначение	Наименование	Кол.	Масса ед.кг	Примечание
		Ригель Рм-28	3		1478.44
Х1	ГОСТ 34028-2016(214-210-0101-0003)	ф 10 А 240 L= 1530	260	0.94	245.26
Ск1	ГОСТ 34028-2016(214-210-0502-0005)	ф 20 А500С L= 820	8	2.02	16.18
Ск6	ГОСТ 34028-2016(214-210-0502-0002)	ф 14 А500С L= 2370	2	2.86	5.73
1	ГОСТ 34028-2016(214-210-0502-0005)	ф 20 А500С L= пог.м.	442	2.47	1090.04
Н5	ГОСТ 34028-2016(214-210-0502-0005)	ф 20 А500С L= 200	30	0.49	14.80
2	ГОСТ 34028-2016(214-210-0502-0002)	ф 14 А500С L= пог.м.	41	1.21	49.54
3	ГОСТ 34028-2016(214-210-0502-0002)	ф 14 А500С L= 2000	6	2.42	14.50
4	ГОСТ 34028-2016(214-210-0502-0002)	ф 14 А500С L= 4000	3	4.83	14.50
Шп1	ГОСТ 34028-2016(214-210-0101-0002)	ф 8 А 240 L= 570	124	0.22	27.89
		Материалы:			
	(212-101-0901)	Класс бетона С 20/25 (В25), м^3			2.15

Позиции со "*" см. "Ведомость деталей" см. на данном листе.

Ведомость расхода стали, кг


Марка элемента	Изделия арматурные								Всего
	Арматура класса								
	А240			А500С					
	ГОСТ 34028-2016(214-210-0101)			ГОСТ 34028-2016(214-210-0502)					
	ф8	ф10	Итого	ф12	ф14	ф20	ф22	Итого	
Ригель Рм-28	27.89	245.26	273.15	0.00	84.27	1121.01	0.00	1205.29	1478.44


Ведомость деталей


Поз.	Эскиз
Х1	520, 245, 345, 420; по в.г. L=1530
Ск1	200, 420, 200; по н.г. L=820
Ск6	1000, 370, 1000; по н.г. L=2370
Шп1	370, 100, 100; по в.г. L=570

Таблица размеров накладок

Марка эл-та	dн	L	вес
	мм.		кг.
Н1	32	320	2.01
Н2	28	280	1.35
Н3	25	250	0.96
Н4	22	220	0.66
Н5	20	200	0.49

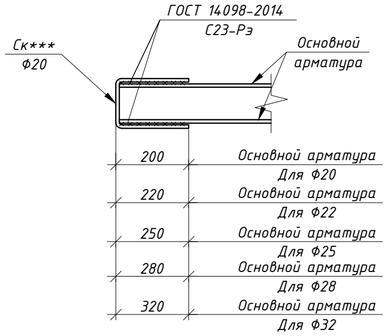

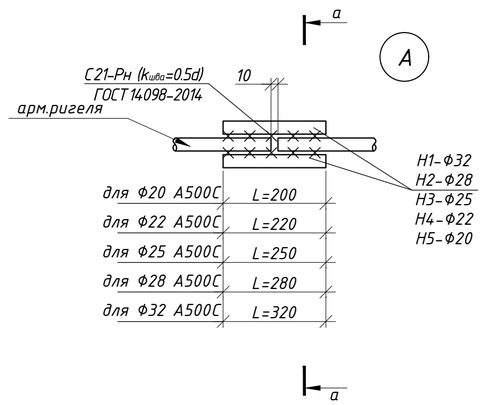

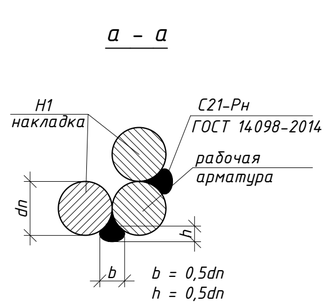


1. Общие указания см. л. - 1.
2. Данный лист читать совместно с л. КЖ-2.2 ... 2.7
3. Стержни, указанные в "Ведомости деталей", должны гнуться механическим способом в холодном состоянии с радиусом гиба 3d - 5d, где d - диаметр стержня


Изм.	Кол.уч.	Лист	N док.	Подп.	Дата	65П-АИП-2024-1-КЖ			
						Строительство многопрофильной больницы на 250 коек с онкологическим центром и поликлиникой на 350 посещений, по адресу: Медеуский район, г. Алматы			
ГКП		Курал М				"Блок 1 Секция 1"	Стадия	Лист	Листов
Проверил		Кыдырбай А					РП	6.28	
Разраб.		Ауез Б				Ригель Рм-28	АстанаИнжПроект		
Н.контроль		Ешенкулова							

Формат А2

Ригель Рм-29

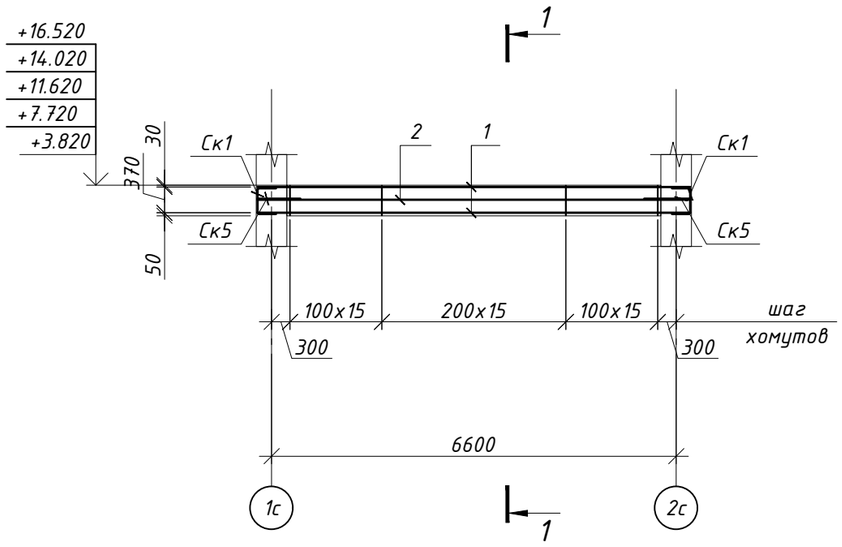

Разрез 1 - 1

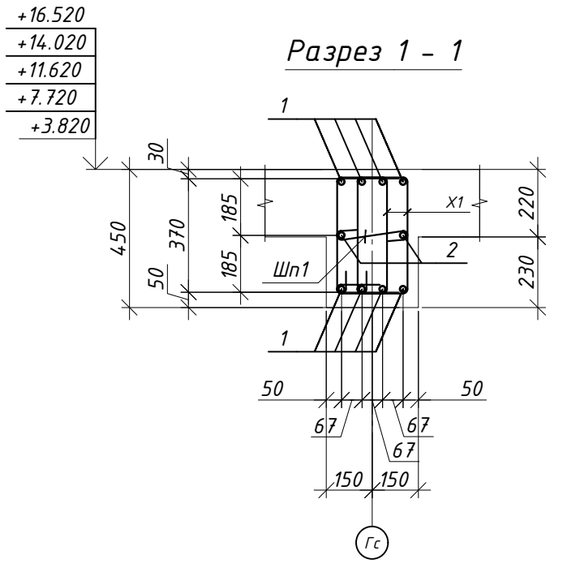

Спецификация элементов

Поз.	Обозначение	Наименование	Кол.	Масса ед.кг	Примечание
		Ригель Рм-29	6		223.10
Х1	ГОСТ 34028-2016(214-210-0101-0002)	ф 8 А 240 L= 1240	92	0.49	45.01
Шп1	ГОСТ 34028-2016(214-210-0101-0002)	ф 8 А 240 L= 420	46	0.17	7.62
Ск1	ГОСТ 34028-2016(214-210-0502-0005)	ф 20 А500С L= 770	8	1.90	15.19
Ск5	ГОСТ 34028-2016(214-210-0502-0001)	ф 12 А500С L= 1940	2	1.72	3.44
1	ГОСТ 34028-2016(214-210-0502-0005)	ф 20 А500С L= 7060	8	17.41	139.29
2	ГОСТ 34028-2016(214-210-0502-0001)	ф 12 А500С L= 7060	2	6.27	12.54
		Материалы:			
	(212-101-0901)	Класс бетона С 20/25 (В25), м³			0.42


Позиции со "*" см. "Ведомость деталей" см. на данном листе.

Ведомость расхода стали, кг

Марка элемента	Изделия арматурные							Всего
	Арматура класса							
	А240 ГОСТ 34028-2016(214-210-0101)		А500С ГОСТ 34028-2016(214-210-0502)					
	ф8	Итого	ф12	ф14	ф16	ф20	Итого	
Ригель Рм-29	52.64	52.64	15.98	0.00	0.00	154.48	170.46	223.10

Ведомость деталей

Поз.	Эскиз	Поз.	Эскиз
Х1	470, 150, 250, 370; по в.г. L=1240	Ск1	200, 370, 200; по н.г. L=770
Шп1	220, 100, 100; по в.г. L=420	Ск5	860, 220, 860; по н.г. L=1940

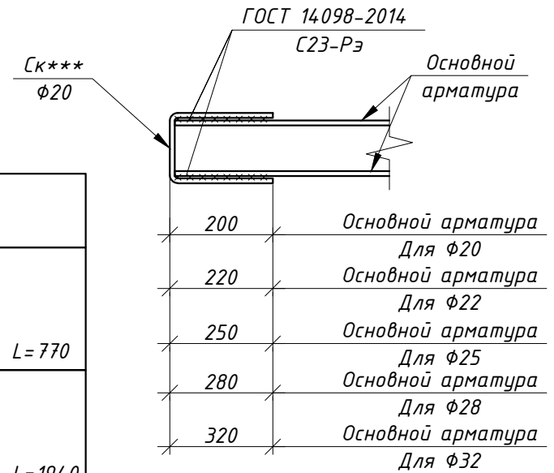


1. Общие указания см. л. - 1.
2. Данный лист читать совместно с л. КЖ-2.2 ... 2.7
3. Стержни, указанные в "Ведомости деталей", должны гнуться механическим способом в холодном состоянии с радиусом гиба 3d - 5d, где d - диаметр стержня


Изм.	Кол.уч.	Лист	N док.	Подп.	Дата	65П-АИП-2024-1-КЖ		
						Строительство многопрофильной больницы на 250 коек с онкологическим центром и поликлиникой на 350 посещений, по адресу: Медеуский район, г. Алматы		
						"Блок 1 Секция 1"	Стадия: РП	Лист: 6.29
ГКП		Курал М						
Проверил		Кыдырбай А				Ригель Рм-29	АстанаИнжПроект	
Разраб.		Ауез Б						
Н.контроль		Ешенкулова						

Формат А3

Ригель Рм-30

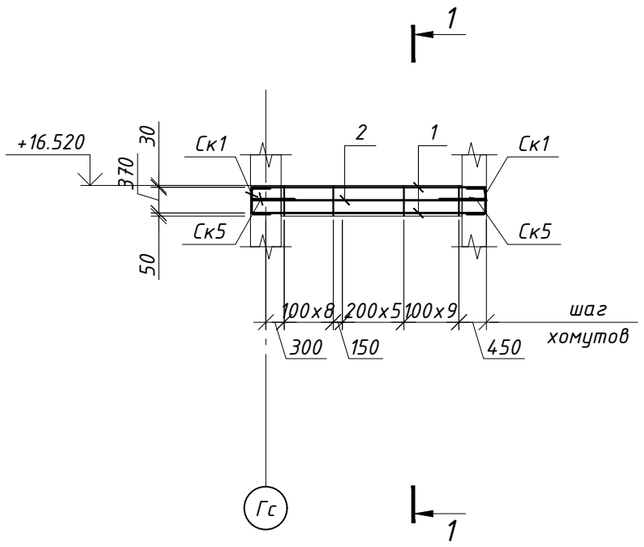

Разрез 1 - 1

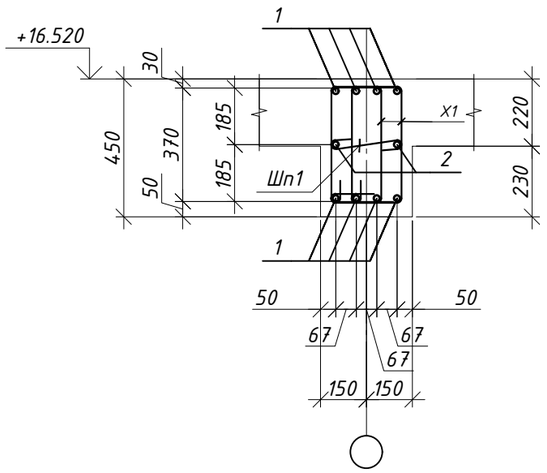

Спецификация элементов

Поз.	Обозначение	Наименование	Кол.	Масса ед.кг	Примечание
		Ригель Рм-30	2		128.03
X1	ГОСТ 34028-2016(214-210-0101-0002)	ф 8 А 240 L= 1240	48	0.49	23.49
Шп1	ГОСТ 34028-2016(214-210-0101-0002)	ф 8 А 240 L= 420	24	0.17	3.98
Ск1	ГОСТ 34028-2016(214-210-0502-0005)	ф 20 А500С L= 770	8	1.90	15.19
Ск5	ГОСТ 34028-2016(214-210-0502-0001)	ф 12 А500С L= 1940	2	1.72	3.44
1	ГОСТ 34028-2016(214-210-0502-0005)	ф 20 А500С L= 3810	8	9.40	75.17
2	ГОСТ 34028-2016(214-210-0502-0001)	ф 12 А500С L= 3810	2	3.38	6.77
		Материалы:			
	(212-101-0901)	Класс бетона С 20/25 (В25), м³			0.20


Позиции со "*" см. "Ведомость деталей" см. на данном листе.

Ведомость расхода стали, кг

Марка элемента	Изделия арматурные							Всего
	Арматура класса							
	А240		А500С					
	ГОСТ 34028-2016(214-210-0101)		ГОСТ 34028-2016(214-210-0502)					
	ф8	Итого	ф12	ф14	ф16	ф20	Итого	
Ригель Рм-30	27.46	27.46	10.21	0.00	0.00	90.36	100.57	128.03

Ведомость деталей

Поз.	Эскиз	Поз.	Эскиз
X1	470, 150, 250, 370; по в.г. L=1240	Ск1	200, 370, 200; по н.г. L=770
Шп1	220, 100, 100; по в.г. L=420	Ск5	860, 220, 860; по н.г. L=1940

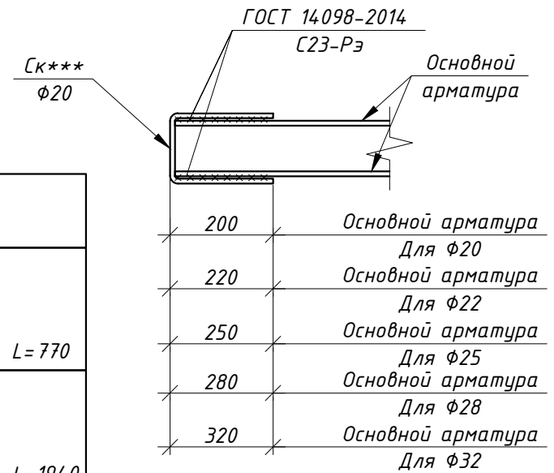

1. Общие указания см. л. - 1.
2. Данный лист читать совместно с л. КЖ-2.2 ... 2.7
3. Стержни, указанные в "Ведомости деталей", должны гнуться механическим способом в холодном состоянии с радиусом гиба 3d - 5d, где d - диаметр стержня

Изм.	Кол.уч	Лист	N док.	Подп.	Дата	65П-АИП-2024-1-КЖ		
						Строительство многопрофильной больницы на 250 коек с онкологическим центром и поликлиникой на 350 посещений, по адресу: Медеуский район, г. Алматы		
						"Блок 1 Секция 1"	Стадия: РП	Лист: 6.30
ГКП		Курал М						
Проверил		Кыдырбай А				Ригель Рм-30	АстанаИнжПроект	
Разраб.		Ауез Б						
Н.контроль		Ешенкулова						

Формат А3