


Опалубочный чертеж плиты перекрытия Пм-1 на отм. -0.080

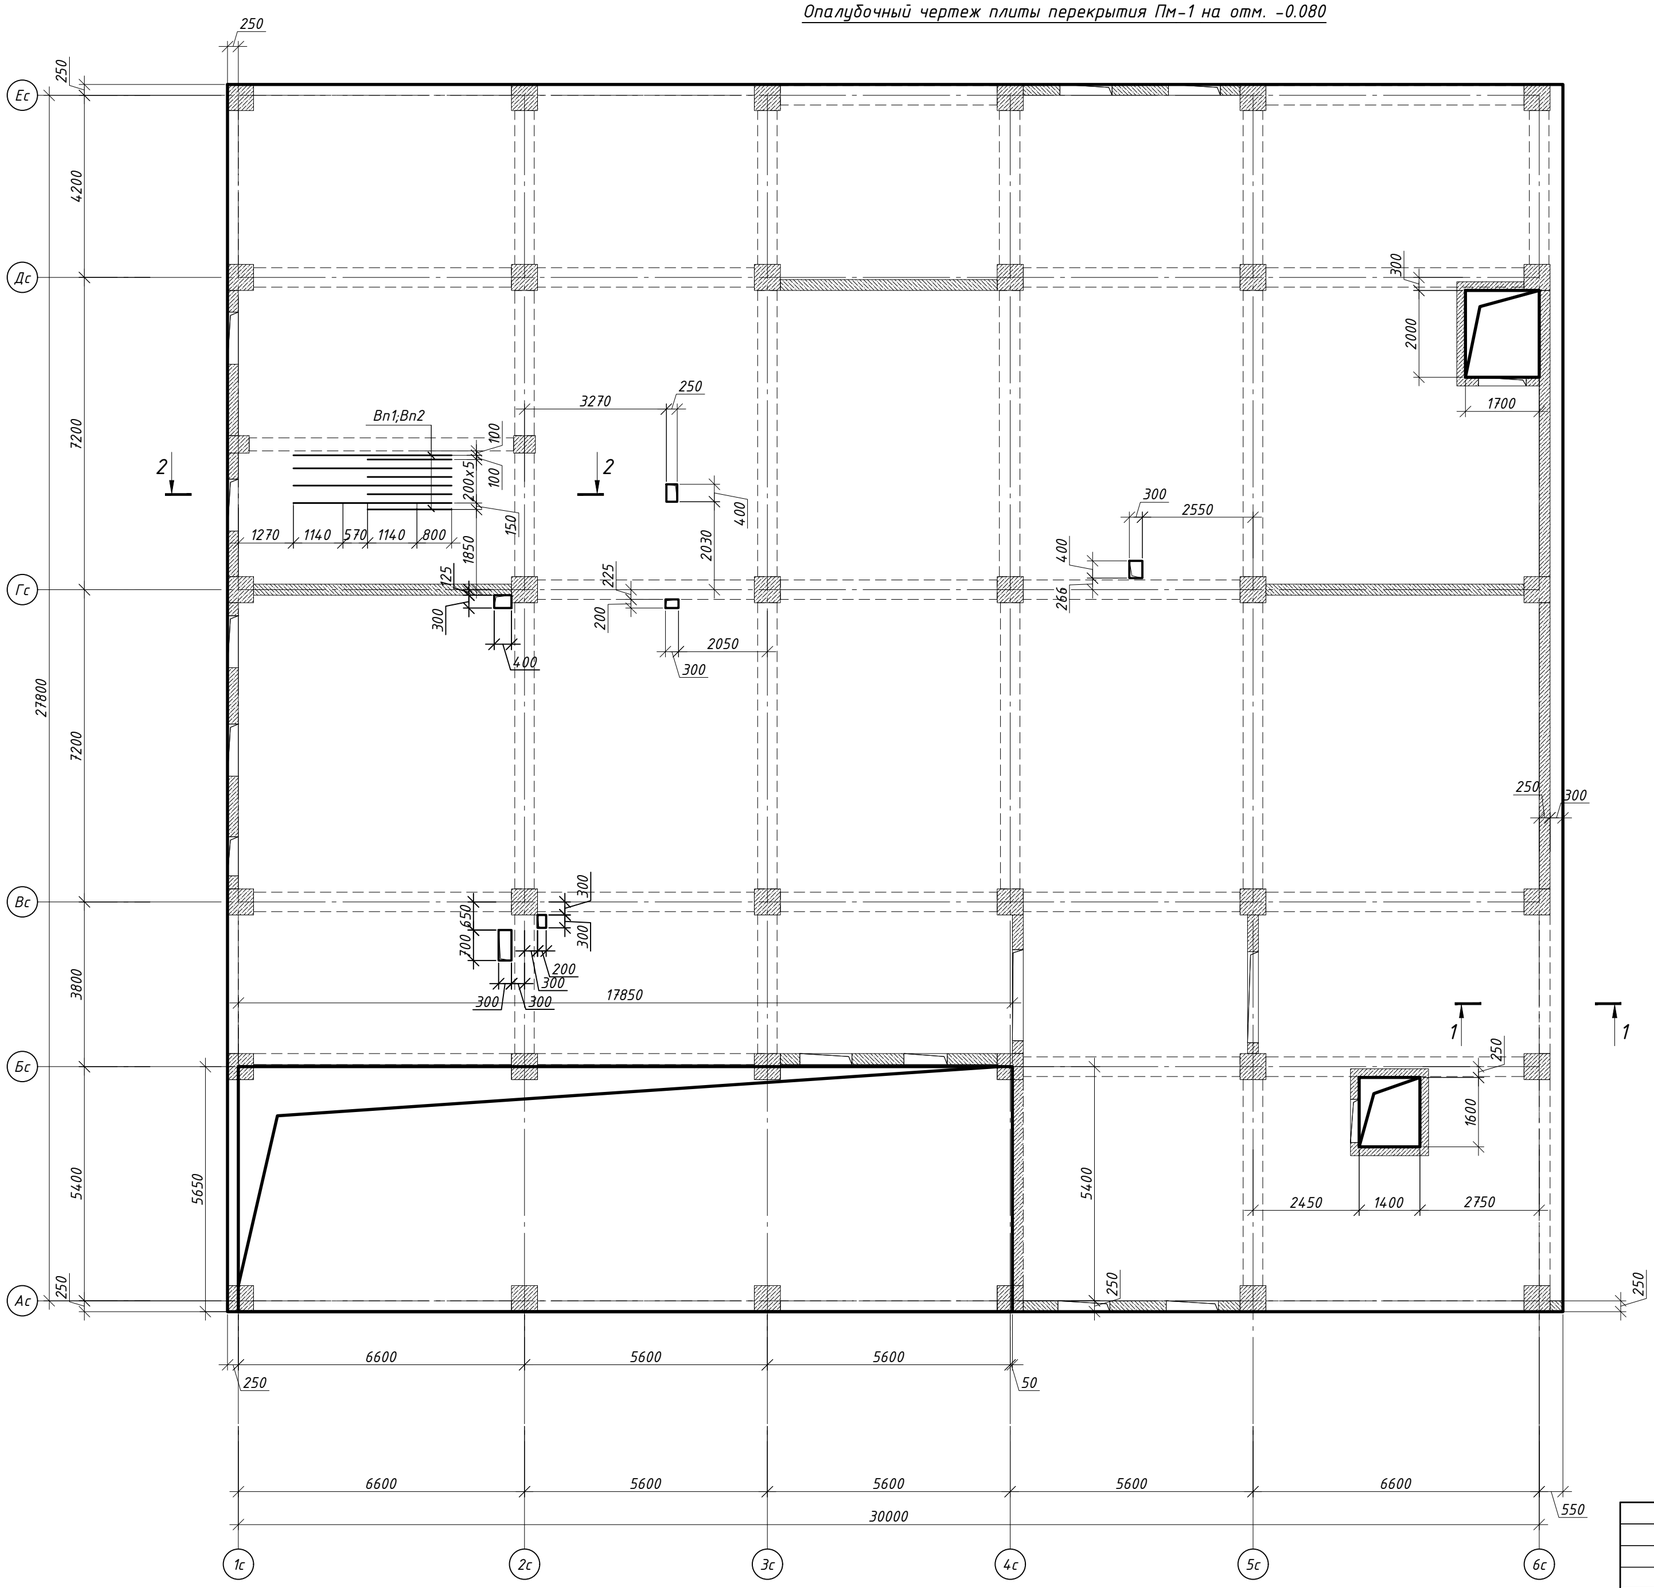

Разрез 1 - 1 (Опалубка)
М 1:50

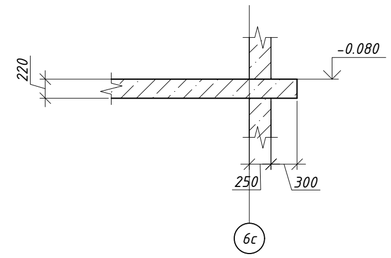

Разрез 2 - 2

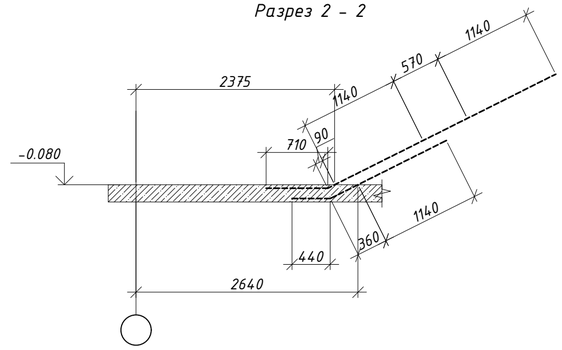


1. Данный лист читать совместно с листами КЖ-2.2 и КЖ-7.1 ... 7.7.
2. Арматура плиты перекрытия стыкуется внахлест.
3. Стыки нижней арматуры выполнять на опоре, стыки верхней арматуры на расстоянии 1/3 - 1/4 пролета от опоры, при этом в одном сечении стыковать не более 50% арматуры.
4. Продольную и поперечную арматуру во всех пересечениях связать вязальной проволокой.
5. Свободные концы основной арматуры у торцов плиты перекрытия должны быть заанкерены "П"-образной скобой (поз. Ск1) при помощи вязальной проволоки (без сварки).
6. Спецификацию см. лист КЖ-7.7

						65П-АИП-2024-1-КЖ	
						Строительство многопрофильной больницы на 250 коек с онкологическим центром и поликлиникой на 350 посещений, по адресу: Медеуский район, г. Алматы	
Изм.	Кол.уч	Лист	N док.	Подп.	Дата		
						"Блок 1 Секция 1"	Стадия: РП; Лист: 7.1; Листов:
ГКП		Курал М					
Проверил		Кыдырбай А				Опалубочный чертеж плиты перекрытия Пм-1 на отм. -0.080	АстанаИнжПроект
Разраб.		Ауез Б					
Н.контроль		Ешенкулова					

Формат А2

Схема расположения основных арматуры плиты перекрытия Пм-1 на отм -0.080

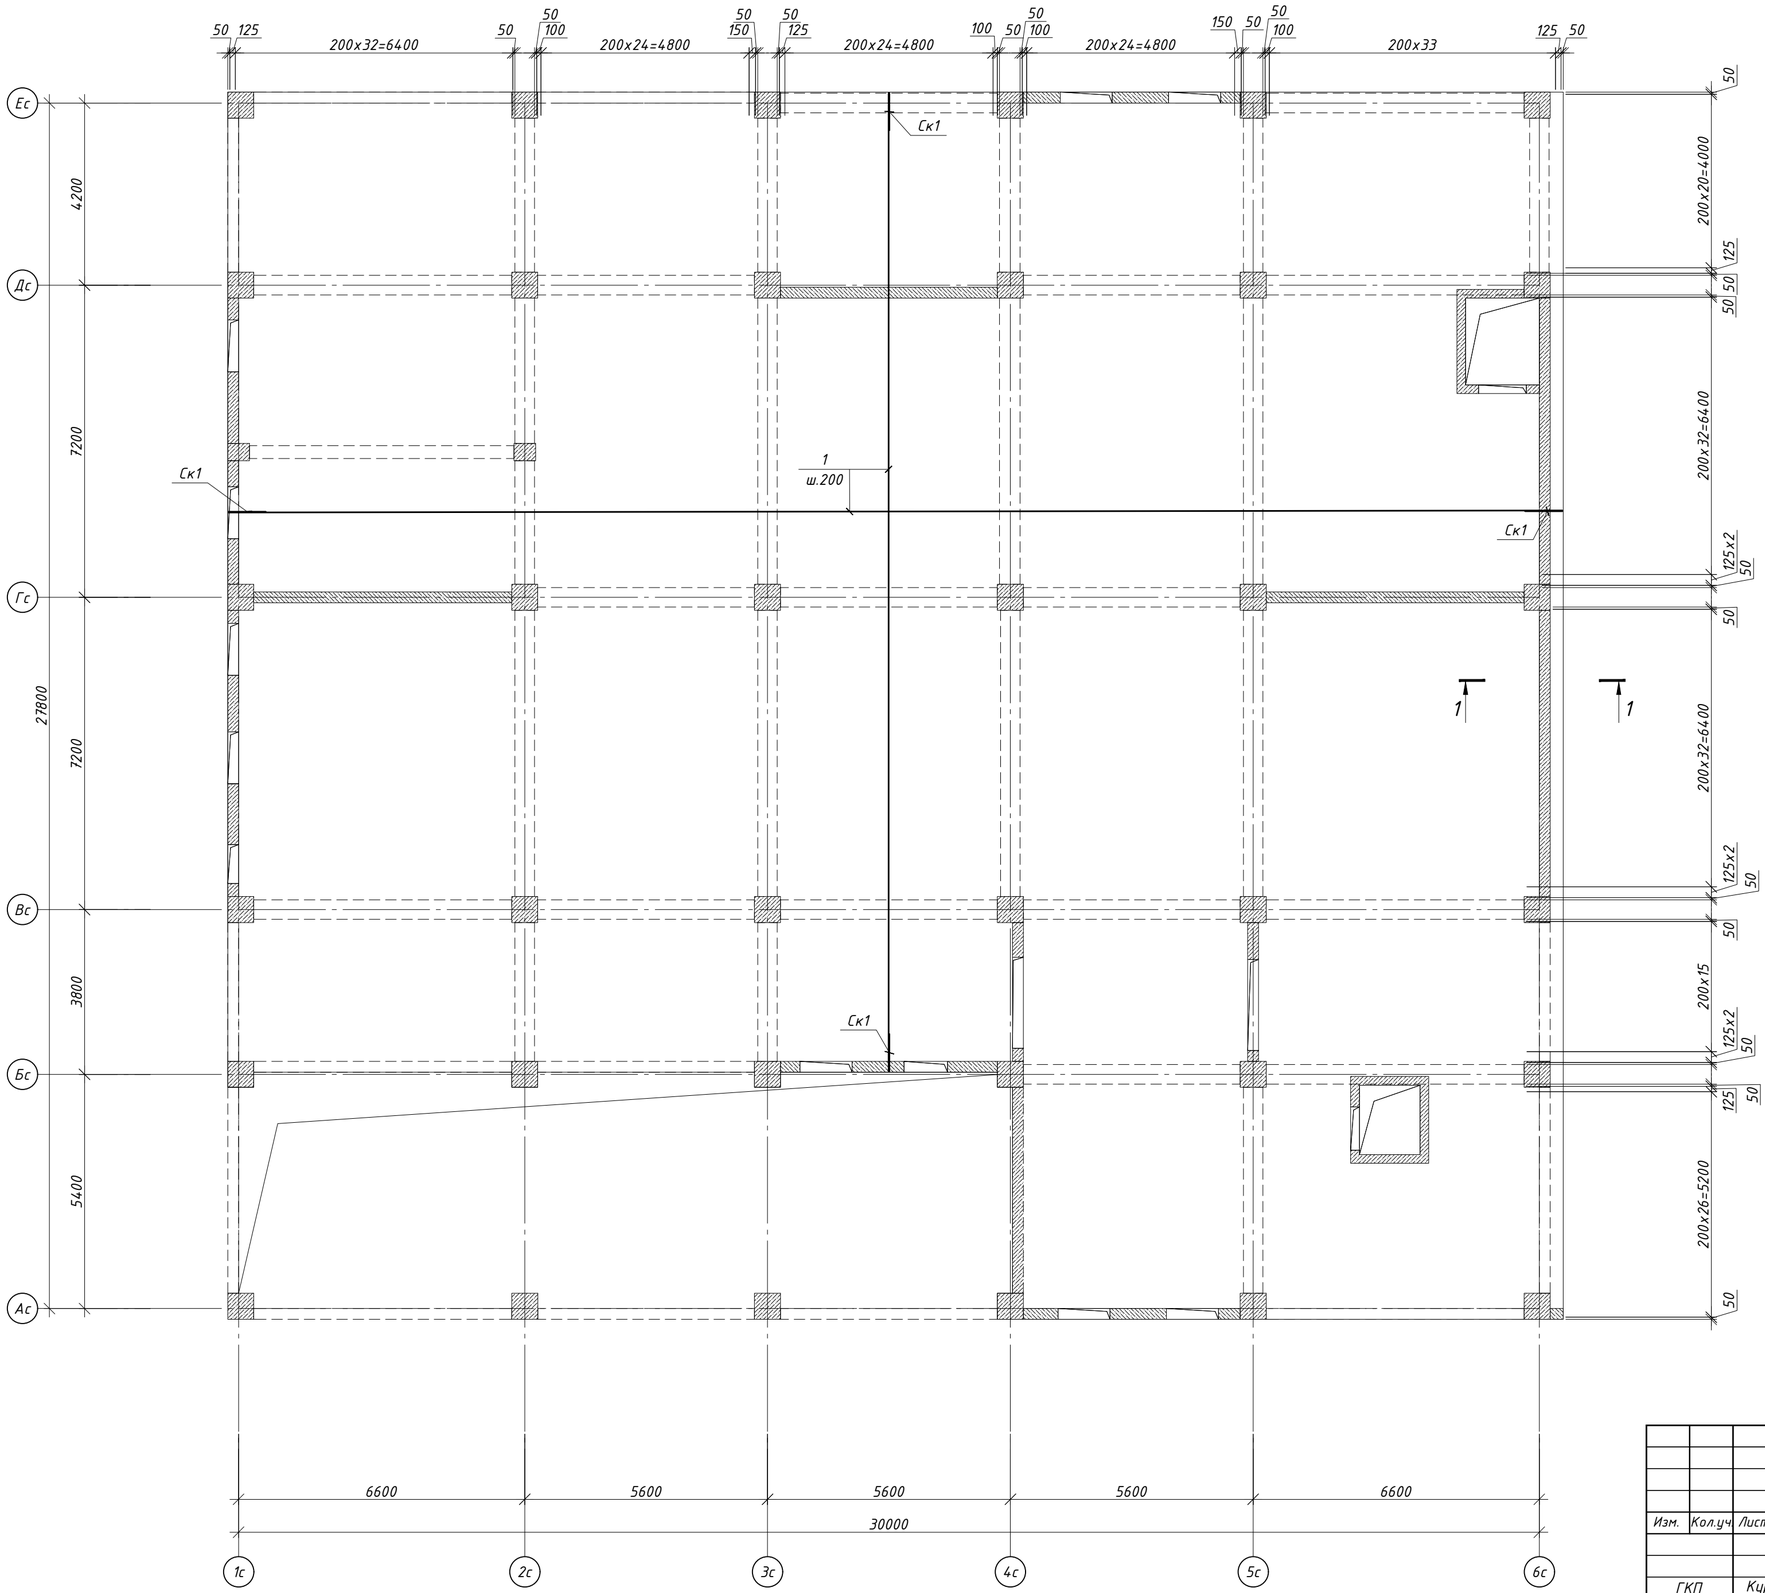


1. Данный лист читать совместно с листами КЖ-2.2 и КЖ-7.1 ... 7.7.
2. Арматура плиты перекрытия стыкуется внахлест.
3. Стыки нижней арматуры выполнять на опоре, стыки верхней арматуры на расстоянии 1/3 - 1/4 пролета от опоры, при этом в одном сечении стыковать не более 50% арматуры.
4. Продольную и поперечную арматуру во всех пересечениях связать вязальной проволокой.
5. Свободные концы основной арматуры у торцов плиты перекрытия должны быть заанкерены "П"-образной скобой (поз. Ск1) при помощи вязальной проволоки (без сварки).
6. Спецификацию см. лист КЖ-7.7

Изм.	Кол.уч	Лист	N док.	Подп.	Дата	65П-АИП-2024-1-КЖ			
						Строительство многопрофильной больницы на 250 коек с онкологическим центром и поликлиникой на 350 посещений, по адресу: Медеуский район, г. Алматы			
ГКП		Курал М				"Блок 1 Секция 1"	Стадия	Лист	Листов
Проверил		Кыдырбай А					РП	7.2	
Разраб.		Ауез Б				Схема расположения основных арматуры плиты перекрытия Пм-1 на отм -0.080	АстанаИнжПроект		
Н.контроль		Ешенкулова							

Формат А2

Схема расположения дополнительного арматуры плиты перекрытия Пм-1 нижней зоны по буквенным осям на отм -0.080

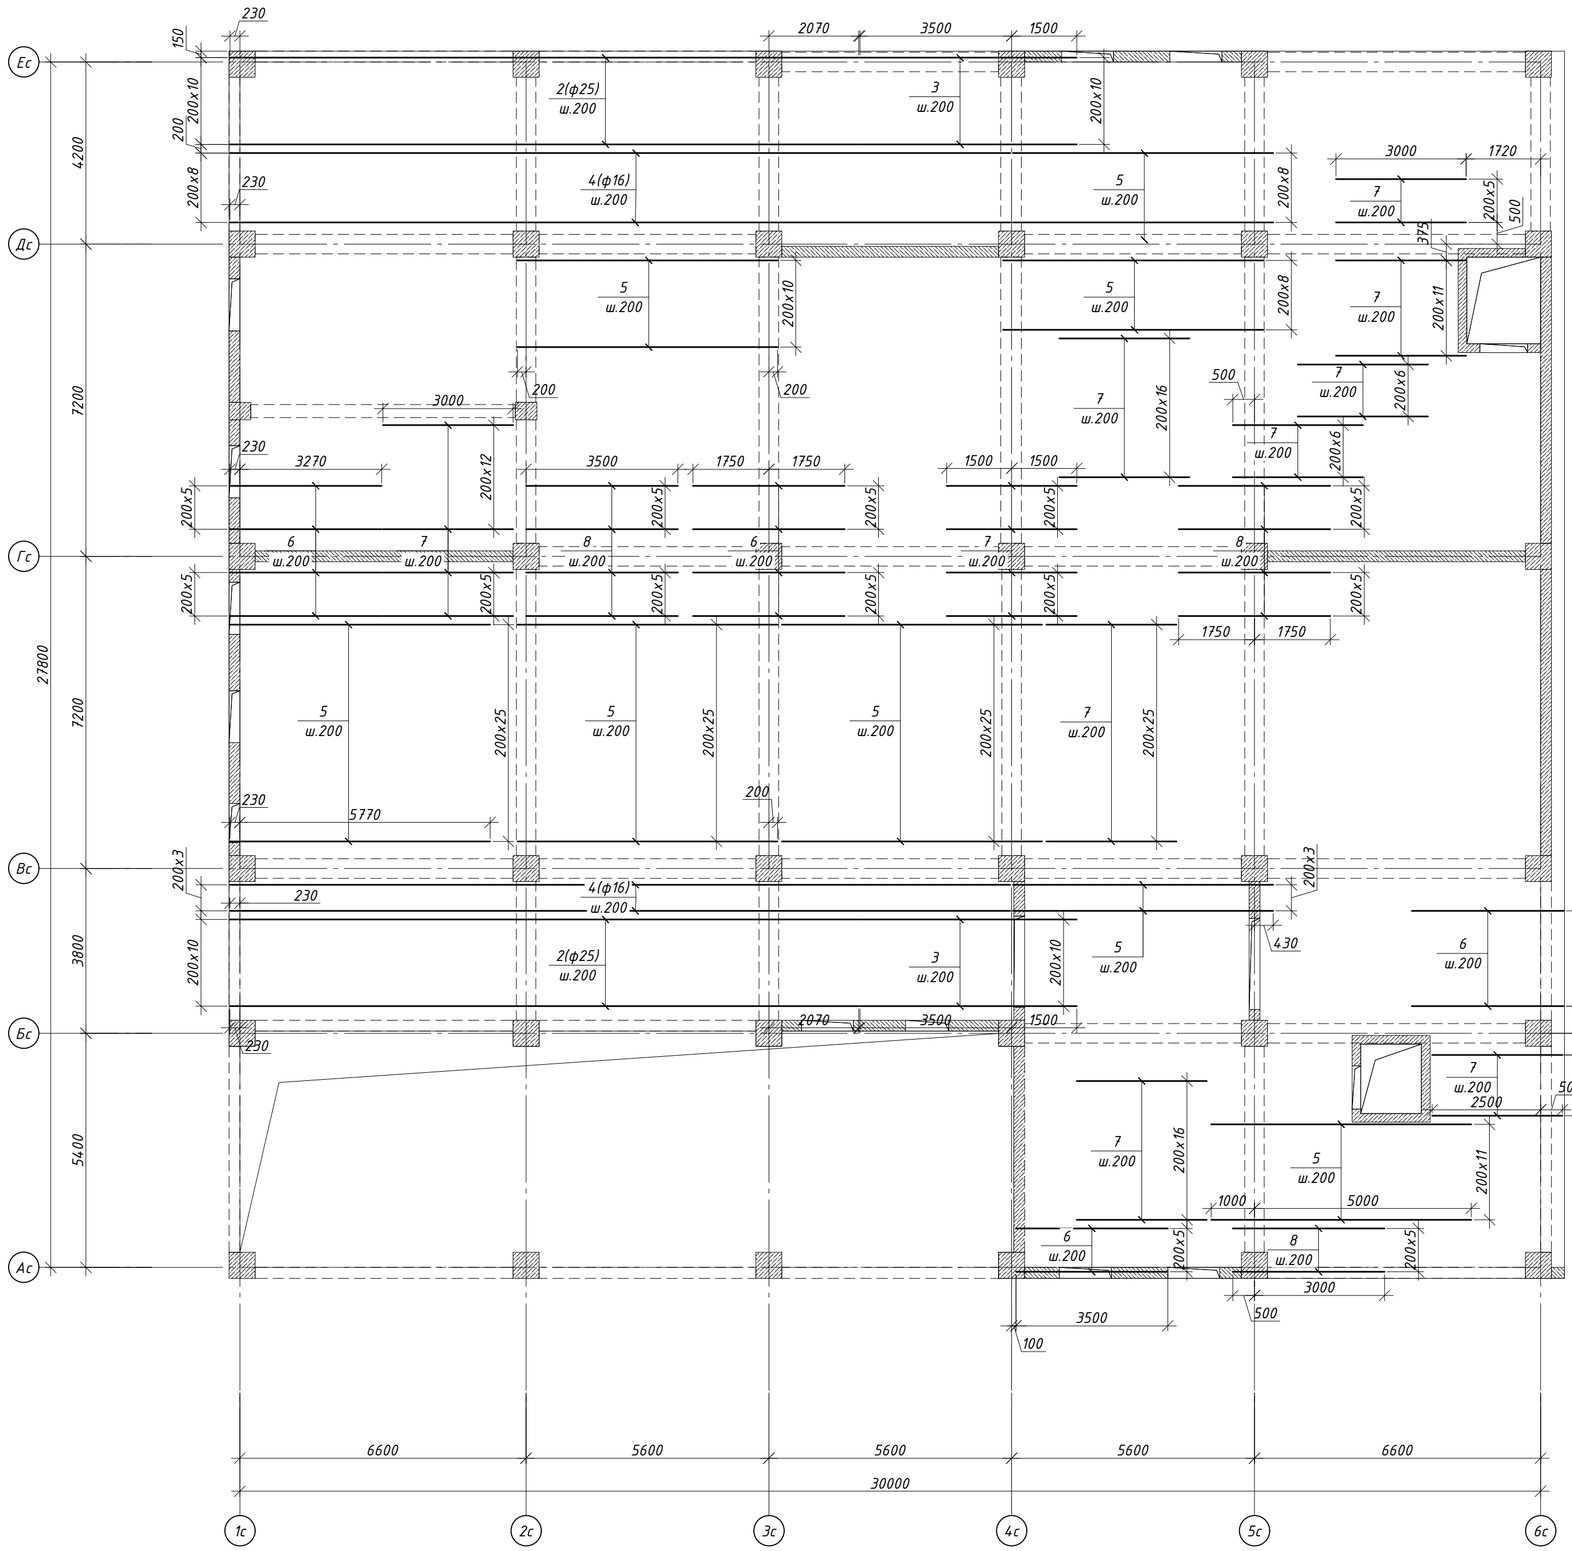


1. Данный лист читать совместно с листами КЖ-2.2 и КЖ-7.1 ... 7.7.
2. Арматура плиты перекрытия стыкуется внахлест.
3. Стыки нижней арматуры выполнять на опоре, стыки верхней арматуры на расстоянии 1/3 - 1/4 пролета от опоры, при этом в одном сечении стыковать не более 50% арматуры.
4. Продольную и поперечную арматуру во всех пересечениях связать вязальной проволокой.
5. Свободные концы основной арматуры у торцов плиты перекрытия должны быть заанкерены "П"-образной скобой (поз. Ск1) при помощи вязальной проволоки (без сварки).
6. Спецификацию см. лист КЖ-7.7

						65П-АИП-2024-1-КЖ	
						Строительство многопрофильной больницы на 250 коек с онкологическим центром и поликлиникой на 350 посещений, по адресу: Медеуский район, г. Алматы	
Изм.	Кол.уч.	Лист	N док.	Подп.	Дата		
ГКП		Курал М				"Блок 1 Секция 1"	Стадия: РП; Лист: 7.3; Листов:
Проверил		Кыдырбай А				Схема расположения дополнительного арматуры плиты перекрытия Пм-1 нижней зоны по буквенным осям на отм -0.080	АстанаИнжПроект
Разраб.		Ауез Б					
Н.контроль		Ешенкулова					

Формат А2

Схема расположения дополнительного арматуры плиты перекрытия Пм-1 верхней зоны по буквенным осям на отм -0.080

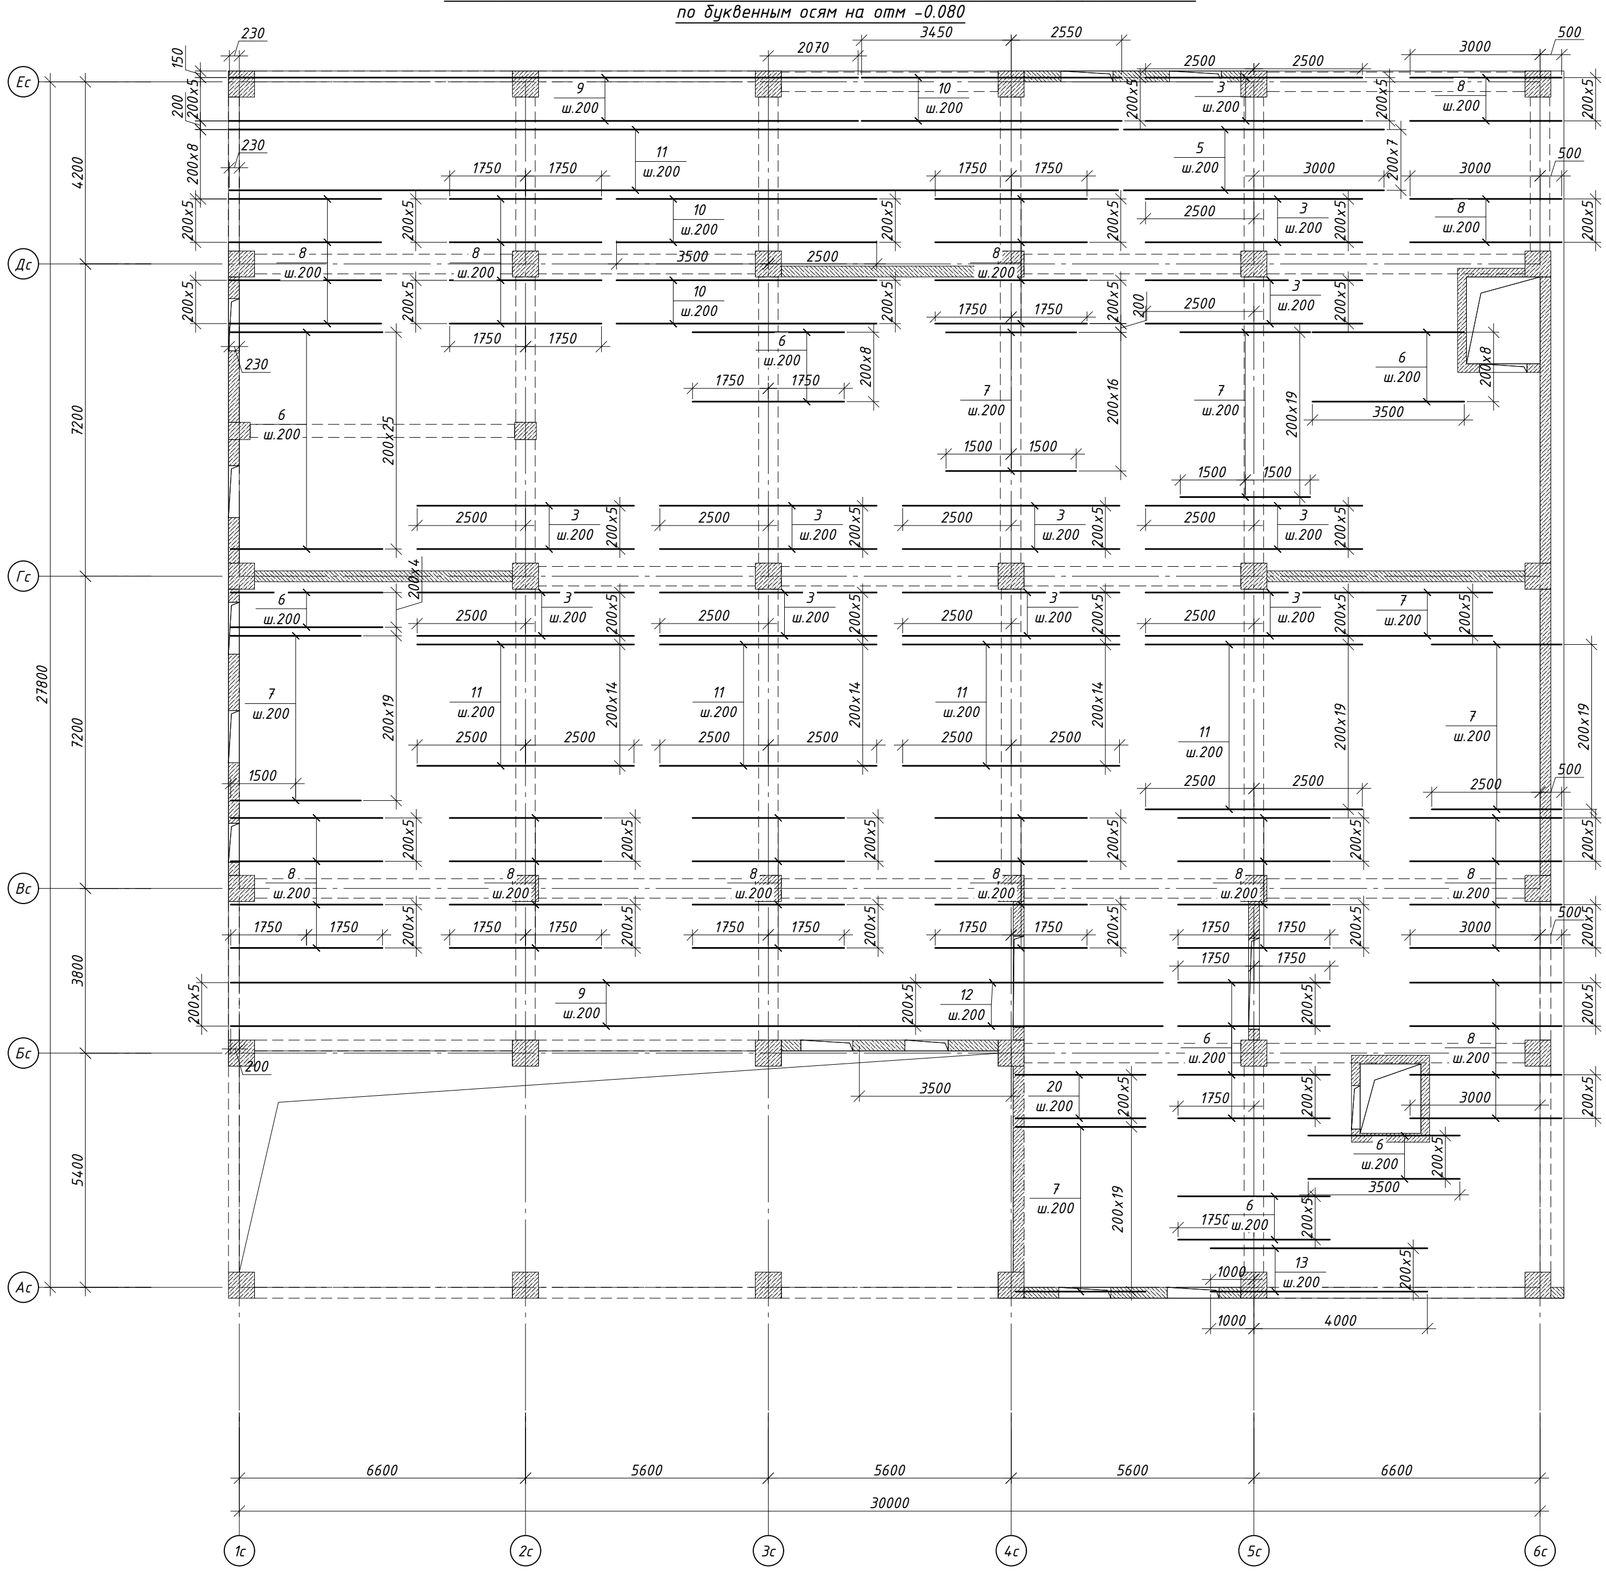


1. Данный лист читать совместно с листами КЖ-2.2 и КЖ-7.1 ... 7.7.
2. Арматура плиты перекрытия стыкуется внахлест.
3. Стыки нижней арматуры выполнять на опоре, стыки верхней арматуры на расстоянии 1/3 - 1/4 пролета от опоры, при этом в одном сечении стыковать не более 50% арматуры.
4. Продольную и поперечную арматуру во всех пересечениях связать вязальной проволокой.
5. Свободные концы основной арматуры у торцов плиты перекрытия должны быть заанкерены "П"-образной скобой (поз. Ск1) при помощи вязальной проволоки (без сварки).
6. Спецификацию см. лист КЖ-7.7

						65П-АИП-2024-1-КЖ
						Строительство многопрофильной больницы на 250 коек с онкологическим центром и поликлиникой на 350 посещений, по адресу: Медеуский район, г. Алматы
Изм.	Кол.уч.	Лист	N док.	Подп.	Дата	
						"Блок 1 Секция 1" — Стадия: РП; Лист: 7.4; Листов:
ГКП		Курал М				Схема расположения дополнительного арматуры плиты перекрытия Пм-1 верхней зоны по буквенным осям на отм -0.080
Проверил		Кыдырбай А				АстанаИнжПроект
Разраб.		Ауез Б				
Н.контроль		Ешенкулова				

Формат А2


Схема расположения дополнительного арматуры плиты перекрытия Пм-1 нижней зоны по цифровым осям на отм -0.080

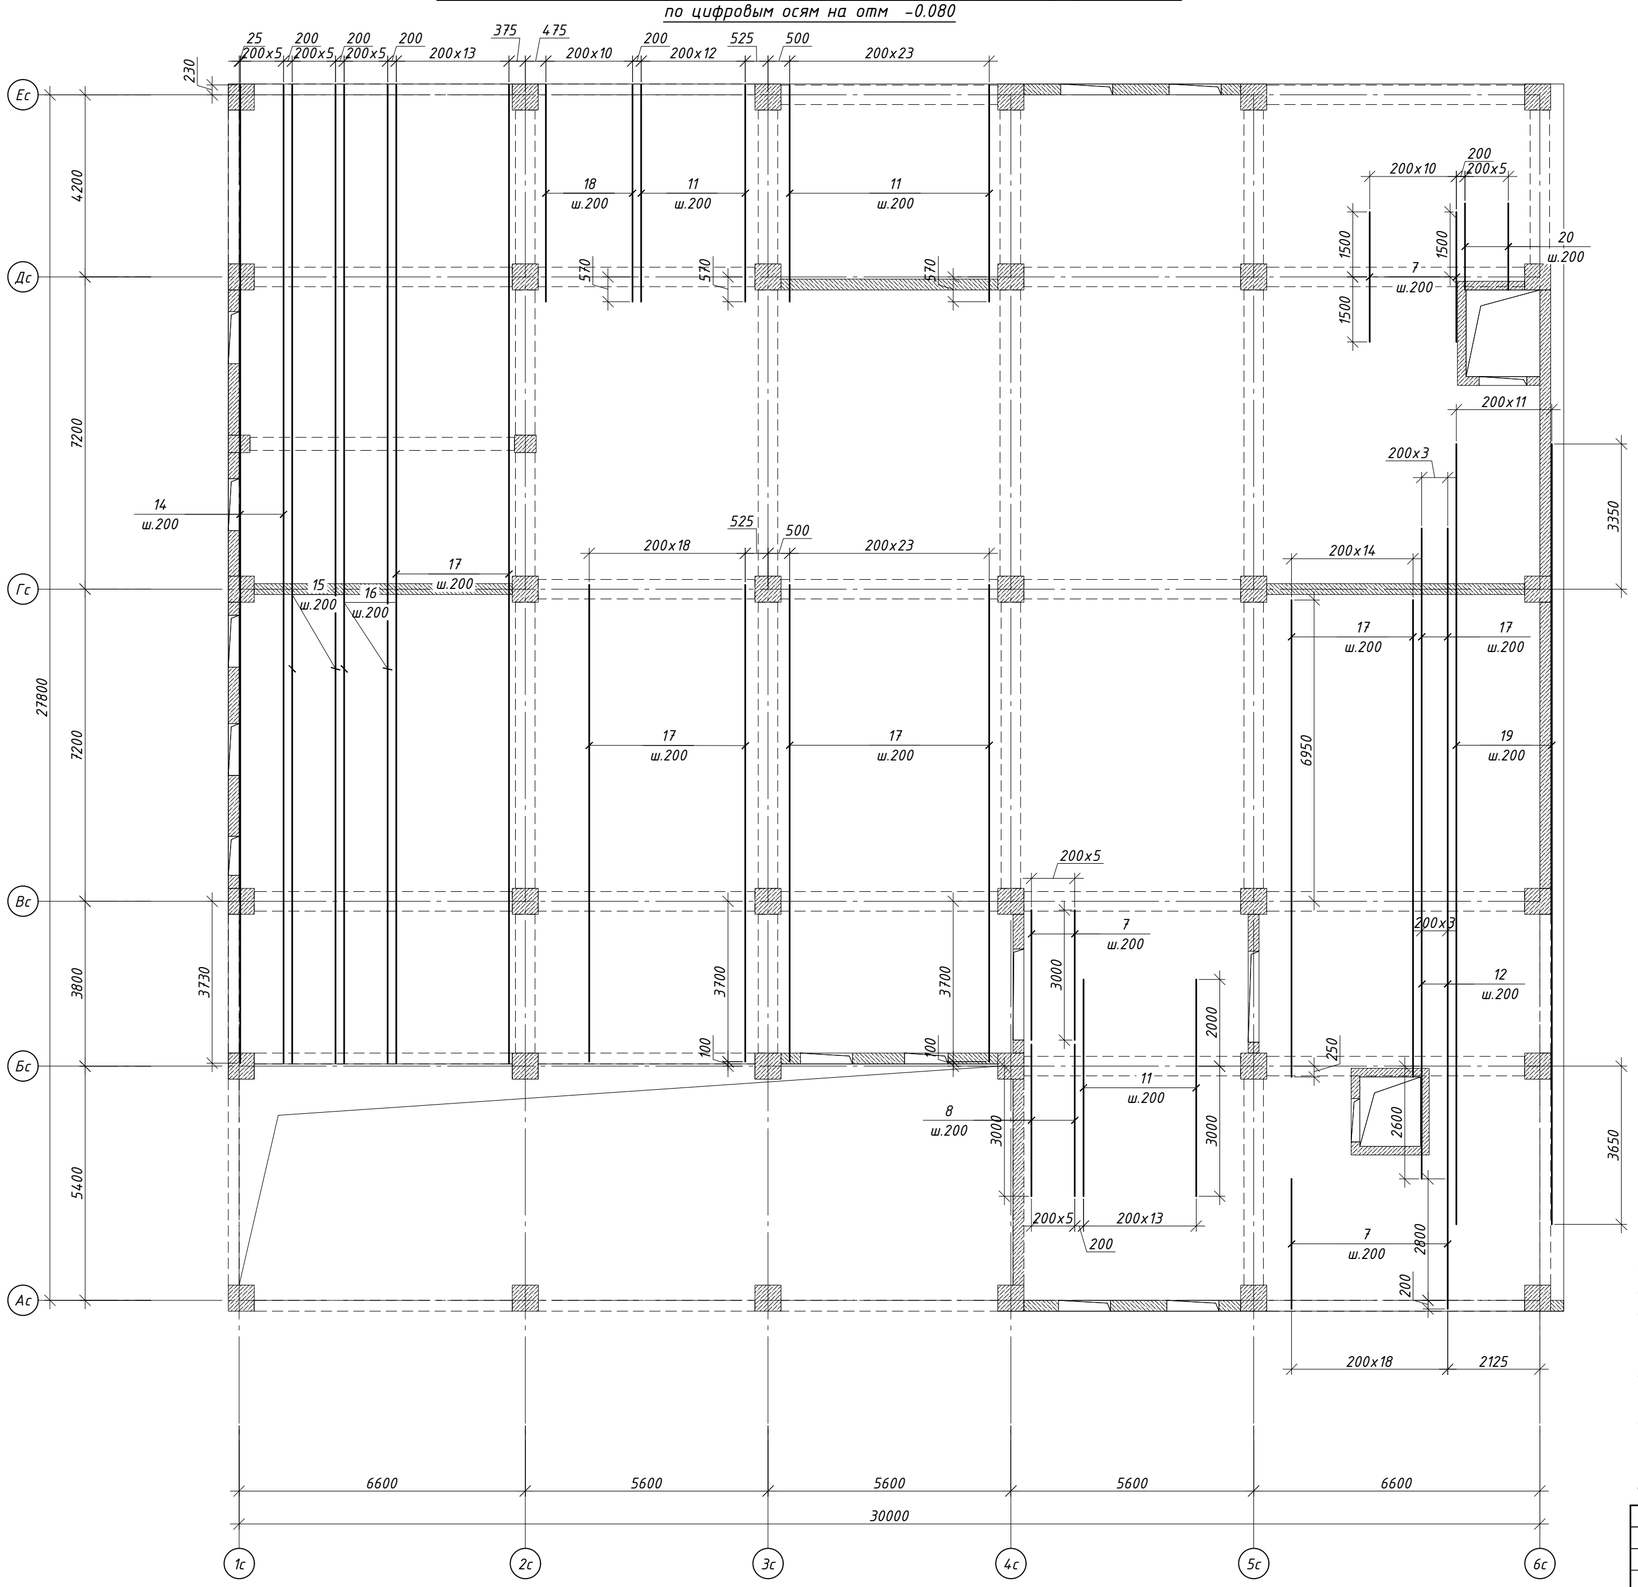

1. Данный лист читать совместно с листами КЖ-2.2 и КЖ-7.1 ... 7.7.
2. Арматура плиты перекрытия стыкуется внахлест.
3. Стыки нижней арматуры выполнять на опоре, стыки верхней арматуры на расстоянии 1/3 - 1/4 пролета от опоры, при этом в одном сечении стыковать не более 50% арматуры.
4. Продольную и поперечную арматуру во всех пересечениях связать вязальной проволокой.
5. Свободные концы основной арматуры у торцов плиты перекрытия должны быть заанкерены "П"-образной скобой (поз. Ск1) при помощи вязальной проволоки (без сварки).
6. Спецификацию см. лист КЖ-7.7

						65П-АИП-2024-1-КЖ
						Строительство многопрофильной больницы на 250 коек с онкологическим центром и поликлиникой на 350 посещений, по адресу: Медеуский район, г. Алматы
Изм.	Кол.уч.	Лист	N док.	Подп.	Дата	
						"Блок 1 Секция 1"
ГКП		Курал М				Стадия: РП; Лист: 7.5; Листов:
Проверил		Кыдырбай А				Схема расположения дополнительного арматуры плиты перекрытия Пм-1 нижней зоны по цифровым осям на отм -0.080
Разраб.		Ауез Б				АстанаИнжПроект
Н.контроль		Ешенкулова				Формат А2

Схема расположения дополнительного арматуры плиты перекрытия Пм-1 верхней зоны по цифровым осям на отм -0.080

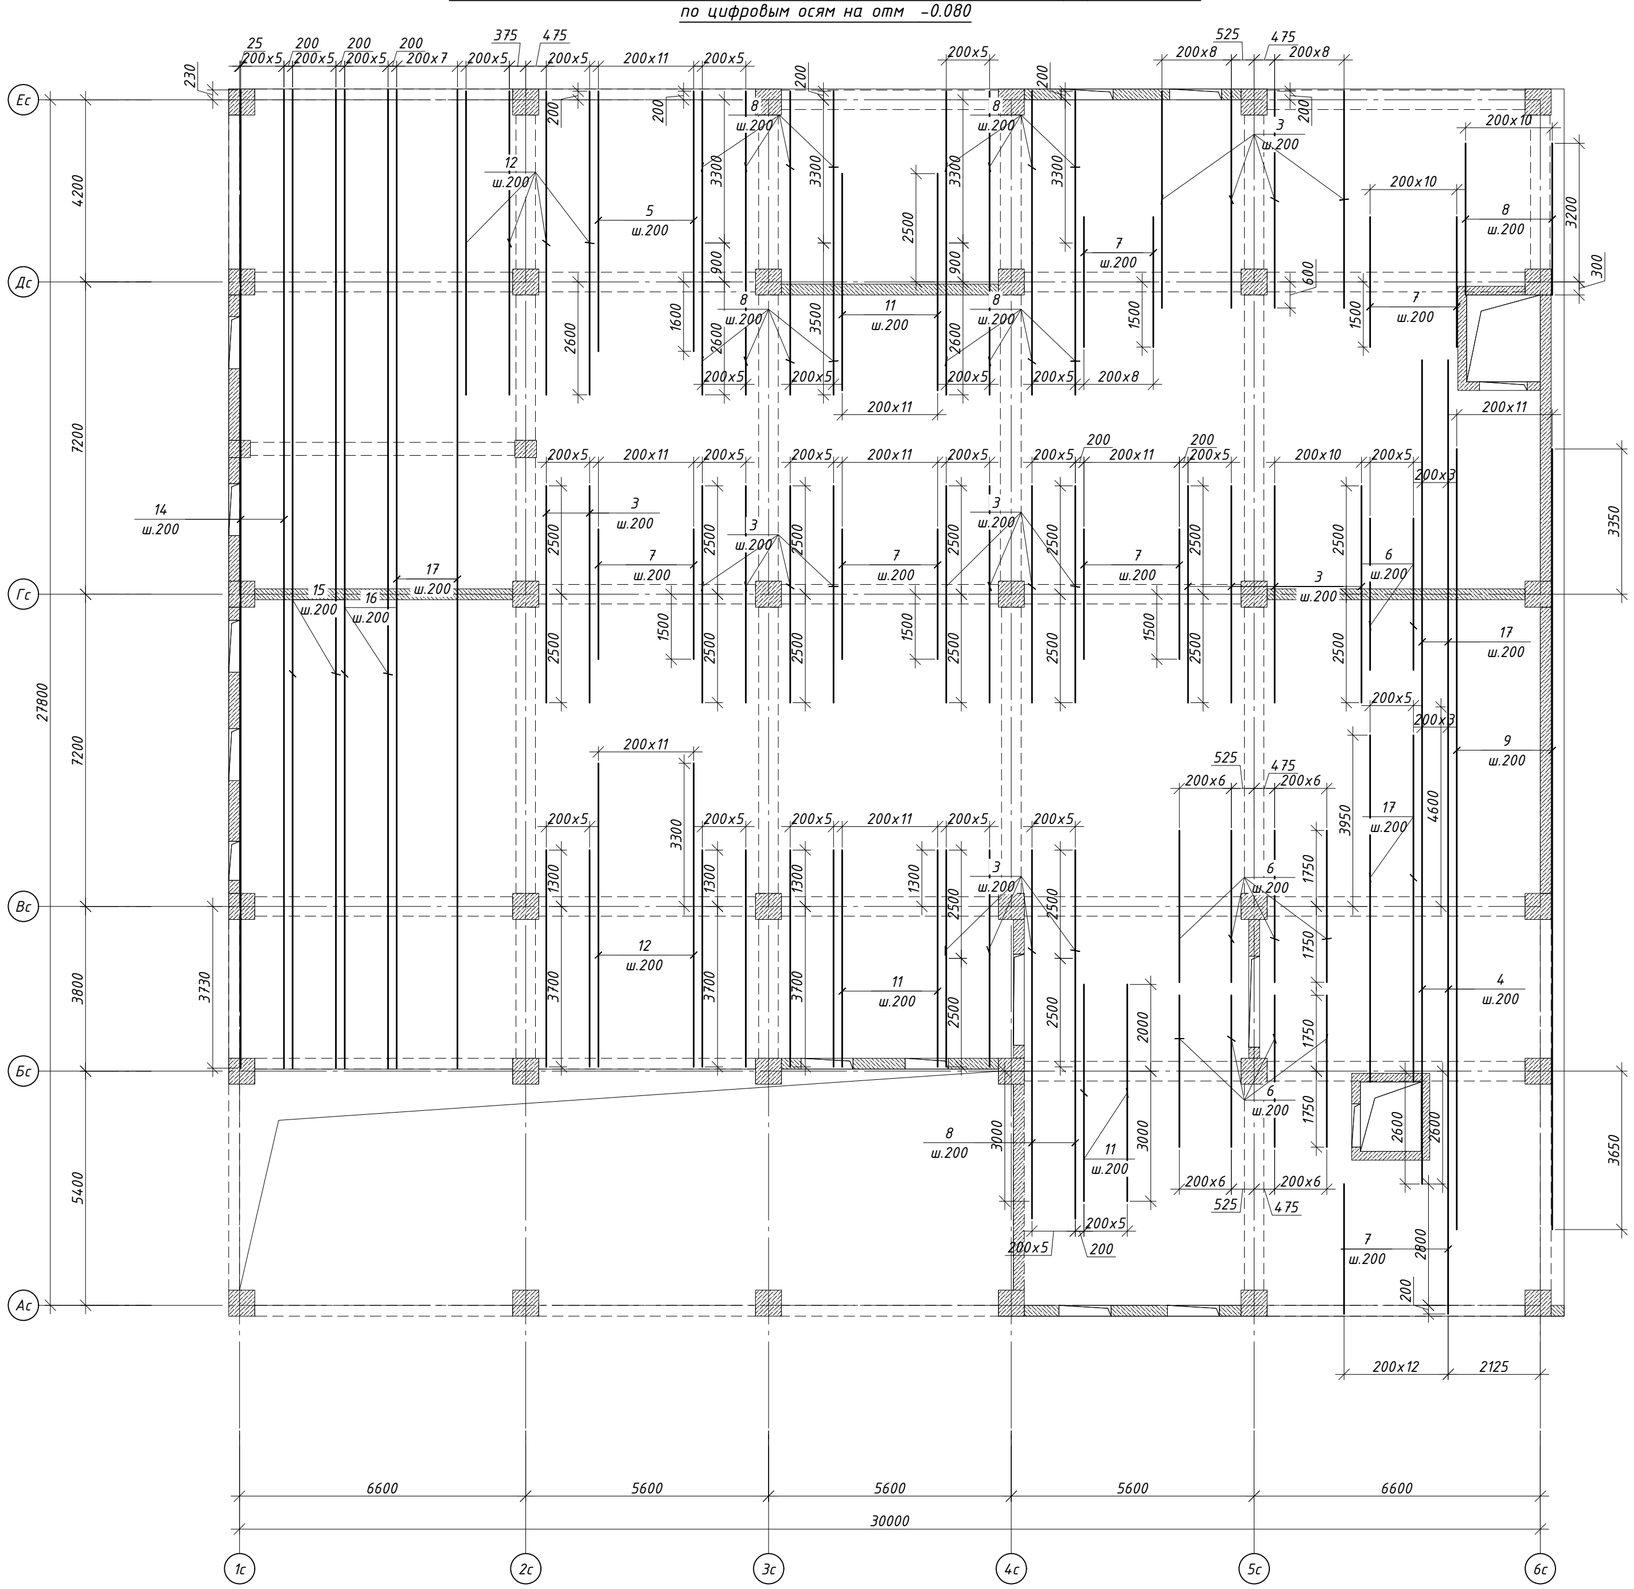


1. Данный лист читать совместно с листами КЖ-2.2 и КЖ-7.1 ... 7.7.
2. Арматура плиты перекрытия стыкуется внахлест.
3. Стыки нижней арматуры выполнять на опоре, стыки верхней арматуры на расстоянии 1/3 - 1/4 пролета от опоры, при этом в одном сечении стыковать не более 50% арматуры.
4. Продольную и поперечную арматуру во всех пересечениях связать вязальной проволокой.
5. Свободные концы основной арматуры у торцов плиты перекрытия должны быть заанкерены "П"-образной скобой (поз. Ск1) при помощи вязальной проволоки (без сварки).
6. Спецификацию см. лист КЖ-7.7

						65П-АИП-2024-1-КЖ	
						Строительство многопрофильной больницы на 250 коек с онкологическим центром и поликлиникой на 350 посещений, по адресу: Медеуский район, г. Алматы	
Изм.	Кол.уч	Лист	N док.	Подп.	Дата		
						"Блок 1 Секция 1"	Стадия: РП; Лист: 7.6; Листов:
ГКП		Курал М				Схема расположения дополнительного арматуры плиты перекрытия Пм-1 верхней зоны по цифровым осям на отм -0.080	АстанаИнжПроект
Проверил		Кыдырбай А					
Разраб.		Ауез Б					
Н.контроль		Ешенкулова					


Формат А2

Детали обрамления отверстий

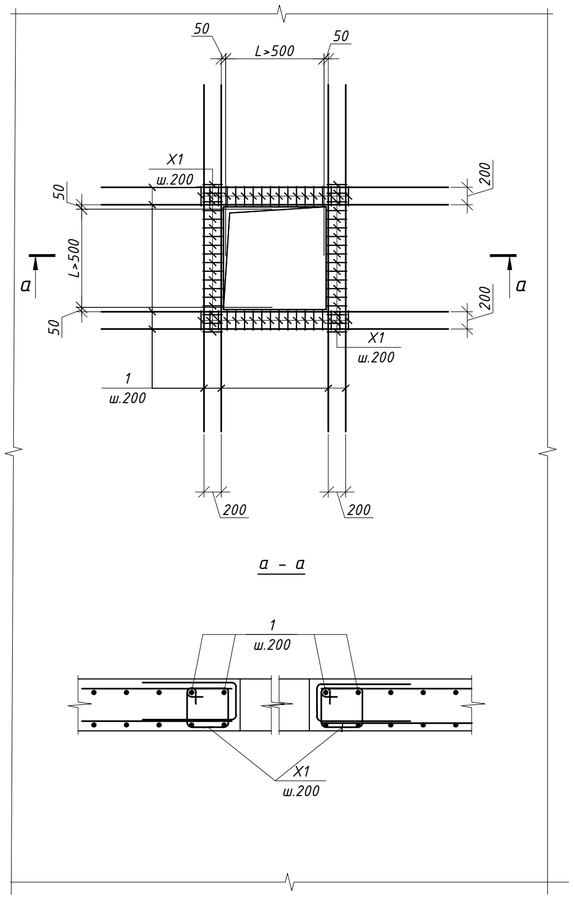

а – а

Разрез 1 – 1 (армирование)

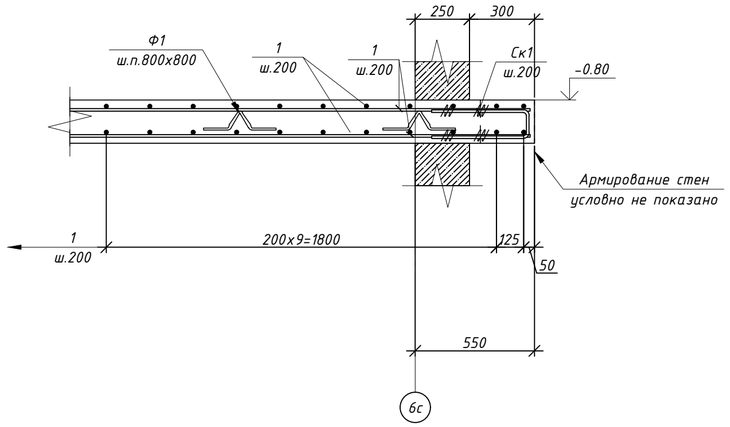

Ведомость деталей

Поз.	Эскиз
Ск1	860; 140; R=2.5ф(<20ф) R=4ф(≥20ф); 860; по н.г. L=1860
Ф1	300; 116; 116; 300; 300; по н.г. L=1132
Х1	320; 220; 320; 220; по в.г. L=1080

Спецификация элементов

Поз.	Обозначение	Наименование	Кол.	Масса ед.кг	Примечание
		Плита Пм-1			33322.08
1	ГОСТ 34028-2016(214-210-0502-0001)	ф 12 А500С L= пог.м.	15659.70	0.89	13902.90
2	ГОСТ 34028-2016(214-210-0502-0007)	ф 25 А500С L= пог.м.	334.95	3.85	1290.68
3	ГОСТ 34028-2016(214-210-0502-0005)	ф 20 А500С L= 5000	182	12.33	2244.20
4	ГОСТ 34028-2016(214-210-0502-0003)	ф 16 А500С L= пог.м.	291.90	1.58	460.72
5	ГОСТ 34028-2016(214-210-0502-0001)	ф 12 А500С L= 6000	143	5.33	761.74
6	ГОСТ 34028-2016(214-210-0502-0002)	ф 14 А500С L= 3500	141	4.23	596.35
7	ГОСТ 34028-2016(214-210-0502-0001)	ф 12 А500С L= 3000	339	2.66	902.91
8	ГОСТ 34028-2016(214-210-0502-0004)	ф 18 А500С L= 3500	233	6.99	1629.03
9	ГОСТ 34028-2016(214-210-0502-0008)	ф 28 А500С L= пог.м.	409.50	4.83	1979.38
10	ГОСТ 34028-2016(214-210-0502-0007)	ф 25 А500С L= 6000	18	23.12	416.16
11	ГОСТ 34028-2016(214-210-0502-0005)	ф 20 А500С L= пог.м.	193.73	2.47	477.75
12	ГОСТ 34028-2016(214-210-0502-0003)	ф 16 А500С L= 7000	34	11.05	375.64
13	ГОСТ 34028-2016(214-210-0502-0006)	ф 22 А500С L= 5000	6	14.92	89.52
14	ГОСТ 34028-2016(214-210-0502-0009)	ф 32 А500С L= пог.м.	284.26	6.31	1794.61
15	ГОСТ 34028-2016(214-210-0502-0004)	ф 18 А500С L= пог.м.	284.26	2.00	567.82
16	ГОСТ 34028-2016(214-210-0502-0002)	ф 14 А500С L= пог.м.	284.26	1.21	343.50
17	ГОСТ 34028-2016(214-210-0502-0001)	ф 12 А500С L= пог.м.	1308.64	0.89	1161.83
18	ГОСТ 34028-2016(214-210-0502-0002)	ф 14 А500С L= 5000	11	6.04	66.46
19	ГОСТ 34028-2016(214-210-0502-0006)	ф 22 А500С L= пог.м.	226.80	2.98	676.78
20	ГОСТ 34028-2016(214-210-0502-0005)	ф 20 А500С L= 3000	6	7.40	44.39
Ск1	ГОСТ 34028-2016(214-210-0502-0001)	ф 12 А500С L= 1860	704	1.65	1162.54
Ф1	ГОСТ 34028-2016(214-210-0502-0001)	ф 12 А500С L= 1132	2290	1.01	2301.46
ВП1	ГОСТ 34028-2016(214-210-0502-0003)	ф 16 А500С L= 3650	8	5.76	46.09
ВП2	ГОСТ 34028-2016(214-210-0502-0003)	ф 16 А500С L= 1940	8	3.06	24.50
Х1	ГОСТ 34028-2016(214-210-0101-0002)	ф 8 А 240 L= 1080	12	0.43	5.11
		Материалы:			
	(212-101-0901)	Класс бетона С 20/25 (В25), м^3			168.34

Позиции со "*" см. "Ведомость деталей" см. на данном листе.


Ведомость расхода стали, кг

Марка элемента	Изделия арматурные													Всего
	Арматура класса													
	А240			А500С										
	ГОСТ 34028-2016(214-210-0101)			ГОСТ 34028-2016(214-210-0502)										
	Ф6	Ф8	Итого	Ф10	Ф12	Ф14	Ф16	Ф18	Ф20	Ф22	Ф25	Ф28	Ф32	Итого
Плита -0.080	---	5.11	5.11	---	20193.38	1006.31	906.94	2196.85	2766.34	766.30	1706.85	1979.38	1794.61	33316.97	33322.08


1. Данный лист читать совместно с листами КЖ-2.2 и КЖ-7.1 ... 7.6.
2. Арматура плиты перекрытия стыкуется внахлест.
3. Стыки нижней арматуры выполнять на опоре, стыки верхней арматуры на расстоянии 1/3 - 1/4 пролета от опоры, при этом в одном сечении стыковать не более 50% арматуры.
4. Продольную и поперечную арматуру во всех пересечениях связать вязальной проволокой.
5. Свободные концы основной арматуры у торцов плиты перекрытия должны быть заанкерены "П"-образной скобой (поз. Ск1) при помощи вязальной проволоки (без сварки).
6. Спецификацию см. лист КЖ-7.7

Изм.	Кол.уч.	Лист	N док.	Подп.	Дата	65П-АИП-2024-1-КЖ			
						Строительство многопрофильной больницы на 250 коек с онкологическим центром и поликлиникой на 350 посещений, по адресу: Медеуский район, г. Алматы			
ГКП		Курал М				"Блок 1 Секция 1"	Стадия	Лист	Листов
Проверил		Кыдырбай А					РП	7.7	
Разраб.		Ауез Б				Спецификация плиты перекрытия Пм-1 на отм -0.080	АстанаИнжПроект		
Н.контроль		Ешенкулова					Формат	А2	


Опалубочный чертеж плиты перекрытия Пм-2 на отм. +3.820

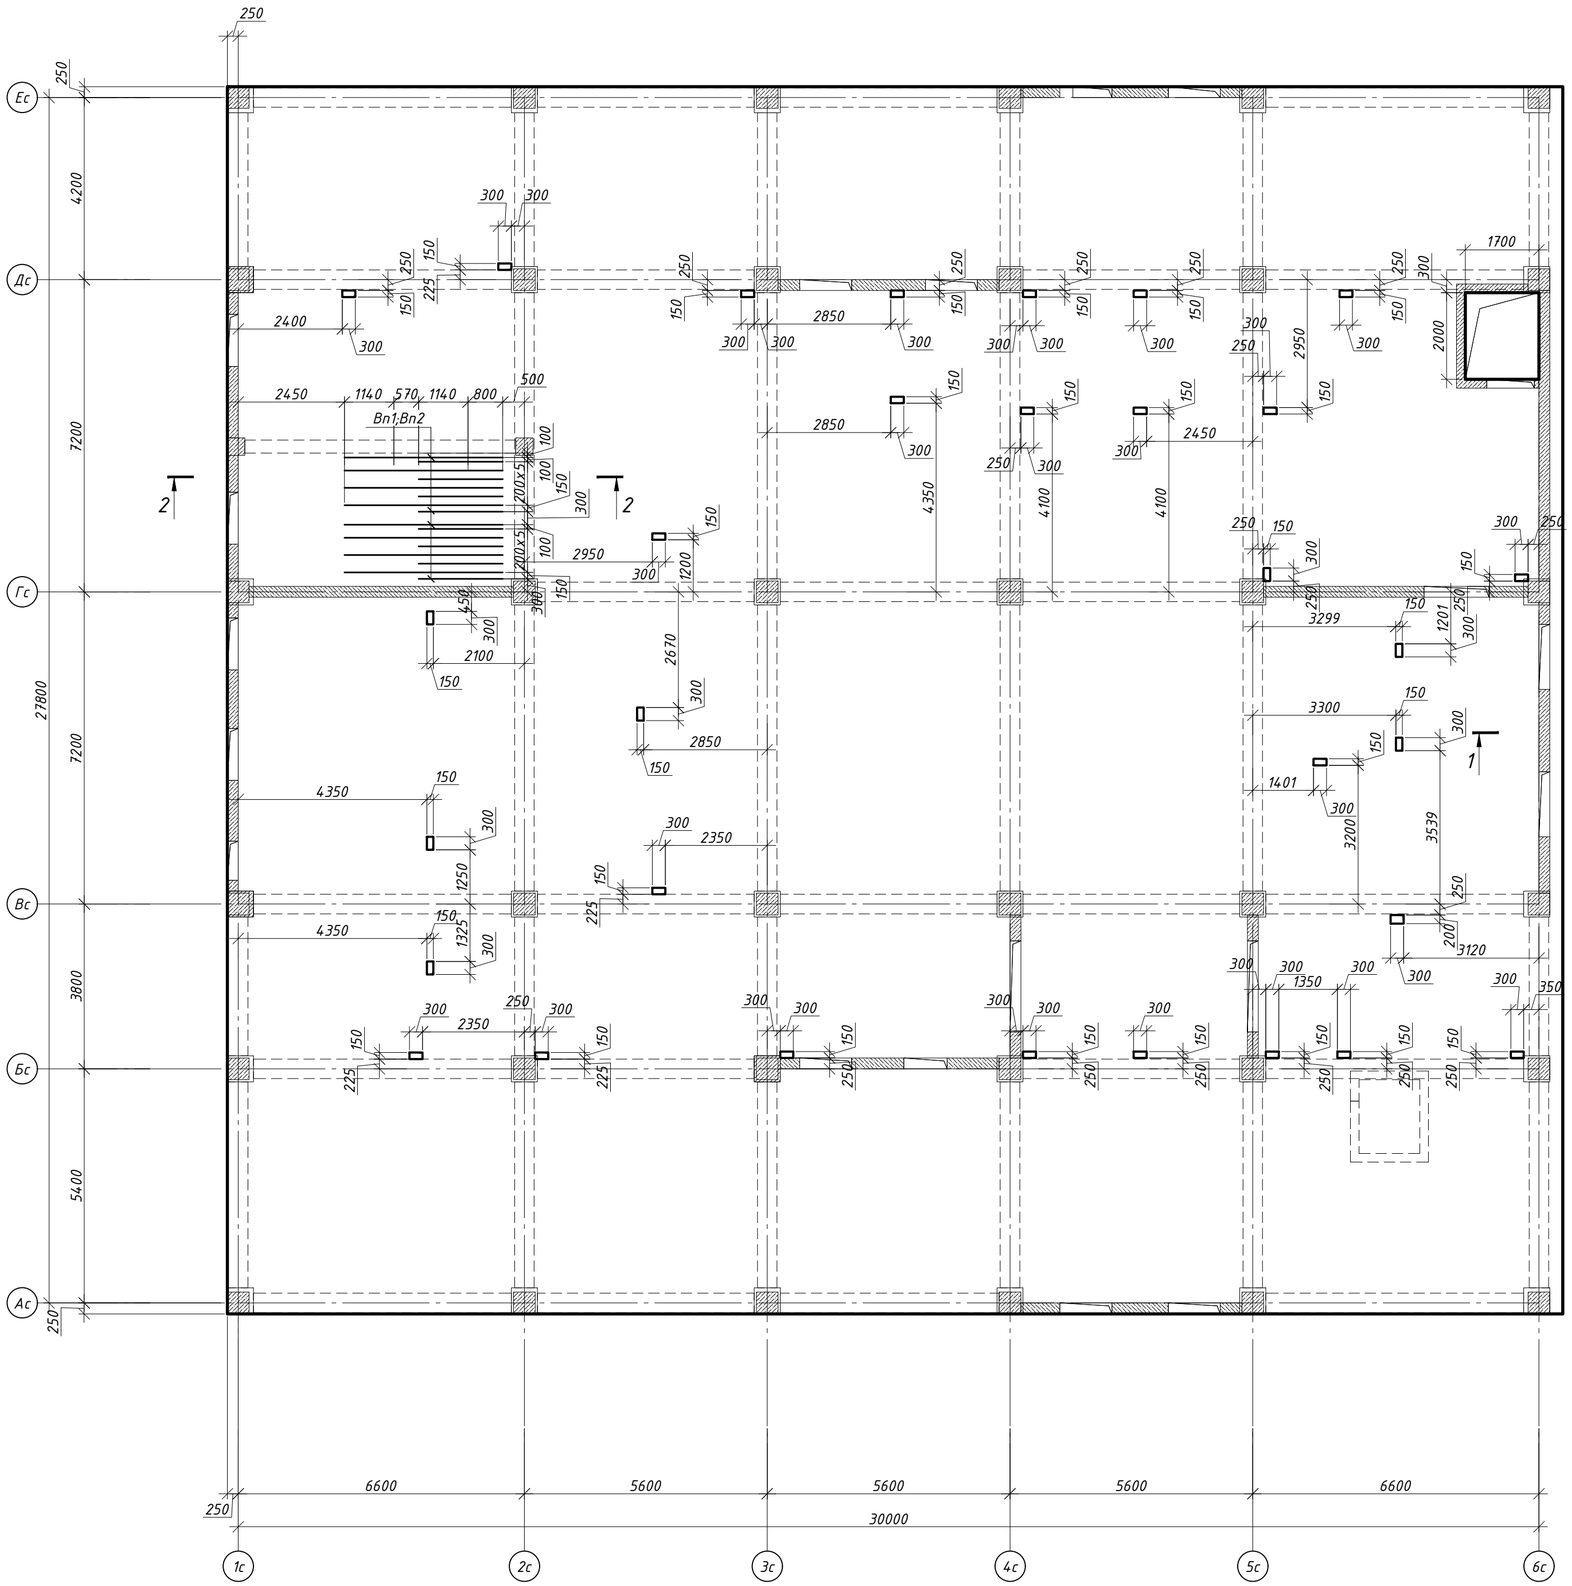

Разрез 1 - 1 (Опалубка)
М 1:50

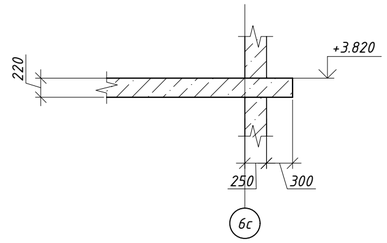

Разрез 2 - 2

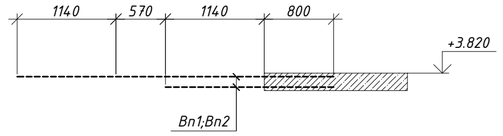


1. Данный лист читать совместно с листами КЖ-2.3 и КЖ-7.9 ... 7.14.
2. Арматура плиты перекрытия стыкуется внахлест.
3. Стыки нижней арматуры выполнять на опоре, стыки верхней арматуры на расстоянии 1/3 - 1/4 пролета от опоры, при этом в одном сечении стыковать не более 50% арматуры.
4. Продольную и поперечную арматуру во всех пересечениях связать вязальной проволокой.
5. Свободные концы основной арматуры у торцов плиты перекрытия должны быть заанкерены "П"-образной скобой (поз. Ск1) при помощи вязальной проволоки (без сварки).
6. Спецификацию см. лист КЖ-7.14

						65П-АИП-2024-1-КЖ
						Строительство многопрофильной больницы на 250 коек с онкологическим центром и поликлиникой на 350 посещений, по адресу: Медеуский район, г. Алматы
Изм.	Кол.уч	Лист	N док.	Подп.	Дата	
ГКП		Курал М				"Блок 1 Секция 1"
Проверил		Кыдырбай А				Стадия: РП; Лист: 7.8; Листов:
Разраб.		Ауез Б				Опалубочный чертеж плиты перекрытия Пм-2 на отм.+3.820
Н.контроль		Ешенкулова				АстанаИнжПроект

Формат А2


Схема расположения основных арматуры плиты перекрытия Пм-2 на отм +3.820

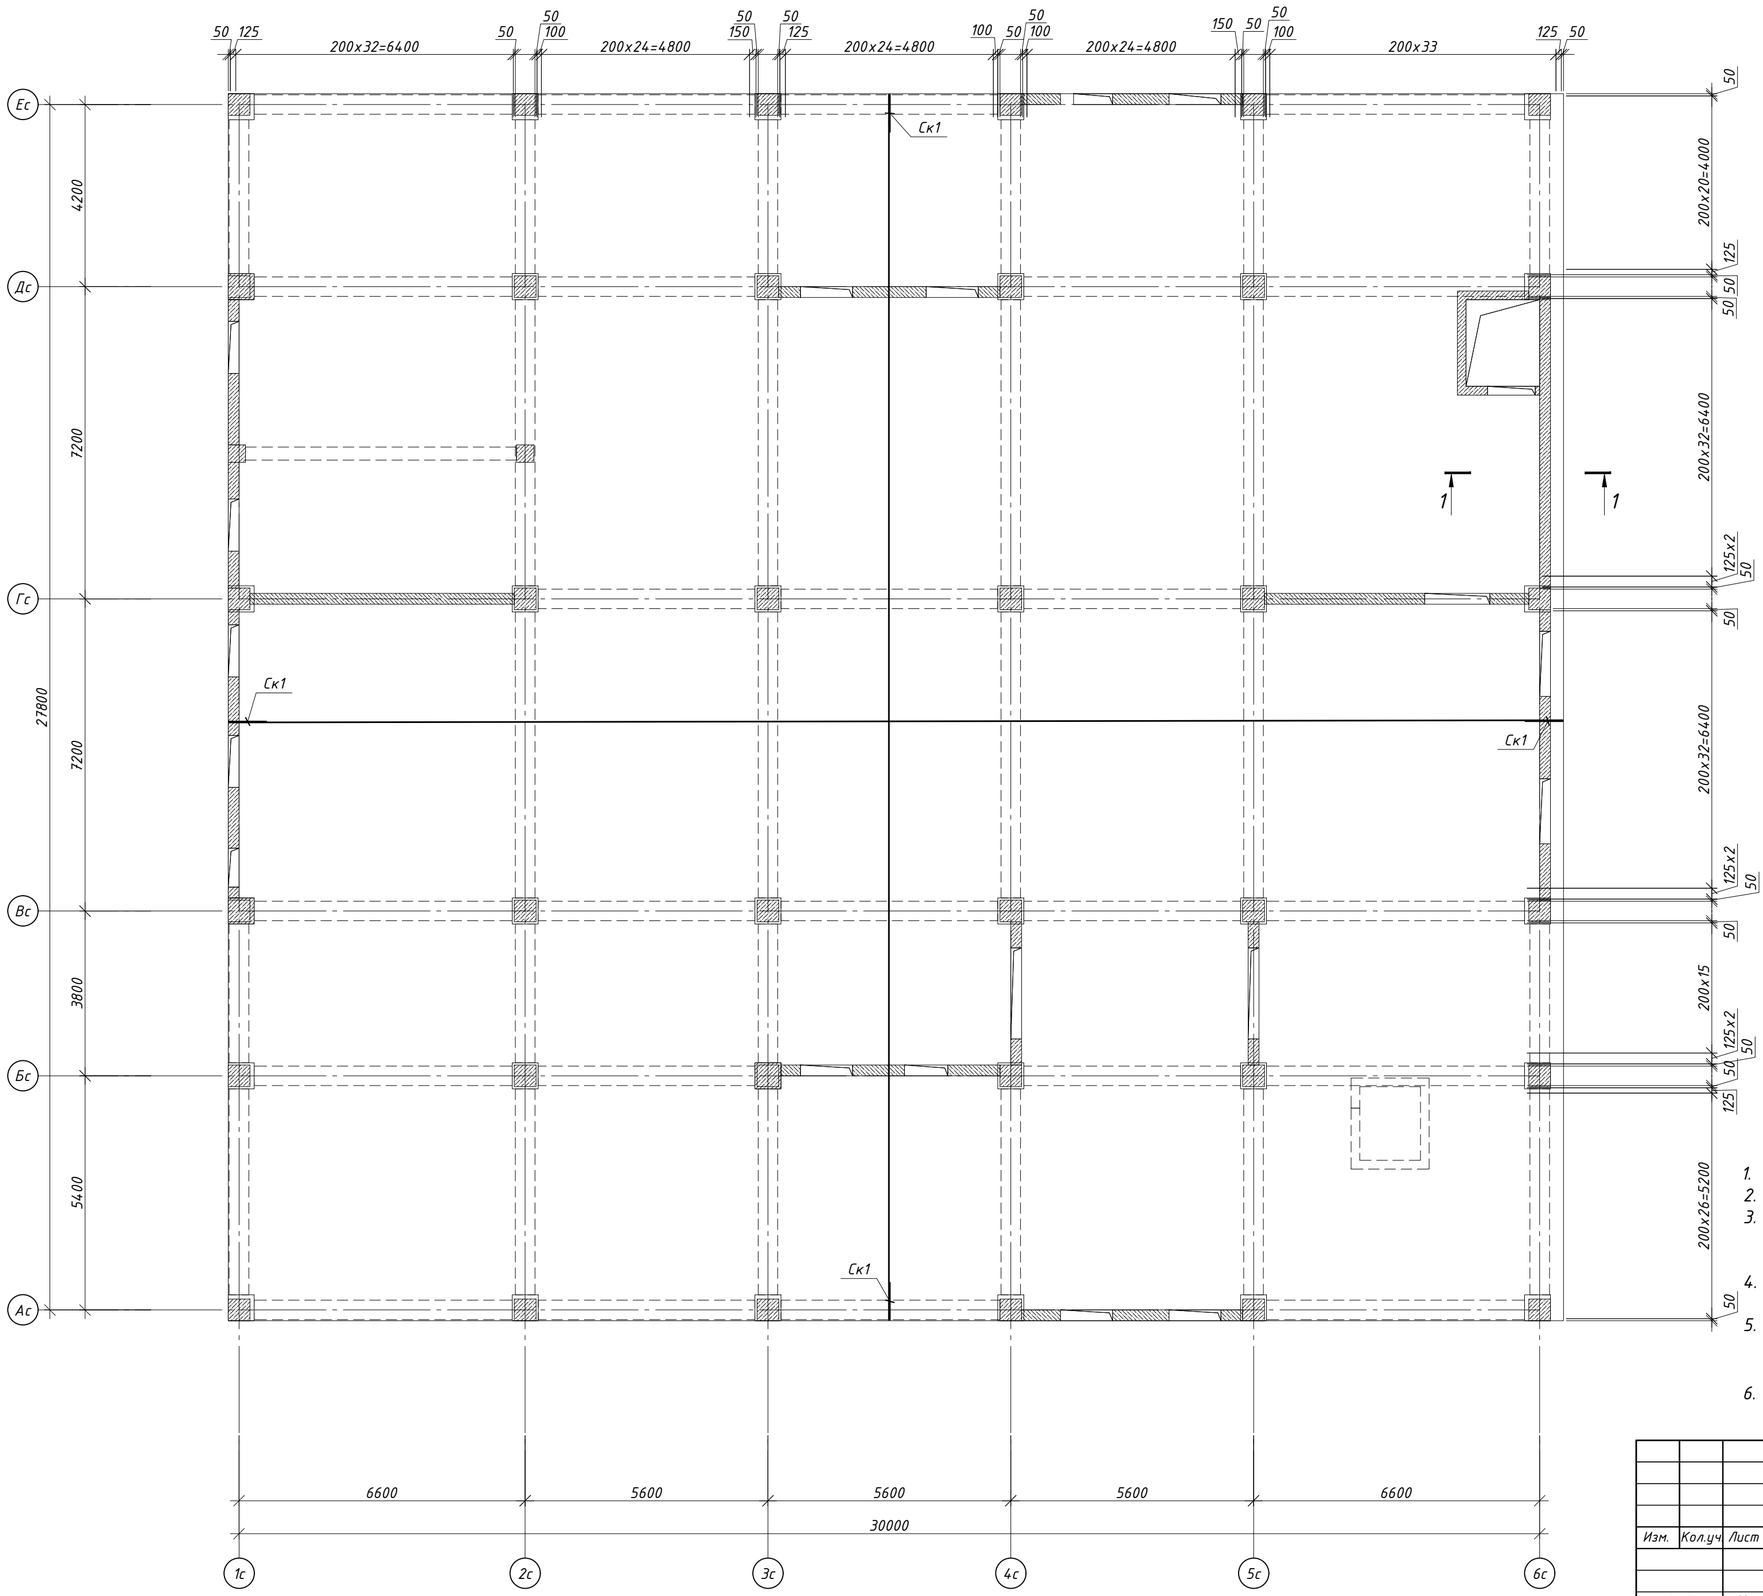

1. Данный лист читать совместно с листами КЖ-2.3 и КЖ-7.8 ... 7.14.
2. Арматура плиты перекрытия стыкуется внахлест.
3. Стыки нижней арматуры выполнять на опоре, стыки верхней арматуры на расстоянии 1/3 - 1/4 пролета от опоры, при этом в одном сечении стыковать не более 50% арматуры.
4. Продольную и поперечную арматуру во всех пересечениях связать вязальной проволокой.
5. Свободные концы основной арматуры у торцов плиты перекрытия должны быть заанкерены "П"-образной скобой (поз. Ск1) при помощи вязальной проволоки (без сварки).
6. Спецификацию см. лист КЖ-7.14

						65П-АИП-2024-1-КЖ
						Строительство многопрофильной больницы на 250 коек с онкологическим центром и поликлиникой на 350 посещений, по адресу: Медеуский район, г. Алматы
Изм.	Кол.уч	Лист	N док.	Подп.	Дата	
						"Блок 1 Секция 1"
ГКП		Курал М				Стадия: РП; Лист: 7.9; Листов:
Проверил		Кыдырбай А				Схема расположения основных арматуры плиты перекрытия Пм-2 на отм +3.820
Разраб.		Ауез Б				АстанаИнжПроект
Н.контроль		Ешенкулова				Формат А2

Схема расположения дополнительного арматуры плиты перекрытия Пм-2 нижней зоны по буквенным осям на отм +3.820

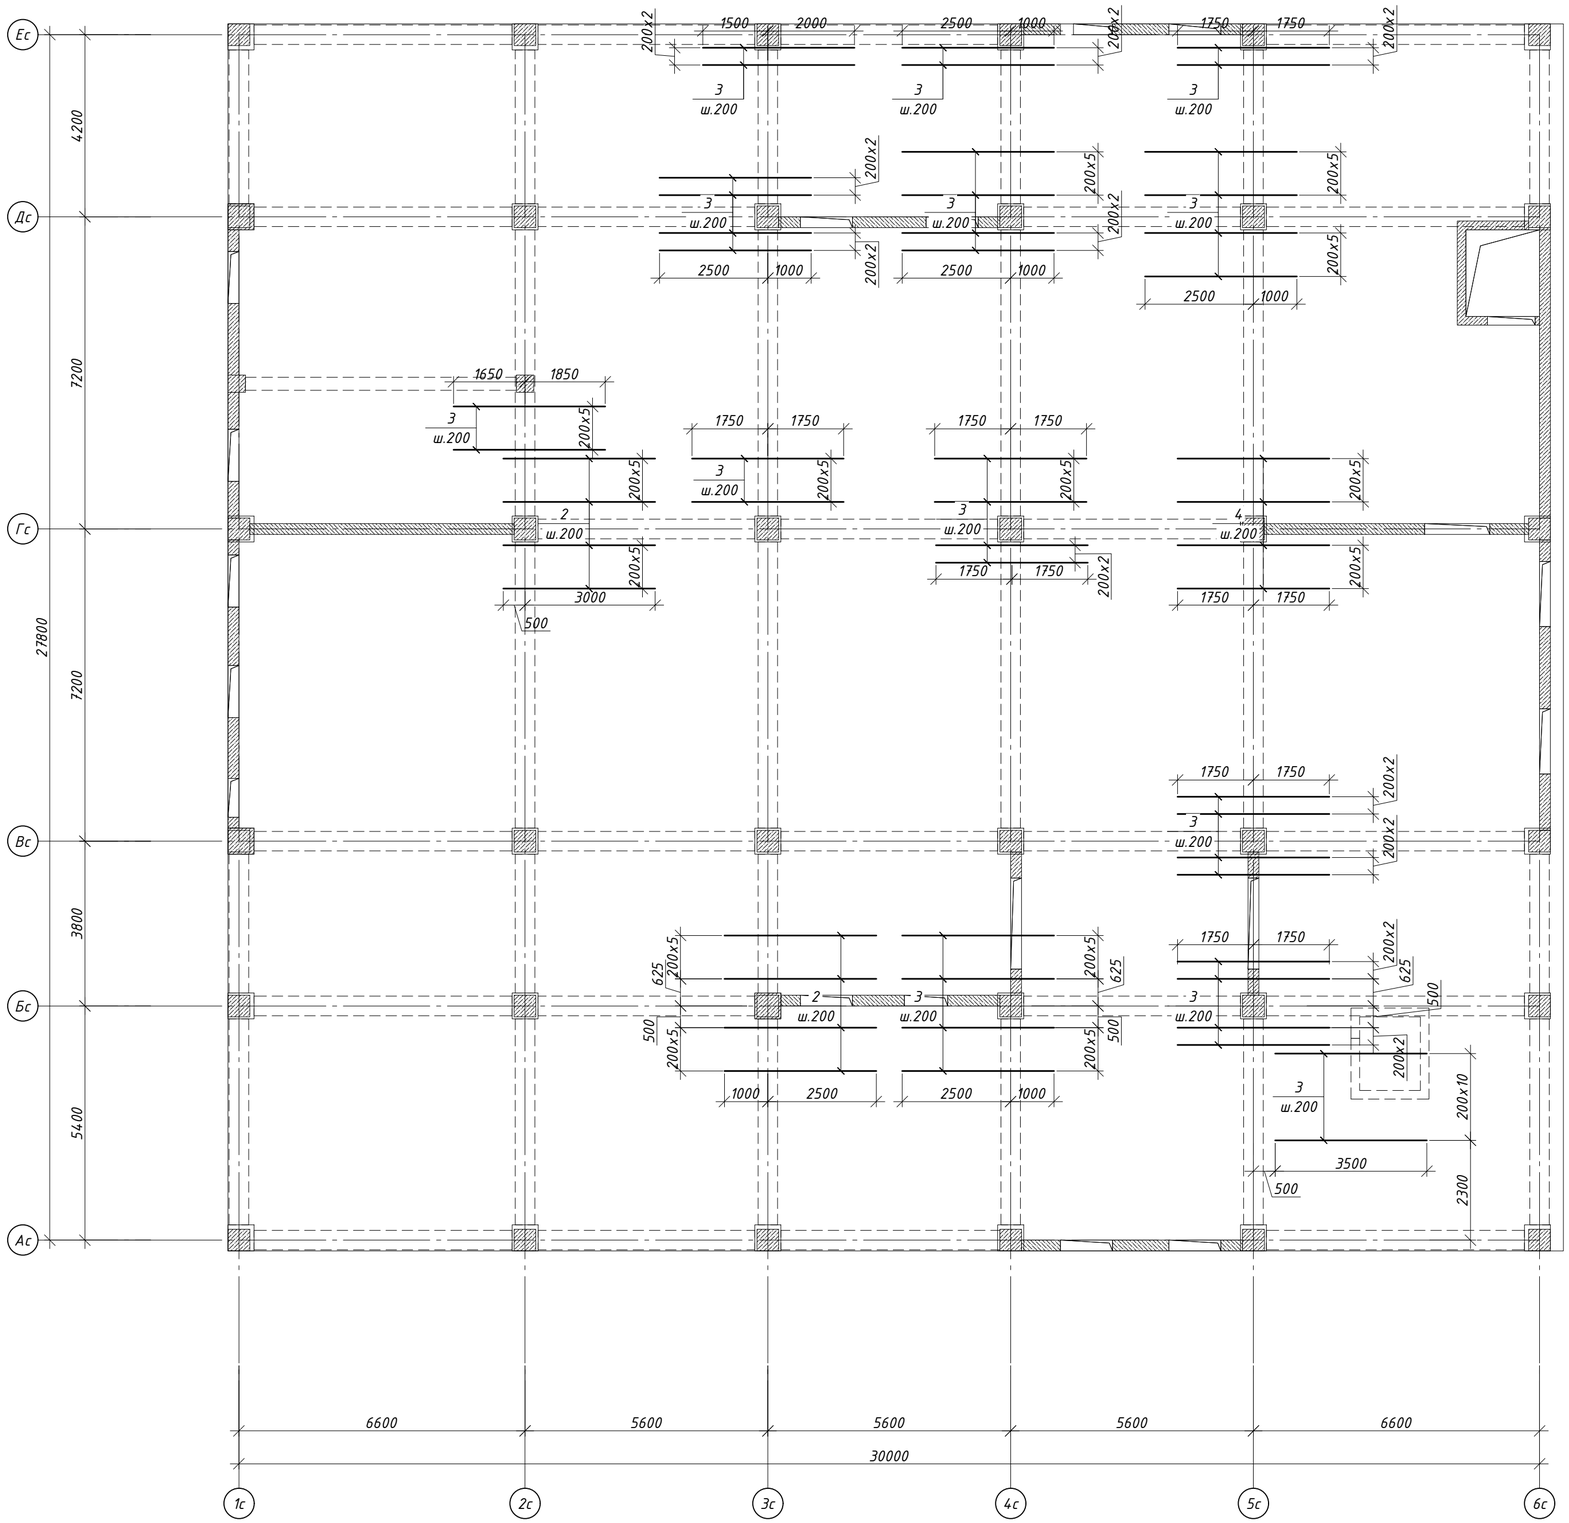


1. Данный лист читать совместно с листами КЖ-2.3 и КЖ-7.8 ... 7.14.
2. Арматура плиты перекрытия стыкуется внахлест.
3. Стыки нижней арматуры выполнять на опоре, стыки верхней арматуры на расстоянии 1/3 - 1/4 пролета от опоры, при этом в одном сечении стыковать не более 50% арматуры.
4. Продольную и поперечную арматуру во всех пересечениях связать вязальной проволокой.
5. Свободные концы основной арматуры у торцов плиты перекрытия должны быть заанкерены "П"-образной скобой (поз. Ск1) при помощи вязальной проволоки (без сварки).
6. Спецификацию см. лист КЖ-7.14

						65П-АИП-2024-1-КЖ
						Строительство многопрофильной больницы на 250 коек с онкологическим центром и поликлиникой на 350 посещений, по адресу: Медеуский район, г. Алматы
Изм.	Кол.уч	Лист	N док.	Подп.	Дата	
						"Блок 1 Секция 1"
ГКП		Курал М				Стадия: РП; Лист: 7.10; Листов:
Проверил		Кыдырбай А				Схема расположения дополнительного арматуры плиты перекрытия Пм-2 нижней зоны по буквенным осям на отм +3.820
Разраб.		Ауез Б				АстанаИнжПроект
Н.контроль		Ешенкулова				

Формат А2

Схема расположения дополнительного арматуры плиты перекрытия Пм-2 верхней зоны по буквенным осям на отм -3.820

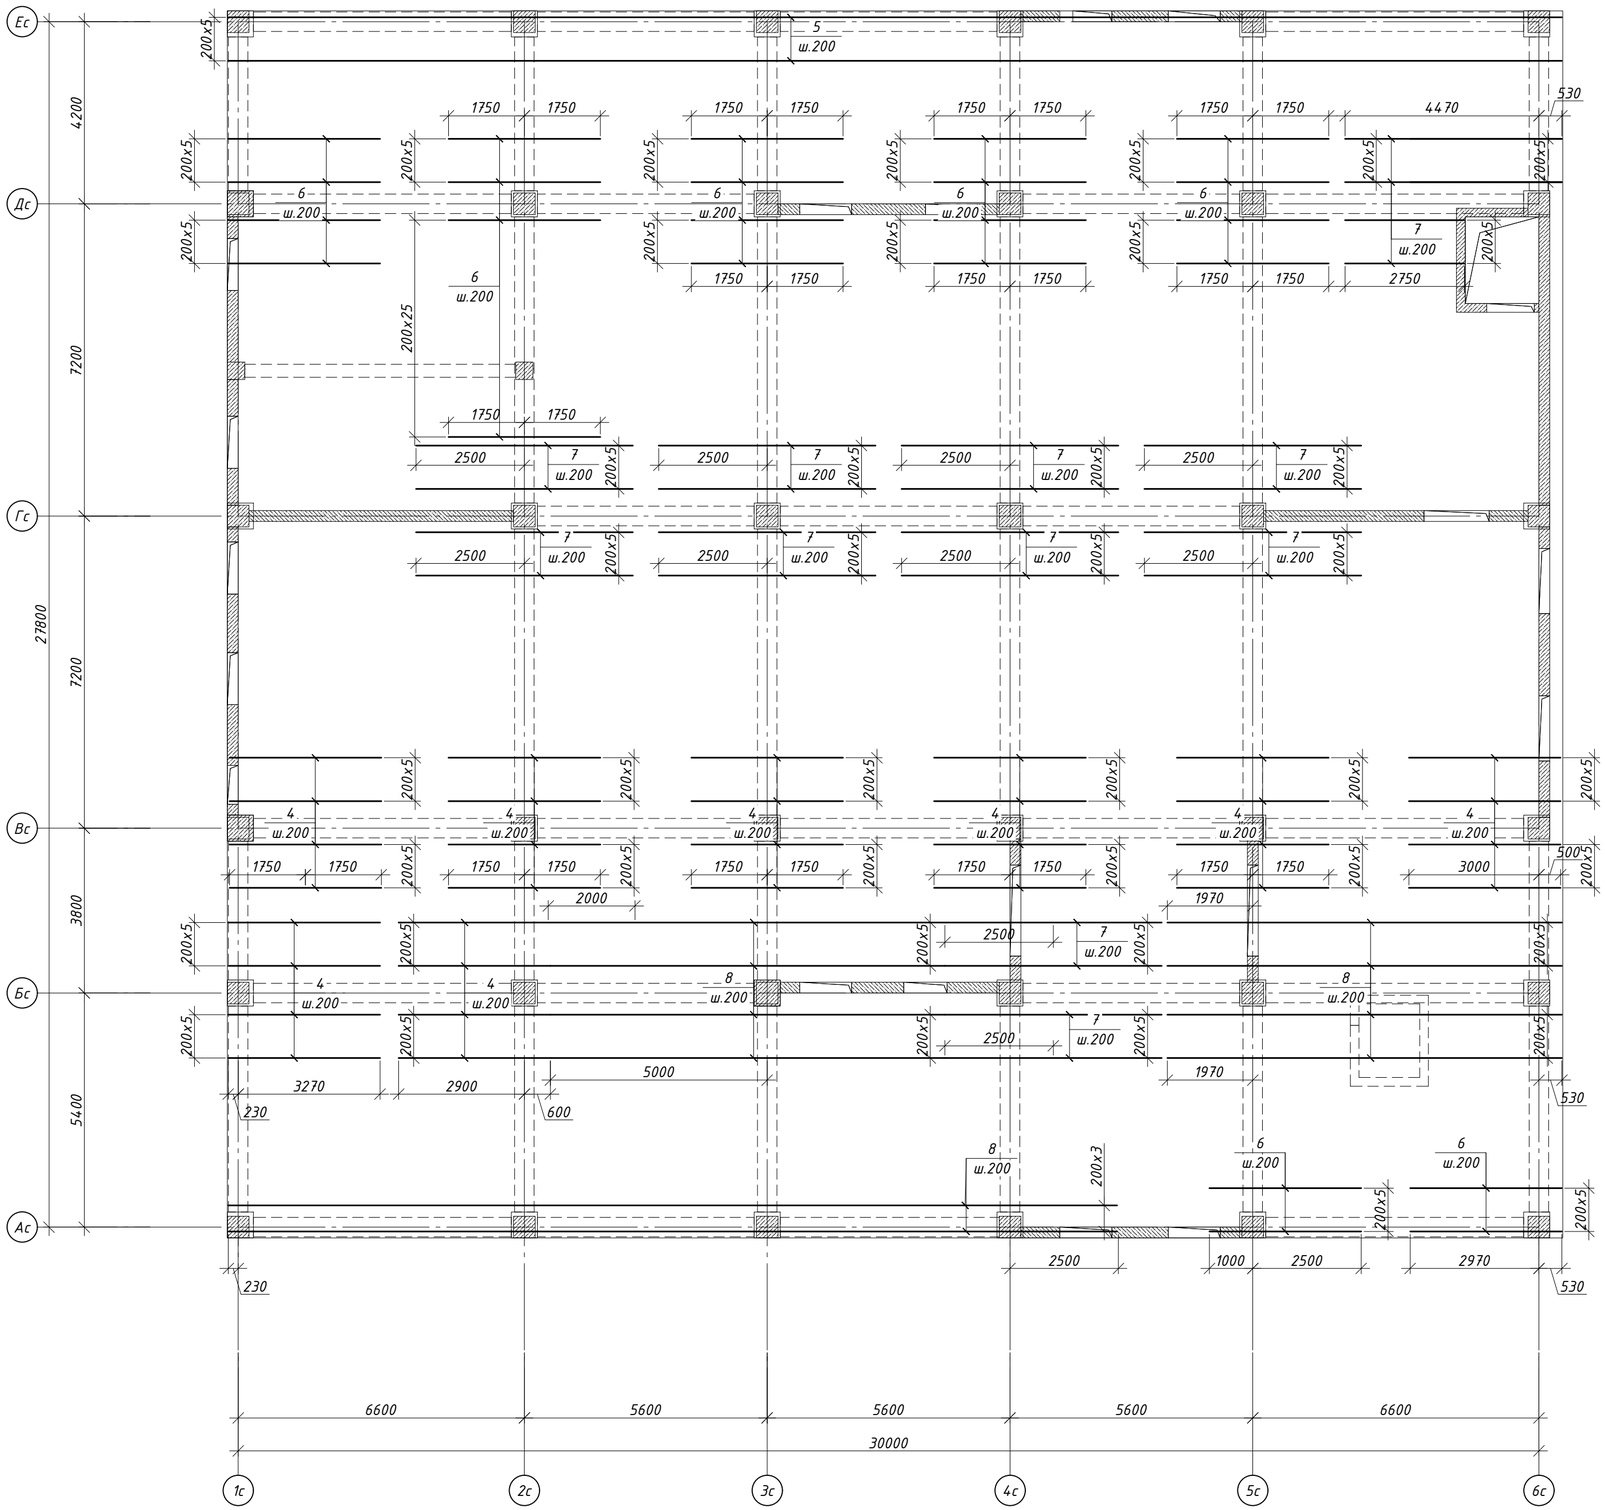


1. Данный лист читать совместно с листами КЖ-2.3 и КЖ-7.8 ... 7.14.
2. Арматура плиты перекрытия стыкуется внахлест.
3. Стыки нижней арматуры выполнять на опоре, стыки верхней арматуры на расстоянии 1/3 - 1/4 пролета от опоры, при этом в одном сечении стыковать не более 50% арматуры.
4. Продольную и поперечную арматуру во всех пересечениях связать вязальной проволокой.
5. Свободные концы основной арматуры у торцов плиты перекрытия должны быть заанкерены "П"-образной скобой (поз. Ск1) при помощи вязальной проволоки (без сварки).
6. Спецификацию см. лист КЖ-7.14

						65П-АИП-2024-1-КЖ
						Строительство многопрофильной больницы на 250 коек с онкологическим центром и поликлиникой на 350 посещений, по адресу: Медеуский район, г. Алматы
Изм.	Кол.уч	Лист	N док.	Подп.	Дата	
						"Блок 1 Секция 1"
ГКП		Курал М				Стадия: РП; Лист: 7.11; Листов:
Проверил		Кыдырбай А				Схема расположения дополнительного арматуры плиты перекрытия Пм-2 верхней зоны по буквенным осям на отм +3.820
Разраб.		Ауез Б				АстанаИнжПроект
Н.контроль		Ешенкулова				

Формат А2

Схема расположения дополнительного арматуры плиты перекрытия Пм-2 нижней зоны по цифровым осям на отм +3.820

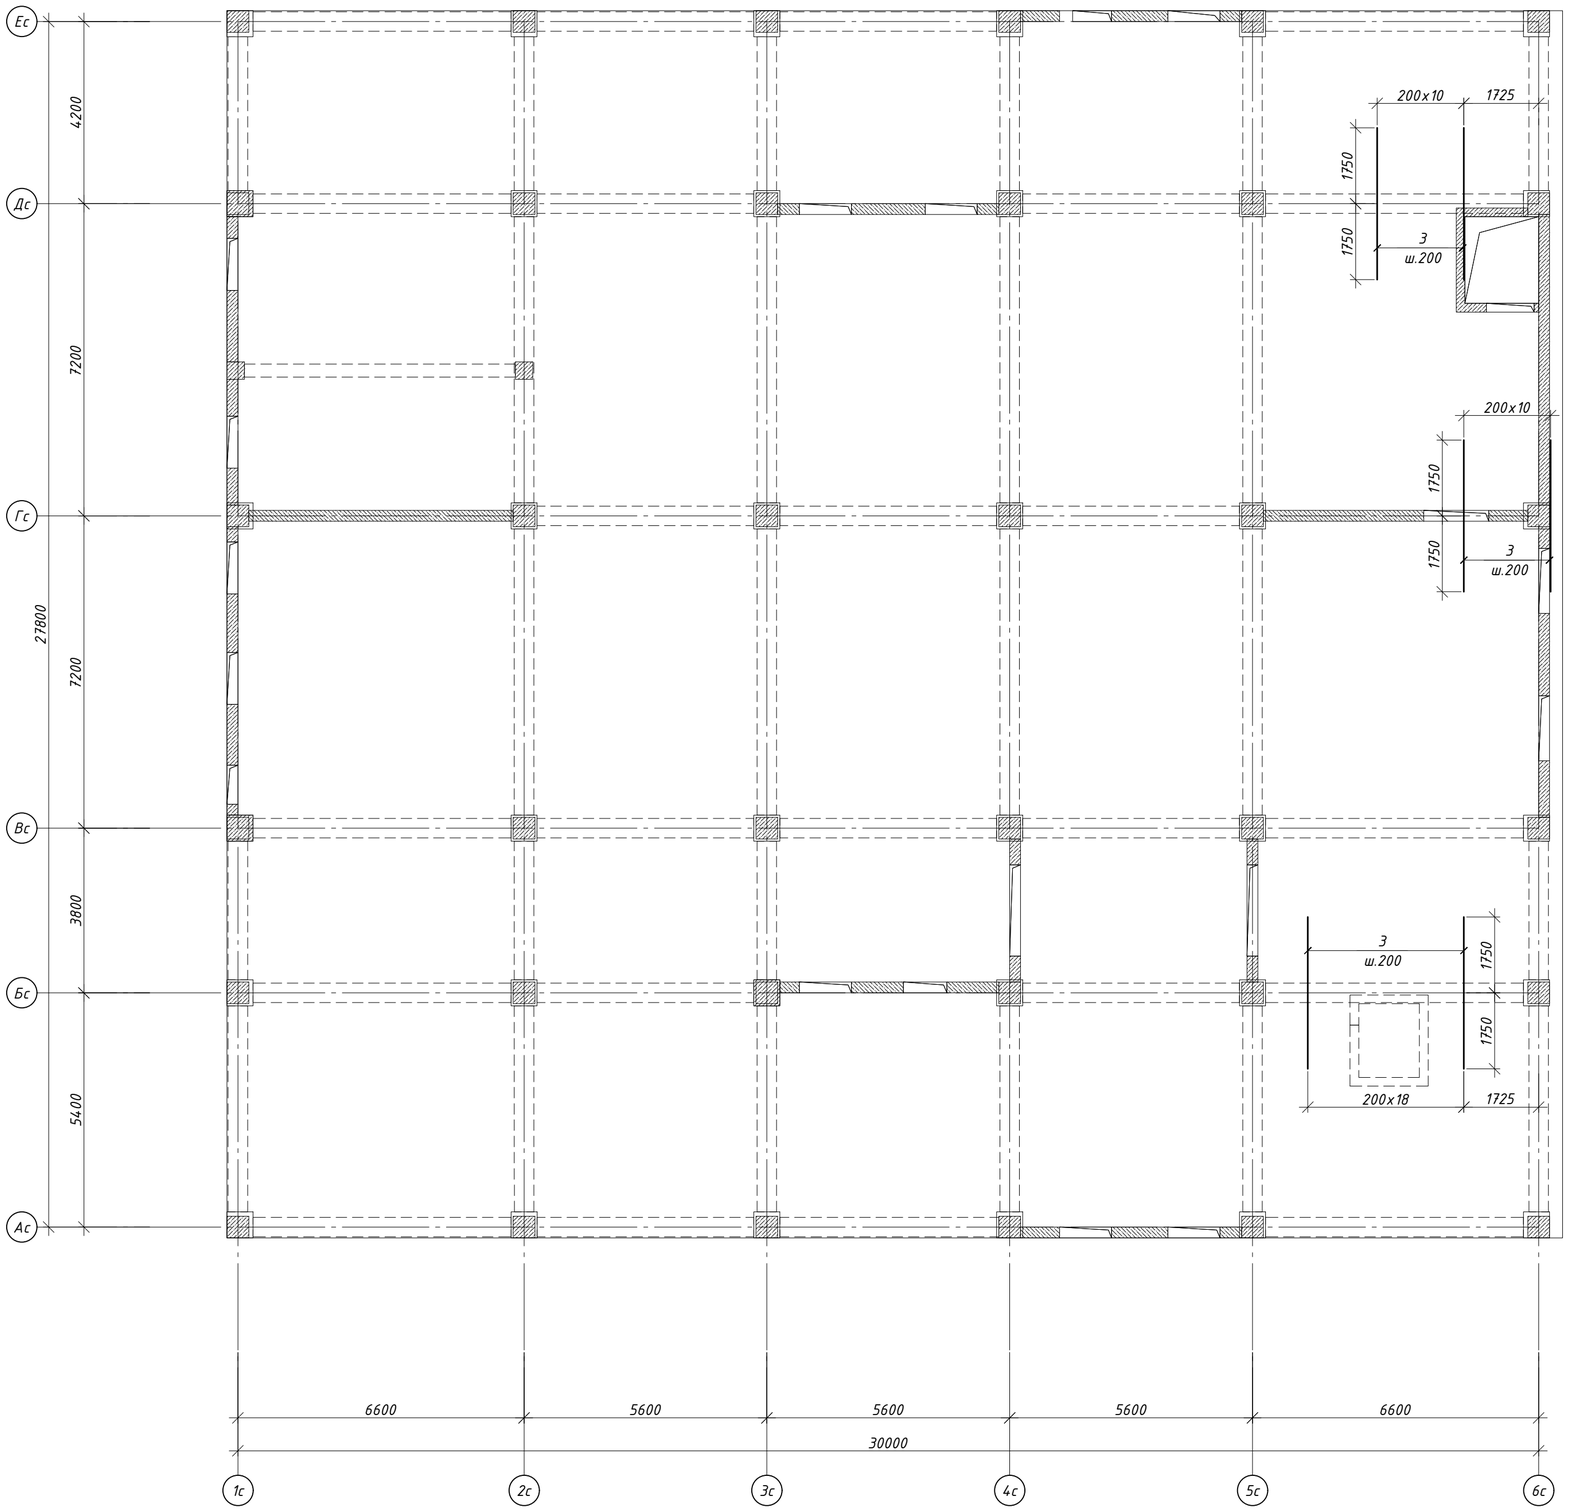


1. Данный лист читать совместно с листами КЖ-2.3 и КЖ-7.8 ... 7.14.
2. Арматура плиты перекрытия стыкуется внахлест.
3. Стыки нижней арматуры выполнять на опоре, стыки верхней арматуры на расстоянии 1/3 - 1/4 пролета от опоры, при этом в одном сечении стыковать не более 50% арматуры.
4. Продольную и поперечную арматуру во всех пересечениях связать вязальной проволокой.
5. Свободные концы основной арматуры у торцов плиты перекрытия должны быть заанкерены "П"-образной скобой (поз. Ск1) при помощи вязальной проволоки (без сварки).
6. Спецификацию см. лист КЖ-7.14

						65П-АИП-2024-1-КЖ	
						Строительство многопрофильной больницы на 250 коек с онкологическим центром и поликлиникой на 350 посещений, по адресу: Медеуский район, г. Алматы	
Изм.	Кол.уч	Лист	N док.	Подп.	Дата		
						"Блок 1 Секция 1"	Стадия: РП; Лист: 7.12; Листов:
ГКП		Курал М				Схема расположения дополнительного арматуры плиты перекрытия Пм-2 нижней зоны по цифровым осям на отм +3.820	АстанаИнжПроект
Проверил		Кыдырбай А					
Разраб.		Ауез Б					
Н.контроль		Ешенкулова					

Формат А2

Схема расположения дополнительного арматуры плиты перекрытия Пм-2 верхней зоны по цифровым осям на отм +3.820

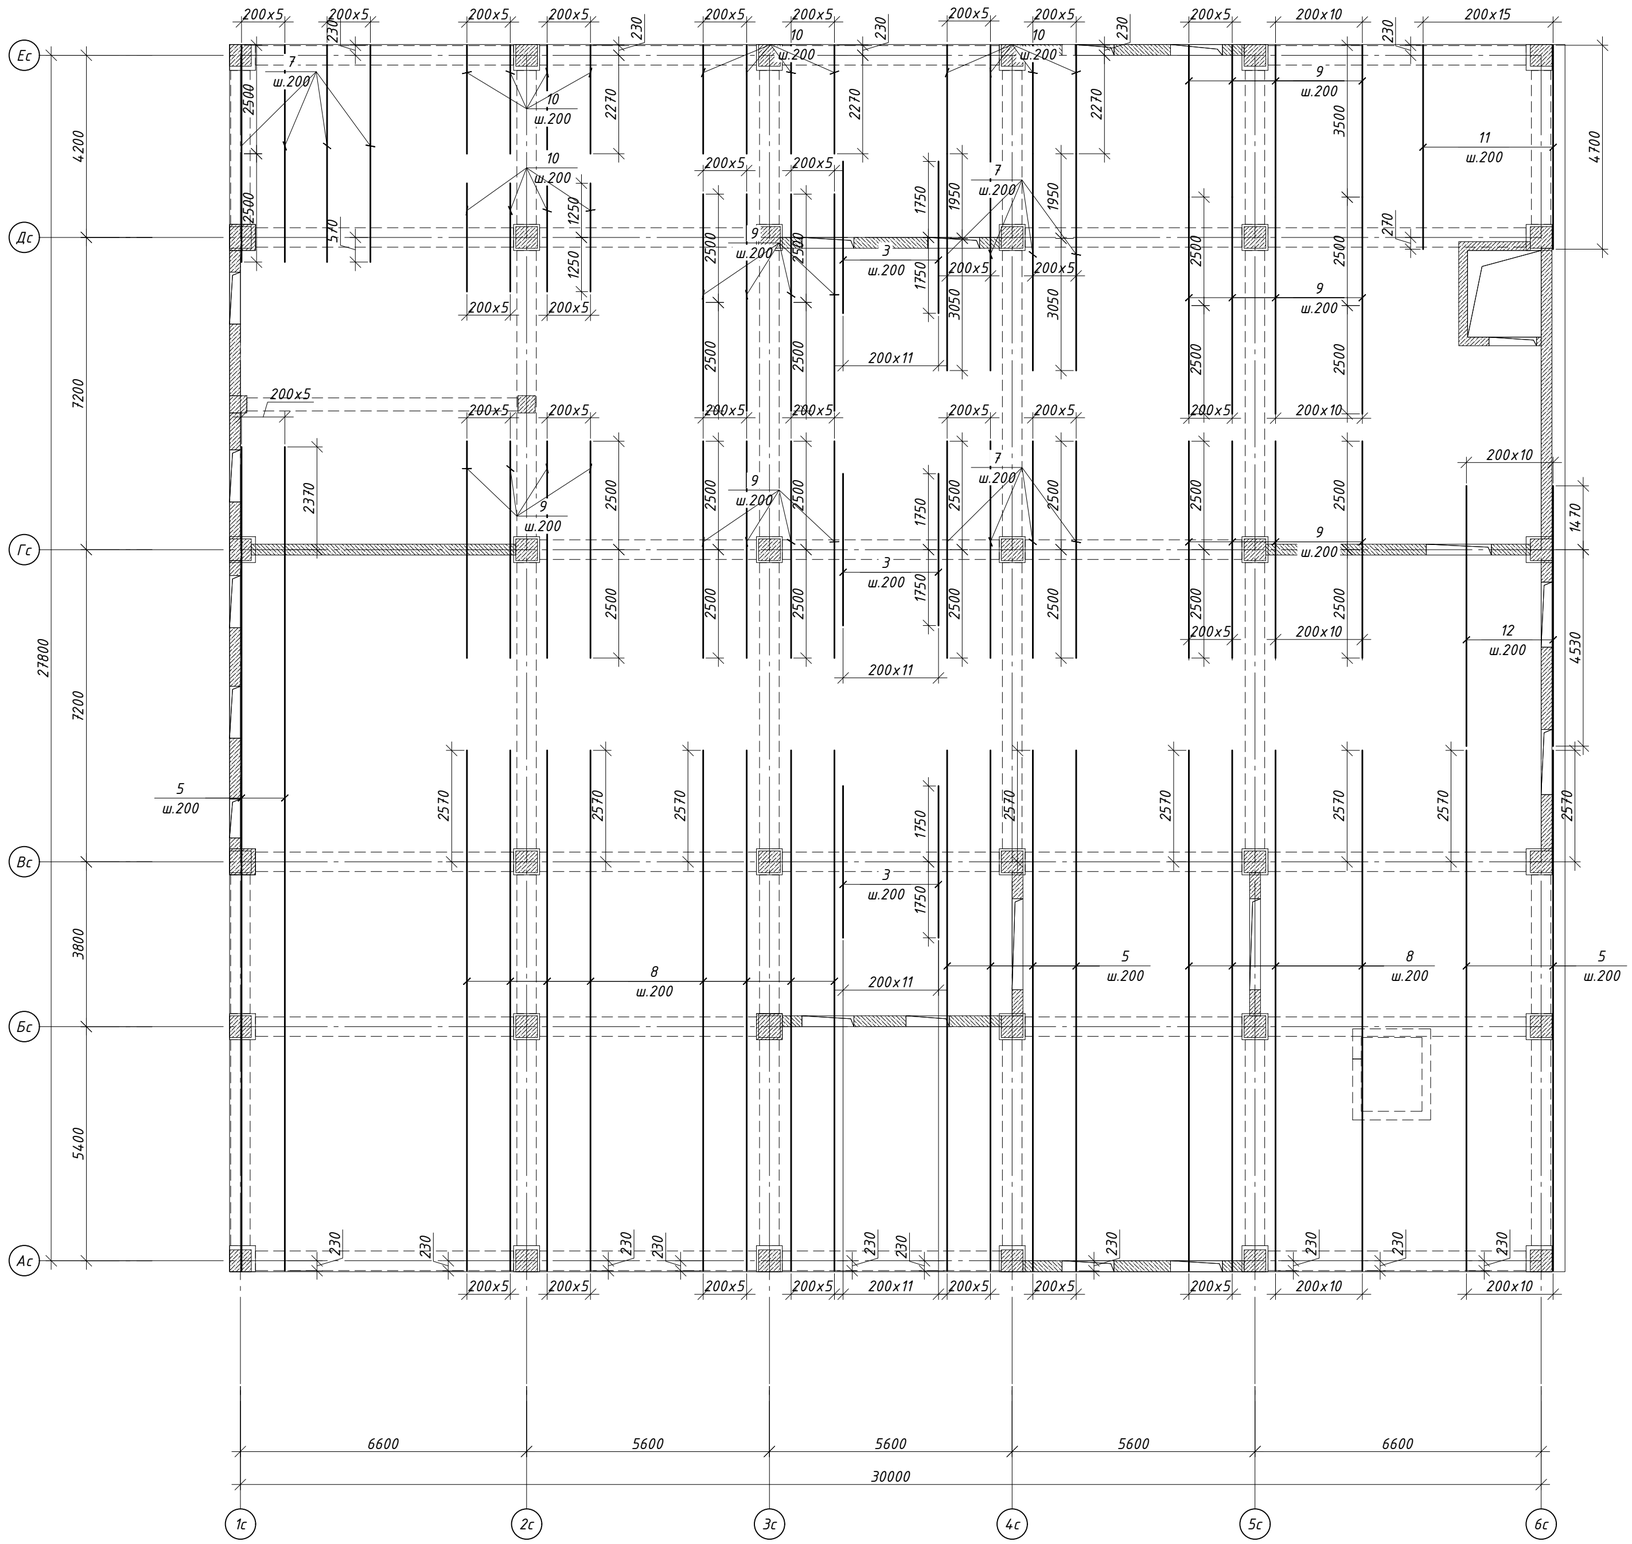


1. Данный лист читать совместно с листами КЖ-2.3 и КЖ-7.8 ... 7.14.
2. Арматура плиты перекрытия стыкуется внахлест.
3. Стыки нижней арматуры выполнять на опоре, стыки верхней арматуры на расстоянии 1/3 - 1/4 пролета от опоры, при этом в одном сечении стыковать не более 50% арматуры.
4. Продольную и поперечную арматуру во всех пересечениях связать вязальной проволокой.
5. Свободные концы основной арматуры у торцов плиты перекрытия должны быть заанкерены "П"-образной скобой (поз. Ск1) при помощи вязальной проволоки (без сварки).
6. Спецификацию см. лист КЖ-7.14


						65П-АИП-2024-1-КЖ
						Строительство многопрофильной больницы на 250 коек с онкологическим центром и поликлиникой на 350 посещений, по адресу: Медеуский район, г. Алматы
Изм.	Кол.уч.	Лист	N док.	Подп.	Дата	
						"Блок 1 Секция 1"
ГКП		Курал М				Стадия: РП; Лист: 7.13; Листов:
Проверил		Кыдырбай А				Схема расположения дополнительного арматуры плиты перекрытия Пм-2 верхней зоны по цифровым осям на отм +3.820
Разраб.		Ауез Б				АстанаИнжПроект
Н.контроль		Ешенкулова				

Формат А2


Детали обрамления отверстий

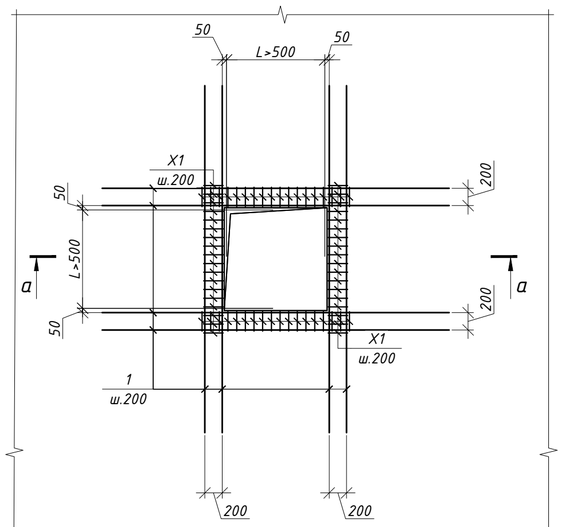

а – а

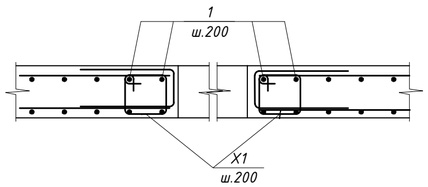

Разрез 1 – 1 (армирование)

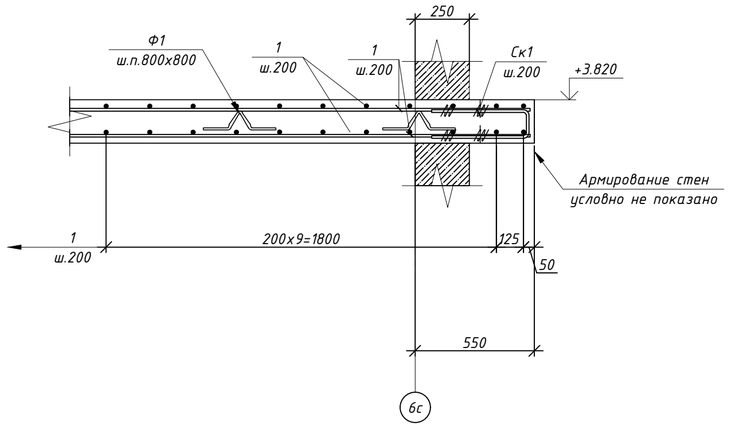

Ведомость деталей

Поз.	Эскиз
Ск1	860; 140; R=2.5Ф(±20Ф); R=4Ф(±20Ф); 860; по н.г. L=1860
Ф1	300; 116; 116; 300; 300; по н.г. L=1132
Х1	320; 220; 320; 220; по в.г. L=1080

Спецификация элементов

Поз.	Обозначение	Наименование	Кол.	Масса ед.кг	Примечание
		Плита Пм-2			27169.63
1	ГОСТ 34028-2016(214-210-0502-0001)	Ф 12 А500С L= пог.м.	17801.70	0.89	15804.60
2	ГОСТ 34028-2016(214-210-0502-0002)	Ф 14 А500С L= 3500	24	4.23	101.51
3	ГОСТ 34028-2016(214-210-0502-0001)	Ф 12 А500С L= 3500	169	3.11	525.14
4	ГОСТ 34028-2016(214-210-0502-0003)	Ф 16 А500С L= 3500	108	5.52	596.61
5	ГОСТ 34028-2016(214-210-0502-0005)	Ф 20 А500С L= пог.м.	615.89	2.47	1518.87
6	ГОСТ 34028-2016(214-210-0502-0004)	Ф 18 А500С L= 3500	92	6.99	643.22
7	ГОСТ 34028-2016(214-210-0502-0005)	Ф 20 А500С L= 5000	108	12.33	1331.72
8	ГОСТ 34028-2016(214-210-0502-0004)	Ф 18 А500С L= пог.м.	832.02	2.00	1662.03
9	ГОСТ 34028-2016(214-210-0502-0004)	Ф 18 А500С L= 5000	76	9.99	759.08
10	ГОСТ 34028-2016(214-210-0502-0002)	Ф 14 А500С L= 2500	48	3.02	145.01
11	ГОСТ 34028-2016(214-210-0502-0005)	Ф 20 А500С L= 4700	16	11.59	185.45
12	ГОСТ 34028-2016(214-210-0502-0002)	Ф 14 А500С L= 6000	11	7.25	79.76
Ск1	ГОСТ 34028-2016(214-210-0502-0001)	Ф 12 А500С L= 1860	616	1.65	1017.22
Ф1	ГОСТ 34028-2016(214-210-0502-0001)	Ф 12 А500С L= 1132	2645	1.01	2658.24
ВП1	ГОСТ 34028-2016(214-210-0502-0003)	Ф 16 А500С L= 3650	16	5.76	92.17
ВП2	ГОСТ 34028-2016(214-210-0502-0003)	Ф 16 А500С L= 1940	16	3.06	48.99
		Материалы:			
	(212-101-0901)	Класс бетона С 20/25 (В25), м³			191.01

Позиции со "*" см. "Ведомость деталей" см. на данном листе.

Ведомость расхода стали, кг


Марка элемента	Изделия арматурные													Всего
	Арматура класса													
	А240			А500С										
	ГОСТ 34028-2016(214-210-0101)			ГОСТ 34028-2016(214-210-0502)										
	Ф6	Ф8	Итого	Ф10	Ф12	Ф14	Ф16	Ф18	Ф20	Ф22	Ф25	Ф28	Ф32	Итого
Плита +3.820	---	---	---	---	20005.20	326.27	737.78	3064.33	3036.05	---	---	---	---	27169.63	27169.63

1. Данный лист читать совместно с листами КЖ-2.3 и КЖ-7.8 ... 7.14.
2. Арматура плиты перекрытия стыкуется внахлест.
3. Стыки нижней арматуры выполнять на опоре, стыки верхней арматуры на расстоянии 1/3 – 1/4 пролета от опоры, при этом в одном сечении стыковать не более 50% арматуры.
4. Продольную и поперечную арматуру во всех пересечениях связать вязальной проволокой.
5. Свободные концы основной арматуры у торцов плиты перекрытия должны быть заанкерены "П"-образной скобой (поз. Ск1) при помощи вязальной проволоки (без сварки).
6. Спецификацию см. лист КЖ-7.14


Изм.	Кол.уч	Лист	N док.	Подп.	Дата	65П-АИП-2024-1-КЖ			
						Строительство многопрофильной больницы на 250 коек с онкологическим центром и поликлиникой на 350 посещений, по адресу: Медеуский район, г. Алматы			
ГКП		Курал М				"Блок 1 Секция 1"	Стадия	Лист	Листов
Проверил		Кыдырбай А					РП	7.14	
Разраб.		Ауез Б				Спецификация плиты перекрытия Пм-2 на отм +3.820	АстанаИнжПроект		
Н.контроль		Ешенкулова							

Формат А2


Опалубочный чертеж плиты перекрытия Пм-3 на отм. +7.720

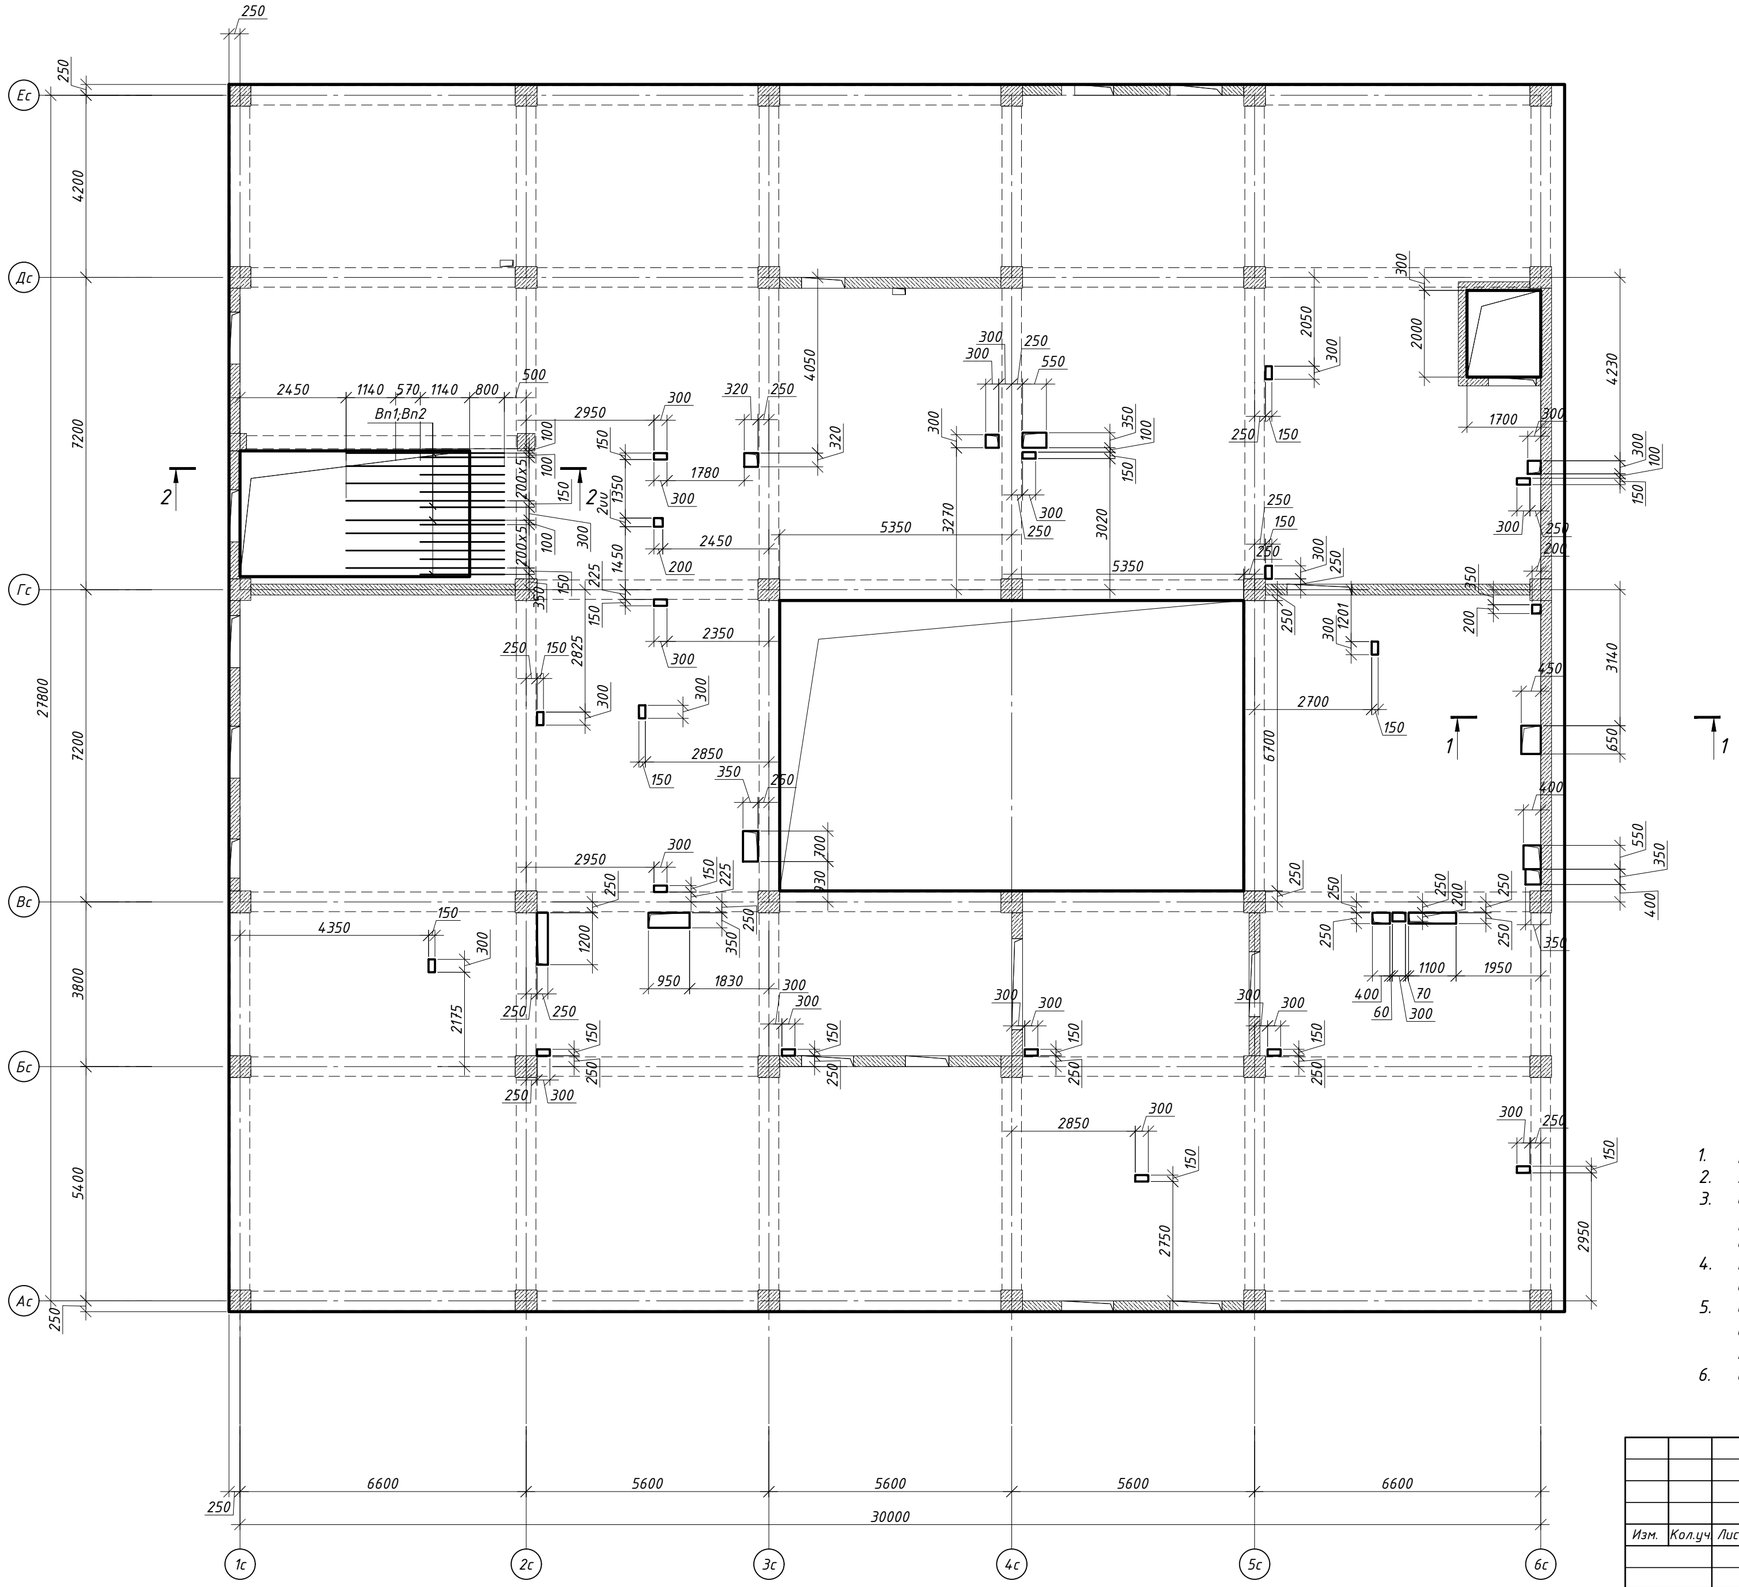

Разрез 1 - 1 (Опалубка)
М 1:50

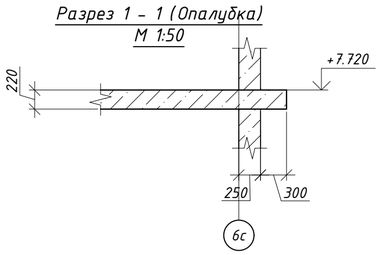

Разрез 2 - 2

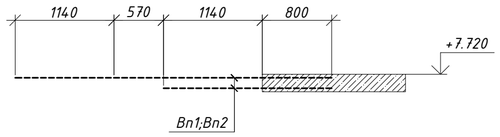


1. Данный лист читать совместно с листами КЖ-2.4 и КЖ-7.16 ... 7.21.
2. Арматура плиты перекрытия стыкуется внахлест.
3. Стыки нижней арматуры выполнять на опоре, стыки верхней арматуры на расстоянии 1/3 - 1/4 пролета от опоры, при этом в одном сечении стыковать не более 50% арматуры.
4. Продольную и поперечную арматуру во всех пересечениях связать вязальной проволокой.
5. Свободные концы основной арматуры у торцов плиты перекрытия должны быть заанкерены "П"-образной скобой (поз. Ск1) при помощи вязальной проволоки (без сварки).
6. Спецификацию см. лист КЖ-7.21

						65П-АИП-2024-1-КЖ	
						Строительство многопрофильной больницы на 250 коек с онкологическим центром и поликлиникой на 350 посещений, по адресу: Медеуский район, г. Алматы	
Изм.	Кол.уч	Лист	N док.	Подп.	Дата		
						"Блок 1 Секция 1"	Стадия: РП; Лист: 7.15; Листов:
ГКП		Курал М				Опалубочный чертеж плиты перекрытия Пм-3 на отм.+7.720	АстанаИнжПроект
Проверил		Кыдырбай А					
Разраб.		Ауез Б					
Н.контроль		Ешенкулова					

Формат А2


Схема расположения основных арматуры плиты перекрытия Пм-3 на отм +7.720

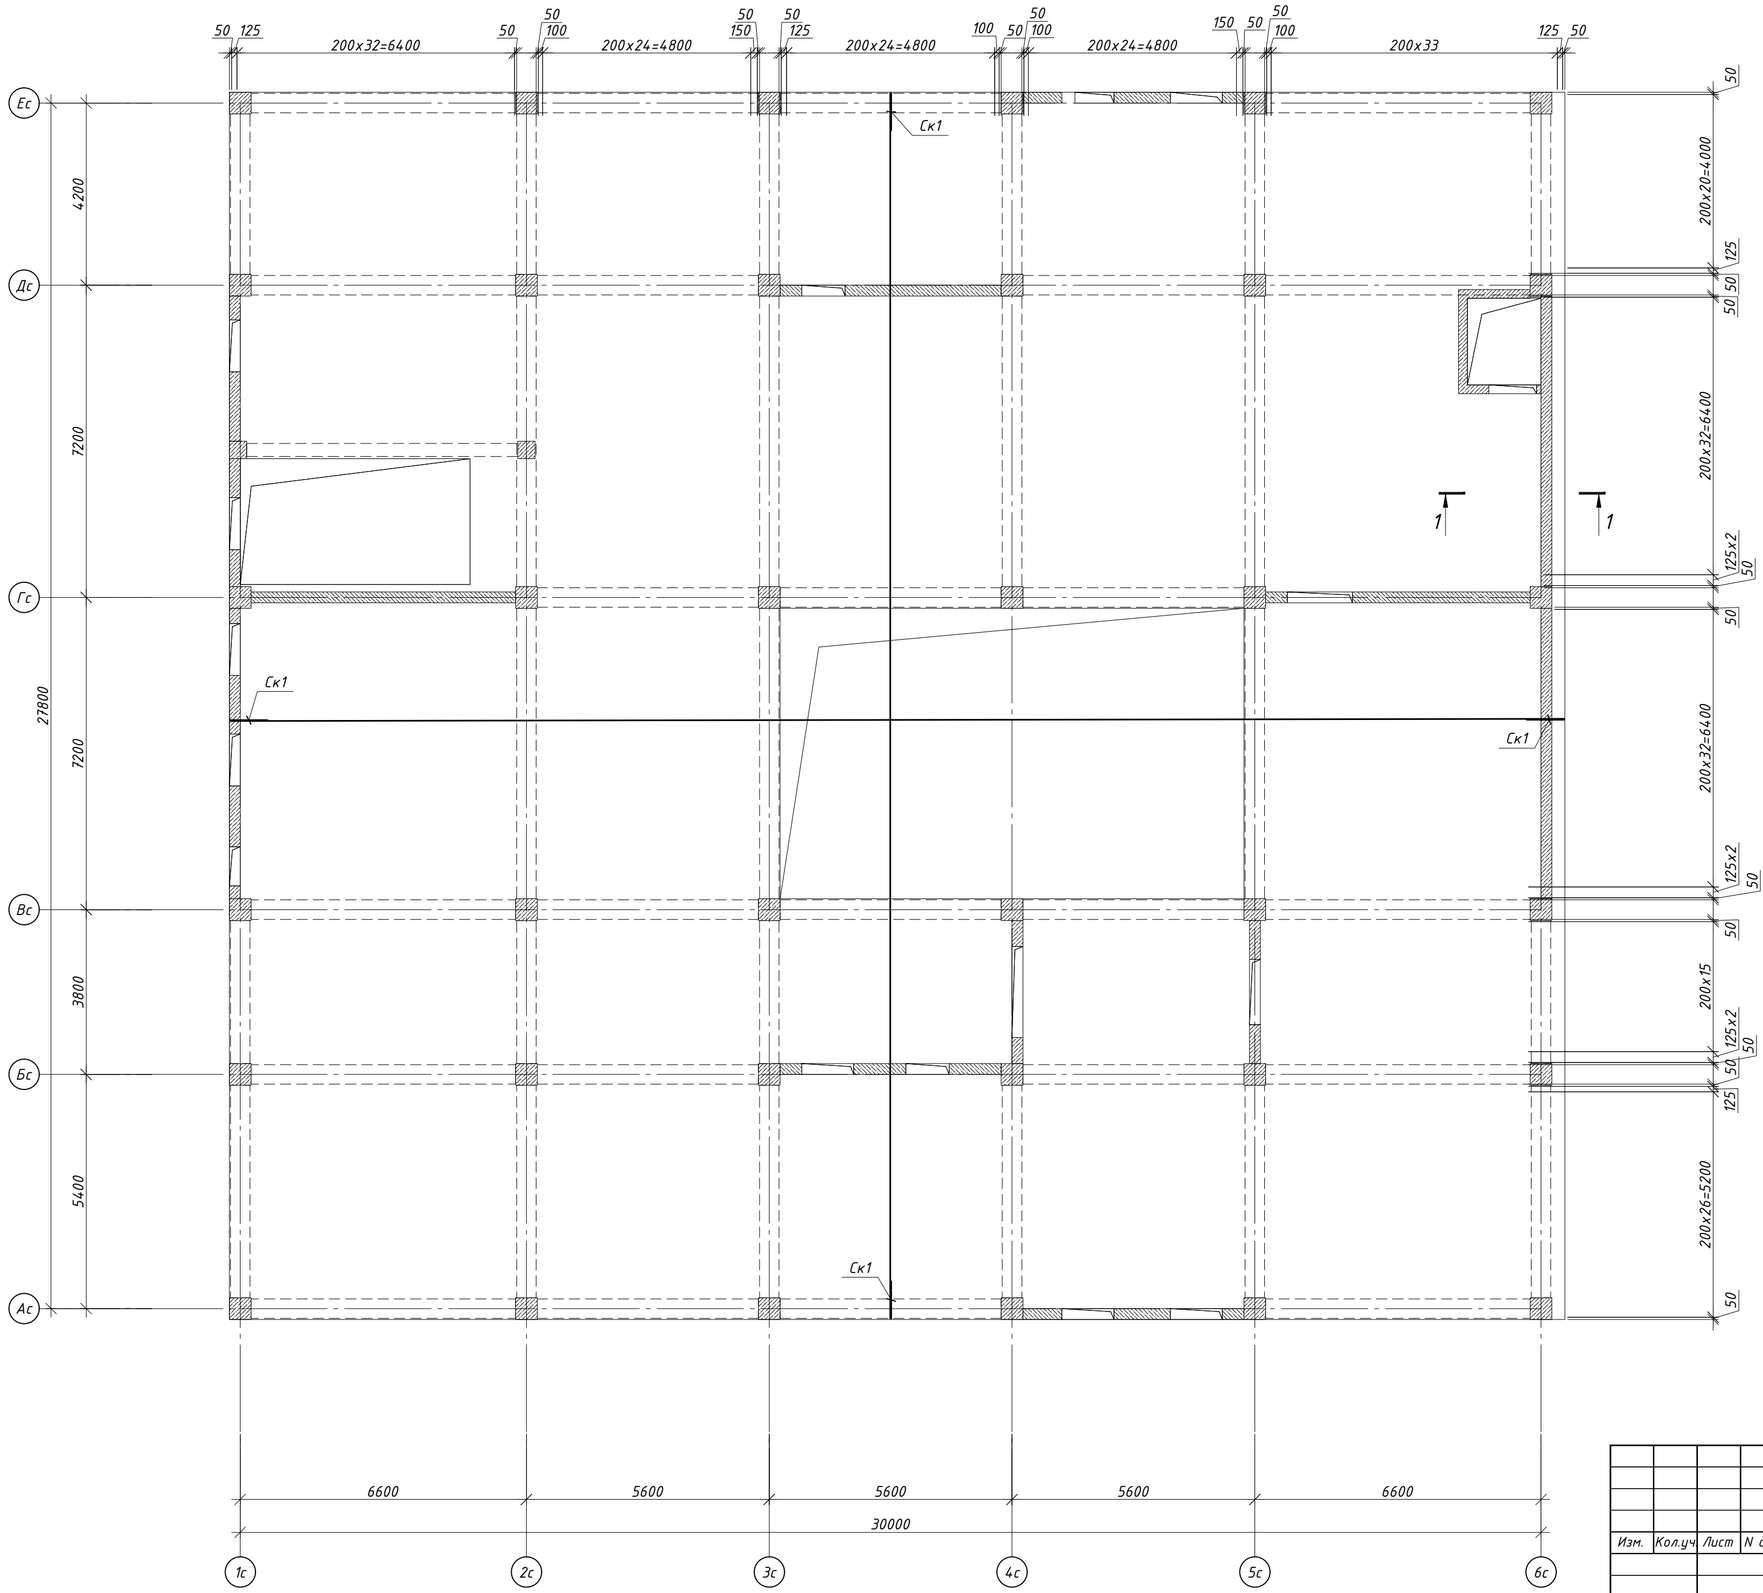

1. Данный лист читать совместно с листами КЖ-2.4 и КЖ-7.15 ... 7.21.
2. Арматура плиты перекрытия стыкуется внахлест.
3. Стыки нижней арматуры выполнять на опоре, стыки верхней арматуры на расстоянии 1/3 - 1/4 пролета от опоры, при этом в одном сечении стыковать не более 50% арматуры.
4. Продольную и поперечную арматуру во всех пересечениях связать вязальной проволокой.
5. Свободные концы основной арматуры у торцов плиты перекрытия должны быть заанкерены "П"-образной скобой (поз. Ск1) при помощи вязальной проволоки (без сварки).
6. Спецификацию см. лист КЖ-7.21

						65П-АИП-2024-1-КЖ
						Строительство многопрофильной больницы на 250 коек с онкологическим центром и поликлиникой на 350 посещений, по адресу: Медеуский район, г. Алматы
Изм.	Кол.уч	Лист	N док.	Подп.	Дата	
						"Блок 1 Секция 1"
ГКП		Курал М				Стадия: РП; Лист: 7.16; Листов:
Проверил		Кыдырбай А				Схема расположения основных арматуры плиты перекрытия Пм-3 на отм +7.720
Разраб.		Ауез Б				АстанаИнжПроект
Н.контроль		Ешенкулова				Формат А2

Схема расположения дополнительного арматуры плиты перекрытия Пм-3 нижней зоны по буквенным осям на отм +7.720

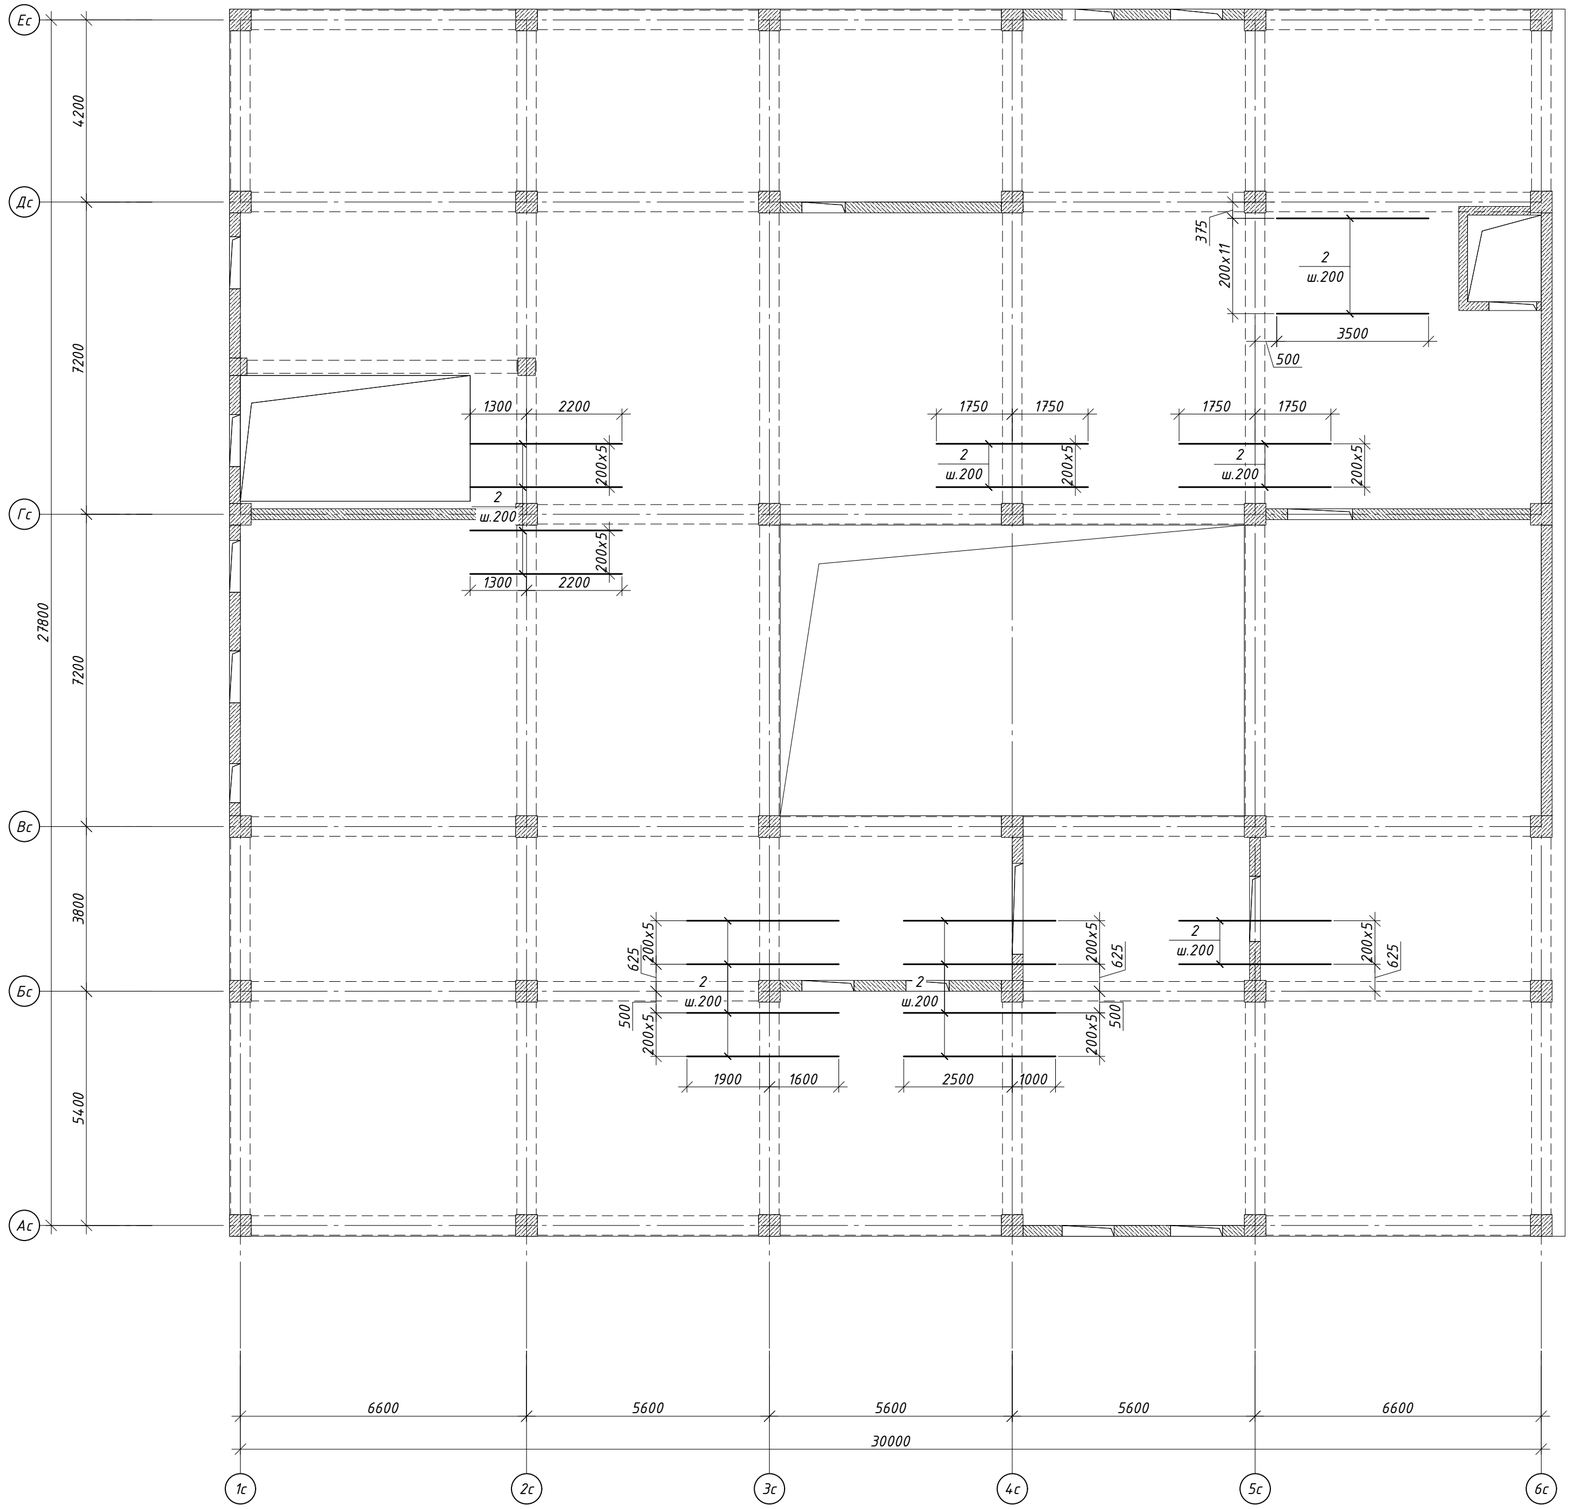


1. Данный лист читать совместно с листами КЖ-2.4 и КЖ-7.15 ... 7.21.
2. Арматура плиты перекрытия стыкуется внахлест.
3. Стыки нижней арматуры выполнять на опоре, стыки верхней арматуры на расстоянии 1/3 - 1/4 пролета от опоры, при этом в одном сечении стыковать не более 50% арматуры.
4. Продольную и поперечную арматуру во всех пересечениях связать вязальной проволокой.
5. Свободные концы основной арматуры у торцов плиты перекрытия должны быть заанкерены "П"-образной скобой (поз. Ск1) при помощи вязальной проволоки (без сварки).
6. Спецификацию см. лист КЖ-7.21

						65П-АИП-2024-1-КЖ
						Строительство многопрофильной больницы на 250 коек с онкологическим центром и поликлиникой на 350 посещений, по адресу: Медеуский район, г. Алматы
Изм.	Кол.уч.	Лист	N док.	Подп.	Дата	
						"Блок 1 Секция 1"
ГКП		Курал М				Стадия: РП; Лист: 7.17; Листов:
Проверил		Кыдырбай А				
Разраб.		Ауез Б				Схема расположения дополнительного арматуры плиты перекрытия Пм-3 нижней зоны по буквенным осям на отм +7.720
Н.контроль		Ешенкулова				АстанаИнжПроект

Формат А2

Схема расположения дополнительного арматуры плиты перекрытия Пм-3 верхней зоны по буквенным осям на отм +7.720

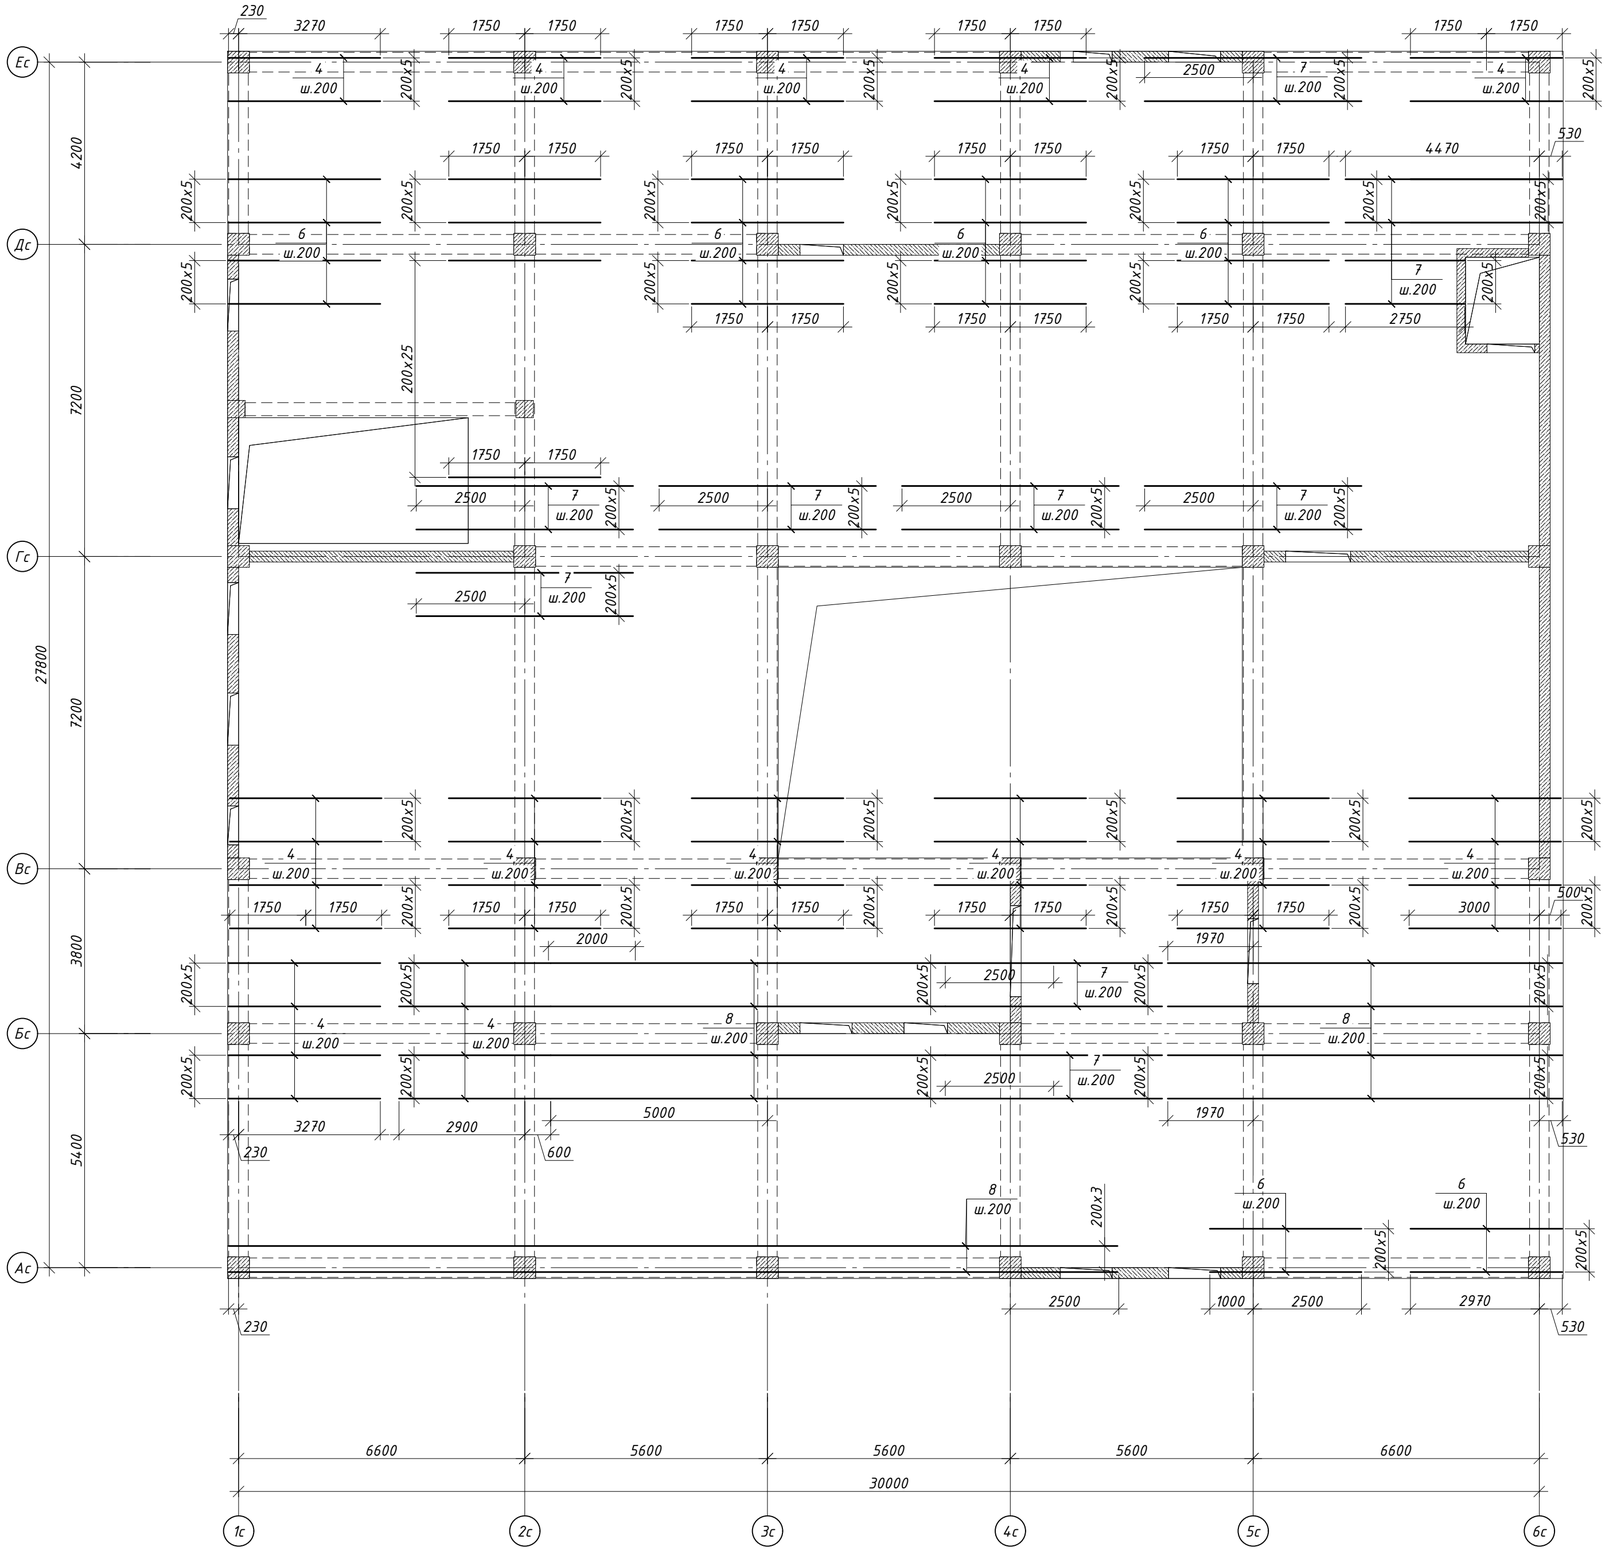


1. Данный лист читать совместно с листами КЖ-2.4 и КЖ-7.15 ... 7.21.
2. Арматура плиты перекрытия стыкуется внахлест.
3. Стыки нижней арматуры выполнять на опоре, стыки верхней арматуры на расстоянии 1/3 - 1/4 пролета от опоры, при этом в одном сечении стыковать не более 50% арматуры.
4. Продольную и поперечную арматуру во всех пересечениях связать вязальной проволокой.
5. Свободные концы основной арматуры у торцов плиты перекрытия должны быть заанкерены "П"-образной скобой (поз. Ск1) при помощи вязальной проволоки (без сварки).
6. Спецификацию см. лист КЖ-7.21

						65П-АИП-2024-1-КЖ
						Строительство многопрофильной больницы на 250 коек с онкологическим центром и поликлиникой на 350 посещений, по адресу: Медеуский район, г. Алматы
Изм.	Кол.уч.	Лист	N док.	Подп.	Дата	
						"Блок 1 Секция 1"
ГКП		Курал М				Стадия: РП; Лист: 7.18; Листов:
Проверил		Кыдырбай А				Схема расположения дополнительного арматуры плиты перекрытия Пм-3 верхней зоны по буквенным осям на отм +7.720
Разраб.		Ауез Б				АстанаИнжПроект
Н.контроль		Ешенкулова				

Формат А2

Схема расположения дополнительного арматуры плиты перекрытия Пм-3 нижней зоны по цифровым осям на отм +7.720

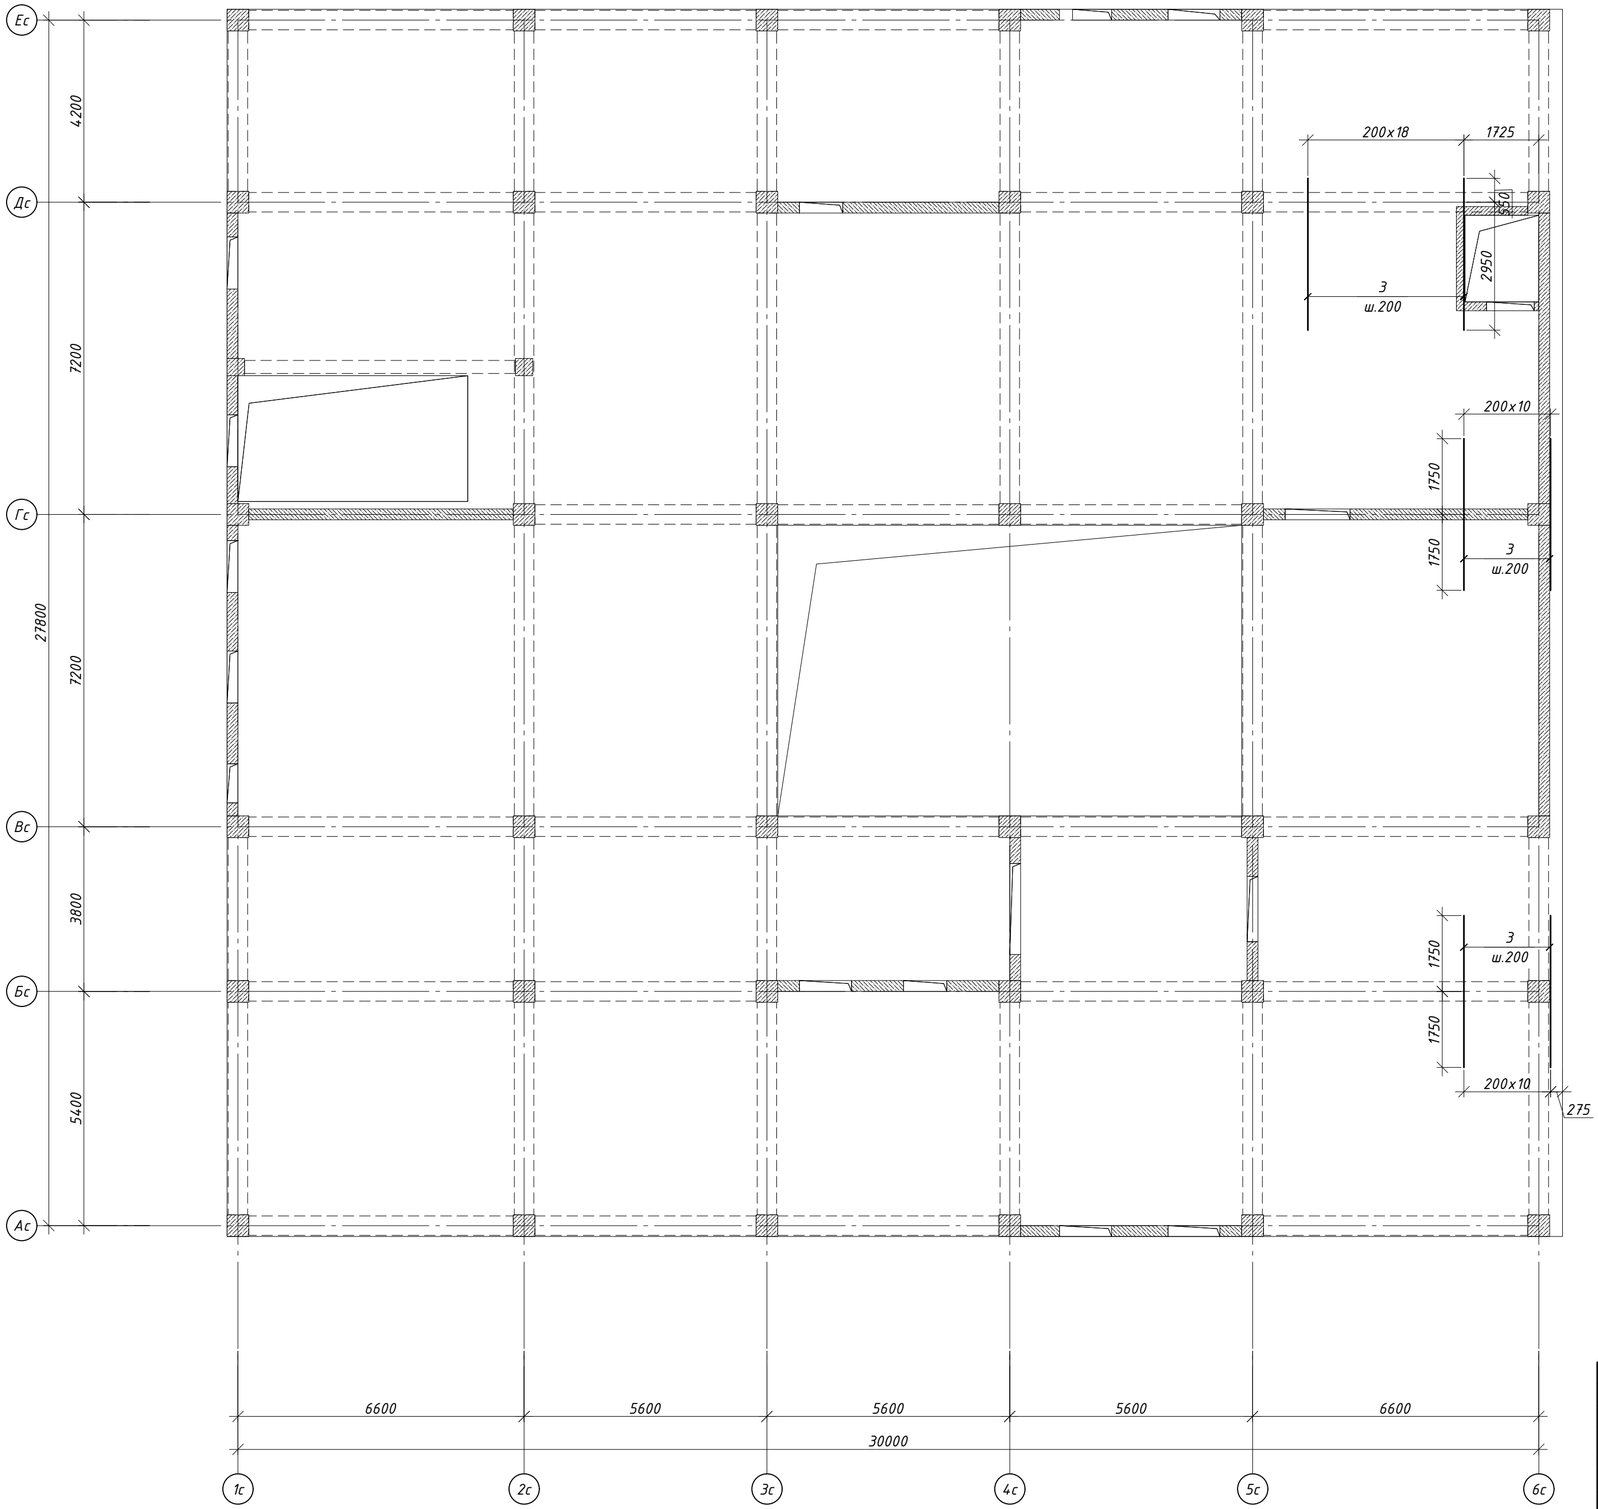


1. Данный лист читать совместно с листами КЖ-2.4 и КЖ-7.15 ... 7.21.
2. Арматура плиты перекрытия стыкуется внахлест.
3. Стыки нижней арматуры выполнять на опоре, стыки верхней арматуры на расстоянии 1/3 - 1/4 пролета от опоры, при этом в одном сечении стыковать не более 50% арматуры.
4. Продольную и поперечную арматуру во всех пересечениях связать вязальной проволокой.
5. Свободные концы основной арматуры у торцов плиты перекрытия должны быть заанкерены "П"-образной скобой (поз. Ск1) при помощи вязальной проволоки (без сварки).
6. Спецификацию см. лист КЖ-7.21

						65П-АИП-2024-1-КЖ
						Строительство многопрофильной больницы на 250 коек с онкологическим центром и поликлиникой на 350 посещений, по адресу: Медеуский район, г. Алматы
Изм.	Кол.уч.	Лист	N док.	Подп.	Дата	
ГКП		Курал М				"Блок 1 Секция 1"
Проверил		Кыдырбай А				Стадия: РП; Лист: 7.19; Листов:
Разраб.		Ауез Б				Схема расположения дополнительного арматуры плиты перекрытия Пм-3 нижней зоны по цифровым осям на отм +7.720
Н.контроль		Ешенкулова				АстанаИнжПроект

Формат А2

Схема расположения дополнительного арматуры плиты перекрытия Пм-3 верхней зоны по цифровым осям на отм +7.720

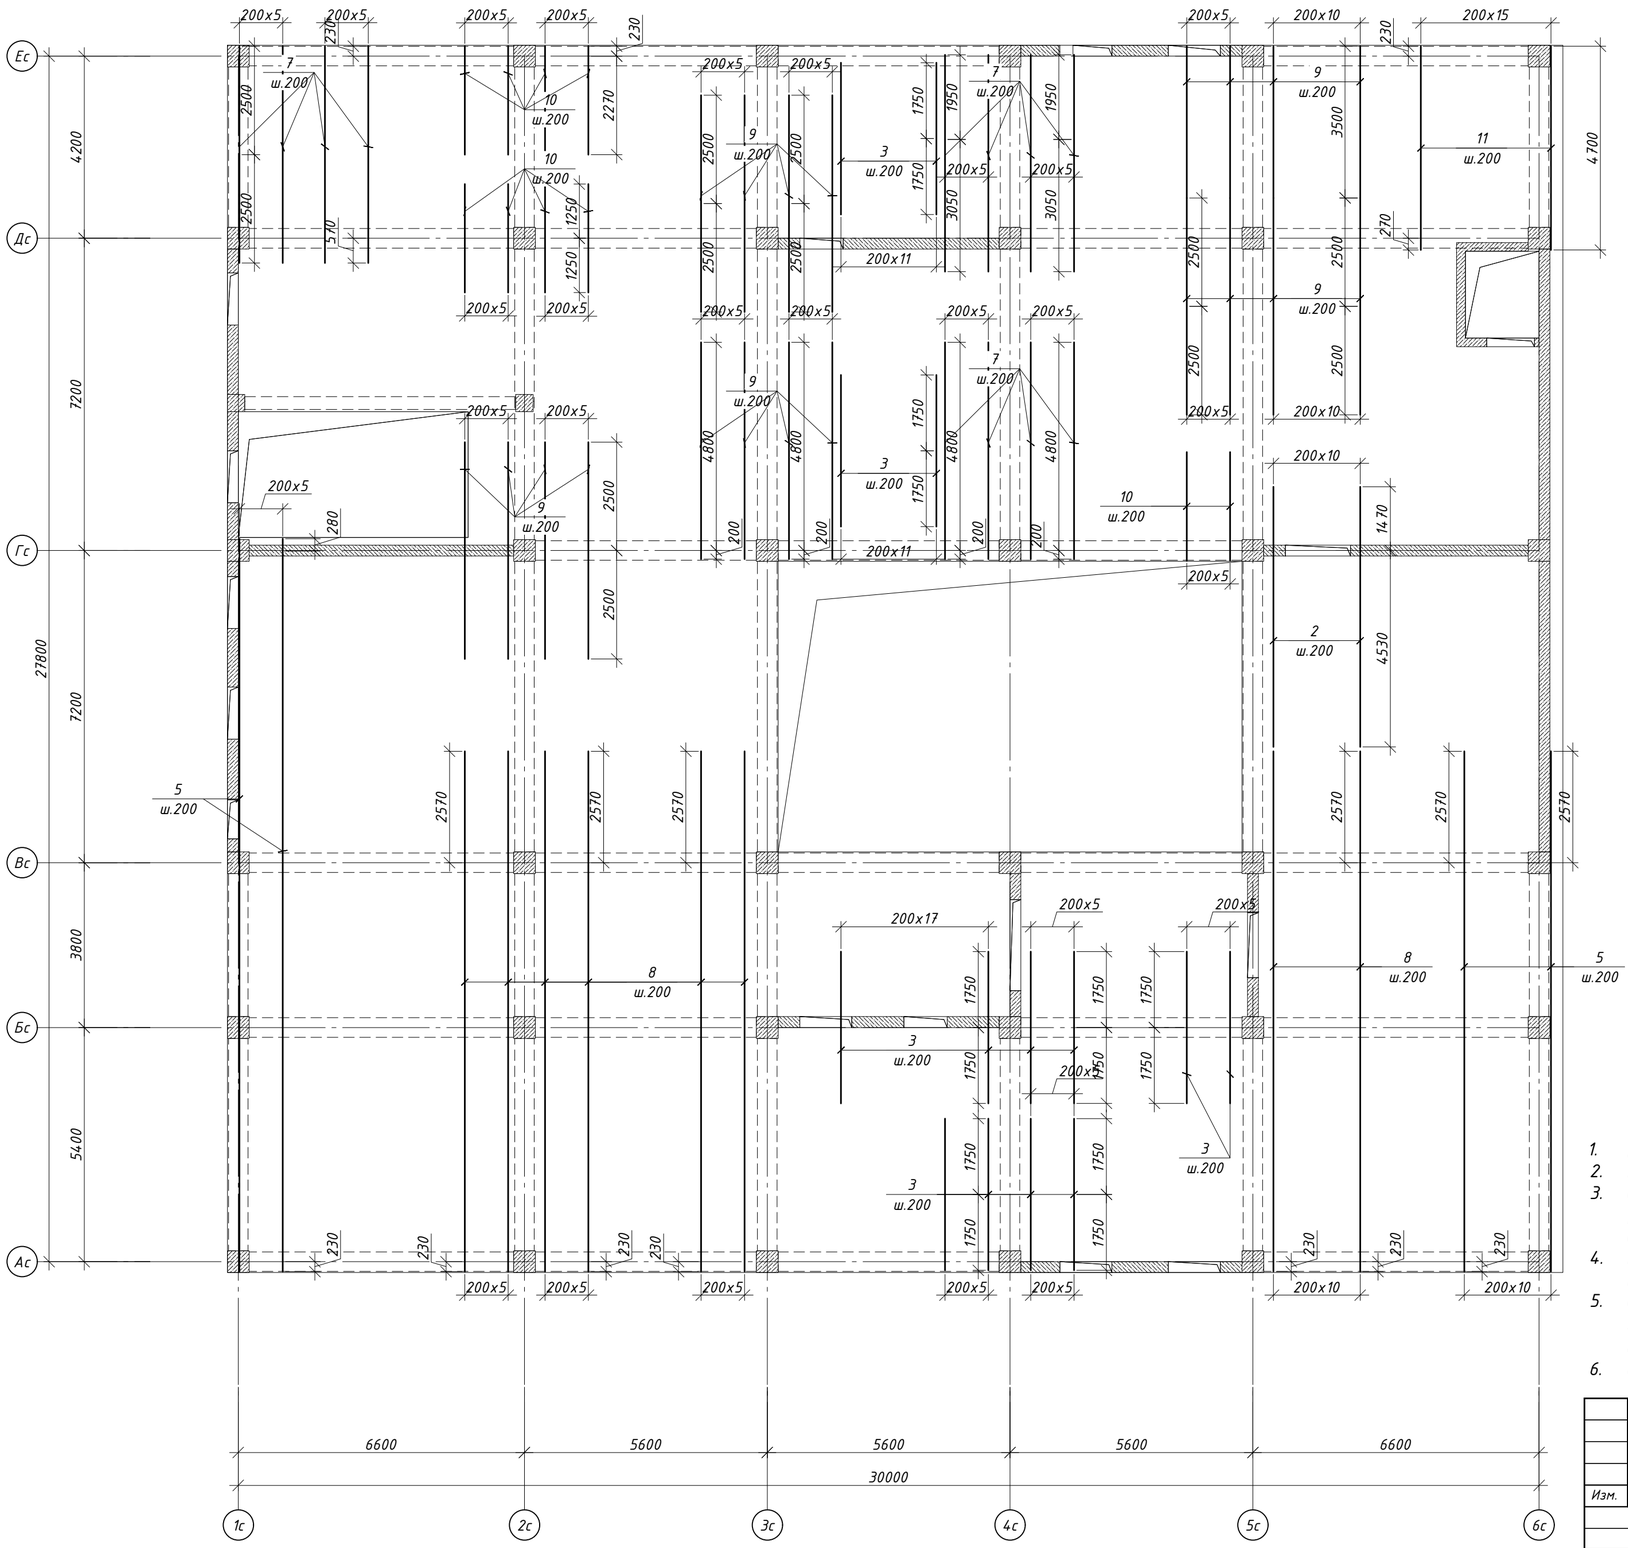


1. Данный лист читать совместно с листами КЖ-2.4 и КЖ-7.15 ... 7.21.
2. Арматура плиты перекрытия стыкуется внахлест.
3. Стыки нижней арматуры выполнять на опоре, стыки верхней арматуры на расстоянии 1/3 - 1/4 пролета от опоры, при этом в одном сечении стыковать не более 50% арматуры.
4. Продольную и поперечную арматуру во всех пересечениях связать вязальной проволокой.
5. Свободные концы основной арматуры у торцов плиты перекрытия должны быть заанкерены "П"-образной скобой (поз. Ск1) при помощи вязальной проволоки (без сварки).
6. Спецификацию см. лист КЖ-7.21


						65П-АИП-2024-1-КЖ
						Строительство многопрофильной больницы на 250 коек с онкологическим центром и поликлиникой на 350 посещений, по адресу: Медеуский район, г. Алматы
Изм.	Кол.уч	Лист	N док.	Подп.	Дата	
						"Блок 1 Секция 1" — Стадия: РП; Лист: 7.20; Листов:
ГКП		Курал М				Схема расположения дополнительного арматуры плиты перекрытия Пм-3 верхней зоны по цифровым осям на отм +7.720
Проверил		Кыдырбай А				АстанаИнжПроект
Разраб.		Ауез Б				
Н.контроль		Ешенкулова				

Формат А2


Детали обрамления отверстий

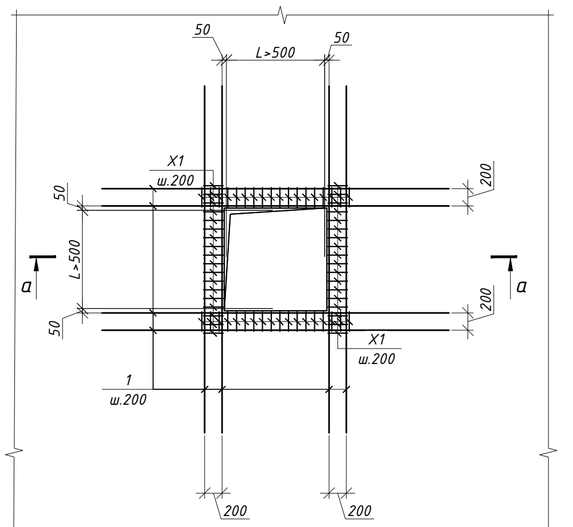

а – а

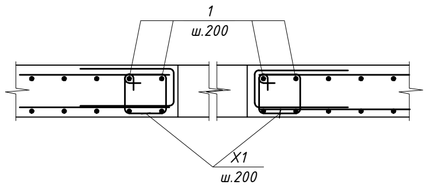

Разрез 1 – 1 (армирование)

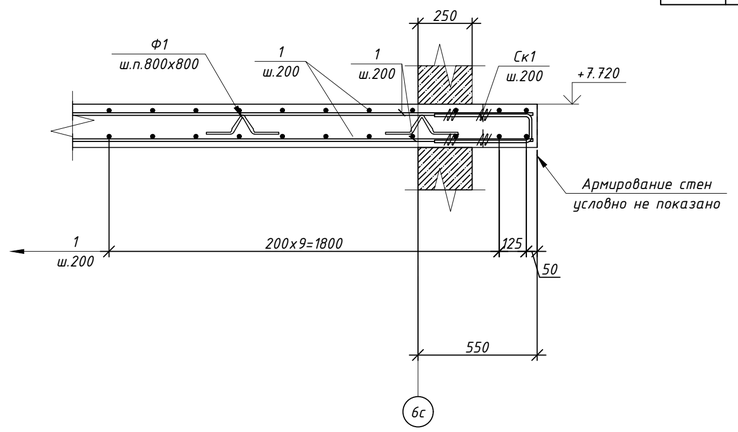

Ведомость деталей

Поз.	Эскиз
Ск1	860; 140; R=2.5ϕ(=20ϕ); R=4ϕ(=20ϕ); 860; по н.г. L=1860
Ф1	300; 116; 116; 300; 300; по н.г. L=1132
Х1	320; 220; 320; 220; по в.г. L=1080

Спецификация элементов

Поз.	Обозначение	Наименование	Кол.	Масса ед.кг	Примечание
		Плита Пм-3			25045.02
1	ГОСТ 34028-2016(214-210-0502-0001)	ϕ 12 А500С L= пог.м.	15934.80	0.89	14147.14
2	ГОСТ 34028-2016(214-210-0502-0006)	ϕ 22 А500С L= 6000	11	17.90	196.95
3	ГОСТ 34028-2016(214-210-0502-0001)	ϕ 12 А500С L= 3500	133	3.11	413.28
4	ГОСТ 34028-2016(214-210-0502-0003)	ϕ 16 А500С L= 3500	126	5.52	696.05
5	ГОСТ 34028-2016(214-210-0502-0005)	ϕ 20 А500С L= пог.м.	451.46	2.47	1113.36
6	ГОСТ 34028-2016(214-210-0502-0004)	ϕ 18 А500С L= 3500	92	6.99	643.22
7	ГОСТ 34028-2016(214-210-0502-0005)	ϕ 20 А500С L= 5000	108	12.33	1331.72
8	ГОСТ 34028-2016(214-210-0502-0004)	ϕ 18 А500С L= пог.м.	680.82	2.00	1359.99
9	ГОСТ 34028-2016(214-210-0502-0004)	ϕ 18 А500С L= 5000	59	9.99	589.29
10	ГОСТ 34028-2016(214-210-0502-0002)	ϕ 14 А500С L= 2500	30	3.02	90.63
11	ГОСТ 34028-2016(214-210-0502-0005)	ϕ 20 А500С L= 4700	16	11.59	185.45
Ск1	ГОСТ 34028-2016(214-210-0502-0001)	ϕ 12 А500С L= 1860	876	1.65	1446.57
Ф1	ГОСТ 34028-2016(214-210-0502-0001)	ϕ 12 А500С L= 1132	2645	1.01	2658.24
ВП1	ГОСТ 34028-2016(214-210-0502-0003)	ϕ 16 А500С L= 3650	16	5.76	92.17
ВП2	ГОСТ 34028-2016(214-210-0502-0003)	ϕ 16 А500С L= 1940	16	3.06	48.99
Х1	ГОСТ 34028-2016(214-210-0101-0002)	ϕ 8 А 240 L= 1080	75	0.43	31.96
		Материалы:			
	(212-101-0901)	Класс бетона С 20/25 (В25), м³			171.84

Позиции со "*" см. "Ведомость деталей" см. на данном листе.

Ведомость расхода стали, кг


Марка элемента	Изделия арматурные													Всего
	Арматура класса													
	А240			А500С										
	ГОСТ 34028-2016(214-210-0101)			ГОСТ 34028-2016(214-210-0502)										
	ϕ6	ϕ8	Итого	ϕ10	ϕ12	ϕ14	ϕ16	ϕ18	ϕ20	ϕ22	ϕ25	ϕ28	ϕ32	Итого	
Плита +7.720	---	31.96	31.96	---	18665.23	90.63	837.21	2592.50	2630.54	196.95	---	---	---	25013.06	25045.02

1. Данный лист читать совместно с листами КЖ-2.4 и КЖ-7.15 ... 7.20.
2. Арматура плиты перекрытия стыкуется внахлест.
3. Стыки нижней арматуры выполнять на опоре, стыки верхней арматуры на расстоянии 1/3 – 1/4 пролета от опоры, при этом в одном сечении стыковать не более 50% арматуры.
4. Продольную и поперечную арматуру во всех пересечениях связать вязальной проволокой.
5. Свободные концы основной арматуры у торцов плиты перекрытия должны быть заанкерены "П"-образной скобой (поз. Ск1) при помощи вязальной проволоки (без сварки).
6. Спецификацию см. лист КЖ-7.21


Изм.	Кол.уч	Лист	N док.	Подп.	Дата	65П-АИП-2024-1-КЖ			
						Строительство многопрофильной больницы на 250 коек с онкологическим центром и поликлиникой на 350 посещений, по адресу: Медеуский район, г. Алматы			
						"Блок 1 Секция 1"	Стадия	Лист	Листов
							РП	7.21	
ГКП		Курал М				Спецификация плиты перекрытия Пм-3 на отм +7.720	АстанаИнжПроект		
Проверил		Кыдырбай А							
Разраб.		Ауез Б							
Н.контроль		Ешенкулова							

Формат А2


Опалубочный чертеж плиты перекрытия Пм-4 на отм. +11.620

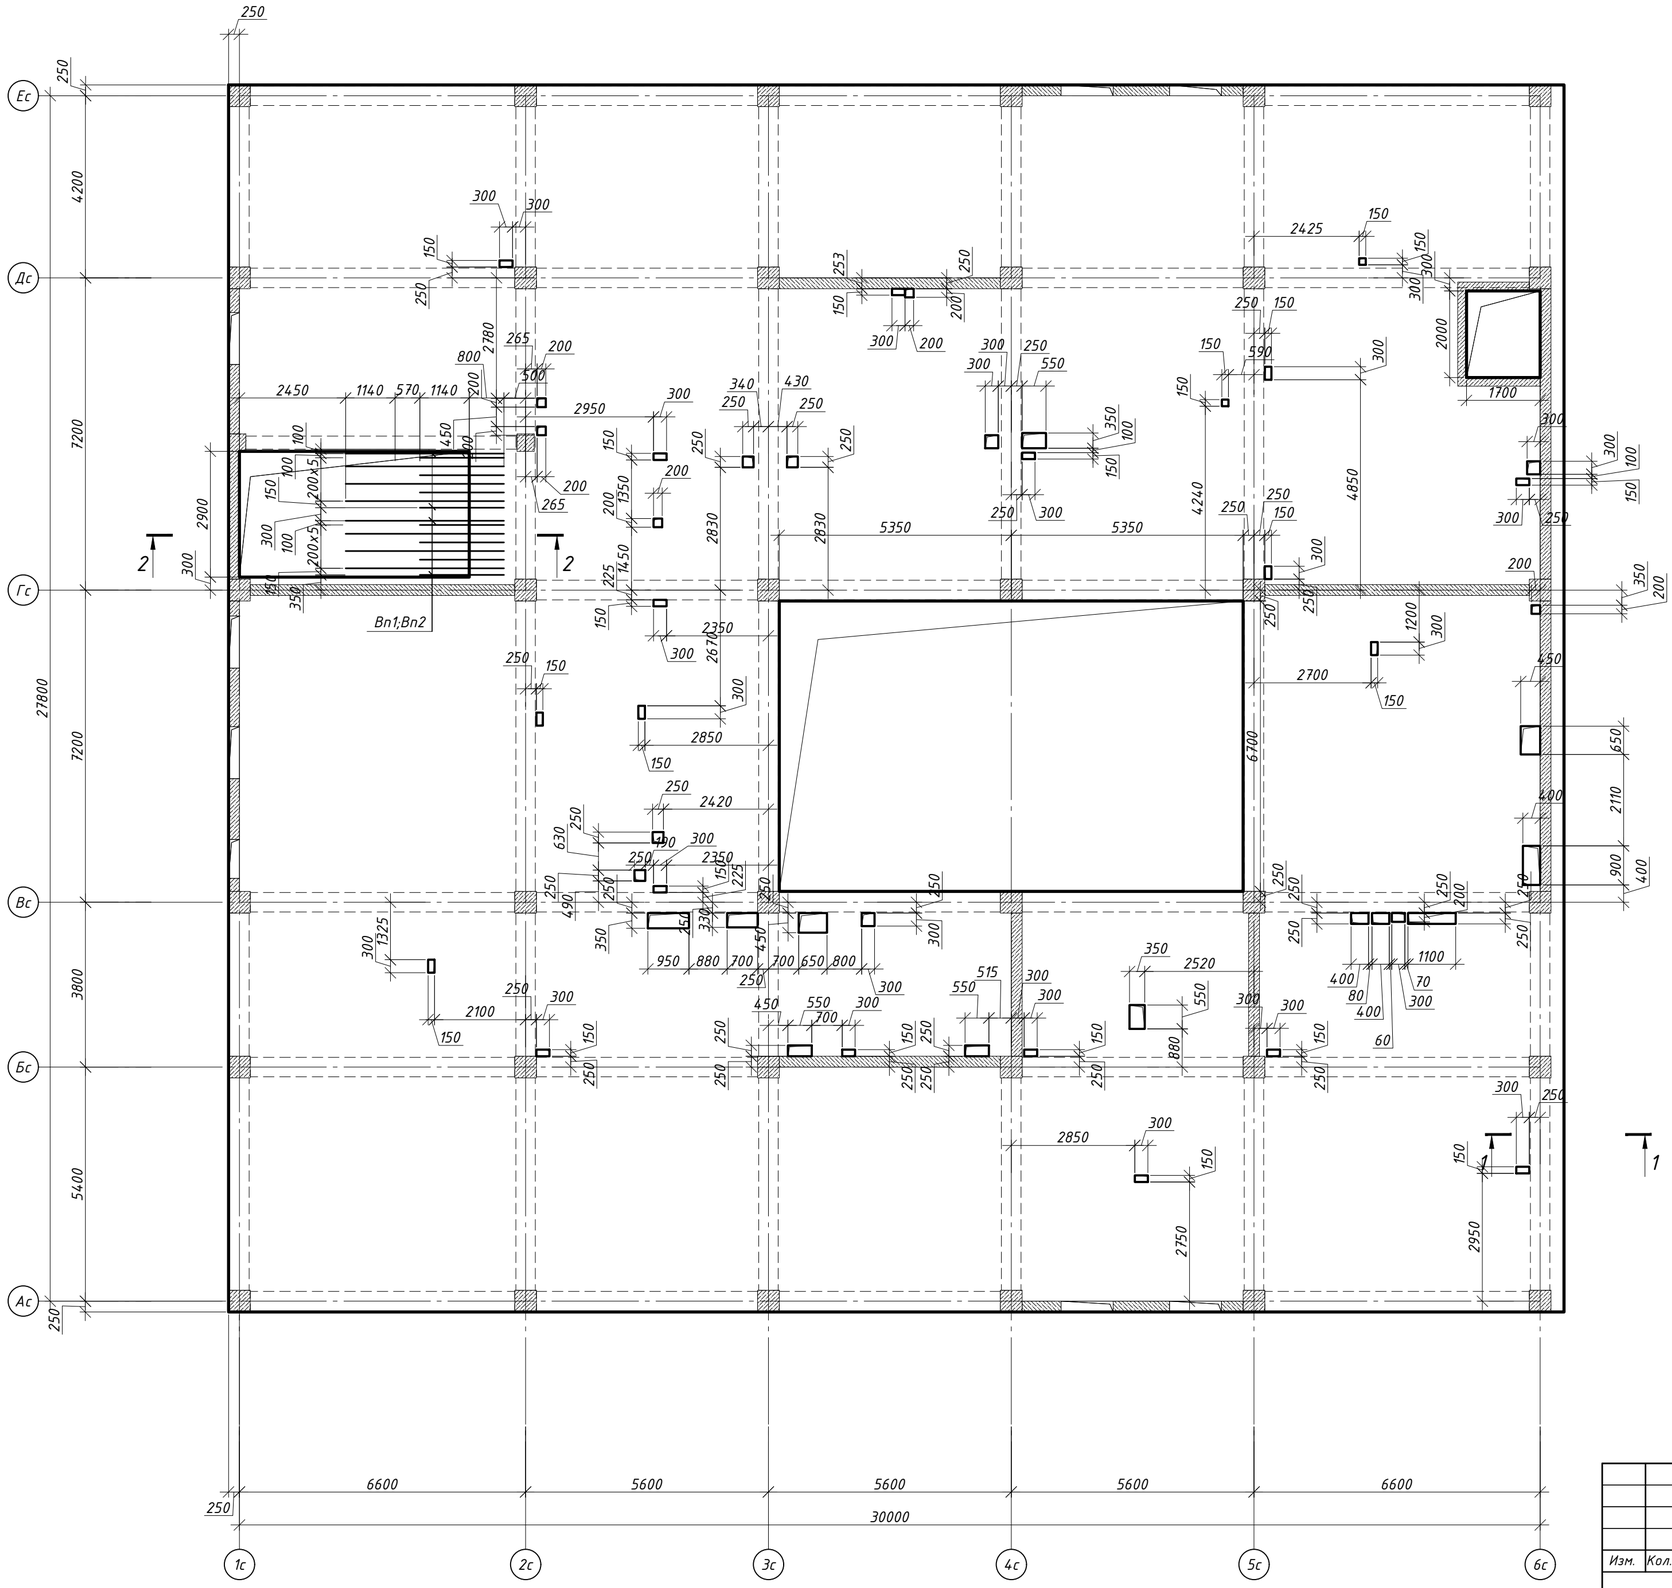

Разрез 1 - 1 (Опалубка)
М 1:50

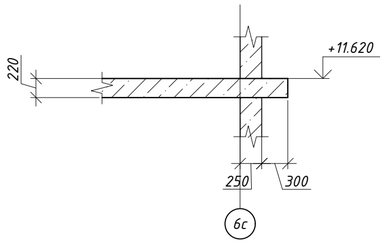

Разрез 2 - 2

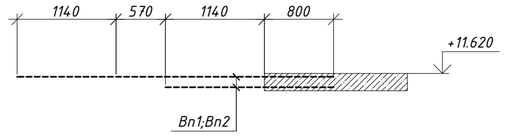


1

1. Данный лист читать совместно с листами КЖ-2.5 и КЖ-7.22 ... 7.28.
2. Арматура плиты перекрытия стыкуется внахлест.
3. Стыки нижней арматуры выполнять на опоре, стыки верхней арматуры на расстоянии 1/3 - 1/4 пролета от опоры, при этом в одном сечении стыковать не более 50% арматуры.
4. Продольную и поперечную арматуру во всех пересечениях связать вязальной проволокой.
5. Свободные концы основной арматуры у торцов плиты перекрытия должны быть заанкерены "П"-образной скобой (поз. Ск1) при помощи вязальной проволоки (без сварки).
6. Спецификацию см. лист КЖ-7.28

						65П-АИП-2024-1-КЖ	
						Строительство многопрофильной больницы на 250 коек с онкологическим центром и поликлиникой на 350 посещений, по адресу: Медеуский район, г. Алматы	
Изм.	Кол.уч	Лист	N док.	Подп.	Дата		
						"Блок 1 Секция 1"	Стадия: РП; Лист: 7.22; Листов:
ГКП		Курал М				Опалубочный чертеж плиты перекрытия Пм-4 на отм.+11.620	АстанаИнжПроект
Проверил		Кыдырбай А					
Разраб.		Ауез Б					
Н.контроль		Ешенкулова					

Формат А2

Схема расположения основных арматуры плиты перекрытия Пм-4 на отм +11.620

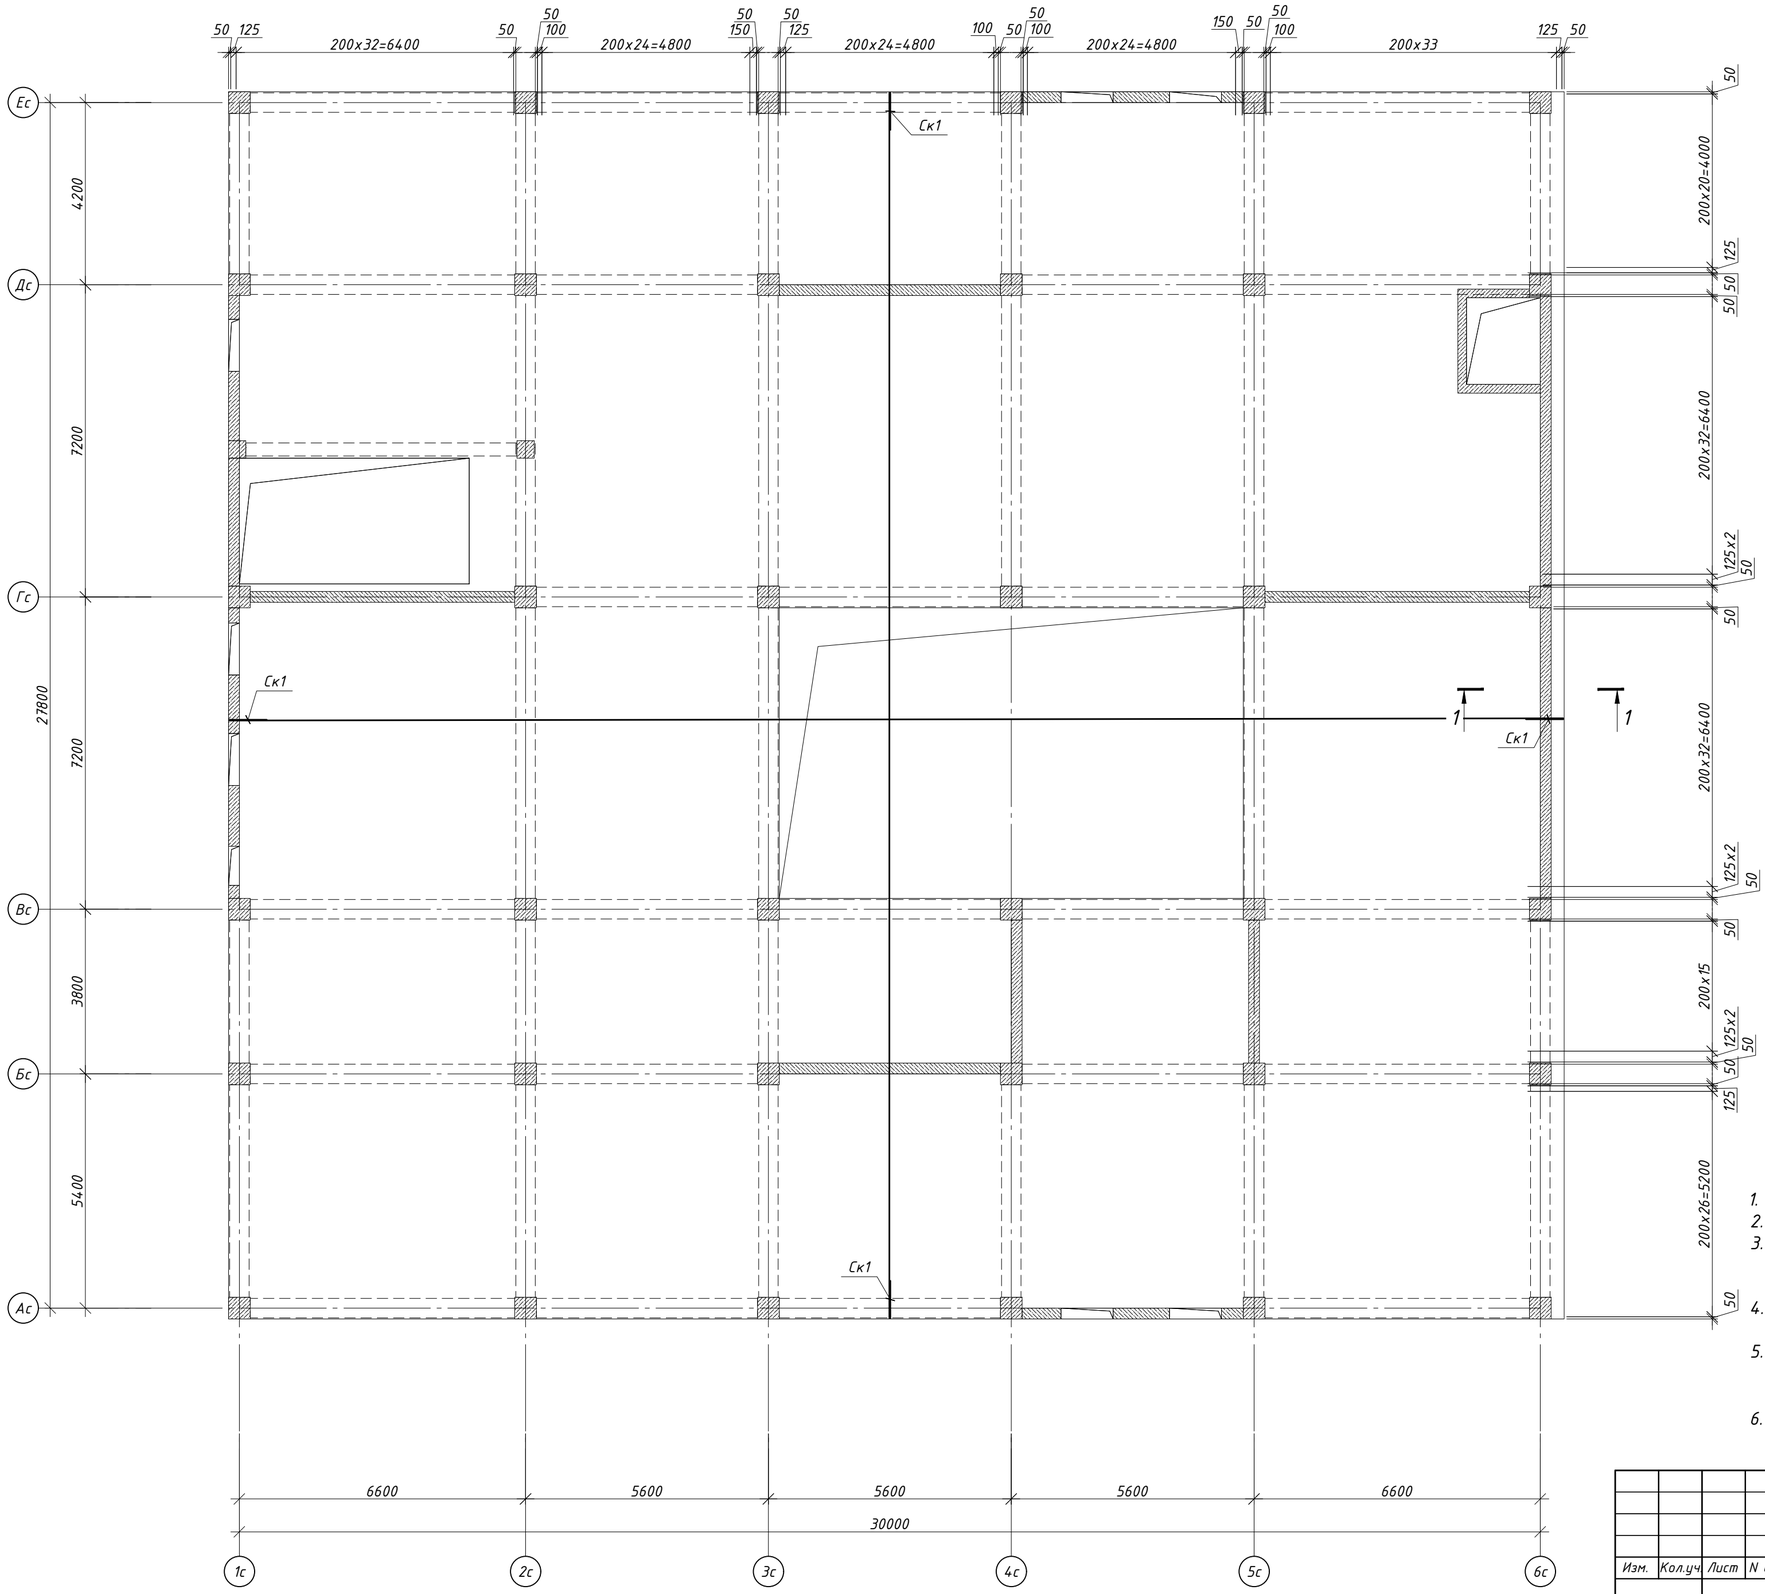


1. Данный лист читать совместно с листами КЖ-2.5 и КЖ-7.22 ... 7.28.
2. Арматура плиты перекрытия стыкуется внахлест.
3. Стыки нижней арматуры выполнять на опоре, стыки верхней арматуры на расстоянии 1/3 - 1/4 пролета от опоры, при этом в одном сечении стыковать не более 50% арматуры.
4. Продольную и поперечную арматуру во всех пересечениях связать вязальной проволокой.
5. Свободные концы основной арматуры у торцов плиты перекрытия должны быть заанкерены "П"-образной скобой (поз. Ск1) при помощи вязальной проволоки (без сварки).
6. Спецификацию см. лист КЖ-7.28

Изм.	Кол.уч.	Лист	N док.	Подп.	Дата	65П-АИП-2024-1-КЖ		
						Строительство многопрофильной больницы на 250 коек с онкологическим центром и поликлиникой на 350 посещений, по адресу: Медеуский район, г. Алматы		
ГКП		Курал М				"Блок 1 Секция 1"	Стадия: РП	Лист: 7.23 / Листов:
Проверил		Кыдырбай А						
Разраб.		Ауез Б				Схема расположения основных арматуры плиты перекрытия Пм-4 на отм +11.620	АстанаИнжПроект	
Н.контроль		Ешенкулова						

Формат А2

Схема расположения дополнительного арматуры плиты перекрытия Пм-4 нижней зоны по буквенным осям на отм +11.620

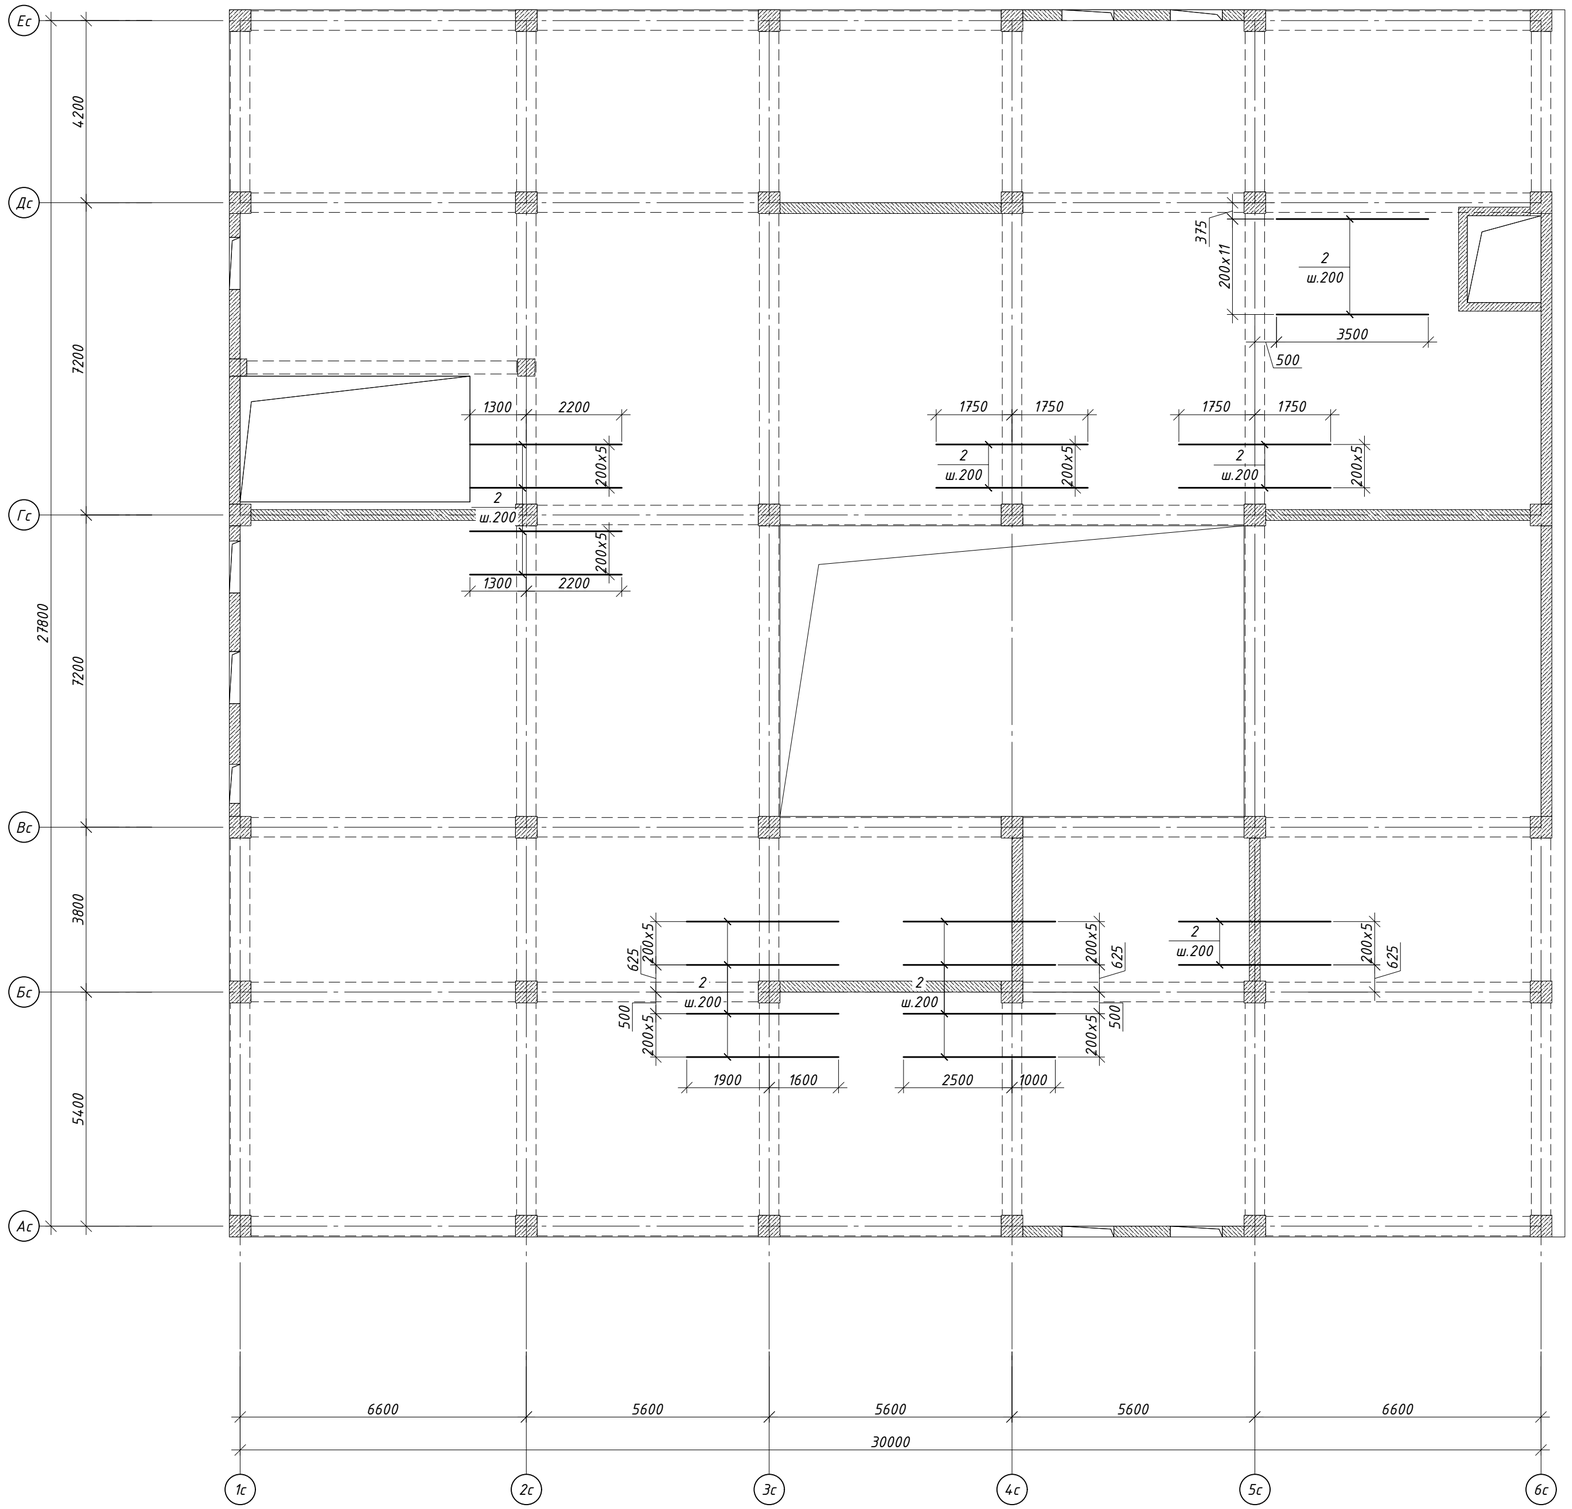


1. Данный лист читать совместно с листами КЖ-2.5 и КЖ-7.22 ... 7.28.
2. Арматура плиты перекрытия стыкуется внахлест.
3. Стыки нижней арматуры выполнять на опоре, стыки верхней арматуры на расстоянии 1/3 - 1/4 пролета от опоры, при этом в одном сечении стыковать не более 50% арматуры.
4. Продольную и поперечную арматуру во всех пересечениях связать вязальной проволокой.
5. Свободные концы основной арматуры у торцов плиты перекрытия должны быть заанкерены "П"-образной скобой (поз. Ск1) при помощи вязальной проволоки (без сварки).
6. Спецификацию см. лист КЖ-7.28

						65П-АИП-2024-1-КЖ	
						Строительство многопрофильной больницы на 250 коек с онкологическим центром и поликлиникой на 350 посещений, по адресу: Медеуский район, г. Алматы	
Изм.	Кол.уч.	Лист	N док.	Подп.	Дата		
						"Блок 1 Секция 1"	Стадия: РП; Лист: 7.24; Листов:
ГКП		Курал М					
Проверил		Кыдырбай А					
Разраб.		Ауез Б				Схема расположения дополнительного арматуры плиты перекрытия Пм-4 нижней зоны по буквенным осям на отм +11.620	АстанаИнжПроект
Н.контроль		Ешенкулова					

Формат А2

Схема расположения дополнительного арматуры плиты перекрытия Пм-4 верхней зоны по буквенным осям на отм +11.620

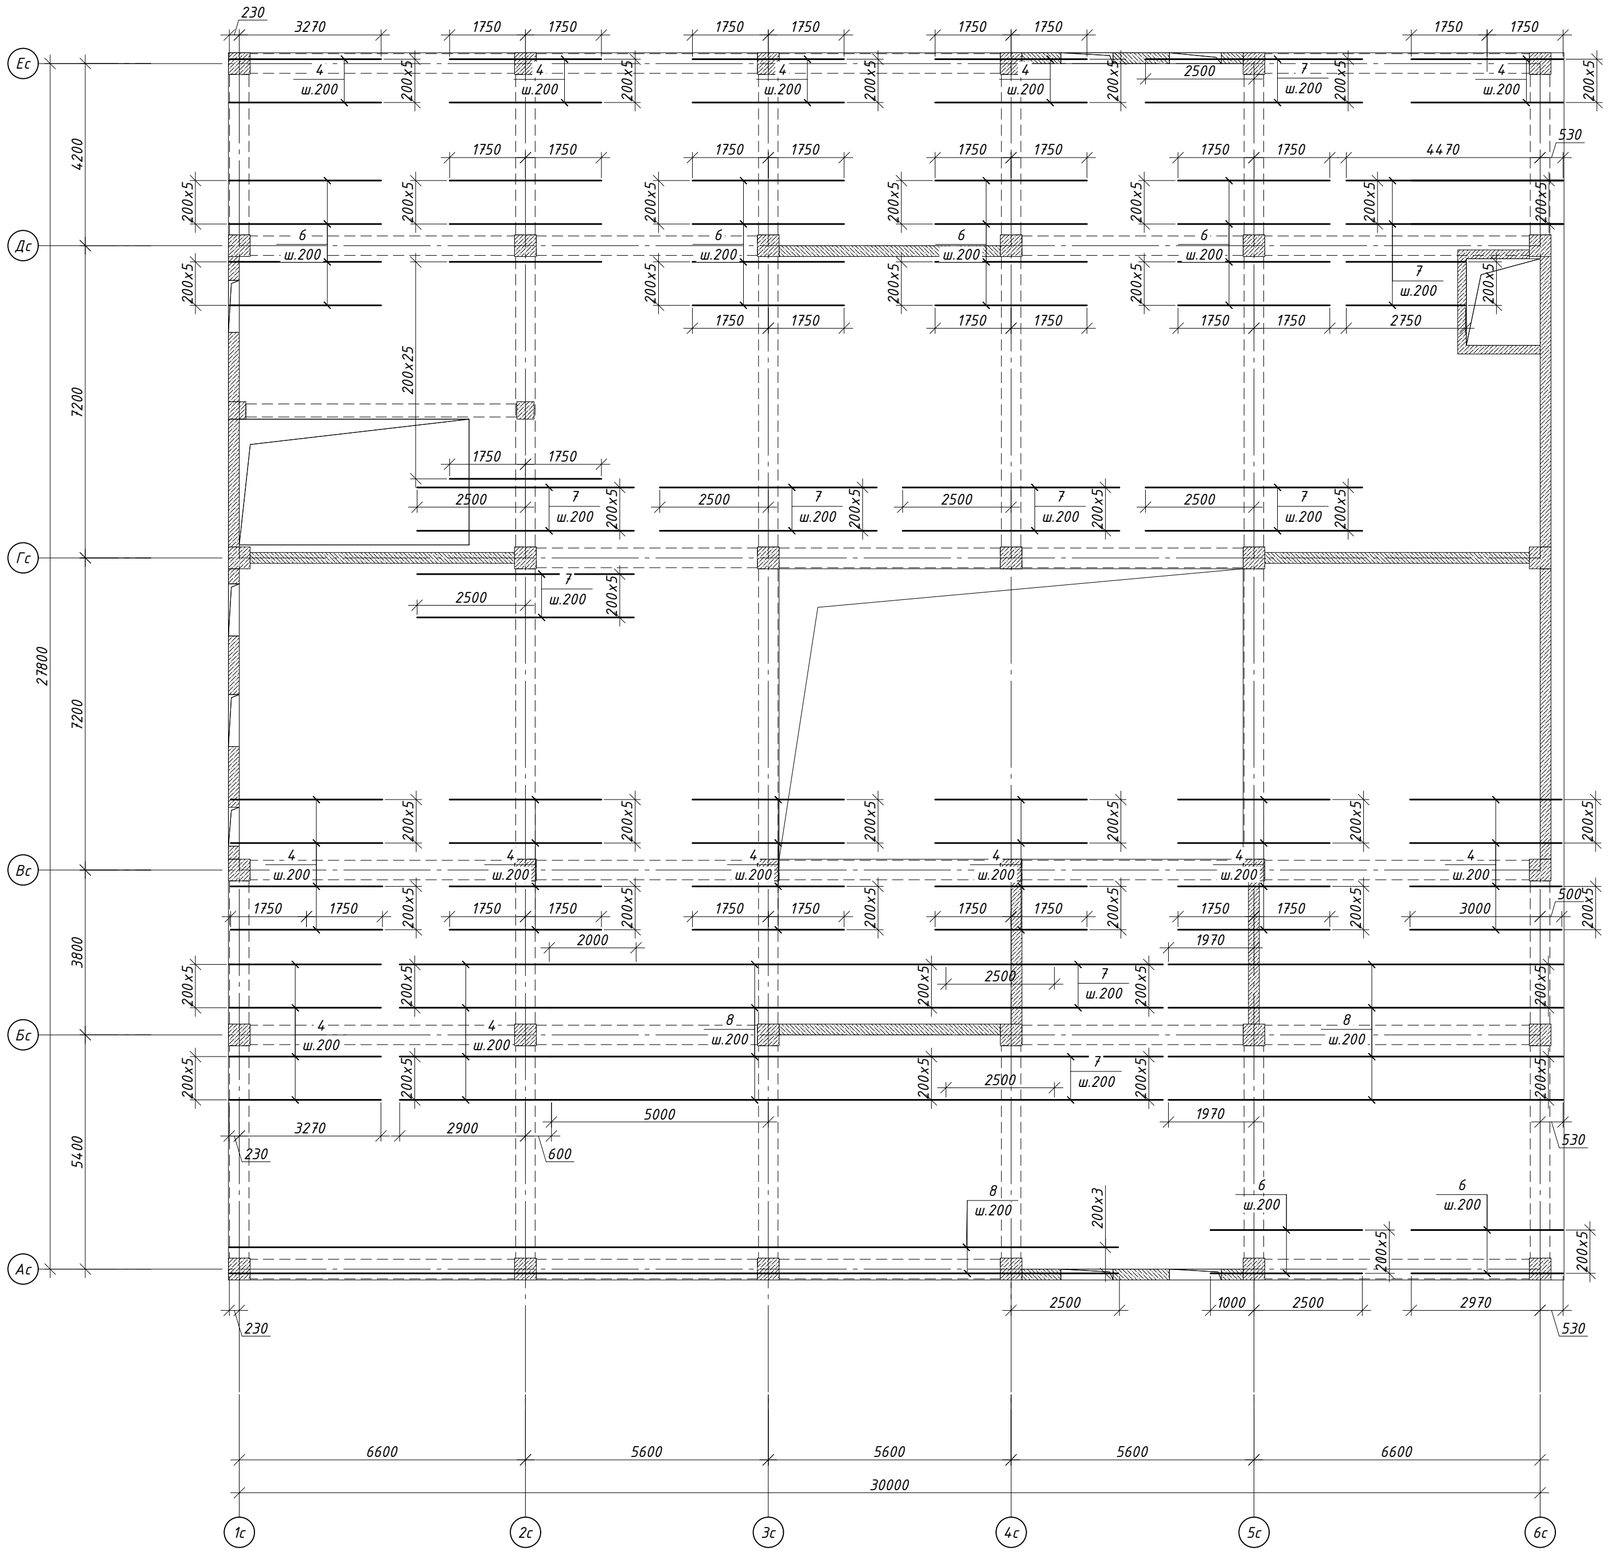


1. Данный лист читать совместно с листами КЖ-2.5 и КЖ-7.22 ... 7.28.
2. Арматура плиты перекрытия стыкуется внахлест.
3. Стыки нижней арматуры выполнять на опоре, стыки верхней арматуры на расстоянии 1/3 - 1/4 пролета от опоры, при этом в одном сечении стыковать не более 50% арматуры.
4. Продольную и поперечную арматуру во всех пересечениях связать вязальной проволокой.
5. Свободные концы основной арматуры у торцов плиты перекрытия должны быть заанкерены "П"-образной скобой (поз. Ск1) при помощи вязальной проволоки (без сварки).
6. Спецификацию см. лист КЖ-7.28

						65П-АИП-2024-1-КЖ
						Строительство многопрофильной больницы на 250 коек с онкологическим центром и поликлиникой на 350 посещений, по адресу: Медеуский район, г. Алматы
Изм.	Кол.уч.	Лист	N док.	Подп.	Дата	
						"Блок 1 Секция 1" — Стадия: РП; Лист: 7.25; Листов:
ГКП		Курал М				Схема расположения дополнительного арматуры плиты перекрытия Пм-4 верхней зоны по буквенным осям на отм +11.620
Проверил		Кыдырбай А				АстанаИнжПроект
Разраб.		Ауез Б				
Н.контроль		Ешенкулова				

Формат А2


Схема расположения дополнительного арматуры плиты перекрытия Пм-4 нижней зоны по цифровым осям на отм +11.620

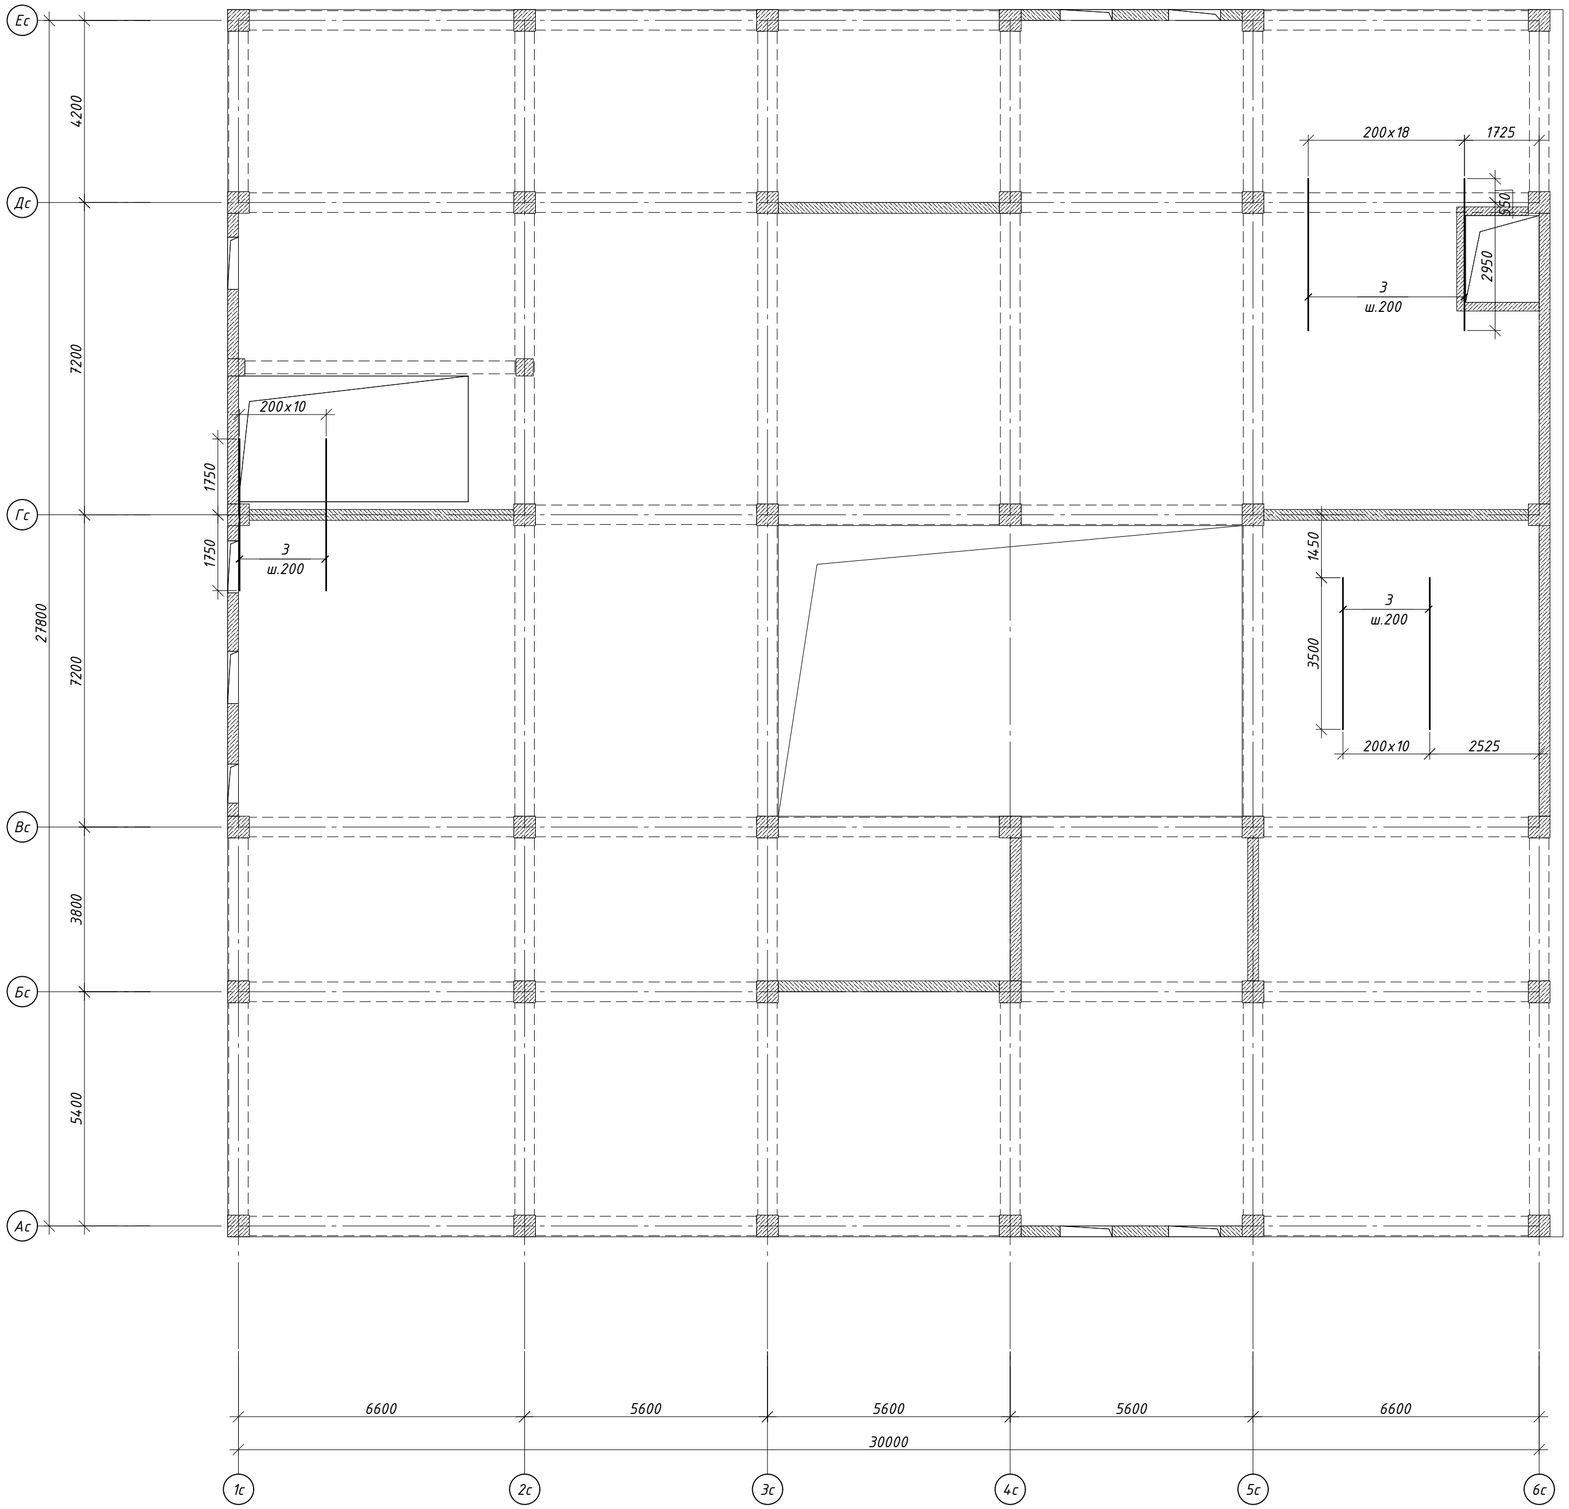

1. Данный лист читать совместно с листами КЖ-2.5 и КЖ-7.22 ... 7.28.
2. Арматура плиты перекрытия стыкуется внахлест.
3. Стыки нижней арматуры выполнять на опоре, стыки верхней арматуры на расстоянии 1/3 - 1/4 пролета от опоры, при этом в одном сечении стыковать не более 50% арматуры.
4. Продольную и поперечную арматуру во всех пересечениях связать вязальной проволокой.
5. Свободные концы основной арматуры у торцов плиты перекрытия должны быть заанкерены "П"-образной скобой (поз. Ск1) при помощи вязальной проволоки (без сварки).
6. Спецификацию см. лист КЖ-7.28

						65П-АИП-2024-1-КЖ
						Строительство многопрофильной больницы на 250 коек с онкологическим центром и поликлиникой на 350 посещений, по адресу: Медеуский район, г. Алматы
Изм.	Кол.уч.	Лист	N док.	Подп.	Дата	
						"Блок 1 Секция 1"
ГКП		Курал М				Стадия: РП; Лист: 7.26; Листов:
Проверил		Кыдырбай А				Схема расположения дополнительного арматуры плиты перекрытия Пм-4 нижней зоны по цифровым осям на отм +11.620
Разраб.		Ауез Б				АстанаИнжПроект
Н.контроль		Ешенкулова				Формат А2

Схема расположения дополнительного арматуры плиты перекрытия Пм-4 верхней зоны по цифровым осям на отм +11.620

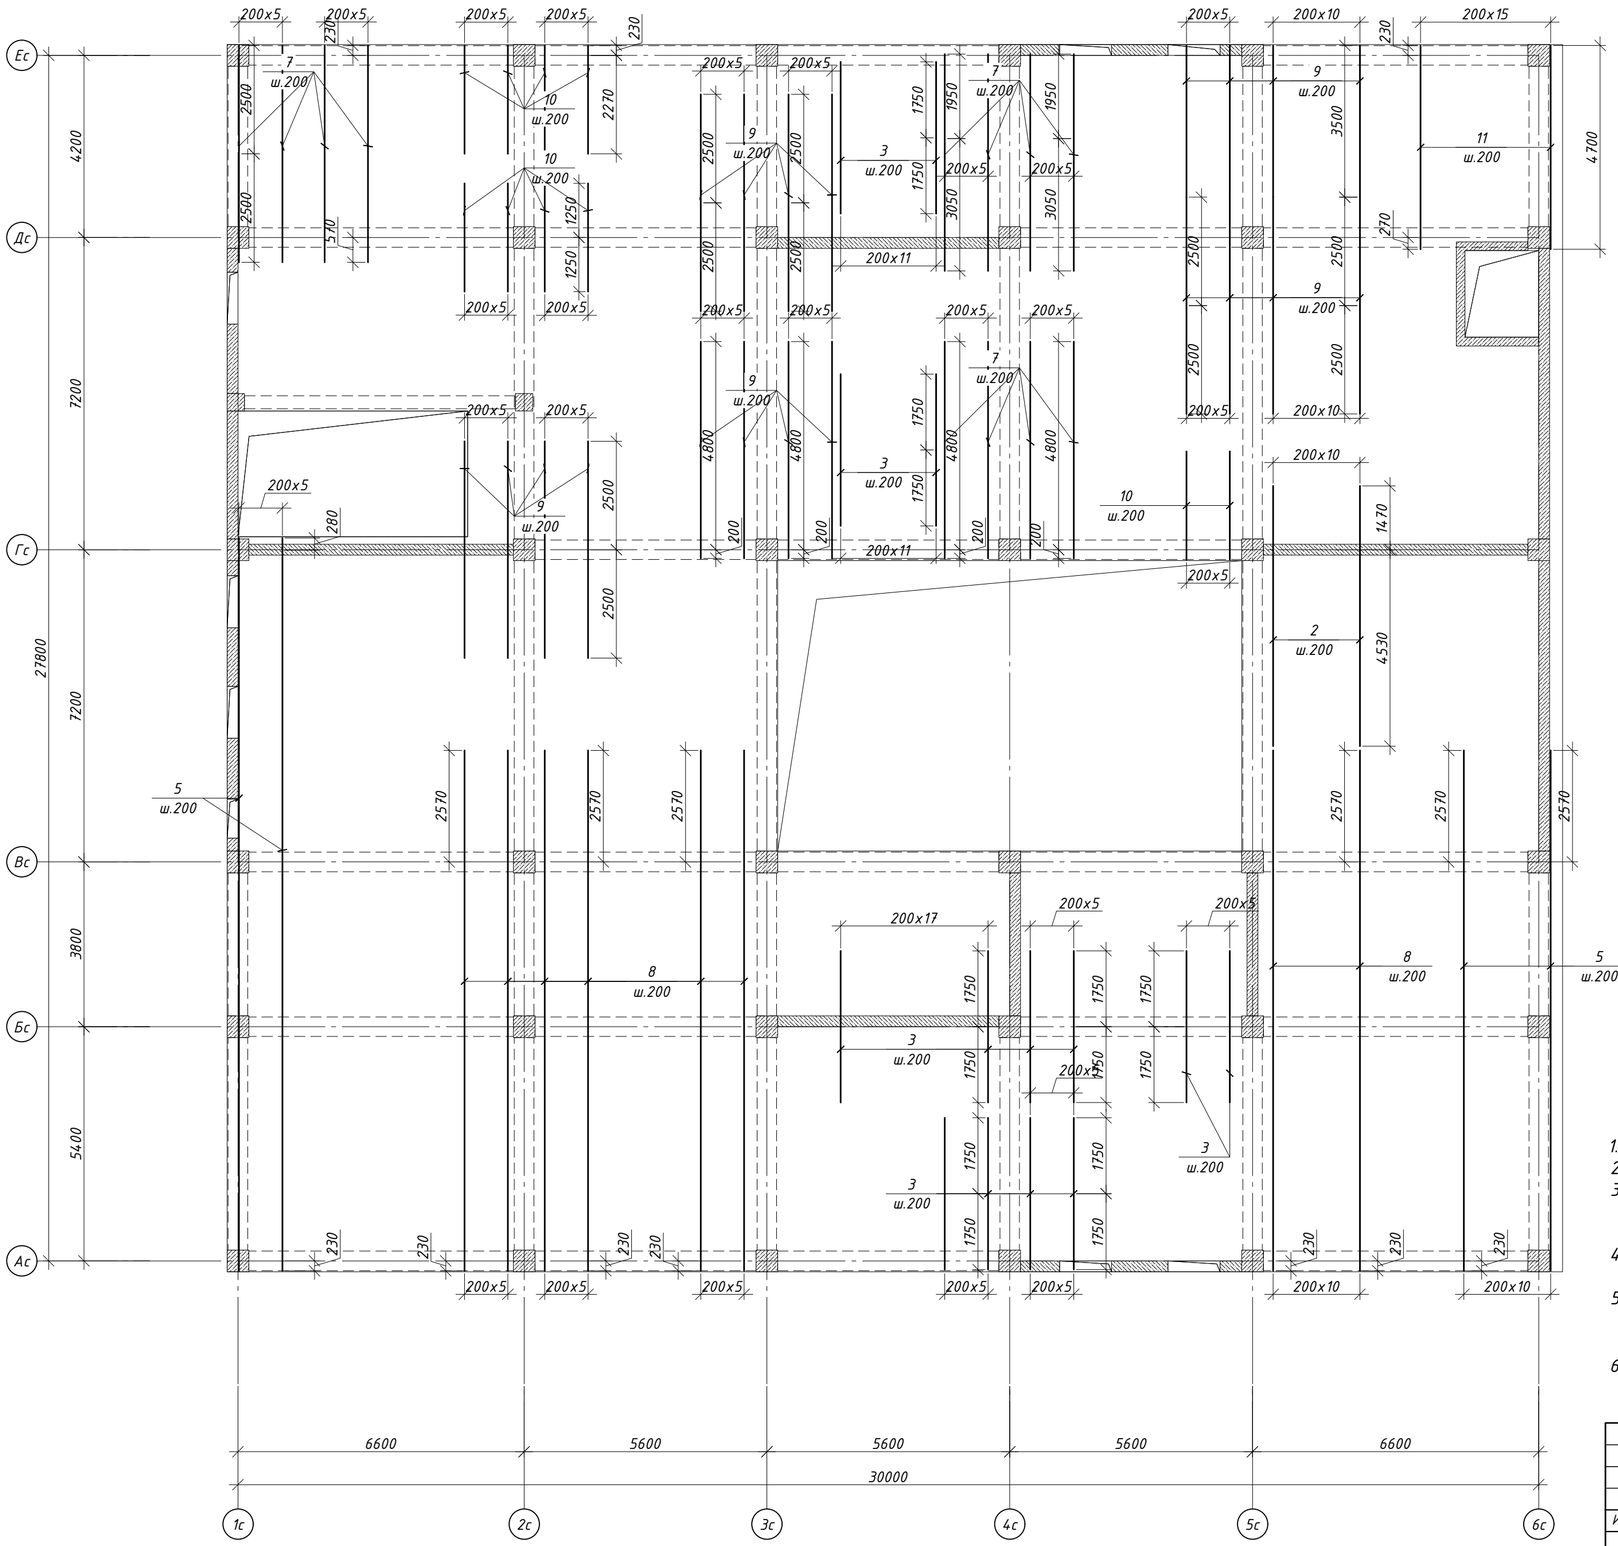


1. Данный лист читать совместно с листами КЖ-2.5 и КЖ-7.22 ... 7.28.
2. Арматура плиты перекрытия стыкуется внахлест.
3. Стыки нижней арматуры выполнять на опоре, стыки верхней арматуры на расстоянии 1/3 - 1/4 пролета от опоры, при этом в одном сечении стыковать не более 50% арматуры.
4. Продольную и поперечную арматуру во всех пересечениях связать вязальной проволокой.
5. Свободные концы основной арматуры у торцов плиты перекрытия должны быть заанкерены "П"-образной скобой (поз. Ск1) при помощи вязальной проволоки (без сварки).
6. Спецификацию см. лист КЖ-7.28


						65П-АИП-2024-1-КЖ	
						Строительство многопрофильной больницы на 250 коек с онкологическим центром и поликлиникой на 350 посещений, по адресу: Медеуский район, г. Алматы	
Изм.	Кол.уч	Лист	N док.	Подп.	Дата		
						"Блок 1 Секция 1"	Стадия: РП; Лист: 7.27; Листов:
ГКП		Курал М				Схема расположения дополнительного арматуры плиты перекрытия Пм-4 верхней зоны по цифровым осям на отм +11.620	АстанаИнжПроект
Проверил		Кыдырбай А					
Разраб.		Ауез Б					
Н.контроль		Ешенкулова					

Формат А2


Детали обрамления отверстий

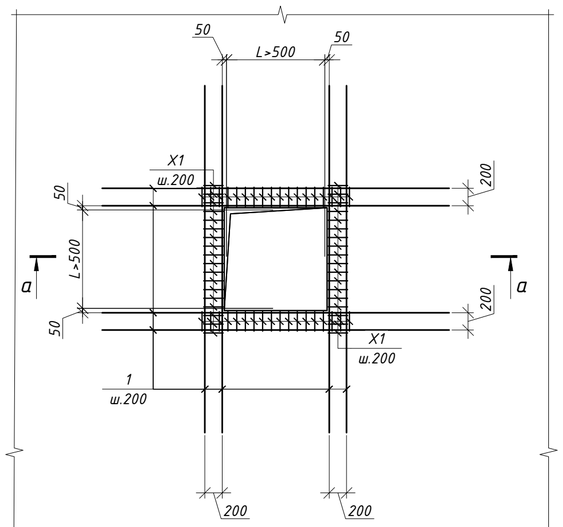

а – а

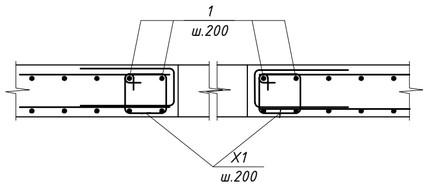

Разрез 1 – 1 (армирование)

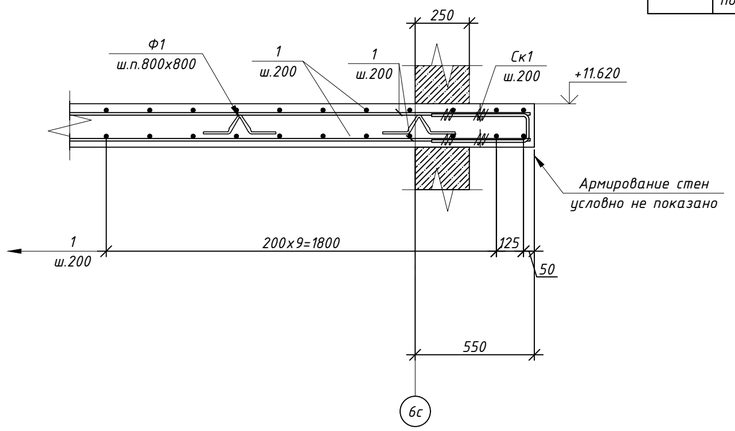

Ведомость деталей

Поз.	Эскиз
Ск1	860; 140; R=2.5ф(≥20ф) R=4ф(≤20ф); 860; по н.г. L=1860
Ф1	300; 116; 116; 300; 300; по н.г. L=1132
Х1	320; 220; 320; 220; по в.г. L=1080

Спецификация элементов

Поз.	Обозначение	Наименование	Кол.	Масса ед.кг	Примечание
		Плита Пм-4			25047.15
1	ГОСТ 34028-2016(214-210-0502-0001)	ф 12 А500С L= пог.м.	15934.80	0.89	14147.14
2	ГОСТ 34028-2016(214-210-0502-0006)	ф 22 А500С L= 6000	11	17.90	196.95
3	ГОСТ 34028-2016(214-210-0502-0001)	ф 12 А500С L= 3500	133	3.11	413.28
4	ГОСТ 34028-2016(214-210-0502-0003)	ф 16 А500С L= 3500	126	5.52	696.05
5	ГОСТ 34028-2016(214-210-0502-0005)	ф 20 А500С L= пог.м.	451.46	2.47	1113.36
6	ГОСТ 34028-2016(214-210-0502-0004)	ф 18 А500С L= 3500	92	6.99	643.22
7	ГОСТ 34028-2016(214-210-0502-0005)	ф 20 А500С L= 5000	108	12.33	1331.72
8	ГОСТ 34028-2016(214-210-0502-0004)	ф 18 А500С L= пог.м.	680.82	2.00	1359.99
9	ГОСТ 34028-2016(214-210-0502-0004)	ф 18 А500С L= 5000	59	9.99	589.29
10	ГОСТ 34028-2016(214-210-0502-0002)	ф 14 А500С L= 2500	30	3.02	90.63
11	ГОСТ 34028-2016(214-210-0502-0005)	ф 20 А500С L= 4700	16	11.59	185.45
Ск1	ГОСТ 34028-2016(214-210-0502-0001)	ф 12 А500С L= 1860	876	1.65	1446.57
Ф1	ГОСТ 34028-2016(214-210-0502-0001)	ф 12 А500С L= 1132	2645	1.01	2658.24
ВП1	ГОСТ 34028-2016(214-210-0502-0003)	ф 16 А500С L= 3650	16	5.76	92.17
ВП2	ГОСТ 34028-2016(214-210-0502-0003)	ф 16 А500С L= 1940	16	3.06	48.99
Х1	ГОСТ 34028-2016(214-210-0101-0002)	ф 8 А 240 L= 1080	80	0.43	34.09
		Материалы:			
	(212-101-0901)	Класс бетона С 20/25 (В25), м³			171.84

Позиции со "*" см. "Ведомость деталей" см. на данном листе.

Ведомость расхода стали, кг


Марка элемента	Изделия арматурные														Всего
	Арматура класса														
	А240			А500С											
	ГОСТ 34028-2016(214-210-0101)			ГОСТ 34028-2016(214-210-0502)											
	ф6	ф8	Итого	ф10	ф12	ф14	ф16	ф18	ф20	ф22	ф25	ф28	ф32	Итого	
Плита +11.620	---	34.09	34.09	---	18665.23	90.63	837.21	2592.50	2630.54	196.95	---	---	---	25013.06	25047.15

1. Данный лист читать совместно с листами КЖ-2.5 и КЖ-7.22 ... 7.28.
2. Арматура плиты перекрытия стыкуется внахлест.
3. Стыки нижней арматуры выполнять на опоре, стыки верхней арматуры на расстоянии 1/3 – 1/4 пролета от опоры, при этом в одном сечении стыковать не более 50% арматуры.
4. Продольную и поперечную арматуру во всех пересечениях связать вязальной проволокой.
5. Свободные концы основной арматуры у торцов плиты перекрытия должны быть заанкерены "П"-образной скобой (поз. Ск1) при помощи вязальной проволоки (без сварки).
6. Спецификацию см. лист КЖ-7.28


Изм.	Кол.уч	Лист	N док.	Подп.	Дата	65П-АИП-2024-1-КЖ			
						Строительство многопрофильной больницы на 250 коек с онкологическим центром и поликлиникой на 350 посещений, по адресу: Медеуский район, г. Алматы			
						"Блок 1 Секция 1"	Стадия	Лист	Листов
							РП	7.28	
ГКП		Курал М				Спецификация плиты перекрытия Пм-4 на отм +11.620	АстанаИнжПроект		
Проверил		Кыдырбай А							
Разраб.		Ауез Б							
Н.контроль		Ешенкулова							

Формат А2


Опалубочный чертеж плиты перекрытия Пм-5 на отм. +14.020

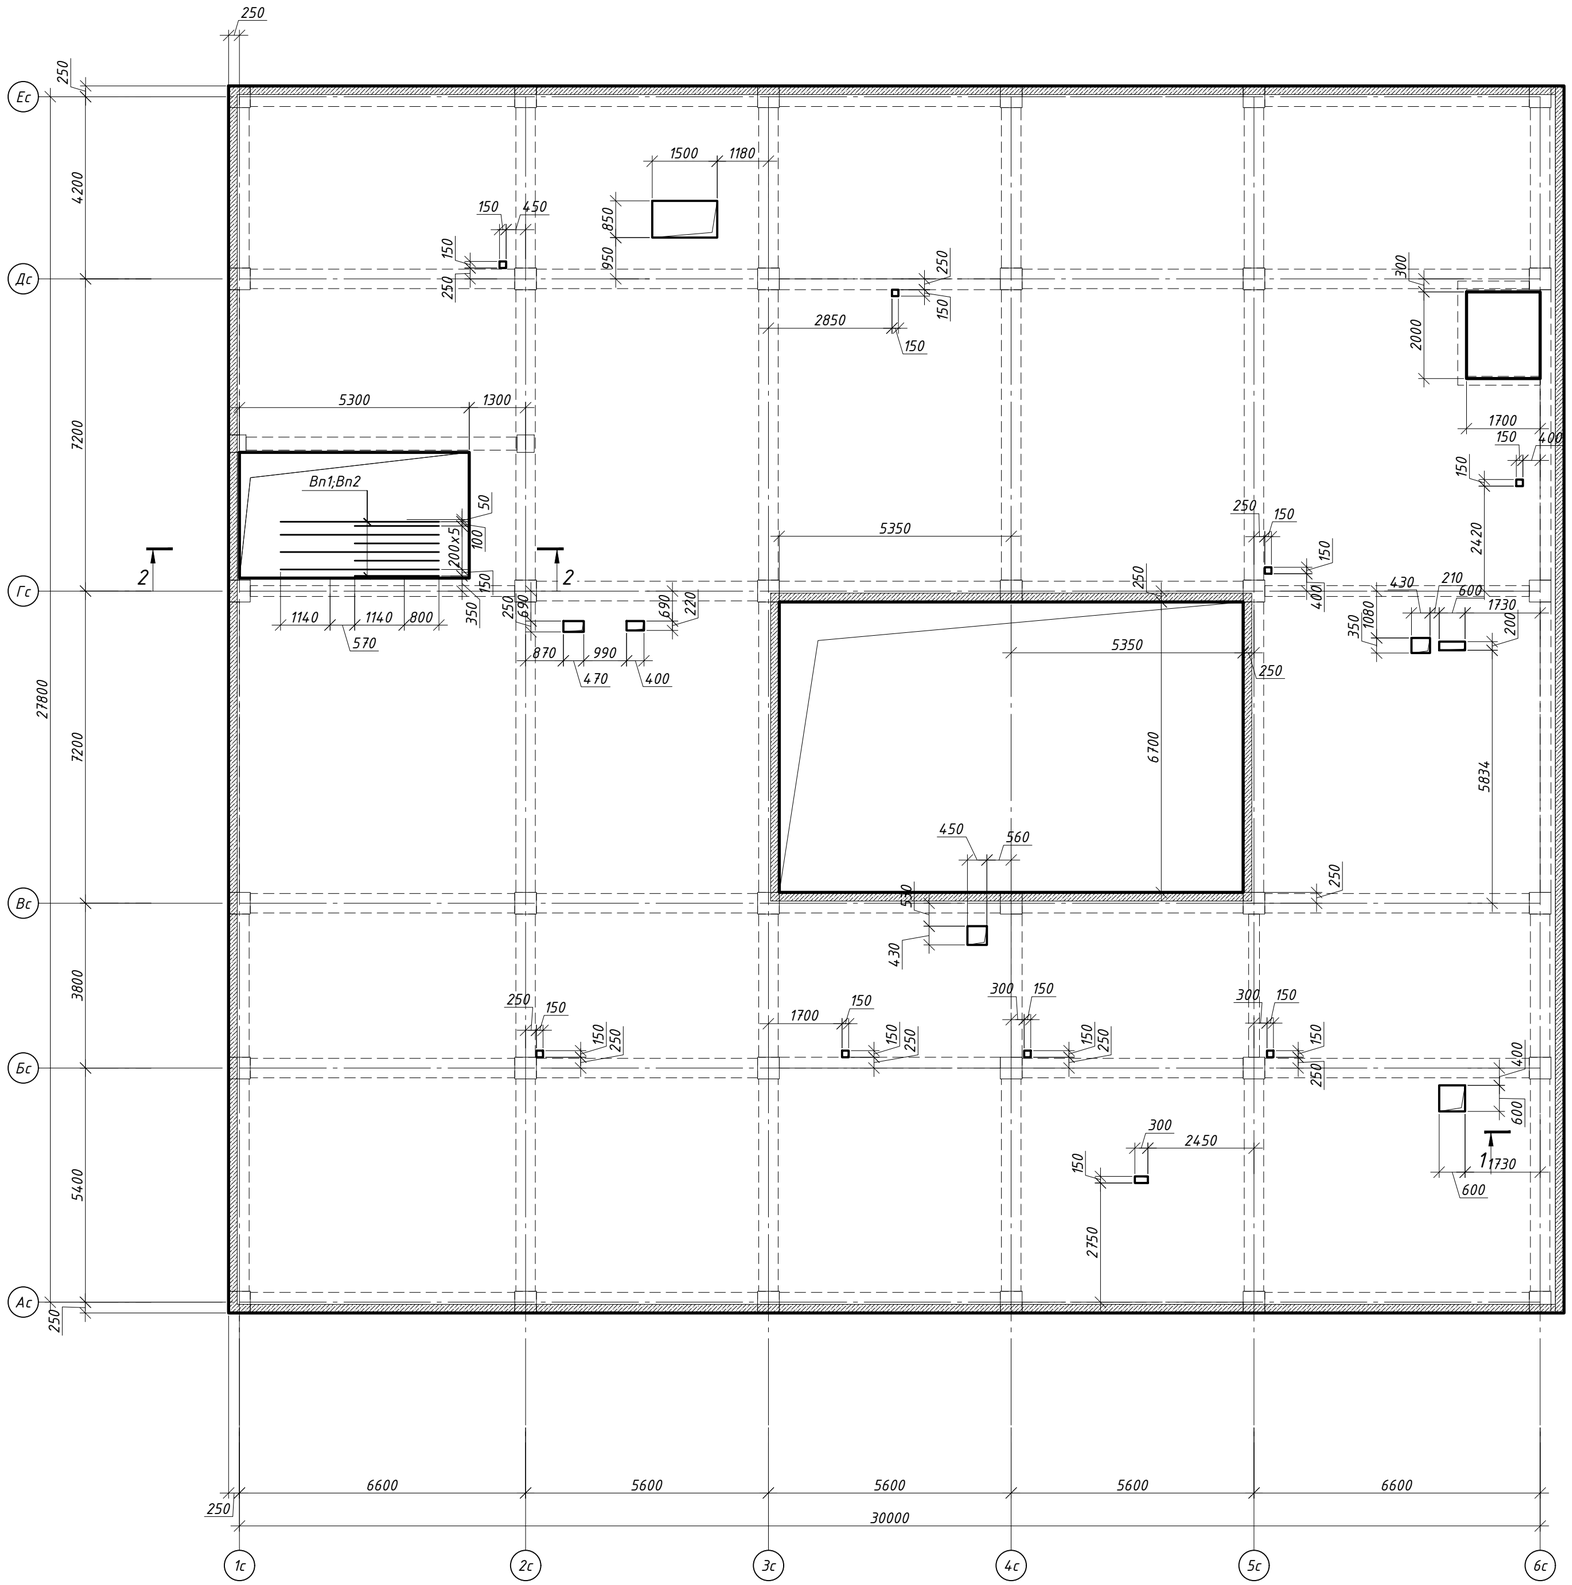

Разрез 1 - 1 (Опалубка)
М 1:50

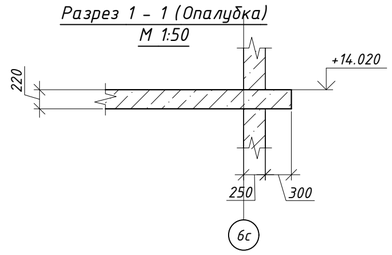

Разрез 2 - 2

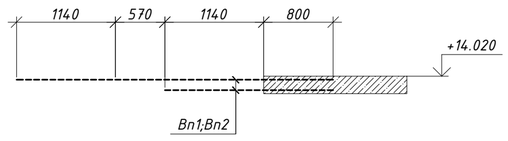


1. Данный лист читать совместно с листами КЖ-2.6 и КЖ-7.29 ... 7.35.
2. Арматура плиты перекрытия стыкуется внахлест.
3. Стыки нижней арматуры выполнять на опоре, стыки верхней арматуры на расстоянии 1/3 - 1/4 пролета от опоры, при этом в одном сечении стыковать не более 50% арматуры.
4. Продольную и поперечную арматуру во всех пересечениях связать вязальной проволокой.
5. Свободные концы основной арматуры у торцов плиты перекрытия должны быть заанкерены "П"-образной скобой (поз. Ск1) при помощи вязальной проволоки (без сварки).
6. Спецификацию см. лист КЖ-7.35

						65П-АИП-2024-1-КЖ
						Строительство многопрофильной больницы на 250 коек с онкологическим центром и поликлиникой на 350 посещений, по адресу: Медеуский район, г. Алматы
Изм.	Кол.уч.	Лист	N док.	Подп.	Дата	
						"Блок 1 Секция 1" — Стадия: РП; Лист: 7.29; Листов:
ГКП		Курал М				Опалубочный чертеж плиты перекрытия Пм-5 на отм.+14.020
Проверил		Кыдырбай А				АстанаИнжПроект
Разраб.		Ауез Б				
Н.контроль		Ешенкулова				

Формат А2

Схема расположения основных арматуры плиты перекрытия Пм-5 на отм +14.020

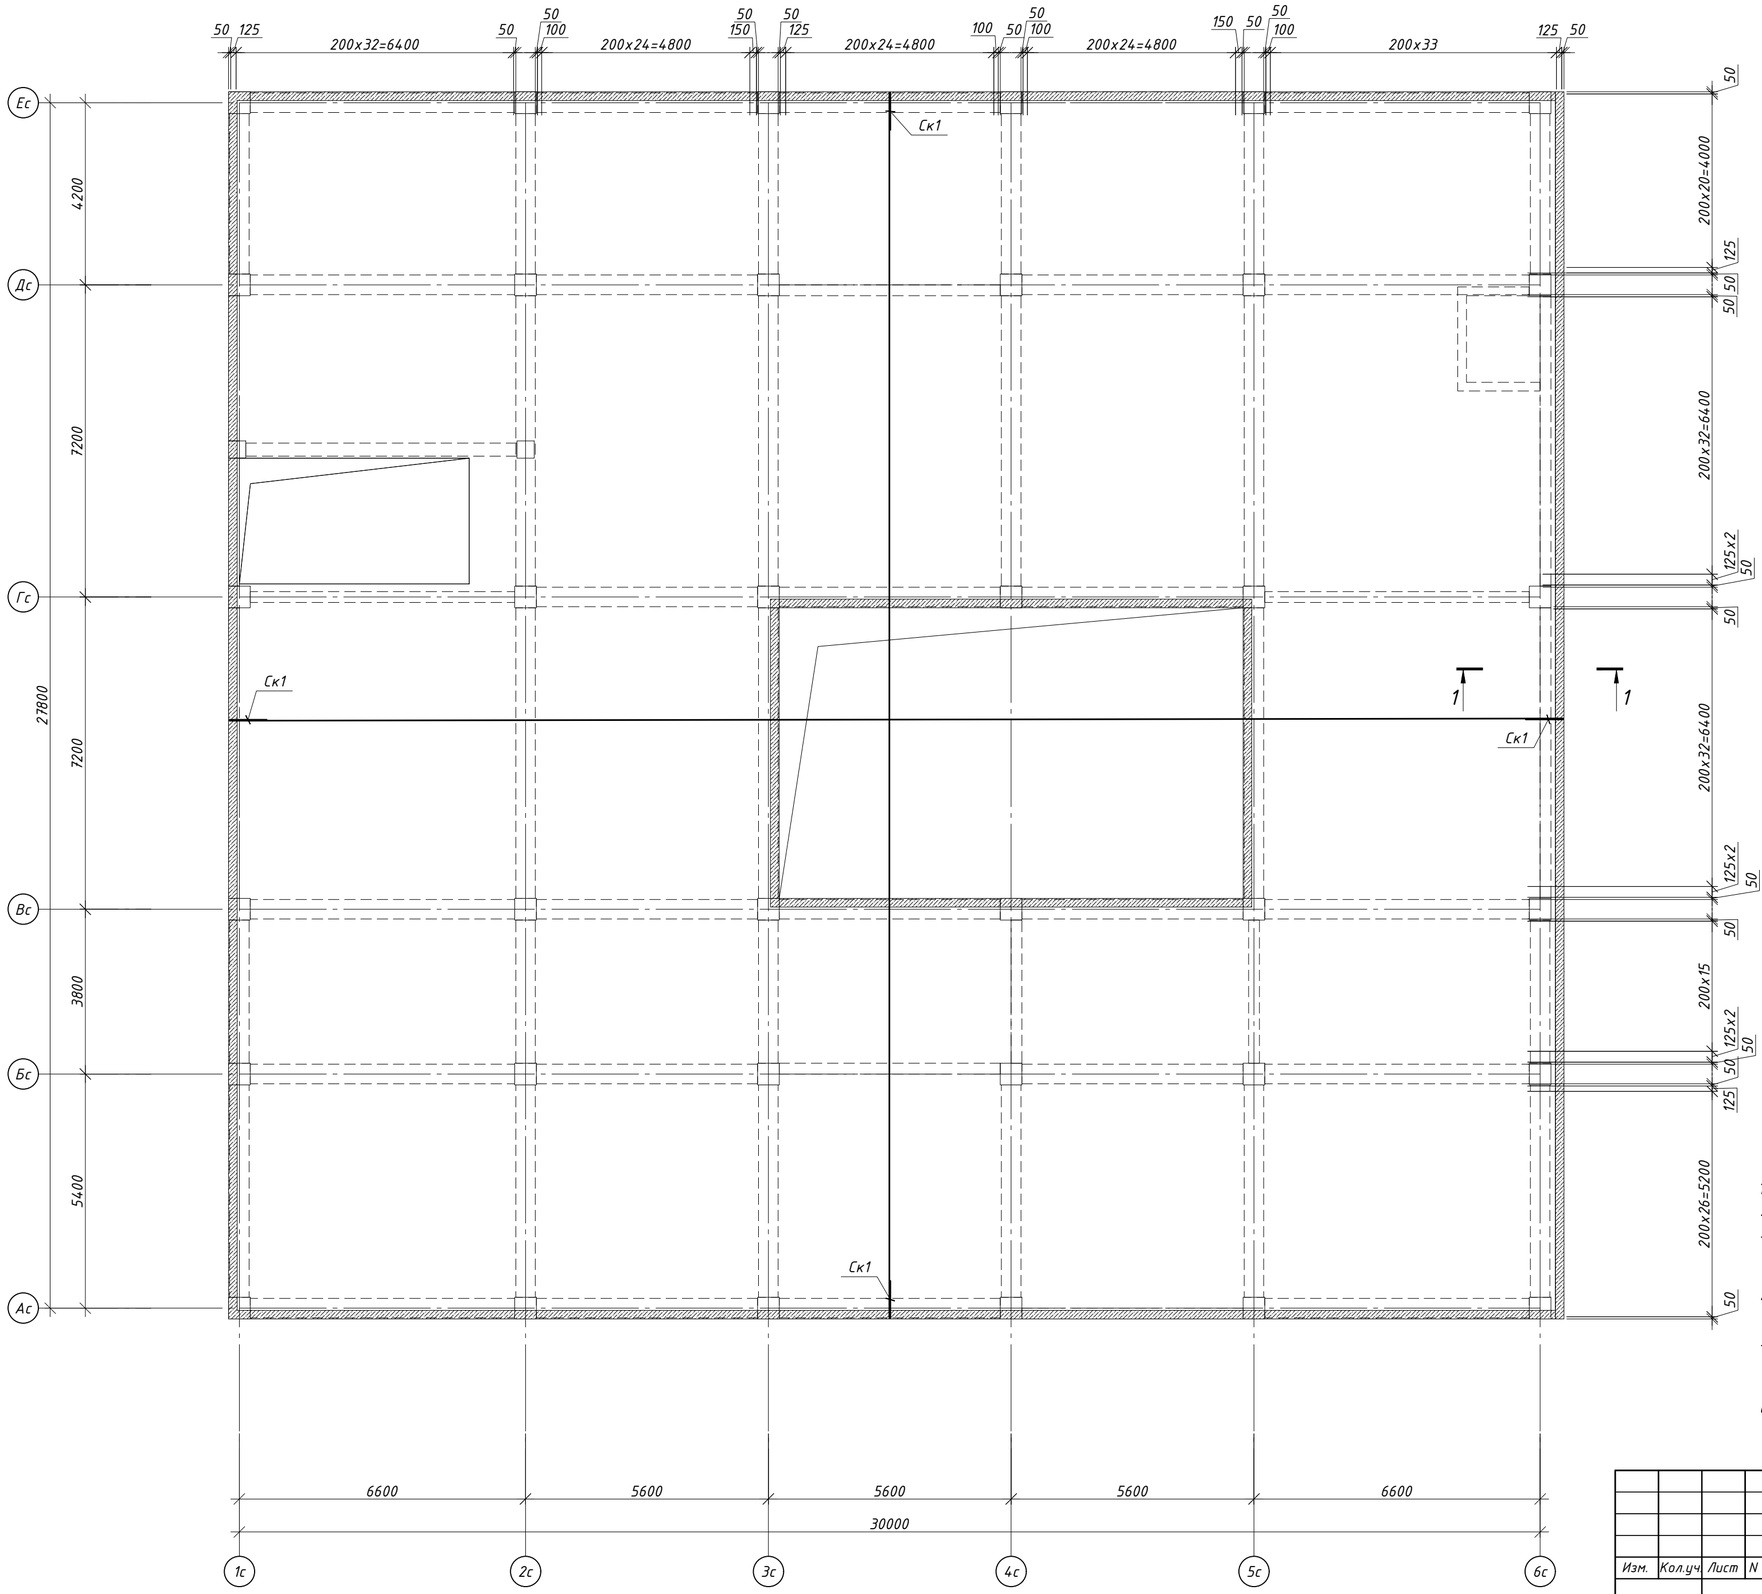


1. Данный лист читать совместно с листами КЖ-2.6 и КЖ-7.29 ... 7.35.
2. Арматура плиты перекрытия стыкуется внахлест.
3. Стыки нижней арматуры выполнять на опоре, стыки верхней арматуры на расстоянии 1/3 - 1/4 пролета от опоры, при этом в одном сечении стыковать не более 50% арматуры.
4. Продольную и поперечную арматуру во всех пересечениях связать вязальной проволокой.
5. Свободные концы основной арматуры у торцов плиты перекрытия должны быть заанкерены "П"-образной скобой (поз. Ск1) при помощи вязальной проволоки (без сварки).
6. Спецификацию см. лист КЖ-7.35

Изм.	Кол.уч.	Лист	N док.	Подп.	Дата	65П-АИП-2024-1-КЖ		
						Строительство многопрофильной больницы на 250 коек с онкологическим центром и поликлиникой на 350 посещений, по адресу: Медеуский район, г. Алматы		
ГКП		Курал М				"Блок 1 Секция 1"	Стадия: РП	Лист: 7.30 / Листов:
Проверил		Кыдырбай А				Схема расположения основных арматуры плиты перекрытия Пм-5 на отм +14.020	АстанаИнжПроект	
Разраб.		Ауез Б						
Н.контроль		Ешенкулова						

Формат А2

Схема расположения дополнительного арматуры плиты перекрытия Пм-5 нижней зоны по буквенным осям на отм +14.020

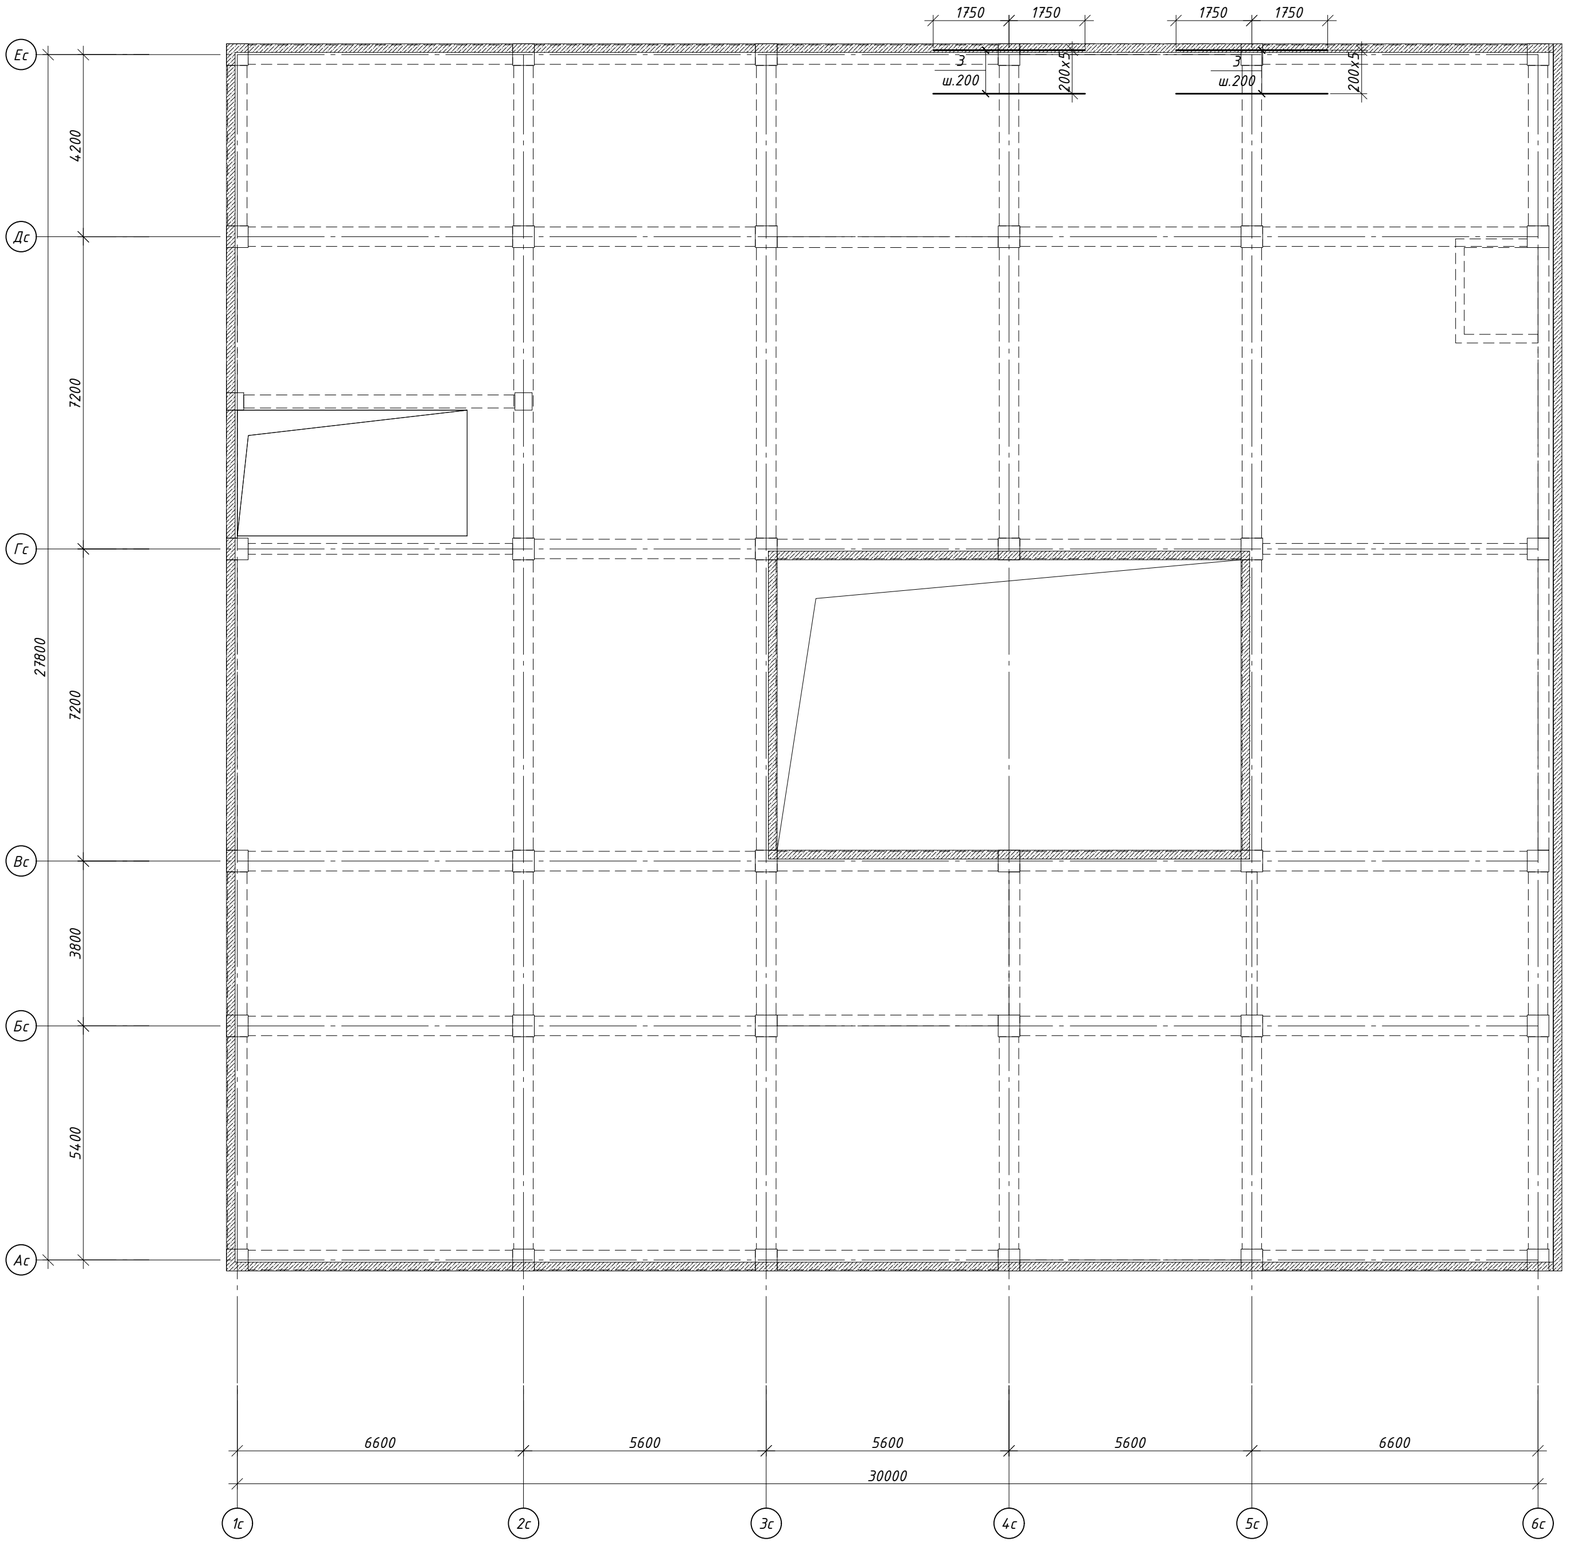


1. Данный лист читать совместно с листами КЖ-2.6 и КЖ-7.29 ... 7.35.
2. Арматура плиты перекрытия стыкуется внахлест.
3. Стыки нижней арматуры выполнять на опоре, стыки верхней арматуры на расстоянии 1/3 - 1/4 пролета от опоры, при этом в одном сечении стыковать не более 50% арматуры.
4. Продольную и поперечную арматуру во всех пересечениях связать вязальной проволокой.
5. Свободные концы основной арматуры у торцов плиты перекрытия должны быть заанкерены "П"-образной скобой (поз. Ск1) при помощи вязальной проволоки (без сварки).
6. Спецификацию см. лист КЖ-7.35

						65П-АИП-2024-1-КЖ
						Строительство многопрофильной больницы на 250 коек с онкологическим центром и поликлиникой на 350 посещений, по адресу: Медеуский район, г. Алматы
Изм.	Кол.уч.	Лист	N док.	Подп.	Дата	
						"Блок 1 Секция 1" — Стадия: РП; Лист: 7.31; Листов:
ГКП		Курал М				Схема расположения дополнительного арматуры плиты перекрытия Пм-5 нижней зоны по буквенным осям на отм +14.020
Проверил		Кыдырбай А				АстанаИнжПроект
Разраб.		Ауез Б				
Н.контроль		Ешенкулова				

Формат А2

Схема расположения дополнительного арматуры плиты перекрытия Пм-5 верхней зоны по буквенным осям на отм +14.020

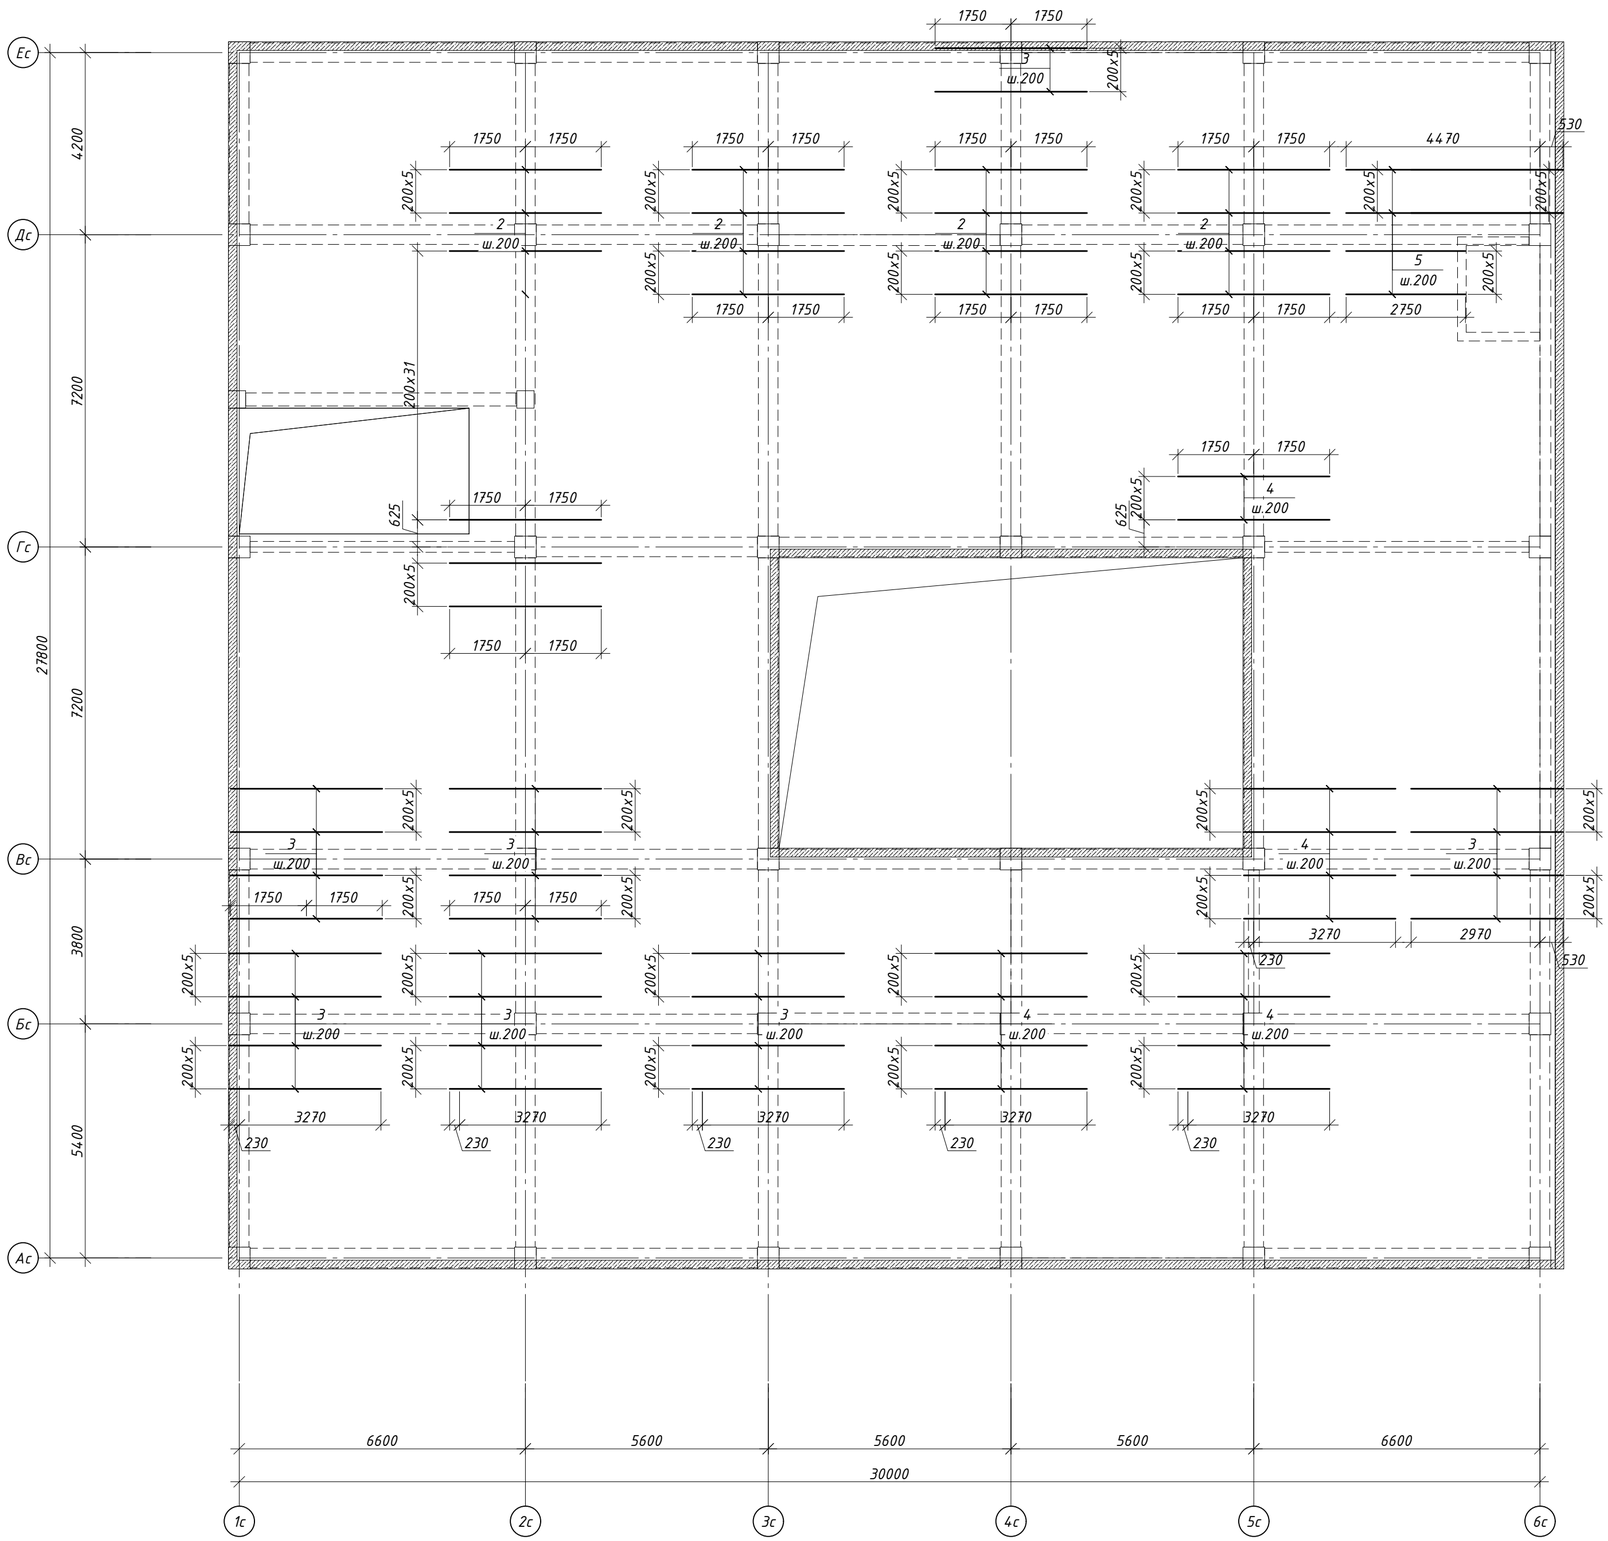


1. Данный лист читать совместно с листами КЖ-2.6 и КЖ-7.29 ... 7.35.
2. Арматура плиты перекрытия стыкуется внахлест.
3. Стыки нижней арматуры выполнять на опоре, стыки верхней арматуры на расстоянии 1/3 - 1/4 пролета от опоры, при этом в одном сечении стыковать не более 50% арматуры.
4. Продольную и поперечную арматуру во всех пересечениях связать вязальной проволокой.
5. Свободные концы основной арматуры у торцов плиты перекрытия должны быть заанкерены "П"-образной скобой (поз. Ск1) при помощи вязальной проволоки (без сварки).
6. Спецификацию см. лист КЖ-7.35

						65П-АИП-2024-1-КЖ
						Строительство многопрофильной больницы на 250 коек с онкологическим центром и поликлиникой на 350 посещений, по адресу: Медеуский район, г. Алматы
Изм.	Кол.уч.	Лист	N док.	Подп.	Дата	
						"Блок 1 Секция 1" — Стадия: РП; Лист: 7.32; Листов:
ГКП		Курал М				Схема расположения дополнительного арматуры плиты перекрытия Пм-5 верхней зоны по буквенным осям на отм +14.020
Проверил		Кыдырбай А				АстанаИнжПроект
Разраб.		Ауез Б				
Н.контроль		Ешенкулова				

Формат А2

Схема расположения дополнительного арматуры плиты перекрытия Пм-5 нижней зоны по цифровым осям на отм +14.020

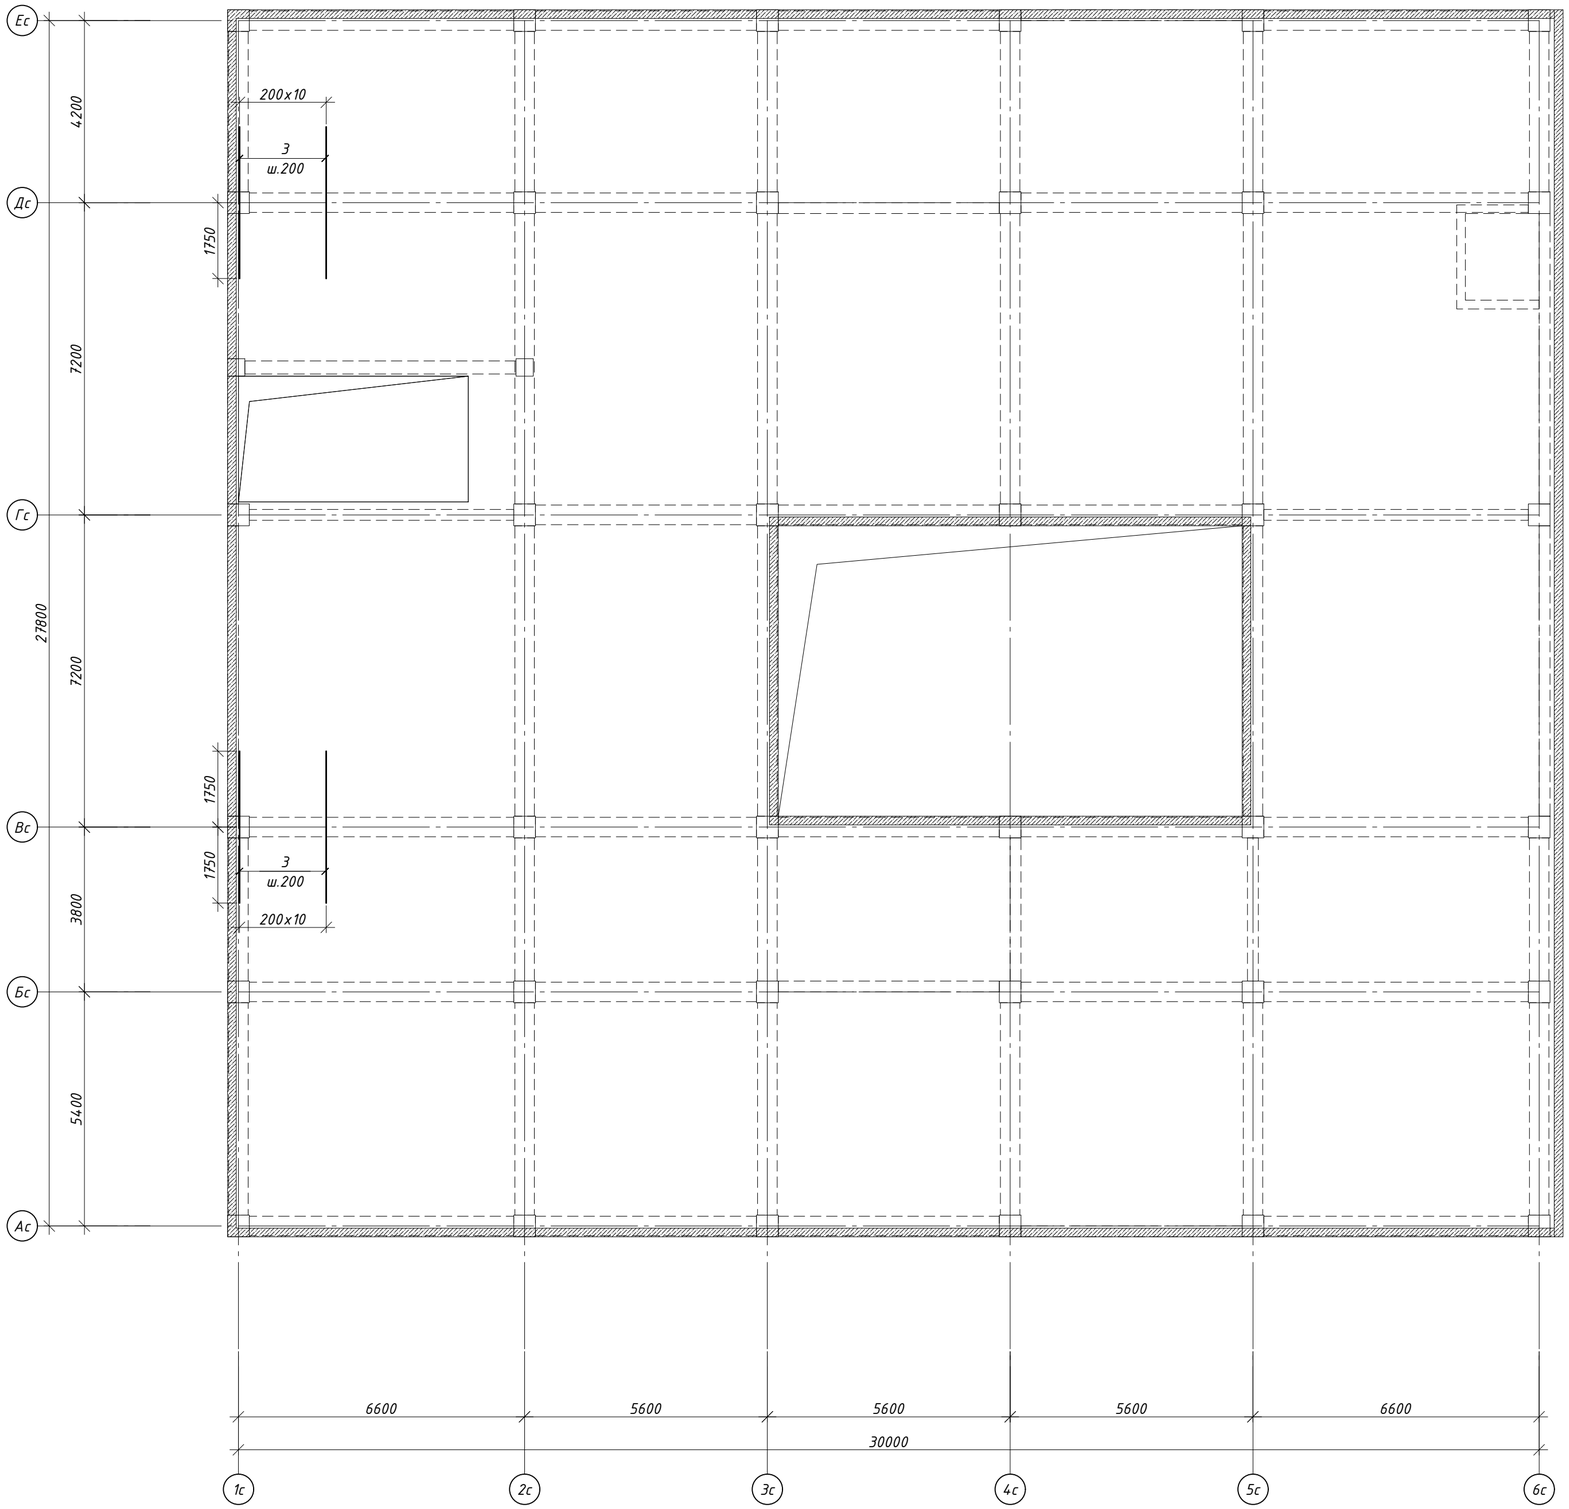


1. Данный лист читать совместно с листами КЖ-2.6 и КЖ-7.29 ... 7.35.
2. Арматура плиты перекрытия стыкуется внахлест.
3. Стыки нижней арматуры выполнять на опоре, стыки верхней арматуры на расстоянии 1/3 - 1/4 пролета от опоры, при этом в одном сечении стыковать не более 50% арматуры.
4. Продольную и поперечную арматуру во всех пересечениях связать вязальной проволокой.
5. Свободные концы основной арматуры у торцов плиты перекрытия должны быть заанкерены "П"-образной скобой (поз. Ск1) при помощи вязальной проволоки (без сварки).
6. Спецификацию см. лист КЖ-7.35

						65П-АИП-2024-1-КЖ
						Строительство многопрофильной больницы на 250 коек с онкологическим центром и поликлиникой на 350 посещений, по адресу: Медеуский район, г. Алматы
Изм.	Кол.уч.	Лист	N док.	Подп.	Дата	
						"Блок 1 Секция 1"
ГКП		Курал М				Стадия: РП; Лист: 7.33; Листов:
Проверил		Кыдырбай А				Схема расположения дополнительного арматуры плиты перекрытия Пм-5 нижней зоны по цифровым осям на отм +14.020
Разраб.		Ауез Б				АстанаИнжПроект
Н.контроль		Ешенкулова				

Формат А2

Схема расположения дополнительного арматуры плиты перекрытия Пм-5 верхней зоны по цифровым осям на отм +14.020

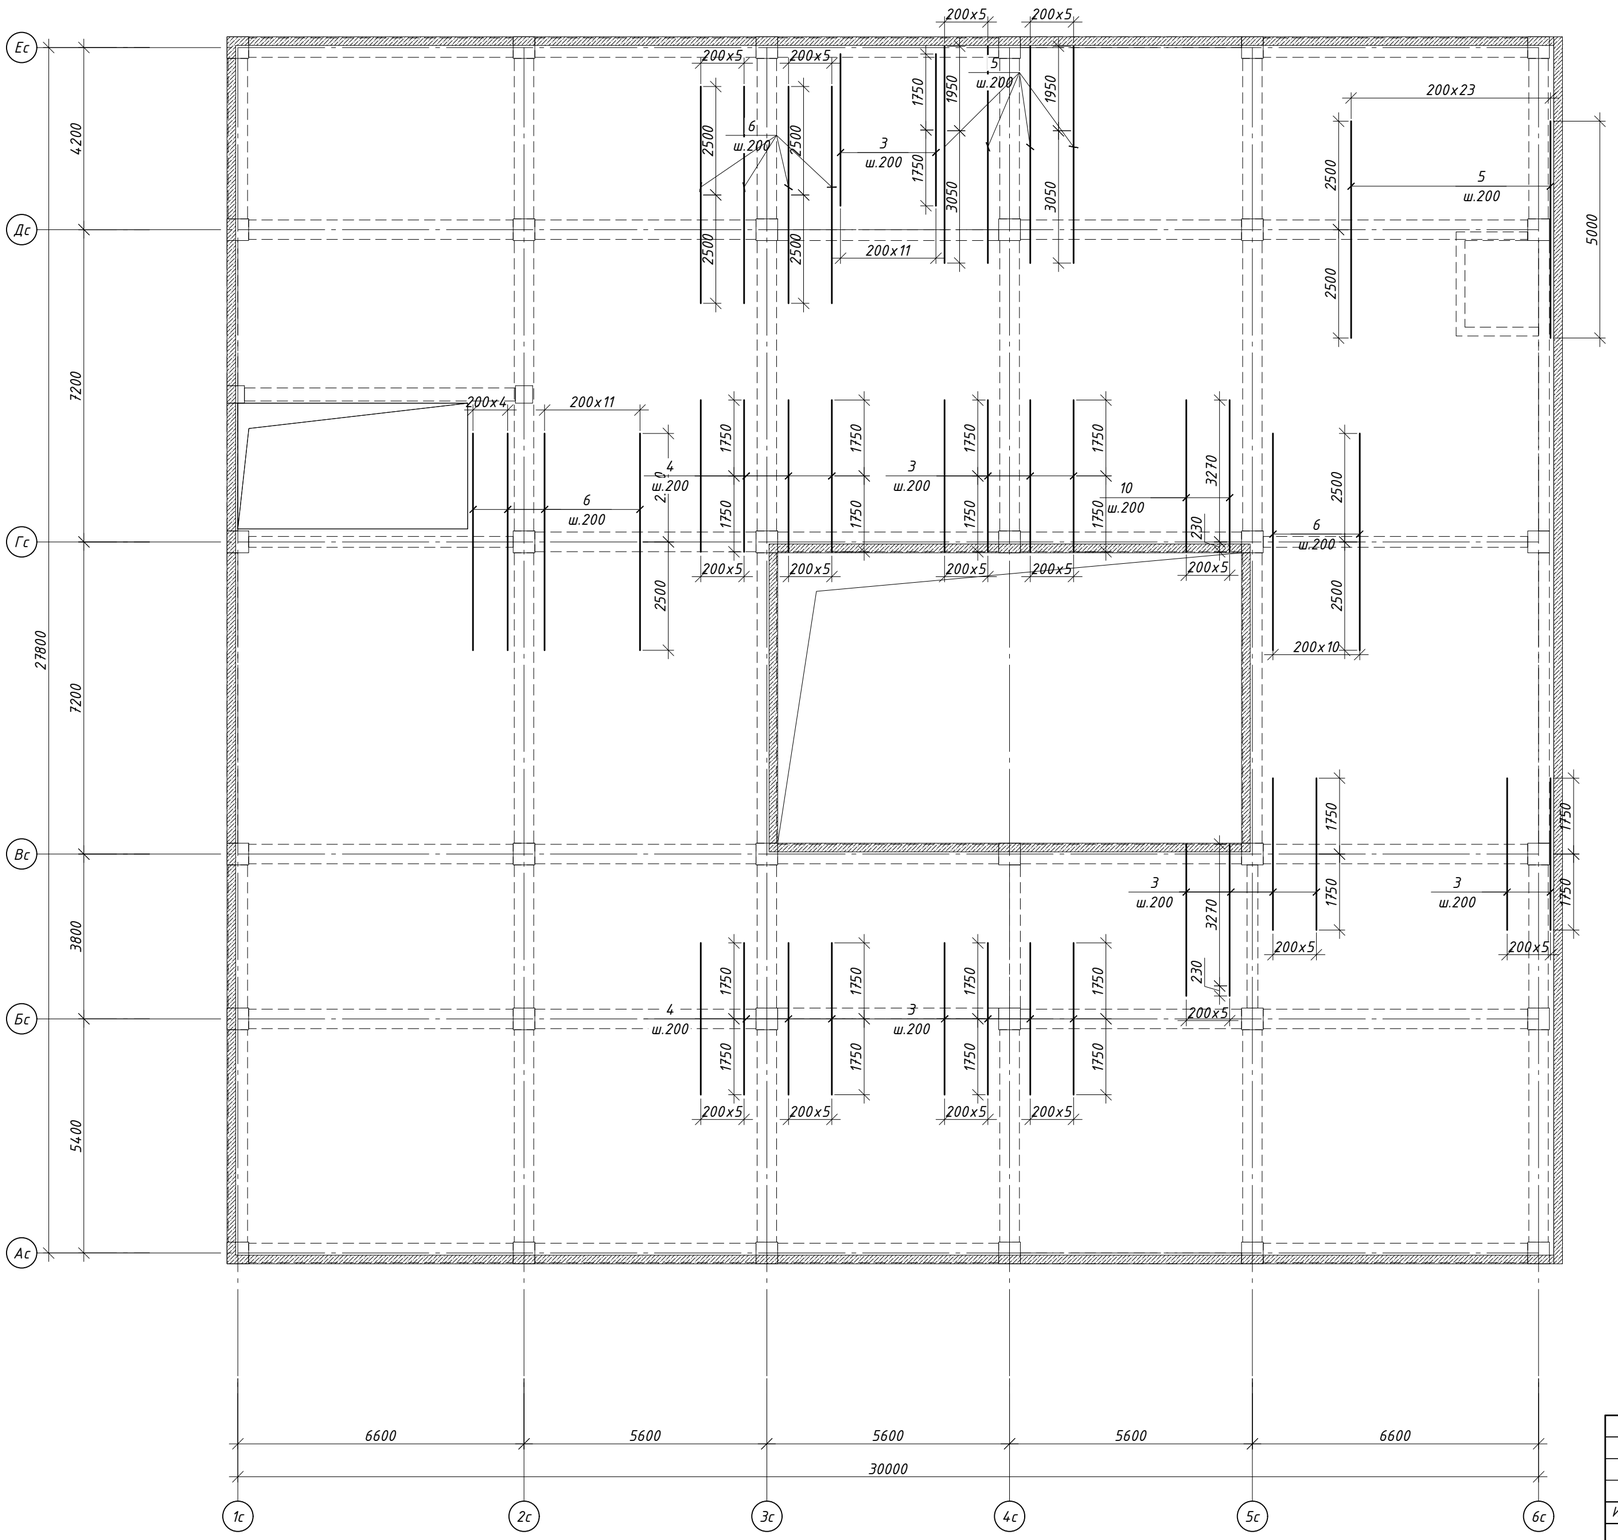


1. Данный лист читать совместно с листами КЖ-2.6 и КЖ-7.29 ... 7.35.
2. Арматура плиты перекрытия стыкуется внахлест.
3. Стыки нижней арматуры выполнять на опоре, стыки верхней арматуры на расстоянии 1/3 - 1/4 пролета от опоры, при этом в одном сечении стыковать не более 50% арматуры.
4. Продольную и поперечную арматуру во всех пересечениях связать вязальной проволокой.
5. Свободные концы основной арматуры у торцов плиты перекрытия должны быть заанкерены "П"-образной скобой (поз. Ск1) при помощи вязальной проволоки (без сварки).
6. Спецификацию см. лист КЖ-7.35

						65П-АИП-2024-1-КЖ
						Строительство многопрофильной больницы на 250 коек с онкологическим центром и поликлиникой на 350 посещений, по адресу: Медеуский район, г. Алматы
Изм.	Кол.уч.	Лист	N док.	Подп.	Дата	
						"Блок 1 Секция 1"
ГКП		Курал М				Стадия: РП; Лист: 7.34; Листов:
Проверил		Кыдырбай А				Схема расположения дополнительного арматуры плиты перекрытия Пм-5 верхней зоны по цифровым осям на отм +14.020
Разраб.		Ауез Б				АстанаИнжПроект
Н.контроль		Ешенкулова				


Формат А2

Детали обрамления отверстий

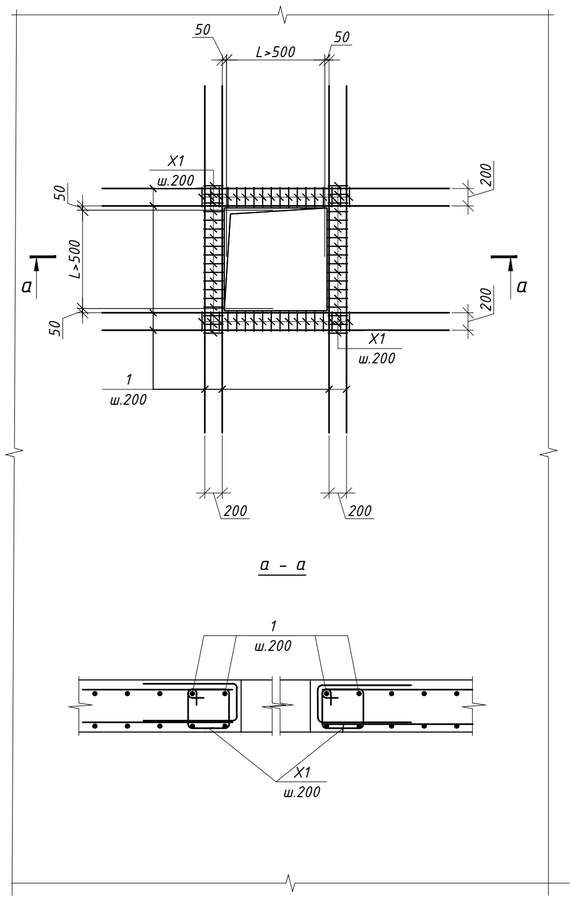

а – а

Разрез 1 – 1 (армирование)

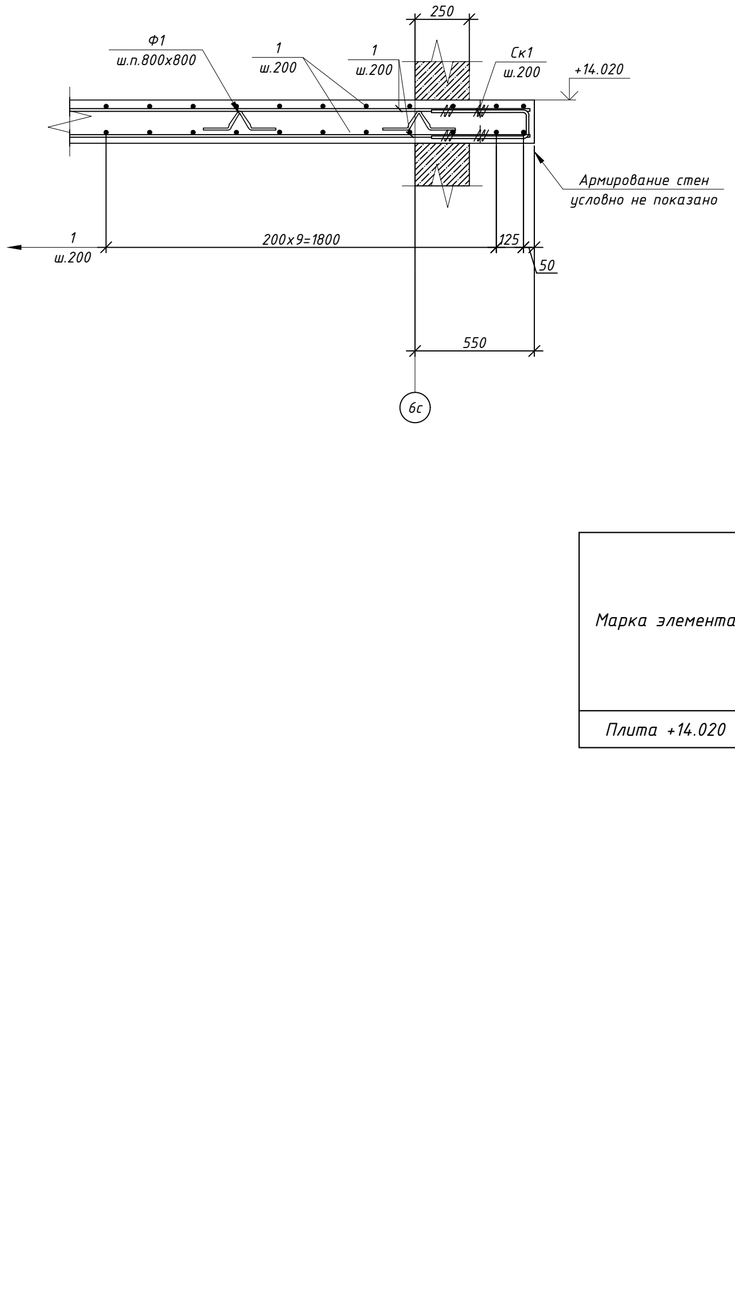

Ведомость деталей

Поз.	Эскиз
Ск1	860; 140; Rs≥250(≥20Ø); R≥40Ø(≥20Ø); 860; по н.г. L=1860
Ф1	300; 116; 116; 300; 300; по н.г. L=1132
Х1	320; 220; 320; 220; по в.г. L=1080

Спецификация элементов

Поз.	Обозначение	Наименование	Кол.	Масса ед.кг	Примечание
		Плита Пм-5			21634.78
1	ГОСТ 34028-2016(214-210-0502-0001)	Ф 12 А500С L= пог.м.	15934.80	0.89	14147.14
2	ГОСТ 34028-2016(214-210-0502-0004)	Ф 18 А500С L= 3500	80	6.99	559.32
3	ГОСТ 34028-2016(214-210-0502-0001)	Ф 12 А500С L= 3500	166	3.11	515.82
4	ГОСТ 34028-2016(214-210-0502-0002)	Ф 14 А500С L= 3500	72	4.23	304.52
5	ГОСТ 34028-2016(214-210-0502-0005)	Ф 20 А500С L= 5000	48	12.33	591.88
6	ГОСТ 34028-2016(214-210-0502-0004)	Ф 18 А500С L= 5000	40	9.99	399.52
7	ГОСТ 34028-2016(214-210-0502-0001)	Ф 12 А500С L= 2860	450	2.54	1142.62
8	ГОСТ 34028-2016(214-210-0502-0001)	Ф 12 А500С L= 2080	328	1.85	605.70
Ск1	ГОСТ 34028-2016(214-210-0502-0001)	Ф 12 А500С L= 1860	876	1.65	1446.57
Ф1	ГОСТ 34028-2016(214-210-0501-0005)	Ф 10 А500С L= 1132	2645	0.70	1846.00
ВП1	ГОСТ 34028-2016(214-210-0502-0003)	Ф 16 А500С L= 3650	8	5.76	46.09
ВП2	ГОСТ 34028-2016(214-210-0502-0003)	Ф 16 А500С L= 1940	8	3.06	24.50
Х1	ГОСТ 34028-2016(214-210-0101-0002)	Ф 8 А 240 L= 1080	12	0.43	5.11
		Материалы:			
	(212-101-0901)	Класс бетона С 20/25 (В25), м³			171.84

Позиции со "*" см. "Ведомость деталей" см. на данном листе.

Ведомость расхода стали, кг


Марка элемента	Изделия арматурные														Всего
	Арматура класса														
	А240			А500С											
	ГОСТ 34028-2016(214-210-0101)			ГОСТ 34028-2016(214-210-0502)											
	Ф6	Ф8	Итого	Ф10	Ф12	Ф14	Ф16	Ф18	Ф20	Ф22	Ф25	Ф28	Ф32	Итого	
Плита +14.020	---	5.11	5.11	1846.00	17857.85	304.52	70.58	958.84	591.88	---	---	---	---	21629.67	21634.78

1. Данный лист читать совместно с листами КЖ-2.6 и КЖ-7.29 ... 7.35.
2. Арматура плиты перекрытия стыкуется внахлест.
3. Стыки нижней арматуры выполнять на опоре, стыки верхней арматуры на расстоянии 1/3 – 1/4 пролета от опоры, при этом в одном сечении стыковать не более 50% арматуры.
4. Продольную и поперечную арматуру во всех пересечениях связать вязальной проволокой.
5. Свободные концы основной арматуры у торцов плиты перекрытия должны быть заанкерены "П"-образной скобой (поз. Ск1) при помощи вязальной проволоки (без сварки).
6. Спецификацию см. лист КЖ-7.35
7. Выпуск из плит см. лист КЖ-7.36


Изм.	Кол.уч	Лист	N док.	Подп.	Дата	65П-АИП-2024-1-КЖ			
						Строительство многопрофильной больницы на 250 коек с онкологическим центром и поликлиникой на 350 посещений, по адресу: Медеуский район, г. Алматы			
						"Блок 1 Секция 1"	Стадия	Лист	Листов
							РП	7.35	
ГКП		Курал М				Спецификация плиты перекрытия Пм-5 на отм +14.020	АстанаИнжПроект		
Проверил		Кыдырбай А							
Разраб.		Ауез Б							
Н.контроль		Ешенкулова							

Формат А2


Схема расположения выпуск из плиты покрытия на отм. +14.020

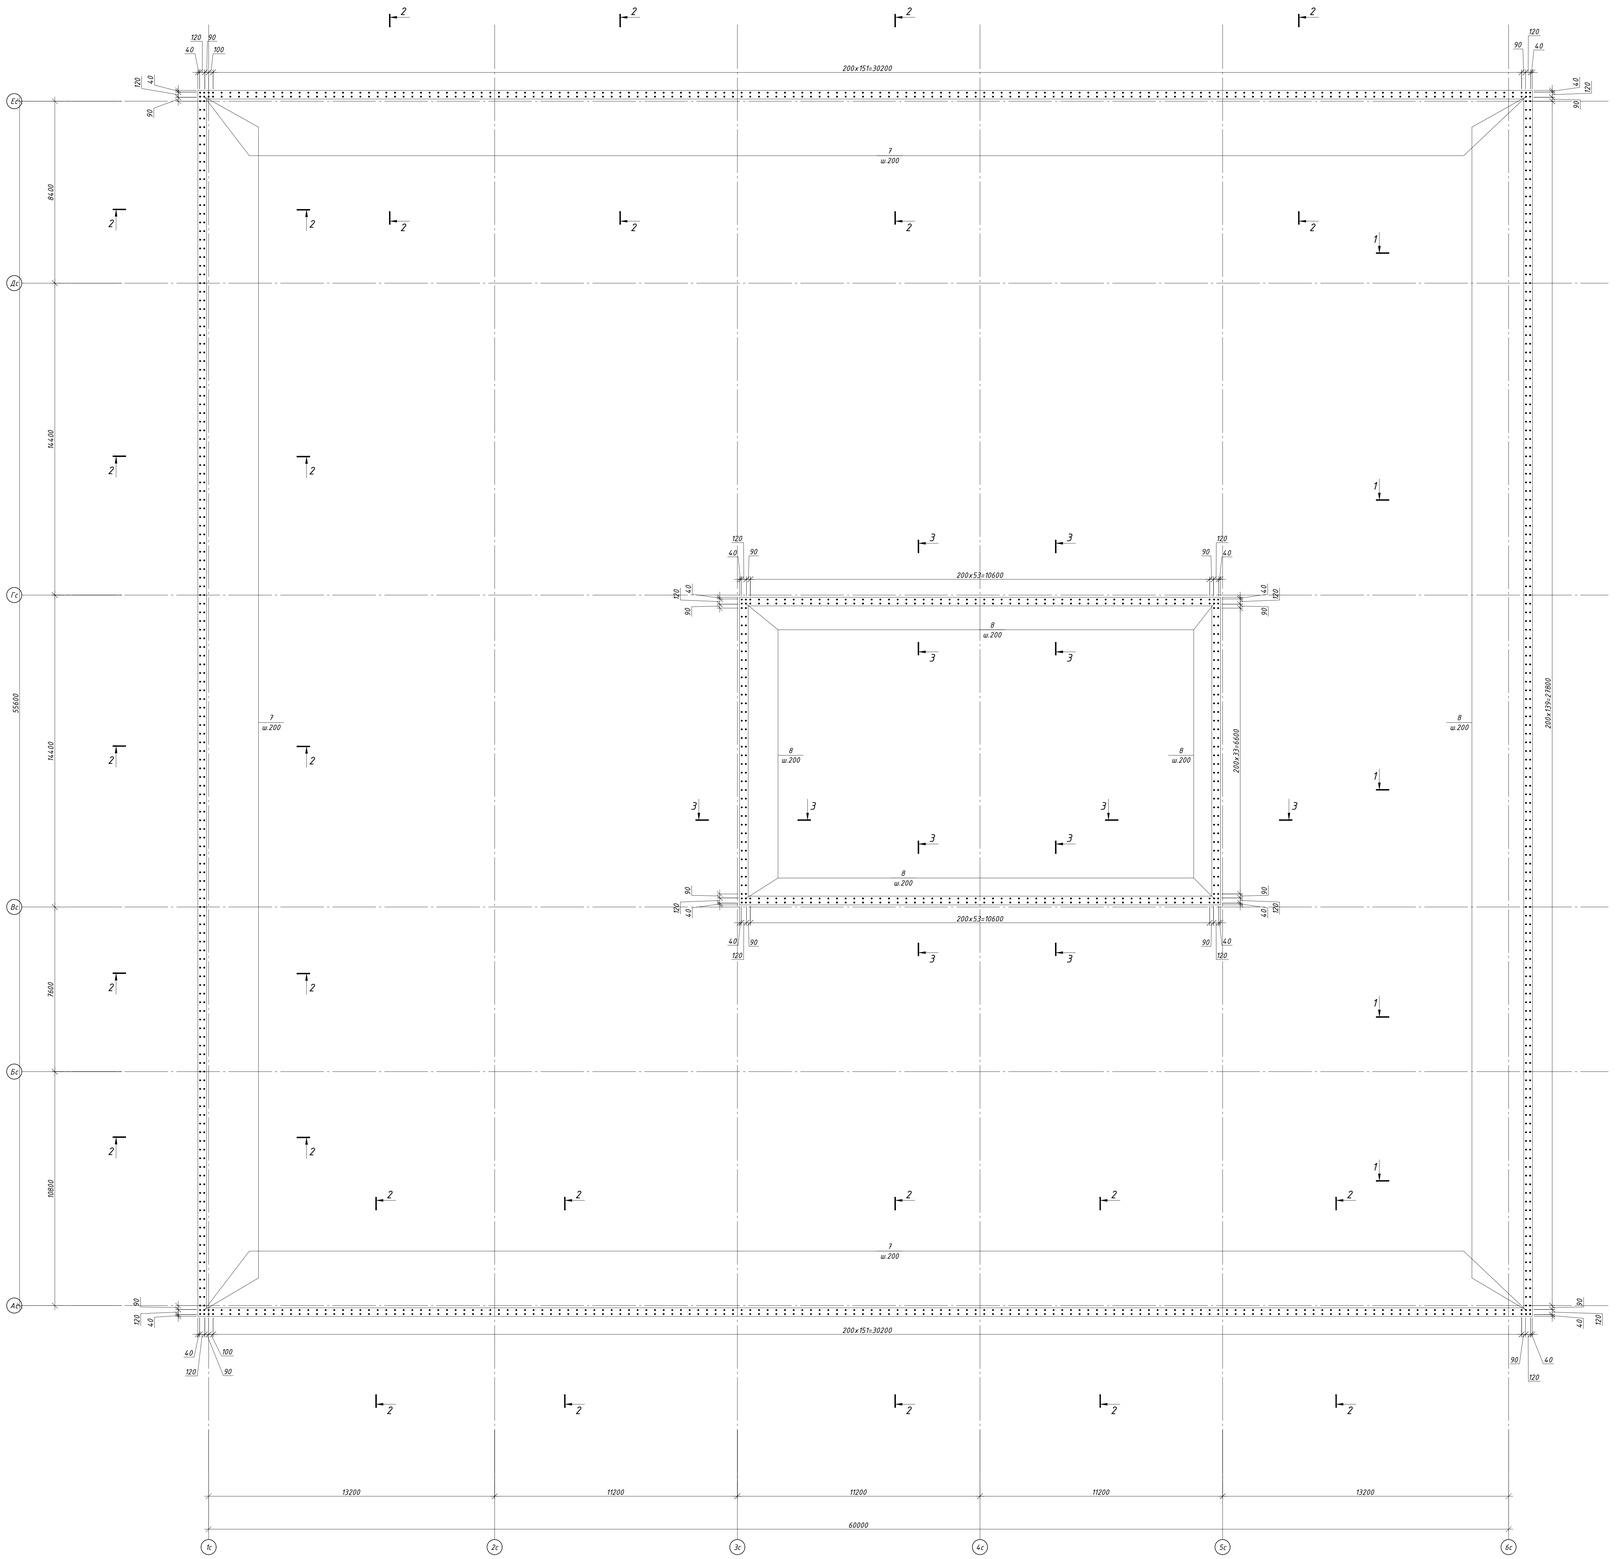


Разрез 3 – 3 (Армирование)
М 1:50

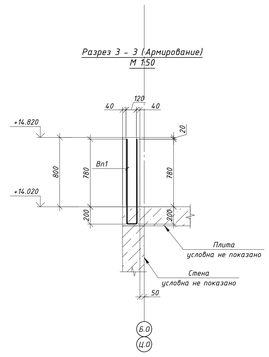

Разрез 1 – 1 (Армирование)
М 1:50

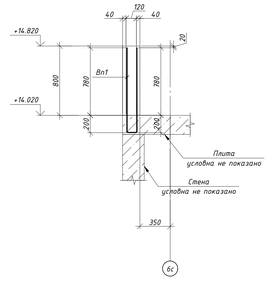


Разрез 2 – 2 (Армирование)
М 1:50

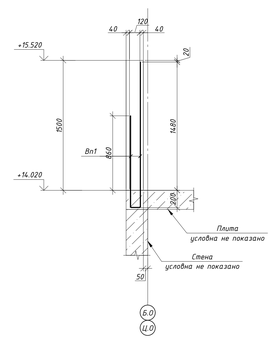

						65П-АИП-2024-1-КЖ	
						Строительство многопрофильной больницы на 250 коек с онкологическим центром и поликлиникой на 350 посещений, по адресу: Медеуский район, г. Алматы	
Изм.	Кол.уч	Лист	N док.	Подп.	Дата		
						"Блок 1 Секция 1"	Стадия: РП; Лист: 7.36; Листов:
ГКП		Курал М.					
Проверил		Кидырбай А.					
Разраб.		Ауез Б.				Схема расположения выпуск из плиты покрытия на отм. +14.020	АстанаИнжПроект
Н.контроль		Ешенкулова					Формат А0

Опалубочный чертеж плита покрытия Пм-6 на отм. +16.520

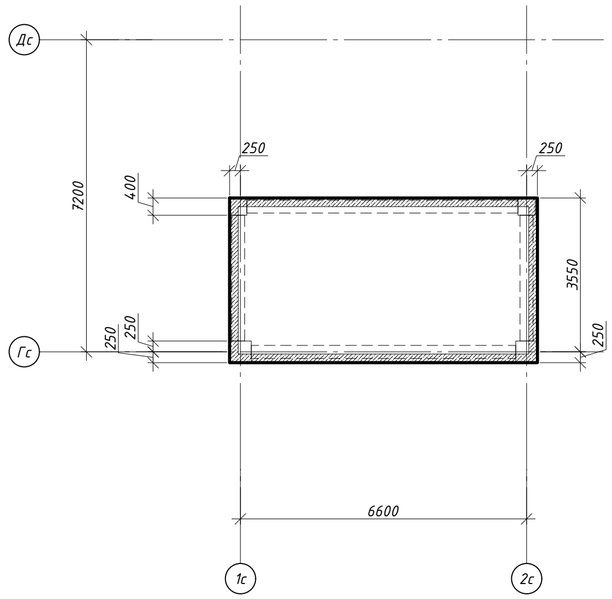

Ведомость деталей

Поз.	Эскиз
Ск1	860; 14.0; R=2.5Ф(=20Ф); R=4Ф(=20Ф); 860; по н.г. L=1860
Ф1	300; 116; 116; 300; 300; по н.г. L=1132

Спецификация элементов


Поз.	Обозначение	Наименование	Кол.	Масса ед.кг	Примечание
		Плита Пм-6	1		1018.01
1	ГОСТ 34028-2016(214-210-0502-0001)	Ф 12 А500С L= пог.м.	585.5	0.89	519.80
2*	ГОСТ 34028-2016(214-210-0502-0001)	Ф 12 А500С L= 2610	112	2.32	259.53
Ск1	ГОСТ 34028-2016(214-210-0502-0001)	Ф 12 А500С L= 1860	112	1.65	184.95
Ф1	ГОСТ 34028-2016(214-210-0501-0005)	Ф 10 А500С L= 1132	77	0.70	53.74
		Материалы:			
	(212-101-0901)	Класс бетона С 20/25 (В25), м³			5.94

Позиции со "*" см. "Ведомость деталей" см. на данном листе.

Ведомость расхода стали на элемент, кг

Марка элемента	Изделия арматурные								Всего
	Арматура класса								
	А240		А500С						
	ГОСТ 34028-2016(214-210-0101)		ГОСТ 34028-2016(214-210-0502)						
	Ф8	Итого	Ф10	Ф12	Ф14	Ф16	Ф18	Итого	
Плита Пм-6	---	---	53.74	964.27	---	---	----	1018.01	1018.01

Схема расположения основных арматуры плита покрытия Пм-6 на отм +16.520

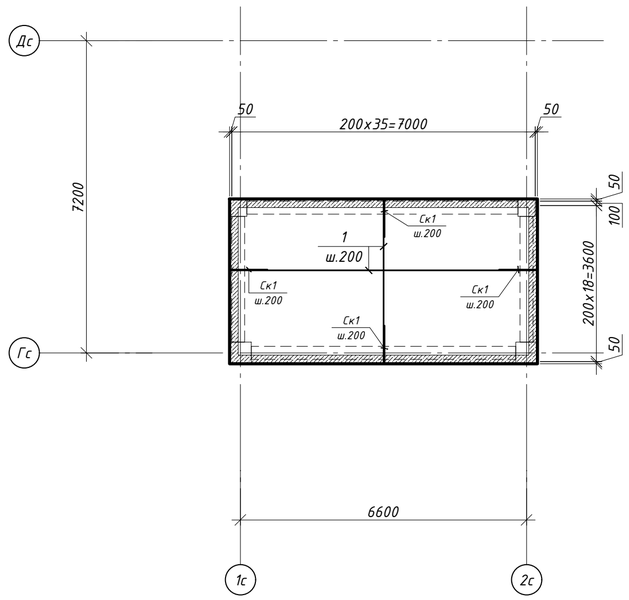


1. Данный лист читать совместно с листами КЖ-2.6
2. Арматура плиты перекрытия стыкуется внахлест.
3. Стыки нижней арматуры выполнять на опоре, стыки верхней арматуры на расстоянии 1/3 - 1/4 пролета от опоры, при этом в одном сечении стыковать не более 50% арматуры.
4. Продольную и поперечную арматуру во всех пересечениях связать вязальной проволокой.
5. Свободные концы основной арматуры у торцов плиты перекрытия должны быть заанкерены "П"-образной скобой (поз. Ск1) при помощи вязальной проволоки (без сварки).
6. Спецификацию см. лист КЖ-7.37


Изм.	Кол.уч.	Лист	N док.	Подп.	Дата	65П-АИП-2024-1-КЖ			
						Строительство многопрофильной больницы на 250 коек с онкологическим центром и поликлиникой на 350 посещений, по адресу: Медеуский район, г. Алматы			
						"Блок 1 Секция 1"	Стадия	Лист	Листов
ГКП		Курал М					РП	7.37	
Проверил		Кыдырбай А				Опалубочный чертеж плиты перекрытия Пм-6 на отм.+16.520	АстанаИнжПроект		
Разраб.		Ауез Б							
Н.контроль		Ешенкулова							

Формат А2

Схема расположения выпуск из плиты покрытия на отм. +16.520

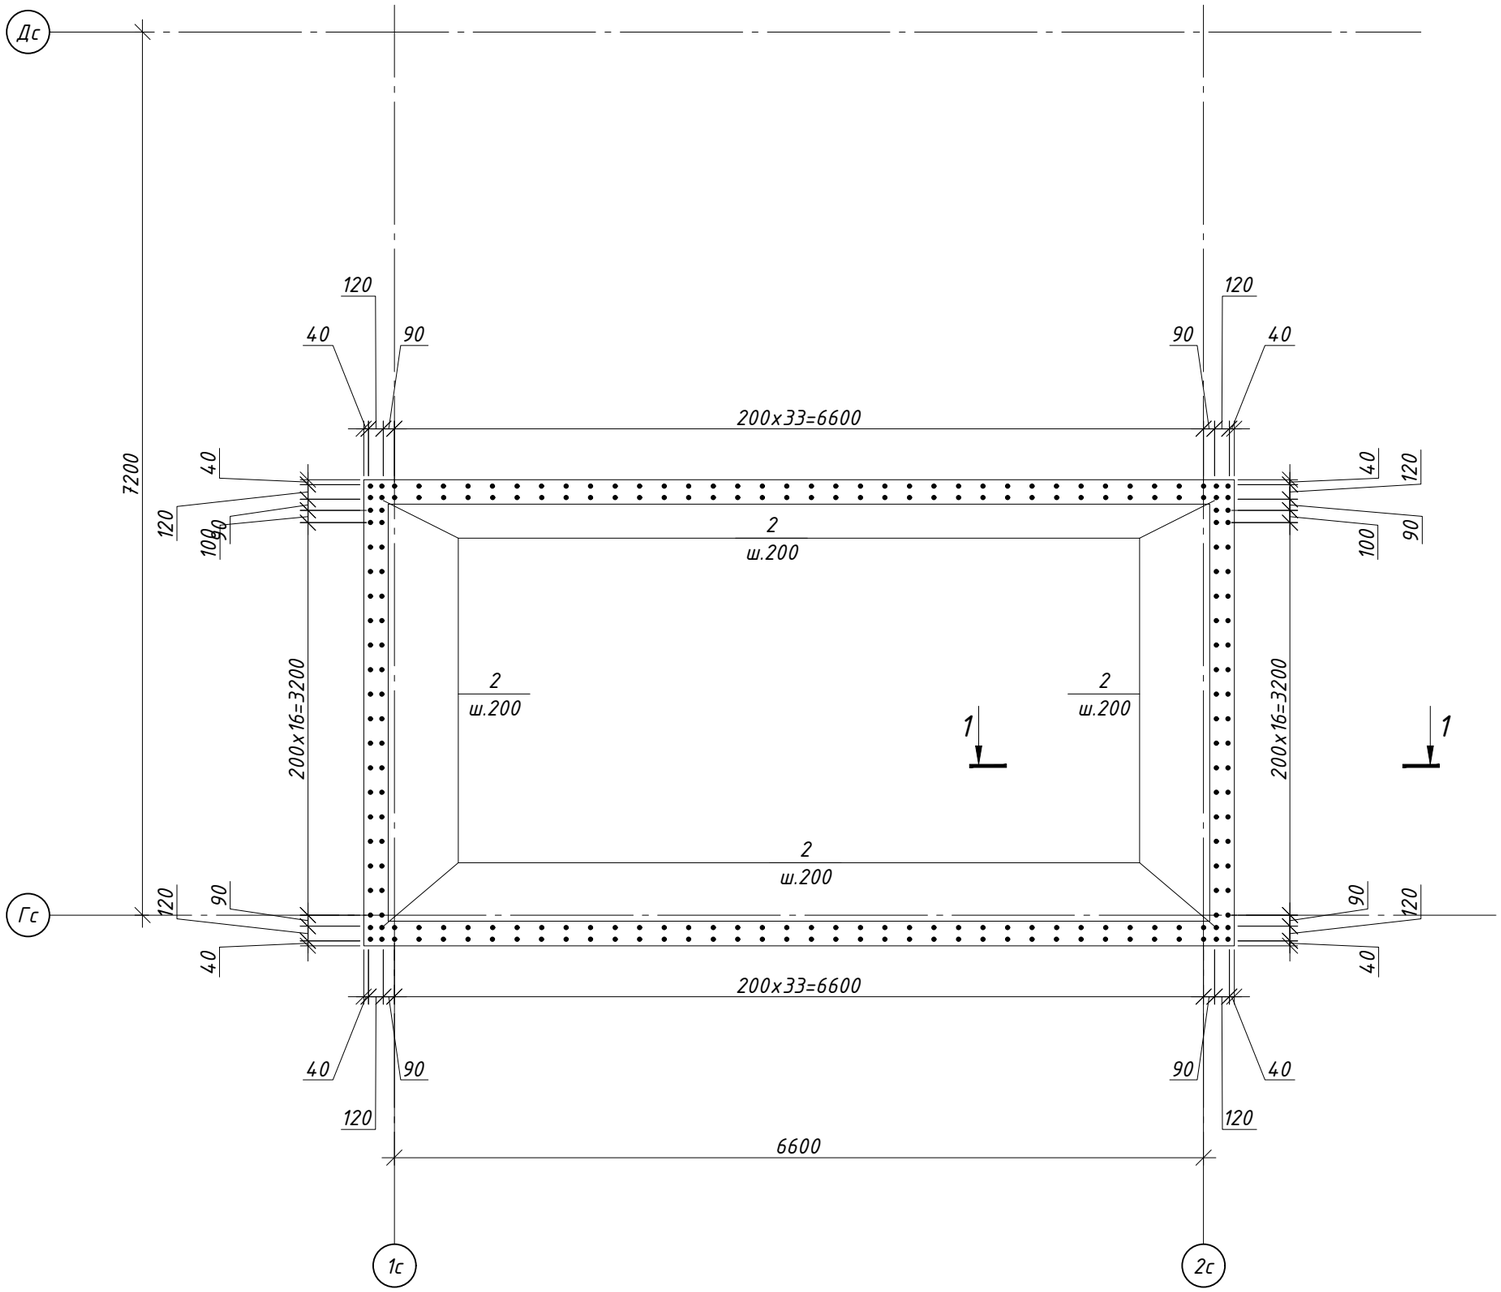


Разрез 2 - 2 (Армирование)
М 1:50

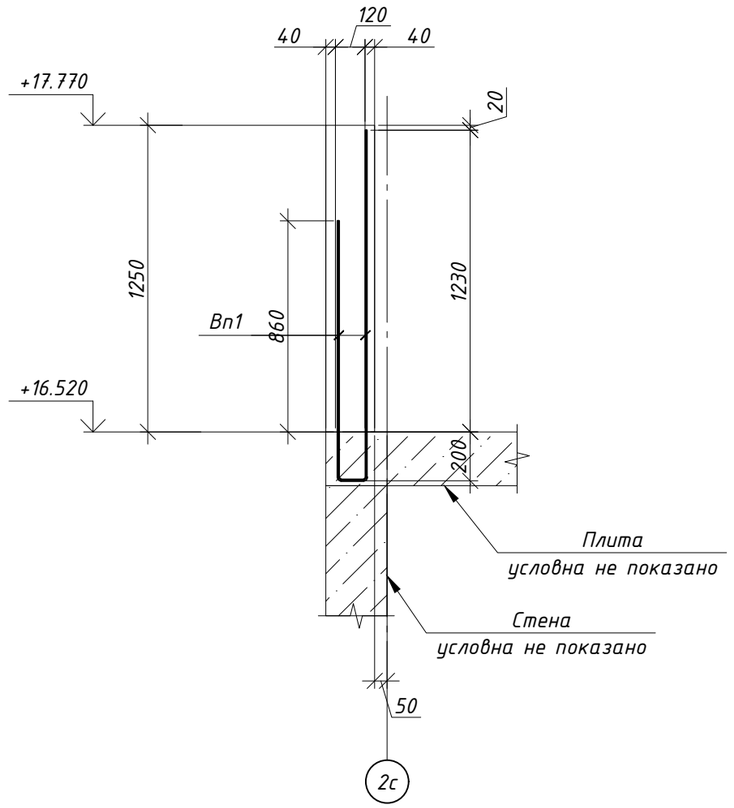


						65П-АИП-2024-1-КЖ
						Строительство многопрофильной больницы на 250 коек с онкологическим центром и поликлиникой на 350 посещений, по адресу: Медеуский район, г. Алматы
Изм.	Кол.уч.	Лист	N док.	Подп.	Дата	
ГКП		Курал М				"Блок 1 Секция 1" — Стадия: РП; Лист: 7.38; Листов:
Проверил		Кыдырбай А				
Разраб.		Ауез Б				Схема расположения выпуск из плиты покрытия на отм. +16.520
Н.контроль		Ешенкулова				АстанаИнжПроект

Формат А3


Схема опалубочный чертеж парапета ПтМ-1 на отм. +14.020

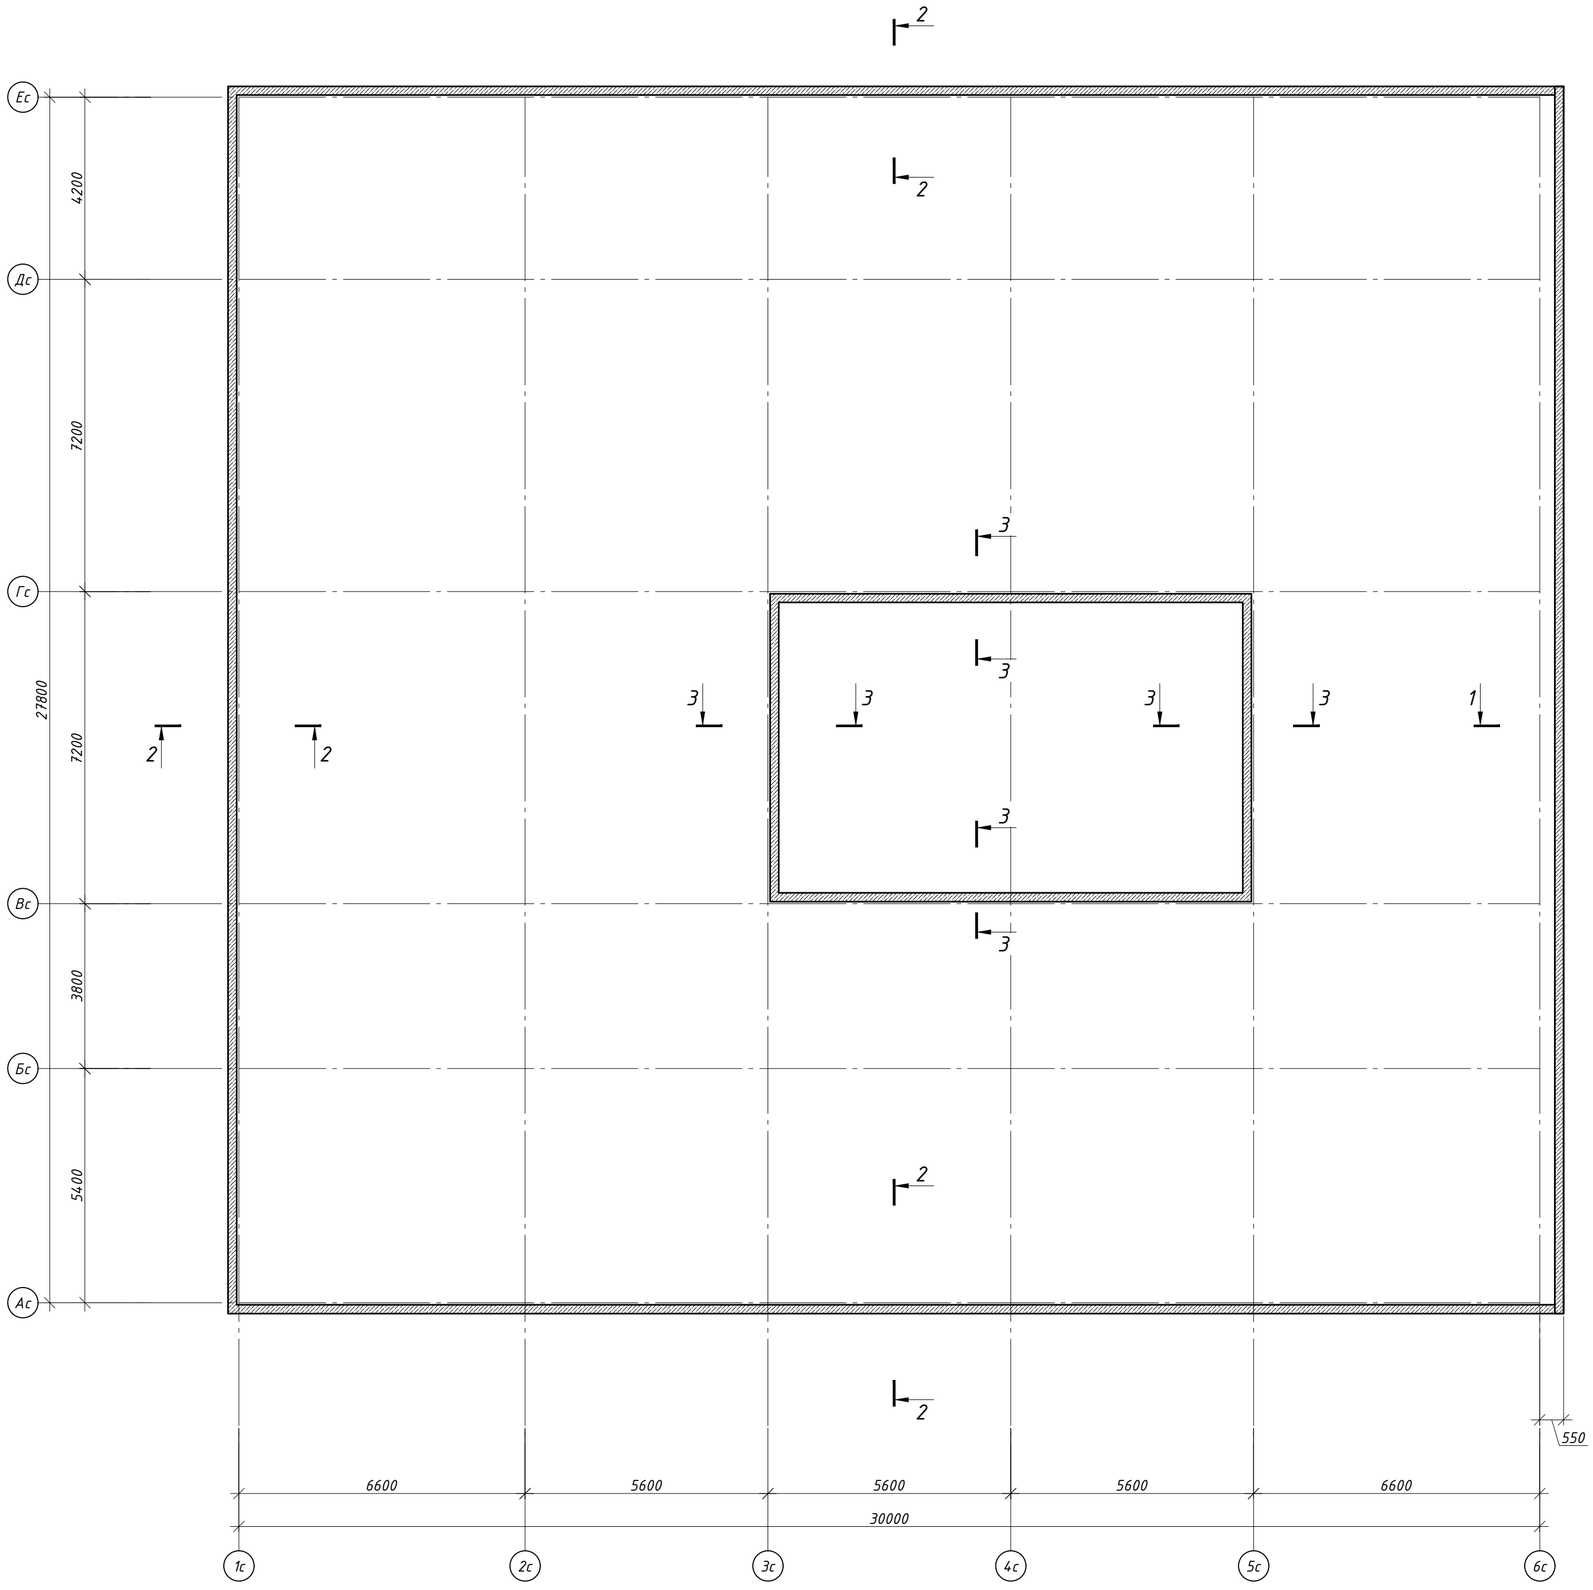


Разрез 1 – 1 (Опалубка)
М 1:50

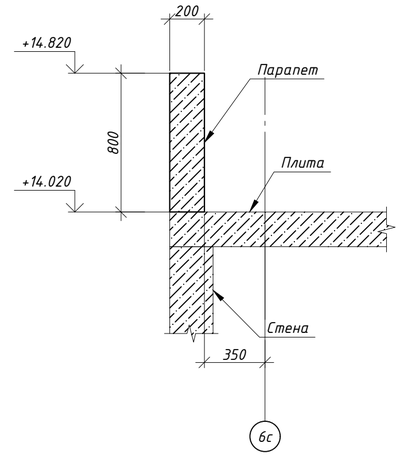

Разрез 3 – 3 (Опалубка)
М 1:50

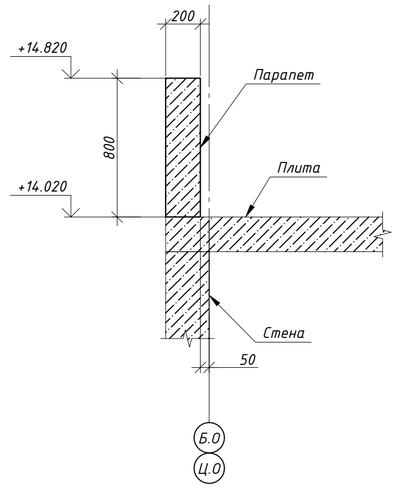


Разрез 2 – 2 (Опалубка)
М 1:50

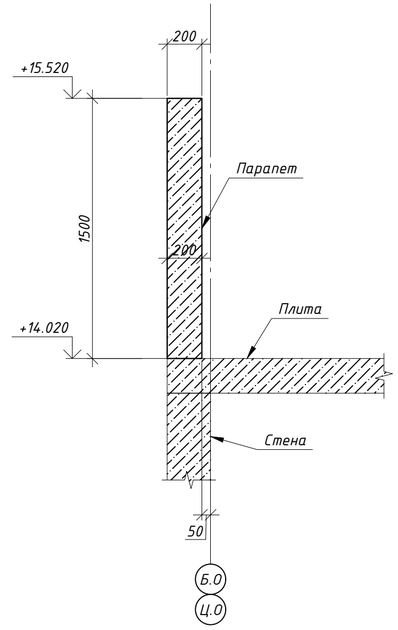

						65П-АИП-2024-1-КЖ	
						Строительство многопрофильной больницы на 250 коек с онкологическим центром и поликлиникой на 350 посещений, по адресу: Медеуский район, г. Алматы	
Изм.	Кол.уч.	Лист	N док.	Подп.	Дата		
ГКП		Курал М				"Блок 1 Секция 1"	Стадия: РП; Лист: 8.1; Листов:
Проверил		Кыдырбай А					
Разраб.		Ауез Б				Схема опалубочный чертеж парапета ПтМ-1 на отм. +14.020	АстанаИнжПроект
Н.контроль		Ешенкулова					

Формат А2

Схема основное армирование парапета ПпМ-1 на отм. +14.020

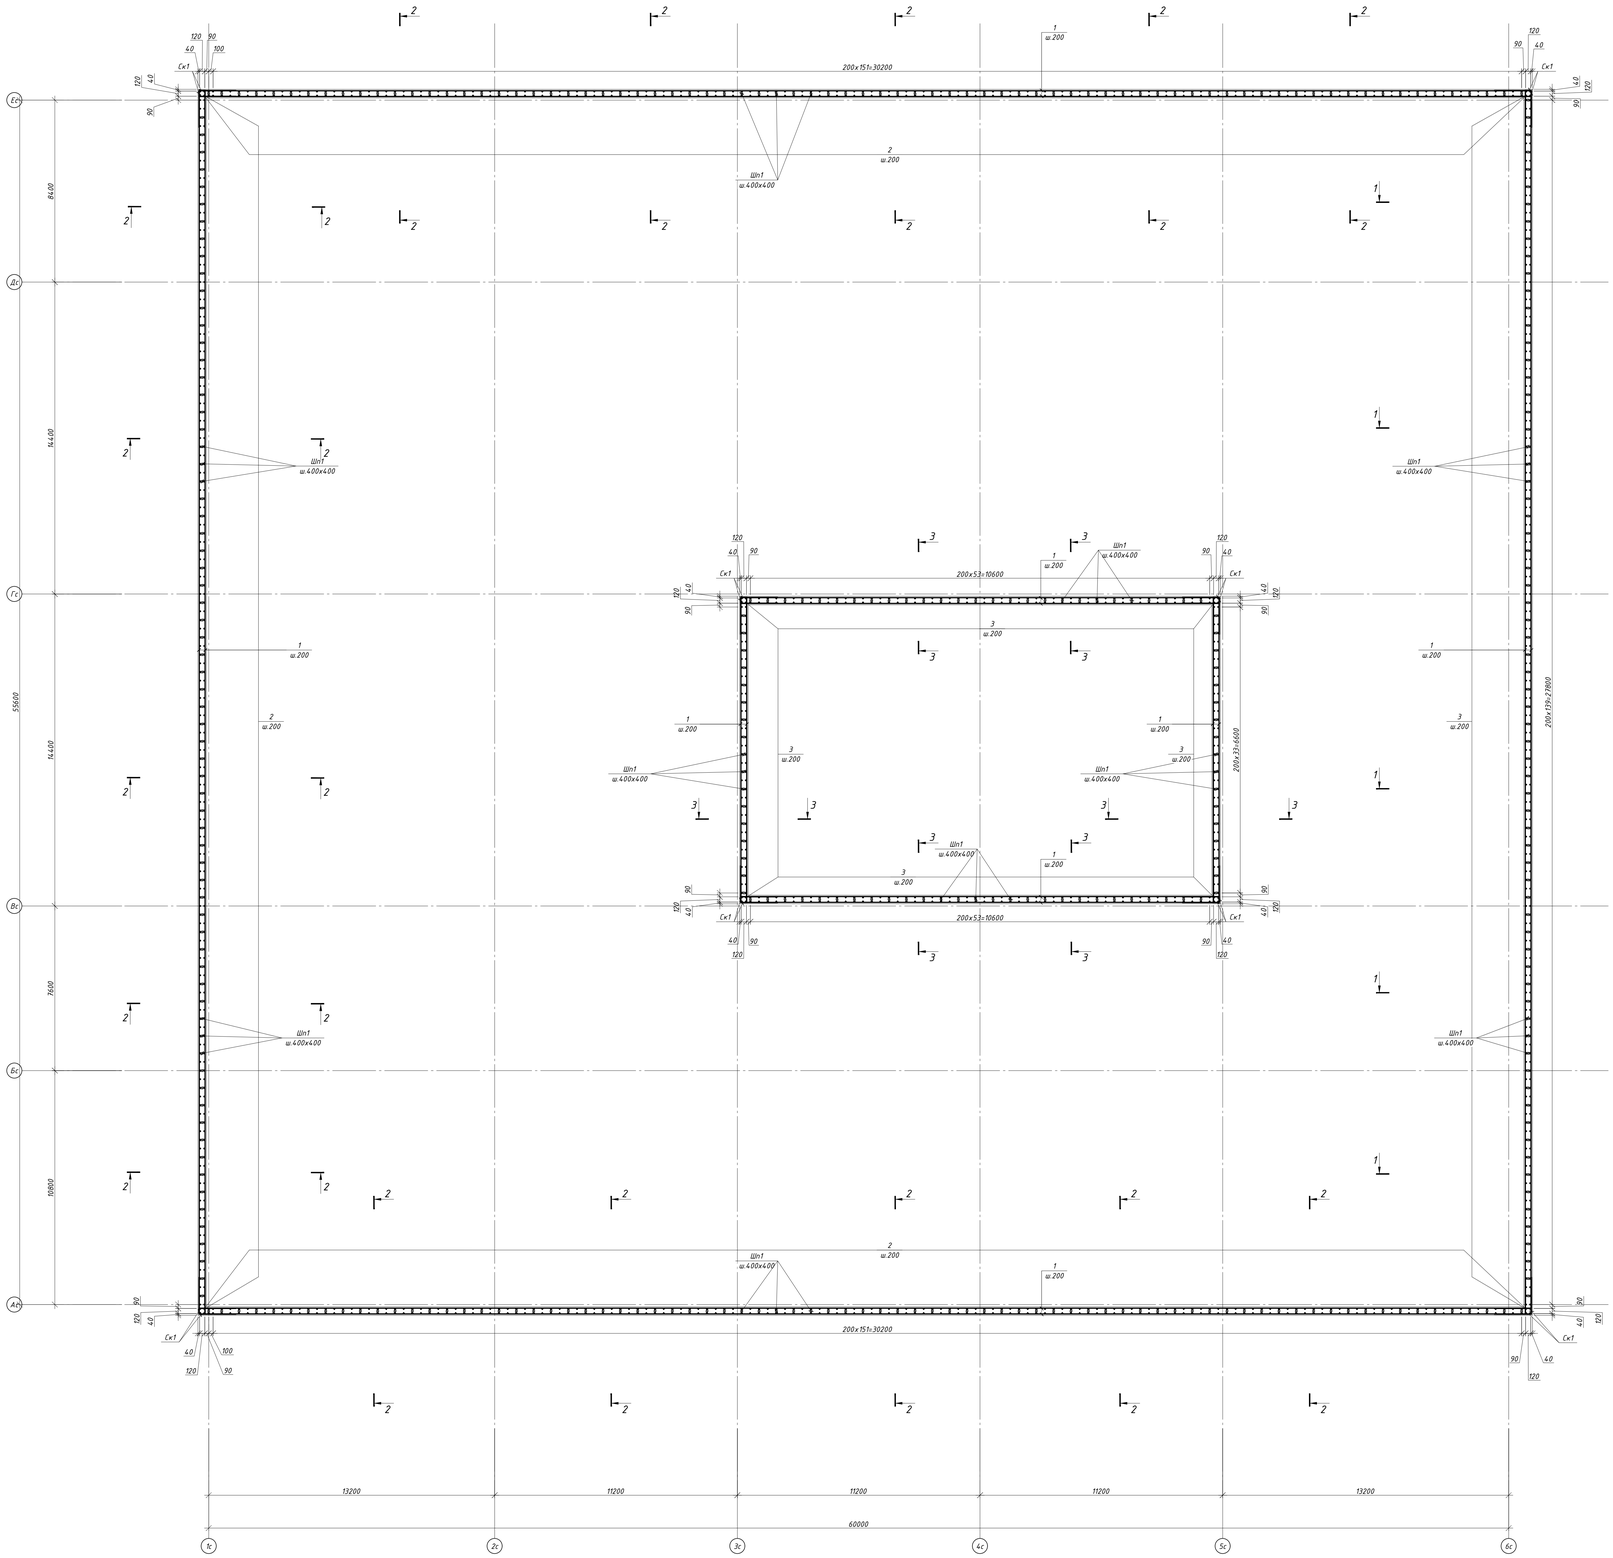

Спецификация элементов


Поз.	Обозначение	Наименование	Кол.	Масса ед.кг	Примечание
		Парапет ПпМ-1			3901.15
1	ГОСТ 34028-2016(214-210-0502-0001)	Ф 12 А500С L=пог.м	2189.67	0.89	1944.02
2*	ГОСТ 34028-2016(214-210-0502-0001)	Ф 12 А500С L= 2460	450	2.18	982.81
3*	ГОСТ 34028-2016(214-210-0502-0001)	Ф 12 А500С L= 1680	328	1.49	489.22
Ск1*	ГОСТ 34028-2016(214-210-0502-0001)	Ф 12 А500С L= 1840	98	1.63	160.09
Шп1*	ГОСТ 34028-2016(214-210-0101-0002)	Ф 8 А500С L= 320	2574	0.13	325.01
		Материалы:			
	(212-101-0901)	Класс бетона С 20/25 (В25), м³			36.95

Позиции со "*" см. "Ведомость деталей" см. на данном листе.


Ведомость расхода стали на элемент, кг

Марка элемента	Изделия арматурные						Всего
	Арматура класса						
	А240			А500С			
	ГОСТ 34028-2016(214-210-0101)			ГОСТ 34028-2016(214-210-0502)			
	Ф6	Ф8	Итого	Ф12	Ф16	Итого	
Парапет ПпМ-1		325.01	325.01	3576.14	---	3576.14	3901.15


Разрез 3 - 3 (Армирование)
М 1:50

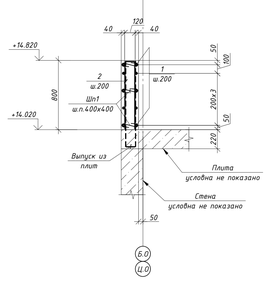

Разрез 1 - 1 (Армирование)
М 1:50

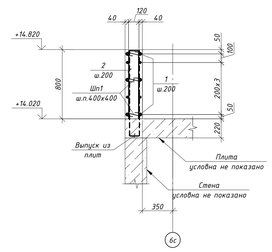

Разрез 2 - 2 (Армирование)
М 1:50

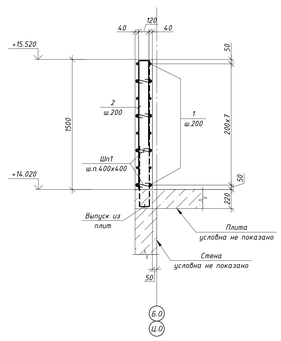


Ведомость деталей


Поз.	Эскиз
Ск1	860, 120, 860; по н.г. L=1840
2*	860, 120, 1480; по н.г. L=2460
3*	780, 120, 780; по н.г. L=1680
Шп1	120, 100, 100; по в.г. L=320

							65П-АИП-2024-1-КЖ	
							Строительство многопрофильной больницы на 250 коек с онкологическим центром и поликлиникой на 350 посещений, по адресу: Медеуский район, г. Алматы	
Изм.	Кол.уч.	Лист	N док.	Подп.	Дата			
							"Блок 1 Секция 1"	Стадия: РП; Лист: 8.2; Листов:
ГКП		Курал М						
Проверил		Кидырбай А					Спецификация схема основное армирование парапета ПпМ-1 на отм. +14.020	АстанаИнжПроект
Разраб.		Ауез Б						Формат А0
Н.контроль		Ешенкулова						

Схема опалубочный чертеж парапета ПтМ-2 на отм. +16.520

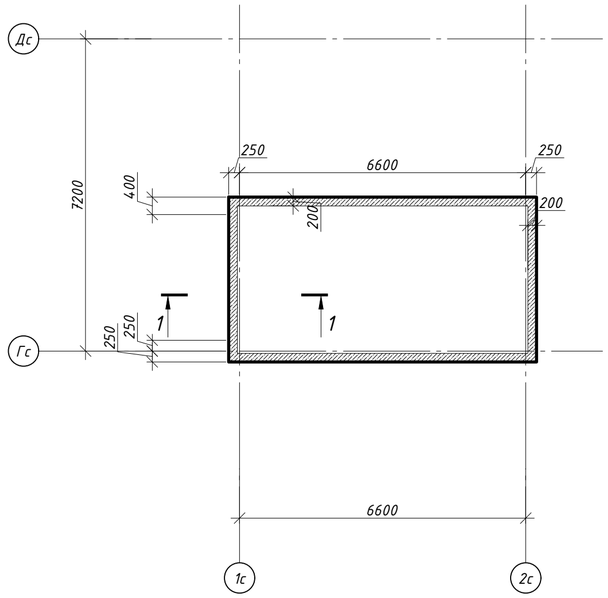

Разрез 1 - 1 (Армирование)
М 1:50

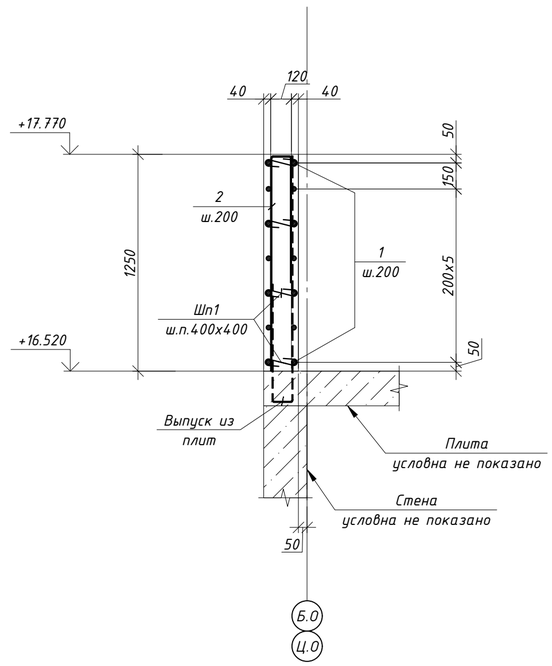

Спецификация элементов


Поз.	Обозначение	Наименование	Кол.	Масса ед.кг	Примечание
		Парапет ПтМ-2			595.08
1	ГОСТ 34028-2016(214-210-0502-0001)	ф 12 А500С L=пог.м.	320.46	0.89	284.51
2*	ГОСТ 34028-2016(214-210-0502-0001)	ф 12 А500С L= 2210	112	1.96	219.75
Ск1*	ГОСТ 34028-2016(214-210-0502-0001)	ф 12 А500С L= 1840	28	1.63	45.74
Шп1*	ГОСТ 34028-2016(214-210-0101-0002)	ф 8 А500С L= 320	357	0.13	45.08
		Материалы:			
	(212-101-0901)	Класс бетона С 20/25 (В25), м^3			3.36

Позиции со "*" см. "Ведомость деталей" см. на данном листе.


Ведомость расхода стали на элемент, кг

Марка элемента	Изделия арматурные						Всего
	Арматура класса						
	А240			А500С			
	ГОСТ 34028-2016(214-210-0101)			ГОСТ 34028-2016(214-210-0502)			
	ф6	ф8	Итого	ф12	ф16	Итого	
Парапет ПтМ-2		45.08	45.08	550.00	---	550.00	595.08

Схема основное армирование парапета ПтМ-2 на отм. +16.500

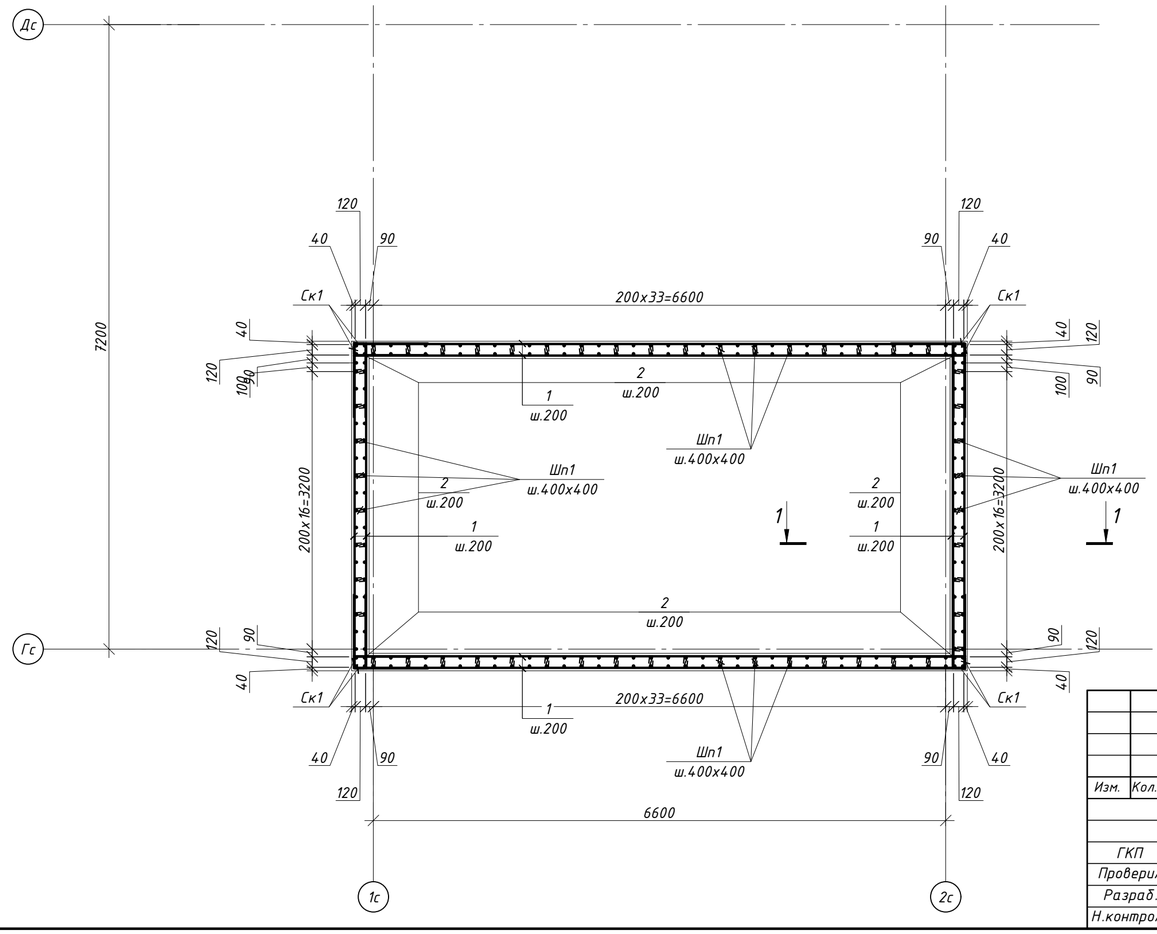

Разрез 1 - 1 (Опалубка)
М 1:50

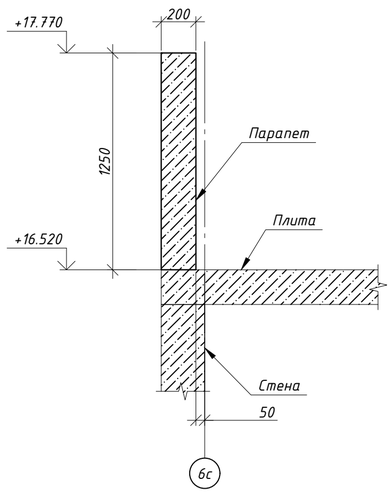

Ведомость деталей

Поз.	Эскиз
Ск1	860, 120, 860; по н.г. L=1840
2*	860, 120, 1230; по н.г. L=2210
Шп1	120, 100, 100; по в.г. L=320

Изм.	Кол.уч	Лист	N док.	Подп.	Дата	65П-АИП-2024-1-КЖ			
						Строительство многопрофильной больницы на 250 коек с онкологическим центром и поликлиникой на 350 посещений, по адресу: Медеуский район, г. Алматы			
						"Блок 1 Секция 1"	Стадия	Лист	Листов
							РП	8.3	
ГКП		Курал М				Спецификация схема основное армирование парапета ПтМ-2 на отм. +16.520	АстанаИнжПроект		
Проверил		Кыдырбай А							
Разраб.		Ауез Б							
Н.контроль		Ешенкулова							

Формат А2