


## Опалубочный чертеж лестницы Л-1 по оси 1с - 2с

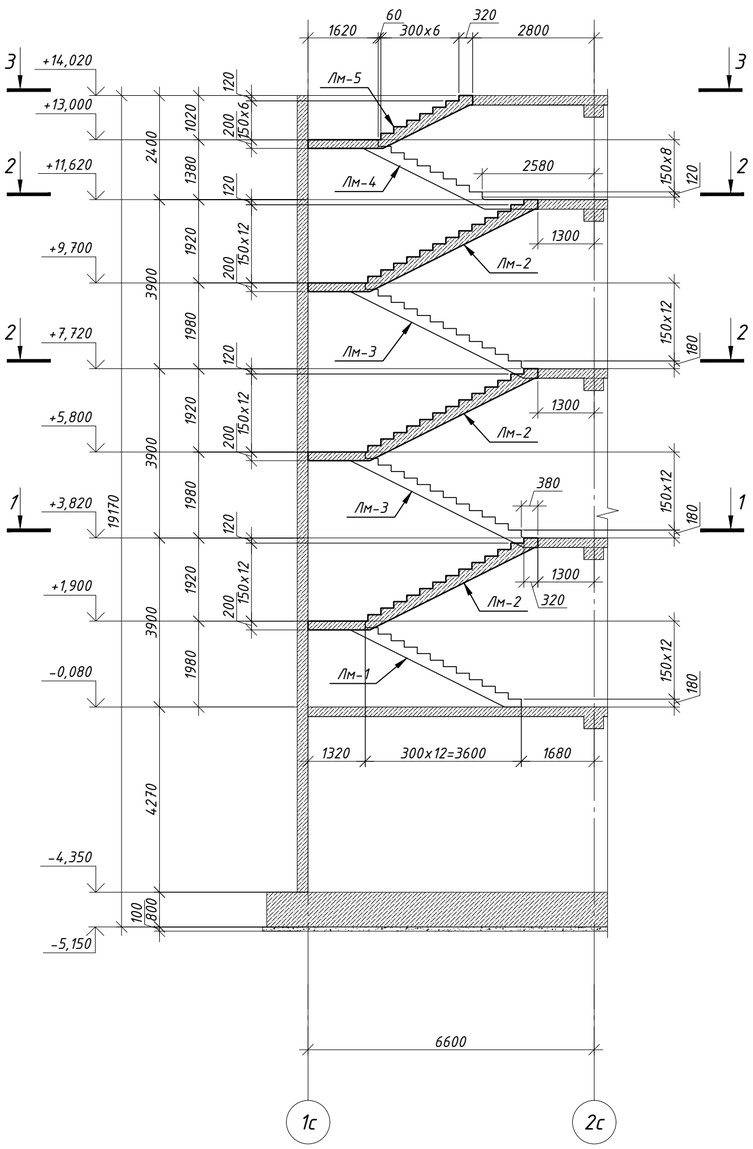



## Разрез 1 - 1

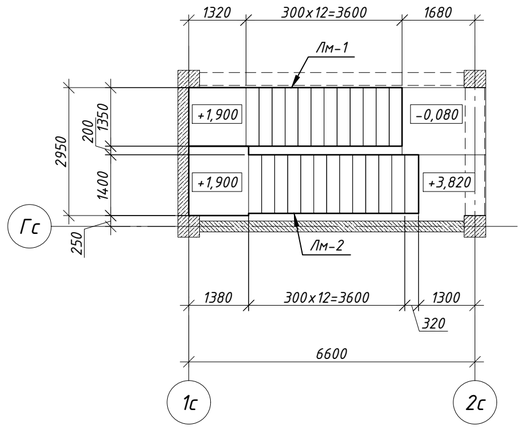


## Разрез 2 - 2

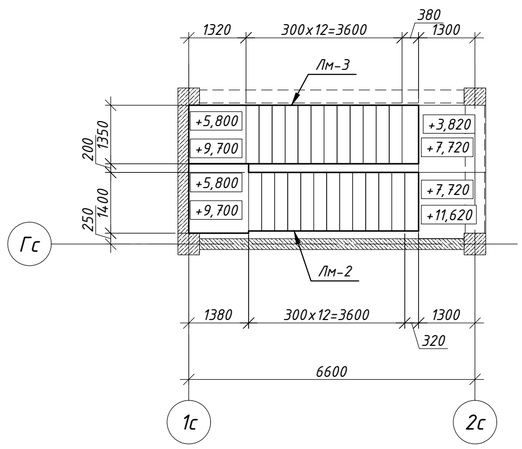


## Разрез 3 - 3

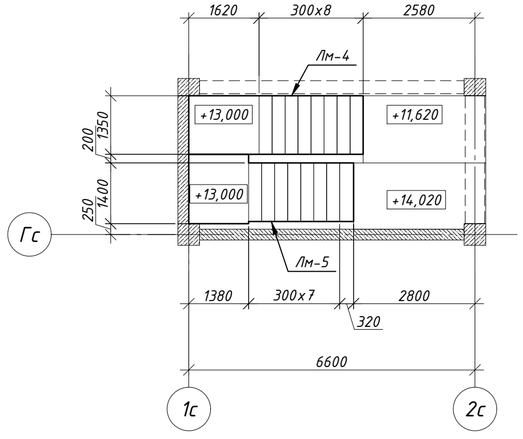



1. Схему расположения монолитной лестницы Л1 см. КЖ - 2.2
2. Отделку площадок и ступеней смотри чертежи марки "АР".
3. Бетонирование монолитной лестницы вести одновременно с монолитными стенами.
4. Арматуру во всех пересечениях вязать вязальной проволокой.
5. Спецификацию элементов и ведомость расхода стали см. КЖ - 9.3
6. Масса металла приведенная в спецификации, составлена без учета 1% на массу трудноустранимых потерь металла при укладке арматуры в монолитные железобетонные конструкции.


| | | | | | | | |
|---|---|---|---|---|---|---|---|
| | | | | | | 65П-АИП-2024-1-КЖ | |
| | | | | | | Строительство многопрофильной больницы на 250 коек с онкологическим центром и поликлиникой на 350 посещений, по адресу: Медеуский район, г. Алматы | |
| Изм. | Кол.уч | Лист | N док. | Подп. | Дата | | |
| | | | | | | "Блок 1 Секция 1" | Стадия: РП; Лист: 9.1; Листов: |
| ГКП | | Курал М | | | | | |
| Проверил | | Кыдырбай А | | | | | |
| Разраб. | | Ауез Б | | | | Опалубочный чертеж лестницы Л-1 по оси 1с - 2с | АстанаИнжПроект |
| Н.контроль | | Ешенкулова | | | | | |

Формат А2


## Лестничный марш Лм-1

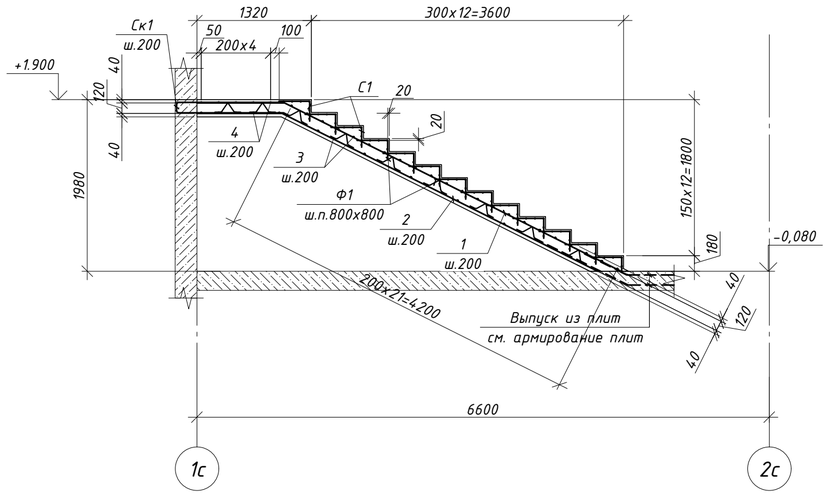



## Лестничный марш Лм-3

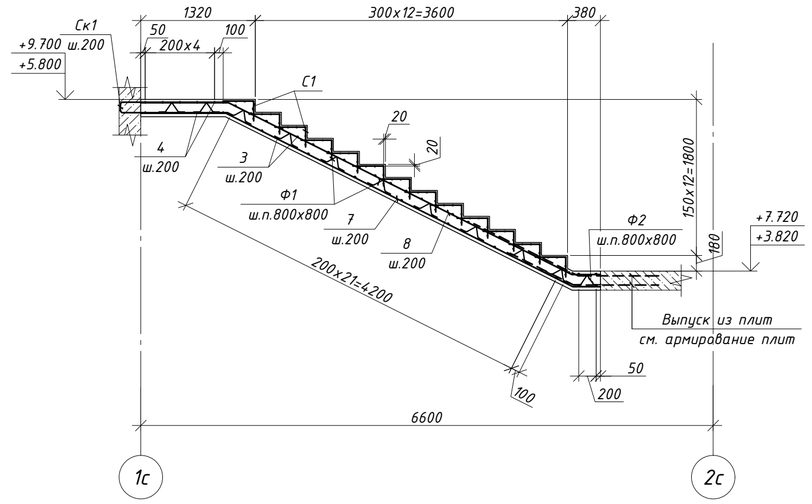



## Лестничный марш Лм-2

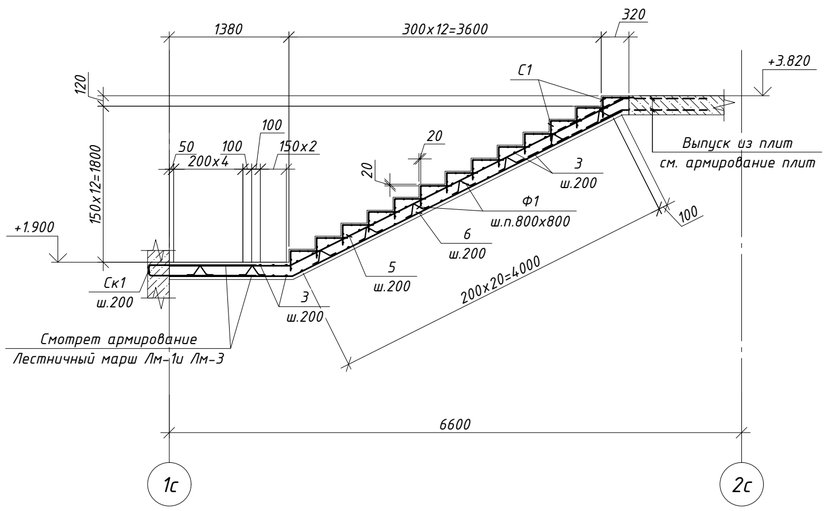


## Лестничный марш Лм-4

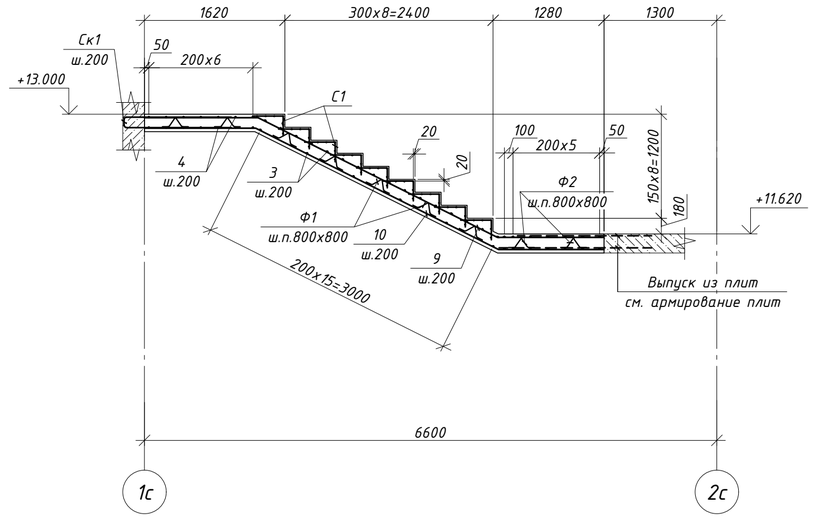


## Лестничный марш Лм-5

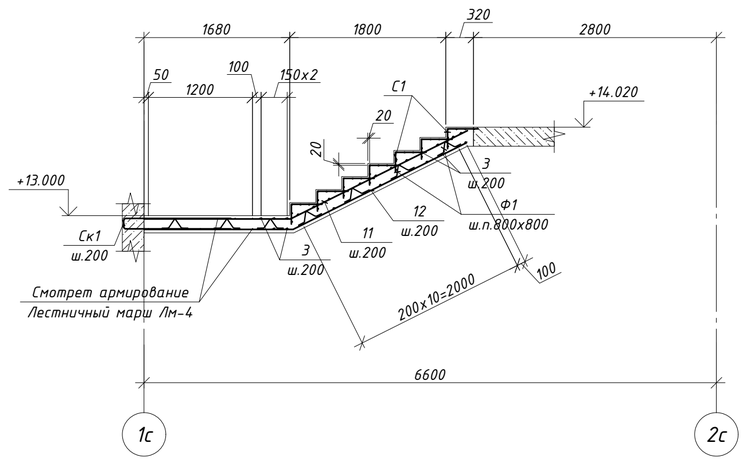


| | | | | | | |
|---|---|---|---|---|---|---|
| | | | | | | 65П-АИП-2024-1-КЖ |
| | | | | | | Строительство многопрофильной больницы на 250 коек с онкологическим центром и поликлиникой на 350 посещений, по адресу: Медеуский район, г. Алматы |
| Изм. | Кол.уч. | Лист | N док. | Подп. | Дата | |
| | | | | | | "Блок 1 Секция 1" — Стадия: РП; Лист: 9.2; Листов: |
| ГКП | | Курал М | | | | Лестничный марш Лм-1...Лм-5 |
| Проверил | | Кыдырбай А | | | | АстанаИнжПроект |
| Разраб. | | Ауез Б | | | | |
| Н.контроль | | Ешенкулова | | | | Формат А2 |

## Спецификация элементов

| Поз. | Обозначение | Наименование | Кол. | Масса ед.кг | Примечание |
|---|---|---|---|---|---|
| | | Лестница Л-1 | | | 2703.60 |
| Лм-1 | данный лист | Лестничный марш Лм-1 | 1 | 337.62 | 337.62 |
| Лм-2 | данный лист | Лестничный марш Лм-2 | 3 | 352.93 | 1058.80 |
| Лм-3 | данный лист | Лестничный марш Лм-3 | 2 | 361.34 | 722.68 |
| Лм-4 | данный лист | Лестничный марш Лм-4 | 1 | 333.54 | 333.54 |
| Лм-5 | данный лист | Лестничный марш Лм-5 | 1 | 250.96 | 250.96 |
| | | Лестничный марш Лм-1 | | | 337.62 |
| 1 | ГОСТ 34028-2016(214-210-0502-0003) | Ф 16 А500С L= 5340 | 8 | 8.43 | 67.43 |
| 2 | ГОСТ 34028-2016(214-210-0502-0003) | Ф 16 А500С L= 5050 | 8 | 7.97 | 63.76 |
| 3 | ГОСТ 34028-2016(214-210-0502-0001) | Ф 12 А500С L= 2290 | 44 | 2.03 | 89.46 |
| 4 | ГОСТ 34028-2016(214-210-0502-0001) | Ф 12 А500С L= 2290 | 12 | 2.03 | 24.40 |
| Ск1 | ГОСТ 34028-2016(214-210-0502-0003) | Ф 16 А500С L= 2120 | 9 | 3.35 | 30.11 |
| Ф1 | ГОСТ 34028-2016(214-210-0502-0001) | Ф 12 А500С L= 1092 | 21 | 0.97 | 20.36 |
| С1 | ГОСТ 23279-2012(214-403-01010) | 4С 5Вр-I-100 / 5Вр-I-100(50) 75х130 | 14 | 3.01 | 42.1 |
| | | Материалы: | | | |
| | (212-101-0901) | Класс бетона С 20/25 (В25), м³ | | | 1.80 |
| | | Лестничный марш Лм-2 | | | 352.93 |
| 5 | ГОСТ 34028-2016(214-210-0502-0003) | Ф 16 А500С L= 5680 | 8 | 8.96 | 71.72 |
| 6 | ГОСТ 34028-2016(214-210-0502-0003) | Ф 16 А500С L= 5670 | 8 | 8.95 | 71.59 |
| 3 | ГОСТ 34028-2016(214-210-0502-0001) | Ф 12 А500С L= 2290 | 60 | 2.03 | 121.99 |
| | | | | | |
| Ск1 | ГОСТ 34028-2016(214-210-0502-0003) | Ф 16 А500С L= 2120 | 9 | 3.35 | 30.11 |
| Ф1 | ГОСТ 34028-2016(214-210-0502-0001) | Ф 12 А500С L= 1092 | 19 | 0.97 | 18.42 |
| С1 | ГОСТ 23279-2012(214-403-01010) | 4С 5Вр-I-100 / 5Вр-I-100(50) 75х130 | 13 | 3.01 | 39.1 |
| | | Материалы: | | | |
| | (212-101-0901) | Класс бетона С 20/25 (В25), м³ | | | 1.96 |
| | | Лестничный марш Лм-3 | | | 361.34 |
| 7 | ГОСТ 34028-2016(214-210-0502-0003) | Ф 16 А500С L= 5770 | 8 | 9.11 | 72.86 |
| 8 | ГОСТ 34028-2016(214-210-0502-0003) | Ф 16 А500С L= 5770 | 8 | 9.11 | 72.86 |
| 3 | ГОСТ 34028-2016(214-210-0502-0001) | Ф 12 А500С L= 2290 | 50 | 2.03 | 101.65 |
| 4 | ГОСТ 34028-2016(214-210-0502-0001) | Ф 12 А500С L= 2290 | 12 | 2.03 | 24.40 |
| Ск1 | ГОСТ 34028-2016(214-210-0502-0001) | Ф 16 А500С L= 2120 | 9 | 3.35 | 30.11 |
| Ф1 | ГОСТ 34028-2016(214-210-0502-0001) | Ф 12 А500С L= 1092 | 21 | 0.97 | 20.36 |
| С1 | ГОСТ 23279-2012(214-403-01010) | 4С 5Вр-I-100 / 5Вр-I-100(50) 75х130 | 13 | 3.01 | 39.1 |
| | | Материалы: | | | |
| | (212-101-0901) | Класс бетона С 20/25 (В25), м³ | | | 1.97 |

## Спецификация элементов

| Поз. | Обозначение | Наименование | Кол. | Масса ед.кг | Примечание |
|---|---|---|---|---|---|
| | | Лестничный марш Лм-4 | | | 333.54 |
| 9 | ГОСТ 34028-2016(214-210-0502-0003) | Ф 16 А500С L= 5620 | 8 | 8.87 | 70.96 |
| 10 | ГОСТ 34028-2016(214-210-0502-0003) | Ф 16 А500С L= 5620 | 8 | 8.87 | 70.96 |
| 3 | ГОСТ 34028-2016(214-210-0502-0001) | Ф 12 А500С L= 2290 | 46 | 2.03 | 93.52 |
| 4 | ГОСТ 34028-2016(214-210-0502-0001) | Ф 12 А500С L= 2290 | 12 | 2.03 | 24.40 |
| Ск1 | ГОСТ 34028-2016(214-210-0502-0003) | Ф 16 А500С L= 2120 | 9 | 3.35 | 30.11 |
| Ф1 | ГОСТ 34028-2016(214-210-0502-0001) | Ф 12 А500С L= 1092 | 17 | 0.97 | 16.48 |
| Ф2 | ГОСТ 34028-2016(214-210-0502-0001) | Ф 12 А500С L= 1132 | 5 | 1.01 | 5.03 |
| С1 | ГОСТ 23279-2012(214-403-01010) | 4С 5Вр-I-100 / 5Вр-I-100(50) 75х130 | 9 | 3.01 | 27.1 |
| | | Материалы: | | | |
| | (212-101-0901) | Класс бетона С 20/25 (В25), м³ | | | 1.80 |
| | | Лестничный марш Лм-5 | | | 250.96 |
| 11 | ГОСТ 34028-2016(214-210-0502-0003) | Ф 16 А500С L= 3970 | 8 | 6.27 | 50.13 |
| 12 | ГОСТ 34028-2016(214-210-0502-0003) | Ф 16 А500С L= 3950 | 8 | 6.23 | 49.88 |
| 3 | ГОСТ 34028-2016(214-210-0502-0001) | Ф 12 А500С L= 2290 | 40 | 2.03 | 81.32 |
| | | | | | |
| Ск1 | ГОСТ 34028-2016(214-210-0502-0003) | Ф 16 А500С L= 2120 | 9 | 3.35 | 30.11 |
| Ф1 | ГОСТ 34028-2016(214-210-0502-0001) | Ф 12 А500С L= 1092 | 19 | 0.97 | 18.42 |
| С1 | ГОСТ 23279-2012(214-403-01010) | 4С 5Вр-I-100 / 5Вр-I-100(50) 75х130 | 7 | 3.01 | 21.1 |
| | | Материалы: | | | |
| | (212-101-0901) | Класс бетона С 20/25 (В25), м³ | | | 1.35 |

## Ведомость деталей

| Поз. | Эскиз | Поз. | Эскиз |
|---|---|---|---|
| Ск1 | 1000, 120, 1000; по н.г. L=2120 | 6 | 1420, 154°, 4250; по н.г. L=5670 |
| Ф1 | 300, 96, 96, 300, 300; по н.г. L=1092 | 7 | 980, 153°, 4470, 153°, 320; по н.г. L=5770 |
| Ф2 | 300, 116, 116, 300, 300; по н.г. L=1132 | 8 | 1010, 4430, 153°, 330; по н.г. L=5770 |
| 1 | 1010, 153°, 4330; по н.г. L=5340 | 9 | 1310, 3080, 153°, 1230; по н.г. L=5620 |
| 2 | 980, 153°, 4070; по н.г. L=5050 | 10 | 1280, 3130, 153°, 1210; по н.г. L=5620 |
| 3 | 1310, 120, 860; по н.г. L=2290 | 11 | 1690, 153°, 2280; по н.г. L=3970 |
| 4 | 2910, 120, 860; по н.г. L=3890 | 12 | 1720, 154°, 2230; по н.г. L=3950 |
| 5 | 1390, 153°, 4290; по н.г. L=5680 | | |

## Ведомость расхода стали, кг

| Марка элемента | Изделия арматурные | | | | | | | Всего |
|---|---|---|---|---|---|---|---|---|
| | Арматура класса | | | | | | | |
| | Вр | | | А500С | | | | |
| | ГОСТ 23279-2012 (214-403-01010) | | | ГОСТ 34028-2016(214-210-0502) | | | | |
| | Ф5 | Ф6 | Итого | Ф12 | Ф14 | Ф16 | Итого | |
| Лестница Л-1 | 280.77 | 0.00 | 280.77 | 1087.42 | 0.00 | 1335.40 | 2422.82 | 2703.59 |

| | | | | | | | |
|---|---|---|---|---|---|---|---|
| | | | | | | | 65П-АИП-2024-1-КЖ |
| | | | | | | | Строительство многопрофильной больницы на 250 коек с онкологическим центром и поликлиникой на 350 посещений, по адресу: Медеуский район, г. Алматы |
| Изм. | Кол.уч. | Лист | N док. | Подп. | Дата | | |
| | | | | | | "Блок 1 Секция 1" | Стадия: РП; Лист: 9.3; Листов: |
| ГКП | | Курал М | | | | | |
| Проверил | | Кыдырбай А | | | | Спецификация лестницы Л-1 по оси 1с - 2с | АстанаИнжПроект |
| Разраб. | | Ауез Б | | | | | |
| Н.контроль | | Ешенкулова | | | | | |

Формат А2